



PLAN CLP

1

BLOC B

RD SEBASTARD GARNIER

RD DES ETUANTS

RD DES ERABLES

ZONE DES TRAVAUX

ARCHITECTE:

leclerc
architectes

105 rue du Parcours • 91000 MONTAIGNEY • 01 69 20 20 20 • contact@leclerc-architectes.com • 0 814 80 80 80

- Légende — D210_ADD (487 marques)
- ◆ Dém. chauffage — à classer (2)
 - Dém. luminaire 1x4 / segment linéaire (179)
 - Dém. luminaire 2x4 (163)
 - Dém. luminaire rond encastré (27)
 - Dém. prise plafond projecteur (2)
 - Détecteur fumée existant — dépose/repose temp. (33)
 - Détecteur sécurité (M) — par autres (8)
 - ▲ Haut-parleur classe — par autres (3)
 - Luminaire 24h existant — dépose/repose temp. (32)
 - Repère EAC — existant à conserver (14)
 - Station manuelle existante (F) — à confirmer (10)
 - ◆ Éclairage existant carré — à classer (13)
 - ◆ Éclairage existant — à classer (1)

CE DOCUMENT NE DOIT
PAS ÊTRE UTILISÉ À DES
FINS DE CONSTRUCTION

01	2026-08-20	EMIS POUR ADDENDA E-01	M-D-A
00	2026-07-09	EMIS POUR APPEL D'OFFRES	M-D-A
No.	Date	Description	Pa



CIMA+ 900-740, rue Notre-Dame Ouest
Montréal QC H3C 3X8
CANADA
T 514 337-2452
F 514 281-1632
cima.ca

CENTRE DE SERVICES
SCOLAIRE DE
SOREL-TRACEY

RÉHABILITATION ET TRAVAUX
CONNEXES
ÉCOLE SECONDAIRE BERNARD-GARIÉPY

ÉCLAIRAGE
REZ-DE-CHAUSSÉE BLOC E
EXISTANT / DÉMOLITION

ÉLECTRICITÉ

DESSIN PAR : P. TORRES	ECHELLE : INDIQUE
CONÇU PAR : M. DUSSAULT-MATTE, ing.	DATE : 2026-04-17
VÉRIFIÉ PAR : M. DUSSAULT-MATTE, ing.	VÉRIFIÉ PAR : T. TAN, ing.
PROJET No : P0002920	DESSIN No : E-D210
FEUILLE No :	



- 1 APPAREIL D'ÉCLAIRAGE 24 H ENLEVER POUR LES TRAVAUX DE DÉMOLITION D PLAFOND ET SUSPENDRE TEMPORAIREMENT DU PLAFOND.
- 2 APPAREIL(S) D'ÉCLAIRAGE AU DEL À ENLEVER ET REMETTRE AU PROPRIÉTAIRE
- 3 DETECTEUR DE FUMÉE À ENLEVER POUR LES TRAVAUX DE DÉMOLITION DES TUILES ET LE SUSPENDRE À PARTIR DU PLAFOND POUR UNE UTILISATION TEMPORAIRE
- 4 ENSEIGNE DE SORTIE À ENLEVER POUR LES TRAVAUX DE DÉMOLITION ET LA SUSPENDRE À PARTIR DU PLAFOND POUR UNE UTILISATION TEMPORAIRE.
- 5 APPAREILS D'ÉCLAIRAGE ET DETECTEURS DE FUMÉE À ENLEVER POUR LES TRAVAUX DE DECONTAMINATION: SUSPENDRE CES ÉQUIPEMENTS POUR UNE UTILISATION TEMPORAIRE.



380, rue St-Jacques, #1810, Mt. Royal JPS info@claciere-architectes.com T 514

- ◆ Alarme existante — à classer (2)
- ◆ Dém. chauffage — à classer (1)
- Dém. luminaire 1x4 / segment linéaire (284)
- Dém. luminaire 2x2 (2)
- Dém. luminaire 2x4 (109)
- Dém. luminaire rond encastré (20)
- ◆ Dém. éclairage — à classer (11)
- Détecteur fumée existant — dépose/repose temp. (46)
- Détecteur sécurité (M) — par autres (3)
- Luminaire 24h existant — dépose/repose temp. (44)
- Repère EAC — existant à conserver (8)
- Station manuelle existante (F) — à confirmer (9)
- ◆ Éclairage existant carré — à classer (17)
- ◆ Éclairage existant — à classer (2)

CE DOCUMENT NE DOIT PAS ÊTRE UTILISÉ À DES FINS DE CONSTRUCTION

01	2026-08-20	ÉMIS POUR ADDENDA E-01	M.D.M.
00	2026-07-09	ÉMIS POUR APPEL D'OFFRES	M.D.M.
No.	Date	Description	Pa

SCHEMA :



CIMA+ 900-740, rue Notre-Dame Ouest
Montréal QC H3C 3X8
CANADA
T 514 337-2452
F 514 281-1632
cima.ca

CENTRE DE SERVICES
SCOLAIRE DE
SOREL-TRACEY

RÉHABILITATION ET TRAVAUX
CONNEXES
ÉCOLE SECONDAIRE BERNARD-GARIÉPY

ÉCLAIRAGE
REZ-DE-CHAUSSÉE BLOC
EXISTANT / DÉMOLITION

DISCIPLINE : ÉLECTRICITÉ

DESIGNÉ PAR : P. TORRES	ECHÉLLE : INDIQUÉ
CONQU PAR : M. DUSSAULT-MATTE, ing.	DATE : 2026-04-17
VÉRIFIÉ PAR : M. DUSSAULT-MATTE, ing.	VÉRIFIÉ PAR : T. TAN, ing.
PROJET No : P0002920	DESIGN No : E-D211
FEUILLE No :	



- CE DOCUMENT NE DOIT
PAS ÊTRE UTILISÉ À DES
FINS DE CONSTRUCTION

01	2026-08-20	EMIS POUR ADDENDA E-01	M-D-Ming
00	2026-07-09	EMIS POUR APPEL D'OFFRES	M-D-Ming
No.	Date	Description	Par




CIMA+

CENTRE DE SERVICES
SCOLAIRE DE
SOREL-TRACEY

RÉHABILITATION ET TRAVAUX
CONNEXES
ÉCOLE SECONDAIRE BERNARD-GARIÉPY

ÉCLAIRAGE
REZ-DE-CHAUSSÉE BLOC C1
EXISTANT / DÉMOLITION

ÉLECTRICITÉ	
DESSIN PAR : P. TORRES	RÉVISÉ PAR : INDIQUÉ
CONÇU PAR : M. DUSSAULT-MATTE, ing.	DATE : 2026-04-17
EXÉCUTÉ PAR : M. DUSSAULT-MATTE, ing.	NOMÉ PAR : T. TAN, ing.
PROJET No : P0002920	DESSIN No : E-D212
ÉCHAELLE No : 06 DE 10	

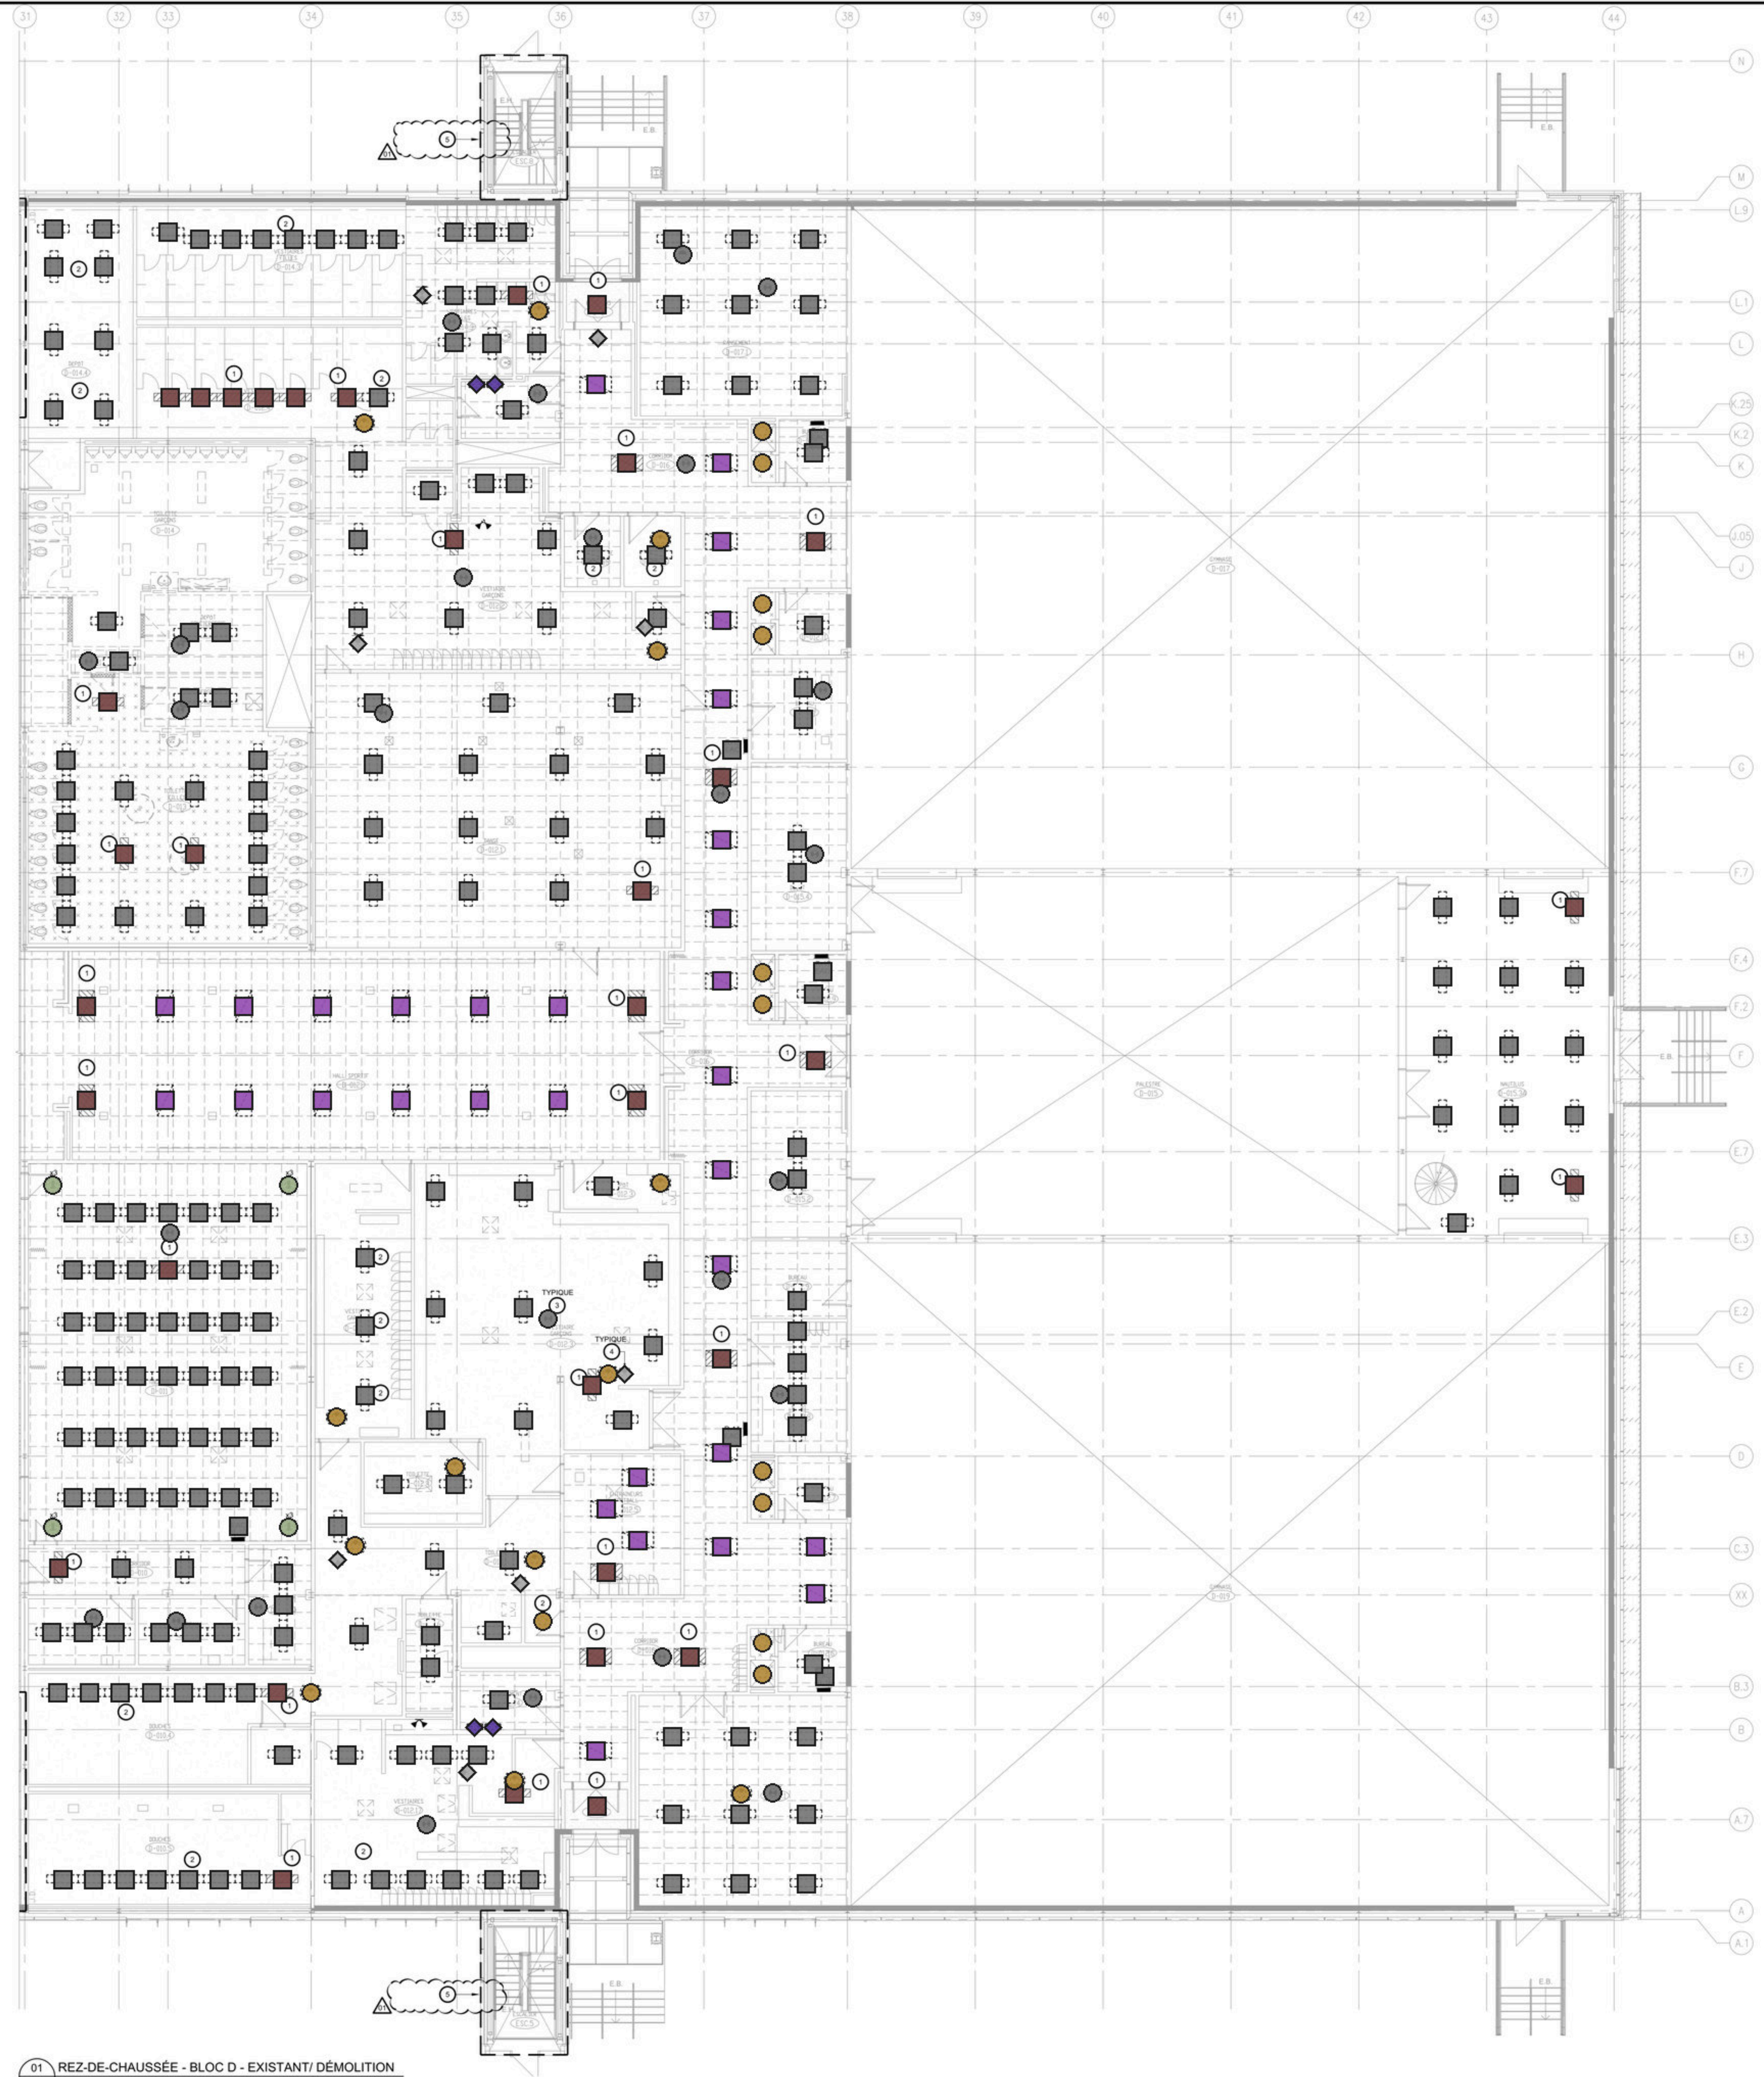

01 REZ-DE-CHAUSSEE - BLOC D - EXISTANT/ DEMOLITION
E-D212 ÉCHELLE : 1:100

- 1 APPAREIL D'ÉCLAIRAGE 24 H À ENLEVER POUR LES TRAVAUX DE DÉMOLITION ET SUSPENDRE TEMPORAIREMENT LE PLAFOND.
- 2 APPAREIL(S) DÉCLARAGE AU DEL À ENLEVER ET REMETTRE AU PROPRIÉTAIRE.
- 3 DÉTECTEUR DE FUMÉE À ENLEVER POUR LES TRAVAUX DE DÉMOLITION DES T ET LE SUSPENDRE À PARTIR DU PLAFOND POUR UNE UTILISATION TEMPORAIRE.
- 4 ENSEIGNE DE SORTIE À ENLEVER POUR LES TRAVAUX DE DÉMOLITION ET LA SUSPENDRE À PARTIR DU PLAFOND POUR UNE UTILISATION TEMPORAIRE.
- 5 APPAREILS D'ÉCLAIRAGE ET DÉTECTEURS DE FUMÉE À ENLEVER POUR LES TRAVAUX DE DÉCONTAMINATION. SUSPENDRE CES ÉQUIPEMENTS POUR UNE UTILISATION TEMPORAIRE.



- Dém. luminaire 1x4 / segment linéaire (221)
- Dém. luminaire 2x4 (31)
- Dém. luminaire rond encastré (24)
- Dém. prise plafond projecteur (4)
- ◆ Dém. éclairage — à classer (4)
- Détecteur fumée existant — dépose/repose temp. (26)
- Luminaire 24h existant — dépose/repose temp. (34)
- Repère EAC — existant à conserver (6)
- ◆ Éclairage existant carré — à classer (8)

CE DOCUMENT NE DOIT
PAS ÊTRE UTILISÉ À DES
FINS DE CONSTRUCTION

01	2026-08-20	ÉMIS POUR ADDENDA E-01	M.D-M
00	2026-07-09	ÉMIS POUR APPEL D'OFFRES	M.D-M
No.	Date	Description	Pa

BEAUM:				
--------	--	--	--	--



CIMA+
900-760, rue Notre-Dame Ouest
Montréal QC H3C 3X8
CANADA
T 514 337-2462
F 514 281-1632
cima.ca

CENTRE DE SERVICES
SCOLAIRE DE
SOREL-TRACEY


RÉHABILITATION ET TRAVAUX
CONNEXES
ÉCOLE SECONDAIRE BERNARD-GARIÉPY

ÉCLAIRAGE
REZ-DE-CHAUSSÉE BLOC
EXISTANT / DÉMOLITION

ÉLECTRICITÉ

DESIGNÉ PAR : P. TORRES	ÉCHELLE : INDIQUÉ
CONQU PAR : M. DUSSAULT-MATTE, ing.	DATE : 2026-04-17
VÉRIFIÉ PAR : M. DUSSAULT-MATTE, ing.	VÉRIFIÉ PAR : T. TAN, ing.
PROJET No : P0002920	DESIGN No : E-D213
FEUILLE No :	

E-D213

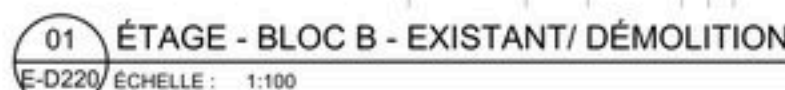

Légende — D220_ADD (553 marques)

- Dém. luminaire 1x4 / segment linéaire (318)
- Dém. luminaire 2x4 (131)
- Dém. prise plafond projecteur (7)
- Détecteur fumée existant — dépose/repose temp. (38)
- Luminaire 24h existant — dépose/repose temp. (37)
- Prise existante — à classer (4)
- Repère EAC — existant à conserver (5)
- Station manuelle existante (F) — à confirmer (4)
- ◆ Éclairage existant carré — à classer (9)

CE DOCUMENT NE DOIT
PAS ÊTRE UTILISÉ À DES
FINS DE CONSTRUCTION

01	2026-08-20	ÉMIS POUR ADDENDA E-01	M-D-M (ing.)
00	2026-07-09	ÉMIS POUR APPEL D'OFFRES	M-D-M (ing.)
No.	Date	Description	Par



CIMA+ 900-740, rue Notre-Dame Ouest
Montréal QC H3C 3X8
CANADA
T 514 337-2462
F 514 281-1632
cima.ca


CENTRE DE SERVICES
SCOLAIRE DE
SOREL-TRACEY

RÉHABILITATION ET TRAVAUX
CONNEXES
ÉCOLE SECONDAIRE BERNARD-GARIÉPY

ÉCLAIRAGE
ÉTAGE BLOC B
EXISTANT / DÉMOLITION

ÉLECTRICITÉ

DESSIN PAR : P. TORRES	ECHELLE : INDIQUE
CONÇU PAR : M. DUSSAULT-MATTE, ing.	DATE : 2028-04-17
VÉRIFIÉ PAR : M. DUSSAULT-MATTE, ing.	VÉRIFIÉ PAR : T. TAN, ing.
PROJET No : P0002920	DESSIN No : E-D220
FEUILLE No :	

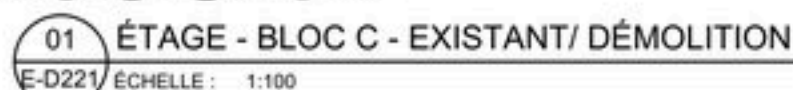

P0002920	E-D221
FEUILLE No : 09 DE 10	



- Légende — D222_ADD (463 marques)
- Dém. luminaire 1x4 / segment linéaire (366)
 - Dém. luminaire 2x4 (45)
 - Détecteur fumée existant — dépose/repose temp. (13)
 - Luminaire 24h existant — dépose/repose temp. (27)
 - Repère EAC — existant à conserver (6)
 - Station manuelle existante (F) — à confirmer (4)
 - ◆ Éclairage existant carré — à classer (2)



CE DOCUMENT NE DOIT
PAS ÊTRE UTILISÉ À DES
FINS DE CONSTRUCTION

01	2026-08-20	ÉMIS POUR ADDENDA E-01			M-D-M
00	2026-07-09	ÉMIS POUR APPEL D'OFFRES			M-D-M
No.	Date	Description			Par



CENTRE DE SERVICES
SCOLAIRE DE
SOREL-TRACEY

PROJET :

RÉHABILITATION ET TRAVAUX
CONNEXES
ÉCOLE SECONDAIRE BERNARD-GARIEPY

ÉCLAIRAGE
ÉTAGE BLOC D
EXISTANT / DÉMOLITION

ÉLECTRICITÉ	
DESIGNÉ PAR P. TORRES	ÉCHELLE INDIQUE
ONDU FANT A. DUSSAULT-MATTE, ing.	DATE 2026-04-17
EXPÉDÉ PAR A. DUSSAULT-MATTE, ing.	VERIFIÉ PAR T. TAN, ing.
MOUET N° 0002920	DESIGN N°
SÉRIE N° 10 DE 10	E-D222



VOIR PI ANT-D401

- LES HAUT-PARLEURS SE TROUVANT DANS LES BLOCS B, C ET C1 SERONT RELEVÉS DURANT LES TRAVAUX DE DÉMOLITION. PLUS RÉUNIONS LOCALES DU HAUT-ÉCARTEMENT. L'ENTREPRENEUR DOIT ENTREPRENDRE LES TRAVAUX DE DÉMOLITION.
- AINSI CÂBLE DE TÉLÉCOMMUNICATION NE DOIT ÊTRE DÉMONTÉ DURANT LES TRAVAUX DE DÉMOLITION.
- PORTER UNE ATTENTION PARTICULIÈRE À PROTÉGER LE LIEN DE FIBRE OPTIQUE ENTRE LES LOCS B-111 ET D-132.
- SE RÉFÉRER AU DEVIS DÉTAILLÉ POUR LES CONDITIONS GÉNÉRALES ET LES DÉFINITIONS ADDITIONNELLES.
- LES CAMÉRAS, BORNES W/F, PROJECTEURS ET HAUT-PARLEURS DE CLASSE SERONT RELEVÉS AVANT LES TRAVAUX D'ENTRÉPRISE PAR LE CAS POUR LA DURÉE DES TRAVAUX.
- TOUTES LES IDENTIFICATIONS EXISTANTES SUR LES GRILLES DU PAVAGE (AUTOCOULANTS JAUNES, BLEUS ET ROUGES) REPRÉSENTENT L'EMPLACEMENT DES BORNES W/F, DES VALES MÉRIQUE ET DES ÉLÉMENTS D'IDENTIFICATION ÉVENTUELLES CONSERVÉS DURANT LES TRAVAUX DE DÉMOLITION.



CE DOCUMENT NE DOIT
PAS ÊTRE UTILISÉ À DES
FINS DE CONSTRUCTION

No.	Date	Description	Par
-----	------	-------------	-----



CIMA+


CENTRE DE SERVICES
SCOLAIRE DE
SOREL-TRACEY

RÉHABILITATION ET TRAVAUX
CONNEXES
ÉCOLE SECONDAIRE BERNARD-GARIÉPY

TÉLÉCOMMUNICATIONS
DÉMOLITION PHASE 1 SOUS-SOL
EXISTANT / DÉMOLITION

DISCIPLINE : **TÉLÉCOMMUNICATIONS**

DESIGNER PAR : C-A. GRAVEL	REVUE : INDIQUE
CONÇU PAR : A. SY, tech.	DATE : 2026-04-17
VÉRIFIÉ PAR :	VÉRIFIÉ PAR : D. VINCENT, ing.
PROJET No : P0002920	DESIGN No : T-D400
FEUILLE No : 1 DE 11	

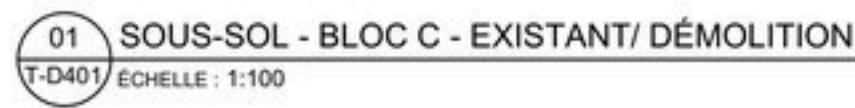

Plan de la zone de travaux. Le schéma illustre la configuration des rues et la zone d'intervention. Les rues représentées sont le BO BERNARD, la GARIEPY, le BO DES ÉTIENNES, le BO DES ÉRABLES et le BO DES ÉTOILES. La zone de travaux est indiquée par un hachurage et une légende en bas à gauche.

leclerc
architectes

CE DOCUMENT NE DOIT
PAS ÊTRE UTILISÉ À DES
FINS DE CONSTRUCTION

0	2026-07-08	EMIS POUR APPEL D'OFFRES	D.V.
No	Date	Description	Par



1000

CIMA+ 900-740, rue Notre-Dame Ouest
Montréal QC H3C 3X5
CANADA
T 514 337-2462
F 514 281-1632
cima.ca

CLIENT

CENTRE DE SERVICES
SCOLAIRE DE
SOREL-TRACEY

PROCUR

RÉHABILITATION ET TRAVAUX
CONNEXES
ÉCOLE SECONDAIRE BERNARD-GARIÉPY


TIME DUO 2000

TÉLÉCOMMUNICATIONS
DÉMOLITION PHASE 1 SOUS-SOL
EXISTANT / DÉMOLITION

DISCIPLINE :


TÉLÉCOMMUNICATIONS

DESIGNÉ PAR : C-A. GRAVEL	EMPELLE : INDIQUE
CONÇU PAR : A. SY, tech.	DATE : 2026-04-17
VERIFIÉ PAR :	VERIFIÉ PAR : D. VINCENT, ing.
PROJET No : P0002920	DESIGN No : T-D401
FEUILLE No : 2 DE 11	

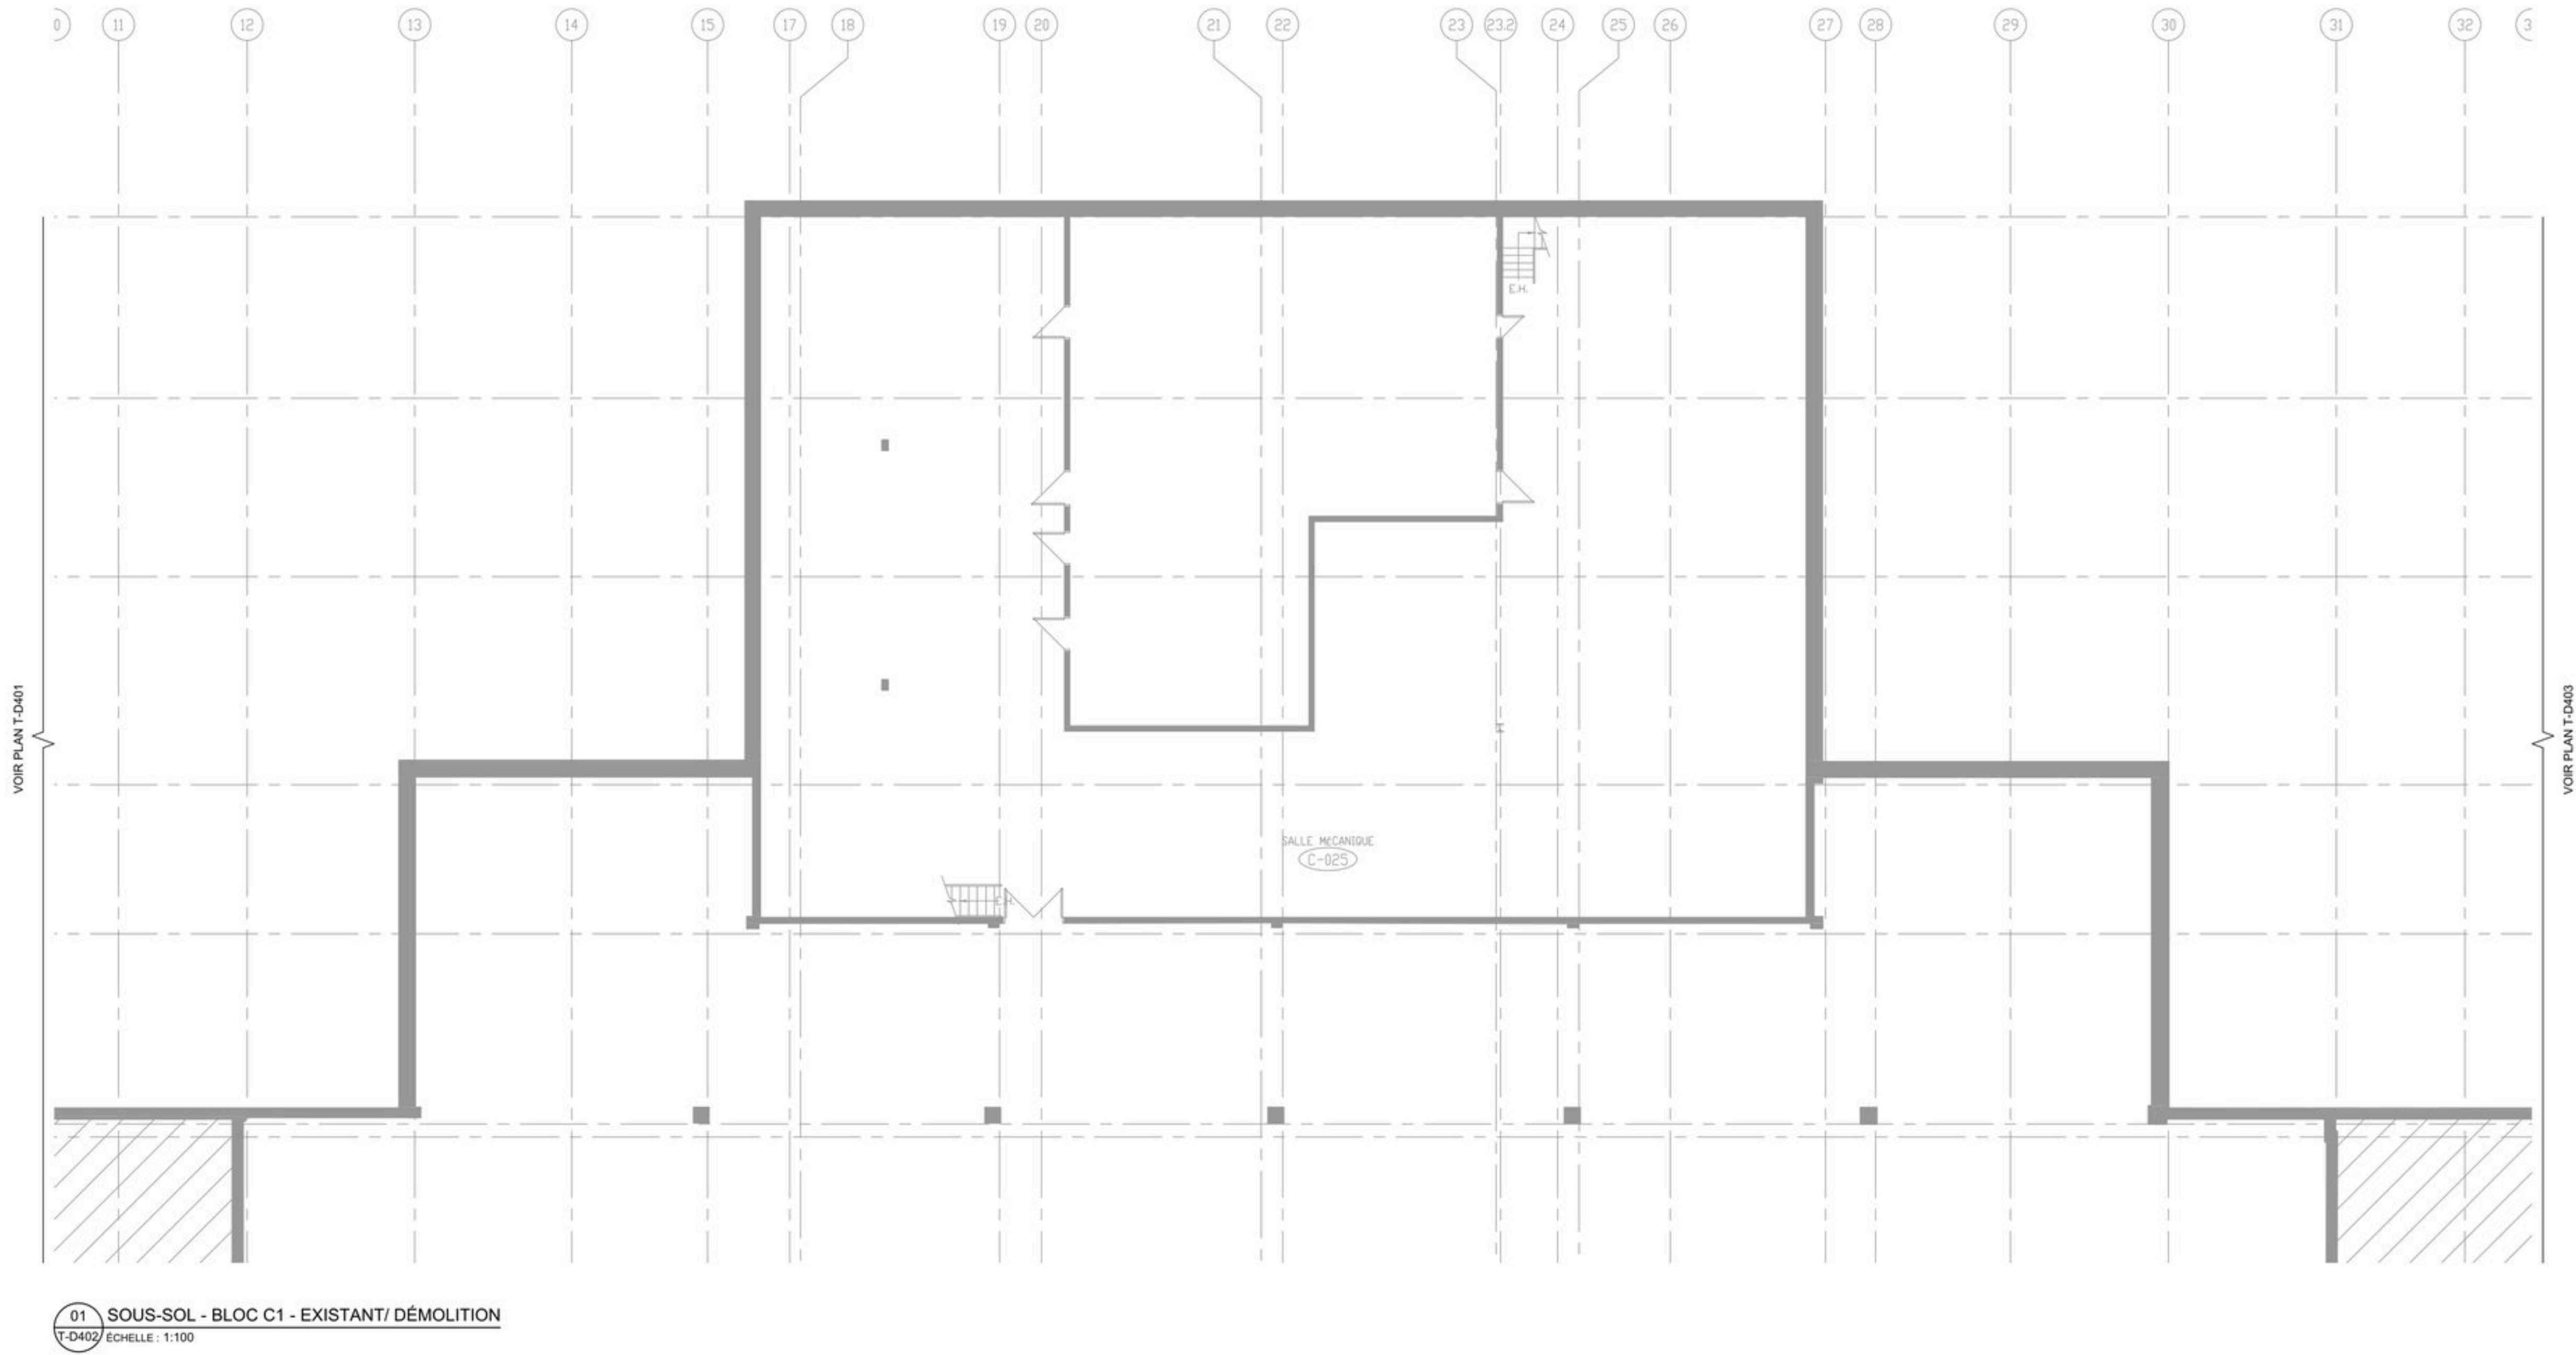

NOTES GÉNÉRALES:

- LES HAUT-PARLEURS SE TROUVANT DANS LES BLOCS B, C ET C1 SERONT RETIRÉS DURANT LES TRAVAUX DE DÉMOLITION PUIS RÉINSTALLÉS LORS DU RÉAMÉNAGEMENT. L'ENTREPRENEUR DEVRA ENTREPOSER LES HAUT-PARLEURS.
- AUCUN CÂBLE DE TÉLÉCOMMUNICATION NE DOIT ÊTRE DÉMANTÉLÉ DURANT LES TRAVAUX DE DÉMOLITION.
- PORTER UNE ATTENTION PARTICULIÈRE À PROTÉGER LE LIEN DE FIBRE OPTIQUE ENTRE LES LOCAUX B-111.4 ET D-132.2.
- SE RÉFÉRER AU DEVS D'ÉLECTRICITÉ POUR LES CONDITIONS GÉNÉRALES ET LES DÉFINITIONS ADDITIONNELLES.
- LES CAMÉRAS, BORNES WI-FI, PROJECTEURS ET HAUT-PARLEURS DE CLASSE SERONT RETIRÉS AVANT LES TRAVAUX ET ENTREPOSÉS PAR LE CSS POUR LA DURÉE DES TRAVAUX.
- TOUTES LES IDENTIFICATIONS EXISTANTES SUR LES GRILLES DU PLAFOND (AUTOCOLLANTS JAUNES, BLEUS ET ROUGES) REPRÉSENTANT L'EMPLACEMENT DES BORNES WI-FI, DES VALVES MÉCANIQUES ET DE L'ÉCLAIRAGE 24H DOIVENT ÊTRE CONSERVÉES DURANT LES TRAVAUX DE DÉMOLITION.

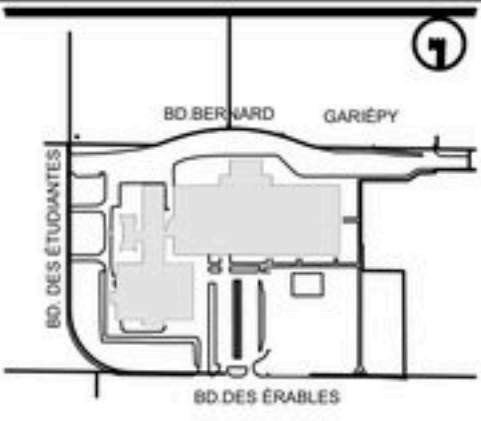

CE DOCUMENT NE DOIT PAS ÊTRE UTILISÉ À DES FINS DE CONSTRUCTION

No.	Date	Description	Par
0	2026-07-08	ÉMISSION POUR APPEL D'OFFRES	D.V.



CENTRE DE SERVICES SCOLAIRE DE SOREL-TRACEY

RÉHABILITATION ET TRAVAUX CONNEXES
ÉCOLE SECONDAIRE BERNARD-GARIÉPY

TÉLÉCOMMUNICATIONS
DÉMOLITION PHASE 1 SOUS-SOL
EXISTANT / DÉMOLITION

DISCIPLINE	
TÉLÉCOMMUNICATIONS	
DESSINÉ PAR C-A. GRAVEL	REVÊLU INDIGUE
APProuvé PAR A. SY, tech.	DATE 2026-04-17
VERIFIÉ PAR D. VINCENT, ing.	DESSINÉ PAR D. VINCENT, ing.
PROJET NO P0002020	DESSIN NO T-D402
3 DE 11	

01 SOUS-SOL - BLOC D - EXISTANT/ DÉMOLITION
T-D403 ÉCHELLE : 1:100

NOTES GÉNÉRALES:

- LES HAUT-PARLEURS DANS LE DOB D'OIENT ÊTRE DÉMANTÉLÉS LORS DES TRAVAUX DE DÉMOLITION. CES HAUT-PARLEURS NE DOIVENT PAS ÊTRE ENTREPOSÉS DURANT LES TRAVAUX.
- AUCUN CÂBLE DE TÉLÉCOMMUNICATION NE DOIT ÊTRE DÉMANTÉLÉ DURANT LES TRAVAUX DE DÉMOLITION.
- SE RÉFÉRER AU DEVS DÉLECTRICITÉ POUR LES CONDITIONS GÉNÉRALES ET LES DÉFINITIONS ADDITIONNELLES
- LES CAMÉRAS, BORNE WS-FL, PROJECTEURS ET HAUT-PARLEURS DE CLASSE SERONT RETIRÉS AVANT LES TRAVAUX ET ENTREPOSÉS PAR LE CSS POUR LA DURÉE DES TRAVAUX.
- TOUTES LES IDENTIFICATIONS EXISTANTES SUR LES GRILLES OU PLATES (AUTOCOLLANTS JAUNES, BLEUS ET ROUGES) REPRÉSENTANT L'EMPLACEMENT DES BORNES WS-FL, DES VALVES MÉCANIQUE ET DE L'ÉCLAIRAGE 24V DOIVENT ÊTRE CONSERVÉES DURANT LES TRAVAUX DE DÉMOLITION



CE DOCUMENT NE DOIT
PAS ÊTRE UTILISÉ À DES
FINS DE CONSTRUCTION

0	2026-07-08	EMIS POUR APPEL D'OFFRES	D.V.
No.	Date	Description	Par



CIMA+ 900-740, rue Notre-Dame Ouest
Montréal QC H3C 3X6
CANADA
T 514 337-2462
F 514 281-1632
cima.ca

CENTRE DE SERVICES
SCOLAIRE DE
SOREL-TRACEY

RÉHABILITATION ET TRAVAUX
CONNEXES
ÉCOLE SECONDAIRE BERNARD-GARIÉPY

TÉLÉCOMMUNICATIONS
DÉMOLITION PHASE 1 SOUS-SOL
EXISTANT / DÉMOLITION

DISCIPLINE :		TÉLÉCOMMUNICATIONS	
VERBIEF PAR : C-A. GRAVEL		BONNELL : INDIQUE	
CONCIS PAR : A. SY, tech.		DATE : 2026-04-17	
VERBIEF PAR :		VERBIEF PAR : D. VINCENT, ing.	
PROJET No : P0002920		DESIGN No : T-D403	
FEUILLE No : 4 DE 11			



01 REZ-DE-CHAUSSEE - BLOC B - EXISTANT/ DÉMOLITION
T-D410 ÉCHELLE : 1:100

NOTES GÉNÉRALES:

- LES HAUT PAREURS SE TROUVANT DANS LES BLOCS B, C ET D SONT RETIRÉS DURANT LE TRAVAIL DE DÉMONTION PLUS RÉSISTANCES LOURD DU TRAVAIL ÉMIGRANT L'ENTREPRENEUR DOIT FAIRE LE TRAVAIL EN SÉCURITÉ
- AUCUN CÂBLE DE TÉLÉCOMMUNICATION NE DOIT ÊTRE DÉMANTÉ DURANT LE TRAVAIL DE DÉMONTION.
- PORTER UNE ATTENTION PARTICULIÈRE À PROTÉGER LE LIEN DE FIBRE OPTIQUE ENTRE LES LOGICIELS B-111 ET D-132-2.
- SE RÉFÉRER AU DES DÉMONTAGE POUR LES CONDITIONS GÉNÉRALES ET LES DES POINTS ADDITIONNELLES
- LES CAMÉRAS BORNES W-LAN, PROJECTEURS ET HAUT PAREURS DE CLASSE C SONT À RETENIR AVANT LE TRAVAIL ET ENTROUSSES PAR CES POUR LA DURÉE DES TRAVAUX
- TOUTES LES IDENTIFICATIONS EXISTANTES SUR LES GRILLES DU PAYSANTEMENT SONT À RETENIR AVANT LE TRAVAIL. DES ÉTIQUETTES SONT À RETENIR AVANT LE TRAVAIL. DES ÉTIQUETTES SONT À RETENIR AVANT LE TRAVAIL. DES ÉTIQUETTES SONT À RETENIR AVANT LE TRAVAIL.



Légende — D410 (23 marques)

▲ Haut-parleur existant — dépose/entreposage (23)

CE DOCUMENT NE DOIT
PAS ÊTRE UTILISÉ À DES
FINS DE CONSTRUCTION



CIMA+


CENTRE DE SERVICES
SCOLAIRE DE
SOREL-TRACEY

RÉHABILITATION ET TRAVAUX
CONNEXES
ÉCOLE SECONDAIRE BERNARD-GARIÉPY

TÉLÉCOMMUNICATIONS
DÉMOLITION PHASE 1
REZ-DE-CHAUSSÉE
EXISTANT / DÉMOLITION

TÉLÉCOMMUNICATIONS

DESIGNÉ PAR : C-A. GRAVEL	ÉCHELLE : INDIQUE
CONÇU PAR : A. SY, tech.	DATE : 2026-04-17
VÉRIFIÉ PAR :	VÉRIFIÉ PAR : D. VINCENT, ing.
PROJET No : P0002920	DESIGN No :
FEUILLE No : S DE 11	T-D410

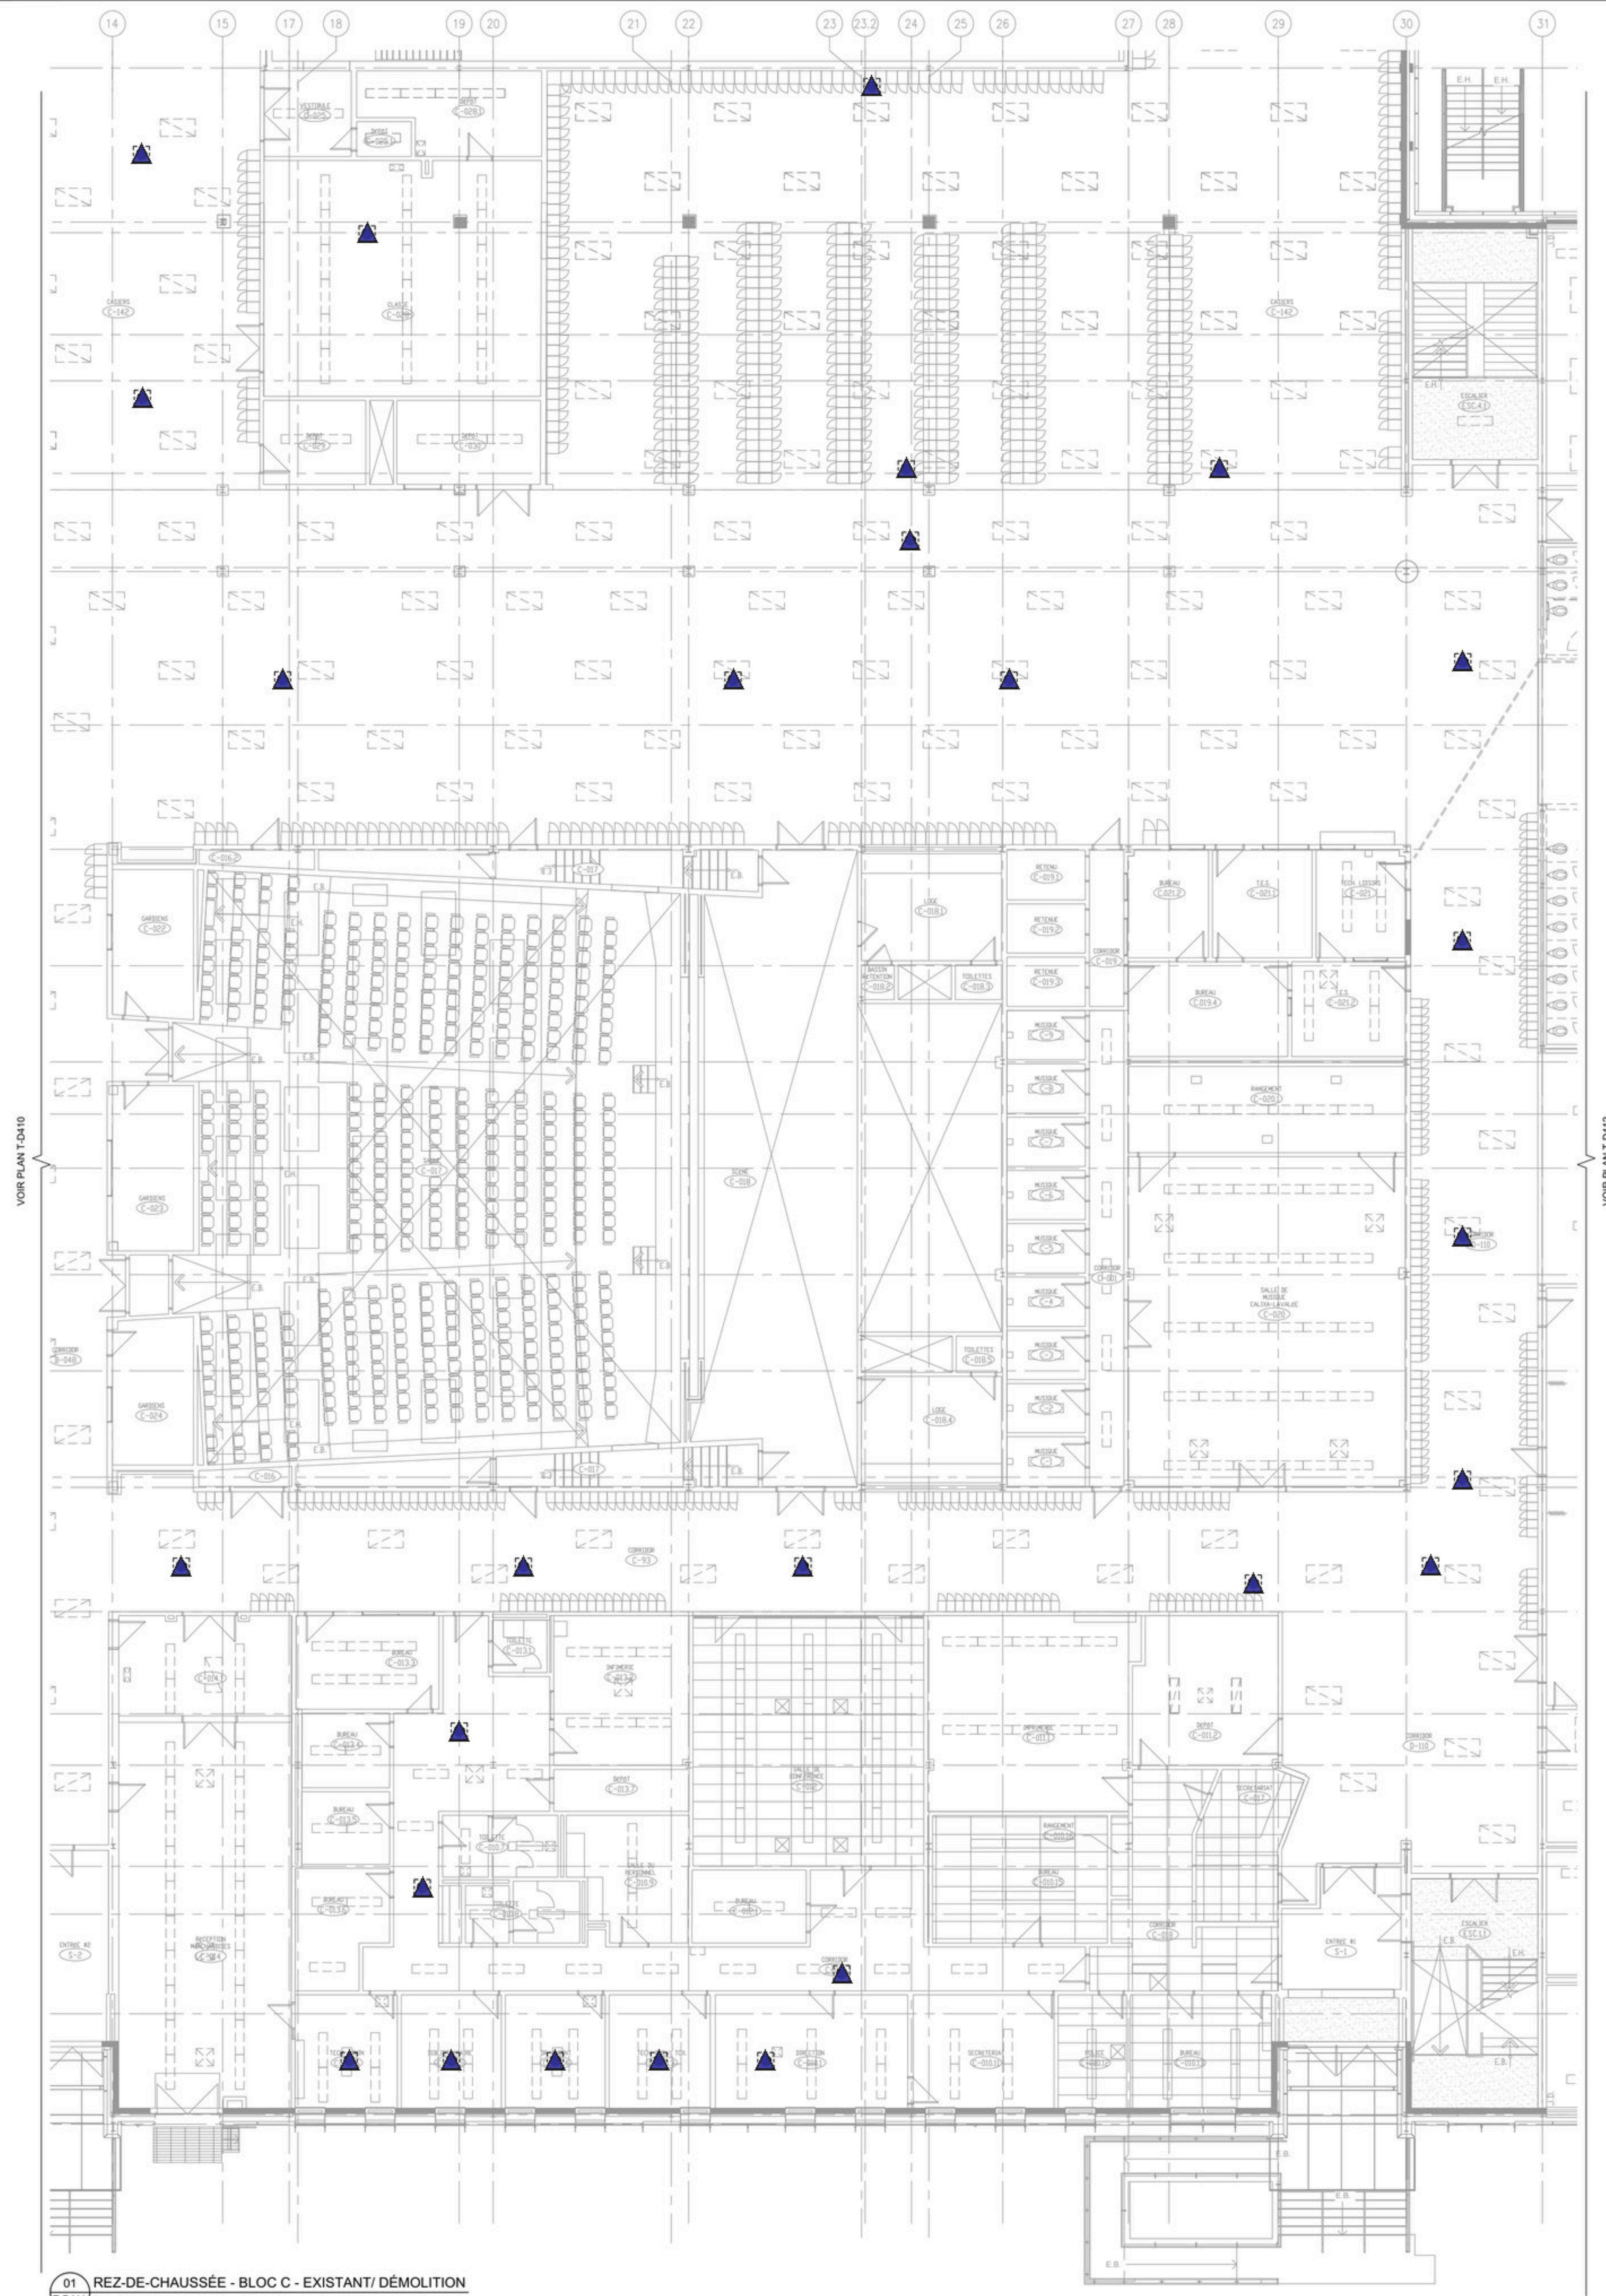

Site plan of the Leclerc store in Lann C'h. The plan shows the building layout, parking areas, and surrounding roads: RD BÉHARD, RD DES ÉTIENNES, RD DES ÉRABLES, and GARNÉPY. A hatched area indicates the 'ZONE DES TRAVAUX' (work zone). A circled number 1 is in the top right corner.

Légende — D411 (27 marques)

▲ Haut-parleur existant — dépose/entreposage (27)

CE DOCUMENT NE DOIT
PAS ÊTRE UTILISÉ À DES
FINS DE CONSTRUCTION

[illegible]

CIMA+ 900-740, rue Notre-Dame Ouest
Montréal QC H3C 3X6
CANADA
T 514 337-2462
F 514 291-1632
cima.ca


CENTRE DE SERVICES
SCOLAIRE DE
SOREL-TRACEY

RÉHABILITATION ET TRAVAUX
CONNEXES
ÉCOLE SECONDAIRE BERNARD-GARIÉPY

TÉLÉCOMMUNICATIONS
DÉMOLITION PHASE 1
REZ-DE-CHAUSSÉE
EXISTANT / DÉMOLITION

TÉLÉCOMMUNICATIONS

DESSIN PAR : C-A. GRAVEL	ECHELLE : INDIQUE
CONÇU PAR : A. SY, tech.	DATE : 2026-04-17
VERIFIÉ PAR :	VERIFIÉ PAR : D. VINCENT, ing.
PROJET No : P0002920	DESSIN No : T-D411
FEUILLE No : 6 DE 11	

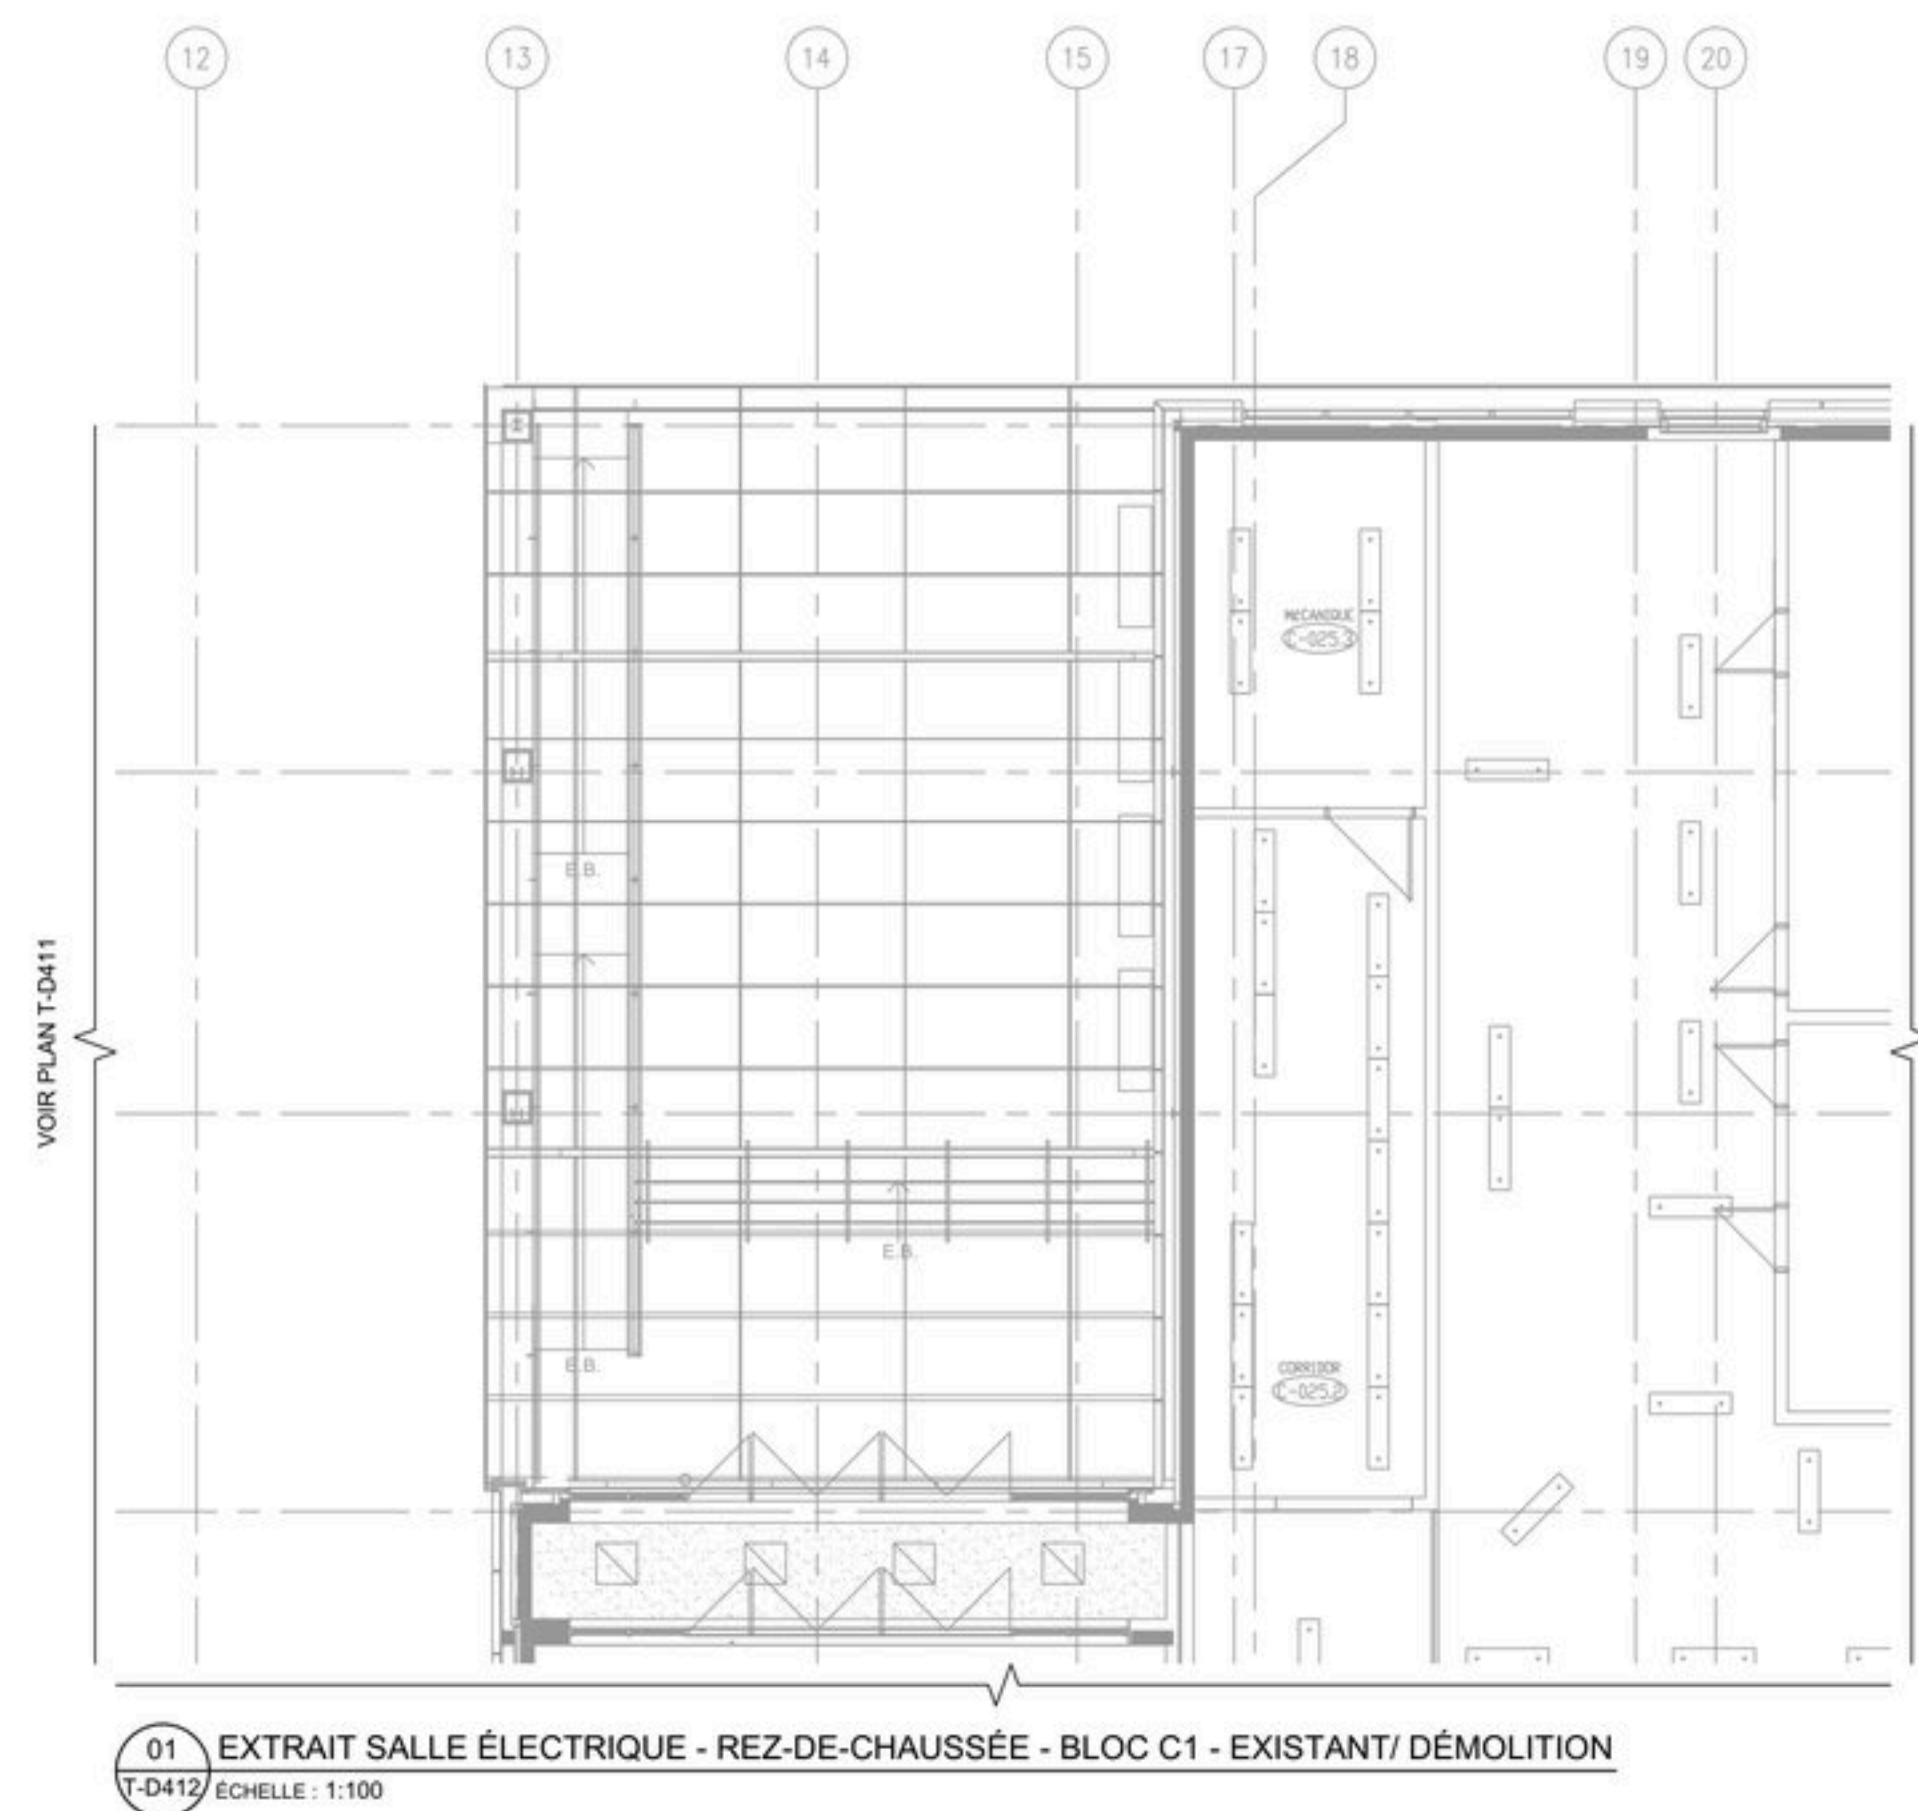

-
- Plan de la zone de travaux. Le schéma illustre la configuration des rues et la zone d'intervention. Les rues représentées sont le BO BERNARD, la GARIEPY, le BO DES ÉTIENNES, le BO DES ÉRABLES et le BO DES ÉTOILES. La zone de travaux est indiquée par un hachurage et une légende en bas à gauche.

leclerc
architectes

CE DOCUMENT NE DOIT
PAS ÊTRE UTILISÉ À DES
FINS DE CONSTRUCTION

0	2026-07-06	EMIS POUR APPEL D'OFFRES	D.V
No.	Date	Description	Par



INGÉNIEUR :

CIMA+

900-740, rue Notre-Dame Ouest
Montréal QC H3C 3X8
CANADA
T 514 337-2462
F 514 281-1632
cima.ca


CENTRE DE SERVICES
SCOLAIRE DE
SOREL-TRACEY

RÉHABILITATION ET TRAVAUX
CONNEXES
ÉCOLE SECONDAIRE BERNARD-GARIÉPY

TITRE DU DESSIN :


TÉLÉCOMMUNICATIONS
DÉMOLITION PHASE 1
REZ-DE-CHAUSSÉE
EXISTANT / DÉMOLITION

SUBJECT: TÉLÉCOMMUNICATIONS	
DRAWN BY: C-A. GRAVEL	SCALE: INDIQUE
CON'D BY: A. SY, tech.	DATE: 2026-04-17
CHECKED BY:	VERIFIED BY: D. VINCENT, ing.
PROJECT No.: P0002920	DESIGN No.:
FEASIBLE No.: 7 DE 11	T-D412

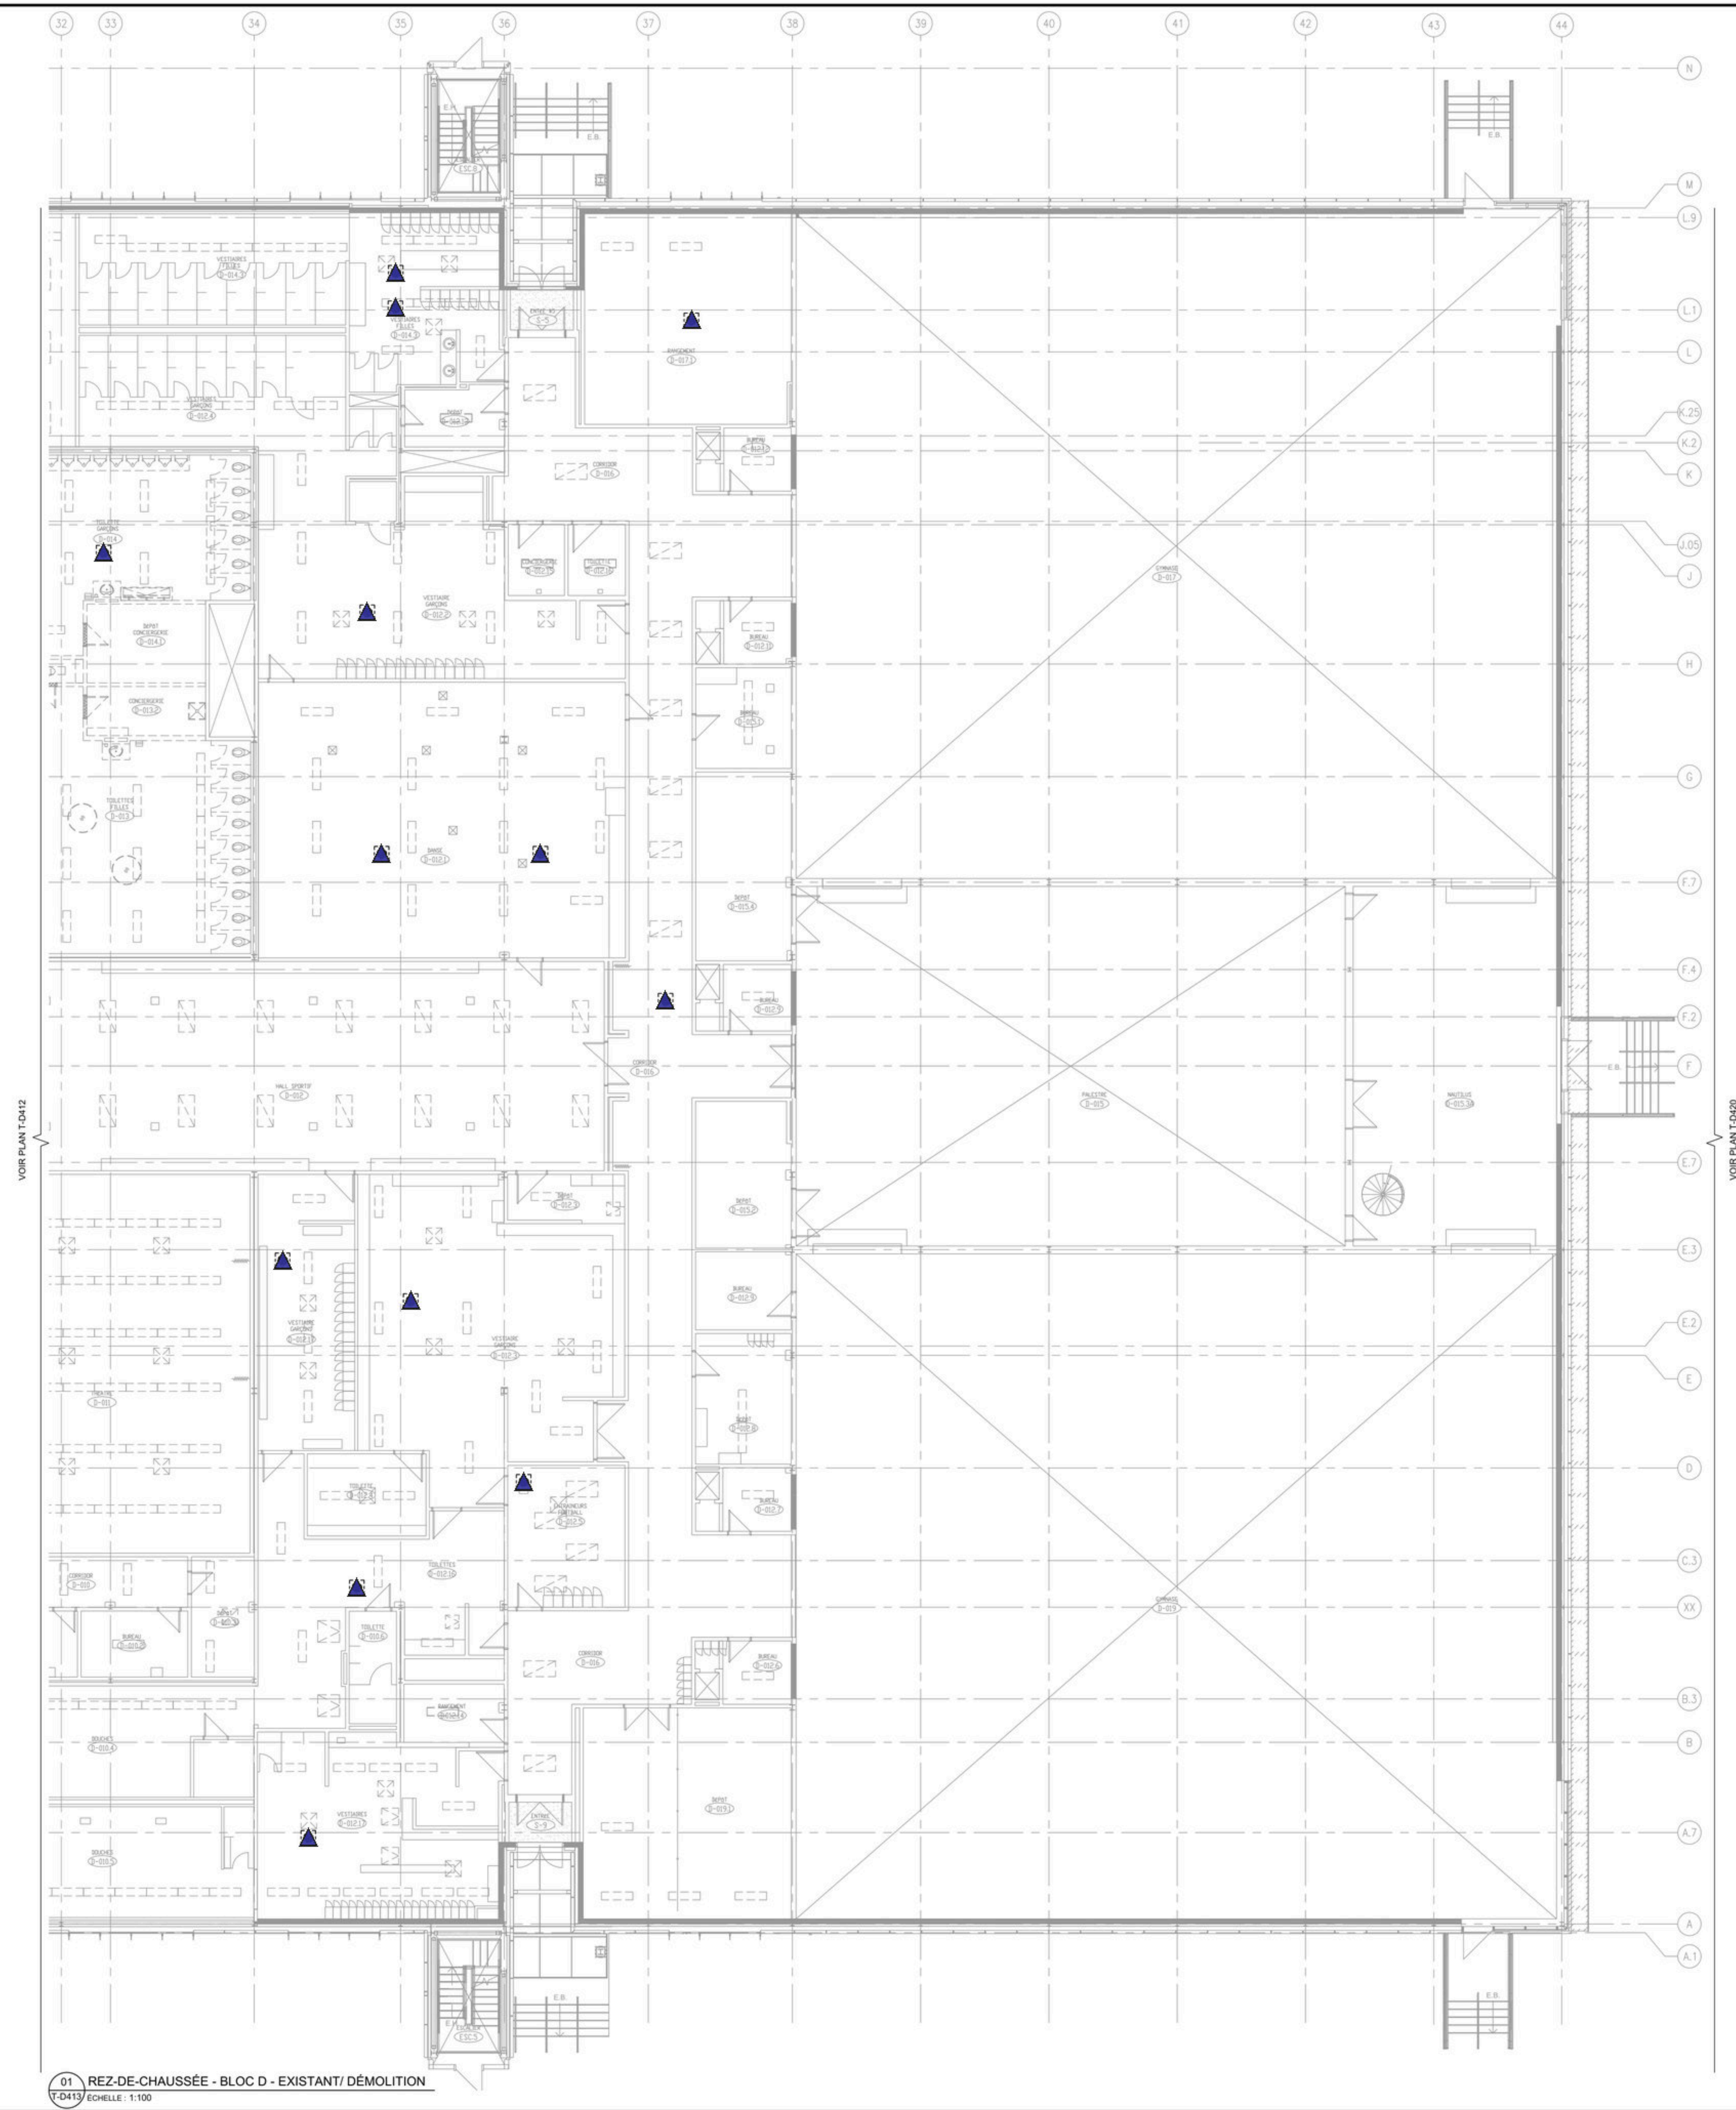

NOTES GÉNÉRALES:

- LES HAUT-PARLEURS DANS LE BLOC D DEVONT ÊTRE DÉMANTÉLÉS LORS DES TRAVAUX DE DÉMOLITION. CES HAUT-PARLEURS NE DOIVENT PAS ÊTRE ENTREPOSÉS DURANT LES TRAVAUX.
- AUCUN CÂBLE DE TÉLÉCOMMUNICATION NE DOIT ÊTRE DÉMANTÉLÉ DURANT LES TRAVAUX DE DÉMOLITION.
- SE RÉFÉRER AU DEVIS DÉLECTROTECHNIQUE POUR LES CONDITIONS GÉNÉRALES ET LES DÉFINITIONS ADDITIONNELLES.
- LES CAMÉRAS, BORNES W-FI, PROJECTEURS ET HAUT-PARLEURS DE CLASSE SONT RETIRÉS AVANT LES TRAVAUX ET ENTREPOSÉS PAR LE CSS POUR LA DURÉE DES TRAVAUX.
- TOUTES LES IDENTIFICATIONS EXISTANTES SUR LES GRILLES DU PAVÉ AUTOCLÉANTS JAUNES, BLEUS ET ROUGES) REPRÉSENTANT L'EMPLACEMENT DES BORNS W-FI, DES RESEAU MÉCANIQUE ET DE L'ÉCLAIRAGE SONT DOIVENT ÊTRE CONSERVÉES DURANT LES TRAVAUX DE DÉMOLITION.

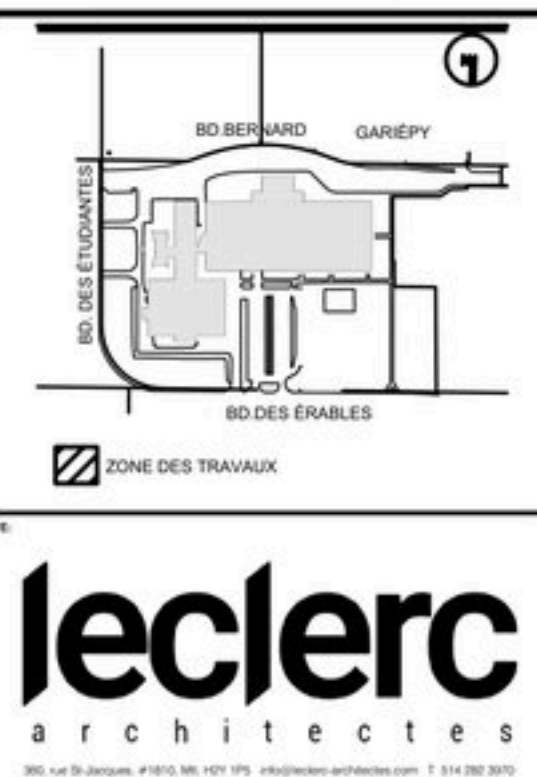

Légende — D413 (13 marques)

▲ Haut-parleur existant — dépose/entrepasage (13)

CE DOCUMENT NE DOIT
PAS ÊTRE UTILISÉ À DES
FINIS DE CONSTRUCTION

0	2026-07-08	EMIS POUR APPEL D'OFFRES	D.V.
No.	Date	Description	Par



CIMA+ 900-740, rue Notre-Dame Ouest
Montréal QC H3C 3X6
CANADA
T 514 337-2462
F 514 281-1632
cima.ca


CENTRE DE SERVICES
SCOLAIRE DE
SOREL-TRACEY

RÉHABILITATION ET TRAVAUX
CONNEXES
ÉCOLE SECONDAIRE BERNARD-GARIÉPY

TÉLÉCOMMUNICATIONS
DÉMOLITION PHASE 1
REZ-DE-CHAUSSÉE
EXISTANT / DÉMOLITION

TÉLÉCOMMUNICATIONS

DESIGNÉ PAR : C-A. GRAVEL	BOULELLE : INDOUE
CONÇU PAR : A. SY, tech.	DATE : 2026-04-17
VERIFIÉ PAR :	VERIFIÉ PAR : D. VINCENT, ing.
PROJET No : P0002920	DESIGN No :
FEUILLE No : 8 DE 11	T-D413

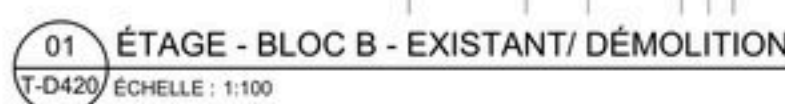

NOTE SPÉCIFIQUE:

1 L'ENTREPRENEUR DOIT PROTÉGER LE CÂBLE DE FIBRE OPTIQUE QUI RELIE LA SALLE S-006 À LA SALLE B-111.4 EN PASSANT PAR S-003 ET B-116.



CE DOCUMENT NE DOIT PAS ÊTRE UTILISÉ À DES FINS DE CONSTRUCTION

1	2026-08-18	ADDENDA T-01	D.V.
0	2026-07-08	EMIS POUR APPEL D'OFFRES	D.V.
No.	Date	Description	Par



CIMA+


CENTRE DE SERVICES
SCOLAIRE DE
SOREL-TRACEY

PROJET :

RÉHABILITATION ET TRAVAUX
CONNEXES
ÉCOLE SECONDAIRE BERNARD-GARIÉPY

TÉLÉCOMMUNICATIONS
DÉMOLITION PHASE 1 ÉTAGE
EXISTANT / DÉMOLITION

PROFILAGE		TÉLÉCOMMUNICATIONS	
DESSINÉ PAR : C-A. GRAVEL		ÉCHELLE : INDIQUE	
CONÇU PAR : A. SY, tech.		DATE : 2026-04-17	
VÉRIFIÉ PAR :		VÉRIFIÉ PAR : D. VINCENT, ing.	
PROJET No : P0002920		DESSIN No :	
ÉCHELLE No :		T-D420	

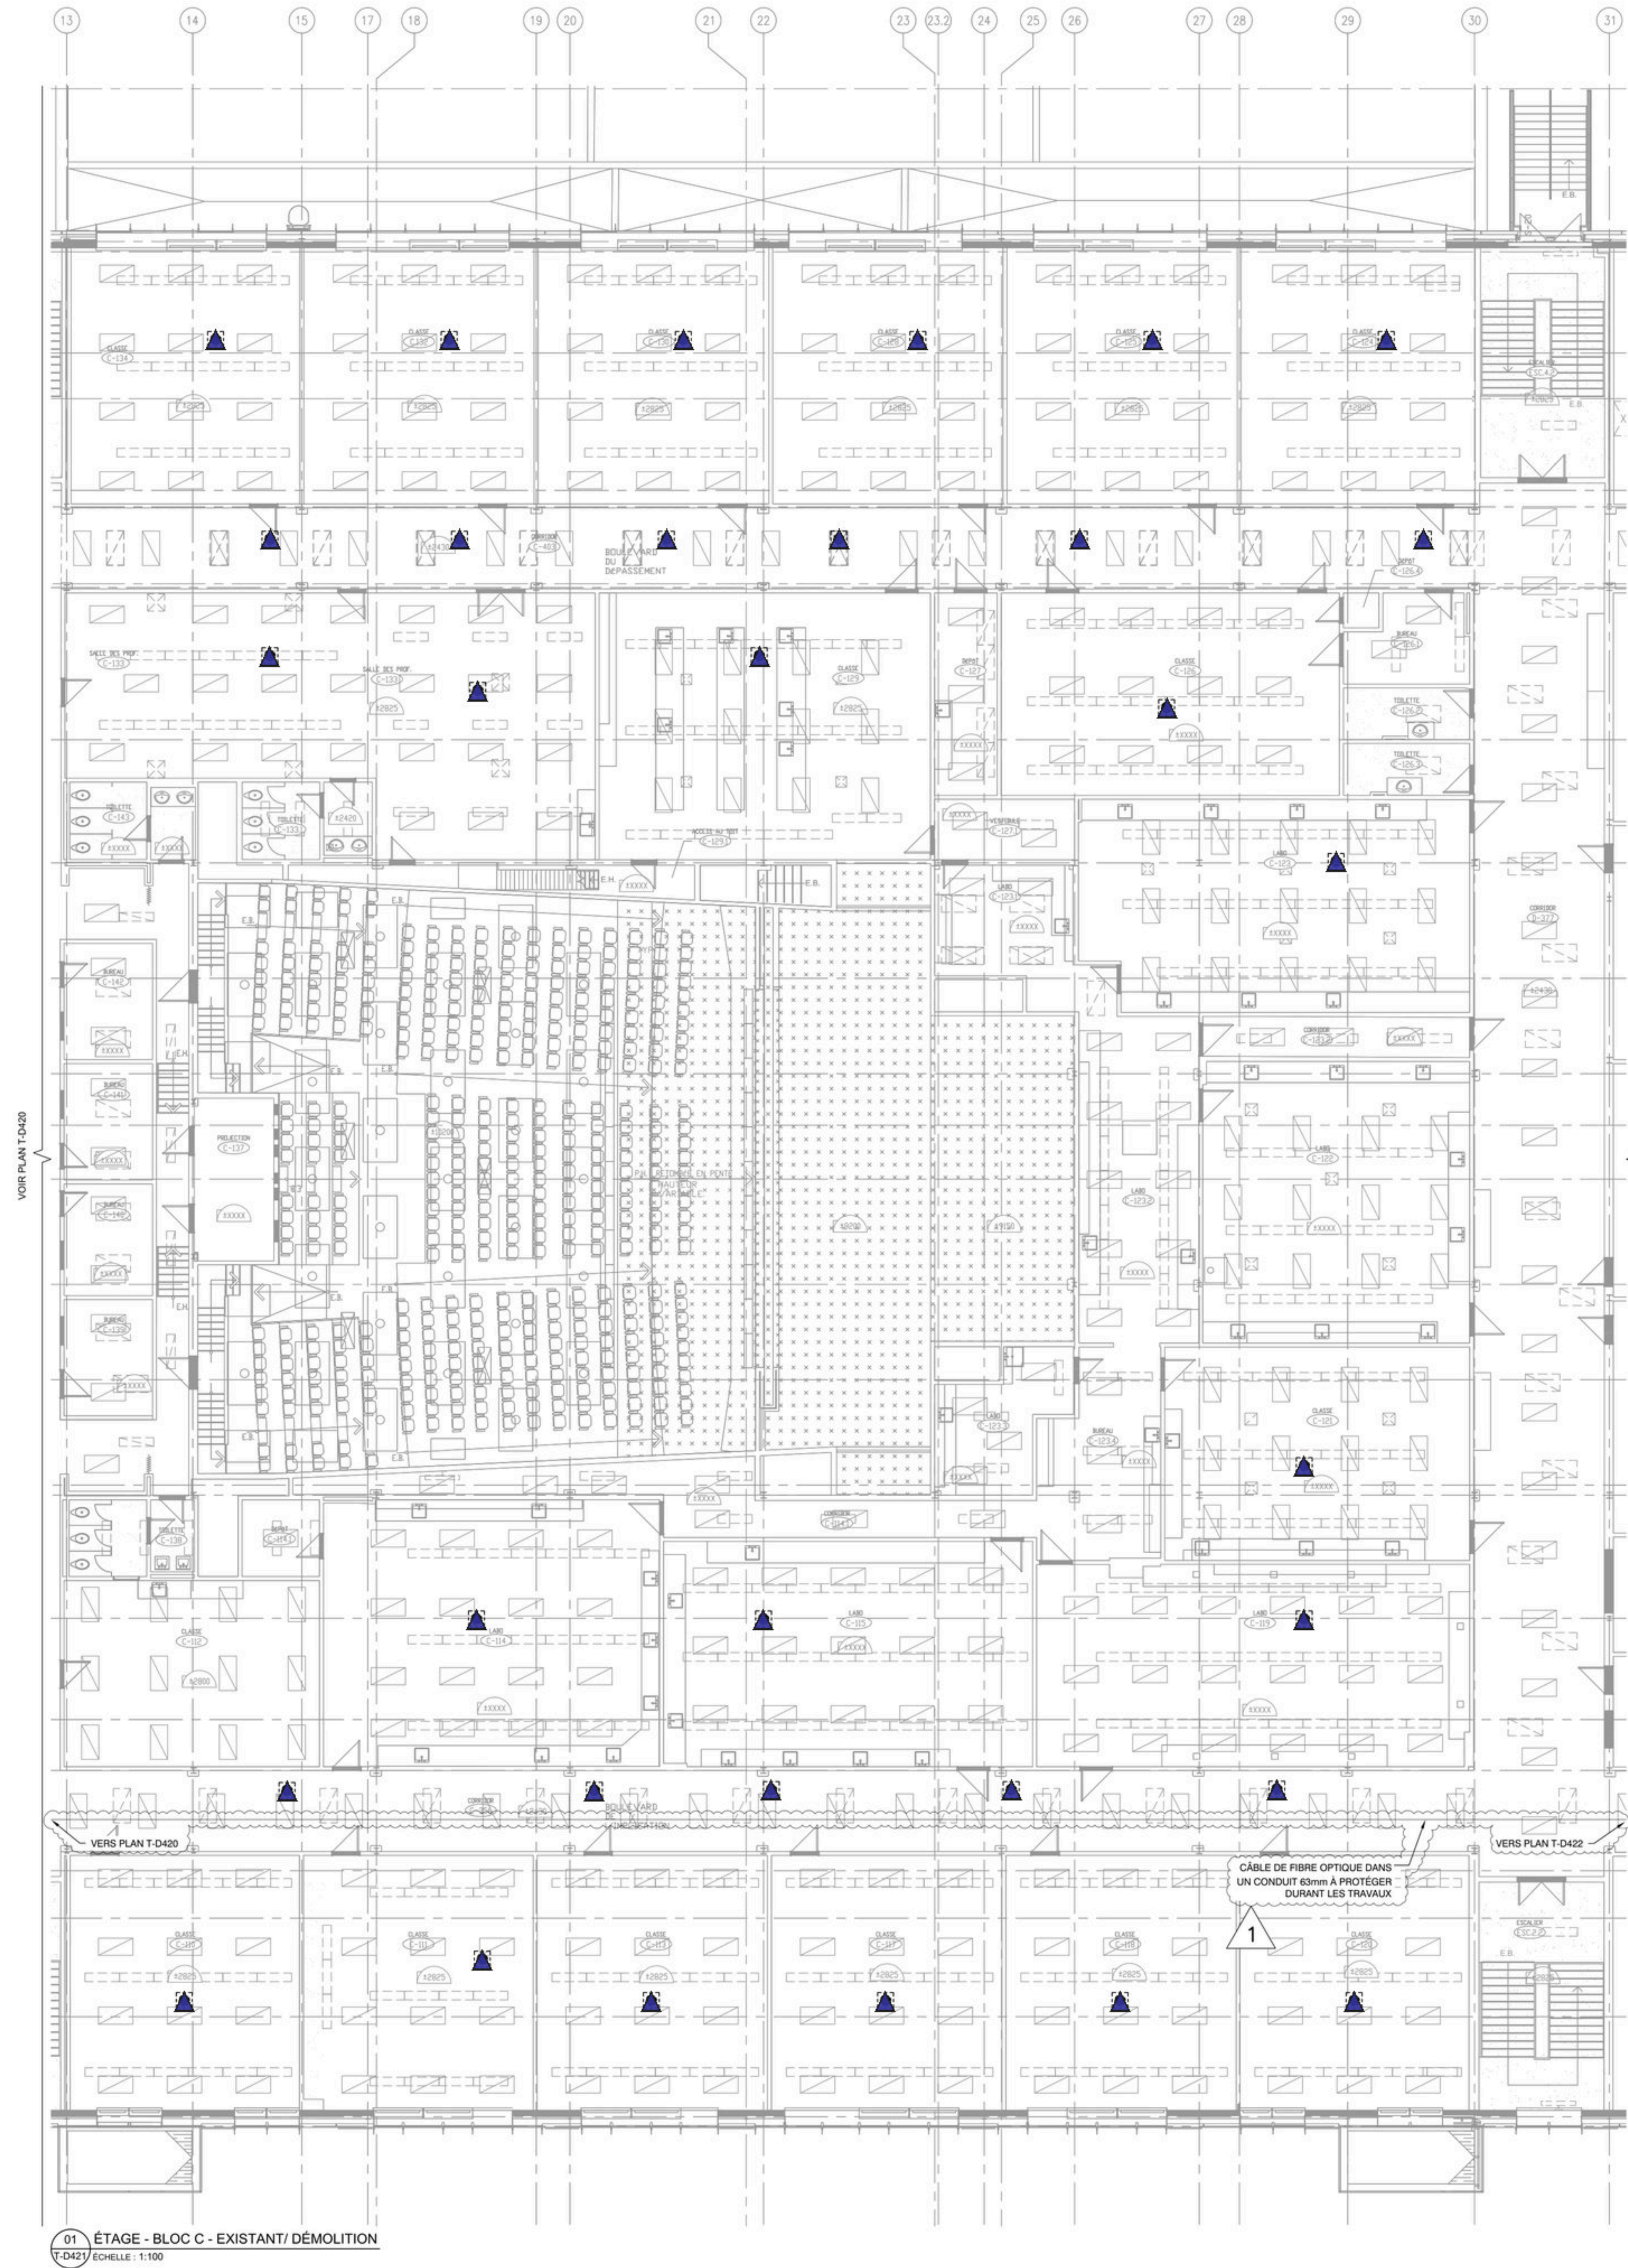

CE DOCUMENT NE DOIT
PAS ÊTRE UTILISÉ À DES
FINS DE CONSTRUCTION

1	2026-08-18	ADDENDA T-01	D.V.
0	2026-07-08	ÉMIS POUR APPEL D'OFFRES	D.V.
No.	Date	Description	Par



CIMA+ 900-360, rue Notre-Dame Ouest
Montréal QC H3C 3X6
CANADA
T 514 337-2462
F 514 291-1632
cima.ca

CENTRE DE SERVICES
SCOLAIRE DE
SOREL-TRACEY

RÉHABILITATION ET TRAVAUX
CONNEXES
ÉCOLE SECONDAIRE BERNARD-GARIÉPY

TÉLÉCOMMUNICATIONS
DÉMOLITION PHASE 1 ÉTAGE
EXISTANT / DÉMOLITION

DISCIPLINE : **TÉLÉCOMMUNICATIONS**

DESSIN PAR : C-A. GRAVEL	ÉCHELLE : INDIQUE
CONQU PAR : A. SY, tech.	DATE : 2026-04-17
VÉRIFIÉ PAR :	VÉRIFIÉ PAR : D. VINCENT, ing.
PROJET No : P0002920	DESSIN No : T-D421
FEUILLE No : 10 25 11	



BO BERNARD GARIEPY

BO DES ÉTUDIANTES

BO DES ERABLES

ZONE DES TRAVAUX

leclerc
architectes
380, rue St-Jacques #1610, Mtl H2Y 1P9 info@leclerc-architectes.com T 514 282 3070

Légende — D422_ADD (9 marques)

CE DOCUMENT NE DOIT
PAS ÊTRE UTILISÉ À DES
FINS DE CONSTRUCTION

1	2026-08-18	ADDENDA T-01	D.V.
0	2026-07-08	EMIS POUR APPEL D'OFFRES	D.V.
No.	Date	Description	Par



CIMA+ 900-760, rue Notre-Dame Ouest
Montréal QC H3C 3K6
CANADA
T 514 337-2462
F 514 291-1632
cima.ca

CENTRE DE SERVICES
SCOLAIRE DE
SOREL-TRACEY

RÉHABILITATION ET TRAVAUX
CONNEXES
ÉCOLE SECONDAIRE BERNARD-GARIÉPY

TÉLÉCOMMUNICATIONS
DÉMOLITION PHASE 1 ÉTAGE
EXISTANT / DÉMOLITION

DISCIPLINE :		TÉLÉCOMMUNICATIONS	
DESSINÉ PAR : C.-A. GRAVEL		RÉVISÉ : INDIQUÉ	
CONCERNÉ PAR : A. SY, tech.		DATE : 2028-04-17	
VÉRIFIÉ PAR :		GÉNÉRIE PAR : D. VINCENT, ing.	
PROJET No : P0002920		DESSIN No : T-D422	
REVUE No : 11 DE 11			