NOTE GÉNÉRALE:

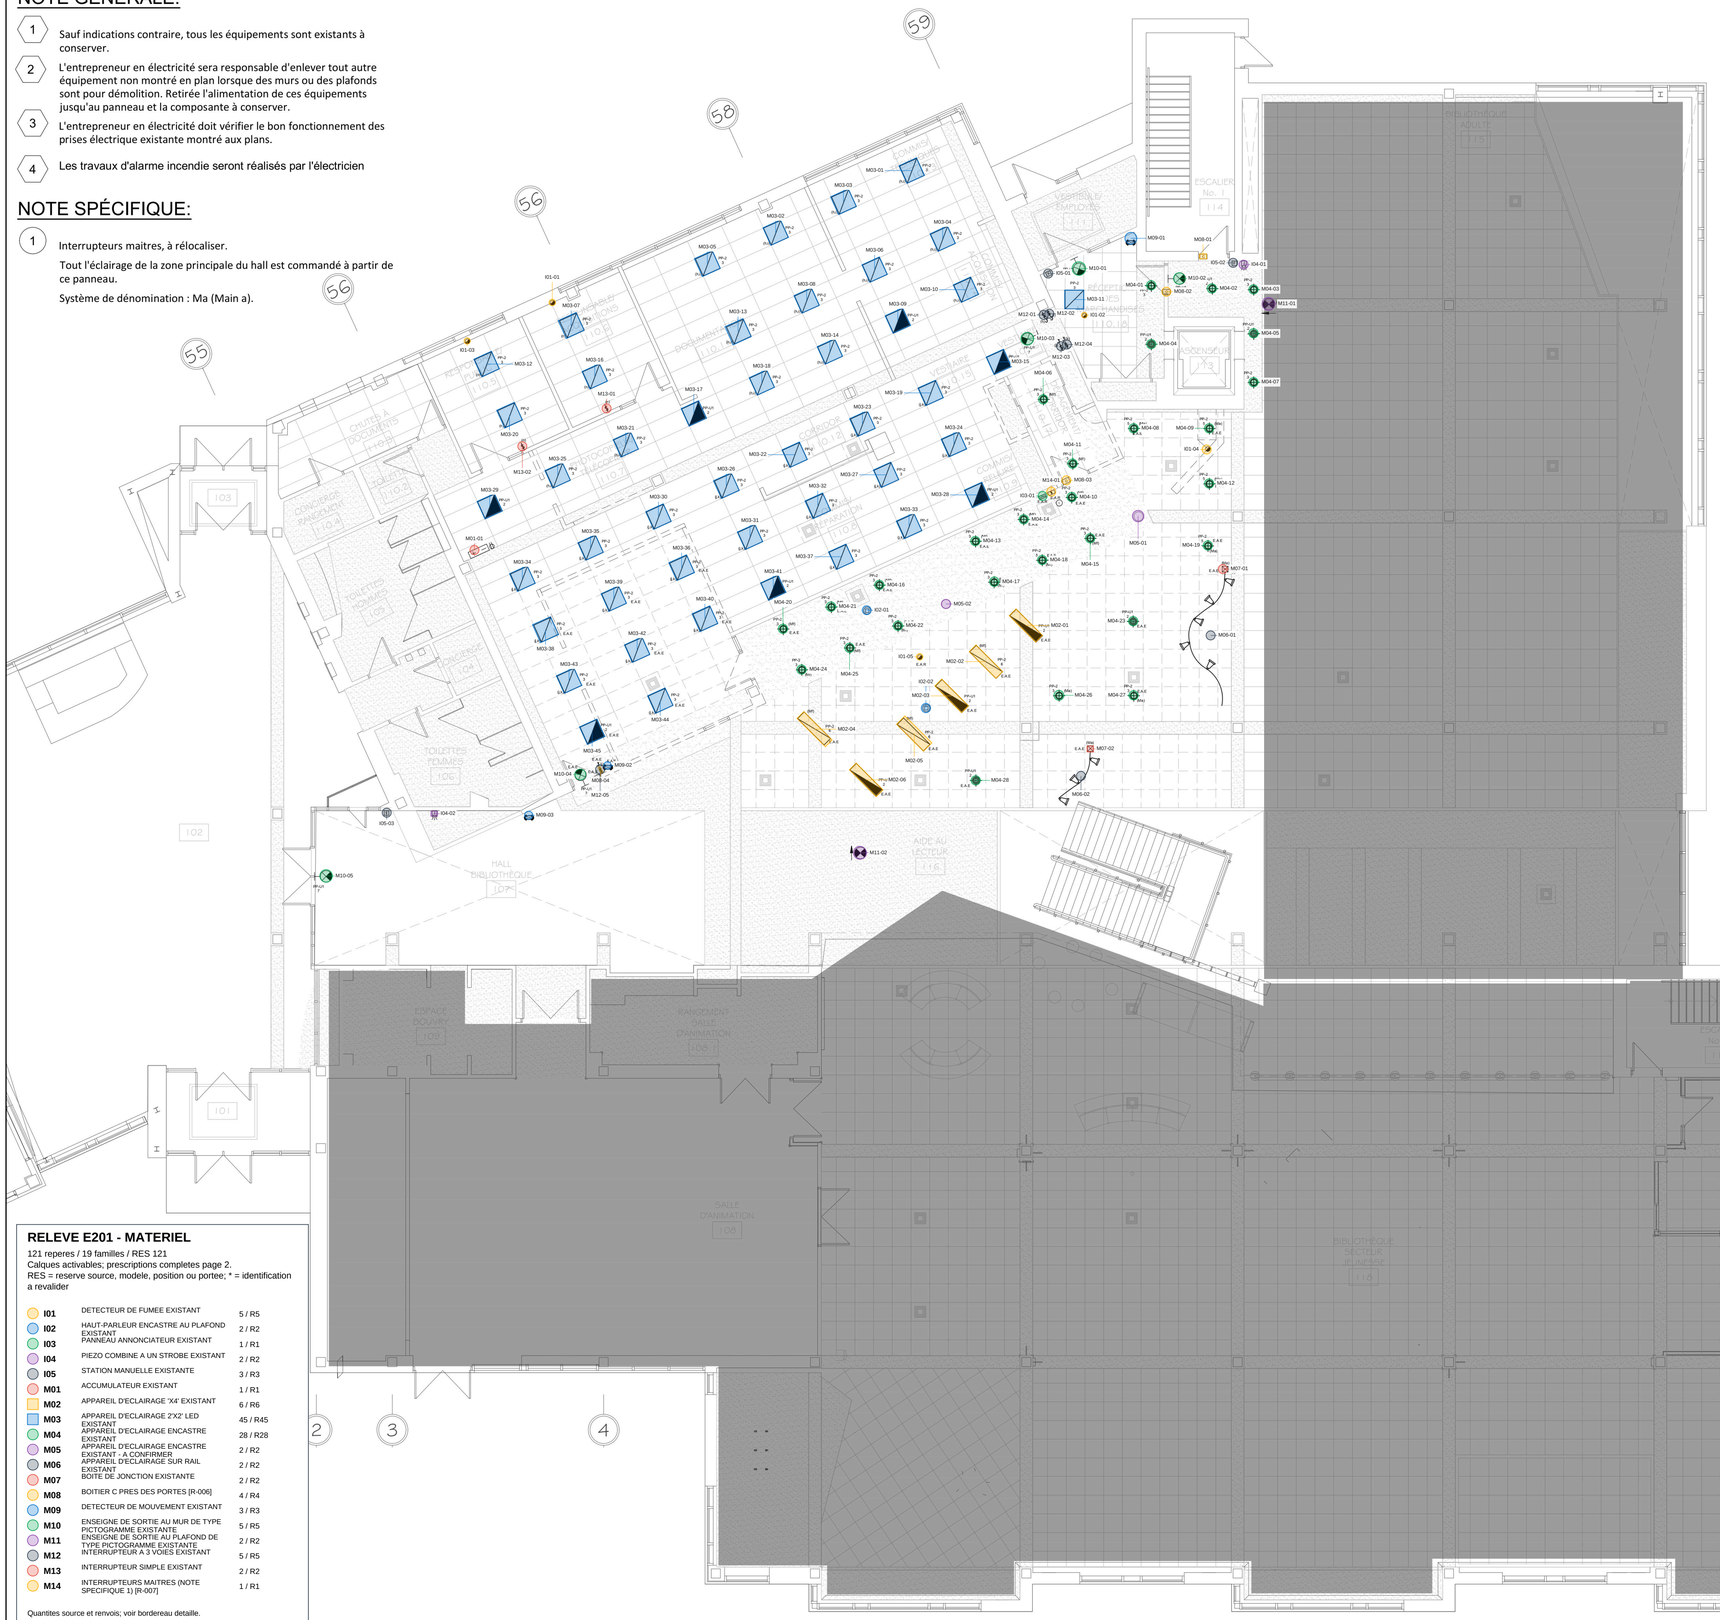
1. Sauf indications contraire, tous les équipements sont existants à conserver.
2. L'entrepreneur en électricité sera responsable d'enlever tout autre équipement non montré en plan lorsque des murs ou des plafonds sont pour démolition. Retirée l'alimentation de ces équipements jusqu'au panneau et la composante à conserver.
3. L'entrepreneur en électricité doit vérifier le bon fonctionnement des prises électrique existante montré aux plans.
4. Les travaux d'alarme incendie seront réalisés par l'électricien

NOTE SPÉCIFIQUE:

1. Interrupteurs maitres, à rélocaliser.

   Tout l'éclairage de la zone principale du hall est commandé à partir de ce panneau.

   Système de dénomination : Ma (Main a).


0"
6"
12"
55
56
58
59
I02
I03
I04
I05
I06
I07
I08
I09
I10.1
I10.2
I10.3
I10.4
I10.5
I10.6
I10.7
I10.8
I10.9
I10.10
I10.11
I10.12
I01
I14
I15
I16
I17
I18
ESCALIER No. 1
ESCALIER No. 2
VESTIBULE EMPLOYÉS
BIBLIOTHÉCAIRE ADULTE
ESPACE DE TRAVAIL
ESPACE DE TRAVAIL EMPLOYÉS
ESPACE DE TRAVAIL BIBLIOTHÉCAIRE
ESPACE DE TRAVAIL BIBLIOTHÉCAIRE JEUNESSE
ESPACE DE TRAVAIL BIBLIOTHÉCAIRE ADULT

BORDEREAU MATERIEL - E201

Quantites representees avec multiplicateurs; portees et composants de chaque ensemble conserves.

Les renvois et composants de panneaux ne constituent pas des ensembles supplementaires a additionner.

Repere / source	Materiel	Designation	Qte	Portee	Modele	Prescription / reserve	Parent
I01-01 E201-014	DETECTEUR DE FUMEE EXISTANT	1/2 NOIR DIAGONAL	1	CONSERVER	EXISTANT CONSERVE - MODELE NON INDIQUE	Cercle coupe en diagonale, moitie noire (A04). 5 au plan ; aucun avertisseur 3/4 noir (A03) - tranche au zoom x20 sur legende et plan (R-004).	
I01-02 E201-022	DETECTEUR DE FUMEE EXISTANT	1/2 NOIR DIAGONAL	1	CONSERVER	EXISTANT CONSERVE - MODELE NON INDIQUE	Cercle coupe en diagonale, moitie noire (A04). 5 au plan ; aucun avertisseur 3/4 noir (A03) - tranche au zoom x20 sur legende et plan (R-004).	
I01-03 E201-028	DETECTEUR DE FUMEE EXISTANT	1/2 NOIR DIAGONAL	1	CONSERVER	EXISTANT CONSERVE - MODELE NON INDIQUE	Cercle coupe en diagonale, moitie noire (A04). 5 au plan ; aucun avertisseur 3/4 noir (A03) - tranche au zoom x20 sur legende et plan (R-004).	
I01-04 E201-052	DETECTEUR DE FUMEE EXISTANT	1/2 NOIR DIAGONAL	1	CONSERVER	EXISTANT CONSERVE - MODELE NON INDIQUE	Cercle coupe en diagonale, moitie noire (A04). 5 au plan ; aucun avertisseur 3/4 noir (A03) - tranche au zoom x20 sur legende et plan (R-004).	
I01-05 E201-097	DETECTEUR DE FUMEE EXISTANT	1/2 NOIR DIAGONAL ; E.A.R	1	RELOCALISER	EXISTANT CONSERVE - MODELE NON INDIQUE	Cercle coupe en diagonale, moitie noire (A04). 5 au plan ; aucun avertisseur 3/4 noir (A03) - tranche au zoom x20 sur legende et plan (R-004).	
I02-01 E201-089	HAUT-PARLEUR ENCASTRE AU PLAFOND EXISTANT	HP	1	CONSERVER	EXISTANT CONSERVE - MODELE NON INDIQUE	Cercle avec carre.	
I02-02 E201-102	HAUT-PARLEUR ENCASTRE AU PLAFOND EXISTANT	HP	1	CONSERVER	EXISTANT CONSERVE - MODELE NON INDIQUE	Cercle avec carre.	
I03-01 E201-058	PANNEAU ANNONCIATEUR EXISTANT	ANN ; E.A.R	1	RELOCALISER	EXISTANT CONSERVE - MODELE NON INDIQUE	ANN dans carre ; E.A.R.	
I04-01 E201-013	PIEZO COMBINE A UN STROBE EXISTANT	PZ	1	CONSERVER	EXISTANT CONSERVE - MODELE NON INDIQUE	F dans carre avec rayons.	
I04-02 E201-118	PIEZO COMBINE A UN STROBE EXISTANT	PZ	1	CONSERVER	EXISTANT CONSERVE - MODELE NON INDIQUE	F dans carre avec rayons.	
I05-01 E201-008	STATION MANUELLE EXISTANTE	SM	1	CONSERVER	EXISTANT CONSERVE - MODELE NON INDIQUE	F dans carre.	
I05-02 E201-012	STATION MANUELLE EXISTANTE	SM	1	CONSERVER	EXISTANT CONSERVE - MODELE NON INDIQUE	F dans carre.	
I05-03 E201-117	STATION MANUELLE EXISTANTE	SM	1	CONSERVER	EXISTANT CONSERVE - MODELE NON INDIQUE	F dans carre.	
M01-01 E201-073	ACCUMULATEUR EXISTANT	+ - AVEC CERCLE ; SANS ETIQUETTE	1	CONSERVER	EXISTANT CONSERVE - MODELE NON INDIQUE	Rectangle + - (R-009).	
M02-01 E201-092	APPAREIL D'ECLAIRAGE 'X4' EXISTANT	PP-U1 2 - MI-NOIR (URGENCE)	1	ENLEVER	EXISTANT CONSERVE - MODELE NON INDIQUE	Rectangle a diagonale ; variante mi-noire = PP-U1 (urgence) en designation.	
M02-02 E201-098	APPAREIL D'ECLAIRAGE 'X4' EXISTANT	PP-2 6 (MF)	1	ENLEVER	EXISTANT CONSERVE - MODELE NON INDIQUE	Rectangle a diagonale ; variante mi-noire = PP-U1 (urgence) en designation.	
M02-03 E201-103	APPAREIL D'ECLAIRAGE 'X4' EXISTANT	PP-U1 2 - MI-NOIR (URGENCE)	1	ENLEVER	EXISTANT CONSERVE - MODELE NON INDIQUE	Rectangle a diagonale ; variante mi-noire = PP-U1 (urgence) en designation.	
M02-04 E201-107	APPAREIL D'ECLAIRAGE 'X4' EXISTANT	PP-2 6 (MF)	1	ENLEVER	EXISTANT CONSERVE - MODELE NON INDIQUE	Rectangle a diagonale ; variante mi-noire = PP-U1 (urgence) en designation.	
M02-05 E201-108	APPAREIL D'ECLAIRAGE 'X4' EXISTANT	PP-2 6 (MF)	1	ENLEVER	EXISTANT CONSERVE - MODELE NON INDIQUE	Rectangle a diagonale ; variante mi-noire = PP-U1 (urgence) en designation.	
M02-06 E201-114	APPAREIL D'ECLAIRAGE 'X4' EXISTANT	PP-U1 2 - MI-NOIR (URGENCE)	1	ENLEVER	EXISTANT CONSERVE - MODELE NON INDIQUE	Rectangle a diagonale ; variante mi-noire = PP-U1 (urgence) en designation.	

BORDEREAU MATERIEL - E201

Quantites representees avec multiplicateurs; portees et composants de chaque ensemble conserves.

Les renvois et composants de panneaux ne constituent pas des ensembles supplementaires a additionner.

Repere / source	Materiel	Designation	Qte	Portee	Modele	Prescription / reserve	Parent
M03-01 E201-001	APPAREIL D'ECLAIRAGE 2'X2' LED EXISTANT	PP-2 3 (H,I)	1	CONSERVER	EXISTANT CONSERVE - MODELE NON INDIQUE	Carre a diagonale. Variante mi-noire = alimente par PP-U1 (urgence) : en designation.	
M03-02 E201-002	APPAREIL D'ECLAIRAGE 2'X2' LED EXISTANT	PP-2 3 (H,I)	1	CONSERVER	EXISTANT CONSERVE - MODELE NON INDIQUE	Carre a diagonale. Variante mi-noire = alimente par PP-U1 (urgence) : en designation.	
M03-03 E201-003	APPAREIL D'ECLAIRAGE 2'X2' LED EXISTANT	PP-2 3 (H,I)	1	CONSERVER	EXISTANT CONSERVE - MODELE NON INDIQUE	Carre a diagonale. Variante mi-noire = alimente par PP-U1 (urgence) : en designation.	
M03-04 E201-004	APPAREIL D'ECLAIRAGE 2'X2' LED EXISTANT	PP-2 3 (H,I)	1	CONSERVER	EXISTANT CONSERVE - MODELE NON INDIQUE	Carre a diagonale. Variante mi-noire = alimente par PP-U1 (urgence) : en designation.	
M03-05 E201-006	APPAREIL D'ECLAIRAGE 2'X2' LED EXISTANT	PP-2 3 (H,I)	1	CONSERVER	EXISTANT CONSERVE - MODELE NON INDIQUE	Carre a diagonale. Variante mi-noire = alimente par PP-U1 (urgence) : en designation.	
M03-06 E201-007	APPAREIL D'ECLAIRAGE 2'X2' LED EXISTANT	PP-2 3 (H,I)	1	CONSERVER	EXISTANT CONSERVE - MODELE NON INDIQUE	Carre a diagonale. Variante mi-noire = alimente par PP-U1 (urgence) : en designation.	
M03-07 E201-015	APPAREIL D'ECLAIRAGE 2'X2' LED EXISTANT	PP-2 3 (N)	1	CONSERVER	EXISTANT CONSERVE - MODELE NON INDIQUE	Carre a diagonale. Variante mi-noire = alimente par PP-U1 (urgence) : en designation.	
M03-08 E201-016	APPAREIL D'ECLAIRAGE 2'X2' LED EXISTANT	PP-2 3 (H,I)	1	CONSERVER	EXISTANT CONSERVE - MODELE NON INDIQUE	Carre a diagonale. Variante mi-noire = alimente par PP-U1 (urgence) : en designation.	
M03-09 E201-017	APPAREIL D'ECLAIRAGE 2'X2' LED EXISTANT	PP-U1 2 - SYMBOLE MI-NOIR (URGENCE)	1	CONSERVER	EXISTANT CONSERVE - MODELE NON INDIQUE	Carre a diagonale. Variante mi-noire = alimente par PP-U1 (urgence) : en designation.	
M03-10 E201-018	APPAREIL D'ECLAIRAGE 2'X2' LED EXISTANT	PP-2 3 (H,I)	1	CONSERVER	EXISTANT CONSERVE - MODELE NON INDIQUE	Carre a diagonale. Variante mi-noire = alimente par PP-U1 (urgence) : en designation.	
M03-11 E201-021	APPAREIL D'ECLAIRAGE 2'X2' LED EXISTANT	PP-2 3	1	CONSERVER	EXISTANT CONSERVE - MODELE NON INDIQUE	Carre a diagonale. Variante mi-noire = alimente par PP-U1 (urgence) : en designation.	
M03-12 E201-029	APPAREIL D'ECLAIRAGE 2'X2' LED EXISTANT	PP-2 3 (N)	1	CONSERVER	EXISTANT CONSERVE - MODELE NON INDIQUE	Carre a diagonale. Variante mi-noire = alimente par PP-U1 (urgence) : en designation.	
M03-13 E201-030	APPAREIL D'ECLAIRAGE 2'X2' LED EXISTANT	PP-2 3 (H,I)	1	CONSERVER	EXISTANT CONSERVE - MODELE NON INDIQUE	Carre a diagonale. Variante mi-noire = alimente par PP-U1 (urgence) : en designation.	
M03-14 E201-031	APPAREIL D'ECLAIRAGE 2'X2' LED EXISTANT	PP-2 3 (H,I)	1	CONSERVER	EXISTANT CONSERVE - MODELE NON INDIQUE	Carre a diagonale. Variante mi-noire = alimente par PP-U1 (urgence) : en designation.	
M03-15 E201-032	APPAREIL D'ECLAIRAGE 2'X2' LED EXISTANT	PP-U1 2 - SYMBOLE MI-NOIR (URGENCE)	1	CONSERVER	EXISTANT CONSERVE - MODELE NON INDIQUE	Carre a diagonale. Variante mi-noire = alimente par PP-U1 (urgence) : en designation.	
M03-16 E201-038	APPAREIL D'ECLAIRAGE 2'X2' LED EXISTANT	PP-2 3 (N)	1	CONSERVER	EXISTANT CONSERVE - MODELE NON INDIQUE	Carre a diagonale. Variante mi-noire = alimente par PP-U1 (urgence) : en designation.	
M03-17 E201-040	APPAREIL D'ECLAIRAGE 2'X2' LED EXISTANT	PP-U1 2 - SYMBOLE MI-NOIR (URGENCE)	1	CONSERVER	EXISTANT CONSERVE - MODELE NON INDIQUE	Carre a diagonale. Variante mi-noire = alimente par PP-U1 (urgence) : en designation.	
M03-18 E201-041	APPAREIL D'ECLAIRAGE 2'X2' LED EXISTANT	PP-2 3 (H,I)	1	CONSERVER	EXISTANT CONSERVE - MODELE NON INDIQUE	Carre a diagonale. Variante mi-noire = alimente par PP-U1 (urgence) : en designation.	
M03-19 E201-042	APPAREIL D'ECLAIRAGE 2'X2' LED EXISTANT	PP-2 3 (J,K)	1	CONSERVER	EXISTANT CONSERVE - MODELE NON INDIQUE	Carre a diagonale. Variante mi-noire = alimente par PP-U1 (urgence) : en designation.	
M03-20 E201-045	APPAREIL D'ECLAIRAGE 2'X2' LED EXISTANT	PP-2 3 (N)	1	CONSERVER	EXISTANT CONSERVE - MODELE NON INDIQUE	Carre a diagonale. Variante mi-noire = alimente par PP-U1 (urgence) : en designation.	

BORDEREAU MATERIEL - E201

Quantites representees avec multiplicateurs; portees et composants de chaque ensemble conserves.

Les renvois et composants de panneaux ne constituent pas des ensembles supplementaires a additionner.

Repere / source	Materiel	Designation	Qte	Portee	Modele	Prescription / reserve	Parent
M03-21 E201-047	APPAREIL D'ECLAIRAGE 2'X2' LED EXISTANT	PP-2 3 (H,I)	1	CONSERVER	EXISTANT CONSERVE - MODELE NON INDIQUE	Carre a diagonale. Variante mi-noire = alimente par PP-U1 (urgence) : en designation.	
M03-22 E201-048	APPAREIL D'ECLAIRAGE 2'X2' LED EXISTANT	PP-2 3 (J,K)	1	CONSERVER	EXISTANT CONSERVE - MODELE NON INDIQUE	Carre a diagonale. Variante mi-noire = alimente par PP-U1 (urgence) : en designation.	
M03-23 E201-049	APPAREIL D'ECLAIRAGE 2'X2' LED EXISTANT	PP-2 3 (J,K)	1	CONSERVER	EXISTANT CONSERVE - MODELE NON INDIQUE	Carre a diagonale. Variante mi-noire = alimente par PP-U1 (urgence) : en designation.	
M03-24 E201-050	APPAREIL D'ECLAIRAGE 2'X2' LED EXISTANT	PP-2 3 (J,K)	1	CONSERVER	EXISTANT CONSERVE - MODELE NON INDIQUE	Carre a diagonale. Variante mi-noire = alimente par PP-U1 (urgence) : en designation.	
M03-25 E201-054	APPAREIL D'ECLAIRAGE 2'X2' LED EXISTANT	PP-2 3 (H,I)	1	CONSERVER	EXISTANT CONSERVE - MODELE NON INDIQUE	Carre a diagonale. Variante mi-noire = alimente par PP-U1 (urgence) : en designation.	
M03-26 E201-055	APPAREIL D'ECLAIRAGE 2'X2' LED EXISTANT	PP-2 3 (J,K)	1	CONSERVER	EXISTANT CONSERVE - MODELE NON INDIQUE	Carre a diagonale. Variante mi-noire = alimente par PP-U1 (urgence) : en designation.	
M03-27 E201-056	APPAREIL D'ECLAIRAGE 2'X2' LED EXISTANT	PP-2 3 (J,K)	1	CONSERVER	EXISTANT CONSERVE - MODELE NON INDIQUE	Carre a diagonale. Variante mi-noire = alimente par PP-U1 (urgence) : en designation.	
M03-28 E201-057	APPAREIL D'ECLAIRAGE 2'X2' LED EXISTANT	PP-U1 2 - SYMBOLE MI-NOIR (URGENCE)	1	CONSERVER	EXISTANT CONSERVE - MODELE NON INDIQUE	Carre a diagonale. Variante mi-noire = alimente par PP-U1 (urgence) : en designation.	
M03-29 E201-064	APPAREIL D'ECLAIRAGE 2'X2' LED EXISTANT	PP-U1 2 - SYMBOLE MI-NOIR (URGENCE)	1	CONSERVER	EXISTANT CONSERVE - MODELE NON INDIQUE	Carre a diagonale. Variante mi-noire = alimente par PP-U1 (urgence) : en designation.	
M03-30 E201-065	APPAREIL D'ECLAIRAGE 2'X2' LED EXISTANT	PP-2 3 (J,K)	1	CONSERVER	EXISTANT CONSERVE - MODELE NON INDIQUE	Carre a diagonale. Variante mi-noire = alimente par PP-U1 (urgence) : en designation.	
M03-31 E201-066	APPAREIL D'ECLAIRAGE 2'X2' LED EXISTANT	PP-2 3 (J,K)	1	CONSERVER	EXISTANT CONSERVE - MODELE NON INDIQUE	Carre a diagonale. Variante mi-noire = alimente par PP-U1 (urgence) : en designation.	
M03-32 E201-067	APPAREIL D'ECLAIRAGE 2'X2' LED EXISTANT	PP-2 3 (J,K)	1	CONSERVER	EXISTANT CONSERVE - MODELE NON INDIQUE	Carre a diagonale. Variante mi-noire = alimente par PP-U1 (urgence) : en designation.	
M03-33 E201-068	APPAREIL D'ECLAIRAGE 2'X2' LED EXISTANT	PP-2 3 (J,K)	1	CONSERVER	EXISTANT CONSERVE - MODELE NON INDIQUE	Carre a diagonale. Variante mi-noire = alimente par PP-U1 (urgence) : en designation.	
M03-34 E201-074	APPAREIL D'ECLAIRAGE 2'X2' LED EXISTANT	PP-2 3 (J,K)	1	CONSERVER	EXISTANT CONSERVE - MODELE NON INDIQUE	Carre a diagonale. Variante mi-noire = alimente par PP-U1 (urgence) : en designation.	
M03-35 E201-075	APPAREIL D'ECLAIRAGE 2'X2' LED EXISTANT	PP-2 3 (J,K)	1	CONSERVER	EXISTANT CONSERVE - MODELE NON INDIQUE	Carre a diagonale. Variante mi-noire = alimente par PP-U1 (urgence) : en designation.	
M03-36 E201-076	APPAREIL D'ECLAIRAGE 2'X2' LED EXISTANT	PP-2 3 (J,K)	1	ENLEVER	EXISTANT CONSERVE - MODELE NON INDIQUE	Carre a diagonale. Variante mi-noire = alimente par PP-U1 (urgence) : en designation.	
M03-37 E201-077	APPAREIL D'ECLAIRAGE 2'X2' LED EXISTANT	PP-2 3 (J,K)	1	CONSERVER	EXISTANT CONSERVE - MODELE NON INDIQUE	Carre a diagonale. Variante mi-noire = alimente par PP-U1 (urgence) : en designation.	
M03-38 E201-083	APPAREIL D'ECLAIRAGE 2'X2' LED EXISTANT	PP-2 3 (J,K)	1	ENLEVER	EXISTANT CONSERVE - MODELE NON INDIQUE	Carre a diagonale. Variante mi-noire = alimente par PP-U1 (urgence) : en designation.	
M03-39 E201-084	APPAREIL D'ECLAIRAGE 2'X2' LED EXISTANT	PP-2 3 (J,K)	1	ENLEVER	EXISTANT CONSERVE - MODELE NON INDIQUE	Carre a diagonale. Variante mi-noire = alimente par PP-U1 (urgence) : en designation.	
M03-40 E201-085	APPAREIL D'ECLAIRAGE 2'X2' LED EXISTANT	PP-2 3 (J,K)	1	ENLEVER	EXISTANT CONSERVE - MODELE NON INDIQUE	Carre a diagonale. Variante mi-noire = alimente par PP-U1 (urgence) : en designation.	

BORDEREAU MATERIEL - E201

Quantites representees avec multiplicateurs; portees et composants de chaque ensemble conserves.

Les renvois et composants de panneaux ne constituent pas des ensembles supplementaires a additionner.

Repere / source	Materiel	Designation	Qte	Portee	Modele	Prescription / reserve	Parent
M03-41 E201-086	APPAREIL D'ECLAIRAGE 2'X2' LED EXISTANT	PP-U1 2 - SYMBOLE MI-NOIR (URGENCE)	1	CONSERVER	EXISTANT CONSERVE - MODELE NON INDIQUE	Carre a diagonale. Variante mi-noire = alimente par PP-U1 (urgence) : en designation.	
M03-42 E201-094	APPAREIL D'ECLAIRAGE 2'X2' LED EXISTANT	PP-2 3 (J,K)	1	ENLEVER	EXISTANT CONSERVE - MODELE NON INDIQUE	Carre a diagonale. Variante mi-noire = alimente par PP-U1 (urgence) : en designation.	
M03-43 E201-100	APPAREIL D'ECLAIRAGE 2'X2' LED EXISTANT	PP-2 3 (J,K)	1	ENLEVER	EXISTANT CONSERVE - MODELE NON INDIQUE	Carre a diagonale. Variante mi-noire = alimente par PP-U1 (urgence) : en designation.	
M03-44 E201-101	APPAREIL D'ECLAIRAGE 2'X2' LED EXISTANT	PP-2 3 (J,K)	1	ENLEVER	EXISTANT CONSERVE - MODELE NON INDIQUE	Carre a diagonale. Variante mi-noire = alimente par PP-U1 (urgence) : en designation.	
M03-45 E201-106	APPAREIL D'ECLAIRAGE 2'X2' LED EXISTANT	PP-U1 2 - SYMBOLE MI-NOIR (URGENCE)	1	ENLEVER	EXISTANT CONSERVE - MODELE NON INDIQUE	Carre a diagonale. Variante mi-noire = alimente par PP-U1 (urgence) : en designation.	
M04-01 E201-023	APPAREIL D'ECLAIRAGE ENCASTRE EXISTANT	PP-2 3	1	CONSERVER	EXISTANT CONSERVE - MODELE NON INDIQUE	Cercle + croix. Variante pleine = PP-U1 (urgence) : en designation.	
M04-02 E201-025	APPAREIL D'ECLAIRAGE ENCASTRE EXISTANT	PP-U1 2	1	CONSERVER	EXISTANT CONSERVE - MODELE NON INDIQUE	Cercle + croix. Variante pleine = PP-U1 (urgence) : en designation.	
M04-03 E201-026	APPAREIL D'ECLAIRAGE ENCASTRE EXISTANT	PP-2 3	1	CONSERVER	EXISTANT CONSERVE - MODELE NON INDIQUE	Cercle + croix. Variante pleine = PP-U1 (urgence) : en designation.	
M04-04 E201-036	APPAREIL D'ECLAIRAGE ENCASTRE EXISTANT	PP-U1 2 - SYMBOLE PLEIN (URGENCE)	1	CONSERVER	EXISTANT CONSERVE - MODELE NON INDIQUE	Cercle + croix. Variante pleine = PP-U1 (urgence) : en designation.	
M04-05 E201-037	APPAREIL D'ECLAIRAGE ENCASTRE EXISTANT	PP-U1 2 - SYMBOLE PLEIN (URGENCE)	1	CONSERVER	EXISTANT CONSERVE - MODELE NON INDIQUE	Cercle + croix. Variante pleine = PP-U1 (urgence) : en designation.	
M04-06 E201-043	APPAREIL D'ECLAIRAGE ENCASTRE EXISTANT	PP-2 3 (MF)	1	CONSERVER	EXISTANT CONSERVE - MODELE NON INDIQUE	Cercle + croix. Variante pleine = PP-U1 (urgence) : en designation.	
M04-07 E201-044	APPAREIL D'ECLAIRAGE ENCASTRE EXISTANT	PP-2 3	1	CONSERVER	EXISTANT CONSERVE - MODELE NON INDIQUE	Cercle + croix. Variante pleine = PP-U1 (urgence) : en designation.	
M04-08 E201-051	APPAREIL D'ECLAIRAGE ENCASTRE EXISTANT	PP-2 5 (MA)	1	ENLEVER	EXISTANT CONSERVE - MODELE NON INDIQUE	Cercle + croix. Variante pleine = PP-U1 (urgence) : en designation.	
M04-09 E201-053	APPAREIL D'ECLAIRAGE ENCASTRE EXISTANT	PP-2 5 (MA)	1	ENLEVER	EXISTANT CONSERVE - MODELE NON INDIQUE	Cercle + croix. Variante pleine = PP-U1 (urgence) : en designation.	
M04-10 E201-061	APPAREIL D'ECLAIRAGE ENCASTRE EXISTANT	PP-2 3 (MF)	1	ENLEVER	EXISTANT CONSERVE - MODELE NON INDIQUE	Cercle + croix. Variante pleine = PP-U1 (urgence) : en designation.	
M04-11 E201-062	APPAREIL D'ECLAIRAGE ENCASTRE EXISTANT	PP-2 3 (MF)	1	CONSERVER	EXISTANT CONSERVE - MODELE NON INDIQUE	Cercle + croix. Variante pleine = PP-U1 (urgence) : en designation.	
M04-12 E201-063	APPAREIL D'ECLAIRAGE ENCASTRE EXISTANT	PP-2 5 (MA)	1	ENLEVER	EXISTANT CONSERVE - MODELE NON INDIQUE	Cercle + croix. Variante pleine = PP-U1 (urgence) : en designation.	
M04-13 E201-069	APPAREIL D'ECLAIRAGE ENCASTRE EXISTANT	PP-2 3 (MF)	1	ENLEVER	EXISTANT CONSERVE - MODELE NON INDIQUE	Cercle + croix. Variante pleine = PP-U1 (urgence) : en designation.	
M04-14 E201-070	APPAREIL D'ECLAIRAGE ENCASTRE EXISTANT	PP-2 3 (MF)	1	ENLEVER	EXISTANT CONSERVE - MODELE NON INDIQUE	Cercle + croix. Variante pleine = PP-U1 (urgence) : en designation.	
M04-15 E201-071	APPAREIL D'ECLAIRAGE ENCASTRE EXISTANT	PP-2 3 (MF)	1	ENLEVER	EXISTANT CONSERVE - MODELE NON INDIQUE	Cercle + croix. Variante pleine = PP-U1 (urgence) : en designation.	

BORDEREAU MATERIEL - E201

Quantites representees avec multiplicateurs; portees et composants de chaque ensemble conserves.

Les renvois et composants de panneaux ne constituent pas des ensembles supplementaires a additionner.

Repere / source	Materiel	Designation	Qte	Portee	Modele	Prescription / reserve	Parent
M04-16 E201-078	APPAREIL D'ECLAIRAGE ENCASTRE EXISTANT	PP-2 3 (MF)	1	ENLEVER	EXISTANT CONSERVE - MODELE NON INDIQUE	Cercle + croix. Variante pleine = PP-U1 (urgence) : en designation.	
M04-17 E201-079	APPAREIL D'ECLAIRAGE ENCASTRE EXISTANT	PP-2 3 (MF)	1	ENLEVER	EXISTANT CONSERVE - MODELE NON INDIQUE	Cercle + croix. Variante pleine = PP-U1 (urgence) : en designation.	
M04-18 E201-080	APPAREIL D'ECLAIRAGE ENCASTRE EXISTANT	PP-2 3 (MF)	1	ENLEVER	EXISTANT CONSERVE - MODELE NON INDIQUE	Cercle + croix. Variante pleine = PP-U1 (urgence) : en designation.	
M04-19 E201-081	APPAREIL D'ECLAIRAGE ENCASTRE EXISTANT	PP-2 5 (MA)	1	ENLEVER	EXISTANT CONSERVE - MODELE NON INDIQUE	Cercle + croix. Variante pleine = PP-U1 (urgence) : en designation.	
M04-20 E201-087	APPAREIL D'ECLAIRAGE ENCASTRE EXISTANT	PP-2 3 (MF)	1	ENLEVER	EXISTANT CONSERVE - MODELE NON INDIQUE	Cercle + croix. Variante pleine = PP-U1 (urgence) : en designation.	
M04-21 E201-088	APPAREIL D'ECLAIRAGE ENCASTRE EXISTANT	PP-2 3 (MF)	1	ENLEVER	EXISTANT CONSERVE - MODELE NON INDIQUE	Cercle + croix. Variante pleine = PP-U1 (urgence) : en designation.	
M04-22 E201-090	APPAREIL D'ECLAIRAGE ENCASTRE EXISTANT	PP-2 3 (MF)	1	ENLEVER	EXISTANT CONSERVE - MODELE NON INDIQUE	Cercle + croix. Variante pleine = PP-U1 (urgence) : en designation.	
M04-23 E201-093	APPAREIL D'ECLAIRAGE ENCASTRE EXISTANT	PP-U1 2 - SYMBOLE PLEIN (URGENCE)	1	ENLEVER	EXISTANT CONSERVE - MODELE NON INDIQUE	Cercle + croix. Variante pleine = PP-U1 (urgence) : en designation.	
M04-24 E201-095	APPAREIL D'ECLAIRAGE ENCASTRE EXISTANT	PP-2 3 (MF)	1	ENLEVER	EXISTANT CONSERVE - MODELE NON INDIQUE	Cercle + croix. Variante pleine = PP-U1 (urgence) : en designation.	
M04-25 E201-096	APPAREIL D'ECLAIRAGE ENCASTRE EXISTANT	PP-2 3 (MF)	1	ENLEVER	EXISTANT CONSERVE - MODELE NON INDIQUE	Cercle + croix. Variante pleine = PP-U1 (urgence) : en designation.	
M04-26 E201-104	APPAREIL D'ECLAIRAGE ENCASTRE EXISTANT	PP-2 3 (MA)	1	CONSERVER	EXISTANT CONSERVE - MODELE NON INDIQUE	Cercle + croix. Variante pleine = PP-U1 (urgence) : en designation.	
M04-27 E201-105	APPAREIL D'ECLAIRAGE ENCASTRE EXISTANT	PP-2 3 (MA)	1	ENLEVER	EXISTANT CONSERVE - MODELE NON INDIQUE	Cercle + croix. Variante pleine = PP-U1 (urgence) : en designation.	
M04-28 E201-115	APPAREIL D'ECLAIRAGE ENCASTRE EXISTANT	PP-U1 2 - SYMBOLE PLEIN (URGENCE)	1	ENLEVER	EXISTANT CONSERVE - MODELE NON INDIQUE	Cercle + croix. Variante pleine = PP-U1 (urgence) : en designation.	
M05-01 E201-072	APPAREIL D'ECLAIRAGE ENCASTRE EXISTANT - A CONFIRMER	EC	1	A PRECISER	EXISTANT CONSERVE - MODELE NON INDIQUE	Cercle simple ~8 pt sans etiquette ni circuit (R-005).	
M05-02 E201-091	APPAREIL D'ECLAIRAGE ENCASTRE EXISTANT - A CONFIRMER	EC	1	A PRECISER	EXISTANT CONSERVE - MODELE NON INDIQUE	Cercle simple ~8 pt sans etiquette ni circuit (R-005).	
M06-01 E201-099	APPAREIL D'ECLAIRAGE SUR RAIL EXISTANT	P-2 39 (MA) ; 5 TETES ; ~125 PT DE LONG	1	ENLEVER	EXISTANT CONSERVE - MODELE NON INDIQUE	Rail courbe avec tetes orientables ; 1 repere par rail, nb de tetes en designation (R-008).	
M06-02 E201-116	APPAREIL D'ECLAIRAGE SUR RAIL EXISTANT	P-2 41 (MA) ; 3 TETES ; ~55 PT DE LONG	1	ENLEVER	EXISTANT CONSERVE - MODELE NON INDIQUE	Rail courbe avec tetes orientables ; 1 repere par rail, nb de tetes en designation (R-008).	
M07-01 E201-082	BOITE DE JONCTION EXISTANTE	P-2 39 (MA)	1	ENLEVER	EXISTANT CONSERVE - MODELE NON INDIQUE	Carre X en tete de rail.	
M07-02 E201-109	BOITE DE JONCTION EXISTANTE	P-2 41 (MA)	1	ENLEVER	EXISTANT CONSERVE - MODELE NON INDIQUE	Carre X en tete de rail.	
M08-01 E201-011	BOITIER C PRES DES PORTES (HORS LEGENDE - R-006)	BC	1	CONSERVER	EXISTANT CONSERVE - MODELE NON INDIQUE	C dans carre, hors legende.	

BORDEREAU MATERIEL - E201

Quantites representees avec multiplicateurs; portees et composants de chaque ensemble conserves.

Les renvois et composants de panneaux ne constituent pas des ensembles supplementaires a additionner.

Repere / source	Materiel	Designation	Qte	Portee	Modele	Prescription / reserve	Parent
M08-02 E201-024	BOITIER C PRES DES PORTES (HORS LEGENDE - R-006)	BC	1	CONSERVER	EXISTANT CONSERVE - MODELE NON INDIQUE	C dans carre, hors legende.	
M08-03 E201-060	BOITIER C PRES DES PORTES (HORS LEGENDE - R-006)	BC	1	CONSERVER	EXISTANT CONSERVE - MODELE NON INDIQUE	C dans carre, hors legende.	
M08-04 E201-112	BOITIER C PRES DES PORTES (HORS LEGENDE - R-006)	E.A.E	1	ENLEVER	EXISTANT CONSERVE - MODELE NON INDIQUE	C dans carre, hors legende.	
M09-01 E201-005	DETECTEUR DE MOUVEMENT EXISTANT	DM	1	CONSERVER	EXISTANT CONSERVE - MODELE NON INDIQUE	Ovale DM.	
M09-02 E201-113	DETECTEUR DE MOUVEMENT EXISTANT	E.A.E	1	ENLEVER	EXISTANT CONSERVE - MODELE NON INDIQUE	Ovale DM.	
M09-03 E201-119	DETECTEUR DE MOUVEMENT EXISTANT	DM	1	CONSERVER	EXISTANT CONSERVE - MODELE NON INDIQUE	Ovale DM.	
M10-01 E201-009	ENSEIGNE DE SORTIE AU MUR DE TYPE PICTOGRAMME EXISTANTE	PP-U1 7	1	CONSERVER	EXISTANT CONSERVE - MODELE NON INDIQUE	Cercle X mi-noir sur tige.	
M10-02 E201-010	ENSEIGNE DE SORTIE AU MUR DE TYPE PICTOGRAMME EXISTANTE	PP-U1 7	1	CONSERVER	EXISTANT CONSERVE - MODELE NON INDIQUE	Cercle X mi-noir sur tige.	
M10-03 E201-033	ENSEIGNE DE SORTIE AU MUR DE TYPE PICTOGRAMME EXISTANTE	PP-U1 7	1	CONSERVER	EXISTANT CONSERVE - MODELE NON INDIQUE	Cercle X mi-noir sur tige.	
M10-04 E201-110	ENSEIGNE DE SORTIE AU MUR DE TYPE PICTOGRAMME EXISTANTE	PP-U1 7	1	ENLEVER	EXISTANT CONSERVE - MODELE NON INDIQUE	Cercle X mi-noir sur tige.	
M10-05 E201-120	ENSEIGNE DE SORTIE AU MUR DE TYPE PICTOGRAMME EXISTANTE	PP-U1 7	1	CONSERVER	EXISTANT CONSERVE - MODELE NON INDIQUE	Cercle X mi-noir sur tige.	
M11-01 E201-027	ENSEIGNE DE SORTIE AU PLAFOND DE TYPE PICTOGRAMME EXISTANTE	PP-U1 7 ; FLECHE VERS LA GAUCHE	1	CONSERVER	EXISTANT CONSERVE - MODELE NON INDIQUE	Cercle X mi-noir avec fleche, sans tige.	
M11-02 E201-121	ENSEIGNE DE SORTIE AU PLAFOND DE TYPE PICTOGRAMME EXISTANTE	FLECHE VERS LE HAUT ; SANS ETIQUETTE LISIBLE	1	CONSERVER	EXISTANT CONSERVE - MODELE NON INDIQUE	Cercle X mi-noir avec fleche, sans tige.	
M12-01 E201-019	INTERRUPTEUR A 3 VOIES EXISTANT	(H)	1	CONSERVER	EXISTANT CONSERVE - MODELE NON INDIQUE	$ avec 3 ; lettre de zone en designation.	
M12-02 E201-020	INTERRUPTEUR A 3 VOIES EXISTANT	(I)	1	CONSERVER	EXISTANT CONSERVE - MODELE NON INDIQUE	$ avec 3 ; lettre de zone en designation.	
M12-03 E201-034	INTERRUPTEUR A 3 VOIES EXISTANT	(J)	1	CONSERVER	EXISTANT CONSERVE - MODELE NON INDIQUE	$ avec 3 ; lettre de zone en designation.	
M12-04 E201-035	INTERRUPTEUR A 3 VOIES EXISTANT	(K)	1	CONSERVER	EXISTANT CONSERVE - MODELE NON INDIQUE	$ avec 3 ; lettre de zone en designation.	
M12-05 E201-111	INTERRUPTEUR A 3 VOIES EXISTANT	3 (J) ; E.A.E	1	ENLEVER	EXISTANT CONSERVE - MODELE NON INDIQUE	$ avec 3 ; lettre de zone en designation.	
M13-01 E201-039	INTERRUPTEUR SIMPLE EXISTANT	(N)	1	CONSERVER	EXISTANT CONSERVE - MODELE NON INDIQUE	$ seul.	
M13-02 E201-046	INTERRUPTEUR SIMPLE EXISTANT	(N)	1	CONSERVER	EXISTANT CONSERVE - MODELE NON INDIQUE	$ seul.	

BORDEREAU MATERIEL - E201

Quantites representees avec multiplicateurs; portees et composants de chaque ensemble conserves.

Les renvois et composants de panneaux ne constituent pas des ensembles supplementaires a additionner.

Repere / source	Materiel	Designation	Qte	Portee	Modele	Prescription / reserve	Parent
M14-01 E201-059	INTERRUPTEURS MAITRES (NOTE SPECIFIQUE 1) (HORS LEGENDE - R-007)	NOTE SPECIFIQUE 1 ; E.A.R	1	RELOCALISER	EXISTANT CONSERVE - MODELE NON INDIQUE	$ dans un carre + bulle 1 ; note specifique 1 : a relocaliser.	

RESERVES ET COMPLEMENTS
Dossier de travail : `OUTBOX/TEST-E201/travail`. Entrée : deux pages PNG (E-001 légende, E-201 plan) converties en PDF
Cartouche E-201 : "ÉCLAIRAGE ET ALARME INCENDIE - EXISTANT/DÉMOLITION - REZ-DE-CHAUSSÉE". Note générale 1 : "sauf
symboles. Résultat : 5 x DÉTECTEUR DE FUMÉE (I01), dont 1 E.A.R (882 ; 704) ; aucun avertisseur 120 V sur E-201.
raster A1 (841 x 594 mm = 2383,9 x 1683,8 pt, image 7946 x 5613 px). Aucune couche texte : tout le relevé est visuel.
indications contraires, tous les équipements sont existants à conserver". Portées appliquées : `CONSERVER` par défaut,
`ENLEVER` quand l'étiquette E.A.E est lue à côté du symbole, `RELOCALISER` pour E.A.R (abréviations de E-001). Aucun
appareil neuf sur cette feuille ; le neuf est sur E-203 (non fournie). `materiel` porte EXISTANT (règle R11).
Les zones grisées (bibliothèque adultes 115, salle d'animation 108, secteur jeunesse 118, moitié sud) sont hors
portée : aucun appareil n'y est dessiné en noir. Zone relevée : x 300-1270 / y 150-990 pt (bureaux 110.x, hall 107,
réception 110.18, corridor 110.12, aide au lecteur 116, escaliers, ascenseur).
44 carrés à diagonale trouvés par appariement de gabarit (score >= 0,81) sur le raster, 1 ajouté après balayage
(réception des marchandises, 1026 ; 370 - texte superposé). Les 3 candidats à score 0,55-0,56 ont été vérifiés
au zoom : vides (pas de symbole). Les 28 encastrés (cercle + croix) : 28 appariés (score >= 0,74), classés
pleins/vides par mesure de l'anneau (noir < 120 -> PP-U1). Étiquettes (PP-2 3, PP-U1 2, (h,i)/(j,k)/(n)/(Mf)/(Ma),
E.A.E) lues une à une sur 3 planches de 25 vignettes.
Première lecture : 4 "avertisseurs 120 V CO" (A03, 3/4 noir) + 1 "détecteur de fumée" (A04, 1/2 noir), d'après le
pourcentage de noir mesuré sur le raster. Corrigé après vérification indépendante : au zoom x20, les 5 symboles
sont identiques - cercle coupé en diagonale, moitié noire - et la légende E-001 montre A03 = 3/4 noir (quart blanc en
haut à gauche), A04 = coupé en diagonale. La mesure de noir était polluée par le trait de mur qui traverse 4 des 5
Leçon : à 4,6 pt, une proportion de noir ne distingue pas deux lignes de légende ; comparer la forme au zoom.
Cercles noirs ~8 pt dans le corridor, sans PP ni circuit ni E.A.E. La légende L04 "appareil d'éclairage encastré"
est un cercle simple, mais tous les autres encastrés de la feuille portent une croix et une étiquette. Relevés sous
"CERCLE SANS ETIQUETTE", portée `A PRECISER`. À trancher : luminaire ou symbole architectural.
Carré portant "C", toujours près d'une porte (1143 ; 334), (1109 ; 367), (1017 ; 542), (582 ; 816 - E.A.E).
Absent des légendes E-001 (ni ÉLECTRICITÉ, ni ALARME INCENDIE/INTRUSION, ni SERVICES). Relevé sous "BOITIER C",
famille `autre`, matériel suffixé (hors legende). À identifier (contact de porte ? bouton de sortie ?).
Symbole "$" dans un carré avec bulle 1 et E.A.R à (1003 ; 552). Note spécifique 1 : "Interrupteurs maîtres, à
relocaliser. Tout l'éclairage de la zone principale du hall est commandé à partir de ce panneau. Système de
dénomination : Ma (Main a)." Relevé 1 repère `RELOCALISER`, hors légende. Les suffixes (Ma)/(Mf) des encastrés
renvoient à ce système.
Deux rails courbes (P-2 39 : 5 têtes, ~125 pt ~ 4,4 m à 1:100 ; P-2 41 : 3 têtes, ~55 pt ~ 1,9 m), tous deux
E.A.E. Longueur estimée depuis l'échelle 1:100 du cartouche (1 pt = 0,0353 m) : à métrer avant chiffrage.
Boîte de jonction (carré X) en tête de chaque rail relevée séparément (S01).
Rectangle "+ " avec un petit cercle accolé, à l'entrée du bureau 110.5. Relevé sous U04 "ACCUMULATEUR",
`CONSERVER` (aucune mention E.A.E lue). Le petit cercle pourrait indiquer un phare : à confirmer.
L02 (rectangle sans description), L03 réglette 4', L08 gradateur, L09 mural, L10/L11 réglettes murales, L13
(hachuré, sans description), L15 347 V, L17 daylight, A02, A05, A07, A08, A10-A13, U03, U05-U10 : cherchées sur toute
la zone blanche, aucune occurrence. Les sections SERVICES, DISTRIBUTION, CHAUFFAGE, FORCE MOTRICE de E-001 ne
s'appliquent pas à une feuille d'éclairage/alarme (seule S01 boîte de jonction y figure).
Un second agent, sans accès aux CSV ni au journal, a compté la feuille à l'aveugle (16 vignettes + légende) puis audité le
rendu : 0 écart de quantité famille par famille (121/121, portées comprises), 0 omission, 0 faux positif ; 4 familles
(R-004, corrigé), 3 décalages sûrs + 2 probables (I05-01, I05-02, M08-01, M10-01, M13-02 : corrigés par lecture au x12/x14),
4 doutes conservés (M01-01 accumulateur seul ou "1 phare" ; M12-01 enseigne au bord de la zone grise ; M05-01/02
cercles sans étiquette, architecture probable). Rapport : `RAPPORT-VERIFICATEUR.md`.
Entrée raster (PNG), pas le PDF vectoriel : `traits.py` inutilisable, coordonnées lues sur les règles des
zooms (précision ~ ±1 pt) et par centroïde raster pour les appariements.
Aucun devis ni addenda fourni : colonne `modele` = EXISTANT CONSERVE - MODELE NON INDIQUE.
Aucune référence d'estimateur : critère d'acceptation à l'étape 1 (identification à l'aveugle),
vérification incomplète.
Modèle exécutant ce relevé : Claude Fable 5.1 (session interactive, route "session = agent" de CLAUDE.md).