



- CE DOCUMENT NE DOIT
PAS ÊTRE UTILISÉ À DES
FINS DE CONSTRUCTION

01	2026-08-20	EMIS POUR ADDENDA E-01	M-D-A
00	2026-07-09	EMIS POUR APPEL D'OFFRES	M-D-A
No.	Date	Description	Pa



CIMA+ 900-740, rue Notre-Dame Ouest
Montréal QC H3C 3X8
CANADA
T 514 337-2462
F 514 281-1632
cima.ca

CENTRE DE SERVICES
SCOLAIRE DE
SOREL-TRACEY

RÉHABILITATION ET TRAVAUX
CONNEXES
ÉCOLE SECONDAIRE BERNARD-GARIÉPY

ÉCLAIRAGE
REZ-DE-CHAUSSÉE BLOC
EXISTANT / DÉMOLITION

ÉLECTRICITÉ	
DESSINÉ PAR : P. TORRES	ÉCHELLE : INDIQUÉ
CONÇU PAR : M. DUSSAULT-MATTE, ing.	DATE : 2026-04-17
VÉRIFIÉ PAR : M. DUSSAULT-MATTE, ing.	VÉRIFIÉ PAR : T. TAN, ing.
PROJET No : P0002920	DESSIN No : E-D210
FEUILLE No :	



- 1 APPAREIL DÉCLARÉ JUSQU'À 24 H À ENLEVER POUR LES TRAVAUX DE DÉMOLITION DU PLAFOND ET SUSPENDRE TEMPORAIREMENT DU PLAFOND.
- 2 APPAREIL(S) DÉCLARÉ JUSQU'À ENLEVER ET REMETTRE AU PROPRIÉTAIRE.
- 3 DÉTECTEUR DE FUMÉE À ENLEVER POUR LES TRAVAUX DE DÉMOLITION DES TULE ET LE SUSPENDRE À PARTIR DU PLAFOND POUR UNE UTILISATION TEMPORAIRE.
- 4 ENSEIGNE DE SORTIE À ENLEVER POUR LES TRAVAUX DE DÉMOLITION ET LA SUSPENDRE À PARTIR DU PLAFOND POUR UNE UTILISATION TEMPORAIRE.
- 5 APPAREILS DÉCLARÉ JUSQU'À 24 H À ENLEVER POUR LES TRAVAUX DE DÉMOLITION DES TULE ET LE SUSPENDRE À PARTIR DU PLAFOND POUR UNE UTILISATION TEMPORAIRE.
- 6 APPAREILS DÉCLARÉ JUSQU'À 24 H À ENLEVER POUR LES TRAVAUX DE DÉMOLITION DES TULE ET LE SUSPENDRE À PARTIR DU PLAFOND POUR UNE UTILISATION TEMPORAIRE.



- ◆ Alarme existante — à classer (2)
- ◆ Dém. chauffage — à classer (1)
- Dém. luminaire 1x4 / segment linéaire (284)
- Dém. luminaire 2x2 (2)
- Dém. luminaire 2x4 (109)
- Dém. luminaire rond encastré (20)
- ◆ Dém. éclairage — à classer (11)
- Détecteur fumée existant — dépose/repose temp. (46)
- Détecteur sécurité (M) — par autres (3)
- Luminaire 24h existant — dépose/repose temp. (44)
- Repère EAC — existant à conserver (8)
- Station manuelle existante (F) — à confirmer (9)
- ◆ Éclairage existant carré — à classer (17)
- ◆ Éclairage existant — à classer (2)

CE DOCUMENT NE DOIT PAS ÊTRE UTILISÉ À DES FINS DE CONSTRUCTION

01	2026-08-20	ÉMIS POUR ADDENDA E-01	M.D-Ming
00	2026-07-09	ÉMIS POUR APPEL D'OFFRES	M.D-Ming
No.	Date	Description	Par



CIMA+ 900-740, rue Notre-Dame Ouest
Montréal QC H3C 3X8
CANADA
T 514 337-2462
F 514 281-1632
cima.ca

CENTRE DE SERVICES
SCOLAIRE DE
SOREL-TRACEY

RÉHABILITATION ET TRAVAUX
CONNEXES
ÉCOLE SECONDAIRE BERNARD-GARIÉPY

ÉCLAIRAGE
REZ-DE-CHAUSSÉE BLOC C
EXISTANT / DÉMOLITION

ÉLECTRICITÉ

DESSIN PAR : P. TORRES	ECHELLE : INDIQUEE
CONCU PAR : M. DUSSAULT-MATTE, ing.	DATE : 2026-04-17
VERIFIE PAR : M. DUSSAULT-MATTE, ing.	VERIFIE PAR : T. TAN, ing.
PROJET No : P0002920	DESSIN No : E-D211
FEUILLE No :	



RD DES ÉTOUVANTES

BLOC C1

RD BERNARD

GARNIER

RD DES ÉRABLES

ZONE DES TRAVAUX

1

- CE DOCUMENT NE DOIT
PAS ÊTRE UTILISÉ À DES
FINS DE CONSTRUCTION

01	2026-08-20	EMIS POUR ADDENDA E-01	M-D-Ming
00	2026-07-09	EMIS POUR APPEL D'OFFRES	M-D-Ming
No.	Date	Description	Par




CIMA+ 900-760, rue Notre-Dame Ouest
Montréal QC H3C 3X8
CANADA
T 514 337-2452
F 514 281-1632
cima.ca

CENTRE DE SERVICES
SCOLAIRE DE
SOREL-TRACEY

RÉHABILITATION ET TRAVAUX
CONNEXES
ÉCOLE SECONDAIRE BERNARD-GARIÉPY

ÉCLAIRAGE
REZ-DE-CHAUSSÉE BLOC C1
EXISTANT / DÉMOLITION

ÉLECTRICITÉ	
DESSIN PAR : P. TORRES	RELEVÉ : INDIQUÉ
CONCÉDÉ PAR : M. DUSSAULT-MATTE, ing.	DATE : 2026-04-17
REVÉRÉ PAR : M. DUSSAULT-MATTE, ing.	NOUVEAU PAR : T. TAN, ing.
PROJET No : P0002920	DESSIN No : E-D212
FEUILLE No : 06 DE 10	

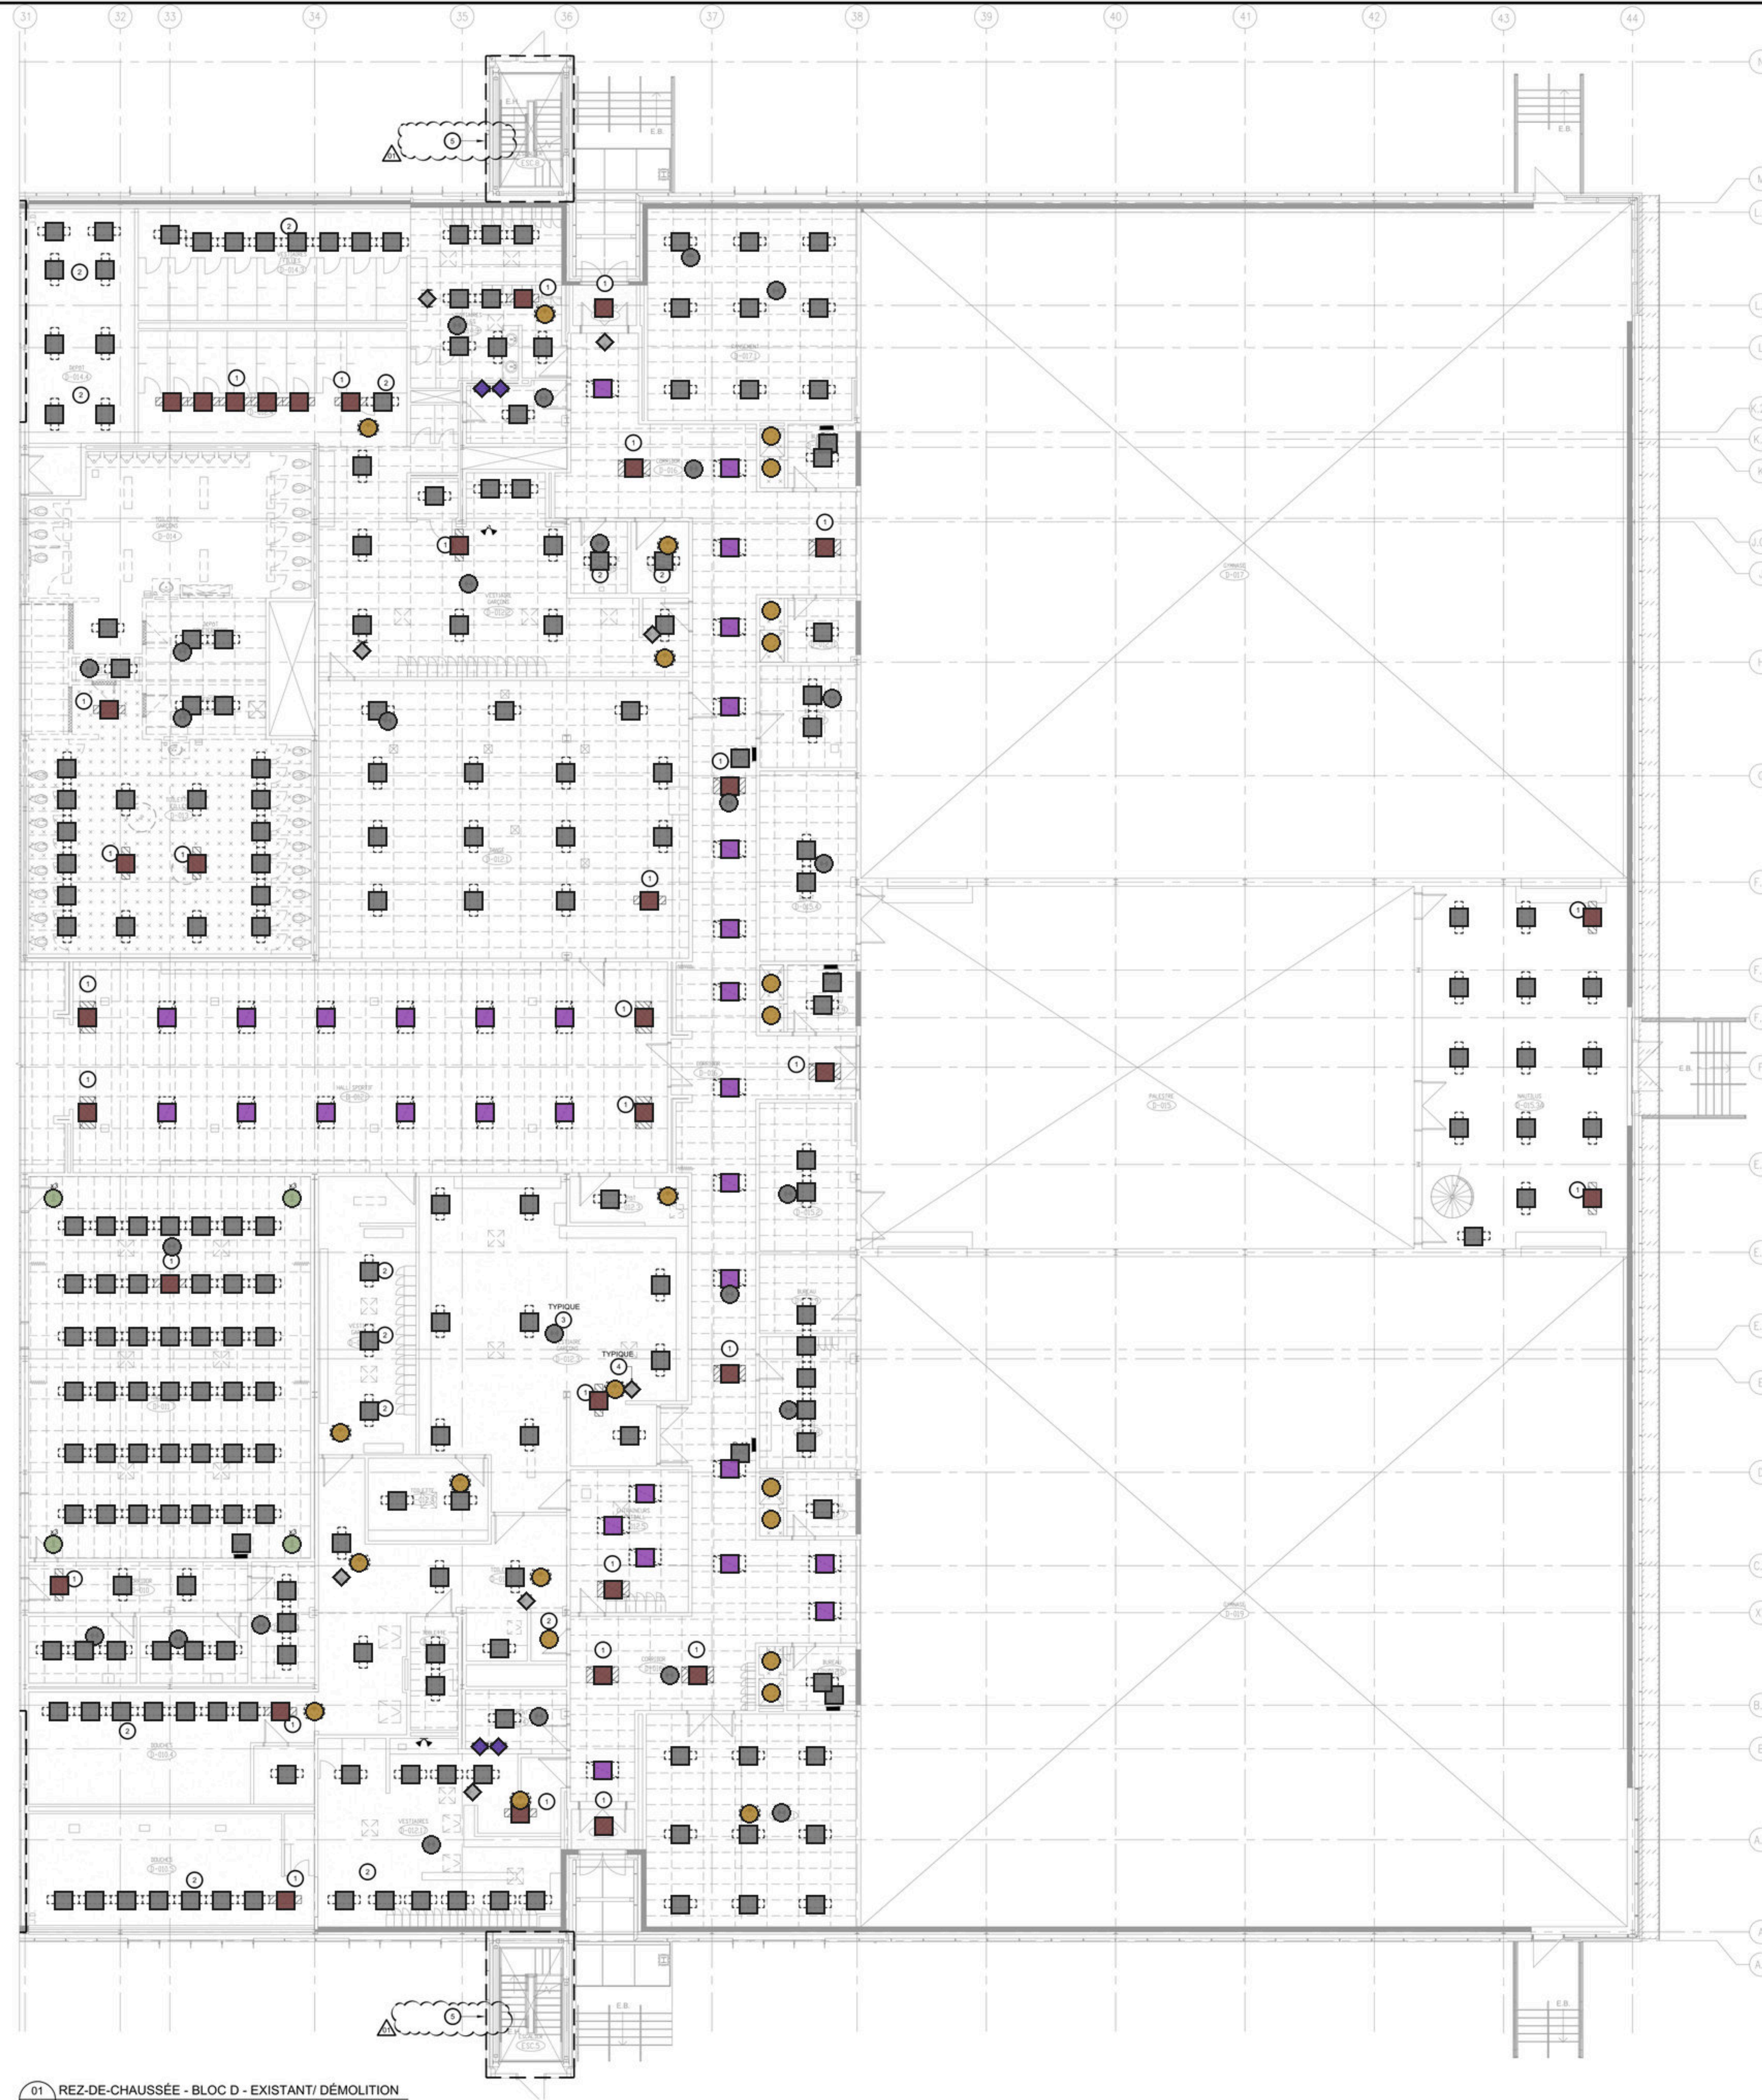


01 REZ-DE-CHAUSSÉE - BLOC D - EXISTANT/ DÉMOLITION
E-D212 ÉCHELLE : 1:100

NOTES GÉNÉRALES :

- ② DE MONT D'INDICATIONS CONTRAIRES, TOUS LES ÉQUIPEMENTS MONTRÉS SUR CE PLAN SONT EXISTANTS À ENLEVER. TOUS LES SERVICES INSTALLÉS AUX MURS SONT EXISTANTS À CONSERVER.
- ③ LES CAMÉRAS, BORNES WIFI, PROJECTEURS ET HAUT-PARLEURS DE CLASSE SERONT RETENUS AVANT LES TRAVAUX ET ENTROUSPÉ PAR LA CIBST POUR LA DURÉE DES TRAVAUX.
- ④ TOUS LES IDENTIFICATIONS EXISTANTES SUR LES GRILLES DU PLAFOND ET LES ÉCROUS ANCIENS, BLEUS ET ROUGES REPRÉSENTENT L'EMPLACEMENT DES BORNES WFI, DES VALVES MÉCANIQUES ET DE LA DÉMOLITION, 24H DONT 12H SONT À ENLEVER, 12H À CONSERVER.
- ⑤ N.Y.A. PRÉSENTEMENT PAS D'ALIMENTATION DANS LE B.L.C.D.

NOTES SPÉCIFIQUES :

- ① APPAREIL D'ÉCLAIRAGE 24H À ENLEVER POUR LES TRAVAUX DE DÉMOLITION DU PLAFOND ET SUSPENDRE TEMPORAIREMENT DU PLAFOND.
- ② APPAREILS D'ÉCLAIRAGE AU DE LA ENLEVER ET REMETTRE AU PROPRIÉTAIRE.
- ③ DÉTECTEUR DE FUMÉE À ENLEVER POUR LES TRAVAUX DE DÉMOLITION DES TUBES ET LE SUSPENDRE À PARTIR DU PLAFOND POUR UNE UTILISATION TEMPORAIRE.
- ④ ENSEMBLE DE SORTIE À ENLEVER POUR LES TRAVAUX DE DÉMOLITION ET LA SUSPENDRE À PARTIR DU PLAFOND POUR LES TRAVAUX DE LA TEMPORAIRE.
- ⑤ APPARELS D'ÉCLAIRAGE ET DÉTECTEURS DE FUMÉE À ENLEVER POUR LES TRAVAUX DE DECONTAMINATION, SUSPENDRE CES ÉQUIPEMENTS POUR UNE UTILISATION TEMPORAIRE.

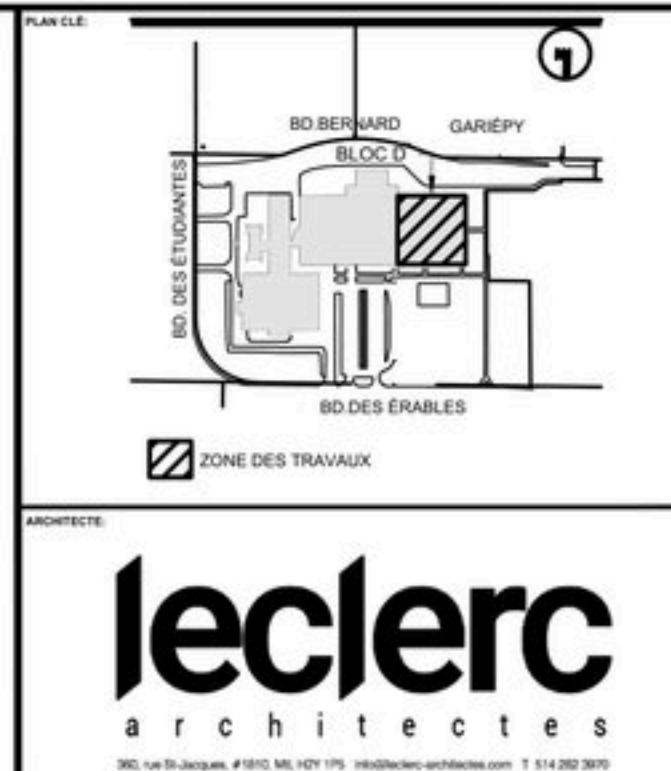

Légende — D213_ADD (358 marques)

- Dém. luminaire 1x4 / segment linéaire (221)
- Dém. luminaire 2x4 (31)
- Dém. luminaire rond encastré (24)
- Dém. prise plafond projecteur (4)
- ◆ Dém. éclairage — à classer (4)
- Détecteur fumée existant — dépose/repose temp. (26)
- Luminaire 24h existant — dépose/repose temp. (34)
- Repère EAC — existant à conserver (6)
- ◆ Éclairage existant carré — à classer (8)

CE DOCUMENT NE DOIT
PAS ÊTRE UTILISÉ À DES
FINS DE CONSTRUCTION

01	2026-08-20	ÉMIS POUR ADDENDA E-01		M-D-M
00	2026-07-09	ÉMIS POUR APPEL D'OFFRES		M-D-A
No.	Date	Description		Pa



CIMA+
900-740, rue Notre-Dame Ouest
Montréal QC H3C 3X5
CANADA
T 514 337-2462
F 514 281-1632
cima.ca


CENTRE DE SERVICES
SCOLAIRE DE
SOREL-TRACEY

RÉHABILITATION ET TRAVAUX
CONNEXES
ÉCOLE SECONDAIRE BERNARD-GARIÉPY

ÉCLAIRAGE
REZ-DE-CHAUSSÉE BLOC D
EXISTANT / DÉMOLITION

ÉLECTRICITÉ

DESSINÉ PAR : P. TORRES	BOULELLE : INDIQUÉ
CONÇU PAR : M. DUSSAULT-MATTE, ing.	DATE : 2026-04-17
VÉRIFIÉ PAR : M. DUSSAULT-MATTE, ing.	VÉRIFIÉ PAR : T. TAN, ing.
PROJET No : P0002920	DESSIN No : E-D213
FEUILLE No :	

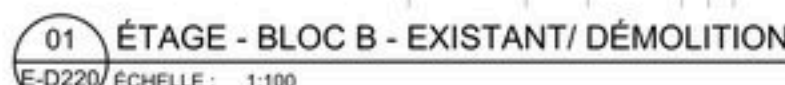

Légende — D220_ADD (553 marques)

- Dém. luminaire 1x4 / segment linéaire (318)
- Dém. luminaire 2x4 (131)
- Dém. prise plafond projecteur (7)
- Détecteur fumée existant — dépose/repose temp. (38)
- Luminaire 24h existant — dépose/repose temp. (37)
- Prise existante — à classer (4)
- Repère EAC — existant à conserver (5)
- Station manuelle existante (F) — à confirmer (4)
- ◆ Éclairage existant carré — à classer (9)

CE DOCUMENT NE DOIT
PAS ÊTRE UTILISÉ À DES
FINS DE CONSTRUCTION

01	2026-08-20	ÉMIS POUR ADDENDA E-01	M-D-M (ing.)
00	2026-07-09	ÉMIS POUR APPEL D'OFFRES	M-D-M (ing.)
No.	Date	Description	Par

**CIMA+**

900-740, rue Notre-Dame Ouest
Montréal QC H3C 3X8
CANADA
T 514 337-2482
F 514 281-1632
clima.ca

CENTRE DE SERVICES
SCOLAIRE DE
SOREL-TRACEY


RÉHABILITATION ET TRAVAUX
CONNEXES
ÉCOLE SECONDAIRE BERNARD-GARIÉPY

ÉCLAIRAGE
ÉTAGE BLOC B
EXISTANT / DÉMOLITION

ÉLECTRICITÉ

DESSIN PAR : P. TORRES	ECHELLE : INDIQUE
CONÇU PAR : M. DUSSAULT-MATTE, ing.	DATE : 2026-04-17
VÉRIFIÉ PAR : M. DUSSAULT-MATTE, ing.	VÉRIFIÉ PAR : T. TAN, ing.
PROJET No : P0002920	DESSIN No : E-D220
FEUILLE No :	

01 ÉTAGE - BLOC C - EXISTANT/ DÉMOLITION
E-D221 ÉCHELLE: 1/100

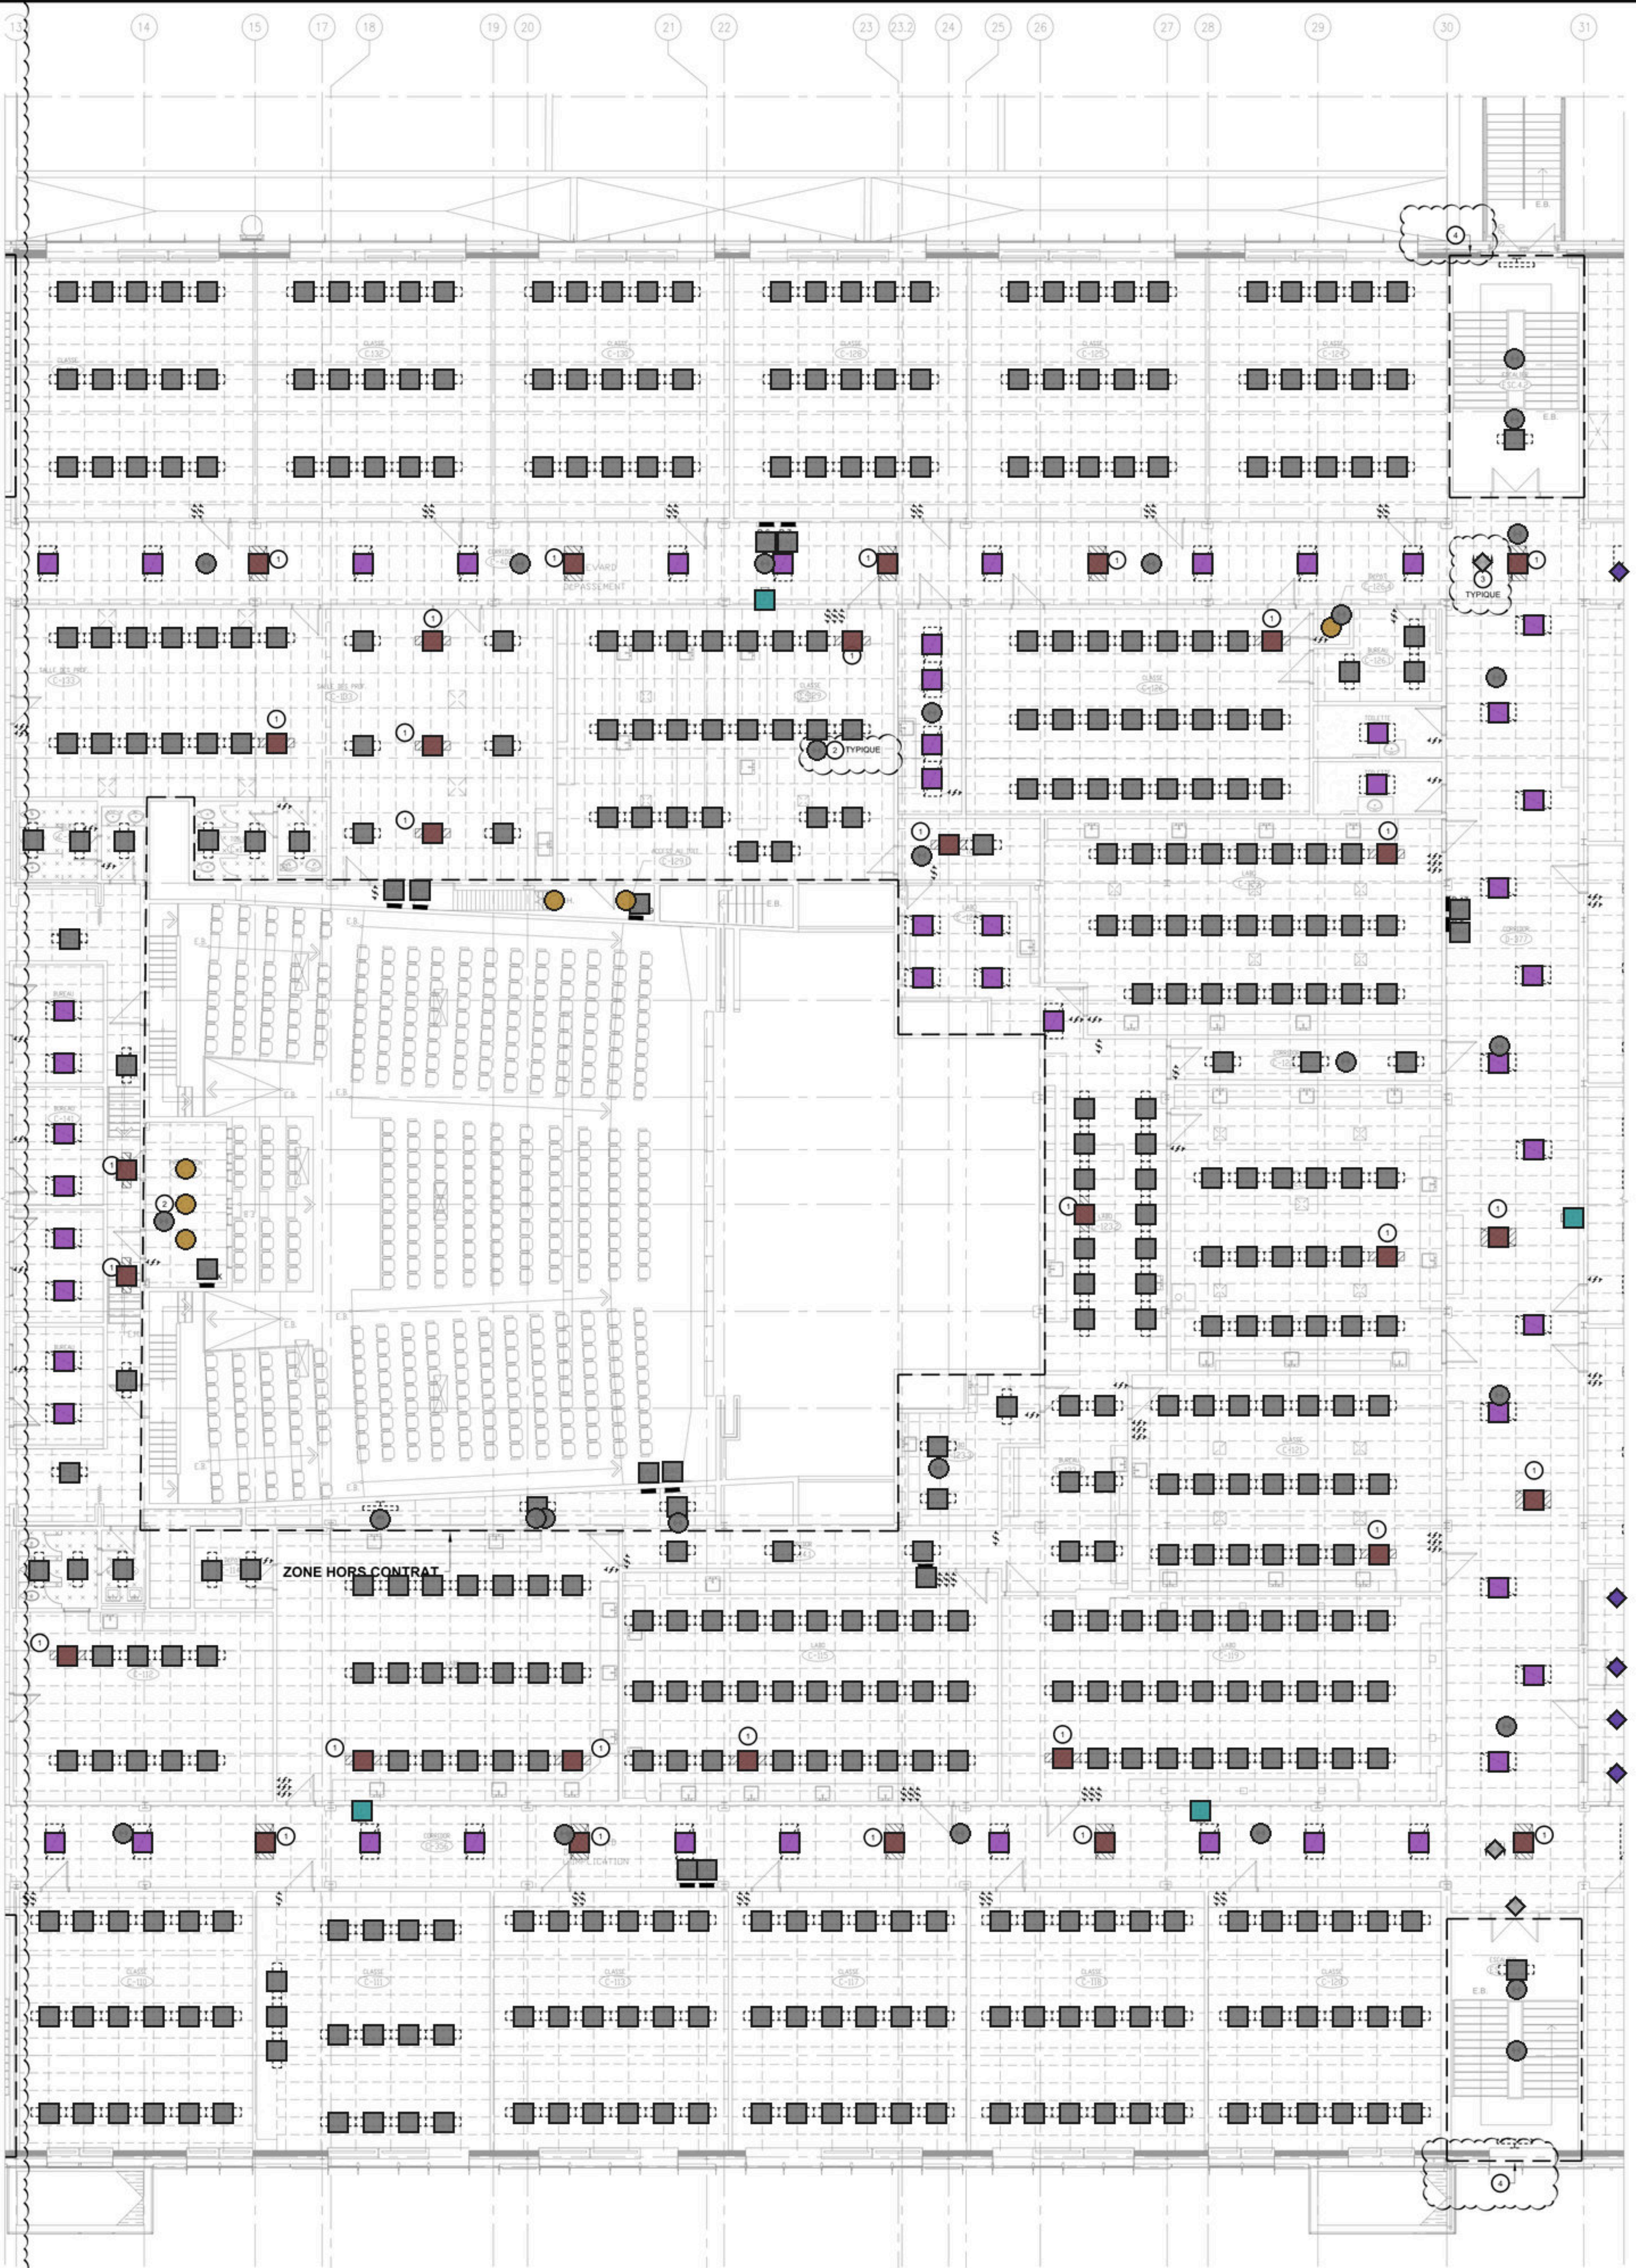

NOTES GÉNÉRALES:

- À MOINS D'INDICATIONS CONTRAIRES, TOUTS LES ÉQUIPEMENTS MONTÉS SUR CE PLAN SONT EXISTANTS À ENLEVER. TOUTS LES SERVICES INSTALLÉS AUX MURS SONT EXISTANTS À CONSERVER.
- LES CAMÉRAS, BORNES WI-FI, PROJECTEURS ET HAUT-PARLEURS DE CLASSE SERONT RETIRÉS AVANT LES TRAVAUX ET ENTREPOSÉS PAR LE CSST POUR LA DURÉE DES TRAVAUX.
- TOUTES LES IDENTIFICATIONS EXISTANTES SUR LES GRILLES DU PLAFOND (AUTOCOOLLANTS JAUNES, BLEUS ET ROUGES) REPRÉSENTANT L'EMPLACEMENT DES BORNES WI-FI, DES VALVES MÉCANIQUES ET DE L'ÉCLAIRAGE 24H DOIVENT ÊTRE CONSERVÉS DURANT LES TRAVAUX DE DÉMOLITION.

NOTES SPÉCIFIQUES:

- 1 APPAREIL D'ÉCLAIRAGE 24 H À ENLEVER POUR LES TRAVAUX DE DÉMOLITION DU PLAFOND ET SUSPENDRE TEMPORAIREMENT DU PLAFOND.
- 2 DÉTECTEUR DE FUMÉE À ENLEVER POUR LES TRAVAUX DE DÉMOLITION DES TUALES ET LE SUSPENDRE À PARTIR DU PLAFOND POUR UNE UTILISATION TEMPORAIRE.
- 3 ENSEIGNE DE SORTIE À ENLEVER POUR LES TRAVAUX DE DÉMOLITION ET LA SUSPENDRE À PARTIR DU PLAFOND POUR UNE UTILISATION TEMPORAIRE.
- 4 APPARELS D'ÉCLAIRAGE ET DÉTECTEURS DE FUMÉE À ENLEVER POUR LES TRAVAUX DE DÉCONTAMINATION. SUSPENDRE CES ÉQUIPEMENTS POUR UNE UTILISATION TEMPORAIRE.

PLAN CLE

1

leclerc
architectes

365, rue St-Jacques, #1010, St-Jacques, Montréal, QC H2Y 1Y5 | info@leclercarchitectes.com | 514 382 3870

Légende — D221_ADD (599 marques)

- Dém. luminaire 1x4 / segment linéaire (459)
- Dém. luminaire 2x4 (51)
- Dém. luminaire rond encastré (6)
- ◆ Dém. éclairage — à classer (5)
- Détecteur fumée existant — dépose/repose temp. (28)
- Luminaire 24h existant — dépose/repose temp. (30)
- Repère EAC — existant à conserver (13)
- Station manuelle existante (F) — à confirmer (4)
- ◆ Éclairage existant carré — à classer (3)

CE DOCUMENT NE DOIT PAS ÊTRE UTILISÉ À DES FINS DE CONSTRUCTION

01	2020-06-20	EMIS POUR ADDENDA E-01		M-D-M .ing
00	2020-07-09	EMIS POUR APPEL D'OFFRES		M-D-M .ing
No.	Date	Description		Par
REMARQUE :				
				
CONCÉDÉ PAR: VÉRIFIÉ PAR:				
PROJETS:				
CLIENT:				
 900-760, rue Notre-Dame Ouest Montréal QC H3C 3S3 CANADA T 514 381-2482 F 514 381-9522 cma@ca				
CENTRE DE SERVICES SCOLAIRE DE SOREL-TRACEY				
PROJET:				
RÉHABILITATION ET TRAVAUX CONNEXES ÉCOLE SECONDAIRE BERNARD-GARIEPY				
TITRE DU DESSIN:				
ÉCLAIRAGE ÉTAGE BLOC C EXISTANT / DÉMOLITION				
DISCIPLINE:				
ÉLECTRICITÉ				
DESSINÉ PAR: P. TORRES		ÉVALUÉ INDIQUÉ		
CONCÉDÉ PAR: M. DUSSAULT-MATTE, ing.		DATE: 2020-04-17		
VÉRIFIÉ PAR: M. DUSSAULT-MATTE, ing.		VÉRIFIÉ PAR: T. TAN, ing.		
PROJET NO. : P0000200		DESSIN NO. :		
PROJET NO. : 09 DE 10		E-D221		



- Légende — D222_ADD (463 marques)
-  Dém. luminaire 1x4 / segment linéaire (366)
 -  Dém. luminaire 2x4 (45)
 -  Détecteur fumée existant — dépose/repose temp. (13)
 -  Luminaire 24h existant — dépose/repose temp. (27)
 -  Repère EAC — existant à conserver (6)
 -  Station manuelle existante (F) — à confirmer (4)
 -  Éclairage existant carré — à classer (2)



CE DOCUMENT NE DOIT
PAS ÊTRE UTILISÉ À DES
FINS DE CONSTRUCTION

01	2026-08-20	EMIS POUR ADDENDA E-01	M-D-M
00	2026-07-09	EMIS POUR APPEL D'OFFRES	M-D-M
No.	Date	Description	Par



CIMA+

CENTRE DE SERVICES
SCOLAIRE DE
SOREL-TRACEY


PROJET :

RÉHABILITATION ET TRAVAUX
CONNEXES
ÉCOLE SECONDAIRE BERNARD-GARIÉPY

ÉCLAIRAGE
ÉTAGE BLOC D
EXISTANT / DÉMOLITION

DISCIPLINE : ÉLECTRICITÉ

DESIGNER PAR : P. TORRES	ÉCHELLE : INDIQUE
CONQU PAR M. DUSSAULT-MATTE, ing.	DATE 2026-04-17
VÉRIFIÉ PAR : M. DUSSAULT-MATTE, ing.	VÉRIFIÉ PAR : T. TAN, ing.
PROJET No : P0002920	DESIGN No : E-D222
FEUILLE No : 10 DE 10	

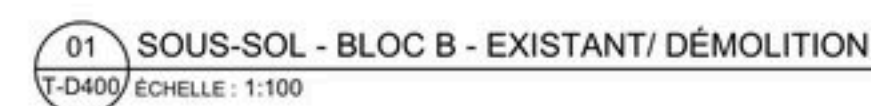

VOIR PLAN T-D401

- LES HAUT-PARLERS SE TROUVANT DANS LES BLOCS B, C ET C1 SE SONT RETIRÉS DURANT LES TRAVAUX DE DÉMONTION PLUS AUSENCE LORS DU REAMÉNAGEMENT. L'ENTREPRENEUR DOIT CONTRÔLER LES DÉPARTS DES HAUT-PARLERS.
- RENTRÉE CÂBLE DE TÉLÉCOMMUNICATION NE DOIT ÊTRE DÉMÂTÉE DURANT LES TRAVAUX DE DÉMONTION.
- PORTER UNE ATTENTION PARTICULIÈRE À PROTÉGER LE LIEN DE FIBRE OPTIQUE ENTRE LES LOCS B-1114 ET D-130-2.
- SE RÉFÉRER AU DEVIS DÉLECTRIQUE POUR LES CONDITIONS GÉNÉRALES ET LES DÉFINITIONS ADDITIONNELLES.
- LES CAMÉRAS, BORNES W-FI, PROJECTEURS ET HAUT-PARLERS DE CLASSE SE SONT RETIRÉS AVANT LES TRAVAUX ET RETROUSSES PAR LE CSS POUR LA DURÉE DES TRAVAUX.
- TOUTES LES IDENTIFICATIONS EXISTANTES SUR LES GRILLES DU POUTRE (AUTOCOCCANTES ANCIENNES, BLEUES ET ROUGES) REPRÉSENTENT EMPLACEMENT DES BORNES W-FI DES CÂBLES MÉCANIQUES ET DE TÉLÉCOMMANDE. LES CÂBLES SONT CONSERVÉS DURANT LES TRAVAUX DE DÉMONTION.



CE DOCUMENT NE DOIT
PAS ÊTRE UTILISÉ À DES
FINS DE CONSTRUCTION

0	2026-07-08	EMIS POUR APPEL D'OFFRES	D.V.
No.	Date	Description	Par



INGÉNIEUR :

CIMA+

900-740, rue Notre-Dame Ouest
Montréal, QC H3C 3S8
CANADA
T 514 337-2462
F 514 280-1632
cima.ca


CENTRE DE SERVICES
SCOLAIRE DE
SOREL-TRACEY

RÉHABILITATION ET TRAVAUX
CONNEXES
ÉCOLE SECONDAIRE BERNARD-GARIÉPY

TÉLÉCOMMUNICATIONS
DÉMOLITION PHASE 1 SOUS-SOL
EXISTANT / DÉMOLITION

DISCIPLINE : **TÉLÉCOMMUNICATIONS**

DESIGNER PAR : C-A. GRAVEL	REVUE PAR : INDIQUE
CONÇU PAR : A. SY, tech.	DATE : 2026-04-17
VERIFIÉ PAR :	VERIFIÉ PAR : D. VINCENT, ing.
PROJET No : P0002920	DESIGN No : T-D400
FEUILLE No : 1 DE 11	

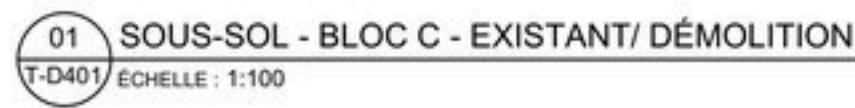

Plan de la zone de travaux. Le schéma illustre la configuration des rues et la zone de travaux. Les rues représentées sont le BO BERNARD, la GARIEPY, le BO DES ÉTIENNES, le BO DES ÉRABLES et le BO DES ÉTOILES. La zone de travaux est indiquée par un hachurage et une légende en bas à gauche.

leclerc
architectes

CE DOCUMENT NE DOIT
PAS ÊTRE UTILISÉ À DES
FINS DE CONSTRUCTION

0	2026-07-08	EMIS POUR APPEL D'OFFRES	D.V.
No	Date	Description	Par



CIMA+ 900-740, rue Notre-Dame Ouest
Montréal QC H3C 3X5
CANADA
T 514 337-2462
F 514 281-1632
cima.ca

CLIENT

CENTRE DE SERVICES
SCOLAIRE DE
SOREL-TRACEY

PROJECT

RÉHABILITATION ET TRAVAUX
CONNEXES
ÉCOLE SECONDAIRE BERNARD-GARIÉPY


TITRE DU DESSIN :

TÉLÉCOMMUNICATIONS
DÉMOLITION PHASE 1 SOUS-SOL
EXISTANT / DÉMOLITION

DISCIPLINE


TÉLÉCOMMUNICATIONS

DESIGNÉ PAR : C-A. GRAVEL	EMPELLE : INDIQUE
CONÇU PAR : A. SY, tech.	DATE : 2026-04-17
VERSIÉ PAR :	VERSIÉ PAR : D. VINCENT, ing.
PROJET No : P0002920	DESIN No : T-D401
FEUILLE No : 2 DE 11	

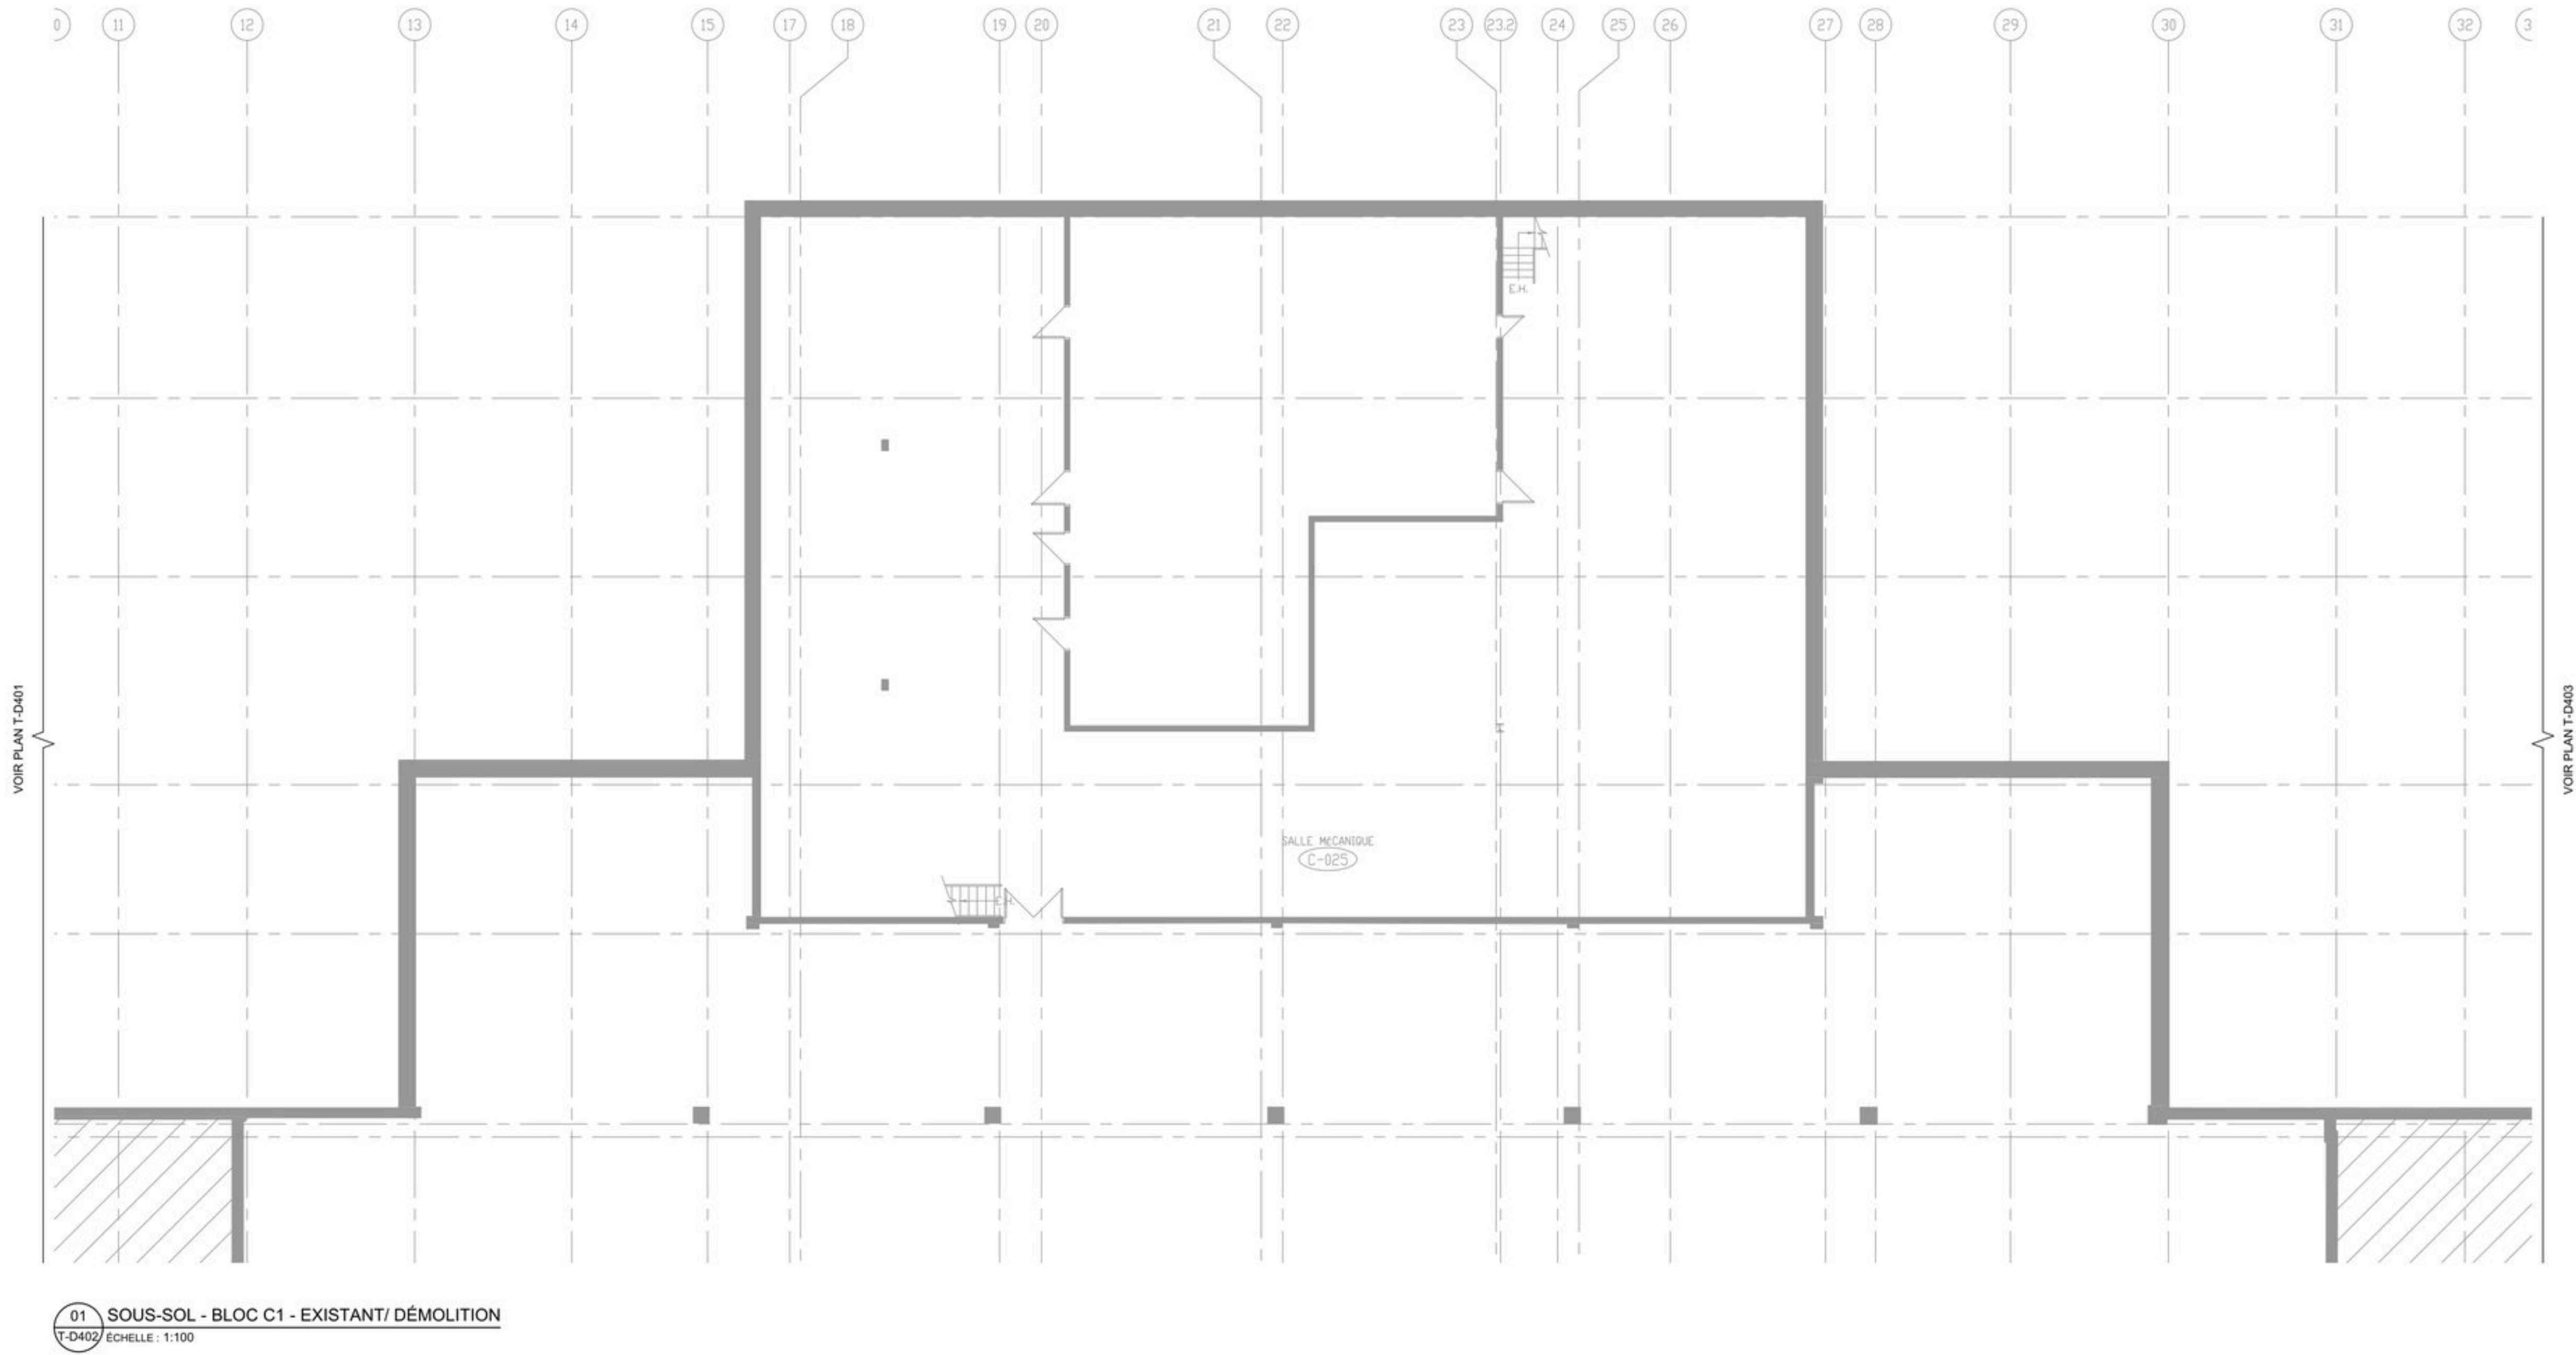

NOTES GÉNÉRALES:

- LES HAUT-PARLEURS SE TROUVANT DANS LES BLOCS B, C ET C1 SERONT RETIRÉS DURANT LES TRAVAUX DE DÉMOLITION PUIS RÉINSTALLÉS LORS DU RÉAMÉNAGEMENT. L'ENTREPRENEUR DEVRA ENTREPOSER LES HAUT-PARLEURS.
- AUCUN CÂBLE DE TÉLÉCOMMUNICATION NE DOIT ÊTRE DÉMANTÉLÉ DURANT LES TRAVAUX DE DÉMOLITION.
- PORTER UNE ATTENTION PARTICULIÈRE À PROTÉGER LE LIEN DE FIBRE OPTIQUE ENTRE LES LOCAUX B-111.4 ET D-132.2.
- SE RÉFÉRER AU DEVS D'ÉLECTRICITÉ POUR LES CONDITIONS GÉNÉRALES ET LES DÉFINITIONS ADDITIONNELLES.
- LES CAMÉRAS, BORNES WI-FI, PROJECTEURS ET HAUT-PARLEURS DE CLASSE SERONT RETIRÉS AVANT LES TRAVAUX ET ENTREPOSÉS PAR LE CSS POUR LA DURÉE DES TRAVAUX.
- TOUTES LES IDENTIFICATIONS EXISTANTES SUR LES GRILLES DU PLAFOND (AUTOCOLLANTS JAUNES, BLEUS ET ROUGES) REPRÉSENTANT L'EMPLACEMENT DES BORNES WI-FI, DES VALVES MÉCANIQUES ET DE L'ÉCLAIRAGE 24H DOIVENT ÊTRE CONSERVÉES DURANT LES TRAVAUX DE DÉMOLITION.

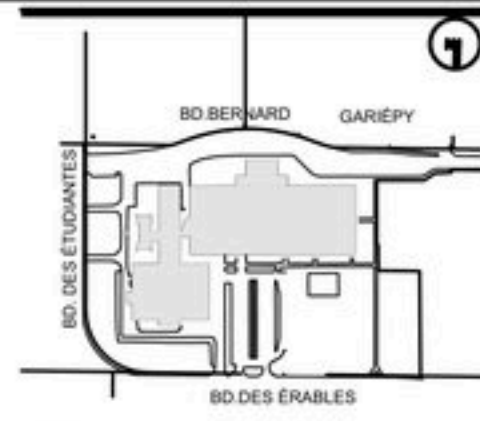

CE DOCUMENT NE DOIT PAS ÊTRE UTILISÉ À DES FINS DE CONSTRUCTION

No.	Date	Description	Par
0	2026-07-08	ÉMISSION POUR APPEL D'OFFRES	D.V.



CENTRE DE SERVICES
SCOLAIRE DE
SOREL-TRACEY

RÉHABILITATION ET TRAVAUX
CONNEXES
ÉCOLE SECONDAIRE BERNARD-GARIÉPY


TÉLÉCOMMUNICATIONS
DÉMOLITION PHASE 1 SOUS-SOL
EXISTANT / DÉMOLITION

TÉLÉCOMMUNICATIONS	
DESSINÉ PAR C-A. GRAVEL	REVÊLU INDIGUE
APProuvé PAR A. SY, tech.	DATE 2026-04-17
VERIFIÉ PAR D. VINCENT, ing.	DESSINÉ PAR T-D402

01 SOUS-SOL - BLOC D - EXISTANT/ DÉMOLITION
T-D403 ÉCHELLE : 1:100

NOTES GÉNÉRALES:

- LES HAUT-PARLEURS DANS LE BOIS DOIVENT ÊTRE DÉMÂTELÉS LORS DES TRAVAUX DE DÉMÔLITION. CES HAUT-PARLEURS NE DOIVENT PAS ÊTRE ENTREPOSÉS DURANT LES TRAVAUX.
- AUCUN CÂBLE DE TÉLÉCOMMUNICATION NE DOIT ÊTRE DÉMÂTELÉ DURANT LES TRAVAUX DE DÉMÔLITION.
- SE RÉFÉRER AU DEVS DÉLECTRICITÉ POUR LES CONDITIONS GÉNÉRALES ET LES DÉFINITIONS ADDITIONNELLES
- LES CAMÉRAS, BORNE WS-FL, PROJECTEURS ET HAUT-PARLEURS DE CLASSE SERONT RETIRÉS AVANT LES TRAVAUX ET ENTREPOSÉS PAR LE CSS POUR LA DURÉE DES TRAVAUX.
- TOUTES LES IDENTIFICATIONS EXISTANTES SUR LES GRILLES OU PLANCHES (AUTOCOLLANTS JAUNES, BLEUS ET ROUGES) REPRÉSENTANT L'EMPLACEMENT DES BORNES WS-FL, DES VALVES MÉCANIQUES ET DE L'ÉCLAIRAGE 24h DOIVENT ÊTRE CONSERVÉES DURANT LES TRAVAUX DE DÉMÔLITION

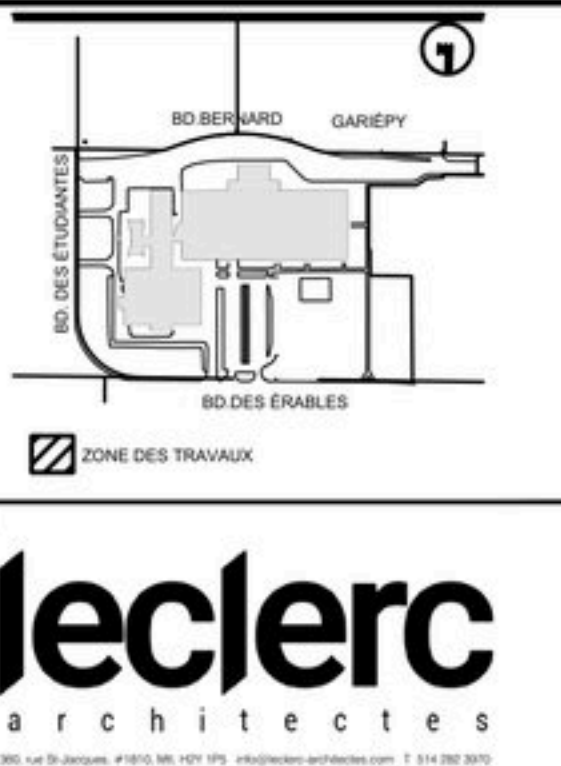

CE DOCUMENT NE DOIT
PAS ÊTRE UTILISÉ À DES
FINS DE CONSTRUCTION

[illegible]



01 REZ-DE-CHAUSSEE - BLOC B - EXISTANT/ DÉMOLITION
T-D410 ÉCHELLE : 1:100

NOTES GÉNÉRALES:

- LES HAUT PAREURS SE TROUVANT DANS LES BLOCS B, C ET D SONT RETIRÉS DURANT LE TRAVAIL DE DÉMOLITION PLUS RÉSISTANTS LOURD DU TRAVAUX DÉMOLITION L'ENTREPRENEUR DOIT FAIRE ATTENTION À NE PAS ENDOMMAGER LES BLOCS C ET D
- AUCUN CÂBLE DE TÉLÉCOMMUNICATION NE DOIT ÊTRE DÉMANTÉ DURANT LE TRAVAIL DE DÉMOLITION.
- PORTER UNE ATTENTION PARTICULIÈRE À PROTÉGER LE LIEN DE FIBRE OPTIQUE ENTRE LES LOGICAB 8-111-4 ET D-132-2.
- SE RÉFÉRER AU DES DÉMOLITION POUR LES CONDITIONS GÉNÉRALES ET LES DES POINTS ADDITIONNELLES
- LES CAMÉRAS BORNES VUE, PROJECTEURS ET HAUT PAREURS DE CLASSEMENT SONT À PROTEGER AVANT LE TRAVAIL ET ENTÉRINÉS PAR CES POUR LA DURÉE DES TRAVAUX
- TOUTES LES IDENTIFICATIONS EXISTANTES SUR LES GRILLES DU PAYSAGE SONT À PROTEGER AVANT LE TRAVAIL DE DÉMOLITION. REPRÉSENTANT L'EMPLACEMENT DES BORNES VUE, DES HAUT PAREURS DE CLASSEMENT ET DES CAMÉRAS BORNES VUE SONT CONSERVÉES DURANT LE TRAVAIL DE DÉMOLITION



Légende — D410 (23 marques)

▲ Haut-parleur existant — dépose/entreposage (23)

CE DOCUMENT NE DOIT
PAS ÊTRE UTILISÉ À DES
FINS DE CONSTRUCTION

0	2026-07-06	ÉMIS POUR APPEL D'OFFRES	D.V.
No.	Date	Description	Par



CIMA+ 900-7403, rue Notre-Dame Ouest
Montréal QC H3C 3X6
Canada
T 514 337-0462
F 514 281-1632
cima.ca


CENTRE DE SERVICES
SCOLAIRE DE
SOREL-TRACEY

RÉHABILITATION ET TRAVAUX
CONNEXES
ÉCOLE SECONDAIRE BERNARD-GARIÉPY

TÉLÉCOMMUNICATIONS
DÉMOLITION PHASE 1
REZ-DE-CHAUSSÉE
EXISTANT / DÉMOLITION

TÉLÉCOMMUNICATIONS

DESIGNÉ PAR : C-A. GRAVEL	ÉCHELLE : INDIQUÉ
CONQUÉ PAR : A. SY, tech.	DATE : 2026-04-17
VÉRIFIÉ PAR :	VÉRIFIÉ PAR : D. VINCENT, ing.
PROJET No : P0002920	DESIGN No : T-D410
FEUILLE No : 5 DE 11	

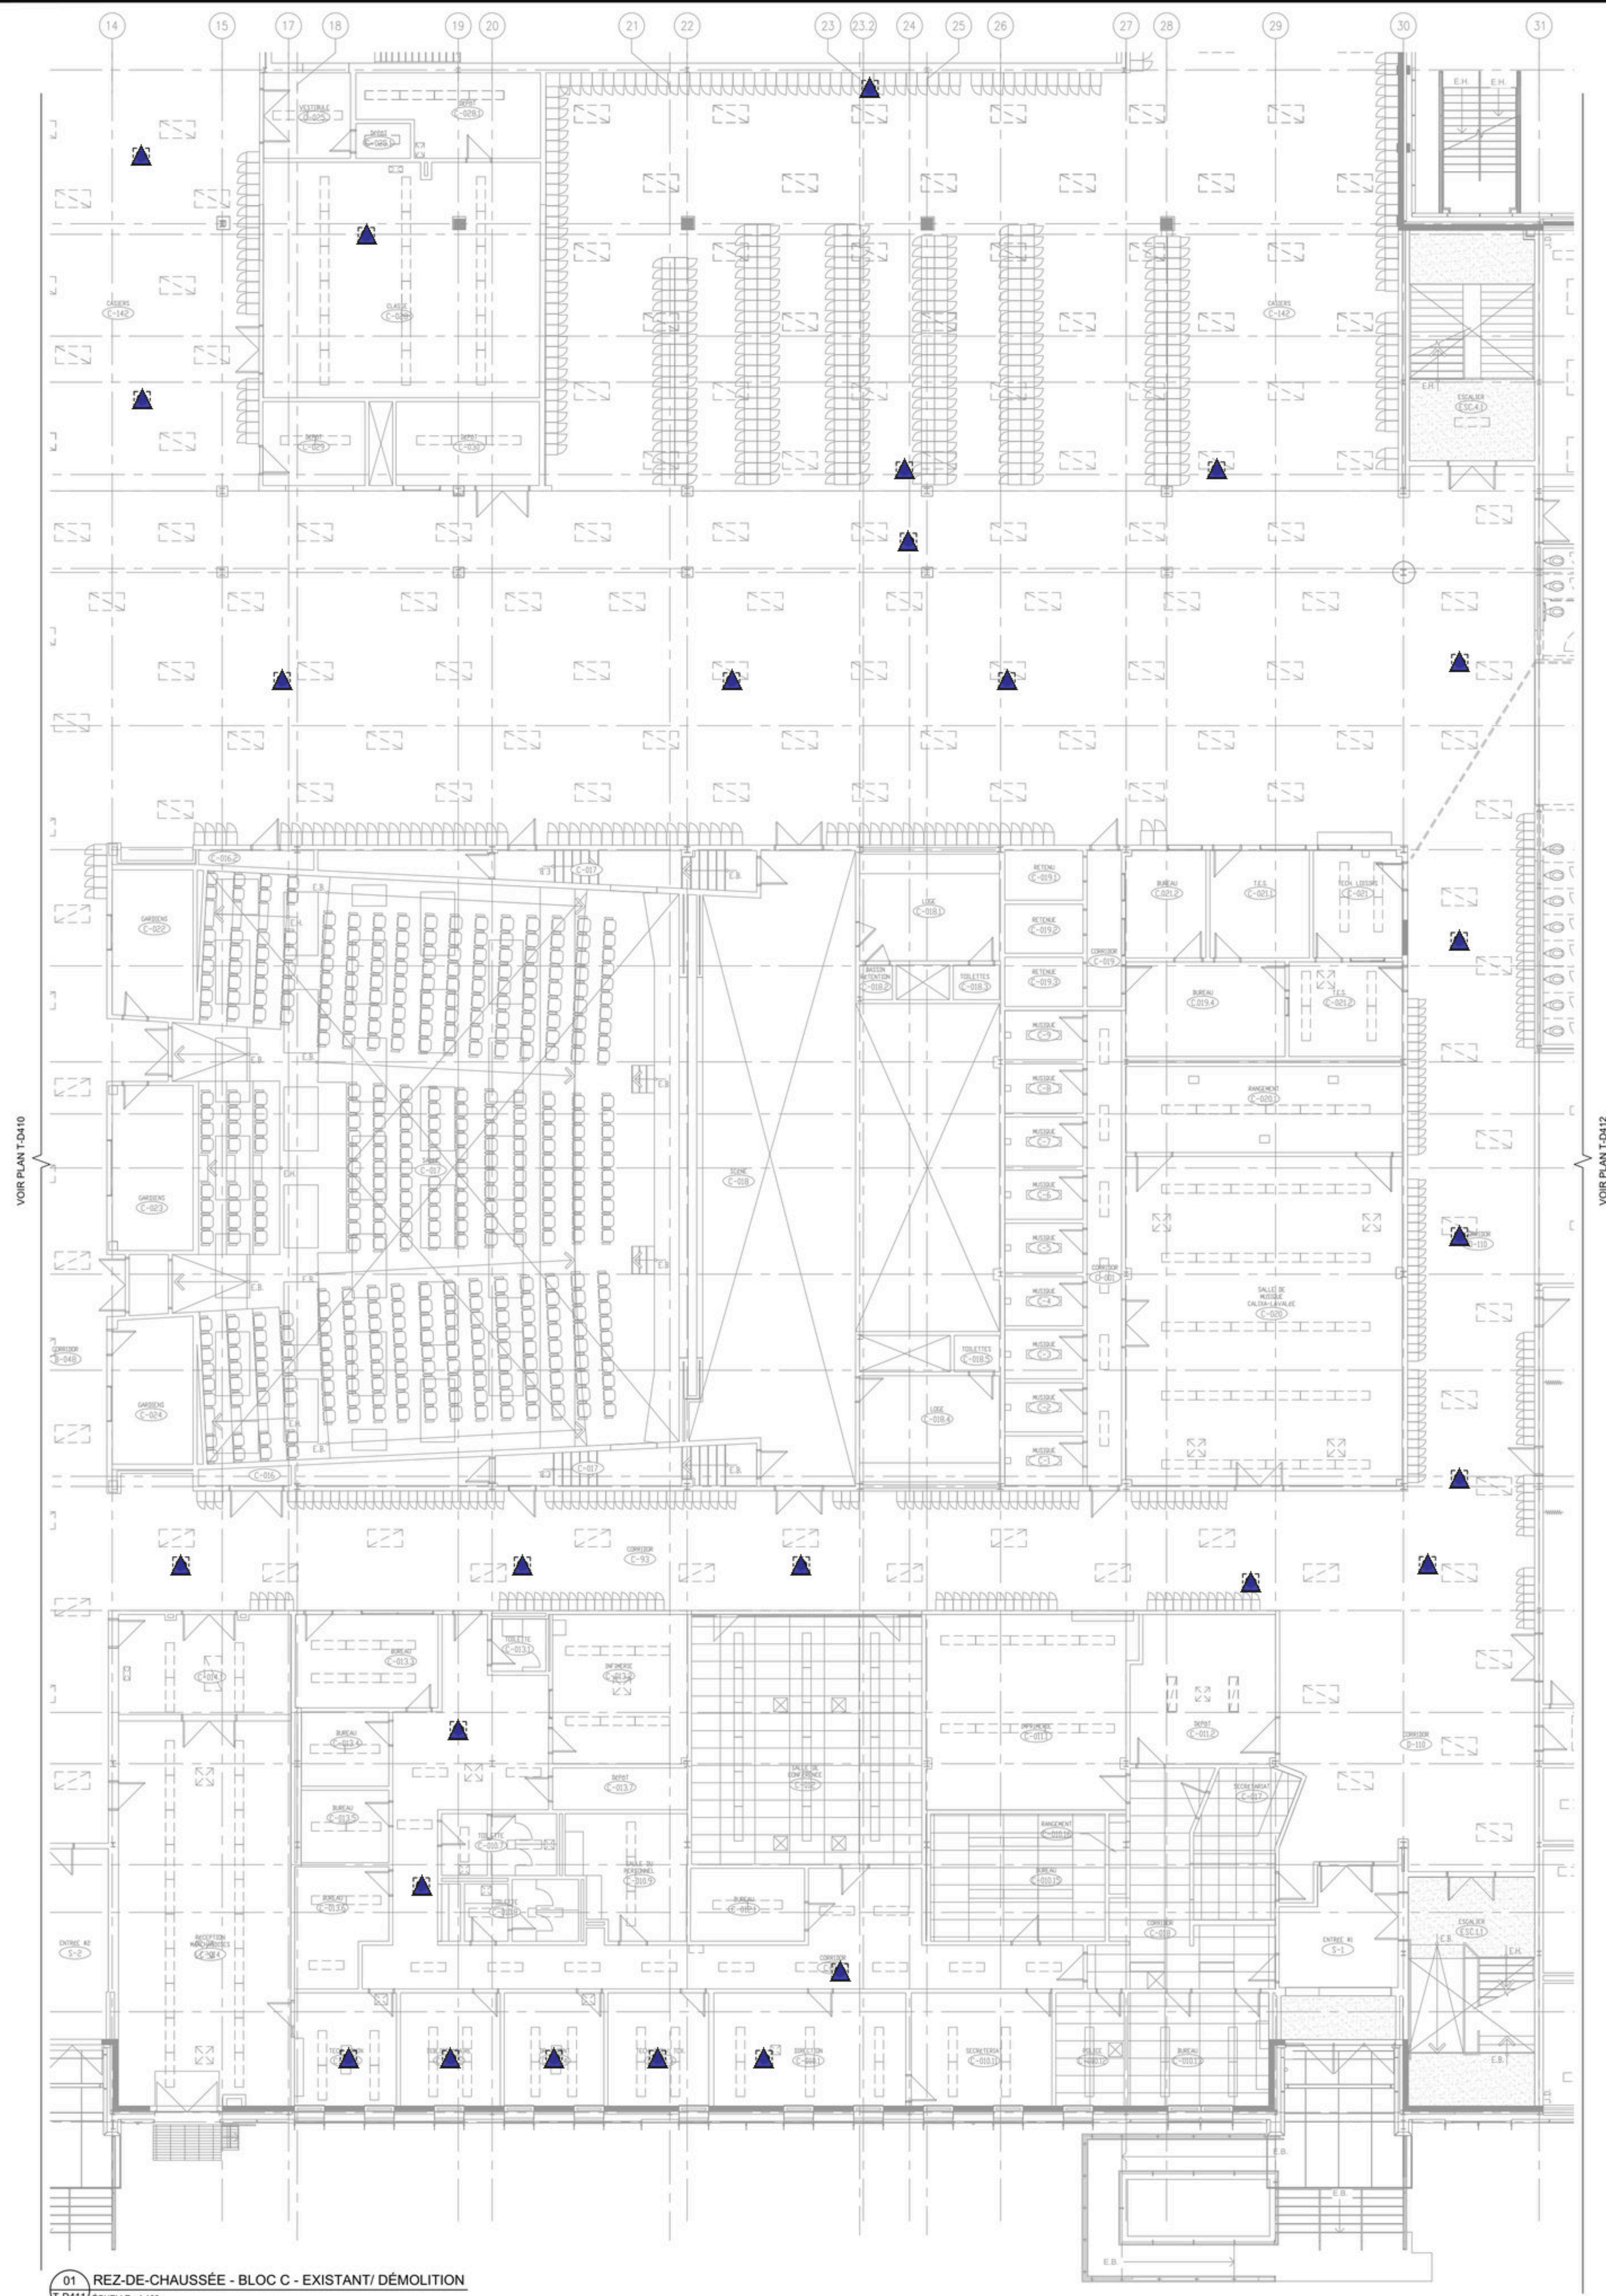

NOTES GÉNÉRALES:

- HAITI PARLEURS SE TROUVANT DANS LES LOCAUX B, C ET C1
 RETIENNES DURANT LE TRAVAIL DE DEMOLITION POUR
 REINSTAUTES LOUS DU REAMENAGEMENT. RENCOUNTER
 LES TRAVAILLEURS HAITI PARLEURS
- AUCUN CÂBLE DE TÉLÉCOMMUNICATION NE DOIT ÊTRE
 DÉMONTÉ DURANT LE TRAVAIL DE DÉMOLITION.
- PORTER UNE ATTENTION PARTICULIÈRE À PROTÉGER LE LIEN DE
 FIBRE OPTIQUE ENTRE LES LOCAUX B-111 ET C-12.
- SE RÉFÉRER AU DSS DE DÉLECTRICITE POUR LES CONDITIONS
 GÉNÉRALES ET LES DÉFINITIONS ADDITIONNELLES
- LES CAMÉRAS BORNES VU, PROJECTEUR ET
 HAITI PARLEURS DE CLASSEMENT. S'ASSURER QUE LES
 TRAVAIL ET ENTREPRISES PAR LE CSS POUR LA DURÉE DES
 TRAVAUX.

TOUTES LES IDENTIFICATIONS EXISTANTES SUR LES GRILLES DU
 FOND AU FONDILLANT. JANTES, BULEX ET RIGIDES
 REPRÉSENTENT L'EMPLACEMENT DES BORNES VU, DES
 BORNES MÉCANIQUES ET DES BORNES ÉLECTRIQUES. LES
 CONSERVÉES DURANT LE TRAVAIL DE DÉMOLITION



Légende — D411 (27 marques)

▲ Haut-parleur existant — dépose/entrepasage (27)

CE DOCUMENT NE DOIT
PAS ÊTRE UTILISÉ À DES
FINS DE CONSTRUCTION

0	2026-07-08	EMIS POUR APPEL D'OFFRES	D.V.
No.	Date	Description	Par




CIMA+ 900-740, rue Notre-Dame Ouest
Montreal QC H3C 3X6
CANADA
T 514 337-2462
F 514 281-1632
cima.ca

CENTRE DE SERVICES
SCOLAIRE DE
SOREL-TRACEY


RÉHABILITATION ET TRAVAUX
CONNEXES
ÉCOLE SECONDAIRE BERNARD-GARIÉPY

**TÉLÉCOMMUNICATIONS
DÉMOLITION PHASE 1
REZ-DE-CHAUSSÉE
EXISTANT / DÉMOLITION**

DISCIPLINE :		TÉLÉCOMMUNICATIONS	
VOSSE PAR : C-A. GRAVEL		BONNELL : INDIQUE	
CONCIS PAR : A. SY, tech.		DATE : 2026-04-17	
VOSSE PAR :		VOSSE PAR : D. VINCENT, ing.	
PROJET No : P0002920		DESIGN No : T-D411	
FEUILLE No : 6 DE 11			

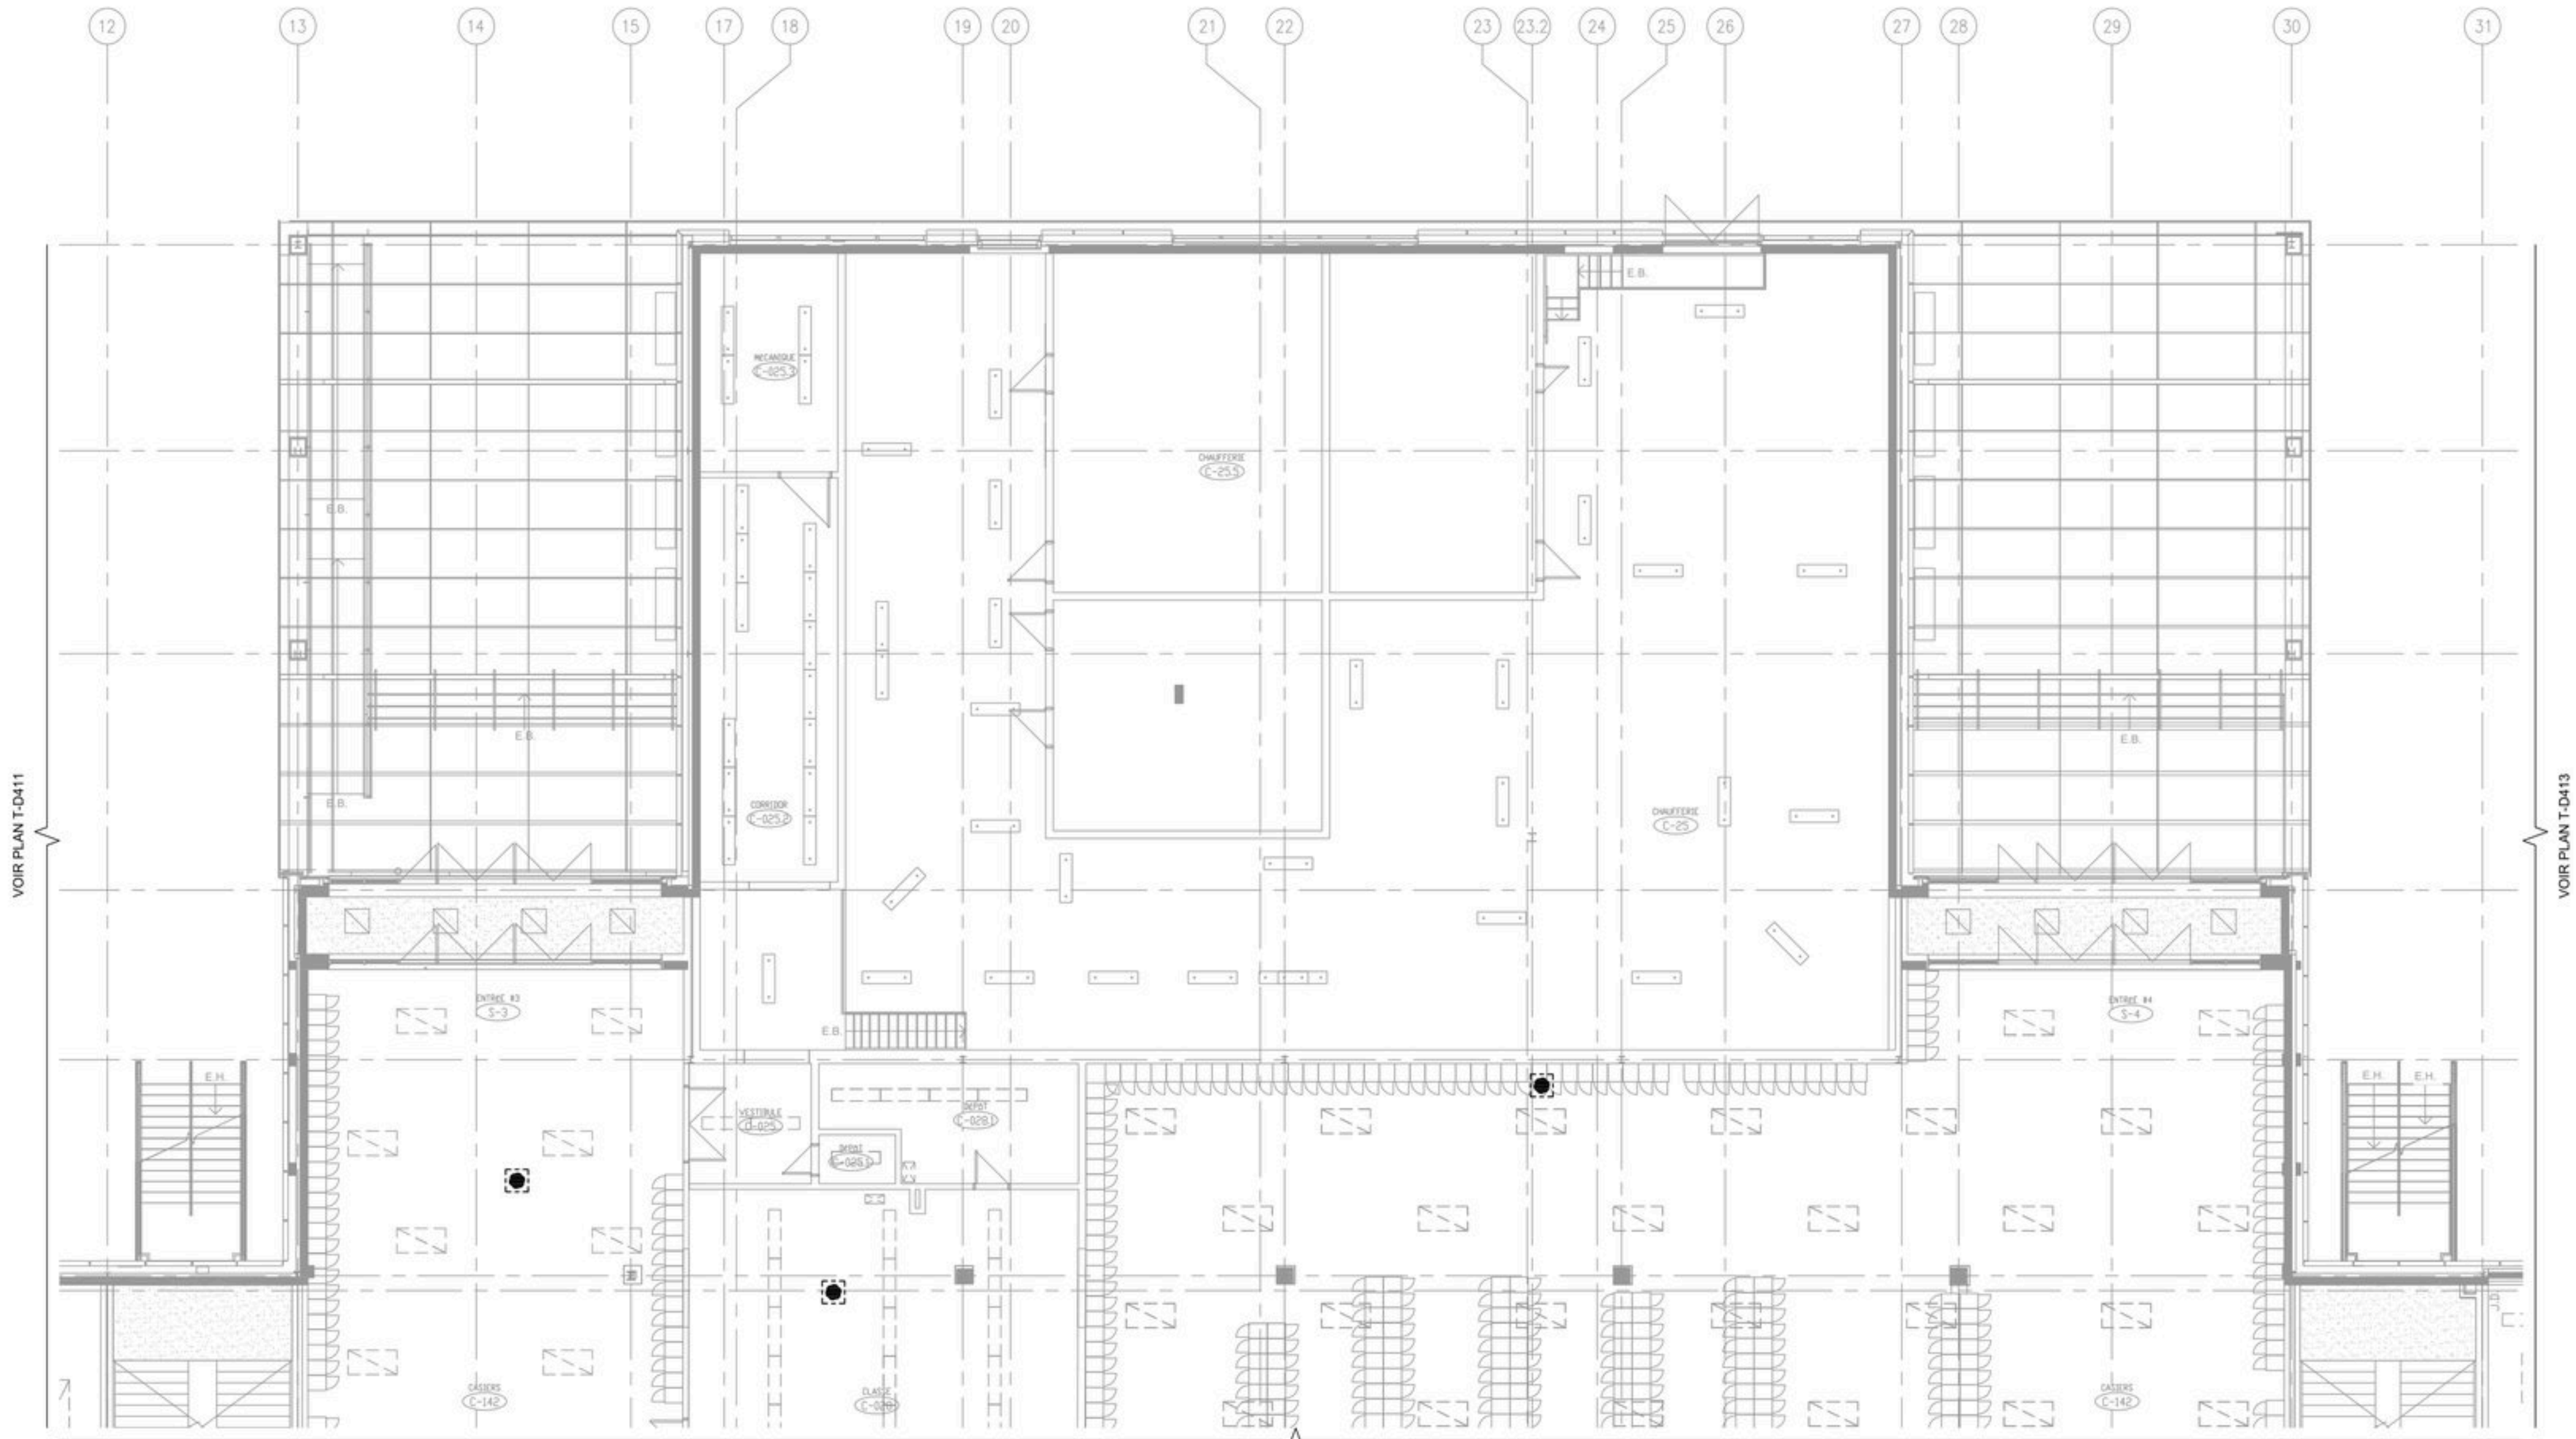


01 REZ-DE-CHAUSSEE - BLOC C1 - EXISTANT/ DÉMOLITION
T-D412/ ÉCHELLE : 1:100

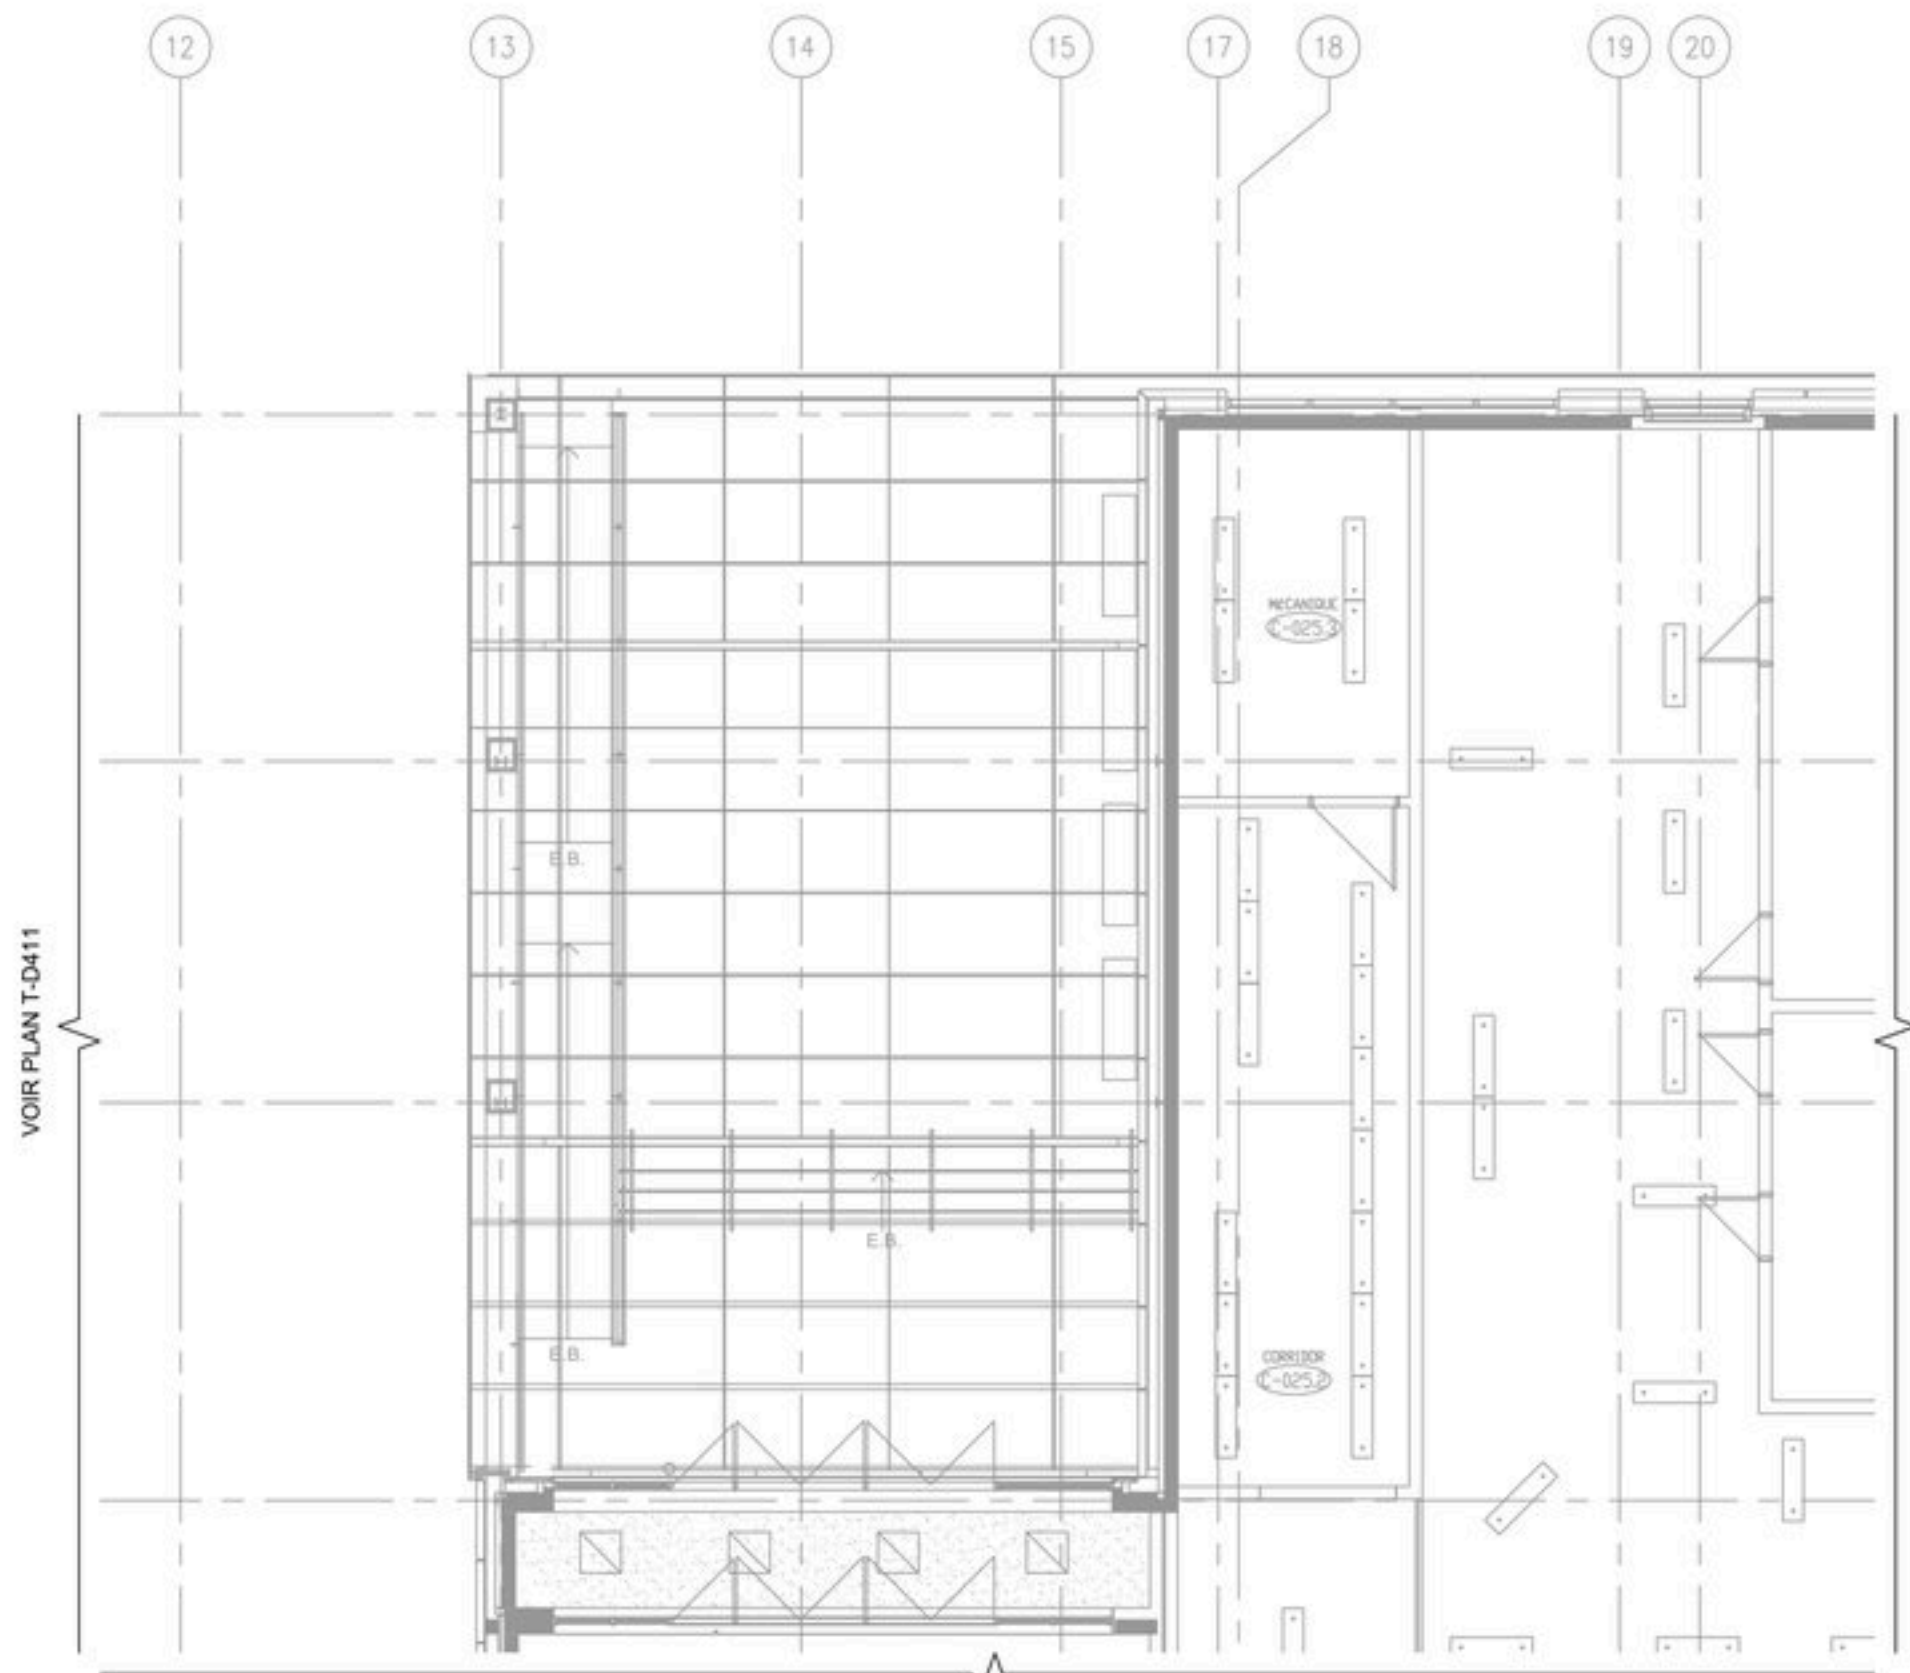

01 EXTRAIT SALLE ÉLECTRIQUE - REZ-DE-CHAUSSEE - BLOC C1 - EXISTANT/ DÉMOLITION
T-D412/ ÉCHELLE : 1:100

NOTES GÉNÉRALES:

- LES HAUT-PARLEURS SE TROUVANT DANS LES BLOCS B, C ET C1 SERONT RETIRÉS DURANT LES TRAVAUX DE DÉMOLITION PUIS RÉINSTALLÉS LORS DU RÉAMÉNAGEMENT. L'ENTREPRENEUR DEVRA ENTREPOSER LES HAUT-PARLEURS.
- AUCUN CÂBLE DE TÉLÉCOMMUNICATION NE DOIT ÊTRE DÉMANTÉLÉ DURANT LES TRAVAUX DE DÉMOLITION.
- PORTER UNE ATTENTION PARTICULIÈRE À PROTÉGER LE LIEN DE FIBRE OPTIQUE ENTRE LES LOCAUX B-111.4 ET D-132.2.
- SE RÉFÉRER AU DEVS D'ÉLECTRICITÉ POUR LES CONDITIONS GÉNÉRALES ET LES DÉFINITIONS ADDITIONNELLES.
- LES CAMÉRAS, BORNES WI-FI, PROJECTEURS ET HAUT-PARLEURS DE CLASSE SERONT RETIRÉS AVANT LES TRAVAUX ET ENTREPOSÉS PAR LE CSS POUR LA DURÉE DES TRAVAUX.
- TOUTES LES IDENTIFICATIONS EXISTANTES SUR LES GRILLES DU PLAFOND (AUTOCOLLANTS JAUNES, BLEUS ET ROUGES) REPRÉSENTANT L'EMPLACEMENT DES BORNES WI-FI, DES VALVES MÉCANIQUES ET DE L'ÉCLAIRAGE 24H DOIVENT ÊTRE CONSERVÉES DURANT LES TRAVAUX DE DÉMOLITION.

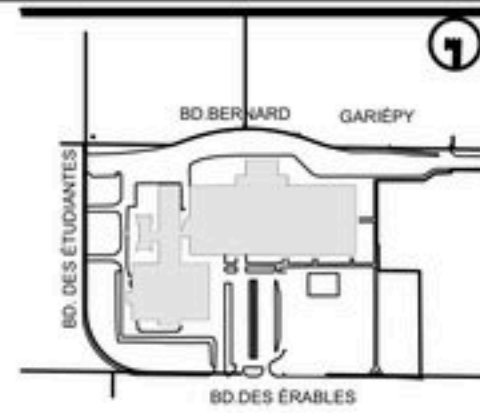

leclerc
architectes

380, rue St-Jacques, #1010, St-Jacques, Québec, QC H3A 2B2
T 514 382 8870

CE DOCUMENT NE DOIT PAS ÊTRE UTILISÉ À DES FINS DE CONSTRUCTION

No.	Date	Description	Par
0	2020-07-08	ÉMISSION POUR APPEL D'OFFRES	D.V.



CIMA+
800-762-1162, rue Notre-Dame Ouest
Montréal, QC H3C 3A8
CANADA
T 514 337 0462
F 514 381 1632
cima.ca


CENTRE DE SERVICES
SCOLAIRE DE
SOREL-TRACEY

RÉHABILITATION ET TRAVAUX
CONNEXES
ÉCOLE SECONDAIRE BERNARD-GARIÉPY

TÉLÉCOMMUNICATIONS
DÉMOLITION PHASE 1
REZ-DE-CHAUSSEE
EXISTANT / DÉMOLITION

TÉLÉCOMMUNICATIONS

DESSIN PAR C.A. GRAVEL	REVÊLU INDIGUE
APProuvé PAR A. SY, tech.	DATE 2020-04-17
VERIFIÉ PAR D. VINCENT, ing.	DESSIN PAR D. VINCENT, ing.
PROJET PAR P0002020	DESSIN PAR T-D412

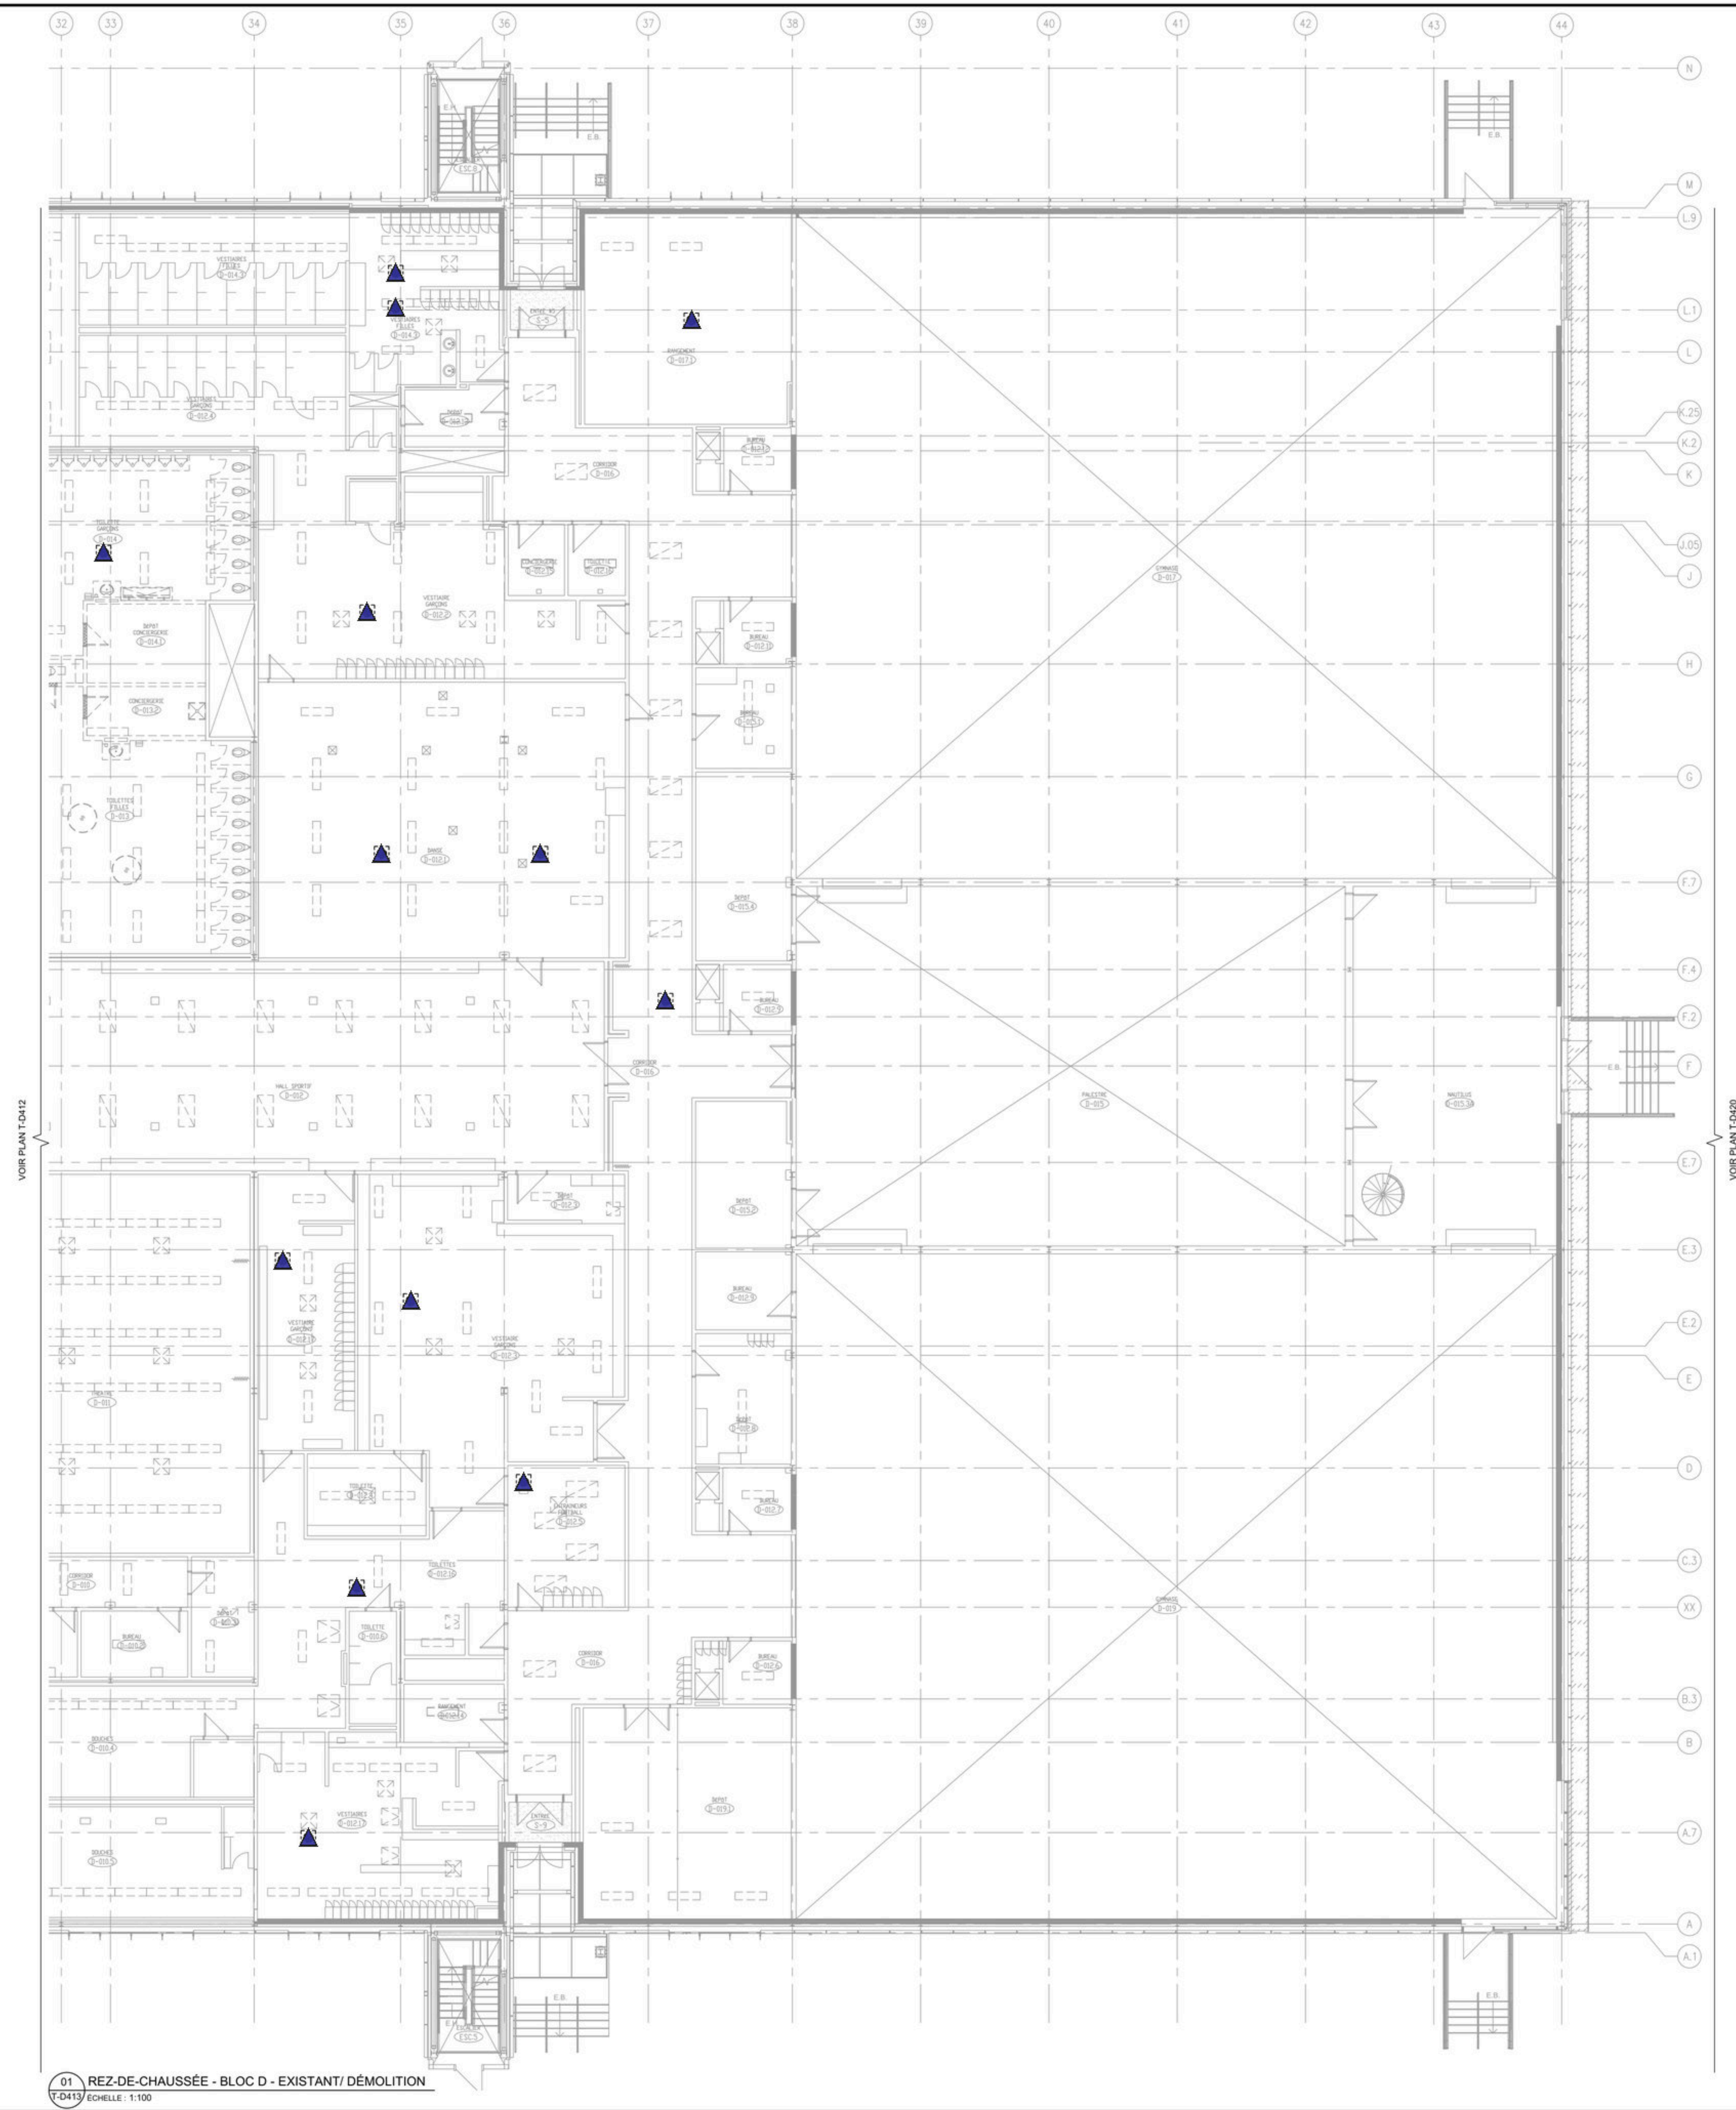

NOTES GÉNÉRALES:

- LES HAUT-PAIRELLEURS DANS LE BLOC D DOIVENT ÊTRE DÉMANTÉLÉS LORS DES TRAVAUX DE DÉMOLITION. CES HAUT-PAIRELLES NE DOIVENT PAS ÊTRE ENTREPOSÉES DURANT LES TRAVAUX.
- AUCUN CÂBLE DE TÉLÉCOMMUNICATION NE DOIT ÊTRE DÉMANTÉLÉ DURANT LES TRAVAUX DE DÉMOLITION.
- SE RÉFÉRER AU DEVIS ÉLECTROTECHNIQUE POUR LES CONDITIONS GÉNÉRALES ET LES DÉFINITIONS ADDITIONNELLES
- LES CAMÉRAS, BORNES W-FI, PROJECTEURS ET HAUT-PAIRELLEURS DE CLASSE SONT RETIRÉS AVANT LES TRAVAUX ET ENTREPOSÉS PAR LE CSS POUR LA DURÉE DES TRAVAUX.
- TOUTES LES IDENTIFICATIONS EXISTANTES SUR LES GRILLES DU PAVILLON AUTOCOLLANTS JAUNES, BLEUS ET ROUGES) REMPLACER L'EMPLOI DES BORNES W-FI, DES RESEAU MEGANETIX ET DE LEÇALIMAGE SONT DOIVENT ÊTRE CONSERVÉES DURANT LES TRAVAUX DE DÉMOLITION.



Légende — D413 (13 marques)

▲ Haut-parleur existant — dépose/entrepasage (13)

CE DOCUMENT NE DOIT
PAS ÊTRE UTILISÉ À DES
FINIS DE CONSTRUCTION

0	2026-07-08	EMIS POUR APPEL D'OFFRES	D.V.
N ^o .	Date	Description	Par



CIMA+

CENTRE DE SERVICES
SCOLAIRE DE
SOREL-TRACEY

RÉHABILITATION ET TRAVAUX
CONNEXES
ÉCOLE SECONDAIRE BERNARD-GARIÉPY

TÉLÉCOMMUNICATIONS
DÉMOLITION PHASE 1
REZ-DE-CHAUSSÉE
EXISTANT / DÉMOLITION

DISCIPLINE		TÉLÉCOMMUNICATIONS	
DESSINÉ PAR : C-A. GRAVEL		BOULELLE INDIQUE	
CONÇU PAR : A. SY, tech.		DATE 2026-04-17	
VÉRIFIÉ PAR :		VÉRIFIÉ PAR : D. VINCENT, ing.	
PROJET No : P0002920		DESSIN No :	
ÉVALUÉ No :		T-D413	



01 ÉTAGE - BLOC B - EXISTANT/ DÉMOLITION
T-D420 ÉCHELLE : 1:100

NOTES GÉNÉRALES:

- LES HAUT PAVILLONS SE TROUVANT DANS LES BLOCS B, C ET CI SERONT RETIRÉS DANS LES TRAVAUX DE DÉMOLITION PLUS RÉGÉNÉRATION LORS DU RÉAMÉNAGEMENT. L'ENTREPRISE POURRA ENVOYER LES HAUT PAVILLONS
- AUCUN CÂBLE DE TÉLÉCOMMUNICATION NE DOIT ÊTRE DÉMANTÉLÉ DURANT LES TRAVAUX DE DÉMOLITION.
- PORTER L'ATTENTION PARTICULIÈRE À PROTÉGER LE LIEN DE FIBRE OPTIQUE ENTRE LES HAUT PAVILLONS
- SE RÉFÉRER AU PLAN DES DÉLÉCTRICITE POUR LES CONDITIONS GÉNÉRALES ET LES DÉFINITIONS ADDITIONNELLES
- LES CAMÉRAS, BONNES W-LF, PROJECTEURS ET HAUT PAVILLONS DE CLASSE SERONT RETIRÉS AVANT LA FIN DES TRAVAUX ET ENTREPOSÉS PAR LE CDS POUR LA DURÉE DES TRAVAUX
- TOUTES LES IDENTIFICATIONS EXISTANTES SUR LES GRILLES DU PNEU ET DES CROCHETS (BLOCS B, C ET CI) SERONT DÉMANTÉLÉES. LES IDENTIFICATIONS DES BLOCS B, C ET CI REPRÉSENTANT L'EMPLACEMENT DES BONNES W-LF, DES VALVES MÉCANIQUE ET DE L'ÉCLAIRAGE D'ÂGE DOIVENT ÊTRE CONSERVÉES DURANT LES TRAVAUX DE DÉMOLITION.

NOTE SPÉCIFIQUE:

○ L'ENTREPRENEUR DOIT PROTÉGER LE CÂBLE DE LA SALLE B-1114 EN PASSANT PAR S-500 ET B-1166.



Légende — D420_ADD (38 marques)

▲ Haut-parleur existant — dépose/entreposage (38)

CE DOCUMENT NE DOIT
PAS ÊTRE UTILISÉ À DES
FINS DE CONSTRUCTION

1	2026-06-18	ADDENDA T-01			D/
0	2026-07-08	EMIS POUR APPEL D'OFFRES			D/
No.	Date	Description			Pa



CIMA+


CENTRE DE SERVICES
SCOLAIRE DE
SOREL-TRACEY

RÉHABILITATION ET TRAVAUX
CONNEXES
ÉCOLE SECONDAIRE BERNARD-GARIÉPY

TÉLÉCOMMUNICATIONS
DÉMOLITION PHASE 1 ÉTAGE
EXISTANT / DÉMOLITION

DISCIPLINE : **TÉLÉCOMMUNICATIONS**

DESSIN PAR : C-A. GRAVEL	ECHELLE : INDIQUEE
CONÇU PAR : A. SY, tech.	DATE : 2026-04-17
VERIFIE PAR :	VERIFIE PAR : D. VINCENT, ing.
PROJET No : P0002920	DESSIN No : T-D420
FEUILLE No :	

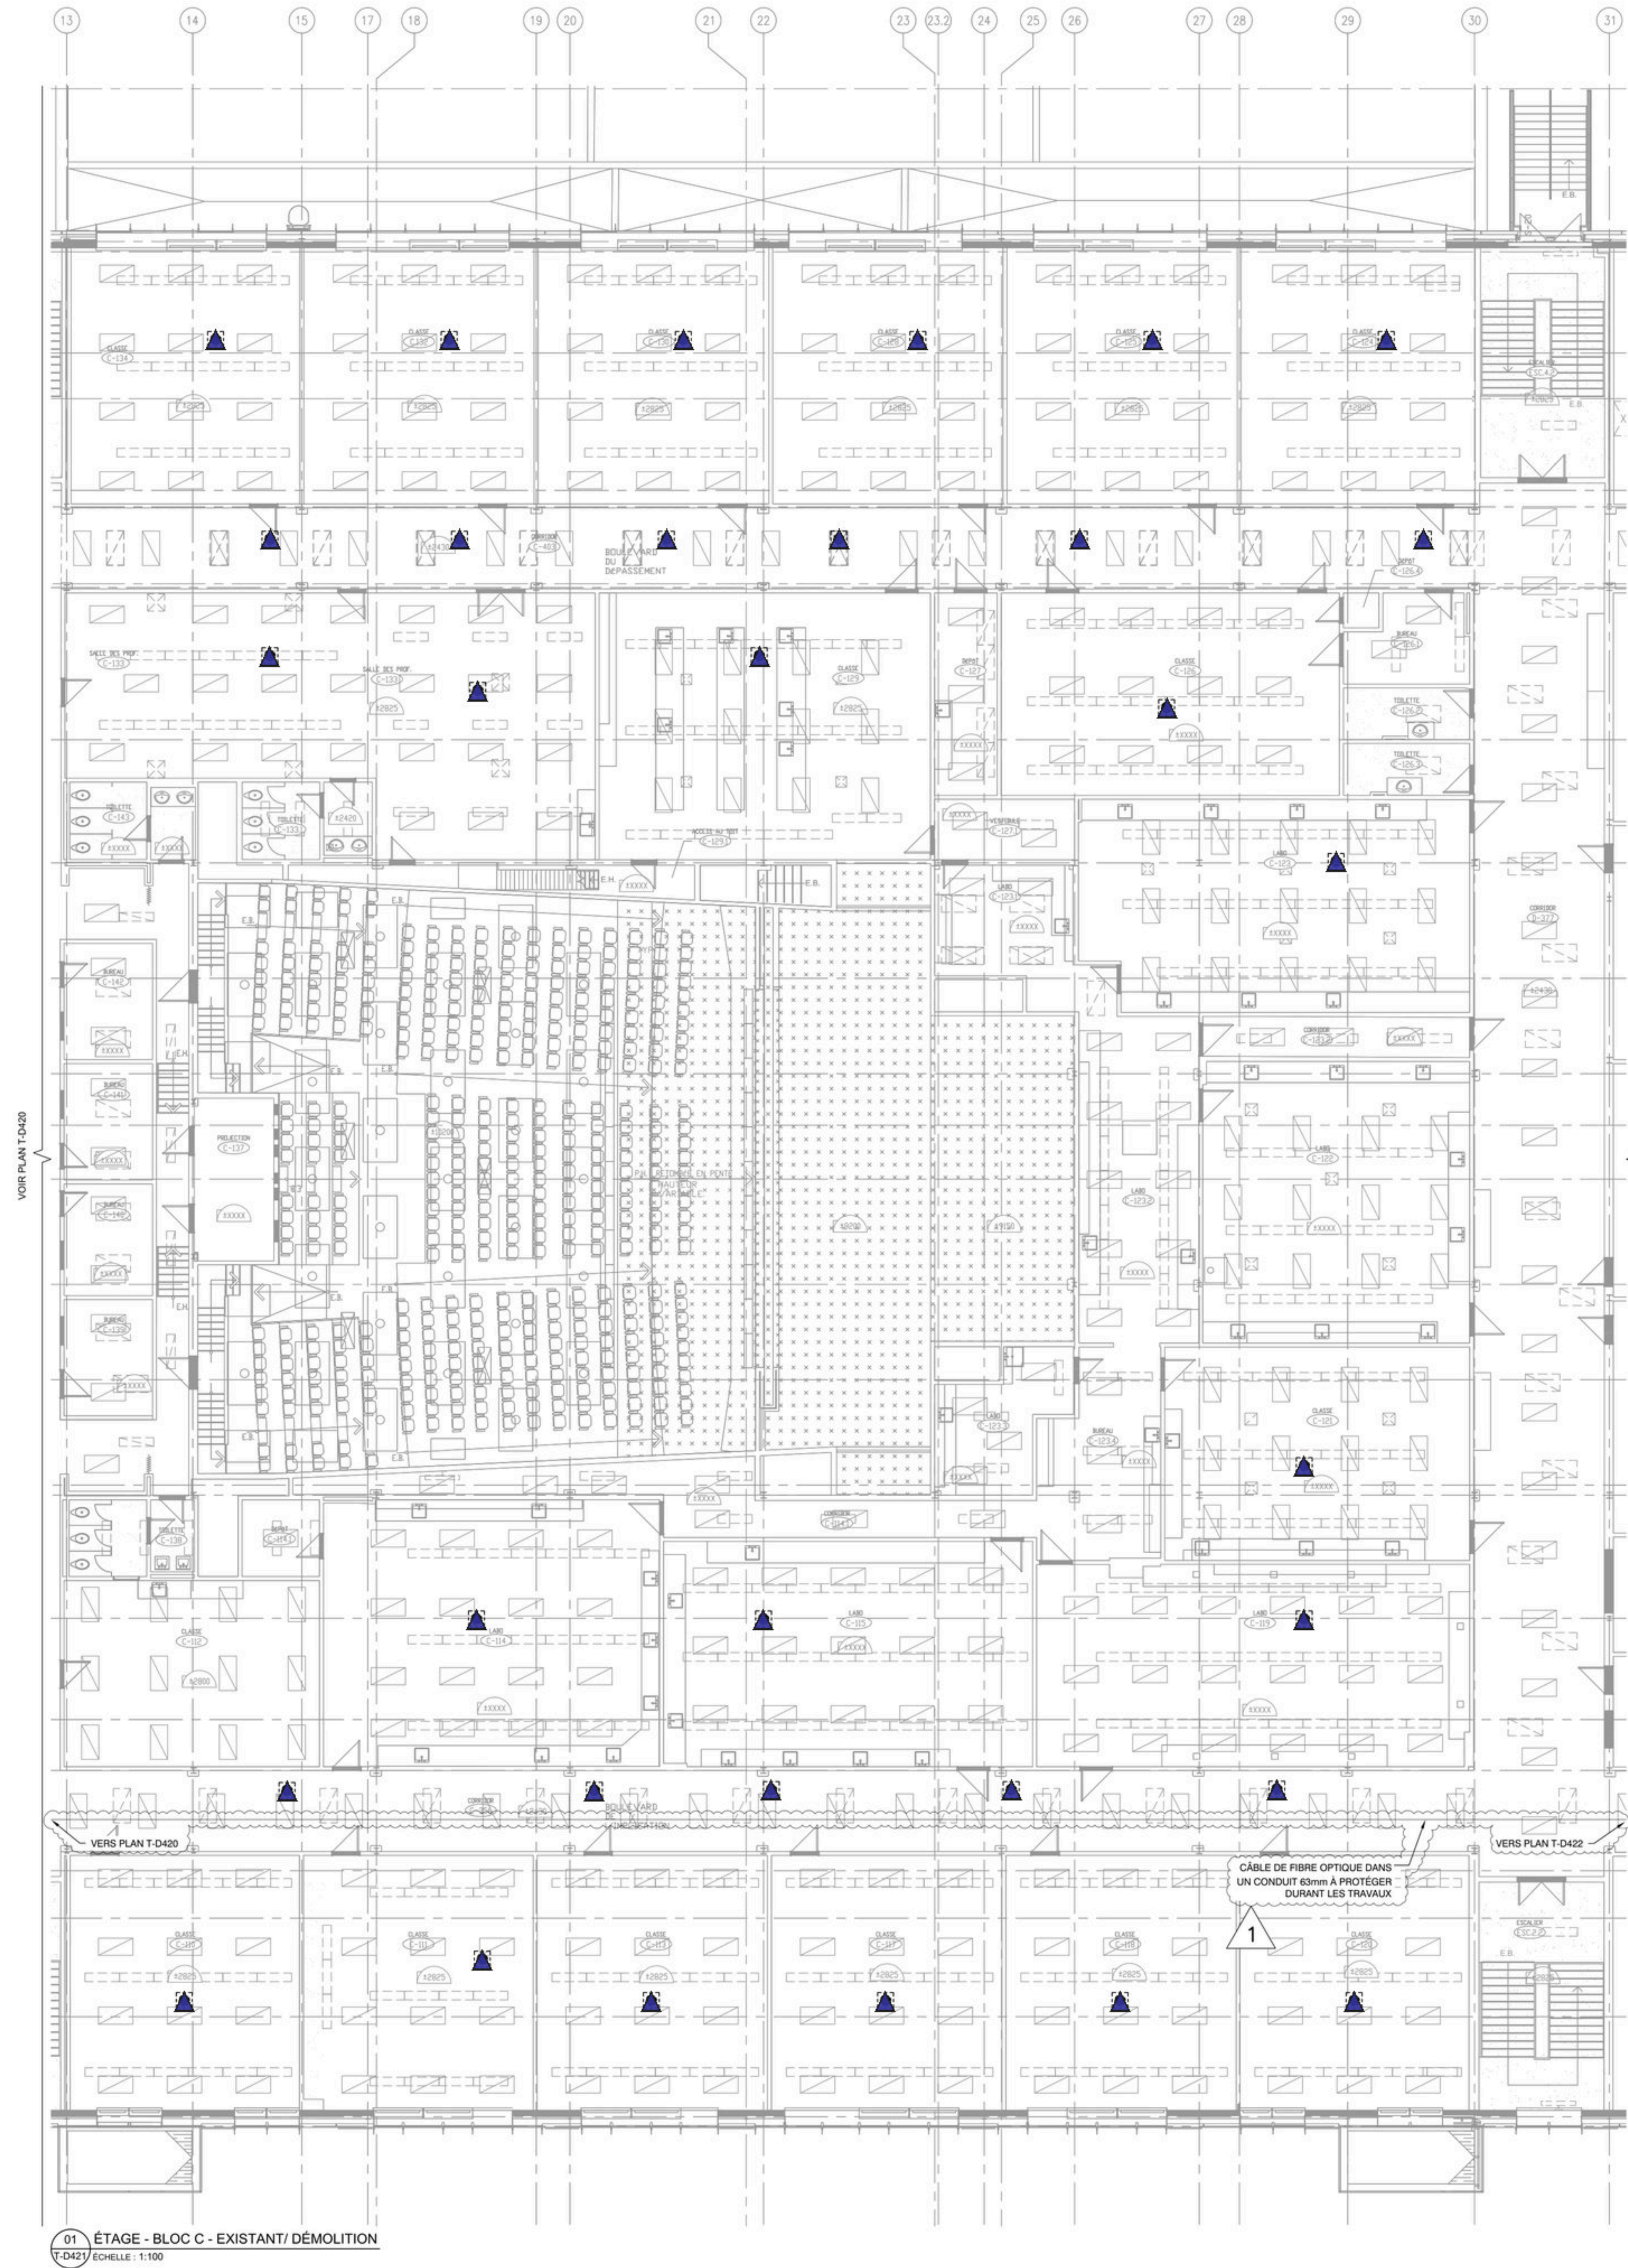

NOTES GÉNÉRALES:

- LES HAUT PARLERS SE TROUVANT DANS LES BLOCS B, C ET C1 SONT RETIRÉS DURANT LES TRAVAUX DE DÉMOLITION PLUS RÉNÉRALISÉS LOU DU RÉAMÉNAGEMENT L'ENTREPRENEUR DEVRA DÉMANTÉLER LES HAUTS PARLERS EN 2017
- AUCUN CÂBLE DE TÉLÉCOMMUNICATION NE DOIT ÊTRE DÉMANTÉ DURANT LES TRAVAUX DE DÉMOLITION.
- PORTER UNE ATTENTION PARTICULIÈRE À PROTÉGER LE LIEN DE FIBRE OPTIQUE ENTRE LES LOCALUX B-111 ET A-D-132-2.
- SE RÉFÉRER AU DVS DÉLECTROPHORE POUR LES CONDITIONS GÉNÉRALES ET LES DÉFINITIONS ADDITIONNELLES
- LES CAMÉRAS BORNES HAUT, PROJECTEURS ET HAUT PARLERS SONT À DÉMANTÉLER AVANT LES TRAVAUX ET ENTROUSSES PAR CES POUR LA DURÉE DES TRAVAUX
- TOUTES LES IDENTIFICATIONS EXISTANTES SUR LES GRILLES DU PLAFOND AUTOCLONANTES (JAUNES, BLEUS ET ROUGES) REPRÉSENTENT L'EMPLACEMENT DES BORNES HAUT, DES VALS ET PROJECTEURS ET DE L'ÉCLAIRAGE SHIMMER SONT CONSERVÉES DURANT LES TRAVAUX DE DÉMOLITION



Légende — D421_ADD (32 marques)

▲ Haut-parleur existant — dépose/entrepasage (32)

CE DOCUMENT NE DOIT
PAS ÊTRE UTILISÉ À DES
FINIS DE CONSTRUCTION

1	2026-08-18	ADDENDA T-01	D.V.
0	2026-07-08	EMIS POUR APPEL D'OFFRES	D.V.
No.	Date	Description	Par



CIMA+ 900-360, rue Notre-Dame Ouest
Montréal QC H3C 3K6
CANADA
T 514 337-2462
F 514 291-1632
cima.ca

CENTRE DE SERVICES
SCOLAIRE DE
SOREL-TRACEY

RÉHABILITATION ET TRAVAUX
CONNEXES
ÉCOLE SECONDAIRE BERNARD-GARIÉPY

TÉLÉCOMMUNICATIONS
DÉMOLITION PHASE 1 ÉTAGE
EXISTANT / DÉMOLITION

TÉLÉCOMMUNICATIONS

DESIGN PAR : C-A. GRAVEL	REVUE : INDIQUE
CONCU PAR : A. SY, tech.	DATE : 2026-04-17
VERIFIE PAR :	VERIFIE PAR : D. VINCENT, ing.
PROJET No : P0002920	DESSIN No :
FEUILLE No : 10 DE 11	T-D421



CE DOCUMENT NE DOIT
PAS ÊTRE UTILISÉ À DES
FINS DE CONSTRUCTION

[illegible]

1	2026-08-18	ADDENDA T-01	D.V.
0	2026-07-08	ÉMIS POUR APPEL D'OFFRES	D.V.
No.	Date	Description	Par



CIMA+ 900-740, rue Notre-Dame Ouest
Montréal QC H3C 3X6
CANADA
T 514 337-2462
F 514 281-1632
cima.ca

CENTRE DE SERVICES
SCOLAIRE DE
SOREL-TRACEY

RÉHABILITATION ET TRAVAUX
CONNEXES
ÉCOLE SECONDAIRE BERNARD-GARIÉPY

TÉLÉCOMMUNICATIONS
DÉMOLITION PHASE 1 ÉTAC
EXISTANT / DÉMOLITION

DISCIPLINE :		TÉLÉCOMMUNICATIONS	
DESSINÉ PAR : C-A. GRAVEL		RÉVISÉ INDIQUÉ	
CONÇU PAR : A. SY, tech.		DATE : 2025-04-17	
VÉRIFIÉ PAR :		VÉRIFIÉ PAR : D. VINCENT, ing.	
PROJET No : P0002930		DESSIN No : T-D422	
FEUILLE No : 11 DE 11			