




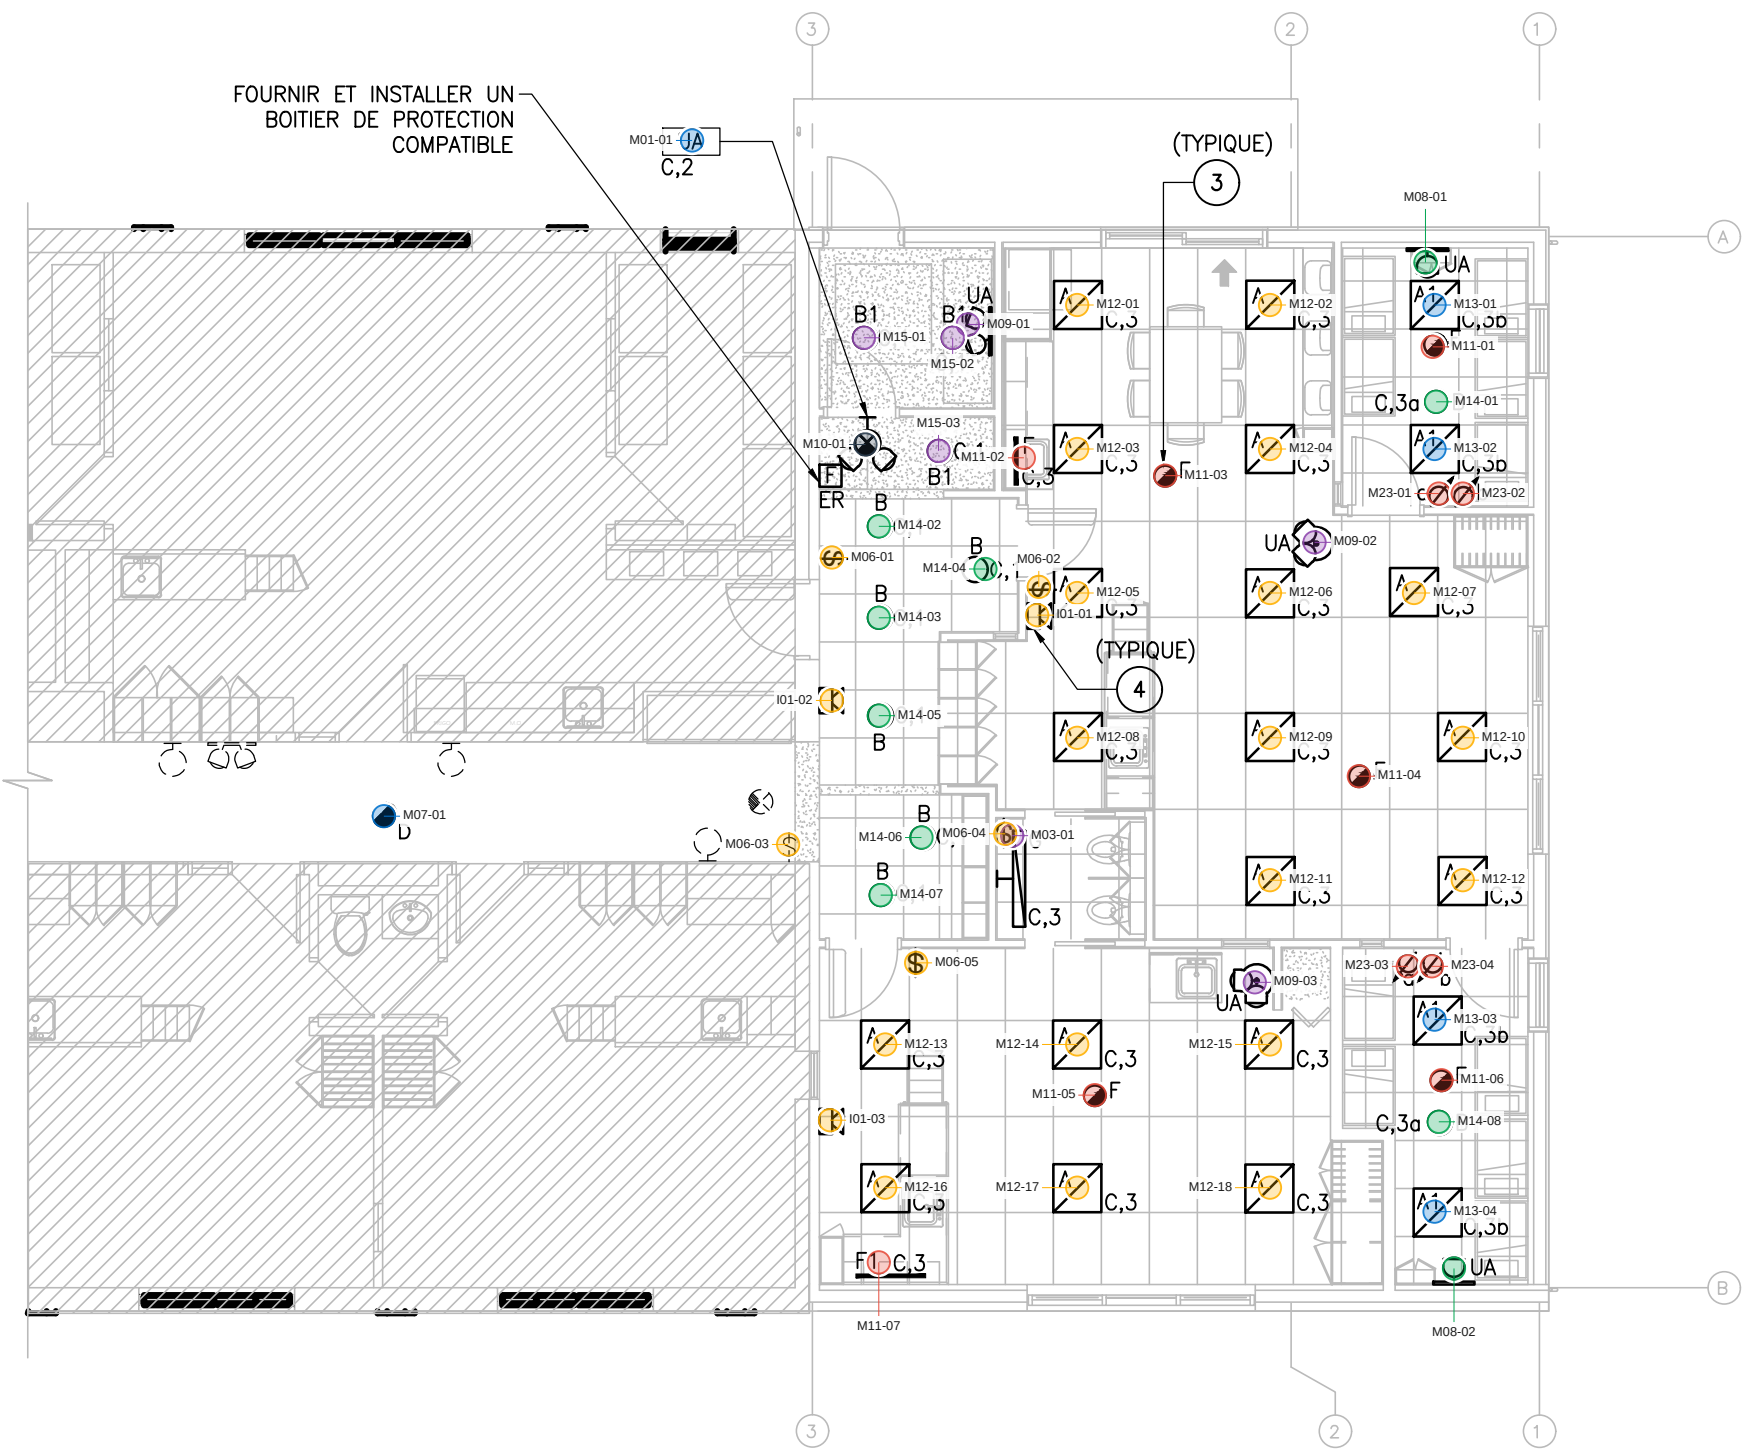


AMÉNAGEMENT - ÉCLAIRAGE ET ALARME INCENDIE
ÉCHELLE 1/8" = 1'-0"

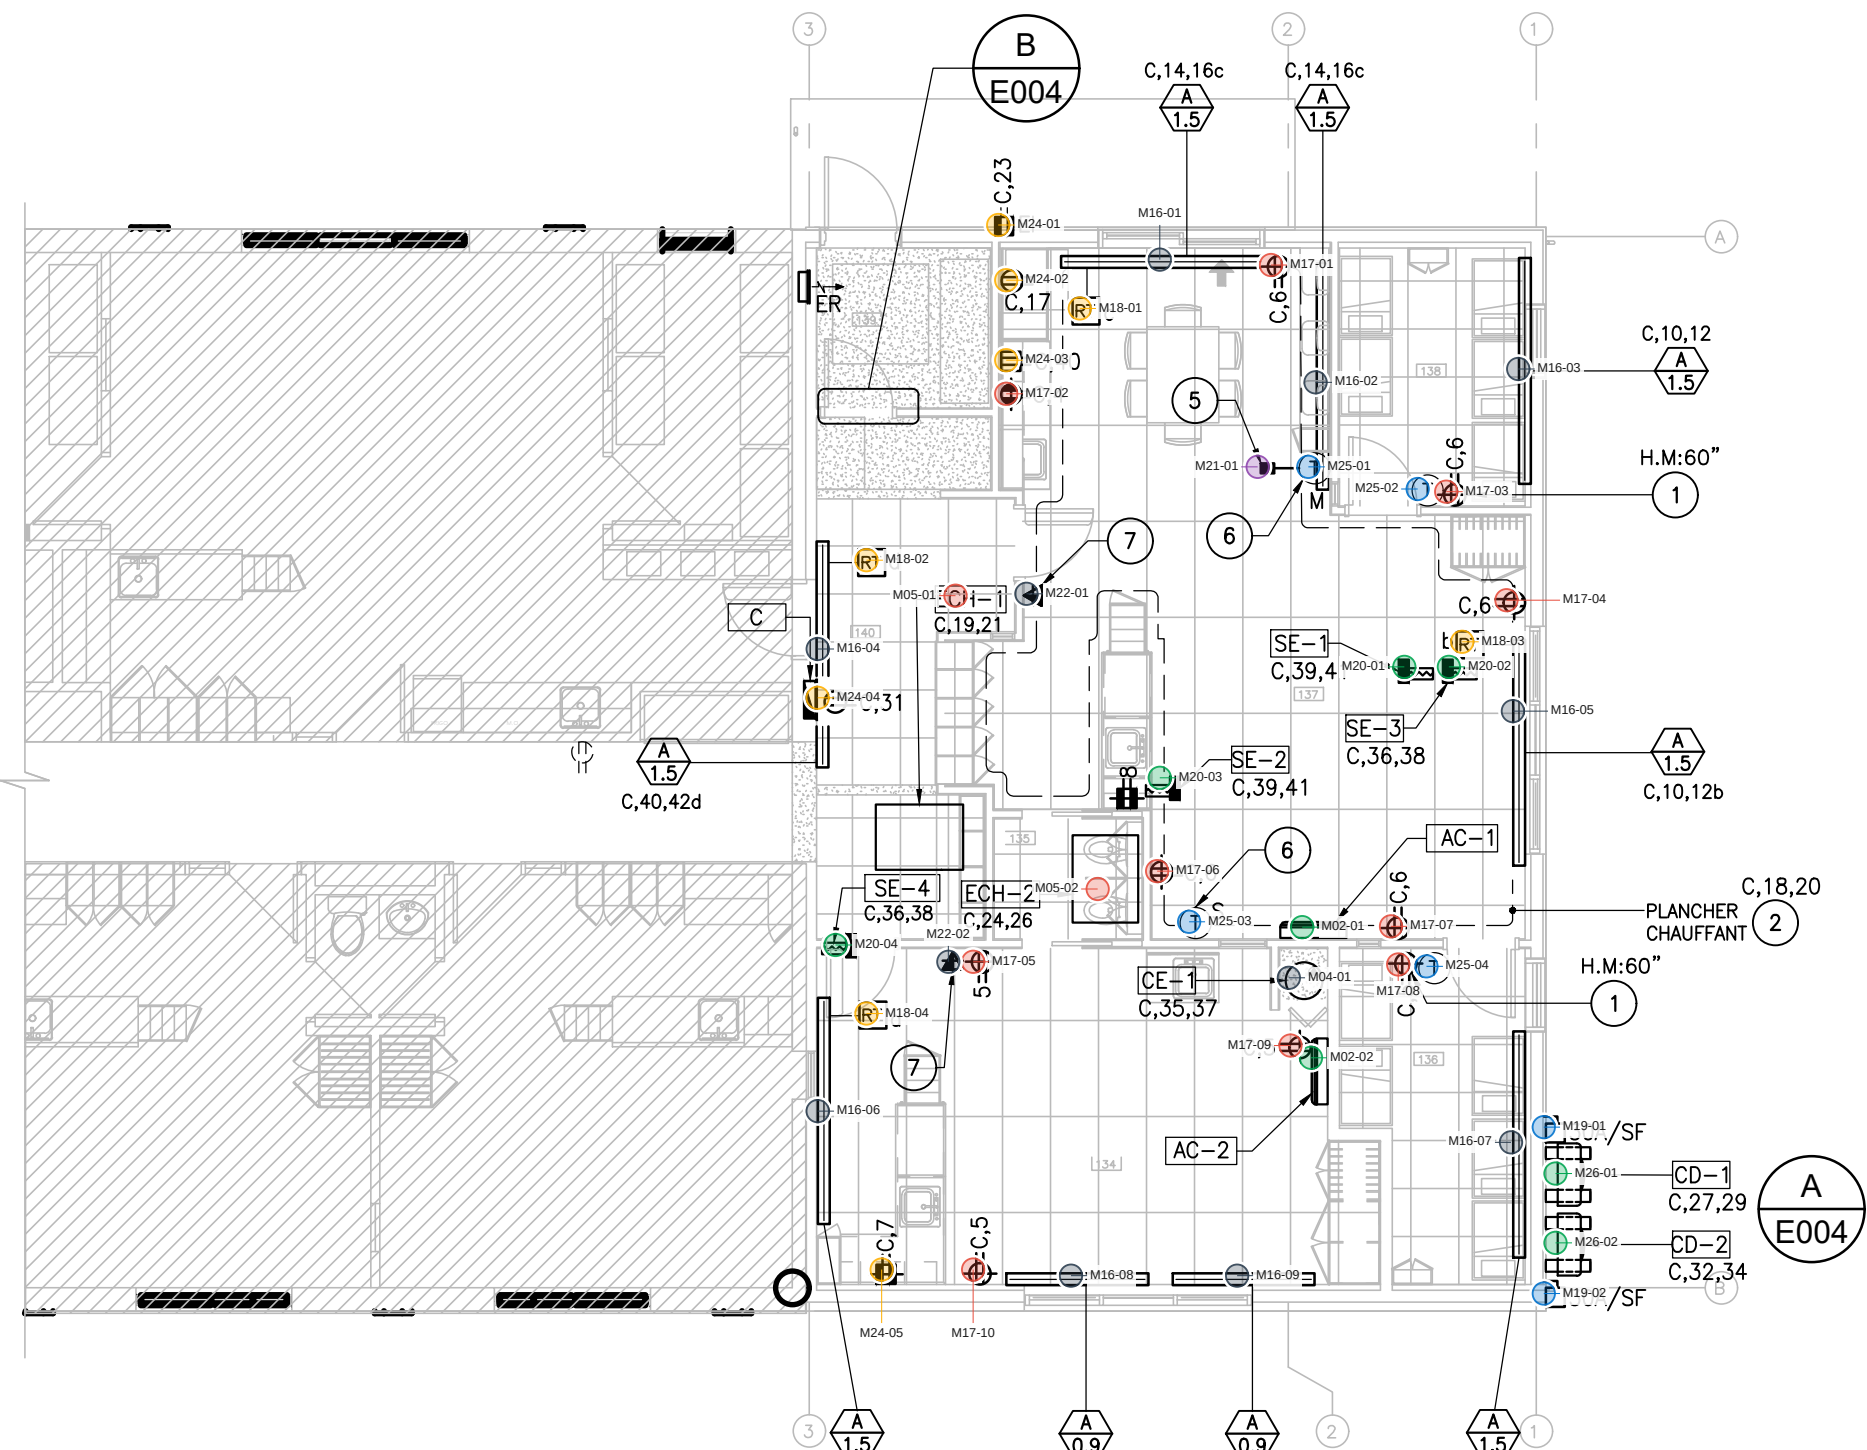

AMÉNAGEMENT - SERVICES
ÉCHELLE 1/8" = 1'-0"

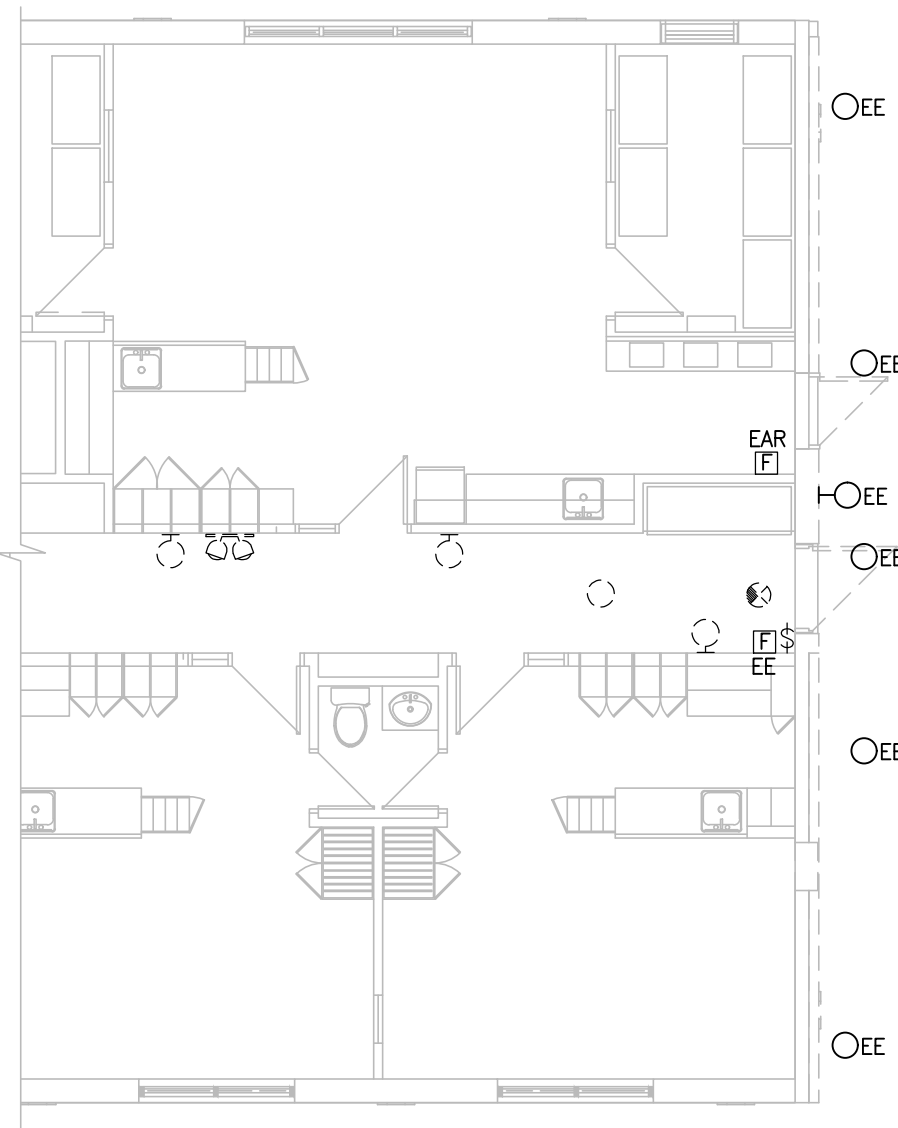

DÉMANTÈLEMENT - ÉCLAIRAGE ET ALARME INCENDIE
ÉCHELLE 1/8" = 1'-0"

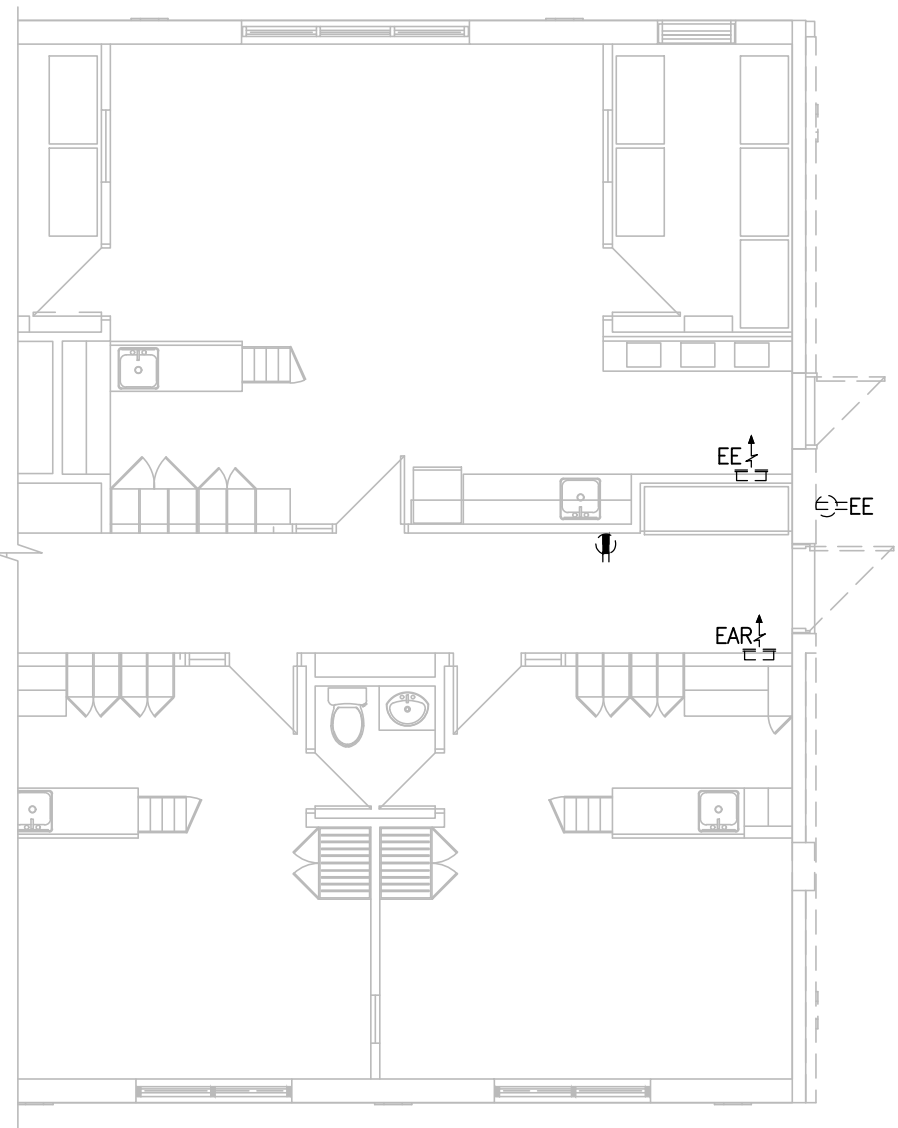

DÉMANTÈLEMENT - SERVICES
ÉCHELLE 1/8" = 1'-0"

NOTES GÉNÉRALES

- A- L'ENTREPRENEUR ÉLECTRICIEN DOIT COORDONNER L'EMPLACEMENT EXACT DES PRISES DANS LES MOBILIERS AVEC LES PLANS D'ARCHITECTURE.
- B- À LA FIN DES TRAVAUX, L'ENTREPRENEUR DOIT METTRE UNE PLAQUE DE RECouvreMENT PLEINE SUR TOUTES LES SORTIES NON UTILISÉES.
- C- LE CONTRÔLE D'ÉCLAIRAGE DOIT ÊTRE FAIT SELON LES INDICATIONS DU DEVIS À L'ARTICLE 2.22 DU DEVIS ÉLECTRIQUE.

NOTES DESCRIPTIVES DES TRAVAUX

- EMPLACEMENT EXACT DE LA PRISE DE COURANT À COORDONNER AVEC LE/LA REPRÉSENTANT(E) DU CPE.
- FOURNIR, INSTALLER ET RACCORDER UN SYSTÈME DE PLANCHER CHAUFFANT TEL QUE OWC-M DE OUELLET 240V, 18" (11W AU PIED CARRE) L'INSTALLATION DU PLANCHER ET LE CONTRÔLE DOIT ÊTRE COORDONNER ET INSTALLÉ SELON LES RECOMMANDATIONS DU MANUFACTURIER. FOURNIR TOUS LES ACCESSOIRES ET DISPOSITIFS POUR UNE INSTALLATION COMPLÈTE ET FONCTIONNELLE. LE PLANCHER DOIT ÊTRE DIVISÉ EN DEUX ZONES DE FAÇON À CE QUE CHAQUE ZONE NE NE SOIT ÊTRE SUPÉRIEUR À 3600W.
- RACCORDER LE DÉTECTEUR DE FUMÉE À LA BOUCLE DE DÉTECTION D'ALARME INCENDIE EXISTANTE.
- RACCORDER LE KLAXON D'ALARME INCENDIE À LA BOUCLE DE DÉTECTION D'ALARME INCENDIE EXISTANTE.
- SONDE POUR PLANCHER CHAUFFANT À INSTALLER DANS LA DALLE. EMBLEMMENT EXACT SELON LES RECOMMANDATIONS DU MANUFACTURIER.
- THERMOSTAT MAÎTRE POUR LE CONTRÔLE DU PLANCHER CHAUFFANT. RELIER CELUI-CI AU THERMOSTAT ESCLAVE POUR LE CONTRÔLE DES ZONES DU PLANCHER CHAUFFANT. FAIRE LES RACCORDEMENTS SELON LES INDICATIONS DU MANUFACTURIER.
- EMPLACEMENT EXACT DE LA BOÎTE DE SORTIE À COORDONNER AVEC LE/LA REPRÉSENTANT(E) DU CPE.

RELEVÉ E401 - MATERIEL

109 repères / 27 familles / RES 109

Calques activables; modèles, prescriptions et réserves complètes page 2

RES = reserve source, modèle, position, portée ou reconciliation; * = identification à revalider

● I01	KLAXON D'ALARME INCENDIE	3 / R3
● M01	ACCUMULATEUR D'URGENCE UA	1 / R1
● M02	APPAREIL AC-1 / AC-2 (CHAUFFAGE MURAL, À CONFIRMER)	2 / R2
● M03	APPLIQUE MURAL TOILETTE TYPE G	1 / R1
● M04	CHAUFFE-EAU CE-1 À RACCORDER	1 / R1
● M05	ECHANGEUR ECH-1 / ECH-2 (À CONFIRMER)	2 / R2
● M06	INTERRUPTEUR D'ÉCLAIRAGE UNIPOLAIRE	5 / R5
● M07	LUMINAIRE APPLIQUE EXTERIEUR TYPE D	1 / R1
● M08	LUMINAIRE D'URGENCE A 1 TÊTE SUR ACCUMULATEUR UA	2 / R2
● M09	LUMINAIRE D'URGENCE A 2 TÊTES SUR ACCUMULATEUR UA	3 / R3
● M10	LUMINAIRE D'URGENCE A 3 TÊTES	1 / R1
● M11	LUMINAIRE DESSOUS ARMOIRE TYPE F	7 / R7
● M12	LUMINAIRE ENCASTRE 2X2 TYPE A	18 / R18
● M13	LUMINAIRE ENCASTRE 2X2 TYPE A1	4 / R4
● M14	LUMINAIRE ENCASTRE ROND 6" TYPE B	8 / R8
● M15	LUMINAIRE ENCASTRE ROND 6" TYPE B1	3 / R3
● M16	PLINTHE / APPAREIL DE CHAUFFAGE RADIANT (HEXAGONE PUISSANCE KW)	9 / R9
● M17	PRISE / RACCORDEMENT DEDIE (CERCLE-CROISE) CIRCUITS 4-6	10 / R10
● M18	RELAIS BAS VOLTAGE AVEC TRANSFORMATEUR RT (A-D)	4 / R4
● M19	SECTIONNEUR 30 A SANS FUSIBLE	2 / R2
● M20	SERPENTIN ÉLECTRIQUE À RACCORDER (SE-1 À SE-4)	4 / R4
● M21	SONDE POUR PLANCHER CHAUFFANT	1 / R1
● M22	SORTIE TÉLÉPHONE/DATA (TRIANGLE)	2 / R2
● M23	SYMBOLE CERCLE-BARRE + FLECHE A/B (À CONFIRMER)	4 / R4
● M24	SYMBOLES NON IDENTIFIÉS (C.17 C.40 C.31 C.7 E)	5 / R5
● M25	THERMOSTAT DE PLINTHE / PLANCHER (T)	4 / R4
● M26	UNITÉ DE CONDENSATION CD-1/CD-2 (RACCORDEMENT)	2 / R2

Quantités source et renvois; voir bordereau détail.

PERMIS ET SOUMISSION

7 MAI 2026

CE PLAN NE DOIT PAS SERVIR À LA CONSTRUCTION

plan clé :

No. 8			
No. 7			
No. 6			
No. 5			
No. 4			
No. 3			
No. 2	PERMIS ET SOUMISSION	26-05-07	D.R.P.
No. 1	COORDINATION	26-02-13	D.R.P.
No.	Revisions:	Date:	Par:
ÉMISSIONS			

architecte:

ingénieur en **structure, civil, mécanique et électricité**

LAROCQUE COUNROYER

INGÉNIEURS

DRUMMONDVILLE
T. 819 477-9191


LA TUQUE
T. 819 676-7038

SAINT-AMBROISE-DE-KILDAIRE
T. 450 752-1106

admin@lc-ing.com
LC-ING.COM

ingénieur en

secours :

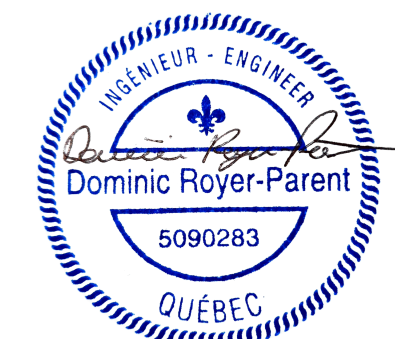

client :



26 MONTÉE LASALINE,
ST-CONSTANT, QC, J5A 2A9

projet :

AGRANDISSEMENT
CPE SOLEIL SOURIANT
26 MONTÉE LASALINE,
ST-CONSTANT

titre :

ÉCLAIRAGE, ALARME INCENDIE ET
SERVICES
DÉMENTÈLEMENT ET
RÉAMÉNAGEMENT

dessiné par : P.ST-AMANT,tech	contrat no. : 25-0075		page :
----------------------------------	--------------------------	--	--

ÉLECTRICITÉ