


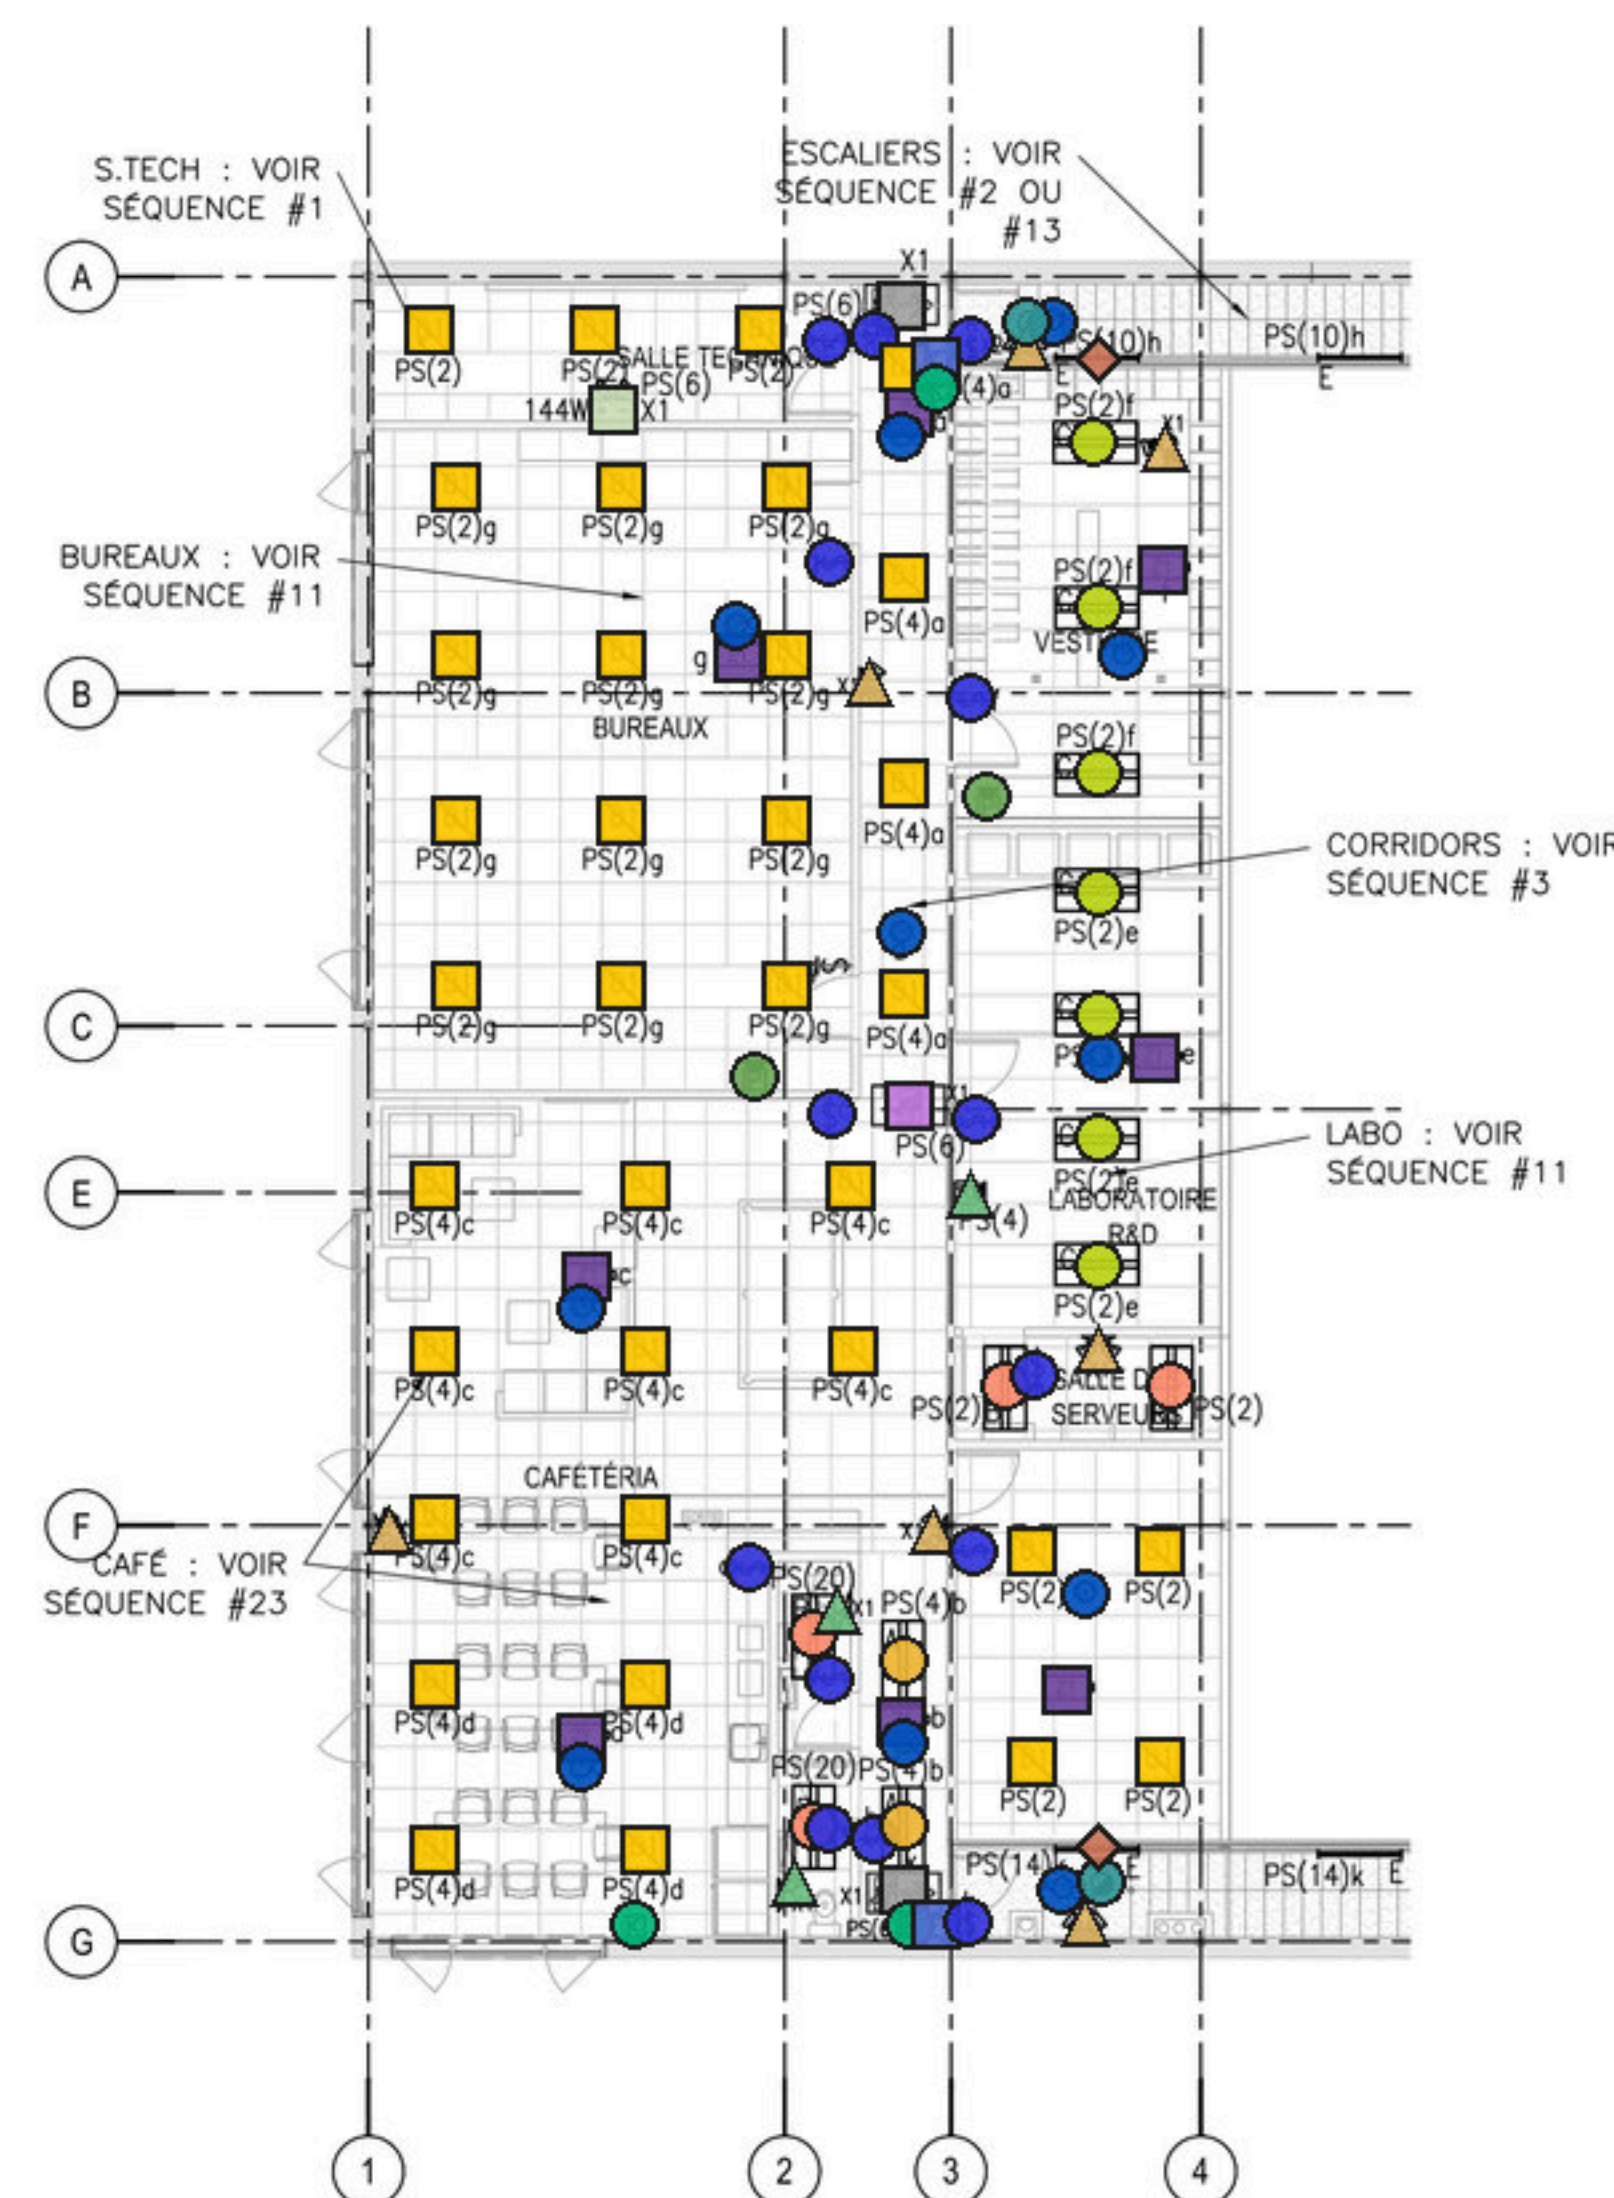

-  Aéroconvecteur mural 4kW (2)
-  Barre de MALT (1)
-  Batterie 2 phares 144W — à confirmer (1)
-  Batterie 2 phares c/a sortie 144W (4)
-  Carré R — à classer (4)
-  Conduit 2po EMT entrée télécom — à métrer (1)
-  Contreplaqué ignifuge 3/4po (1)
-  Contrôleur BBR-HV (Z1) (10)
-  Détecteur RooM-PIR (DP) (13)
-  Détecteur de fumée (2)
-  Indicateur sortie mural (2)
-  Indicateur sortie plafond (1)
-  Interrupteur détecteur présence (1)
-  Interrupteur sécurité 30A EI (1)
-  Interrupteur — type à confirmer (18)
-  Klaxon alarme incendie (3)
-  Klaxon miniature (3)
-  Luminaire A 2x4 24W (2)
-  Luminaire B 2x4 30W (4)
-  Luminaire C 2x4 38W (7)
-  Luminaire D1 2x2 30W (35)
-  Luminaire E réglette 26W (4)
-  Luminaire F 2x4 surface 30W (4)
-  Mini aéroconvecteur plafond 2kW — à confirmer
-  Moteur monophasé (ventilateur) (3)
-  Panneau PP-MEZZ 347/600V (1)
-  Panneau PS-MEZZ 120/208V (1)
-  Phare double LED (7)
-  Phare simple LED (3)
-  Plinthe électrique 1500W (1)
-  Plinthe électrique 2000W (4)
-  Plinthe électrique 2500W (3)
-  Plinthe électrique 500W (2)
-  Plinthe électrique 750W (1)
-  Prise comptoir 20A (10)
-  Prise comptoir DDFT — à confirmer (3)
-  Prise double (26)
-  Prise double USB (1)
-  Prise extérieure DDFT (2)
-  Prise lave-vaisselle (LV) (2)
-  Prise micro-onde (MO) (2)
-  Protection ignifuge 1 h (note) (3)
-  Raccordement auget existant (1)



firmer (3) ÉLECTRICITÉ





CONTRAT N°	BAFZALI, tech. principal	DATE CAH-VAR-PROJ	13-01-2022
DESIGNE N°	BAFZALI, tech. principal	ECHÉLLE	
VERSION N°	J.BACHKONGI, ing.	N° DE PROJET	21-03-2021-01
APPROUVE N°	J.BACHKONGI, ing.	PLAN N°	E-001



1 ÉCLAIRAGE ABRI EXTÉRIEUR
E-005 3/32"=1'-0"

1- FOURNIR, INSTALLER ET RACCORDER LES CONDUCTEURS POUR CONTRÔLE 0-10V SOUS CONDUIT EMT POUR L'ENSEMBLE DES LUMINAIRES MONTRES AUX PLANS. COORDONNER LES TRAVAUX DE PROGRAMMATION DES CONTRÔLES D'ÉCLAIRAGE AVEC UN REPRÉSENTANT DE LA COMPAGNIE D'ÉCLAIRAGE.



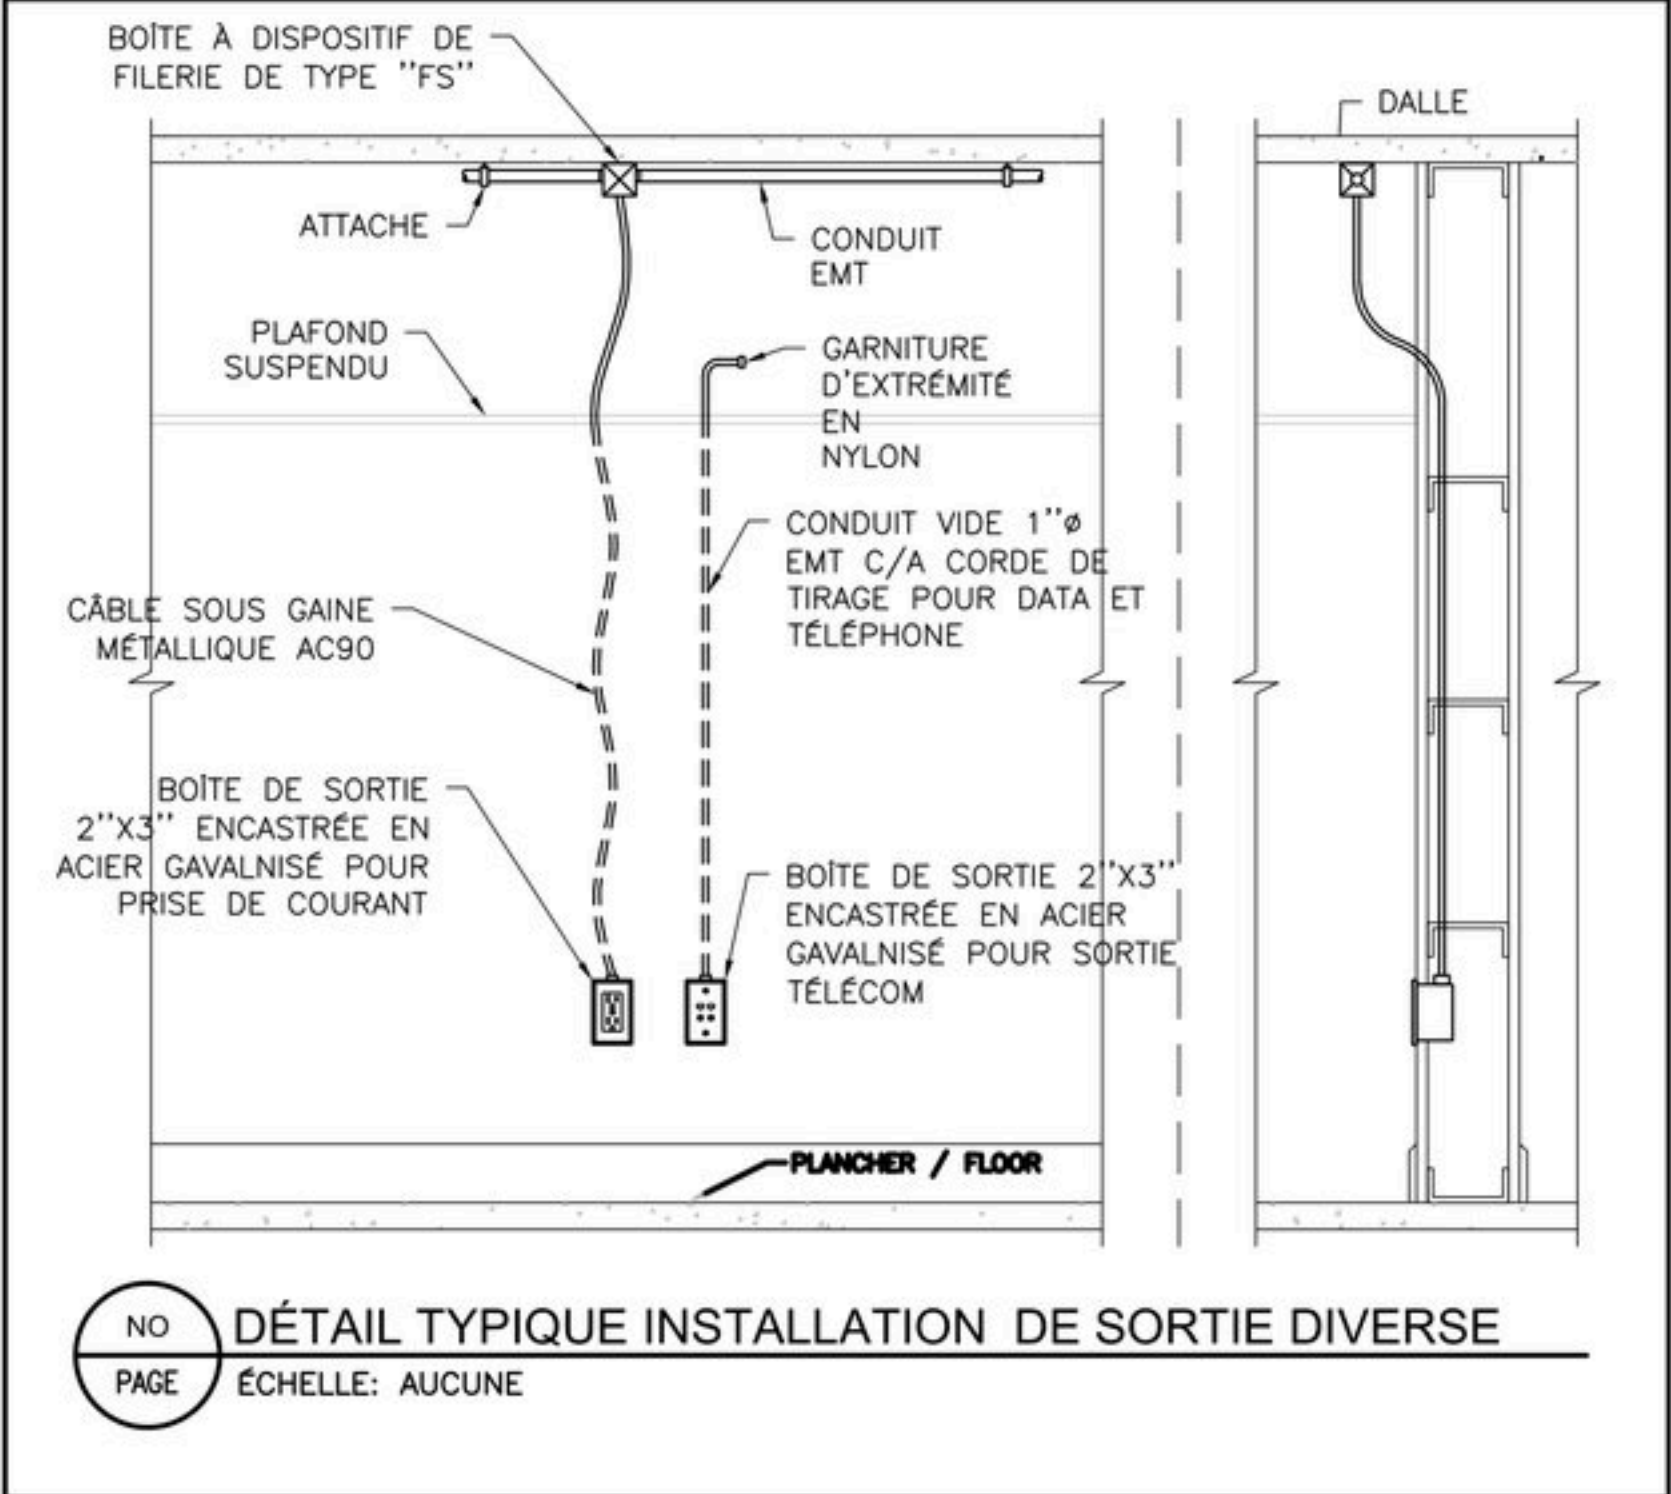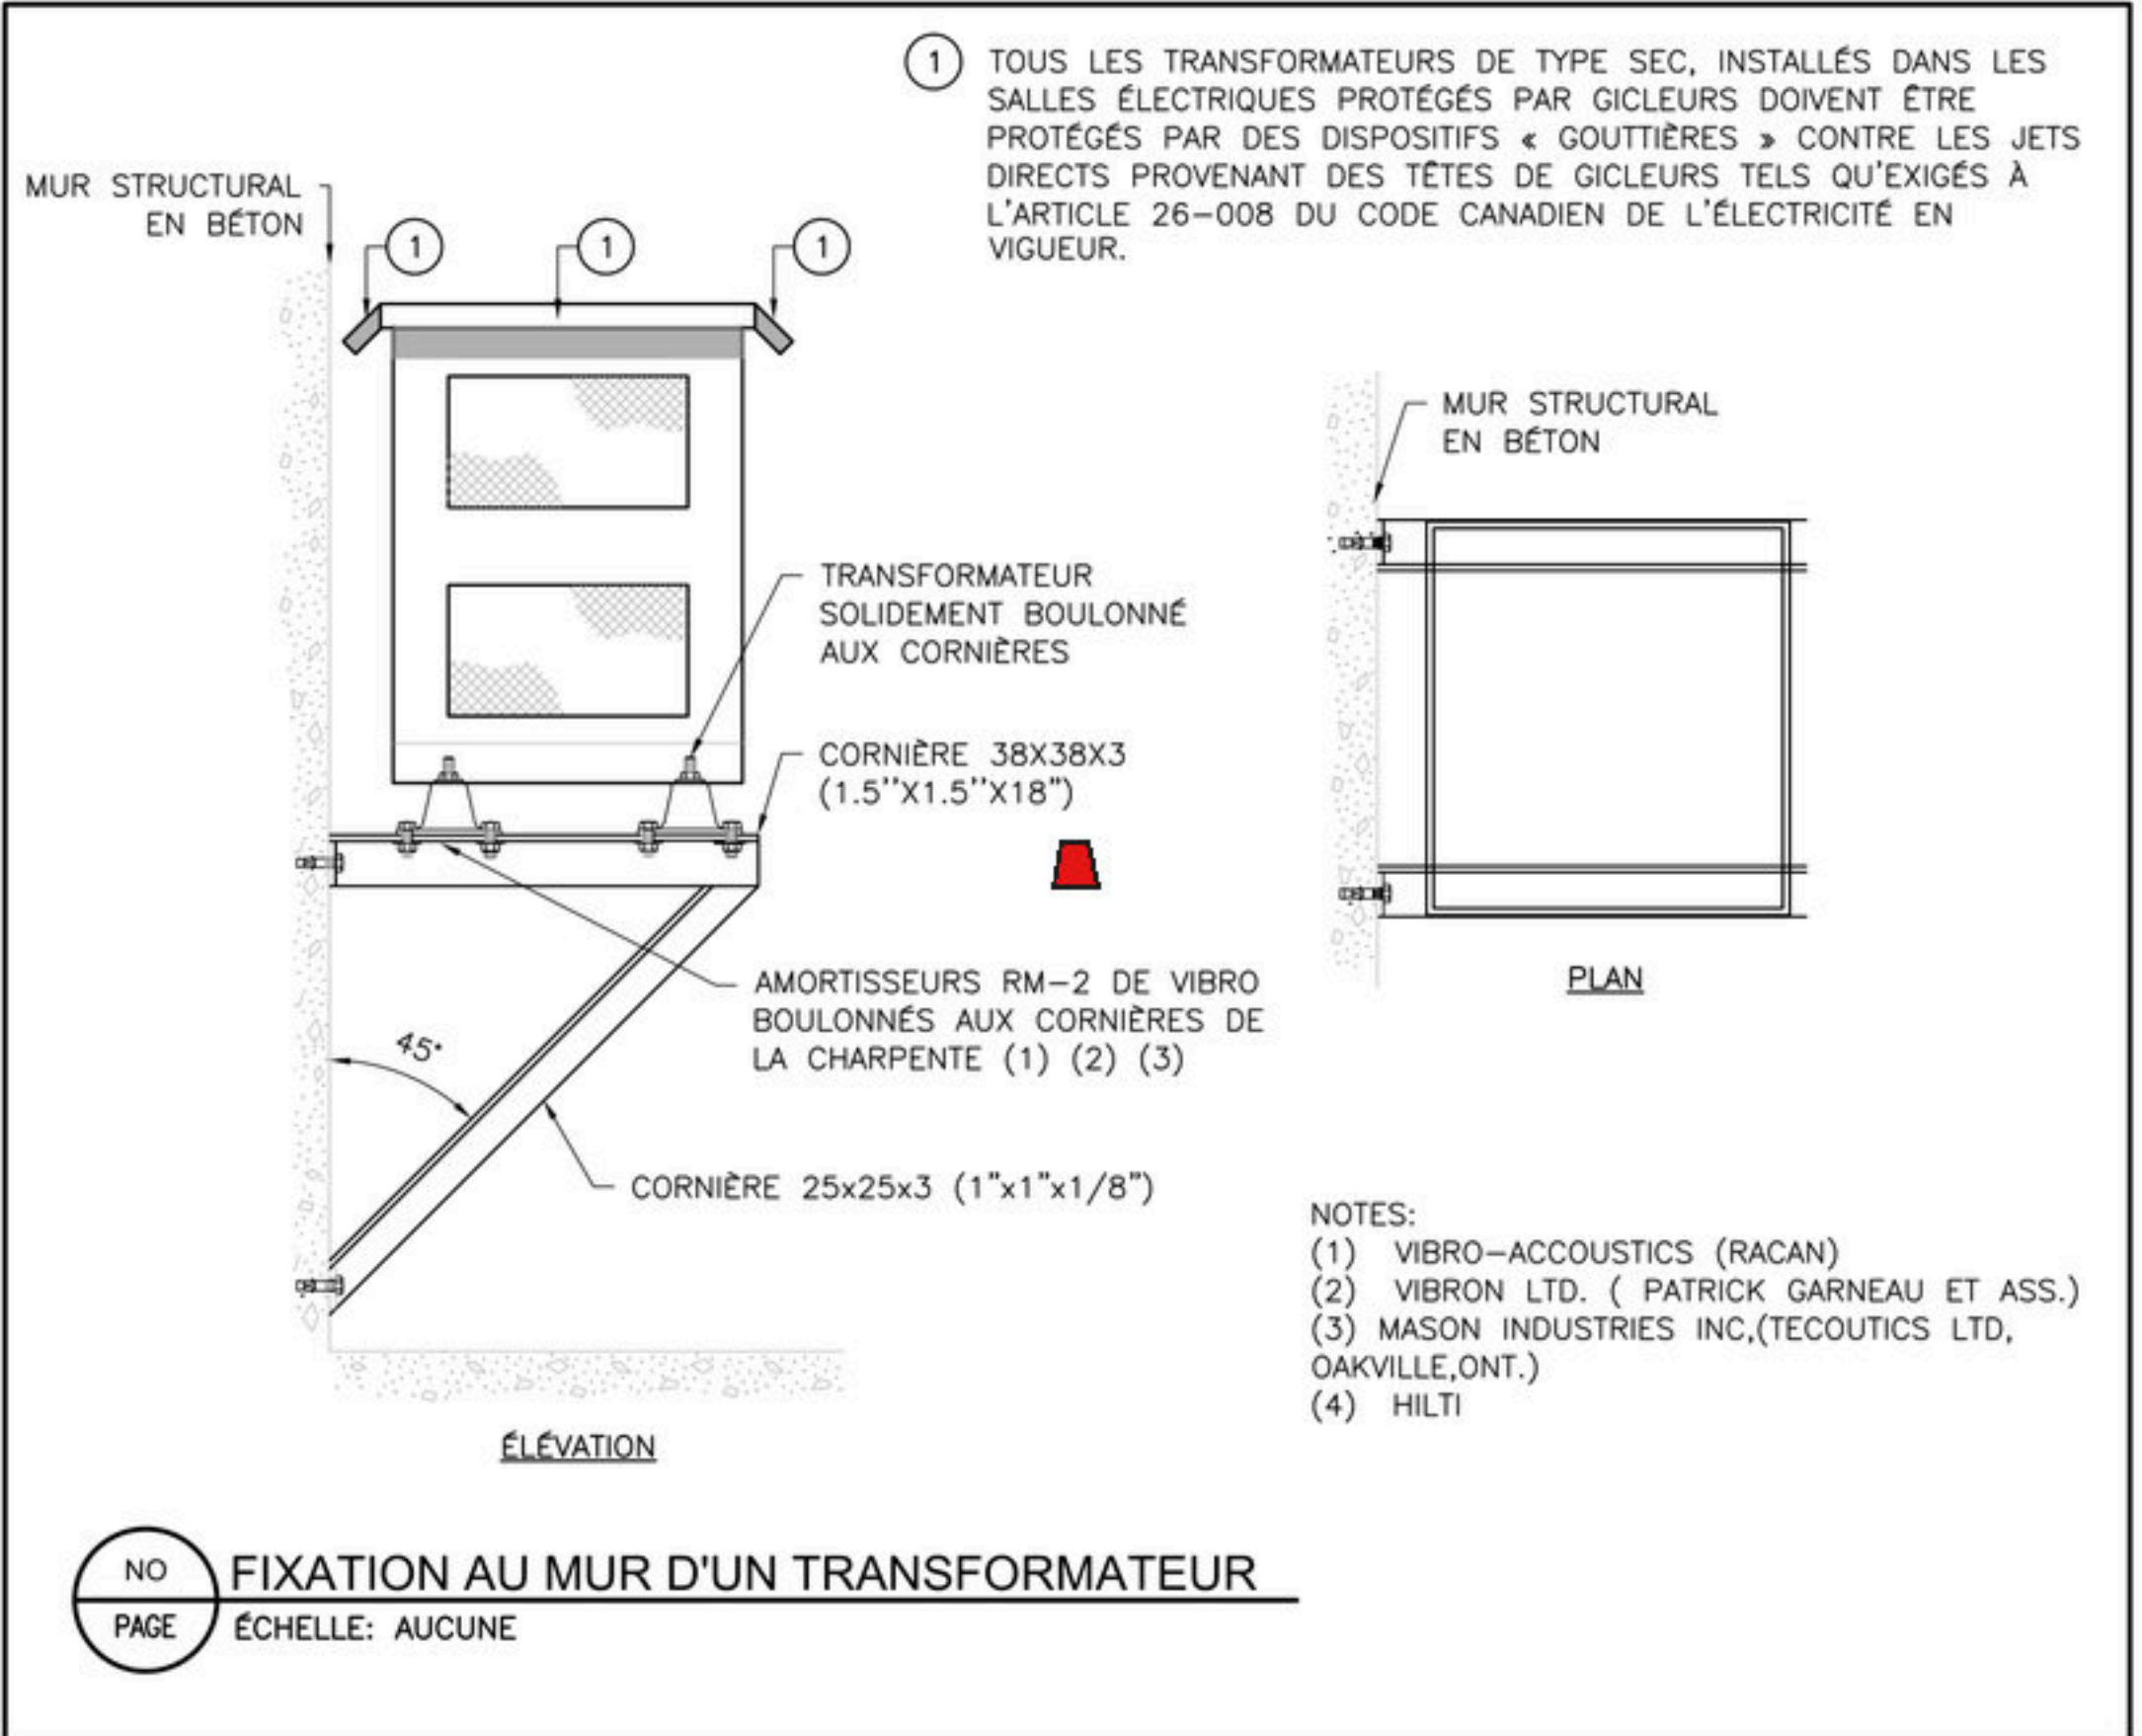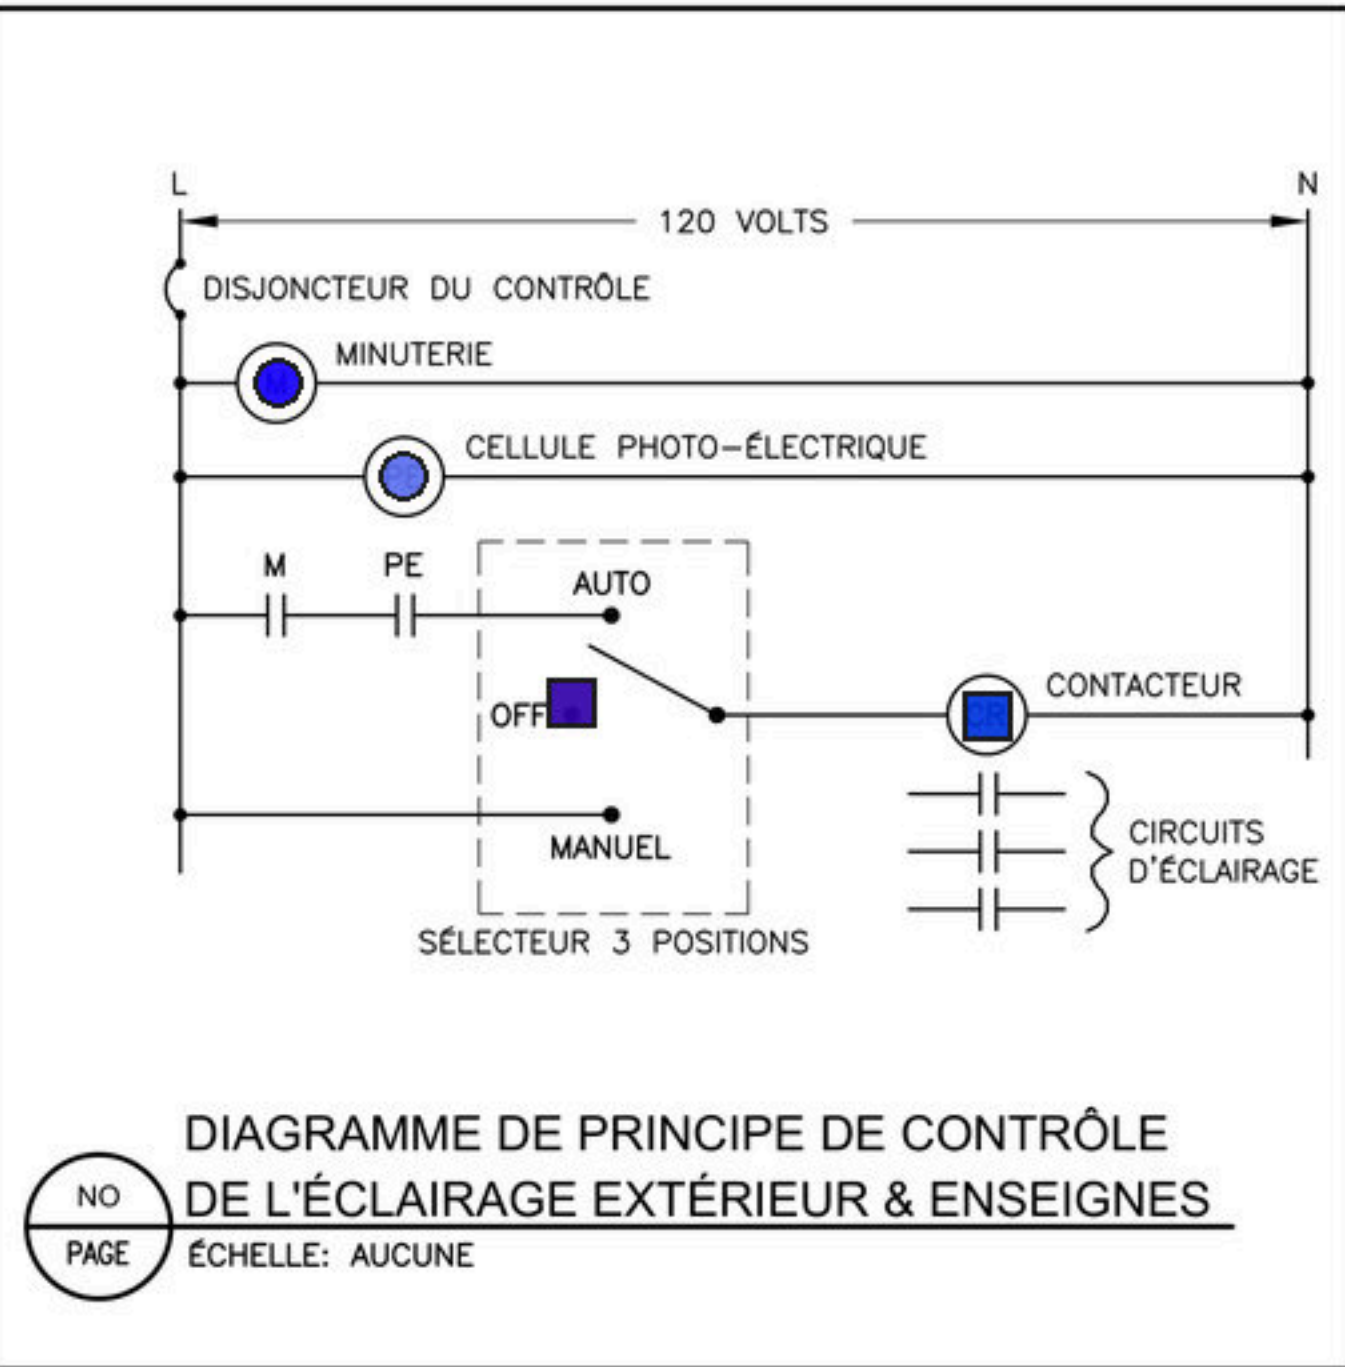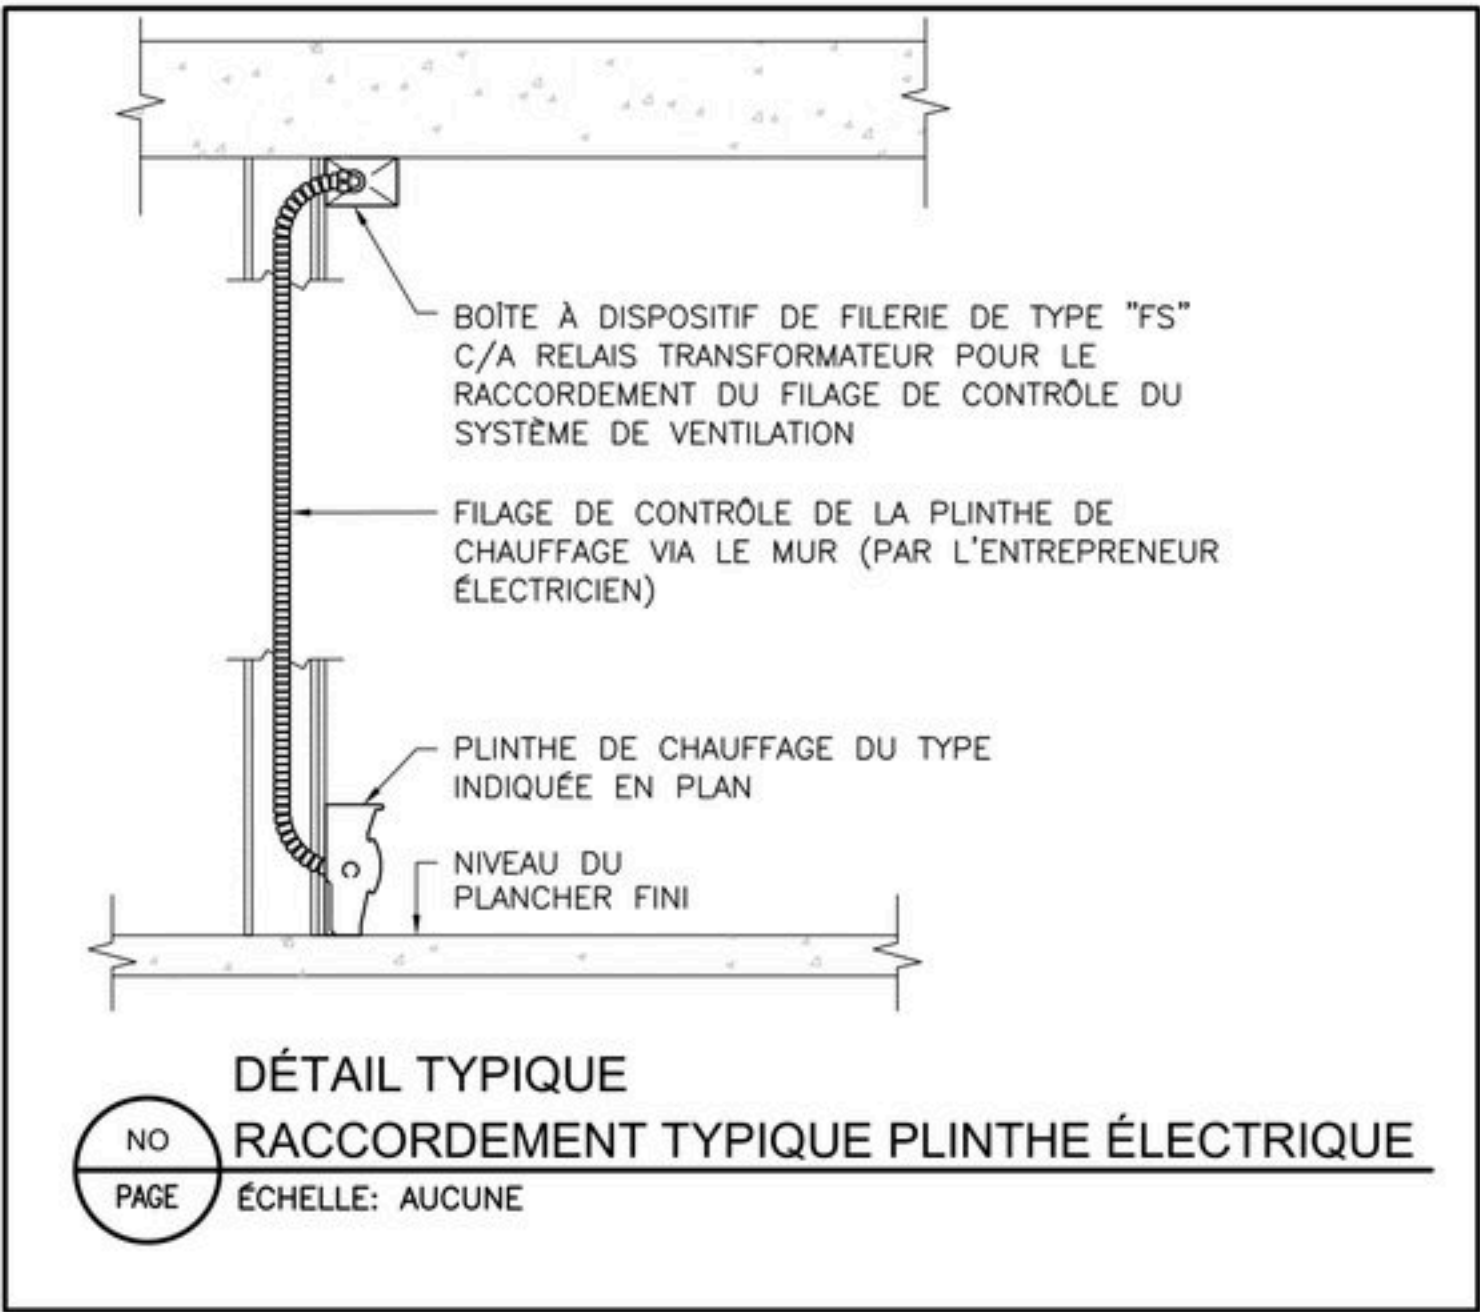

SÉQUENCE DE CONTRÔLE DE L'ÉCLAIRAGE														
SÉQUENCE #	TYPE D'ESPACE	DESCRIPTION DU TYPE DE CONTRÔLE	NARATIF DU CONTRÔLE SELON LE CNEB-2017 CANADA	DENSITÉ DE PUISSANCE D'ÉCLAIRAGE EN W/m²	FACTEUR D'ADJUSTEMENT	POURCENTAGE DE DIMINUTION DE LA DPE	4.2.2.1.3 CONTRÔLE MANUEL	4.2.2.1.6 LIMITE À LA MISE EN CIRCUIT	4.2.2.1.8 LIMITE À LA MISE EN CIRCUIT AUTO PARTIELLE 50%	4.2.2.1.9 A2 NIVEAUX RADIATION ACCEPTÉE	4.2.2.1.10 MISE HORS CIRCUIT AUTO PARTIELLE	4.2.2.1.12 MISE HORS CIRCUIT AUTO COMPLETE	4.2.2.1.14 MISE HORS CIRCUIT PROGRAM MEE	4.2.2.1.14 MISE HORS CIRCUIT PROGRAM MEE AVEC LA RÉSERVE DU PARAGRAPHE 17
SÉQUENCE #1	RANGEMENT-LOCAUX TECHNIQUE	CONTRÔLE SANS GRADATION ET AUTOMATIQUE ON/OFF	ON AUTOMATIQUE PAR DÉTECTION DE MOUVEMENT ET AUTO OFF APRÈS 20 MINUTES D'OCCUPATION (DÉTECTION DE MOUVEMENT)				X					X		
SÉQUENCE #2	ESCALIER	CONTRÔLE AUTOMATIQUE 100%/50% DIRECTEMENT AU LUMINAIRE	CHAQUE LUMINAIRE EST ÉQUIPÉ DE CAPTEUR DE MOUVEMENT. ON AUTOMATIQUE À 100% BASÉ SUR LA DÉTECTION DE MOUVEMENT. APRÈS 20 MINUTES D'OCCUPATION LE NIVEAU DE L'ÉCLAIRAGE BAISSE DE 50%. L'ÉCLAIRAGE NE S'ÉTEINT JAMAIS				X			X	X			
SÉQUENCE #3	CORRIDOR	CONTRÔLE AUTOMATIQUE 100%/50% SUR DÉTECTION	ON AUTOMATIQUE À 100% BASÉ SUR LA DÉTECTION DE MOUVEMENT. APRÈS 20 MINUTES D'OCCUPATION LE NIVEAU DE L'ÉCLAIRAGE BAISSE DE 50%. L'ÉCLAIRAGE NE S'ÉTEINT JAMAIS (VOIR CODE DE SÉCURITÉ).				X			X	C	O	C	X
ÉCLAIRAGE EXTÉRIEUR		DESCRIPTION DU TYPE DE CONTRÔLE	NARATIF DU CONTRÔLE SELON LE CNEB-2017 4.2.4.1.											
SÉQUENCE #7a CNEB SECTION 4.2.4.1.		CONTRÔLE POUR ÉCLAIRAGE EXTÉRIEUR (SÉCURITÉ)	AU COUCHER DU SOLEIL L'ÉCLAIRAGE S'ALLUME À 100%. AU LEVER DU SOLEIL L'ÉCLAIRAGE S'ÉTEINT.				X							
SÉQUENCE #9	AIRES POUR PERSONNES ASSISSES			5.9	4	S.O.	X	A	A	-	-	B	B	
SÉQUENCE #10	BUANDERIES			6.5	4	S.O.	X	A	A	X	-	B	B	
BUREAUX														
SÉQUENCE #11	BUREAUX À AIRE OUVERTE			10.6	4	(5% POUR C1 OU C2) (25% POUR C3) (30% POUR C4)	X	A	A	X	-	B	B	
SÉQUENCE #12a	BUREAUX FERMÉS ET DON L'AIRE s25m²			12.0	8	5% POUR C1 OU C2	X	A	A	X	-	X	-	
SÉQUENCE #13	CAGES D'ESCALIER			7.4	10	10% POUR C2	X			Y	Y	B	B	
CORRIDORS ET AIRES DE TRANSITION														
SÉQUENCE #14	POUR ESPACES CONFORMES À LA NORME ANSI/IES RP-28 «LIGHTING AND THE VISUAL ENVIRONMENT FOR SENIOR LIVING» ET UTILISÉS PRINCIPALEMENT PAR LES RÉSIDENTS			9.9	LARG EUR <2.4m (VOIR 4.2.1.6.4)	10% POUR C2	X							
SÉQUENCE #22	LOCAUX DES INSTALLATIONS ÉLECTRIQUES OU MÉCANIQUES			4.6	6	124%	X							
SALLES À MANGER														
SÉQUENCE #23	POUR LES CAFÉTÉRIAS ET LES RESTAURANTS RAPIDES			7.0	4	10% POUR C2	X							
SALLES D'ENTREPOSAGE														
SÉQUENCE #28a	<5m²			13.3	6	S.O.	X							
SÉQUENCE #28b	≥5m² et ≤100m²			6.8	6	S.O.	X	A	A	-	-	X	-	
SÉQUENCE #28c	>100m²			6.8	6	S.O.	X	A	A	-	X	B	B	
SÉQUENCE #29	SALLES DE SERVEURS			18.4	4	S.O.	X	A	A	X	-	B	B	
SALLES DE CLASSE, AUDITORIUMS ET SALLES DE FORMATION														
SÉQUENCE #30	(AUTRES)			13.4	4	10% POUR C1 OU C2	X	A	A	X	-	X	-	
SÉQUENCE #31	SALLES DE CONFÉRENCE, SALLES DE RÉUNION ET SALLES MULTIFONCTIONS			13.3	6	10% POUR C1 OU C2	X	A	A	X	-	X	-	
SÉQUENCE #32	SALLES DE PHOTOCOPIE ET D'IMPRESSION DE DOCUMENTS			7.8	6	S.O.	X	A	A	X	-	X	-	
SALLES DE TOILETTES														
SÉQUENCE #33	POUR LES ESPACES CONFORMES À LA NORME ANSI/IES RP-28 «LIGHTING AND THE VISUAL ENVIRONMENT FOR SENIOR LIVING» ET UTILISÉS PRINCIPALEMENT PAR LES RÉSIDENTS			13.1	8	S.O.	X	-	-	-	-	X	-	
SÉQUENCE #34	(AUTRES)			10.5	8	S.O.	X	-	-	-	-	X	-	
SÉQUENCE #35	VESTIAIRES			8.1	6	S.O.	X	A	A	A	-	X	-	


Légende — E006 (6 marques)

- Cellule photo-électrique (1)
- Contacteur d'éclairage (1)
- ▲ Fixation murale transformateur
- Minuterie astronomique (1)
- ◆ Programmation contrôles électroniques
- Sélecteur 3 positions (1)

L'ENTREPRENEUR DOIT FOURNIR LES DESSINS D'ATELIER ET SCHÉMA DE CONTRÔLE À L'INGÉNIEUR POUR APPROBATION. LE TABLEAU EST À TITRE INDICATIF, CE RÉFÉRER AU CNEB EN VIGUEUR.

1. LES COMMANDES C1 À C4 DÉSIGNENT LES COMMANDES SUIVANTES:
C1: COMMANDE L'ÉCLAIRAGE À L'AIDE D'UN GRADATEUR MANUEL;
C2: COMMANDE L'ÉCLAIRAGE À L'AIDE D'UNE PROGRAMMATION HORAIRE DE NIVEAUX MULTIPLES D'ÉCLAIREMENT;
C3: COMMANDE L'ÉCLAIRAGE À L'AIDE DE DÉTECTEURS D'OCCUPANT, LORSQUE L'ÉCLAIRAGE RÉPOND AUX CRITÈRES SUIVANTS:
a. L'ÉCLAIRAGE EST DÉDIÉ EXCLUSIVEMENT AUX POSTES DE TRAVAIL;
b. L'ÉCLAIRAGE DE CHAQUE POSTE DE TRAVAIL EST COMMANDE INDÉPENDAMMENT;
c. LA PORTION DE L'ÉCLAIRAGE DIRIGÉE VERS LA SURFACE DE TRAVAIL EST COMMANDEE INDÉPENDAMMENT DE LA PORTION DIRIGÉE VERS LE PLAFOND;
d. LA PORTION DE L'ÉCLAIRAGE DIRIGÉE VERS LA SURFACE DE TRAVAIL S'ÉTEINT AUTOMATIQUEMENT PAR GRADATION CONTINUE DANS LES 30 PREMIÈRES MINUTES D'OCCUPATION; LA GRADATION D'ARRÊT DE L'ÉCLAIRAGE DOIT DURER UN MINIMUM DE 2MIN.
e. À L'ARRIVÉE DE L'OCCUPANT, LA PORTION DE L'ÉCLAIRAGE DIRIGÉE VERS LA SURFACE DE TRAVAIL S'ALLUME AUTOMATIQUEMENT À UN PREMIER NIVEAU MINIMAL D'ÉCLAIREMENT, PUIS PAR GRADATION CONTINUE PENDANT AU MOINS 30s AVANT D'ATTEINDRE UN NIVEAU SUPÉRIEUR PRÉÉTABLI; ET
f. LA PORTION DE L'ÉCLAIRAGE DIRIGÉE VERS LE PLAFOND RÉPOND AUX EXIGENCES DU PARAGRAPHE 4.2.2.1.12);
C4: COMMANDE L'ÉCLAIRAGE À L'AIDE D'UNE COMMANDE C3, TOUT EN PERMETTANT D'AJUSTER MANUELLEMENT LE NIVEAU D'ÉCLAIREMENT PAR GRADATION CONTINUE DE L'ÉCLAIRAGE DIRIGÉ VERS LE POSTE DE TRAVAIL.
2. S.O.: SANS OBJET.
A: AU MOINS UNE DES COMMANDES D'ÉCLAIRAGE MARQUÉES D'un «+» DOIT ÊTRE INSTALLÉE DANS CE TYPE D'ESPACE;
B: AU MOINS UNE DES COMMANDES D'ÉCLAIRAGE MARQUÉES D'un «+» DOIT ÊTRE INSTALLÉE DANS CE TYPE D'ESPACE;
X: TOUTES LES COMMANDES D'ÉCLAIRAGE MARQUÉES D'un «+» DOIVENT ÊTRE INSTALLÉE DANS CE TYPE D'ESPACE; ET
- (TRAIT): IL N'EST PAS NÉCESSAIRE QUE CETTE COMMANDE D'ÉCLAIRAGE SOIT INSTALLÉE DANS CE TYPE D'ESPACE.
3. LES COMMANDES QUI SATISFONT AUX EXIGENCES DE «MISE EN CIRCUIT AUTOMATIQUE PARTIELLE» DU PARAGRAPHE 4.2.2.1.8) SATISFONT ÉGALEMENT AUX EXIGENCES DES «COMMANDES D'ÉCLAIRAGE À DEUX NIVEAUX» DU PARAGRAPHE 4.2.2.1.9);
4. LES COMMANDES QUI SATISFONT AUX EXIGENCES DE «MISE HORS CIRCUIT AUTOMATIQUE COMPLETE» DU PARAGRAPHE 4.2.2.1.12) SATISFONT ÉGALEMENT AUX EXIGENCES DE «MISE HORS CIRCUIT AUTOMATIQUE PARTIELLE» DU PARAGRAPHE 4.2.2.1.10)

NOTES ÉCLAIRAGE ET CONTRÔLES	
1. L'ENTREPRENEUR ÉLECTRICIEN DEVRA MANDATER LE FOURNISSEUR D'APPAREIL D'ÉCLAIRAGE POUR LA MISE EN MARCHÉ ET LA PROGRAMMATION DES SYSTÈMES DE CONTRÔLE D'ÉCLAIRAGE. LE TECHNICIEN DE CONTRÔLE DES APPAREILS D'ÉCLAIRAGE SERA SOUS LA RESPONSABILITÉ DE L'ENTREPRENEUR ÉLECTRICIEN.	
2. L'ENTREPRENEUR ÉLECTRICIEN DEVRA INCLURE DANS SA SOUMISSION LES FRAIS DU FOURNISSEUR D'APPAREIL D'ÉCLAIRAGE POUR LA MISE EN MARCHÉ DU SYSTÈME DE CONTRÔLE (PROGRAMMATION ET MISE EN MARCHÉ) ET LA COORDINATION ENTRE EUX (ENTREPRENEUR ÉLECTRICIEN ET SON SOUS-TRAITANT EN CONTRÔLE D'ÉCLAIRAGE).	

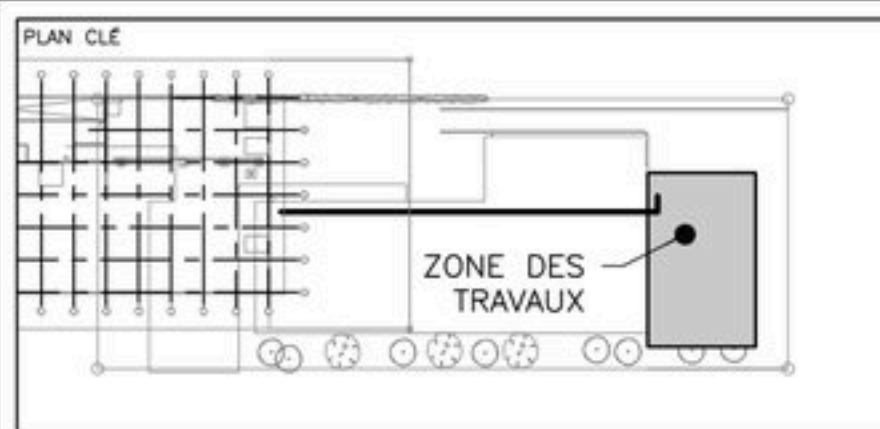

LEGENDE / NOTES

Légende — E006 (6 marques)

- Cellule photo-électrique (1)
- Contacteur d'éclairage (1)
- Fixation murale transformateur (1)
- Minuterie astronomique (1)
- Programmation contrôles éclairage (1)
- Sélecteur 3 positions (1)

1	2025-12-18	ÉMIS POUR CONSTRUCTION	J.B.
0	2025-10-28	ÉMIS POUR SOUMISSIONS	J.B.
NO	DATE (JJ-MM-AAAA)	REVISION	PAR



Titre du projet
Réaménagement de la mezzanine et de la cour arrière l'usine pultrusion
1830, rue marie-victorin
saint-bruno-de-montarville

Titre du dessin
CONTRÔLE D'ÉCLAIRAGE ET DÉTAILS

DISCIPLINE	
ÉLECTRICITÉ	
CONÇU PAR	DATE (JJ-MM-AAAA)
B.AFZALI, tech. principal	13-04-2022
DESSINÉ PAR	ÉCHELLE
B.AFZALI, tech. principal	ÉCHELLE
VÉRIFIÉ PAR	NO DE PROJET
J.BACHKONGI, ing.	21-0291-01
APPROUVÉ PAR	PLAN NO
J.BACHKONGI, ing.	E-006