


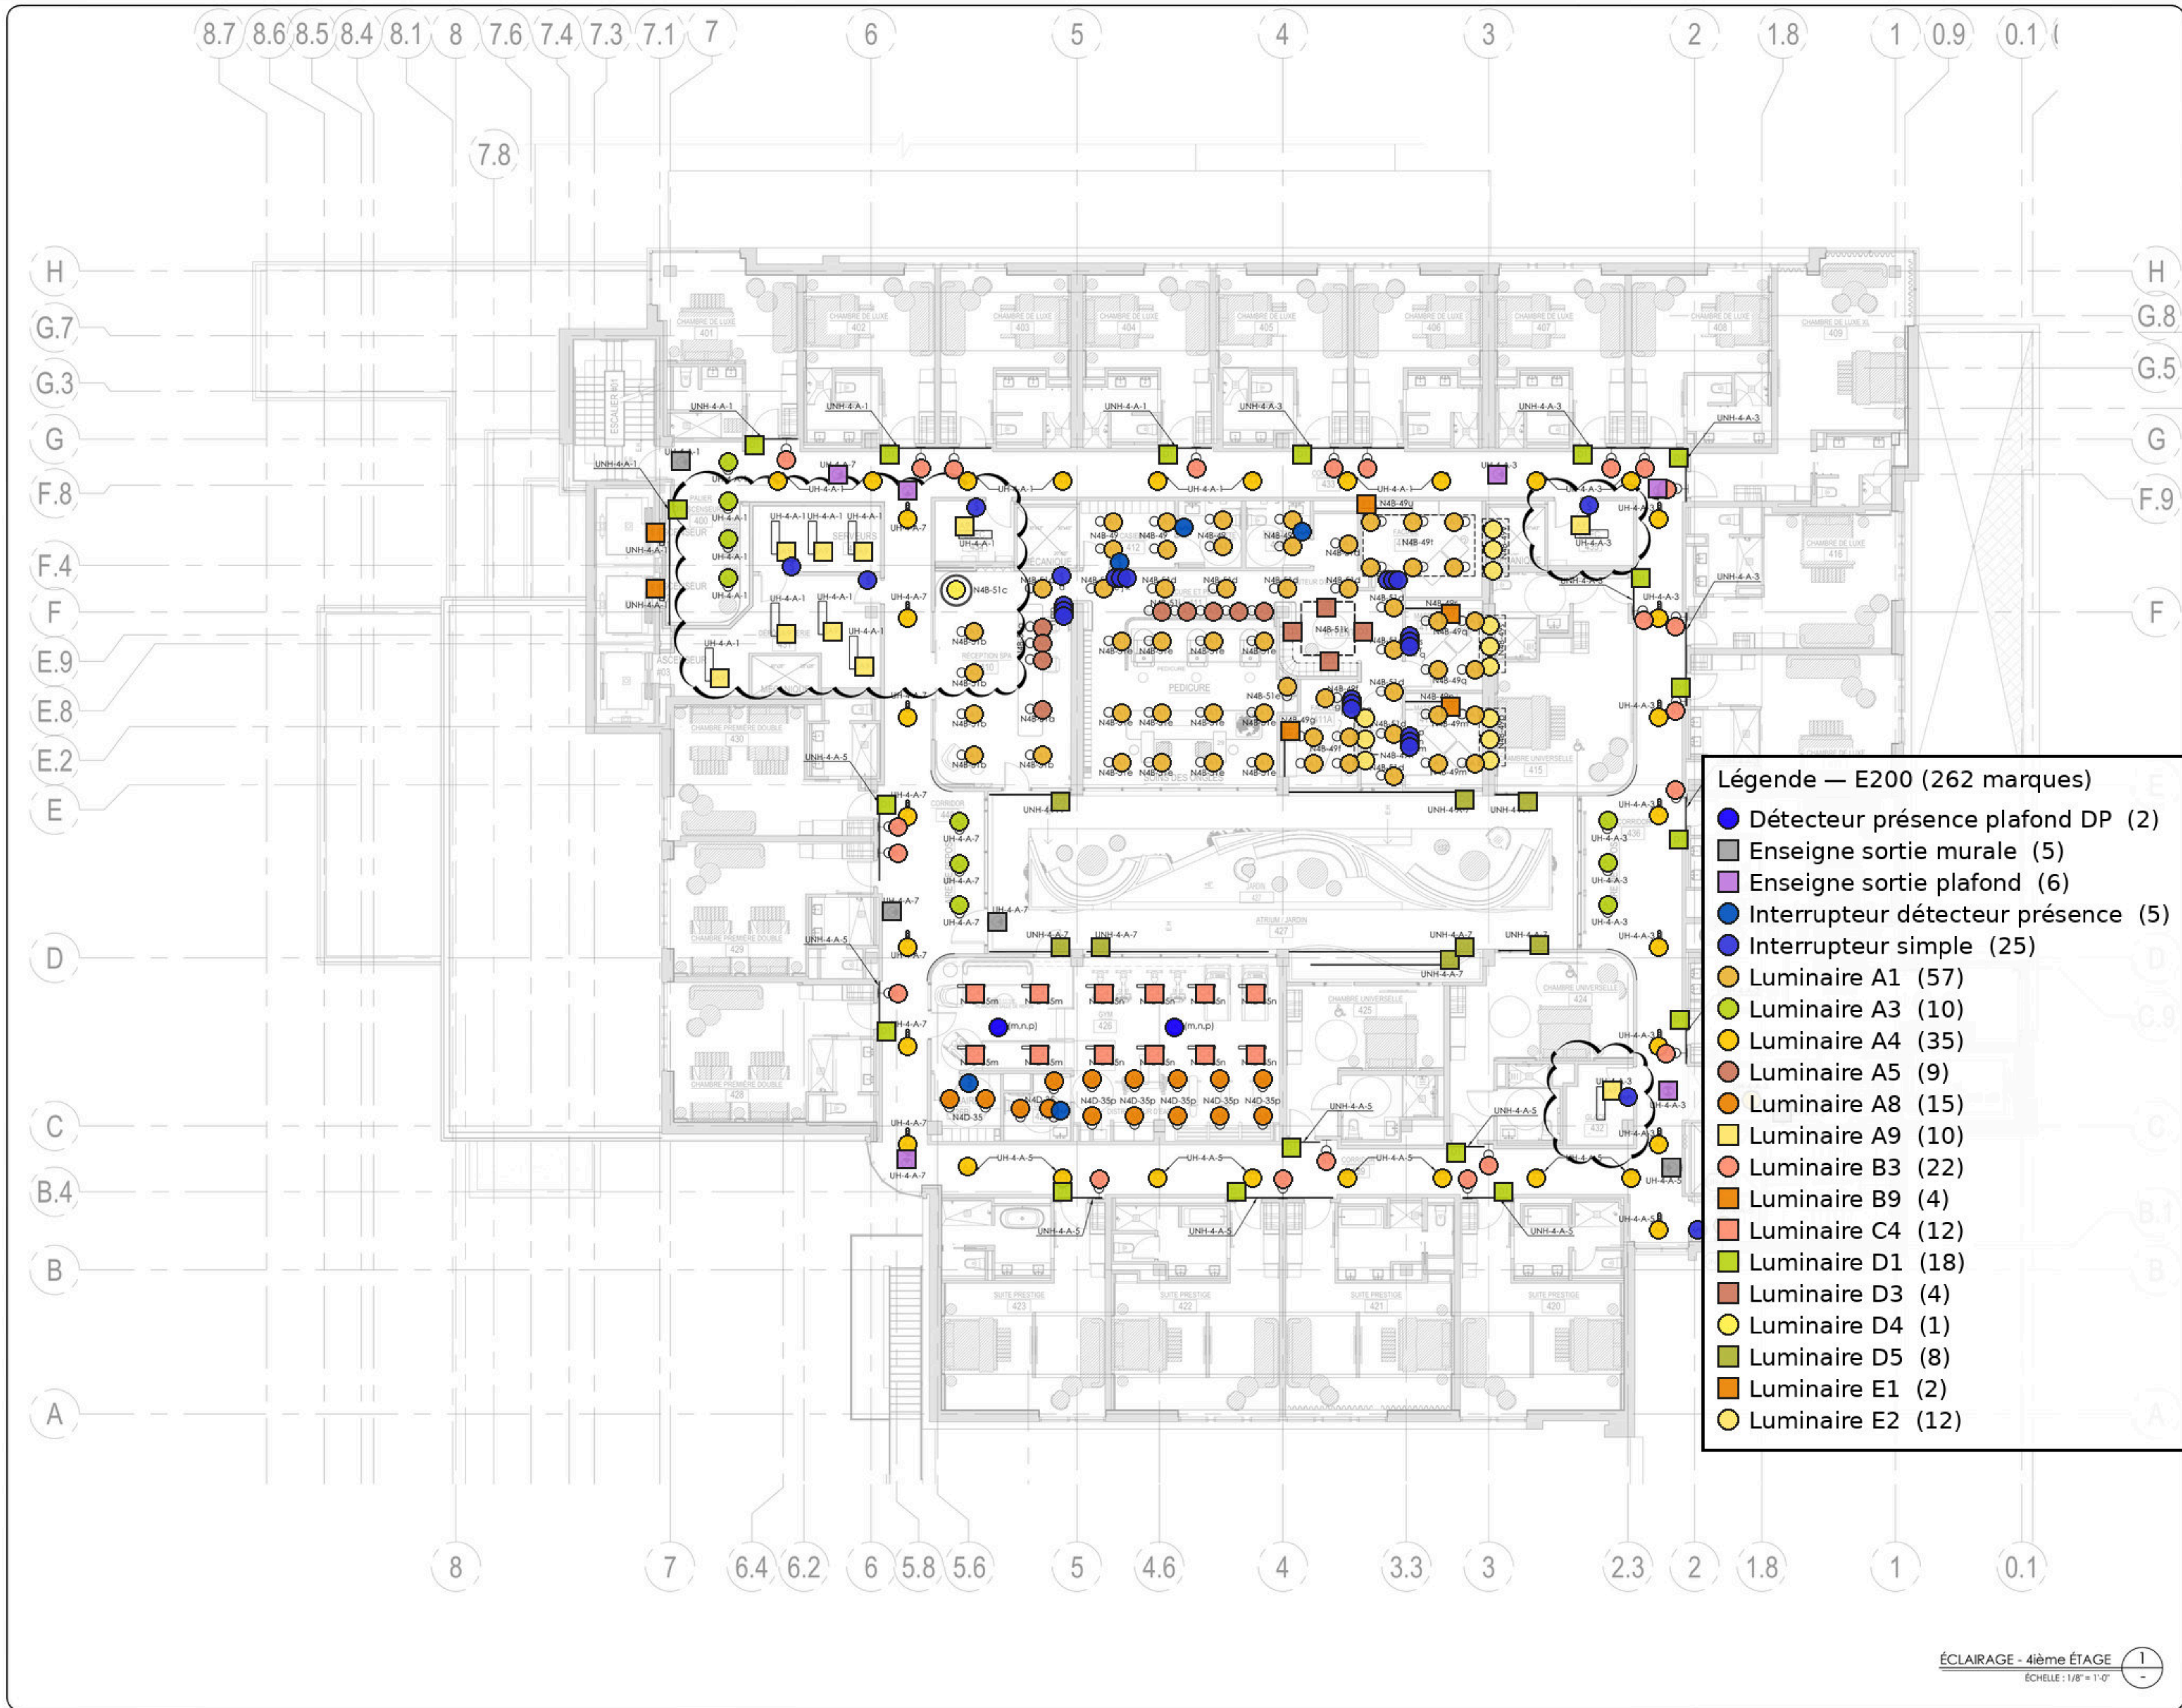

- Légende — E200 (262 marques)**
- Détecteur présence plafond DP (2)
 - Enseigne sortie murale (5)
 - Enseigne sortie plafond (6)
 - Interrupteur détecteur présence (5)
 - Interrupteur simple (25)
 - Luminaire A1 (57)
 - Luminaire A3 (10)
 - Luminaire A4 (35)
 - Luminaire A5 (9)
 - Luminaire A8 (15)
 - Luminaire A9 (10)
 - Luminaire B3 (22)
 - Luminaire B9 (4)
 - Luminaire C4 (12)
 - Luminaire D1 (18)
 - Luminaire D3 (4)
 - Luminaire D4 (1)
 - Luminaire D5 (8)
 - Luminaire E1 (2)
 - Luminaire E2 (12)

ÉCLAIRAGE - 4ième ÉTAGE
ÉCHELLE : 1/8" = 1'-0"

NOTE GÉNÉRALE

- ◇ COORDONNER LES CONTRÔLES D'ÉCLAIRAGE AVEC LE CLIENT (SYSTÈME LUTRON ET CONTRÔLE LOCAL).
- ◇ DANS LES CORRIDORS ET DANS LE JARDIN, PRÉVOIR UNE ZONE D'ÉCLAIRAGE PAR TYPE D'APPAREIL.

PROJET

lemay

20-02-26 APPEL D'OFFRES RÉVISION 1 M.S.
17-07-25 APPEL D'OFFRES M.S.
NO. J - M - A DESCRIPTION PAR

ÉMIS POUR:

BFA Experts conseils - microcontrôle électrique - électricité
Blondin Fortin Associés
305, boul. Cyrille-Lapointe
Sudbury, Ontario, Canada
G1T 1A1
Tél. : 416-428-5555
www.blondinfortin.ca

PLAYGROUND POKER


PLAYGROUND HOTEL,
1 500 QC-138 C, KAHNAWAKE,
QC, J0L 1B0

ÉLECTRICITÉ

ÉCLAIRAGE
4ième ÉTAGE

PRÉPARÉ PAR: M. SIMARD
Dessiné par: G. BLONDIN
NO. DE PROJET: 2024-023

ÉCHELLE: TEL QU'INDIQUÉ
PLANCHE NO.: E-200

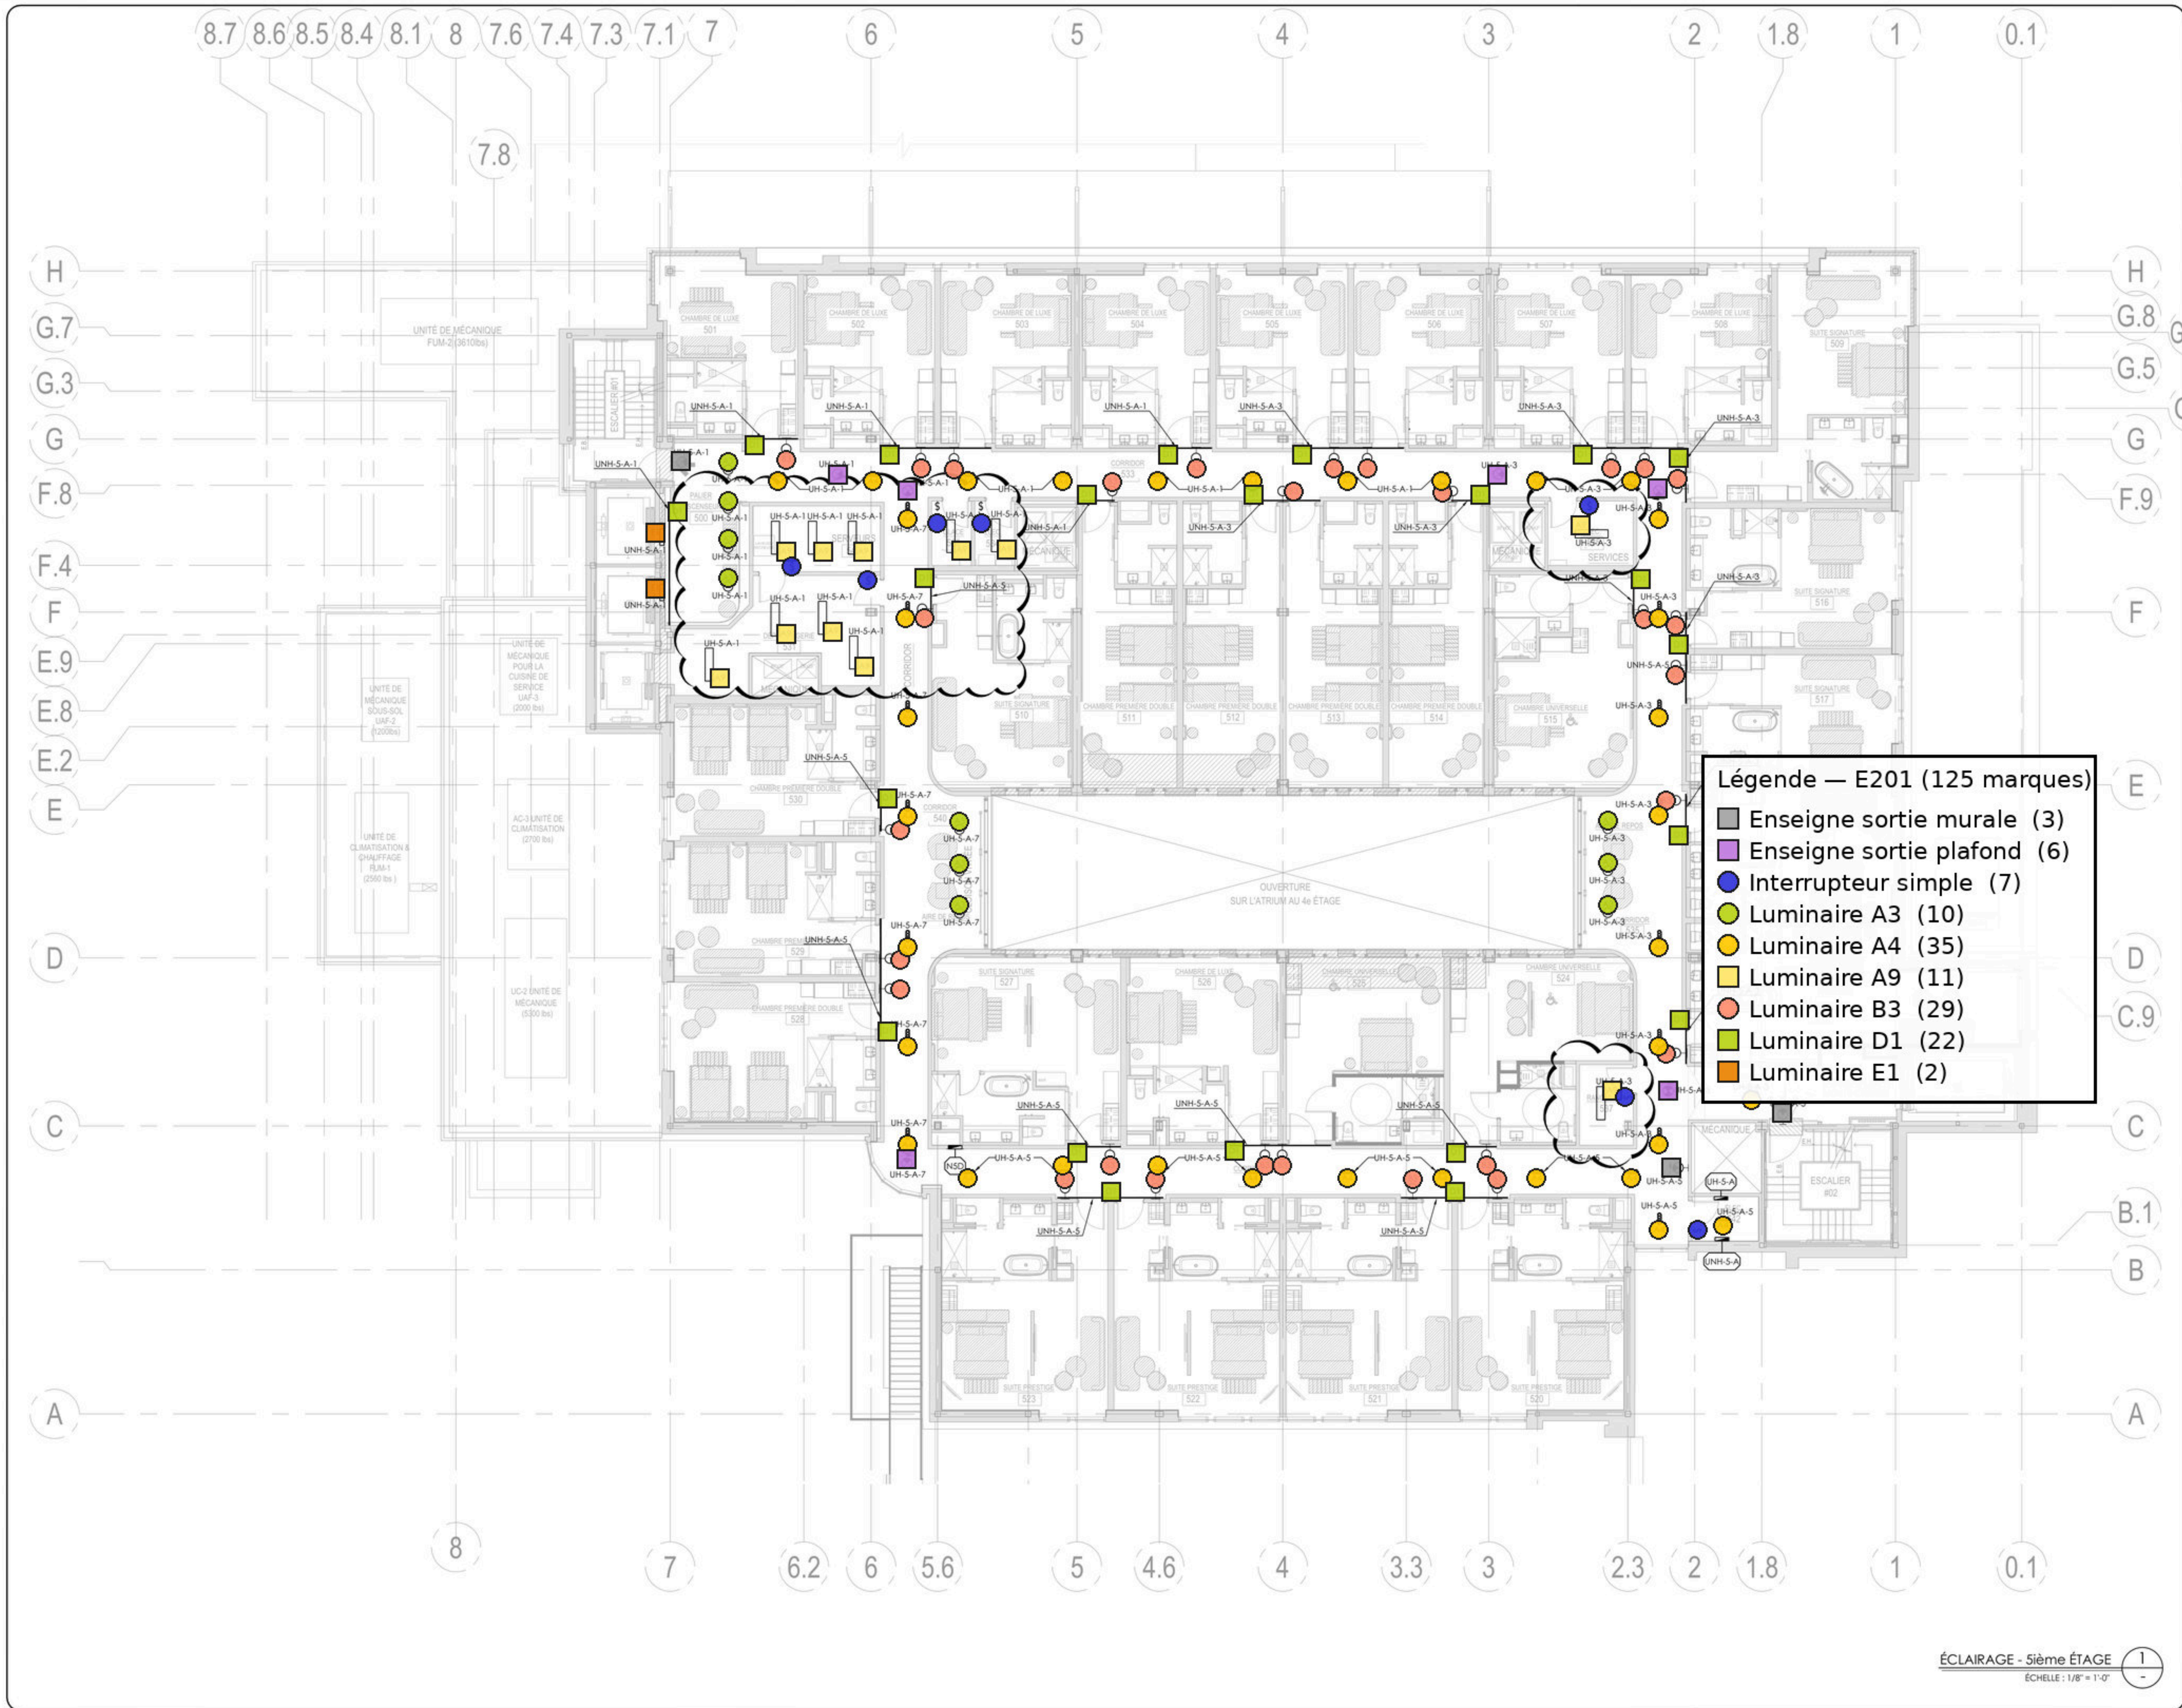

- Légende — E201 (125 marques)**
- Enseigne sortie murale (3)
 - Enseigne sortie plafond (6)
 - Interrupteur simple (7)
 - Luminaire A3 (10)
 - Luminaire A4 (35)
 - Luminaire A9 (11)
 - Luminaire B3 (29)
 - Luminaire D1 (22)
 - Luminaire E1 (2)

ÉCLAIRAGE - 8ième ÉTAGE
ÉCHELLE : 1/8" = 1'-0"

NOTE GÉNÉRALE

- COORDONNER LES CONTRÔLES D'ÉCLAIRAGE AVEC LE CLIENT (SYSTÈME LUTRON ET CONTRÔLE LOCAL).
- DANS LES CORRIDORS ET DANS LE JARDIN, PRÉVOIR UNE ZONE D'ÉCLAIRAGE PAR TYPE D'APPAREIL.

PLAN GÉNÉRAL

PROJET

lemay

20-02-26 APPEL D'OFFRES RÉVISION 1 M.S.
17-07-25 APPEL D'OFFRES M.S.
NO. J - M - A DESCRIPTION PAR

ÉMIS POUR:

DATE

2024-02-20

Experts conseils: mécanique électrique - électricité

BFA Blondin Fortin Associés

305, boul. Cyrille-Lapointe
Sudbury, Ontario, Canada
G1T 1A1
Tél. : 416-428-5555
www.blondinfortin.ca

PROJET

PLAYGROUND POKER

PROJET

PLAYGROUND HOTEL,
1 500 QC-138 C, KAHNAWAKE,
QC, J0L 1B0



DESCRIPTION

ÉLECTRICITÉ

ÉCLAIRAGE
8ième ÉTAGE

PRÉPARÉ PAR: M. SIMARD
VÉRIFIÉ PAR: G. BLONDIN
NO. DE PROJET: 2024-023


ÉCHELLE: TEL QU'INDIQUÉ
PLANCHE NO.: E-201

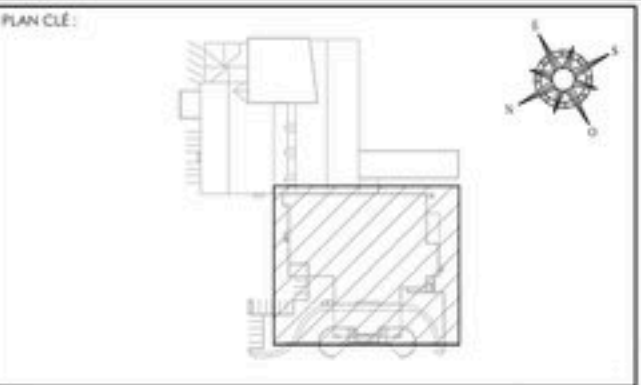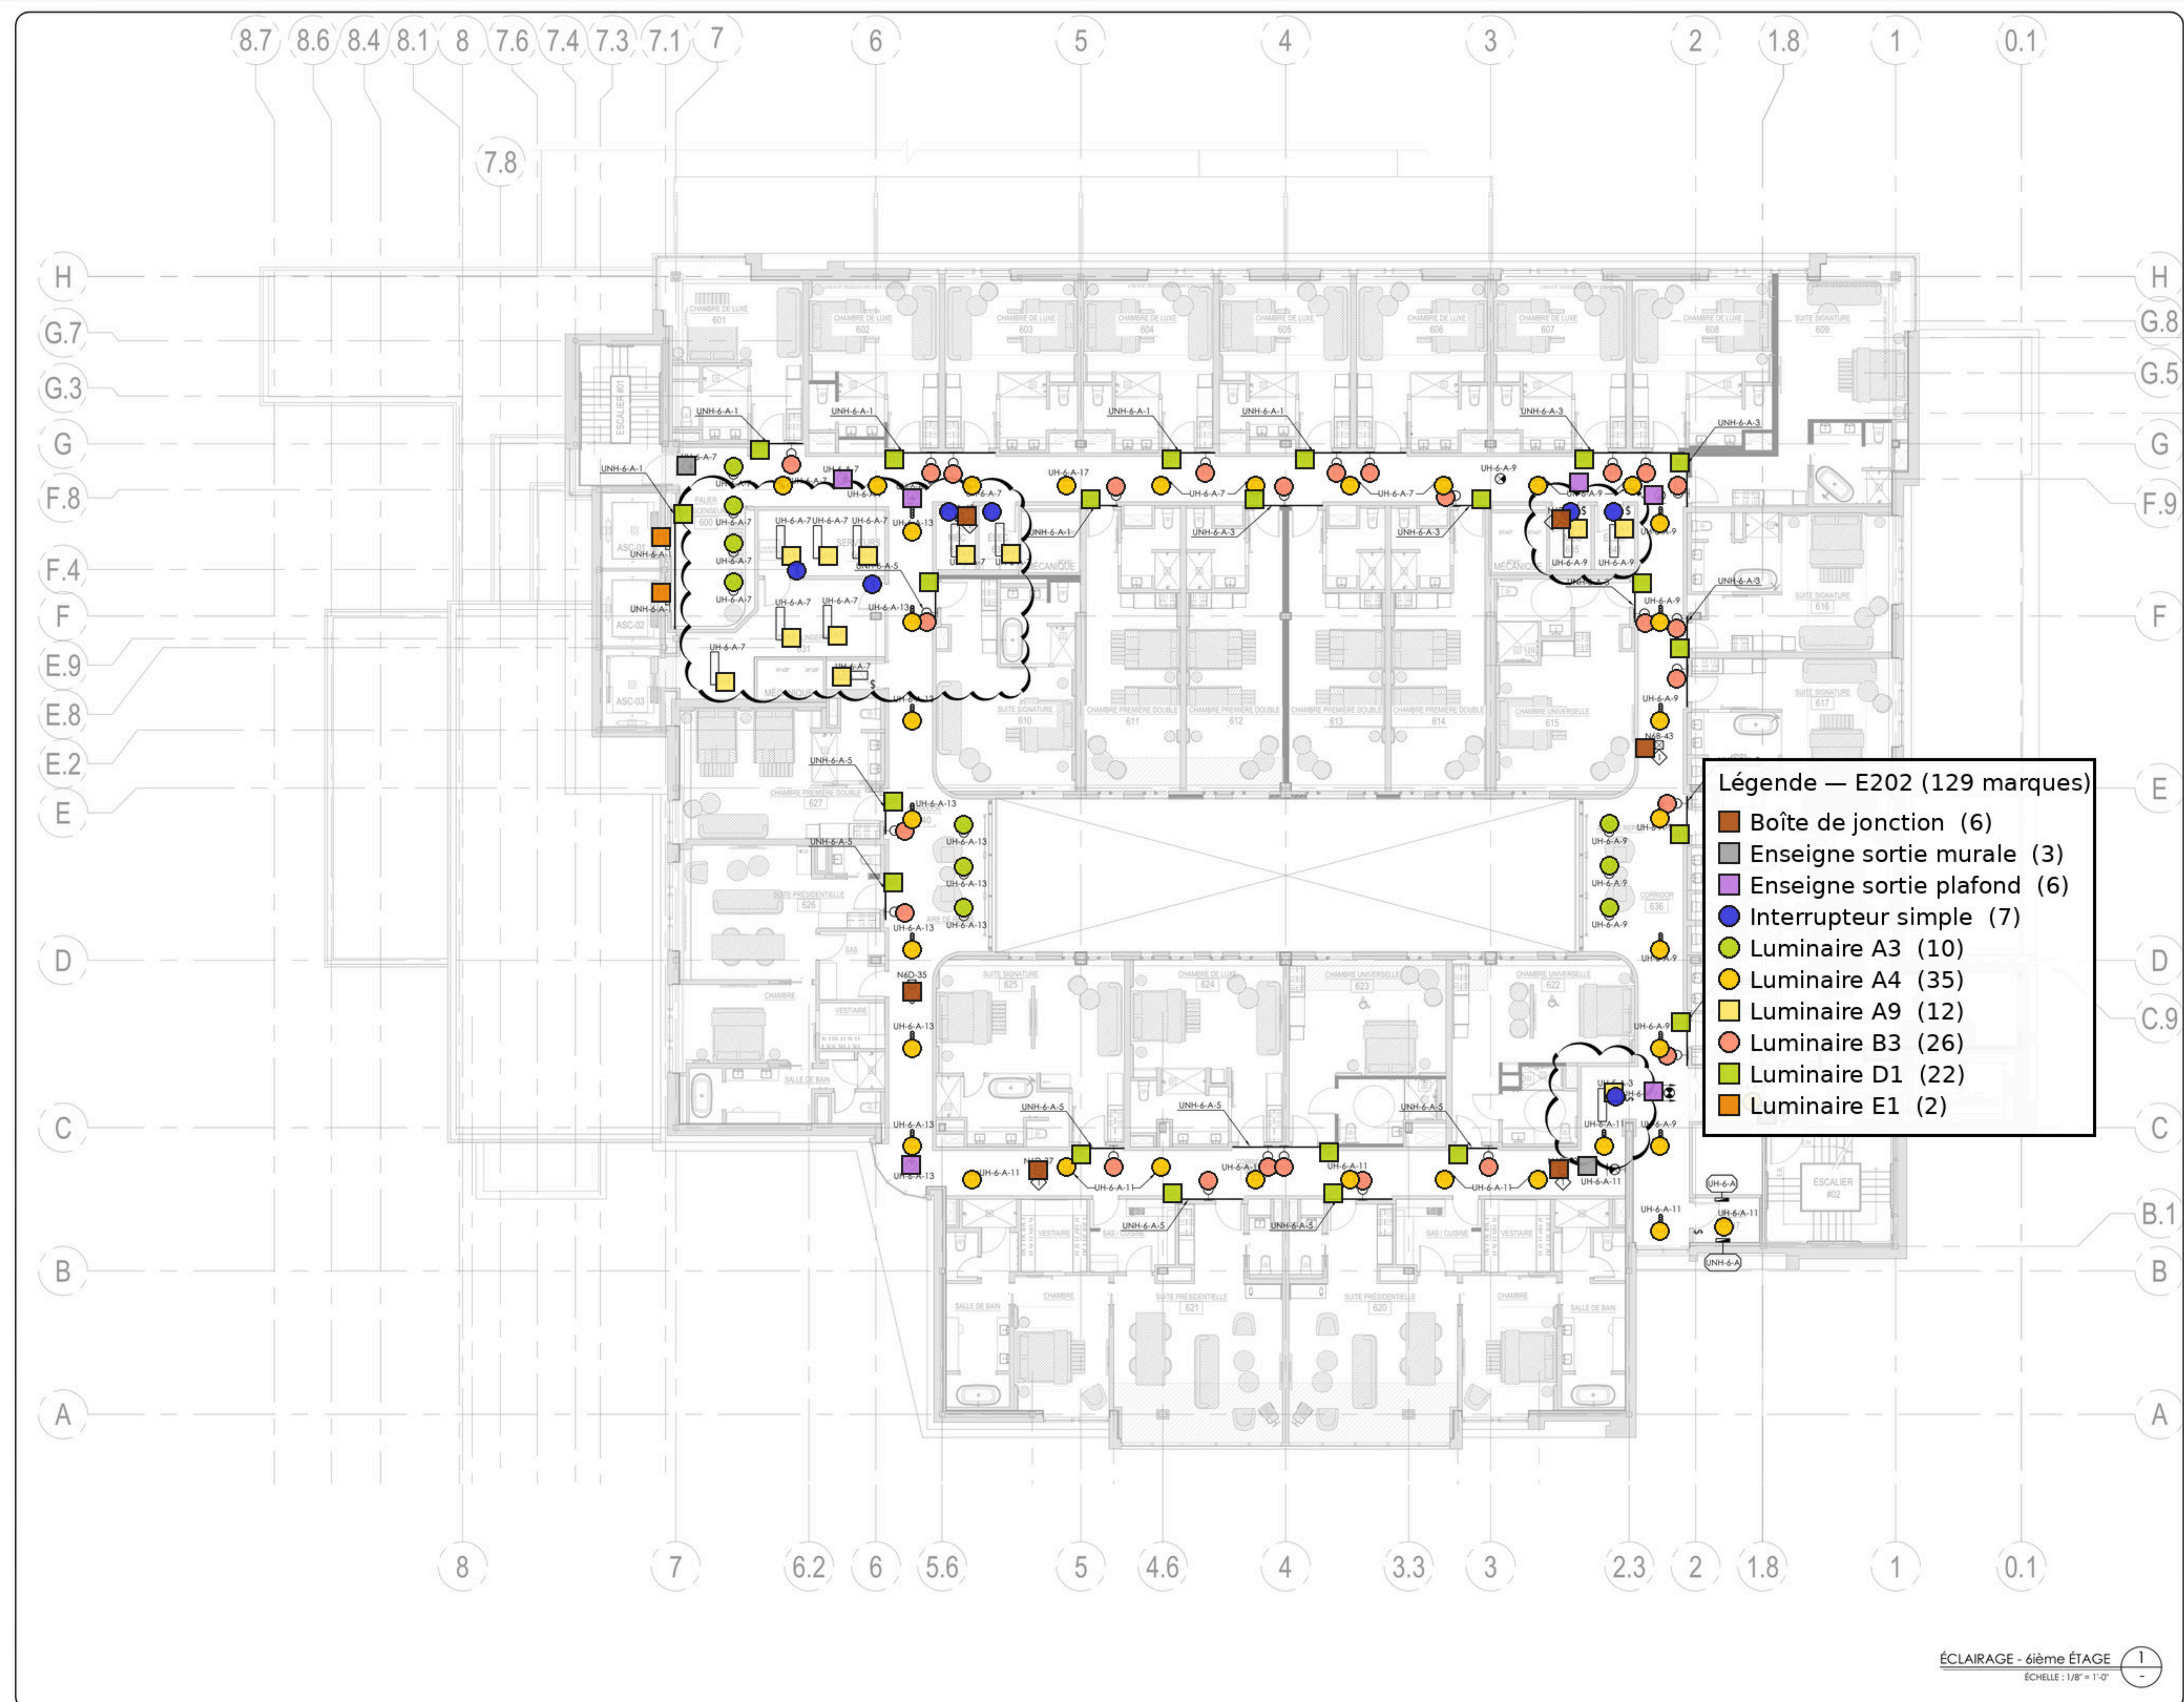[illegible]

PLAYGROUND POKER

PLAYGROUND HOTEL,
1 500 QC-138 C, KAHNAWAKE,
QC, J0L 1B0


ÉLECTRICITÉ	
ÉCLAIRAGE 6ième ÉTAGE	
PRÉPARÉ PAR: M. SIMARD	ÉCHELLE: TEL QU'INDIQUÉ
RESSORTI PAR: G. BLONDIN	PLANCHE NO:
NO DE PROJET: 2024-023	E-202

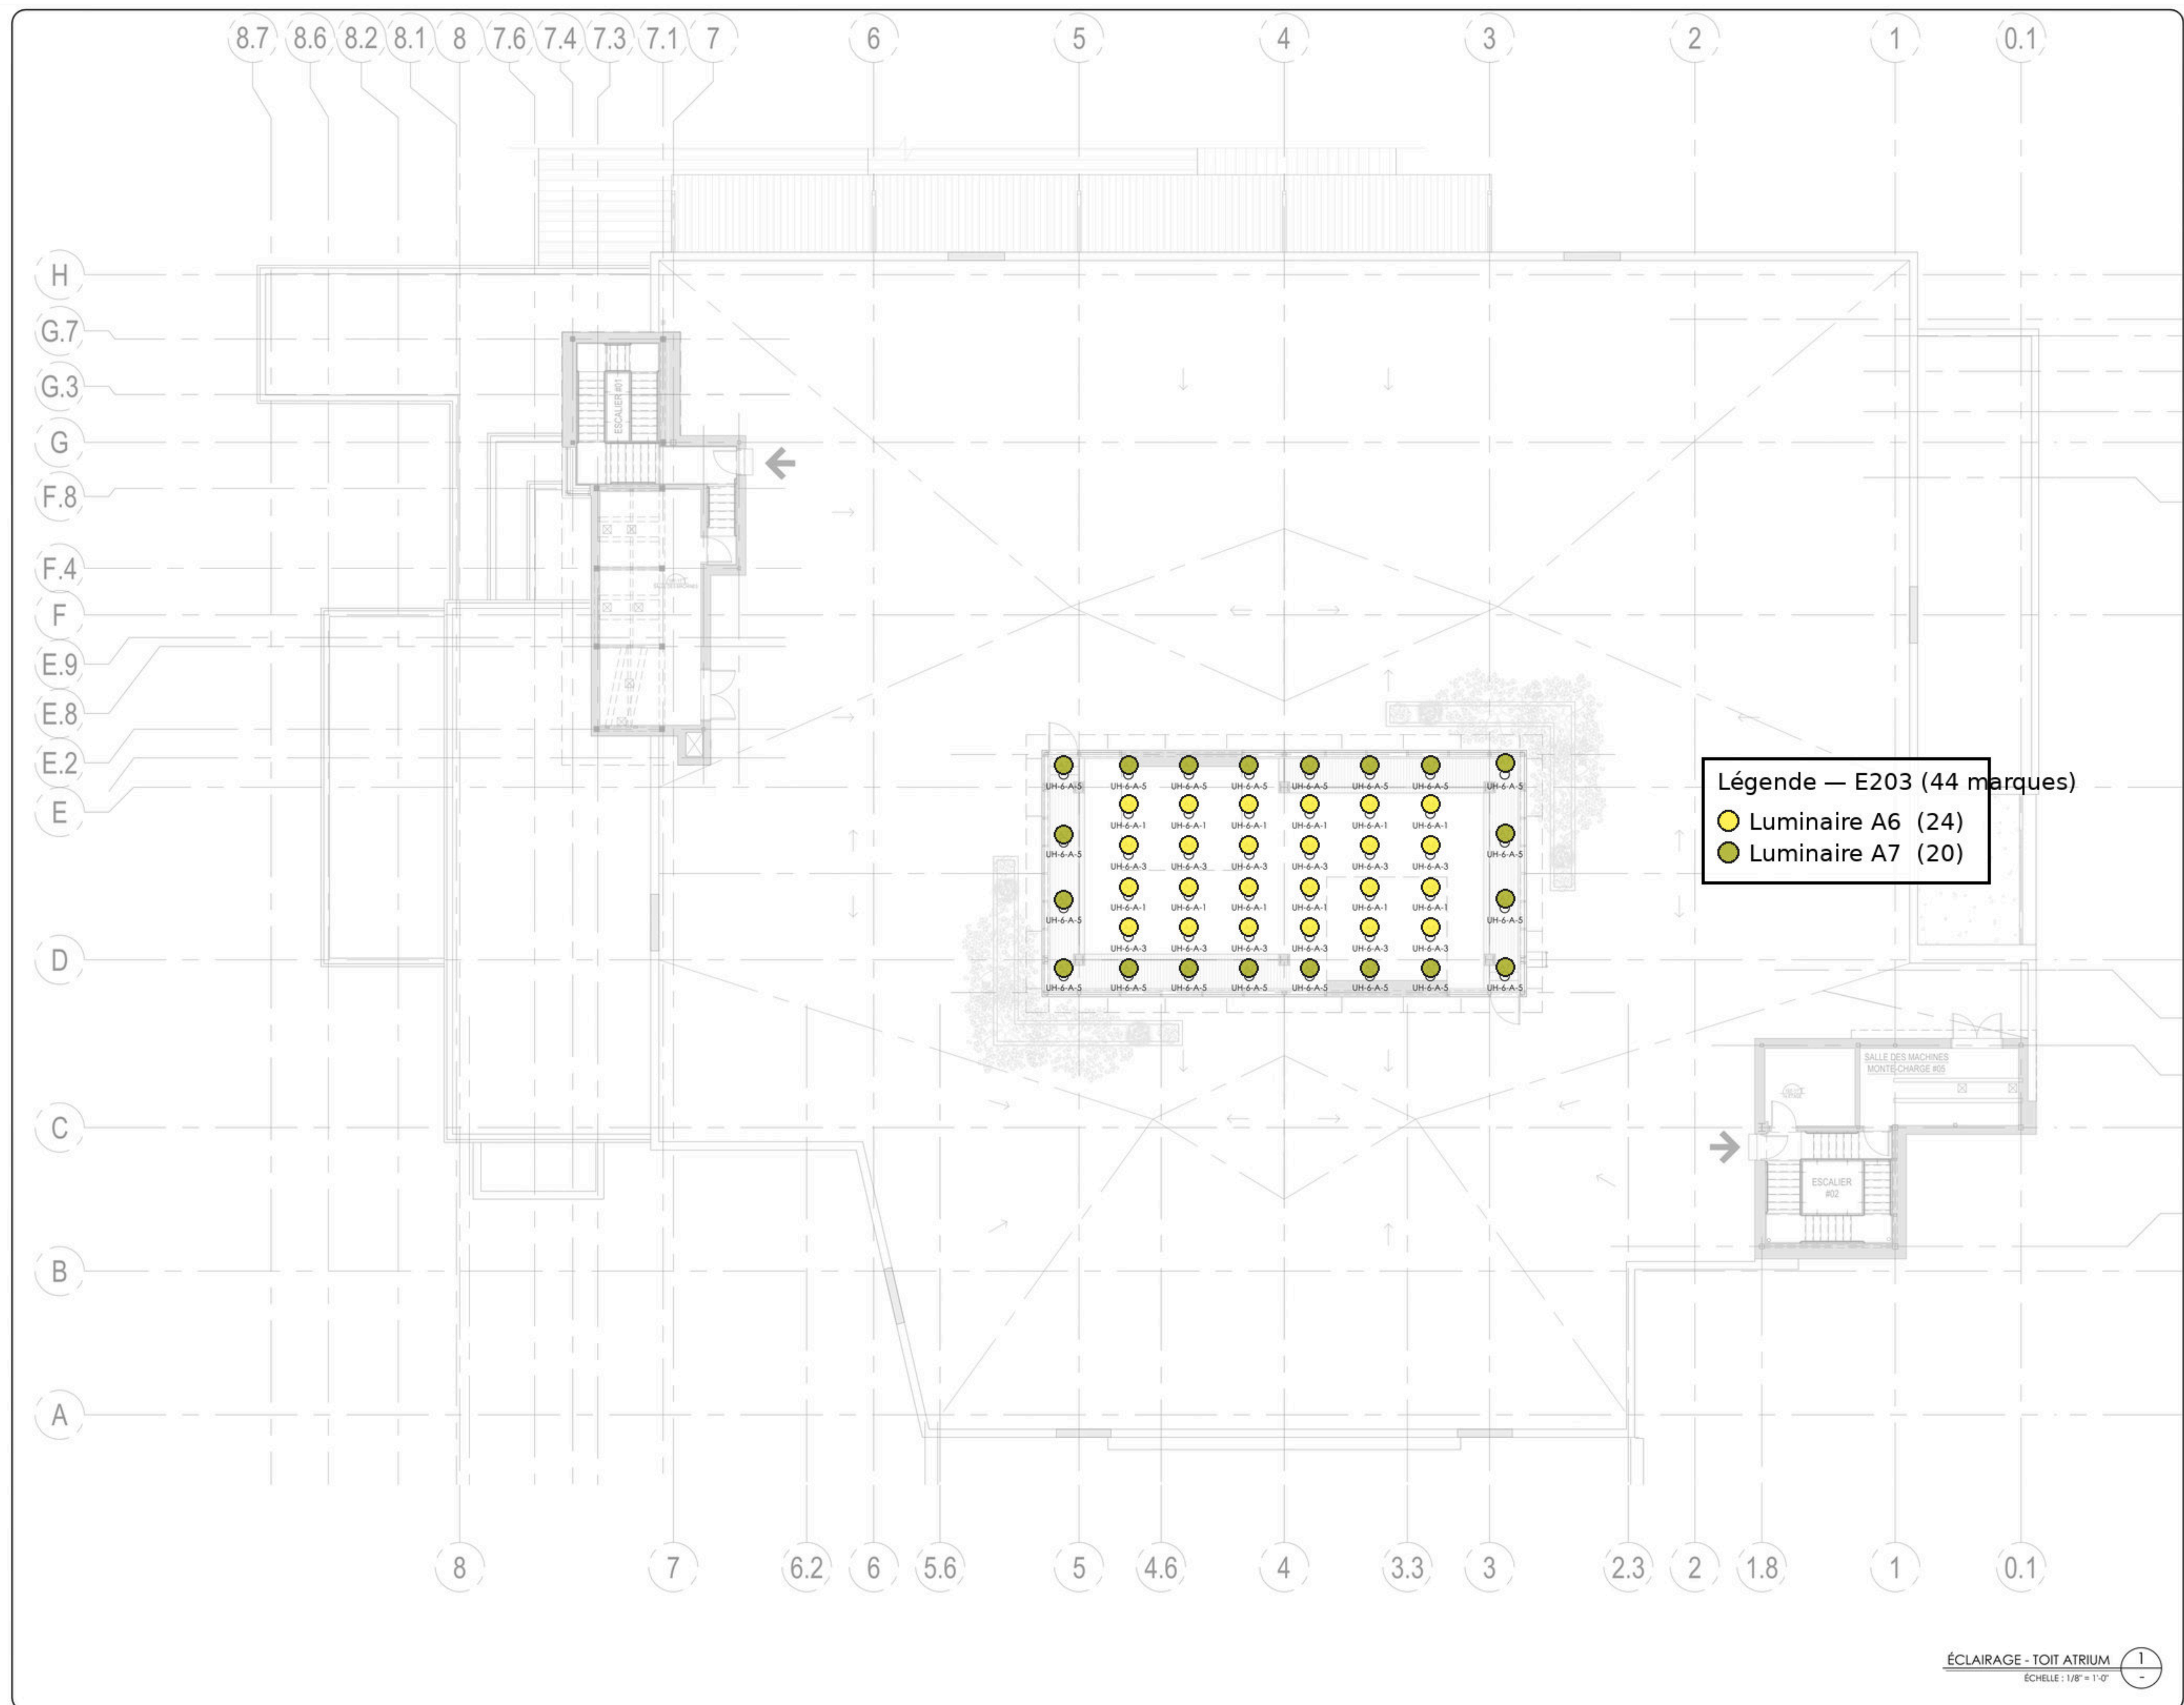

ÉCLAIRAGE - TOIT ATRIUM
ÉCHELLE : 1/8" = 1'-0"

NOTE GÉNÉRALE

- A** COORDONNER LES CONTRÔLES D'ÉCLAIRAGE AVEC LE CLIENT (SYSTÈME LUTRON ET CONTRÔLE LOCAL).
- B** DANS LES CORRIDORS ET DANS LE JARDIN, PRÉVOIR UNE ZONE D'ÉCLAIRAGE PAR TYPE D'APPAREIL.

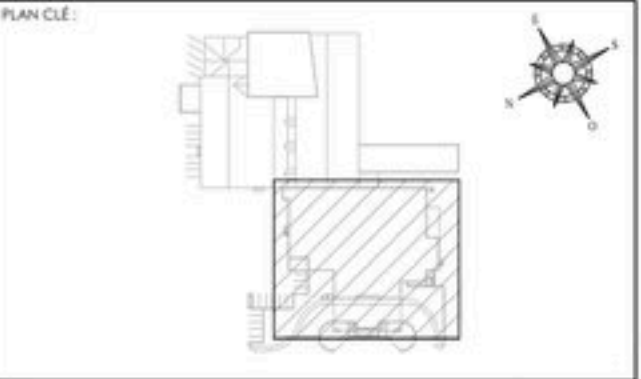


NOTES:

[illegible]

PLAYGROUND POKER


PLAYGROUND HOTEL,
1 500 QC-138 C, KAHNAWAKE,
QC, J0L 1B0

DISCIPLINE:		ÉLECTRICITÉ	
OBJET DU PLAN:			
ÉCLAIRAGE TOIT ATRIUM			
RÉFÉREncer PAR:		ÉCHELLE:	
M. SIMARD		TEL QU'INDIQUÉ	
Dessiné PAR:		PLANCHE NO.:	
G. BLONDIN		E-203	
NO DE PROJET:			
2024-023			

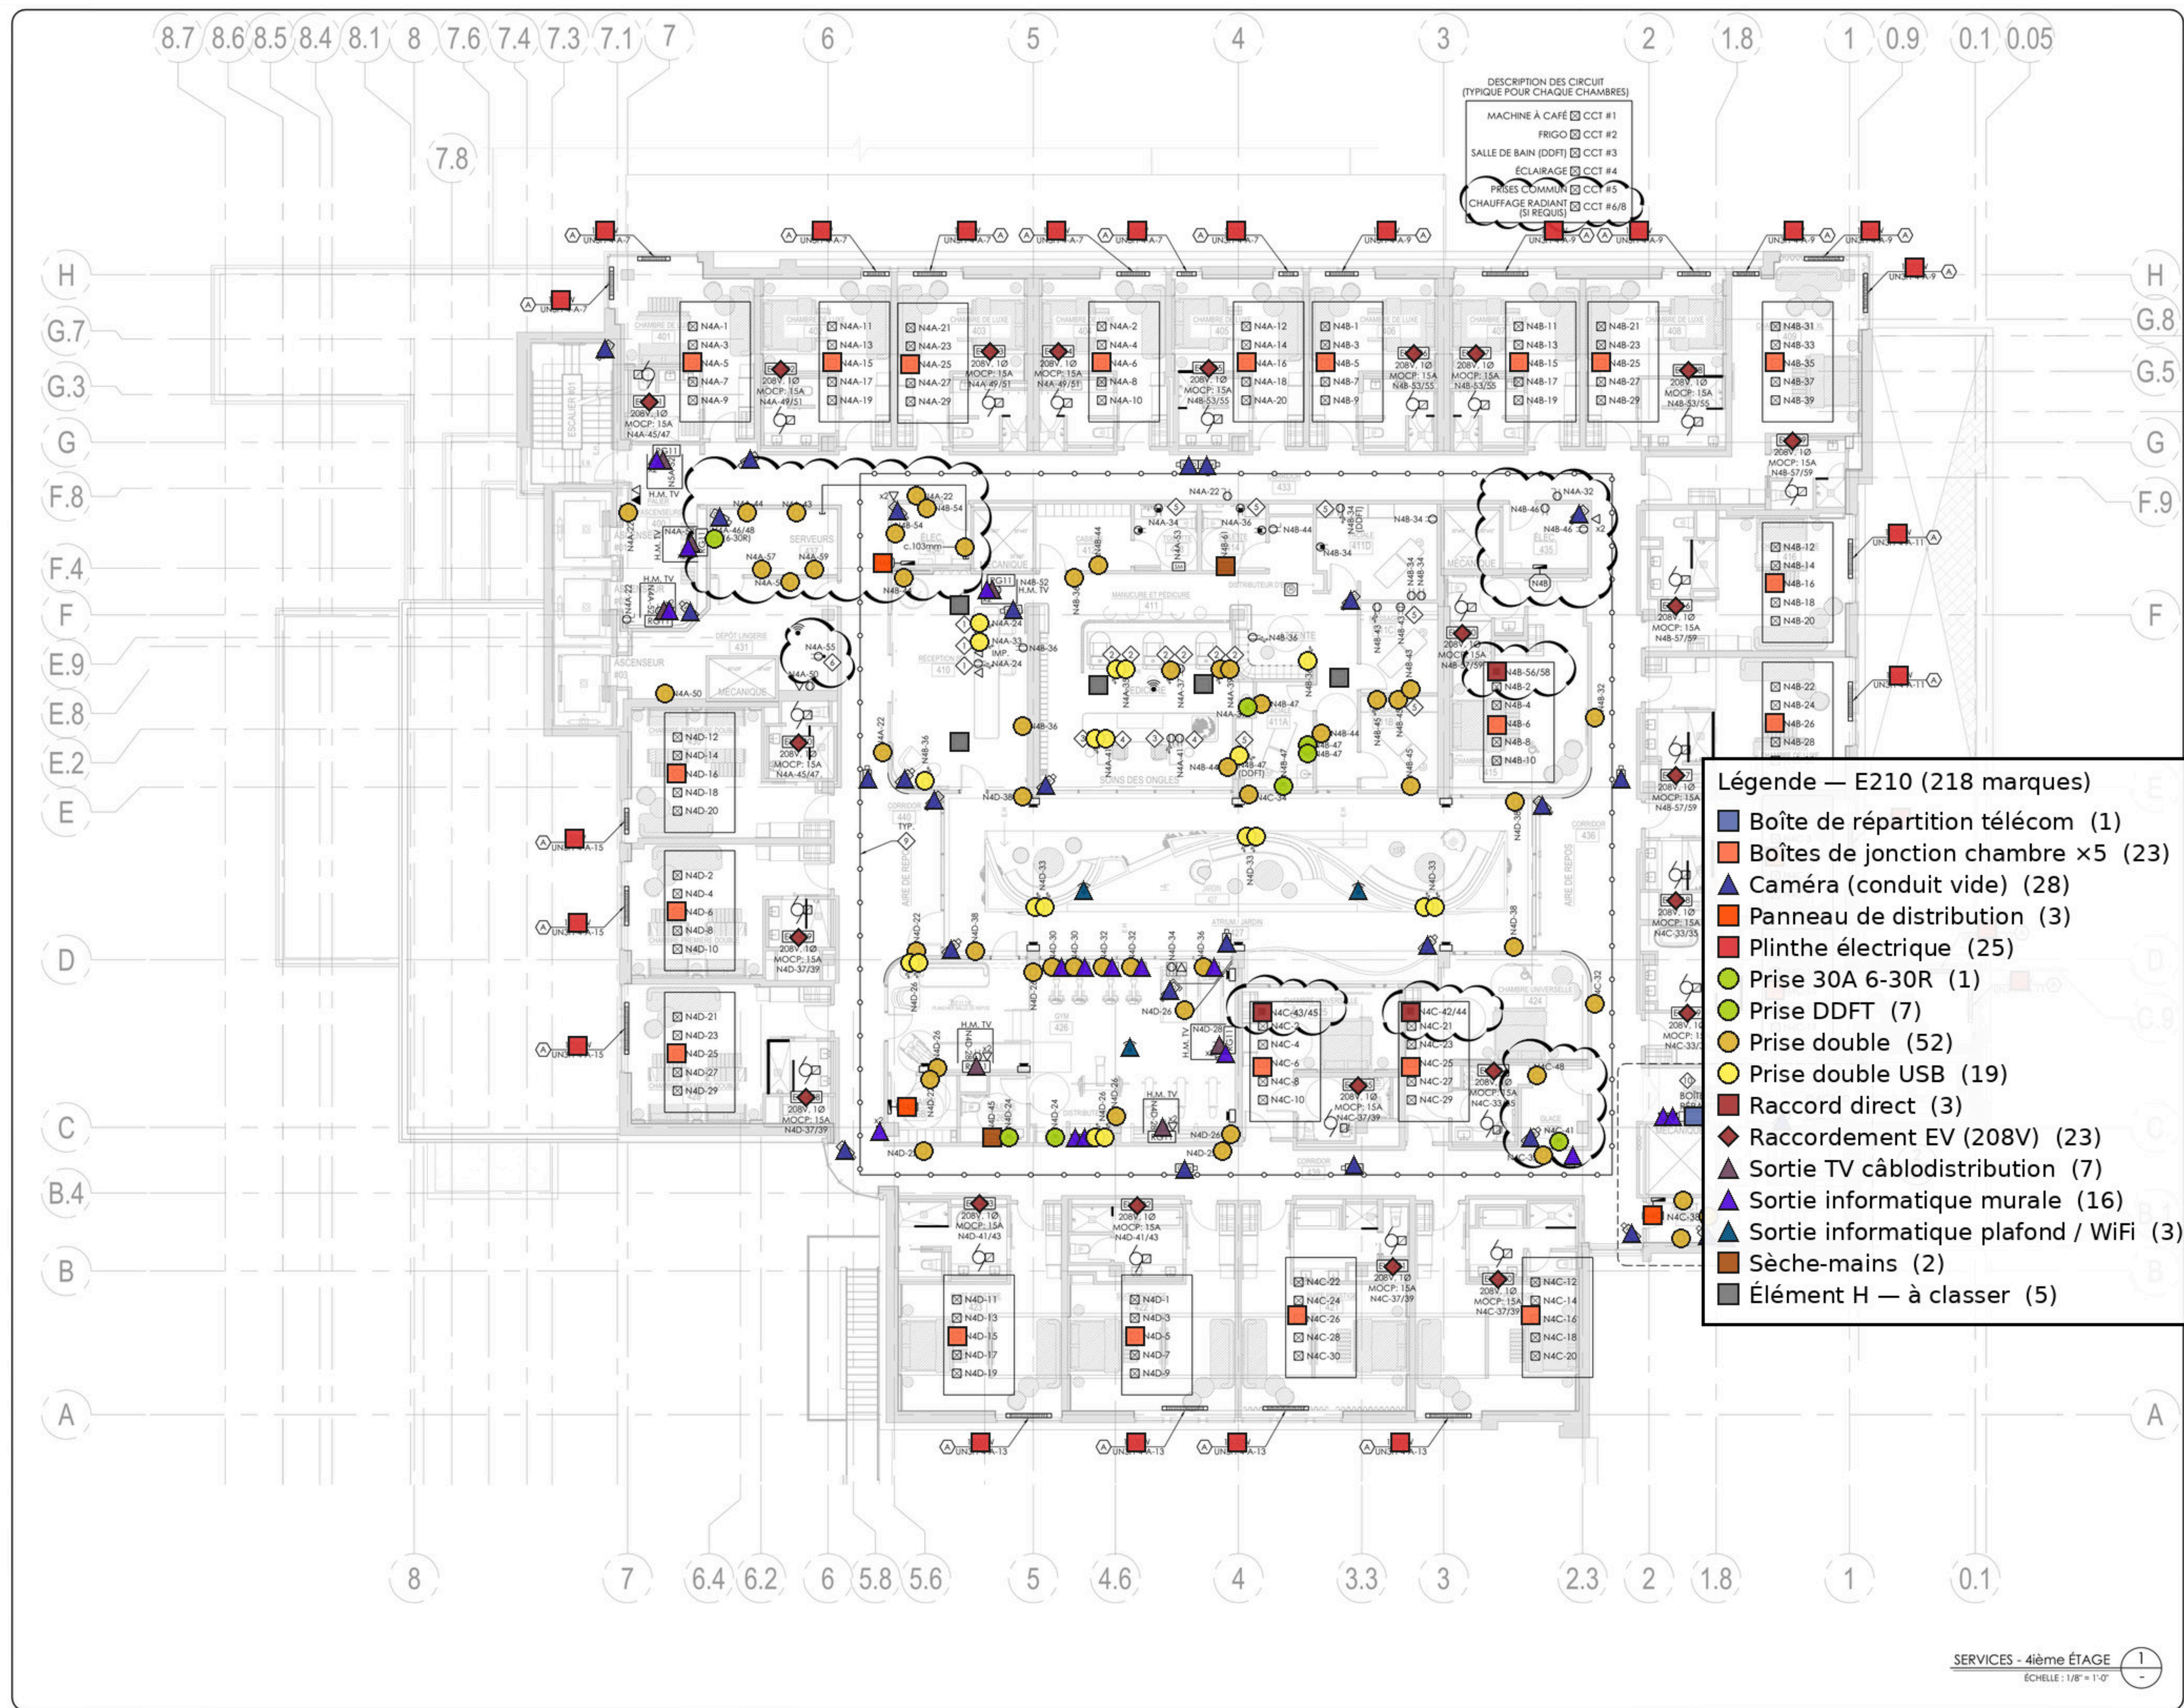

- Légende — E210 (218 marques)**
- Boîte de répartition télécom (1)
 - Boîtes de jonction chambre x5 (23)
 - Caméra (conduit vide) (28)
 - Panneau de distribution (3)
 - Plinthe électrique (25)
 - Prise 30A 6-30R (1)
 - Prise DDFT (7)
 - Prise double (52)
 - Prise double USB (19)
 - Raccord direct (3)
 - Raccordement EV (208V) (23)
 - Sortie TV câblodistribution (7)
 - Sortie informatique murale (16)
 - Sortie informatique plafond / WiFi (3)
 - Sèche-mains (2)
 - Élément H — à classer (5)

- NOTES SPÉCIFIQUES**
- HAUTEUR D'INSTALLATION À 34" DU PLANCHER FINI.
 - HAUTEUR D'INSTALLATION À 6" DU PLANCHER FINI.
 - HAUTEUR D'INSTALLATION À 12" DU PLANCHER FINI.
 - HAUTEUR D'INSTALLATION À 36" DU PLANCHER FINI.
 - HAUTEUR D'INSTALLATION À 40" DU PLANCHER FINI.
 - POSITION DE LA PRISE POUR LA DÉTECTION DE FUITE À COORDONNER AVEC L'ENTREPRENEUR EN PLOMBERIE.
 - N/A
 - N/A
 - CROCHETS DE SUSPENSION POUR CÂBLES RÉSEAU (L'ÉCHELON À TOUS LES 1.2m).
 - INTERCEPTER LE CONDUIT EXISTANT VIA LA BOÎTE DE RÉPARATION ET LE PROLONGER JUSQU'À LA POSITION DU PANNEAU D'ÉLECTRICITÉ ET LE RACCORDER.

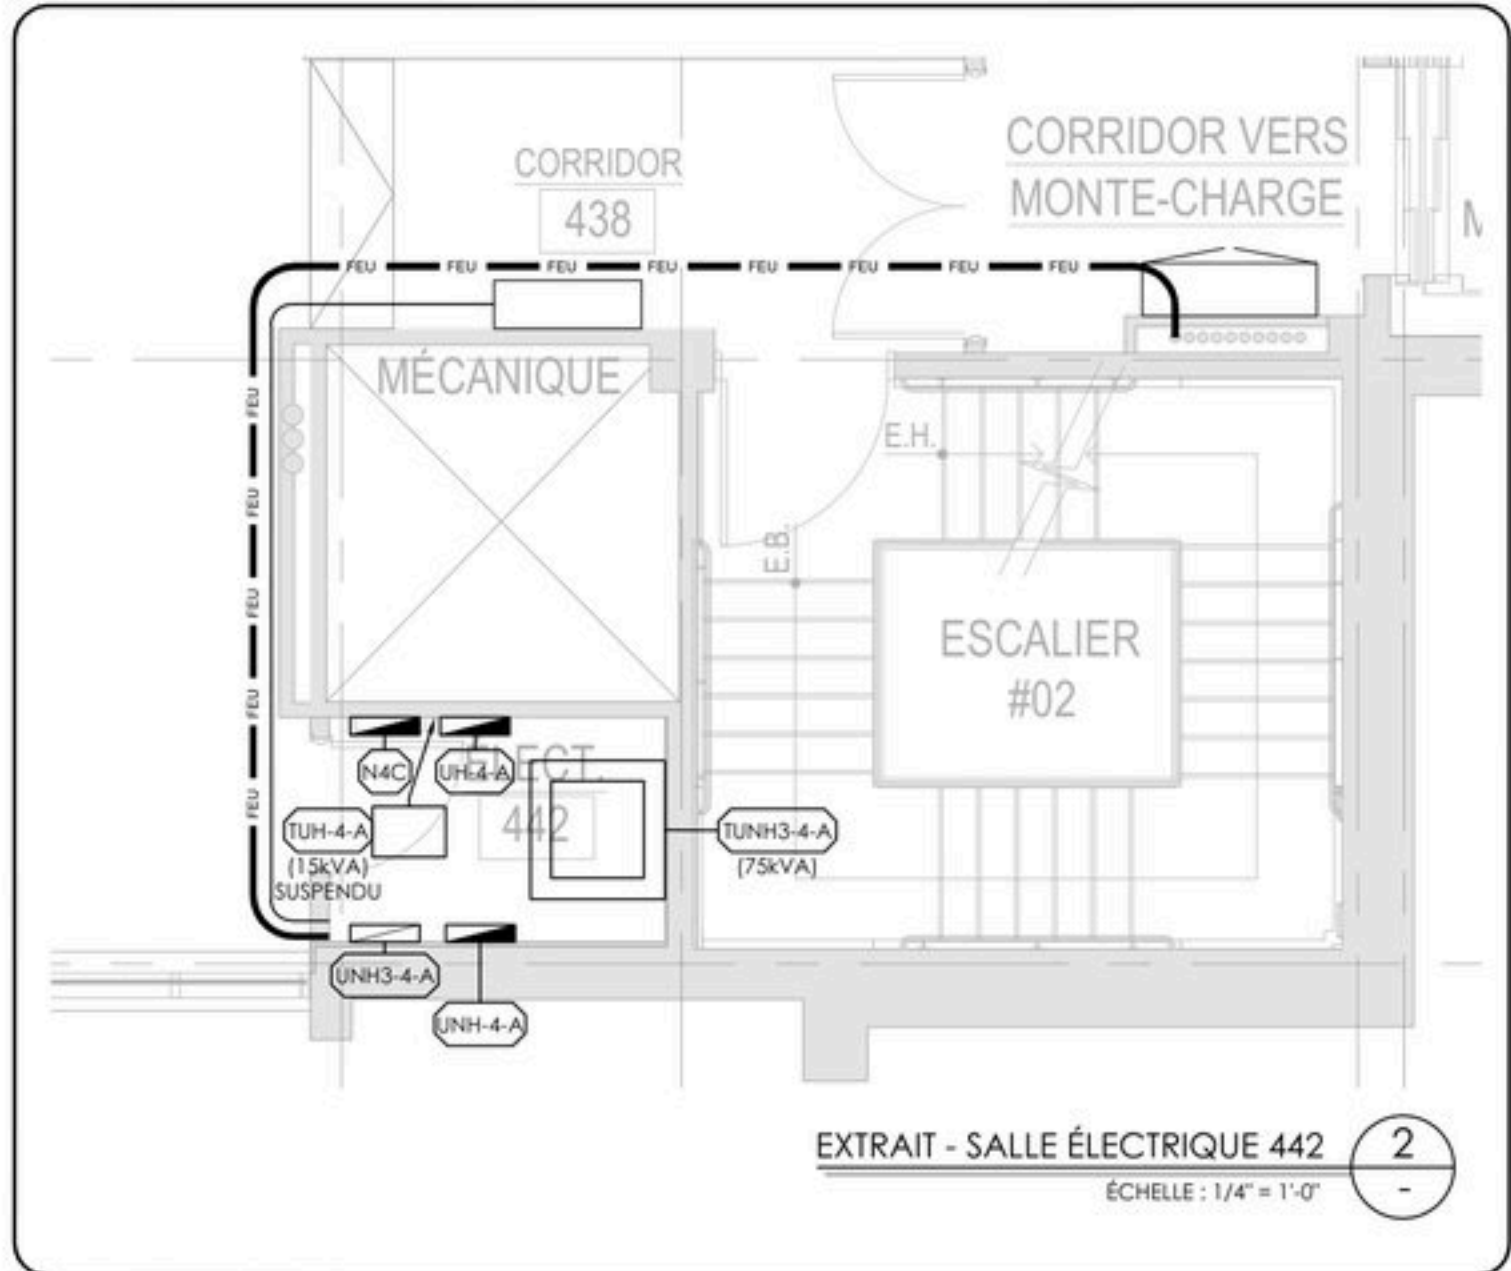

le may

NE PAS UTILISER POUR CONSTRUCTION

NO.	J - M - A	DESCRIPTION	PAR
2	20-02-26	APPEL D'OFFRES RÉVISION 1	M.S.
1	23-09-25	ADDENDA ME-01	M.S.
0	17-07-25	APPEL D'OFFRES	M.S.

ÉMIS POUR:

BFA
Blondin Fortin Associés

Experts conseil - mécanique
électrique - électricité

305, boul. Cyrille-Lapointe
Suite 200, 2000
Québec H1L 2P9
Tél. : 418-428-5555
www.blondinfortin.ca

PLAYGROUND POKER


PLAYGROUND HOTEL,
1 500 QC-138 C, KAHNAWAKE,
QC, J0L 1B0

ÉLECTRICITÉ

SERVICES
4ième ÉTAGE


PRÉPARÉ PAR: M. SIMARD
Dessiné par: G. BLONDIN
2024-02-3

ÉCHELLE: TEL QU'INDIQUÉ
PLANCHE NO: E-210

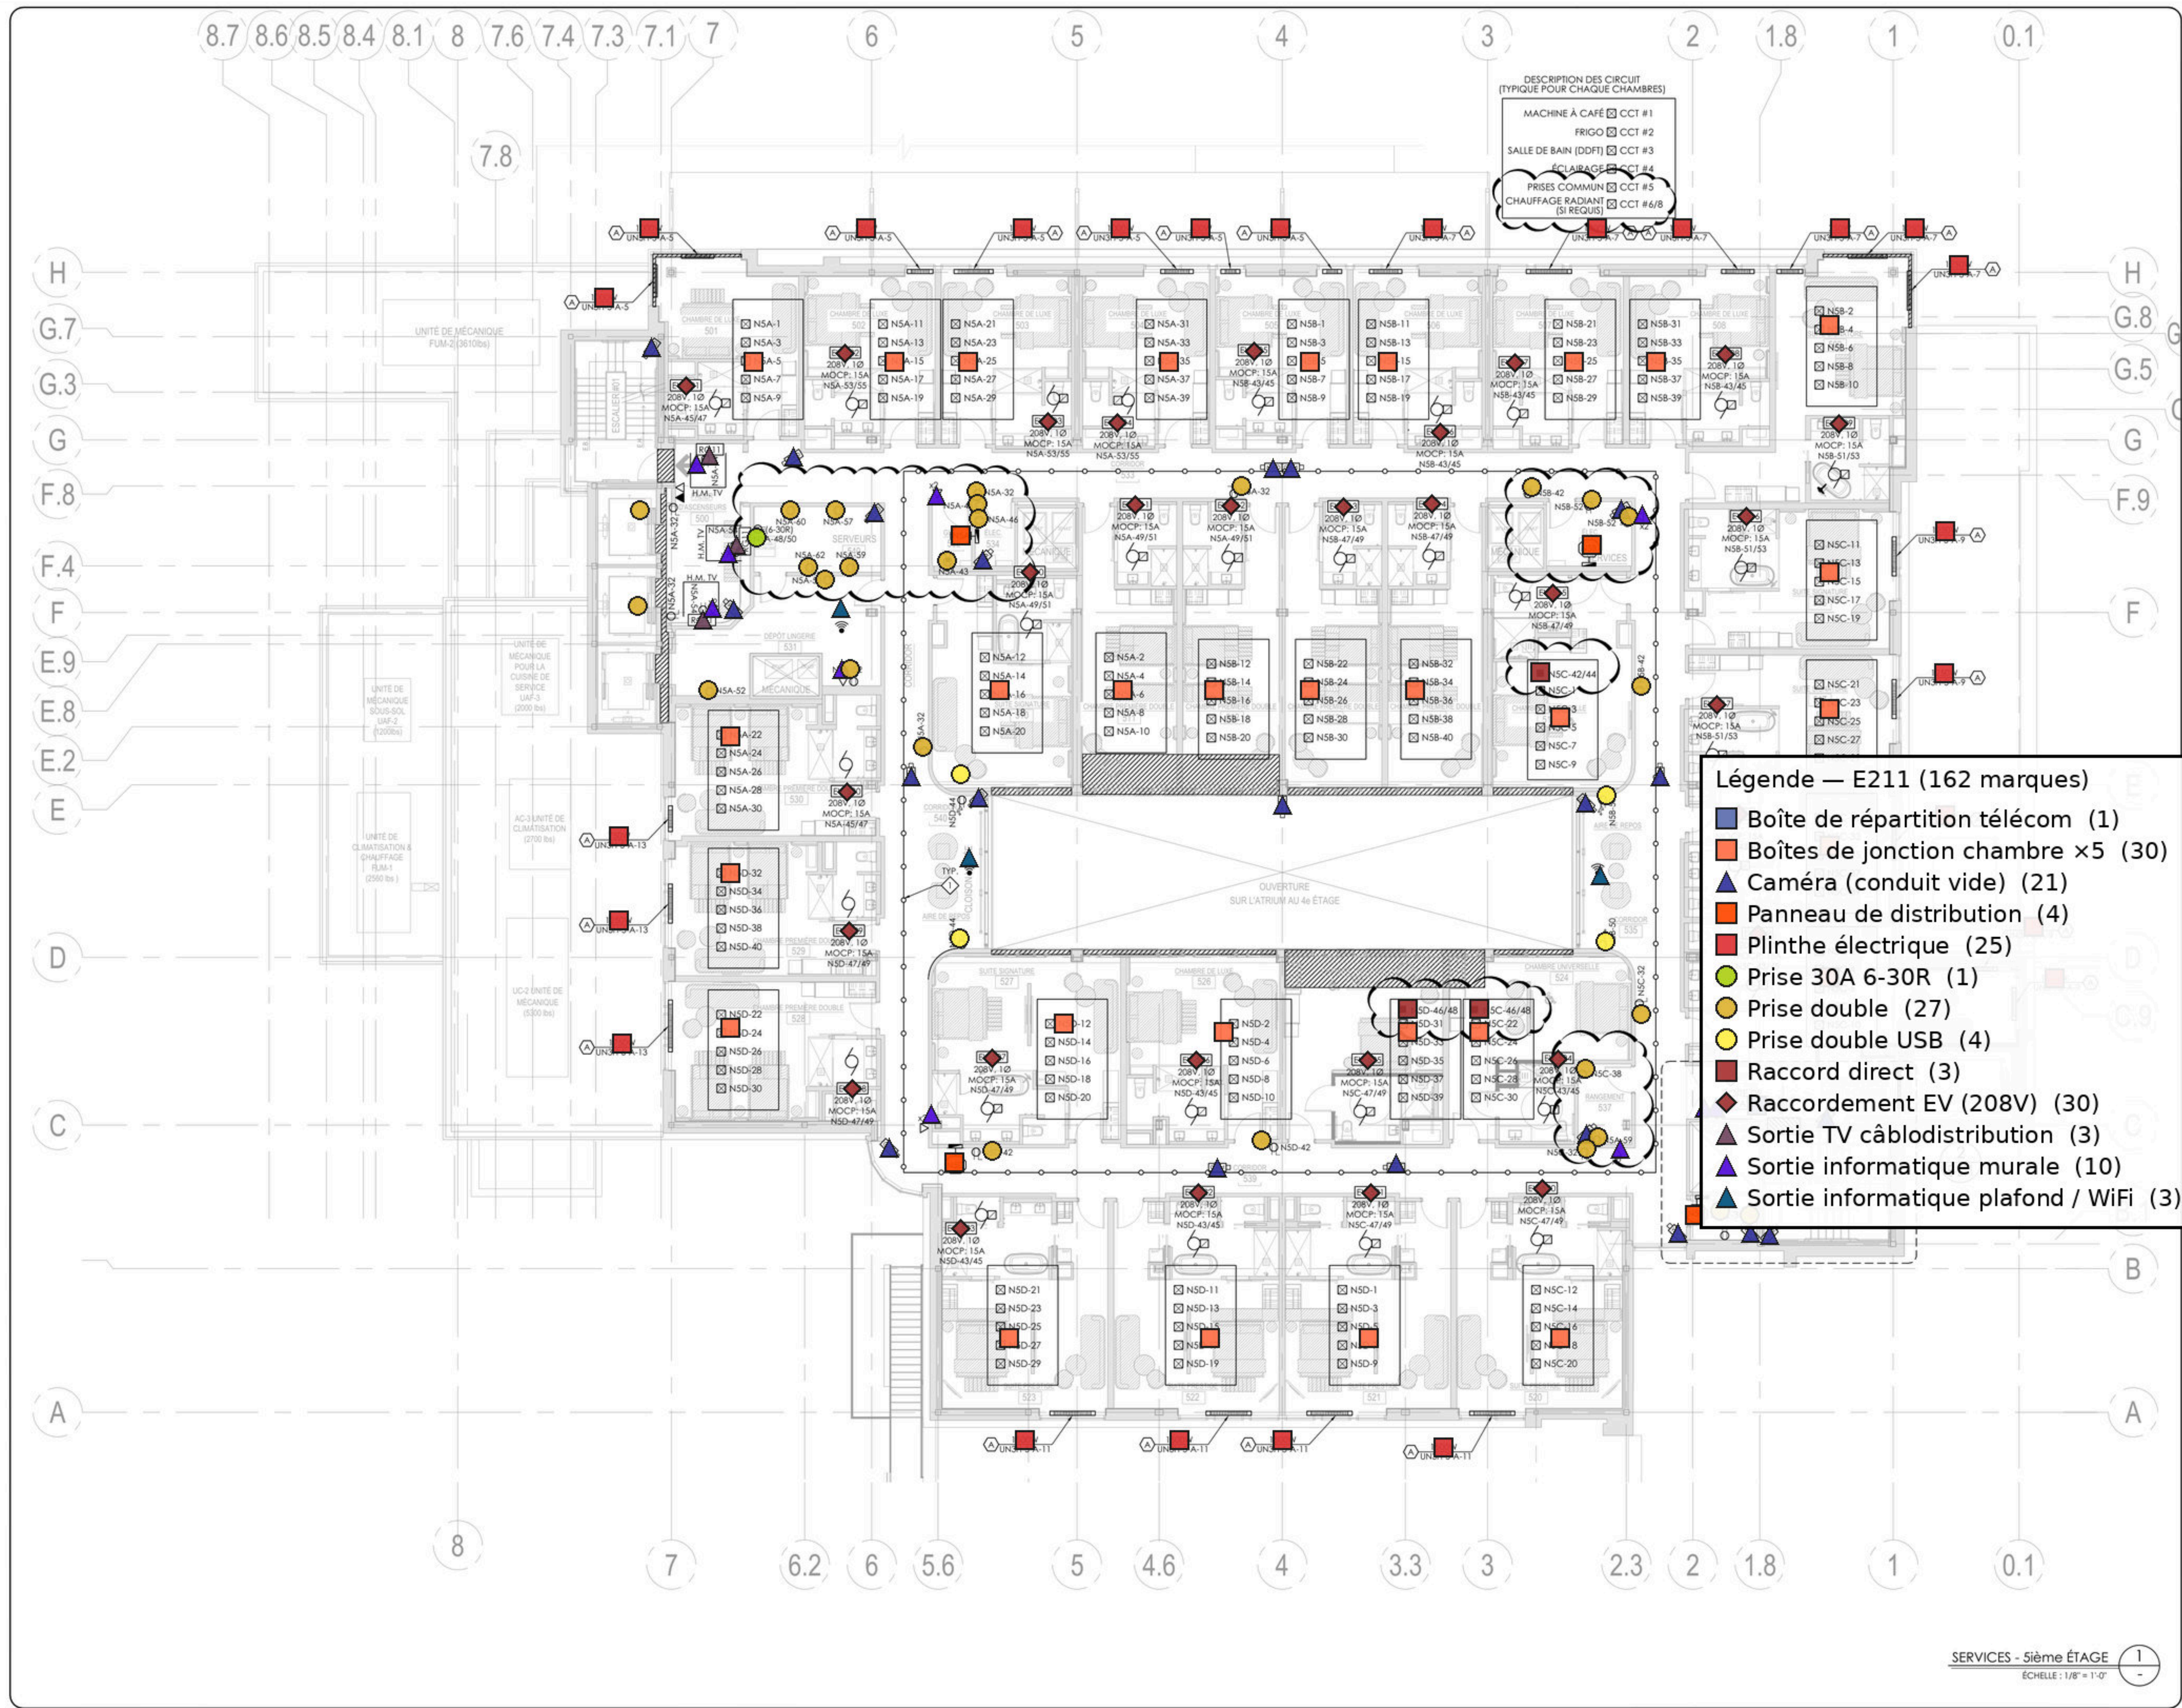

NOTES SPÉCIFIQUES

- ◇ CROCHETS DE SUSPENSION POUR CÂBLES RÉSEAU (HOOK) À TOUS LES 1.2m.
- ◇ INTERCÉPER LE CONDUIT EXISTANT VIA LA BOÎTE DE RÉPARTITION ET LE PROLONGER JUSQU'À LA POSITION DU PANNEAU D'ÉLECTRICITÉ ET LE RACCORDER.

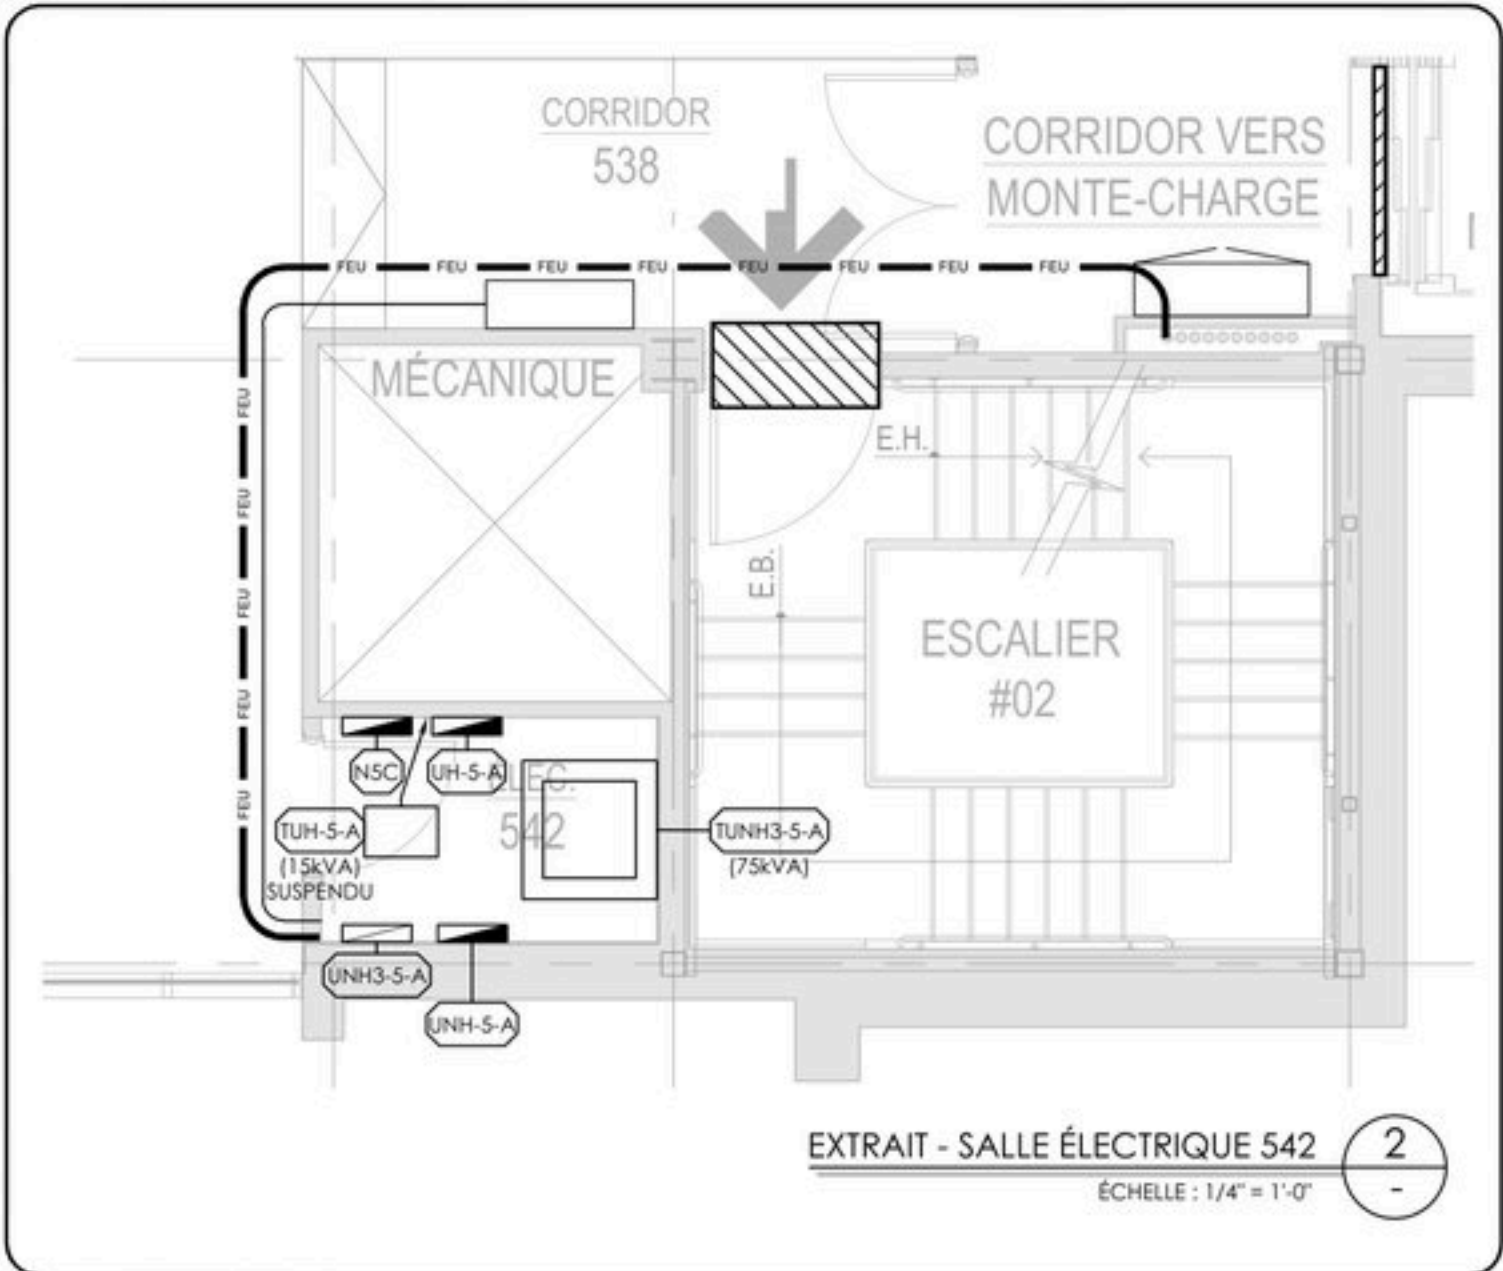

PLAN GÉNÉRAL

PROJET

NE PAS UTILISER POUR CONSTRUCTION

2	20-02-26	APPEL D'OFFRES RÉVISION 1	M.S.
1	24-09-25	ADDENDA ME-01	M.S.
0	17-07-25	APPEL D'OFFRES	M.S.
NO	J - M - A	DESCRIPTION	PAR

ÉMIS POUR:

PROJET


PROJET

PLAYGROUND POKER

PROJET

PLAYGROUND HOTEL,
1 500 QC-138 C, KAHNAWAKE,
QC, J0L 1B0

PROJET	ÉLECTRICITÉ
PROJET	SERVICES Sième ÉTAGE
PRÉPARÉ PAR	M. SIMARD
PROJETÉ PAR	G. BLONDIN
DATE DE RÉVISION	2024-02-3
ÉCHELLE	TEL QU'INDIQUÉ
PLANCHE NO	E-211

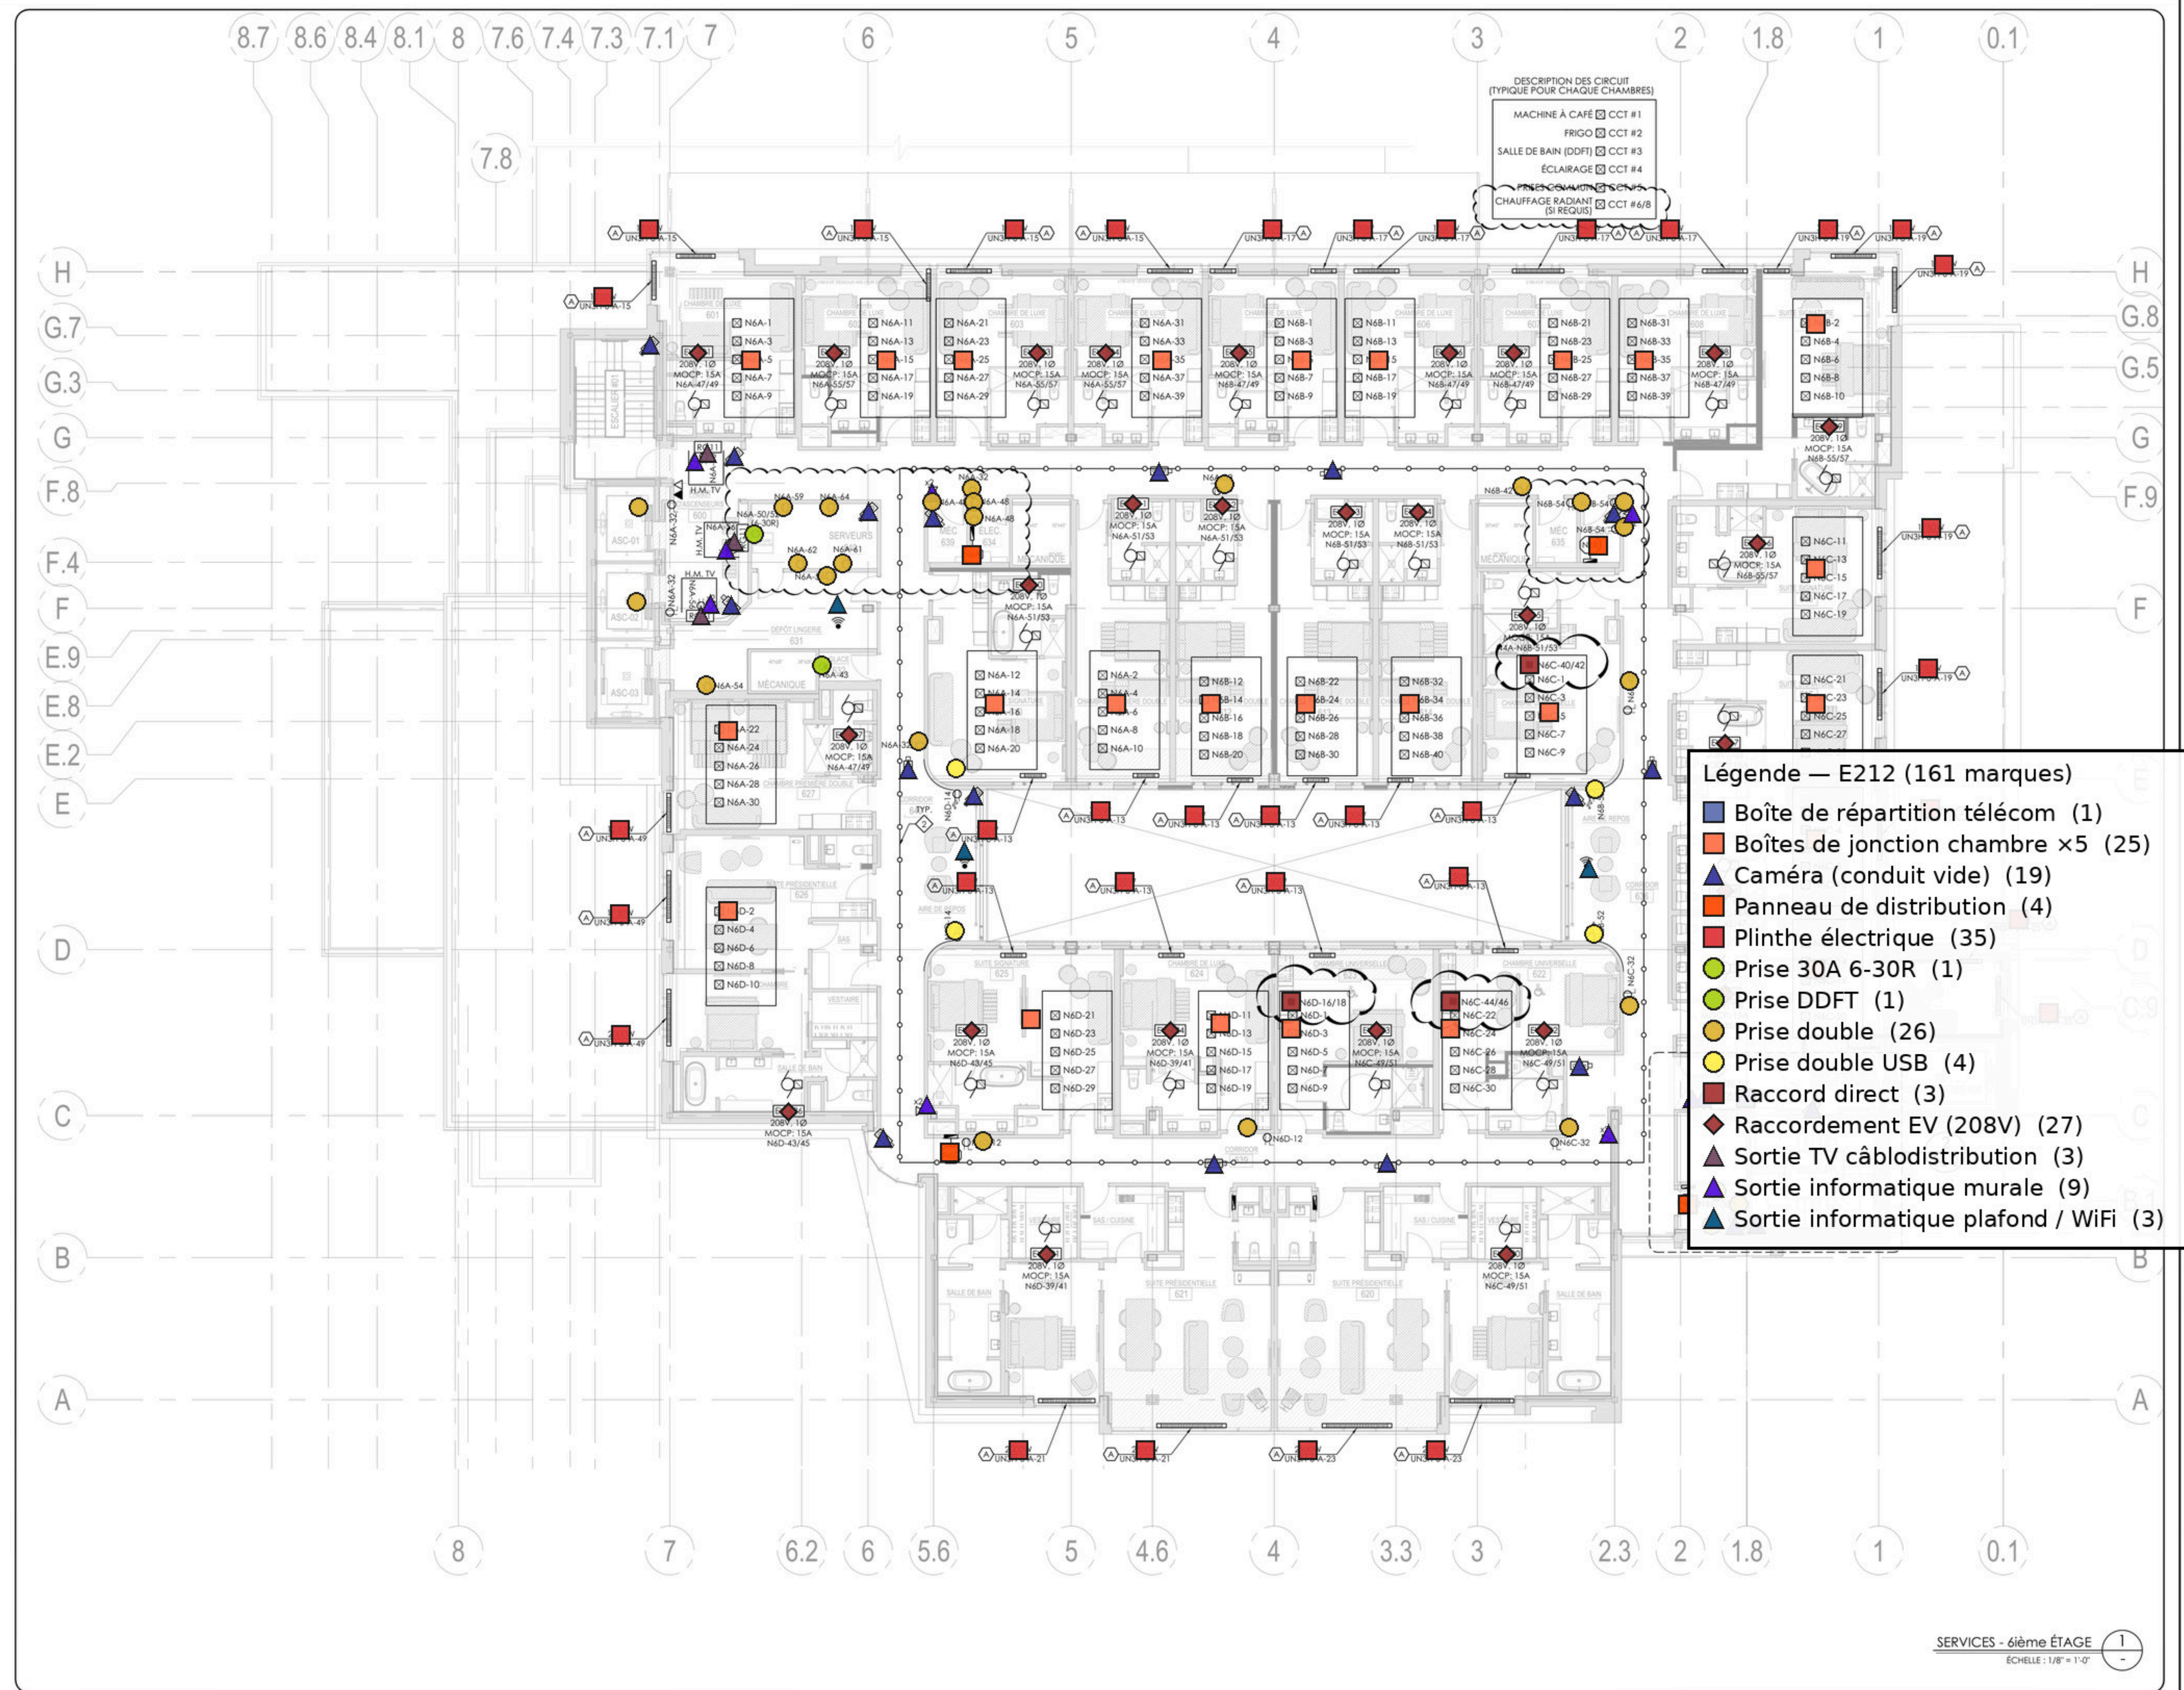

DESCRIPTION DES CIRCUITS
(TYPIQUE POUR CHAQUE CHAMBRE)


MACHINE À CAFÉ CCT #1
FRIGO CCT #2
SALLE DE BAIN (DDFT) CCT #3
ÉCLAIRAGE CCT #4

CHAUFFAGE RADIANT CCT #6/8
(SI REQUIS)

- Légende — E212 (161 marques)**
- Boîte de répartition télécom (1)
 - Boîtes de jonction chambre x5 (25)
 - Caméra (conduit vide) (19)
 - Panneau de distribution (4)
 - Plinthe électrique (35)
 - Prise 30A 6-30R (1)
 - Prise DDFT (1)
 - Prise double (26)
 - Prise double USB (4)
 - Raccord direct (3)
 - Raccordement EV (208V) (27)
 - Sortie TV câblodistribution (3)
 - Sortie informatique murale (9)
 - Sortie informatique plafond / WiFi (3)

NOTES SPÉCIFIQUES

- N/A
- CROCHETS DE SUSPENSION POUR CÂBLES RÉSEAU (J-HOOK) À TOUTS LES 1.2m.
- INTERCEPTER LE CONDUIT EXISTANT VIA LA BOÎTE DE RÉPARATION ET LE PROLONGER JUSQU'À LA POSITION DU PANNEAU D'ÉLECTRICITÉ ET LE RACCORDER.

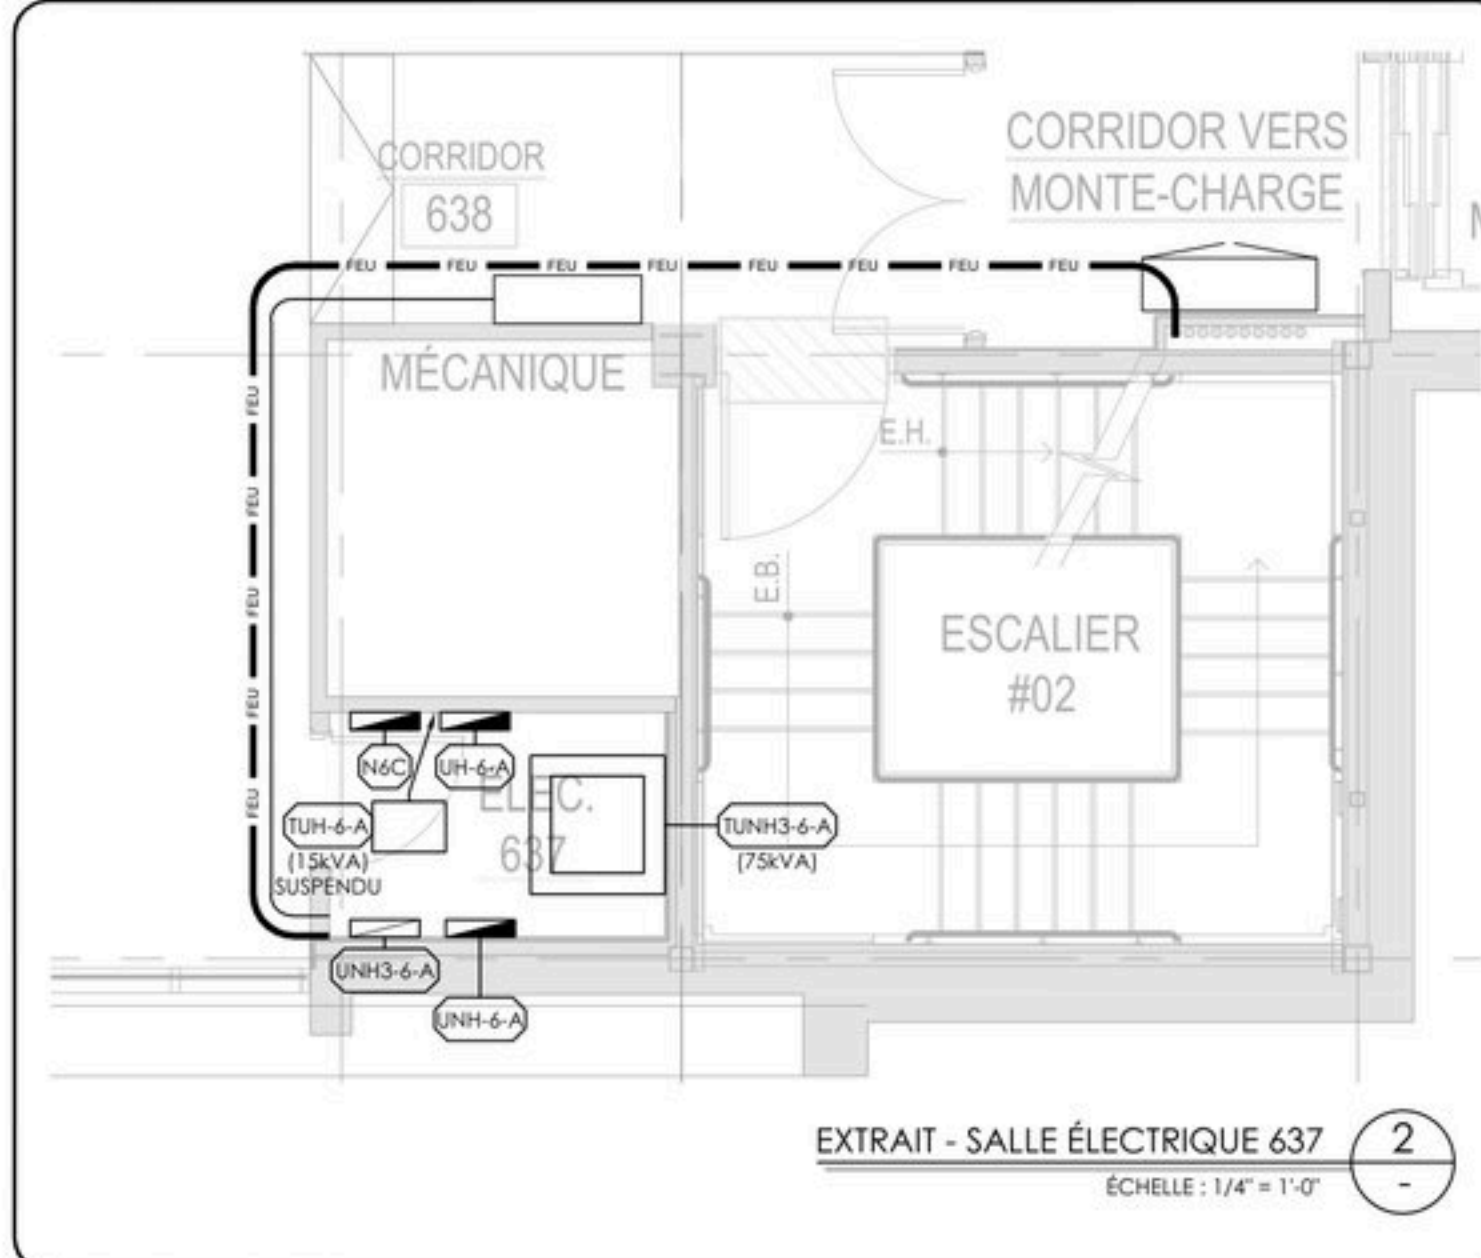

PLAN GÉNÉRAL

PROJET

PLAYGROUND POKER

CLIENT

PLAYGROUND HOTEL,
1 500 QC-138 C, KAHNAWAKE,
QC, J0L 1B0

PROJET

ÉLECTRICITÉ

SERVICES
6ième ÉTAGE


PRÉPARÉ PAR: M. SIMARD

REVISÉ PAR: G. BLONDIN

DATE DE RÉVISION: 2024-02-23


TEL QU'INDIQUÉ

PLANCHE NO: E-212

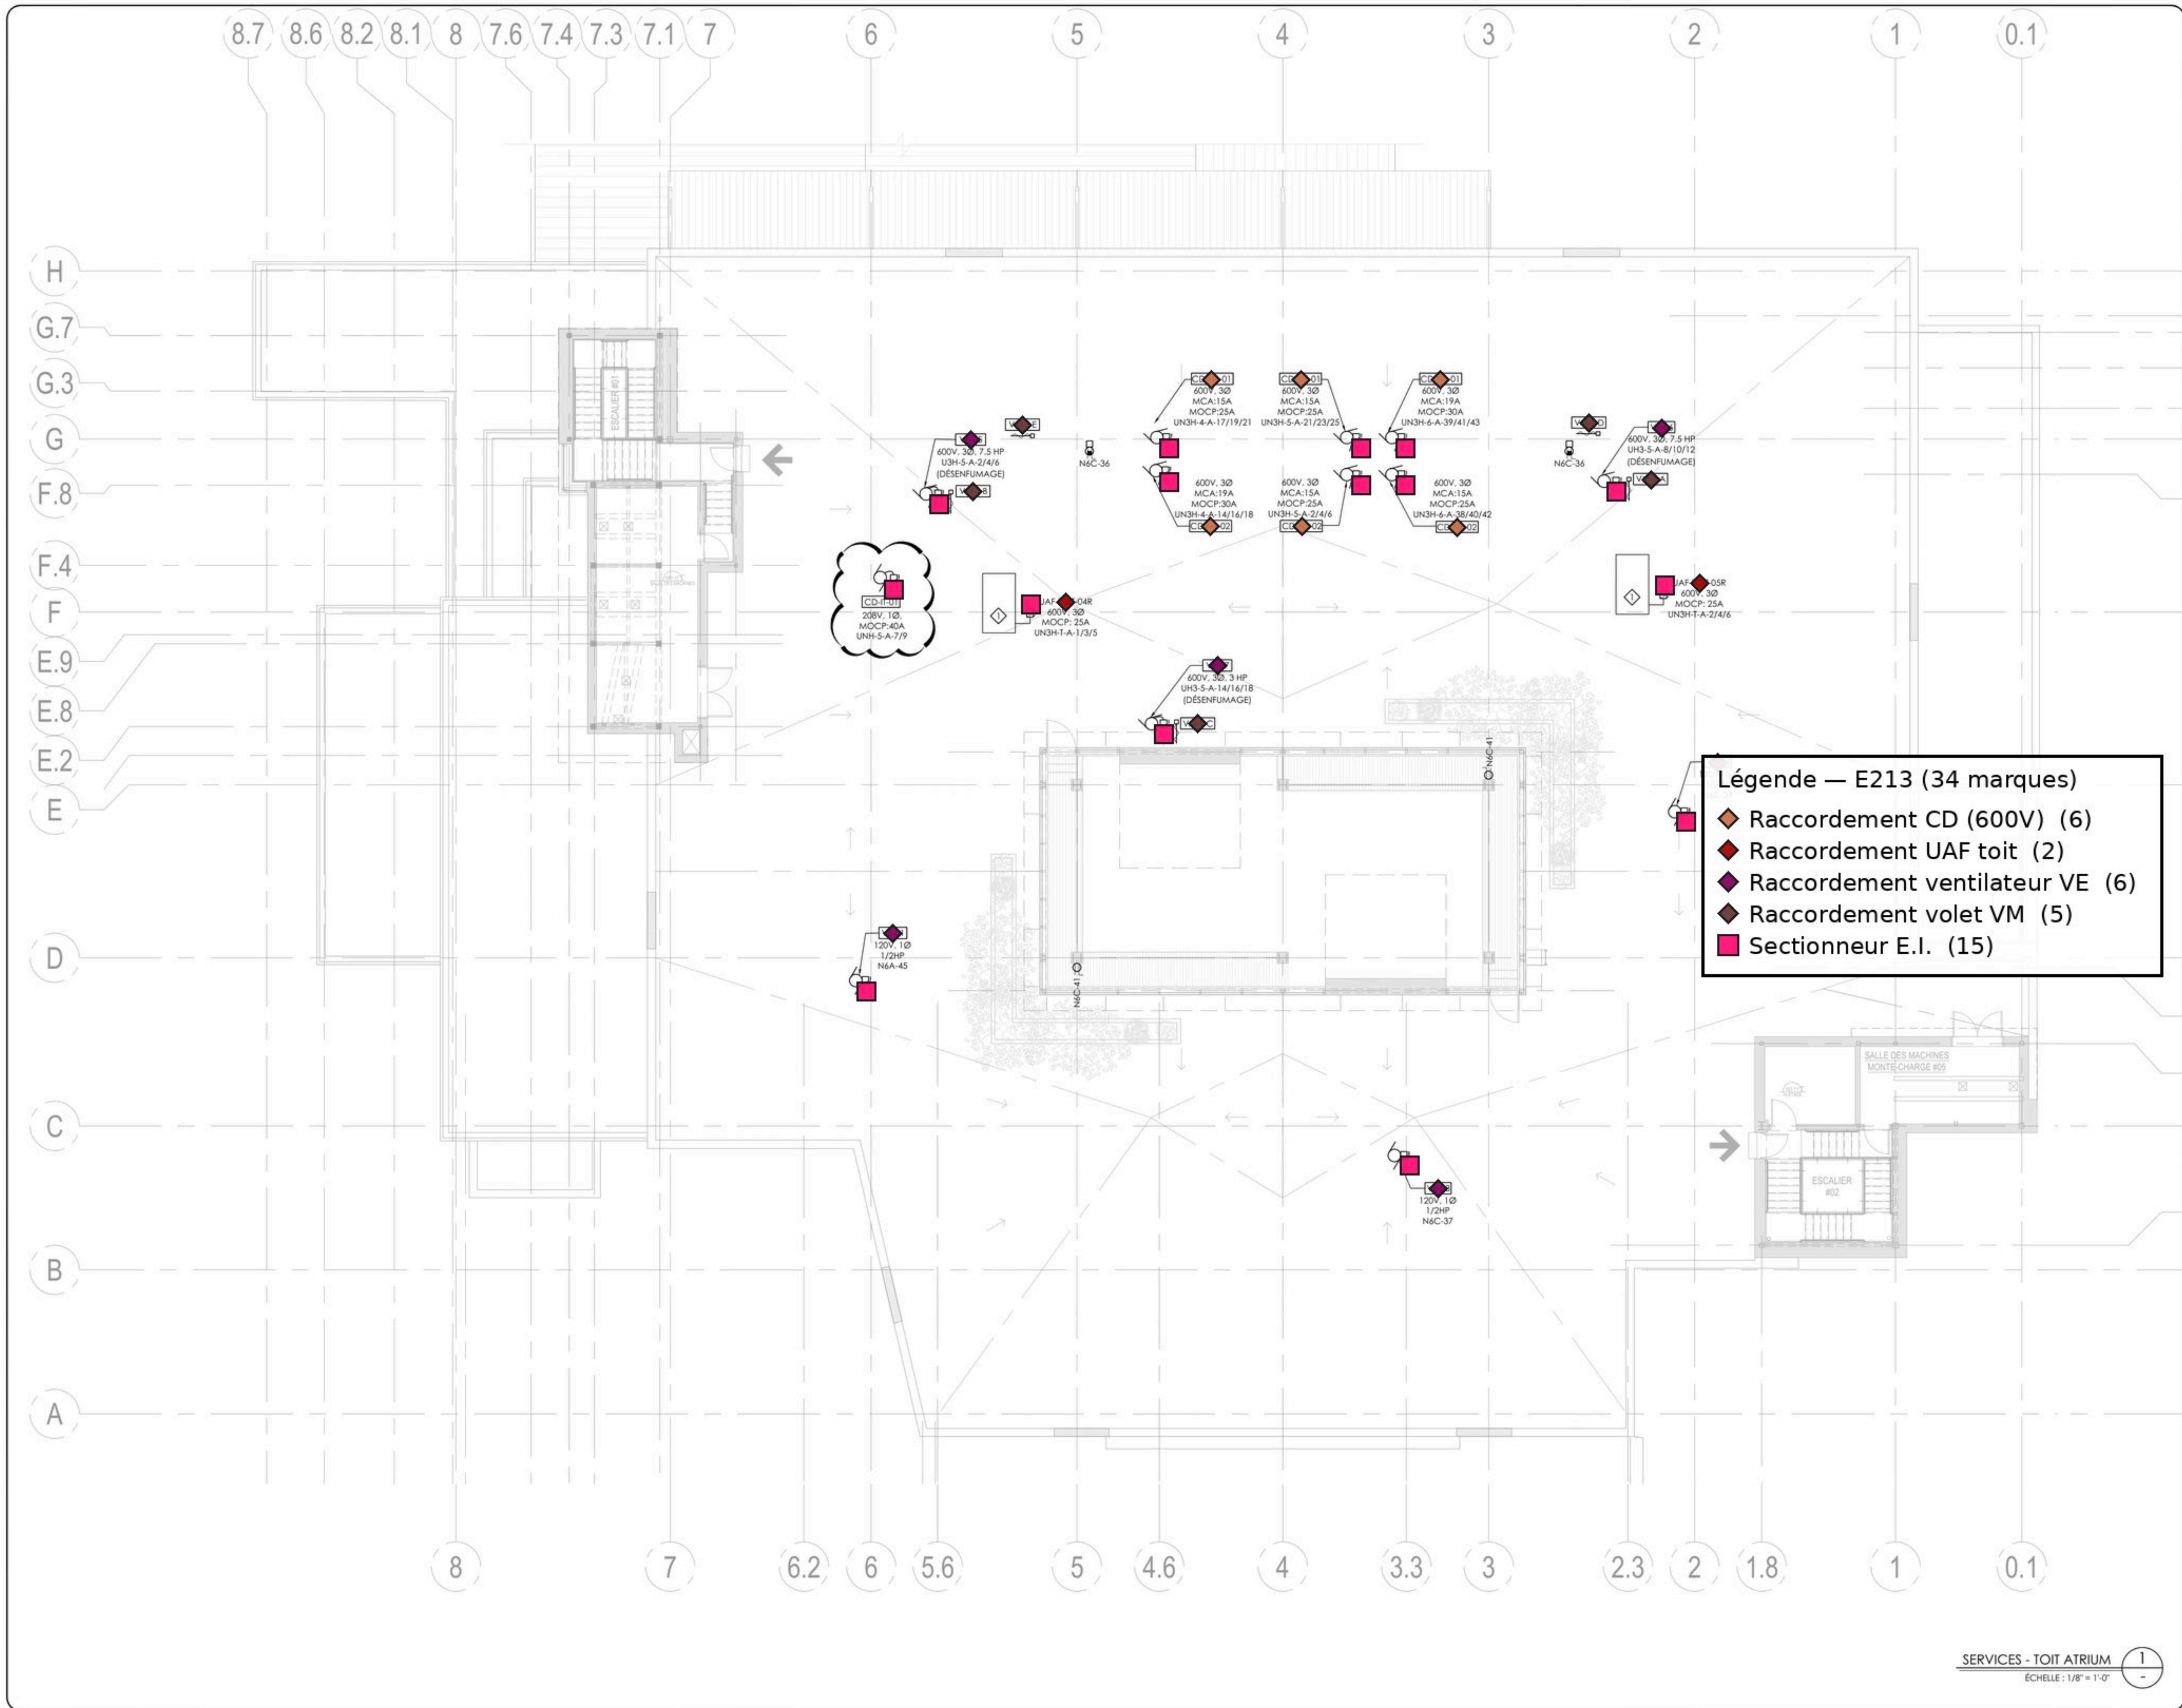

NOTE SPÉCIFIQUE

LES ÉQUIPEMENTS DOIVENT ÊTRE ARRÊTÉS EN CAS DE DÉTECTION DE FUMÉE DANS LE CONDUIT D'ALIMENTATION. VOIR PLAN E-802 ET E-804

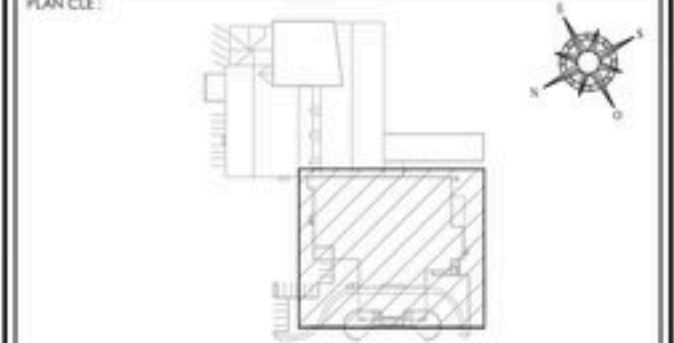

PROJET

PROJET

PROJET

lemay

ÉLECTRICIEN

2024-02-20

NE PAS UTILISER POUR CONSTRUCTION			
2	20-02-26	APPEL D'OFFRES RÉVISION 1	M.S.
1	24-09-25	ADDENDA ME-01	M.S.
0	17-07-25	APPEL D'OFFRES	M.S.
NO.	J - M - A	DESCRIPTION	PAR
ÉMIS POUR:			

2024-02-20

BFA

Blondin Fortin Associés


Experts conseil - mécanique électrique - électricité

305, boul. Cyrille-Lévesque, 200
Québec, QC G1R 1H1
Tél. : 418-428-5555
www.blondinfortin.ca

PLAYGROUND POKER

PLAYGROUND HOTEL,
1 500 QC-138 C, KAHNAWAKE,
QC, J0L 1B0

ÉLECTRICITÉ	
SERVICES TOIT ATRIUM	
PRÉPARÉ PAR: M. SIMARD	TEL QU'INDIQUÉ
DESIGNÉ PAR: G. BLONDIN	PLANCHE NO:
NO DE PROJET: 2024-023	E-213

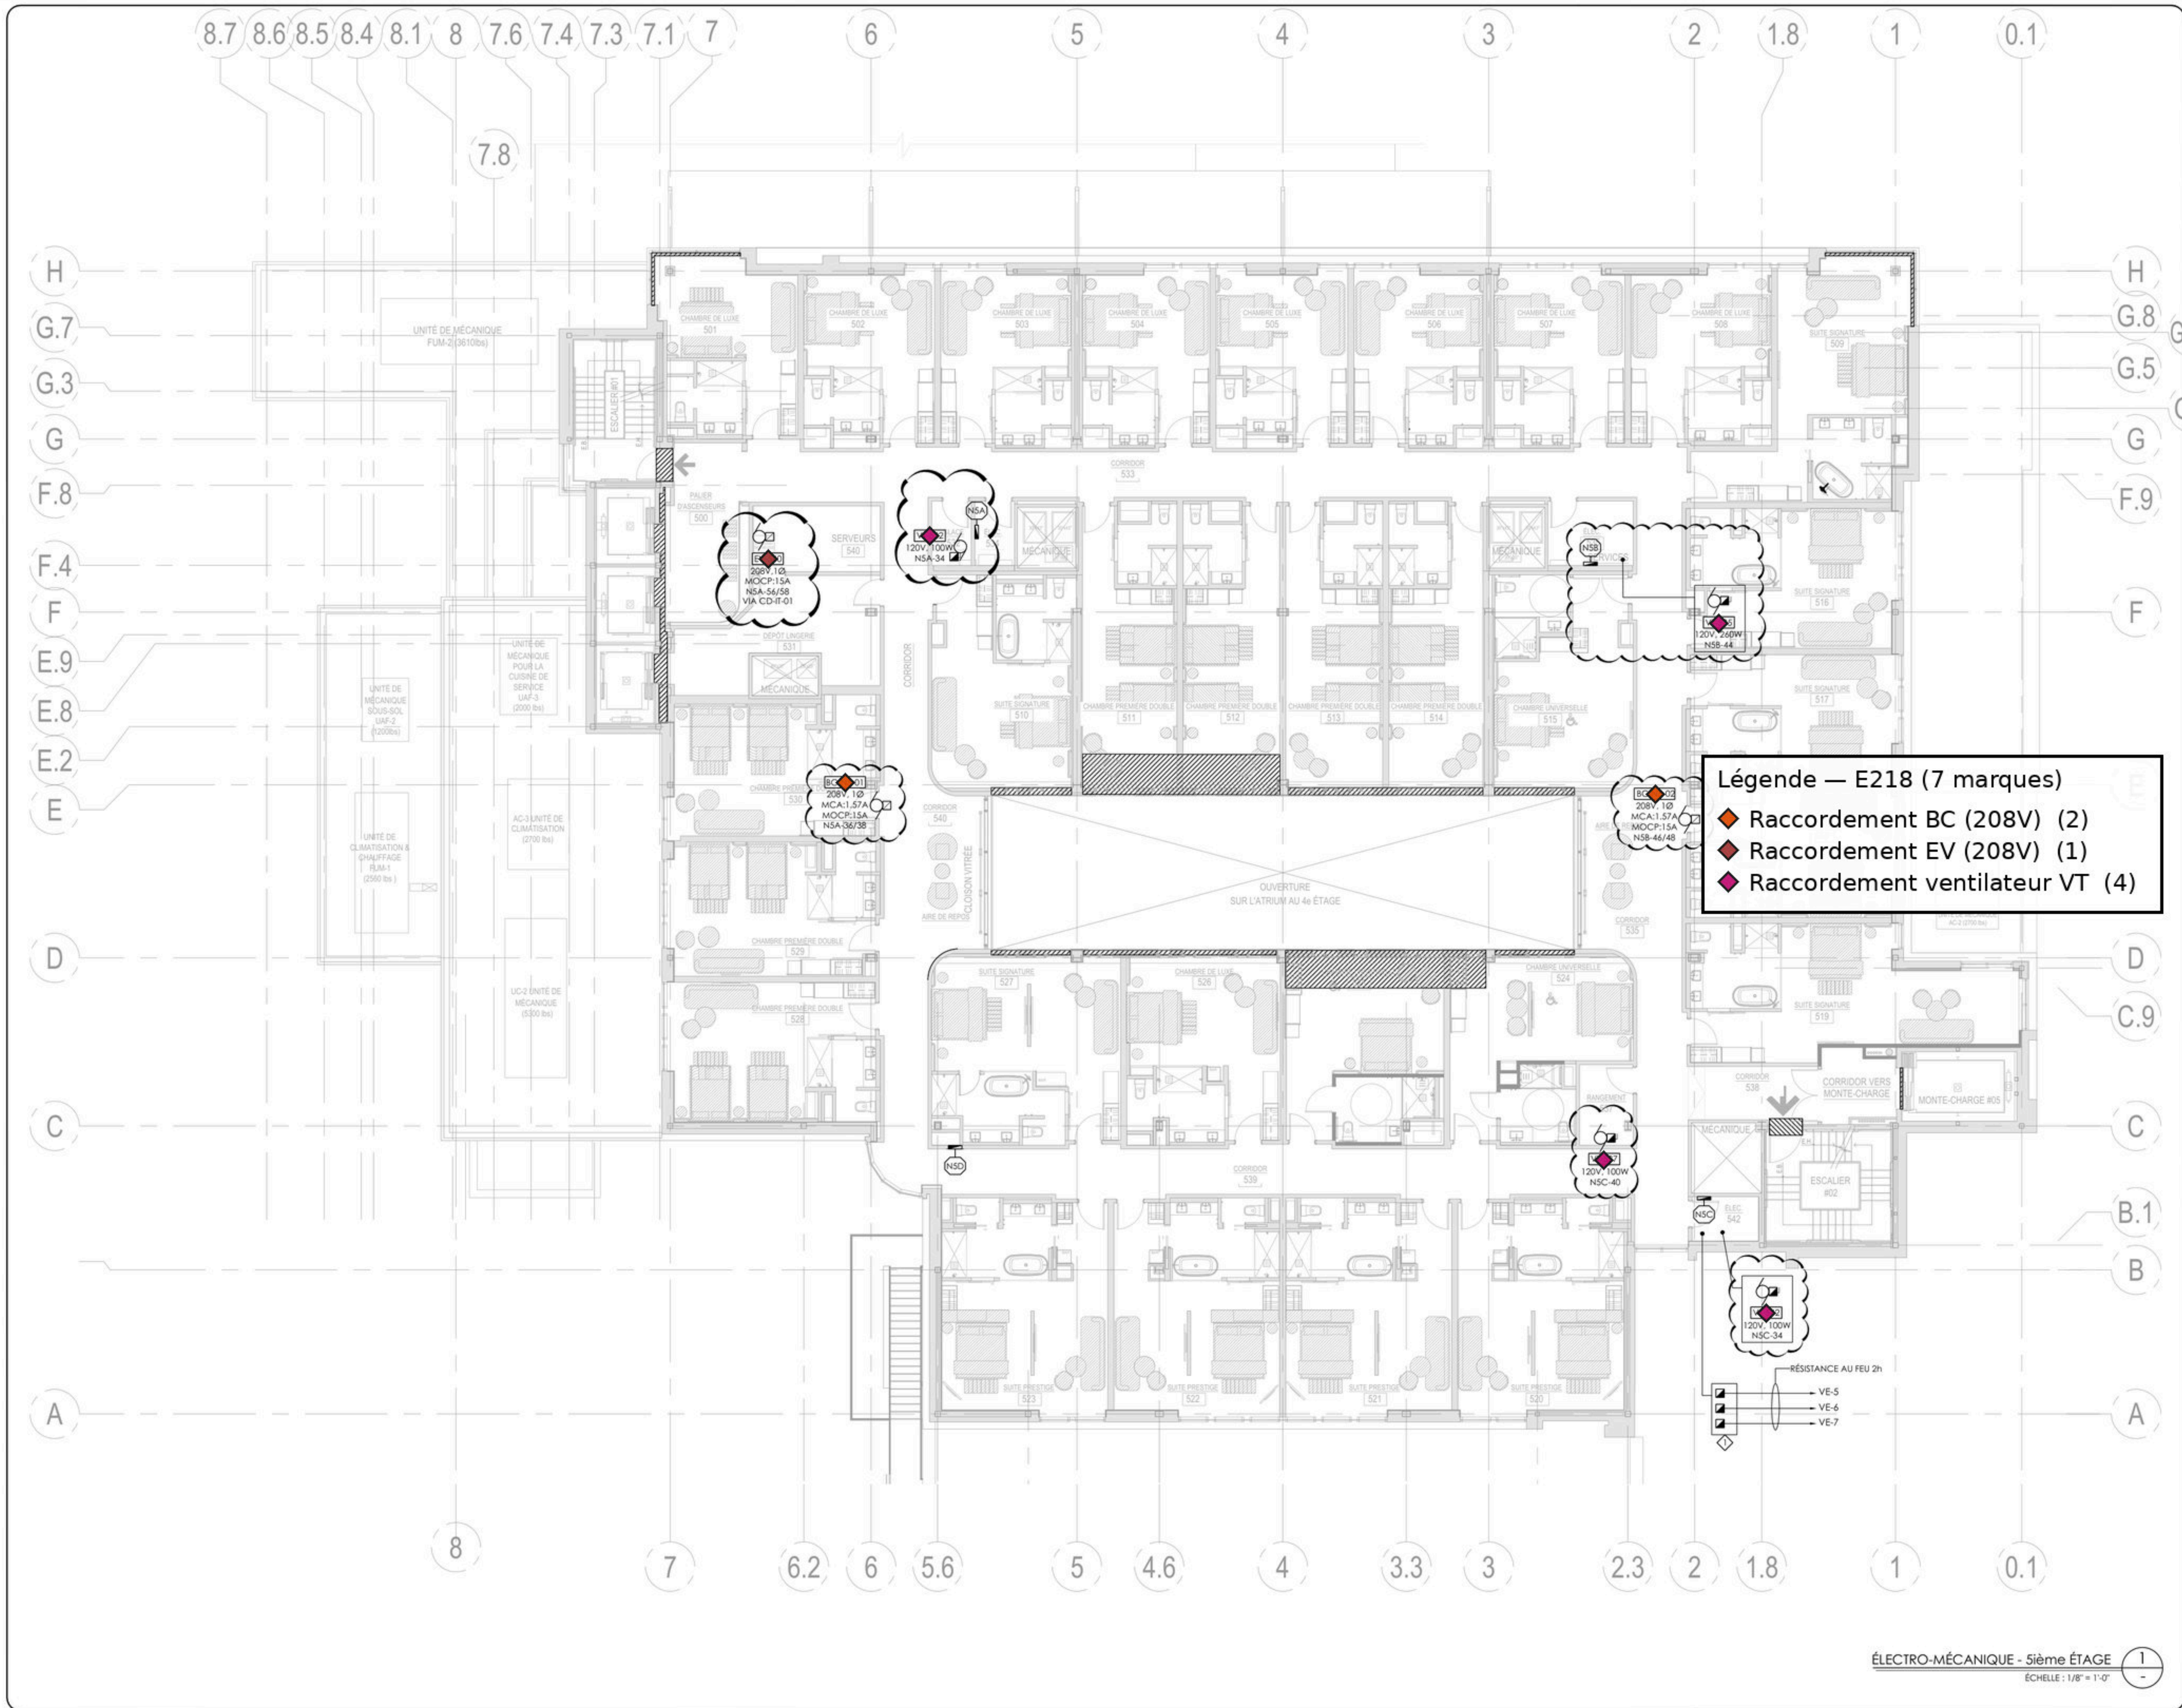

Légende — E218 (7 marques)

- ◆ Raccordement BC (208V) (2)
- ◆ Raccordement EV (208V) (1)
- ◆ Raccordement ventilateur VT (4)

ÉLECTRO-MÉCANIQUE - Sième ÉTAGE
ÉCHELLE : 1/8" = 1'-0"

NOTE SPÉCIFIQUE
◆ POSITIONS EXACTES À COORDONNER AU CHANTIER.

PLAN GÉNÉRAL

NOTES

lemay

ÉLECTRO-MÉCANIQUE

NE PAS UTILISER POUR CONSTRUCTION		
0	20-02-26	APPEL D'OFFRES RÉVISION 1
NO.	J - M - A	DESCRIPTION
ÉMIS POUR:		PAR

PROJET

2020-02-20

BFA

Blondin Fortin Associés

Experts conseils : mécanique, électricité, énergie

305, boul. Cyrille-Lapointe, 200
Saint-Jovite, Québec J0V 1P0
Tél : 450-428-5555
www.blondinfortin.ca


CLIENT

PLAYGROUND POKER


PROJET

PLAYGROUND HOTEL,
1 500 QC-138 C, KAHNAWAKE,
QC, J0L 1B0


ÉLECTRICITÉ	
ÉLECTRO-MÉCANIQUE Sième ÉTAGE	
PRÉPARÉ PAR : M. SIMARD	TEL QU'INDIQUÉ
COORDONNÉ PAR : G. BLONDIN	PLANCHE NO.
NO DE PROJET : 2024-023	E-218

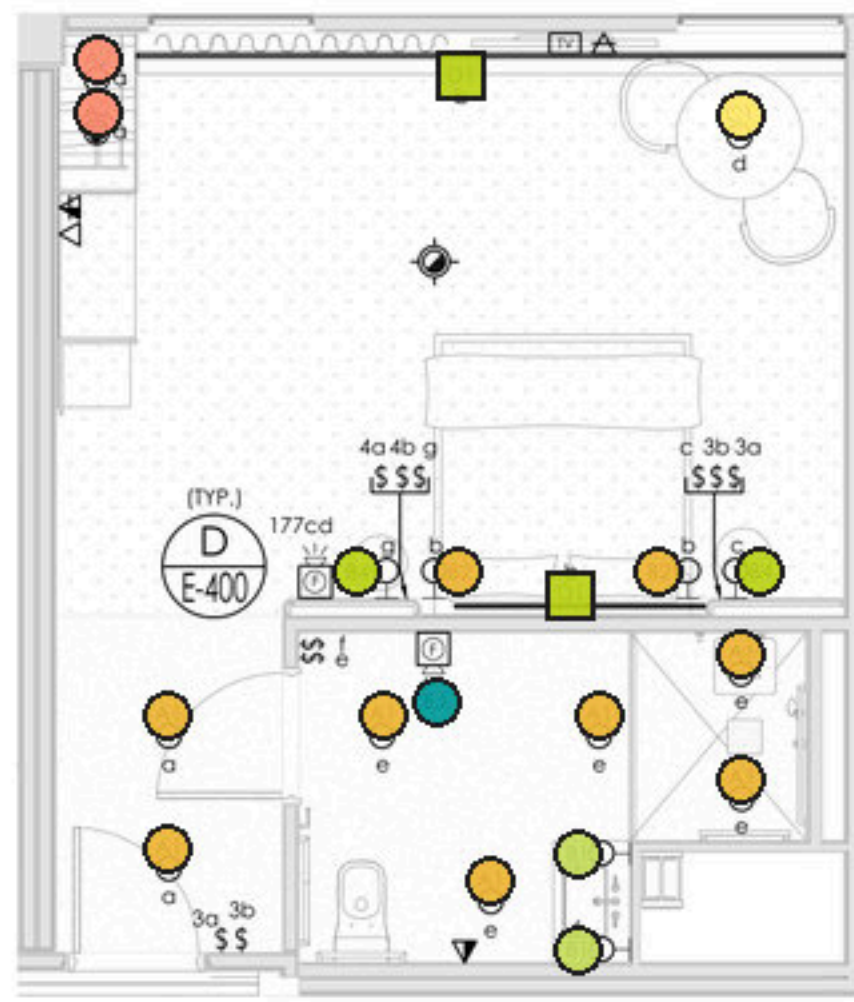

CHAMBRE UNIVERSELLE 3
ÉCHELLE : 1/4" = 1'-0"

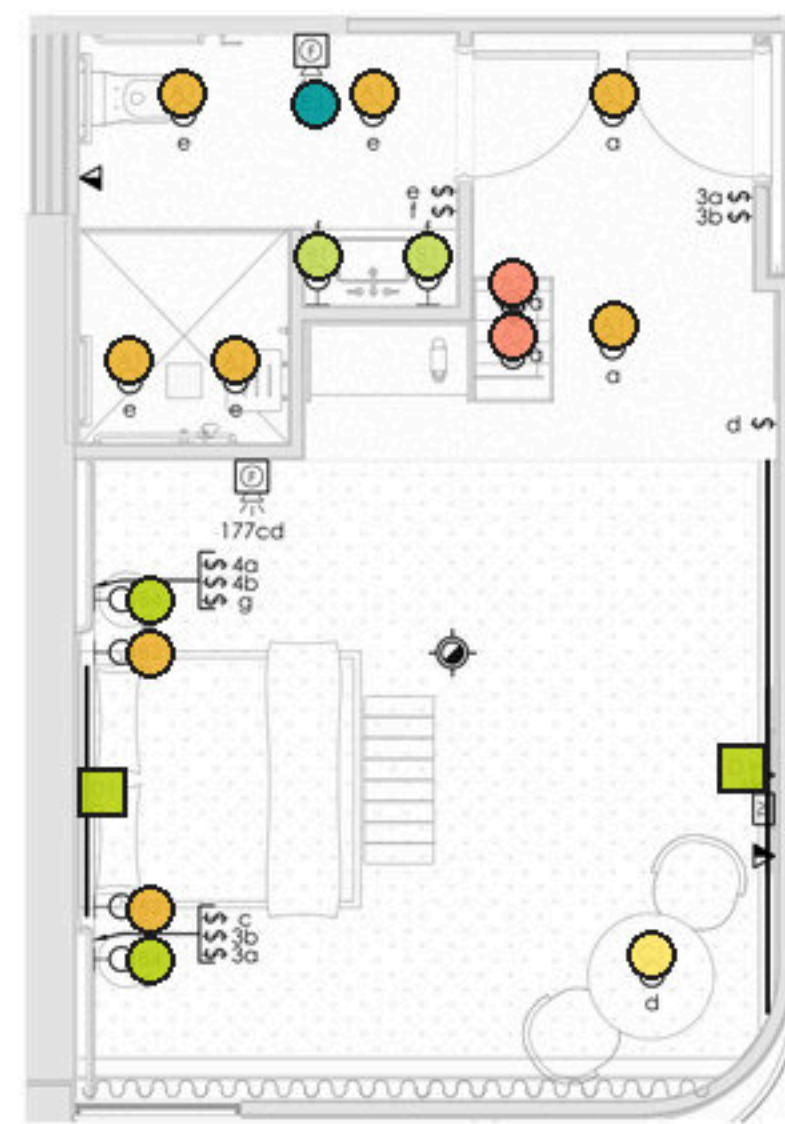


CHAMBRE UNIVERSELLE 1
ÉCHELLE : 1/4" = 1'-0"

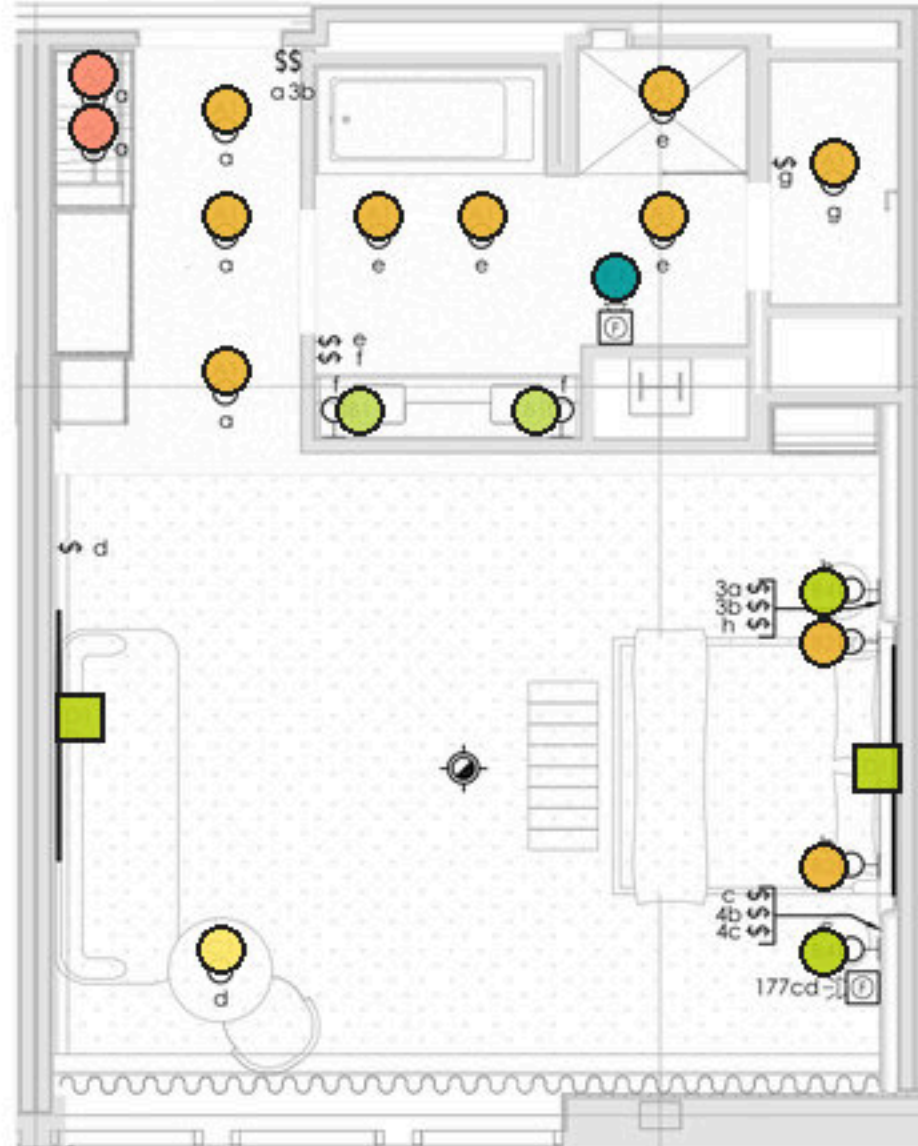

SUITE PRESTIGE 1
ÉCHELLE : 1/4" = 1'-0"




CHAMBRE DE LUXE (503)
ÉCHELLE : 1/4" = 1'-0"

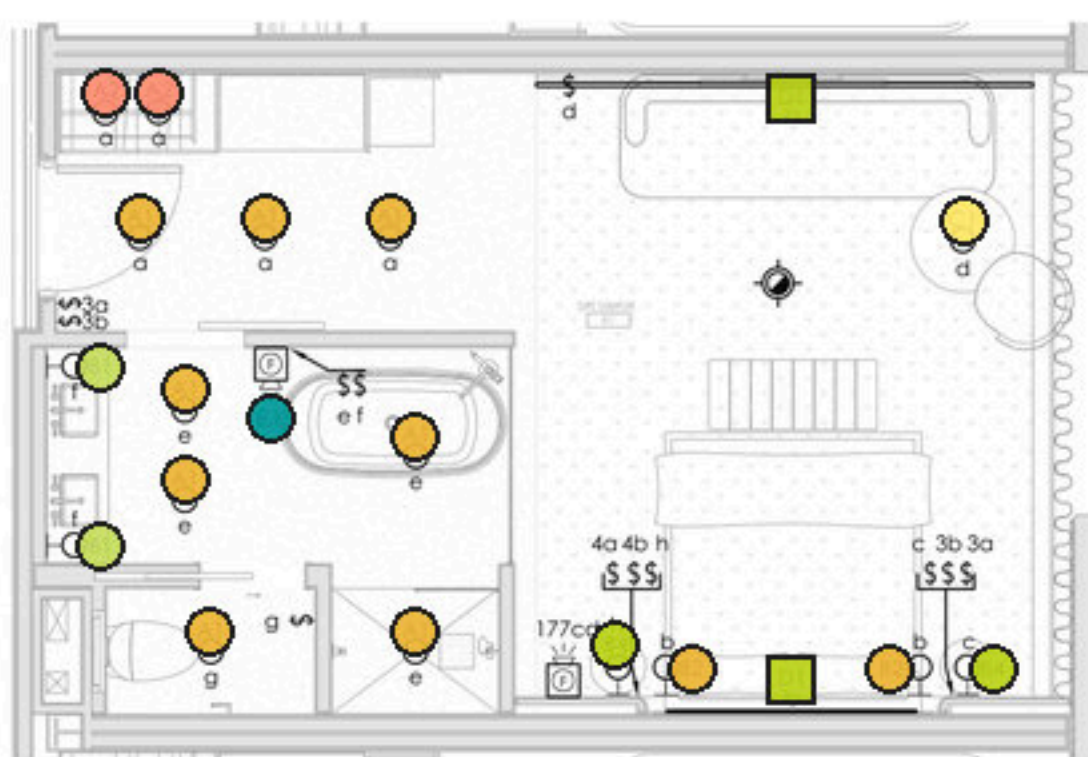


SUITE SIGNATURE
ÉCHELLE : 1/4" = 1'-0"




CHAMBRE UNIVERSELLE 2
ÉCHELLE : 1/4" = 1'-0"

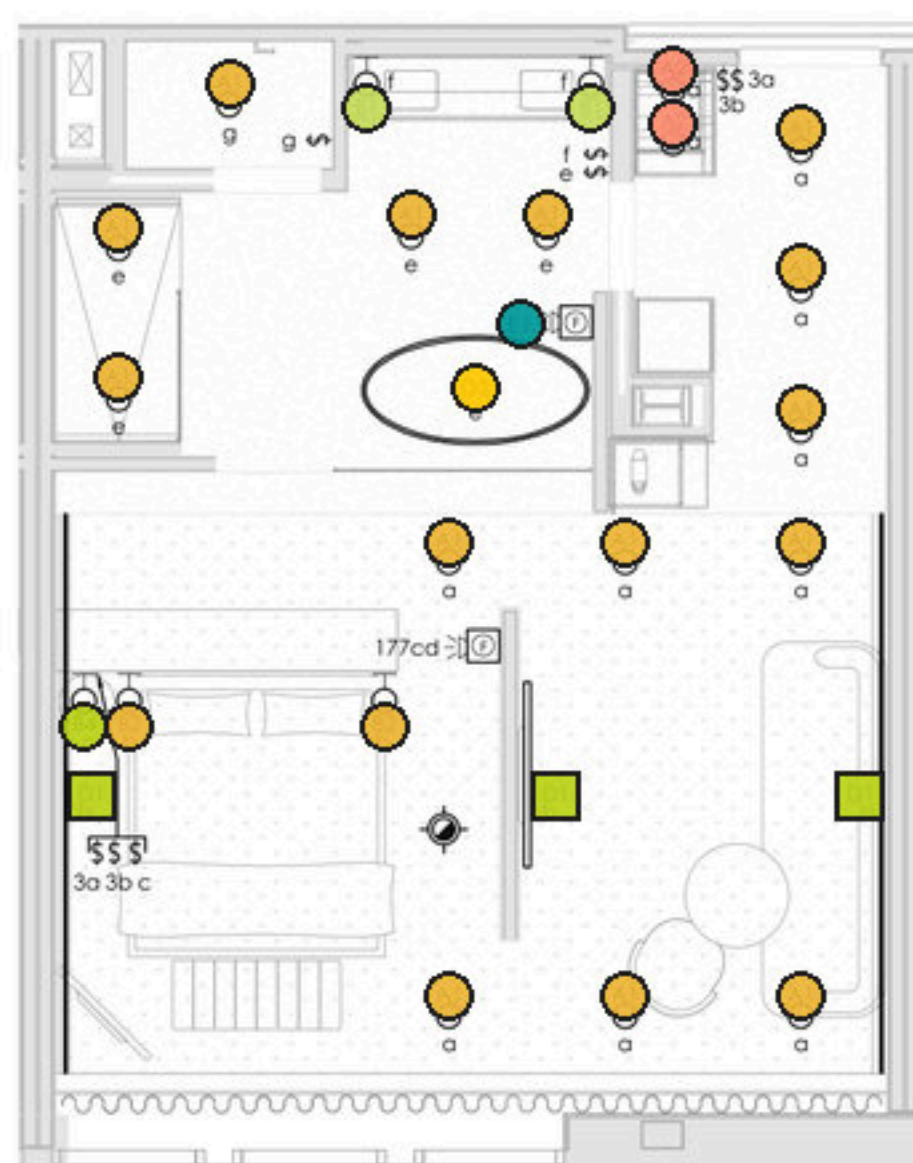


SUITE PRESTIGE 2 (523)
ÉCHELLE : 1/4" = 1'-0"

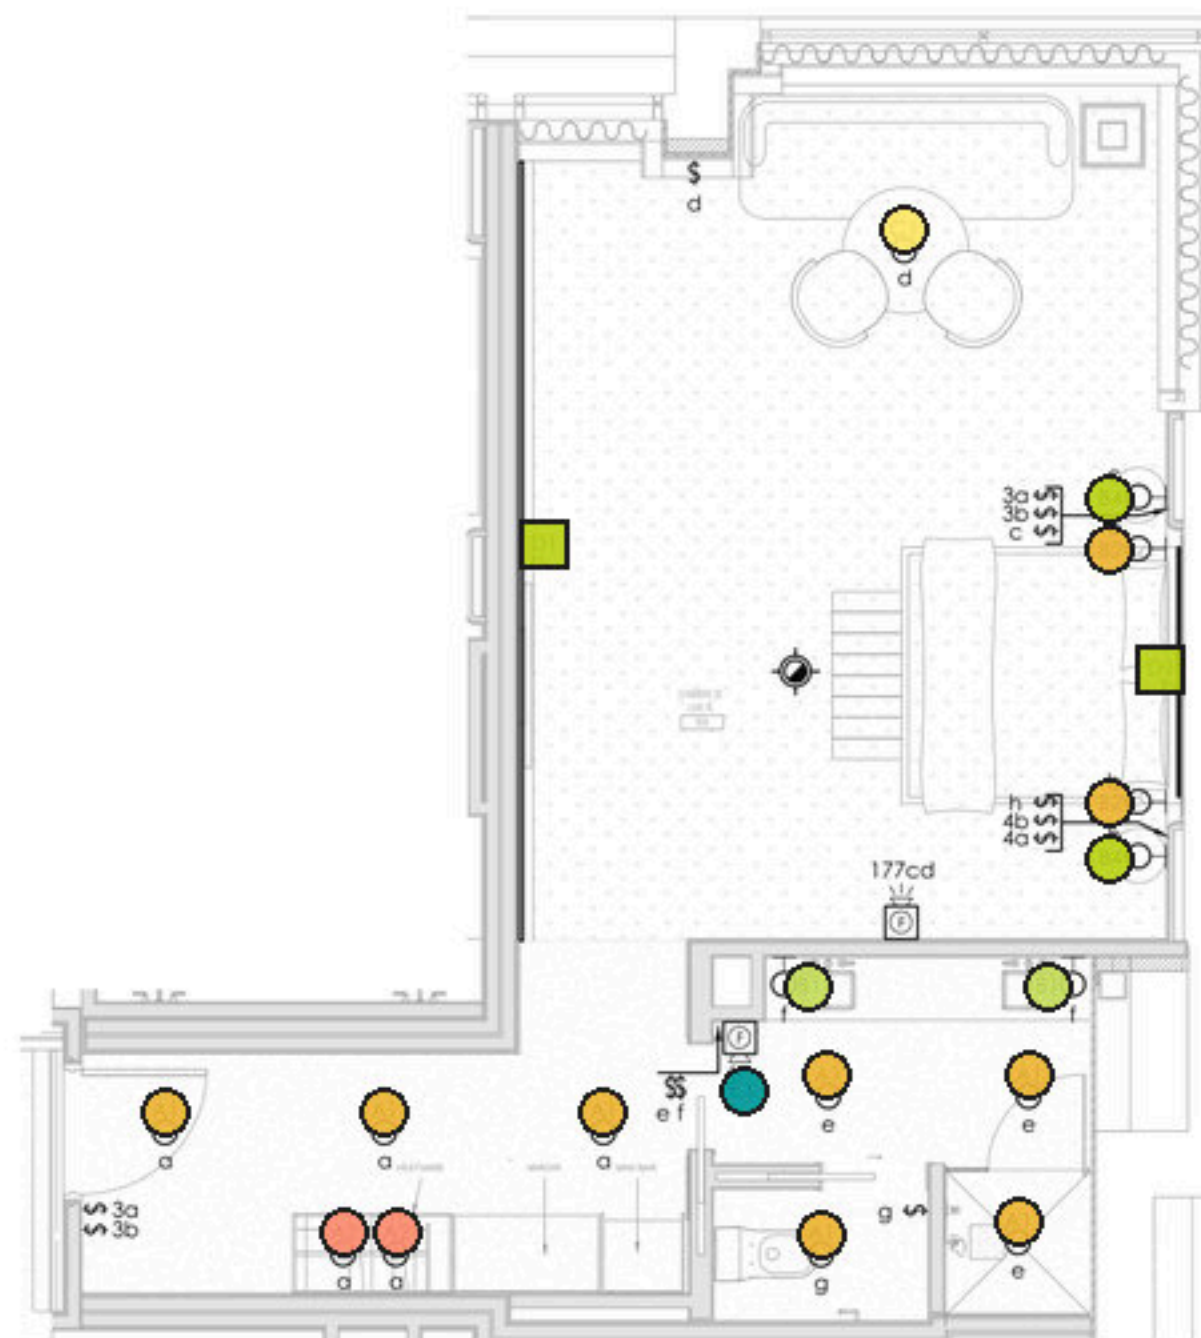


CHAMBRE DE LUXE XL
ÉCHELLE : 1/4" = 1'-0"

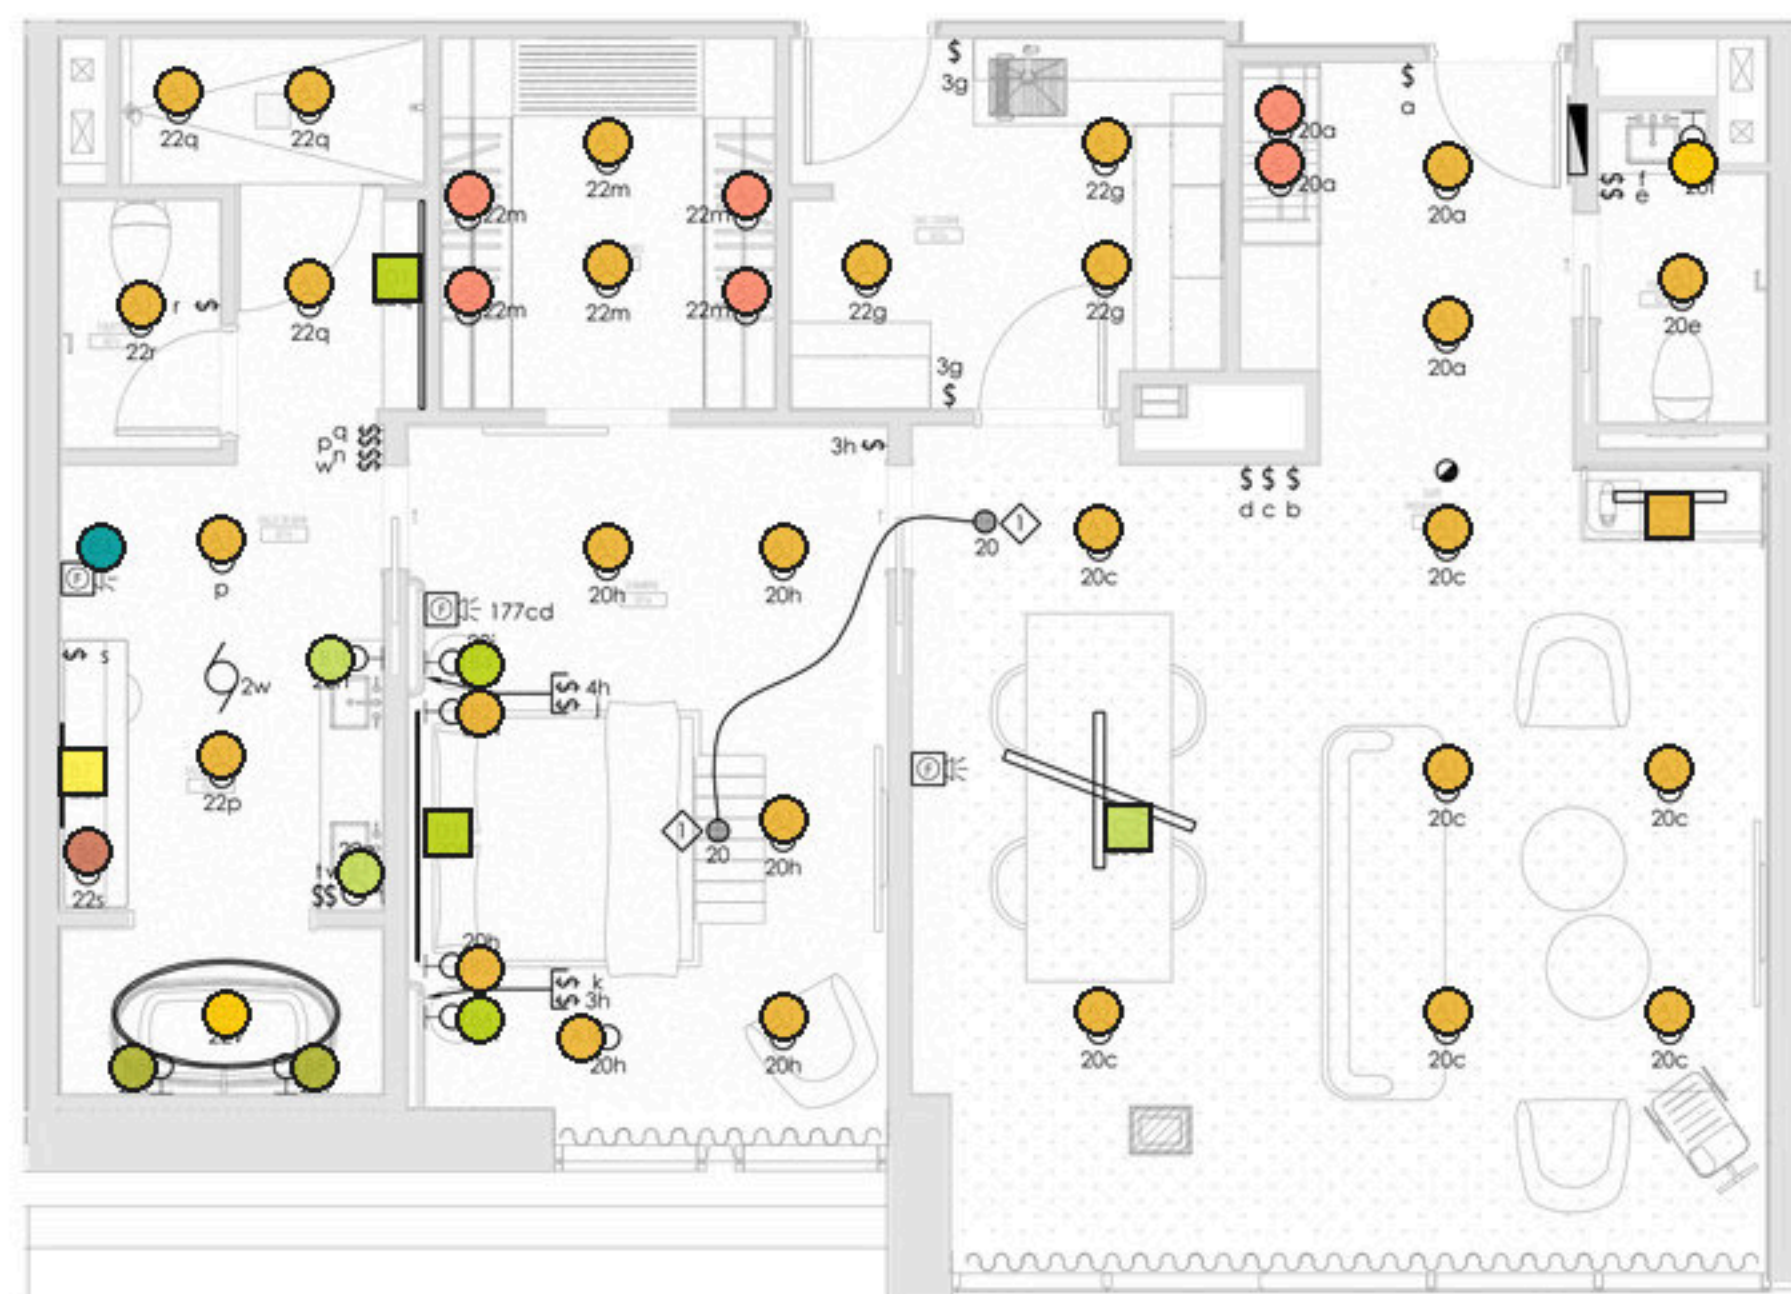

SUITE PRÉSIDENTIELLE
ÉCHELLE : 1/4" = 1'-0"

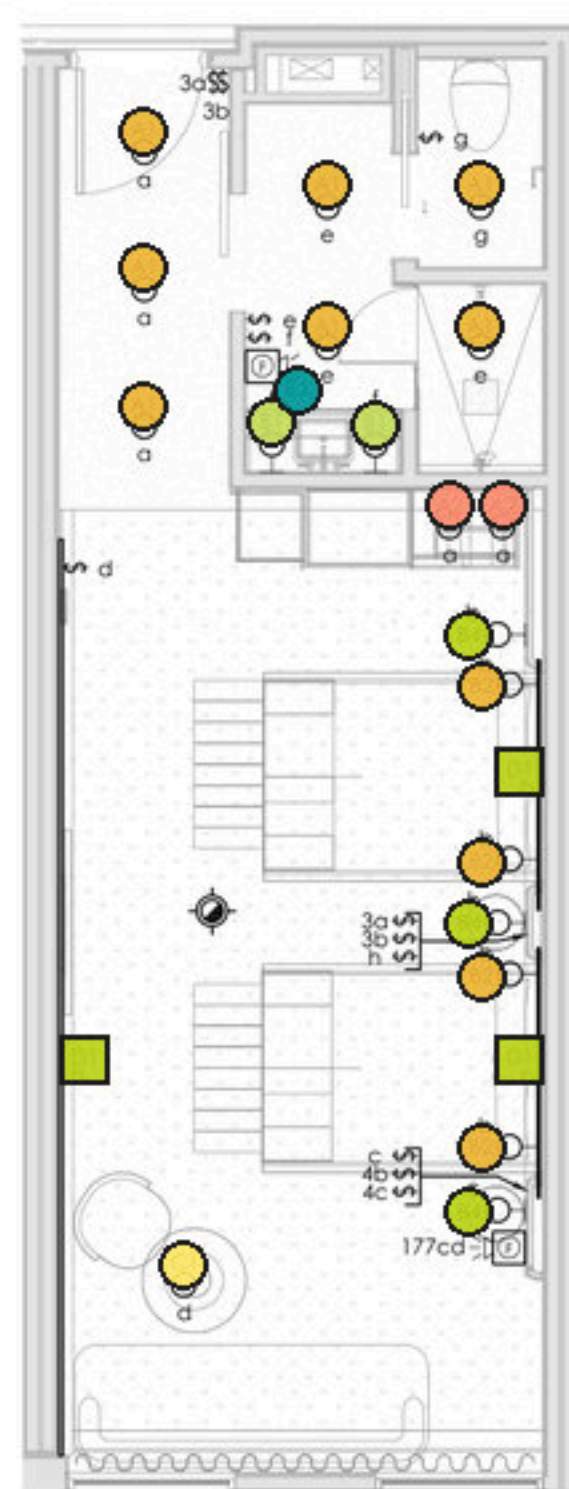

CHAMBRE DOUBLE 2
ÉCHELLE : 1/4" = 1'-0"

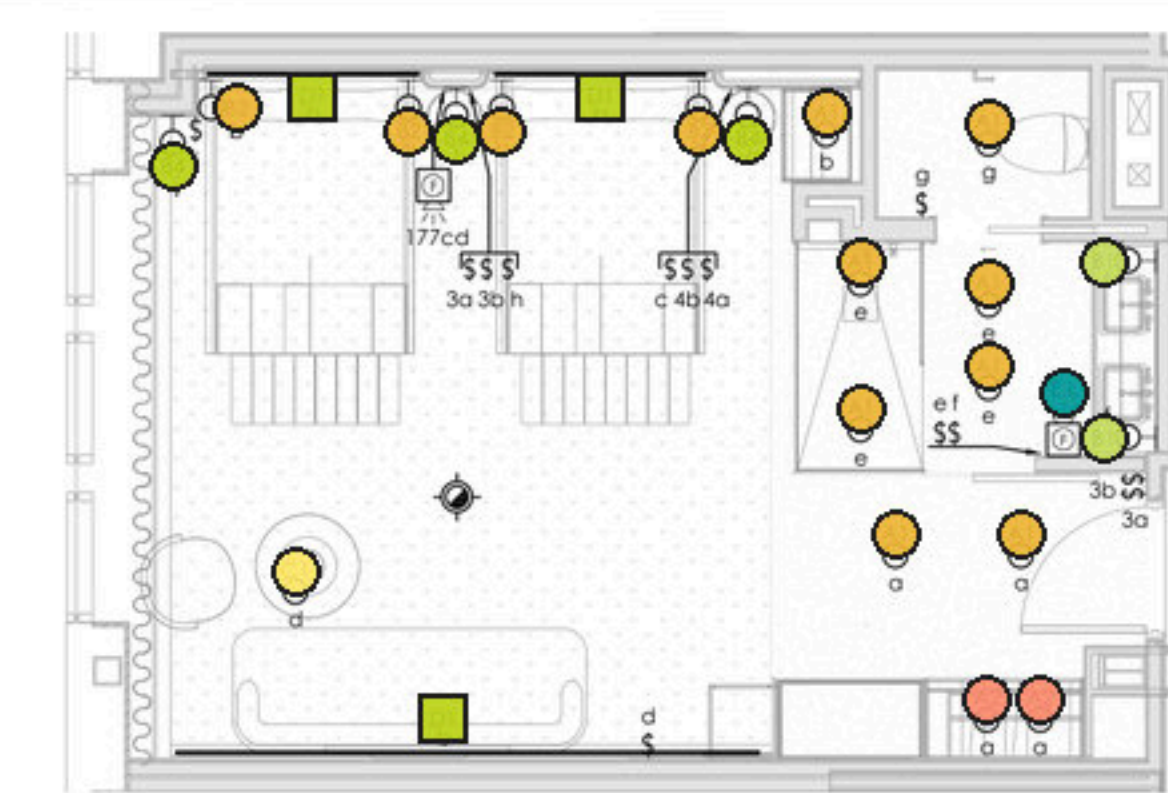


CHAMBRE DOUBLE 1
ÉCHELLE : 1/4" = 1'-0"

NOTE SPÉCIFIQUE


LES DEUX AVERTISSEURS DE FUMÉE DOIVENT ÊTRE INTERLIÉS DE SORTIE QUE LE DÉCLICHÈMENT DE L'UN ENTRAÎNE LE DÉCLICHÈMENT DE L'AUTRE.

NOTE GÉNÉRALE


DANS CHAQUE CHAMBRE OU SUITE, TOUTS LES INTERRUPTEURS D'ÉCLAIRAGE DOIVENT ÊTRE C/A GRADATEUR.

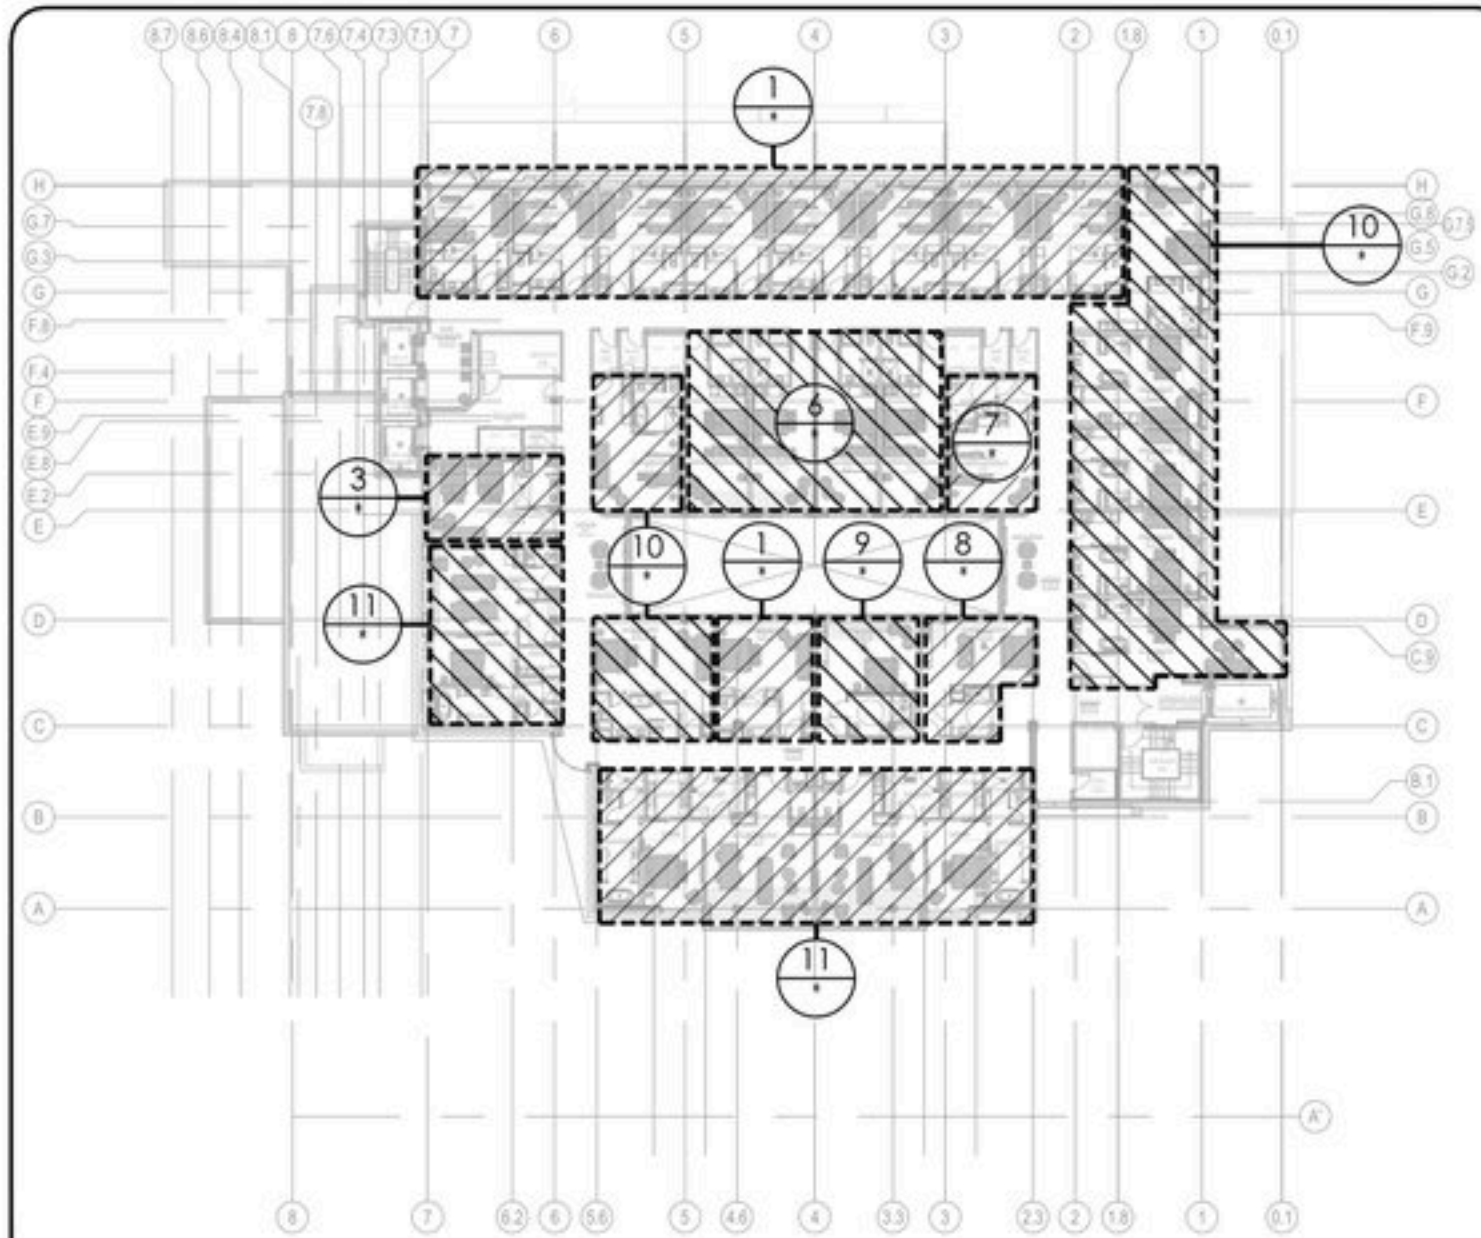

PLAN CLÉ - NIVEAU 6
ÉCHELLE : 1/32" = 1'-0"

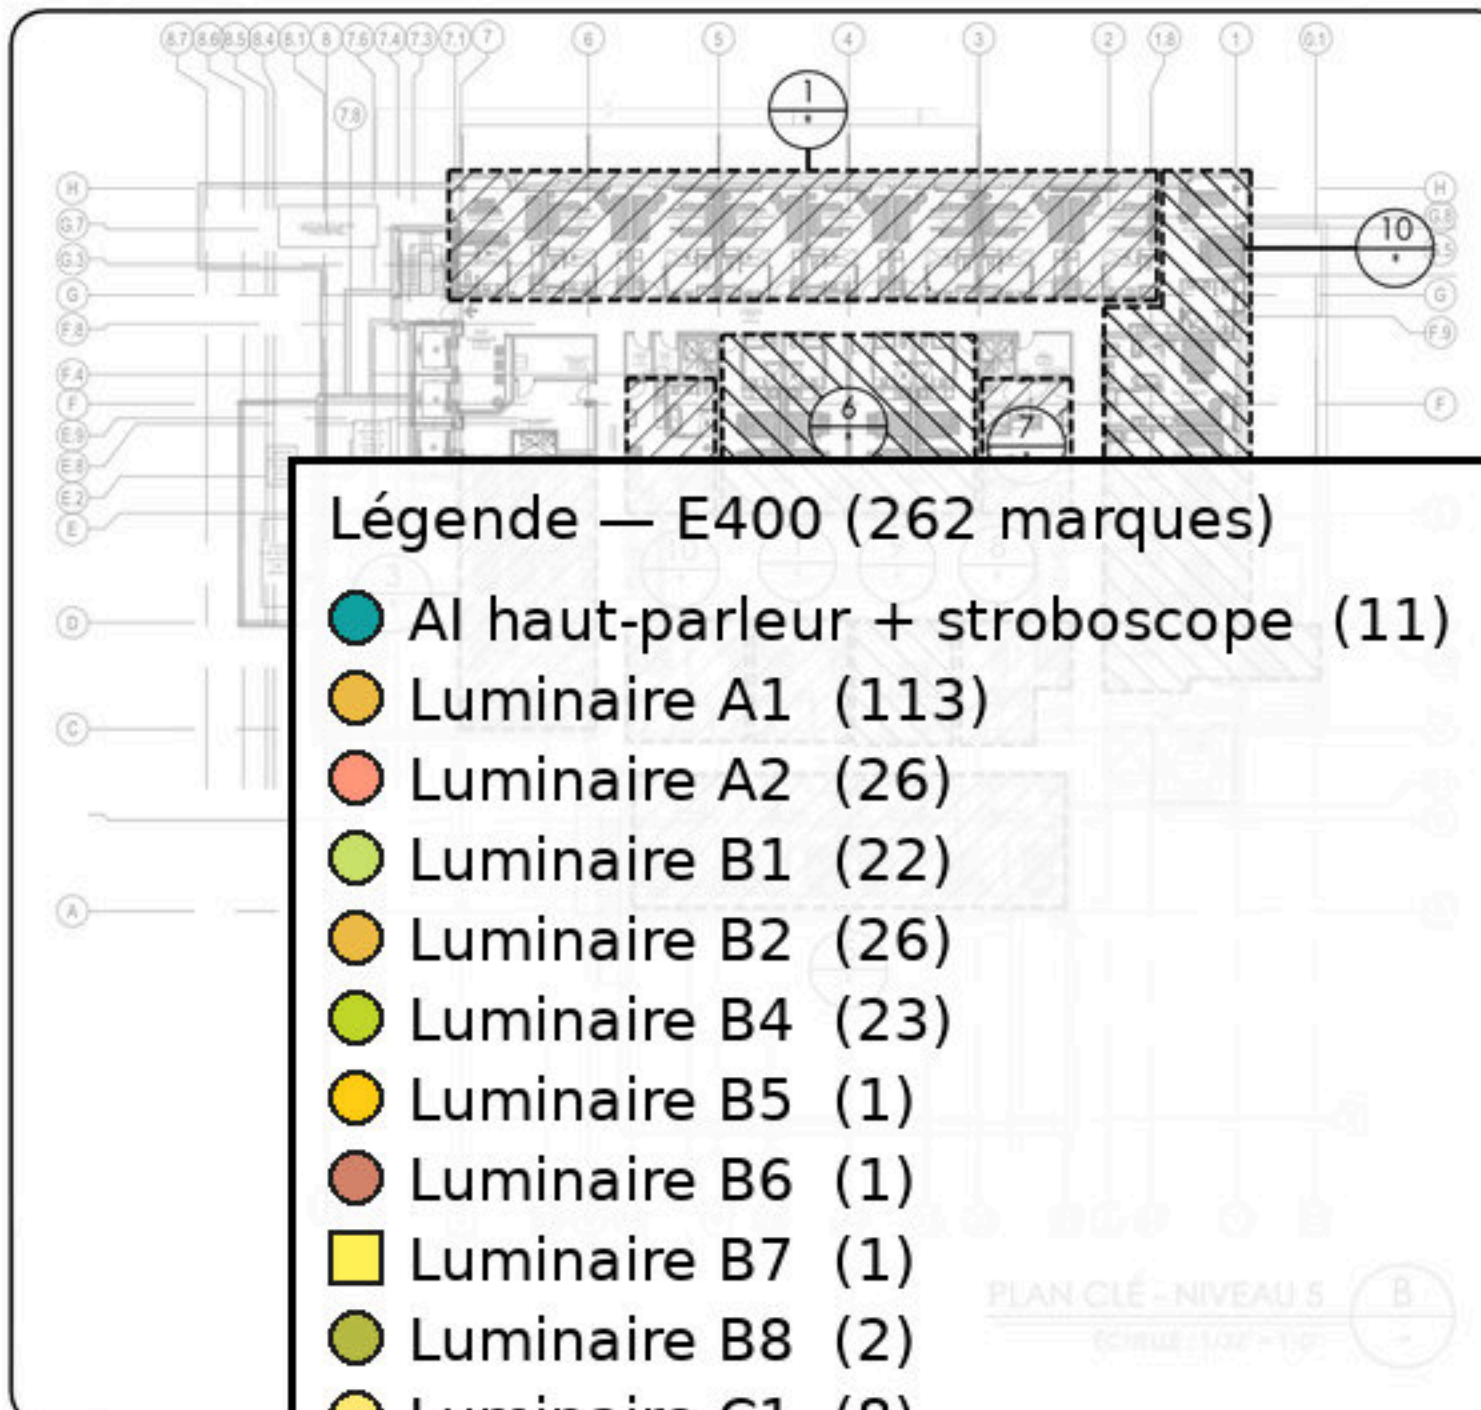


PLAN CLÉ - NIVEAU 5
ÉCHELLE : 1/32" = 1'-0"

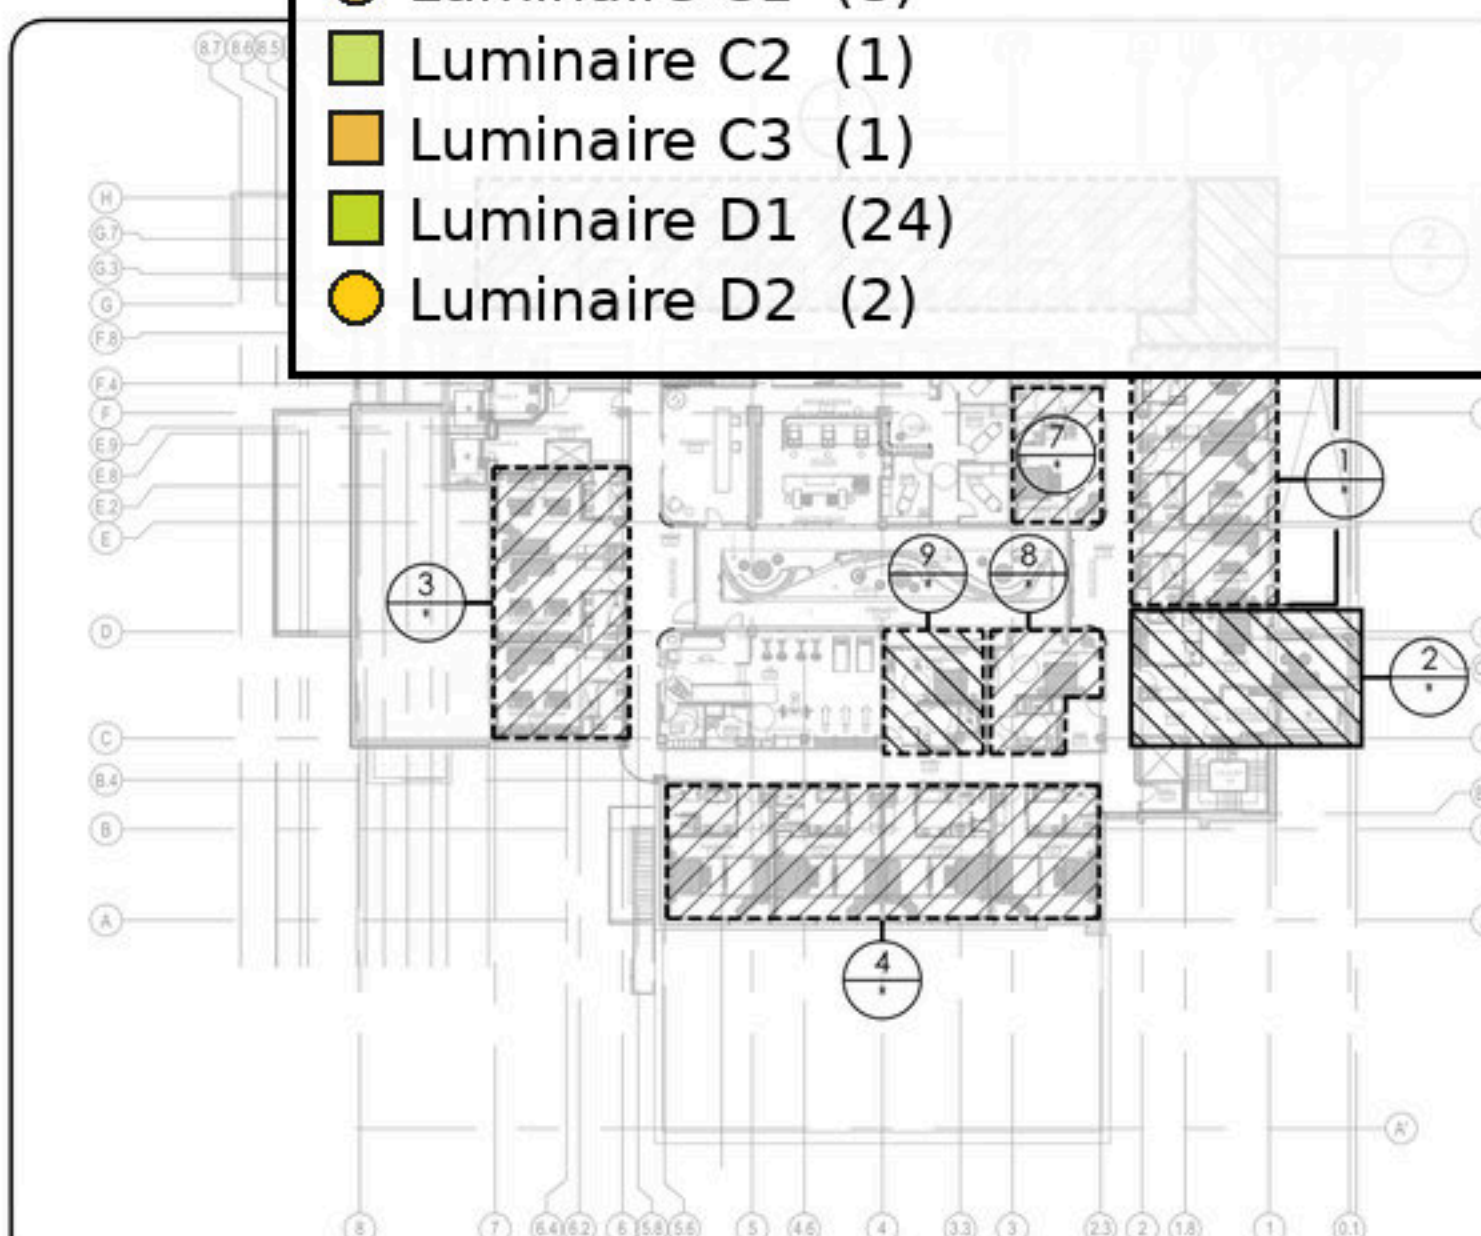

PLAN CLÉ - NIVEAU 4
ÉCHELLE : 1/32" = 1'-0"

Légende — E400 (262 marques)



- AI haut-parleur + stroboscope (11)
- Luminaire A1 (113)
- Luminaire A2 (26)
- Luminaire B1 (22)
- Luminaire B2 (26)
- Luminaire B4 (23)
- Luminaire B5 (1)
- Luminaire B6 (1)
- Luminaire B7 (1)
- Luminaire B8 (2)
- Luminaire C1 (8)
- Luminaire C2 (1)
- Luminaire C3 (1)
- Luminaire D1 (24)
- Luminaire D2 (2)

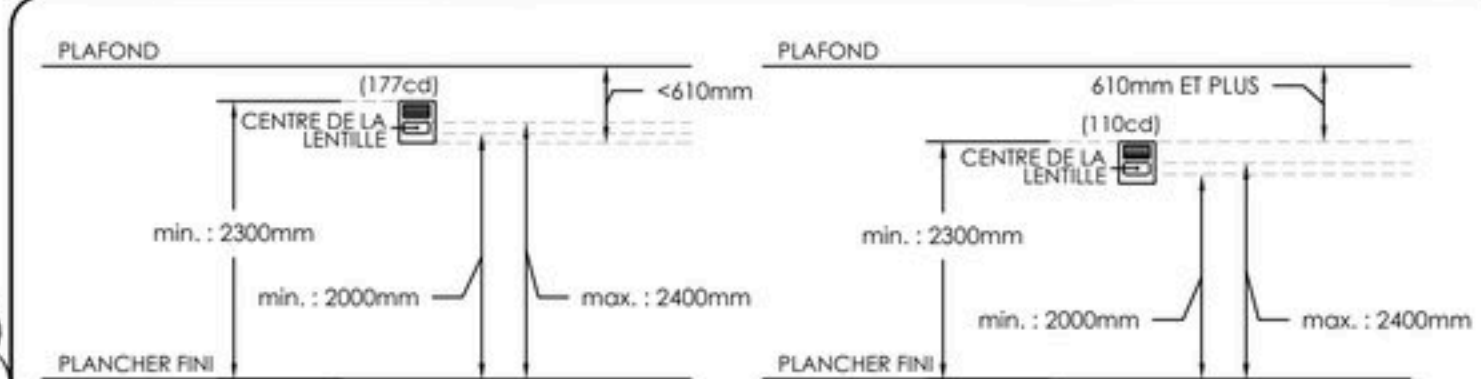


NOTES:
• SI LE DISPOSITIF DE SIGNALISATION EST INSTALLÉ À UNE DISTANCE INFÉRIEURE À 610mm DU PLAFOND, L'INTENSITÉ DE LA LAMPE STROBOSCOPIQUE DOIT ÊTRE DE 177cd.
• LORSQUE LES HAUTEURS DE PLAFOND LE PERMETTENT, LES DISPOSITIFS DE SIGNALISATION SONORE DOIVENT ÊTRE INSTALLÉS DE FAÇON QUE LE DESSUS DU DISPOSITIF NE SOIT PAS SITUÉ À MOINS DE 2300 mm AU-DESSUS DU NIVEAU DU PLANCHER FINI.
• SI LES HAUTEURS DE PLAFOND LE PERMETTENT, LES LAMPES STROBOSCOPIQUES MURALES DOIVENT ÊTRE INSTALLÉES DE FAÇON QUE LA TOTALITÉ DE LA LENTILLE SOIT SITUÉE À AU MOINS 2000 mm ET À AU PLUS 2400 mm AU-DESSUS DU NIVEAU DU PLANCHER FINI.

INSTALLATION TYPIQUE - HAUT-PARLEUR C/A LAMPE STROBOSCOPIQUE

ÉCHELLE : AUCUNE

 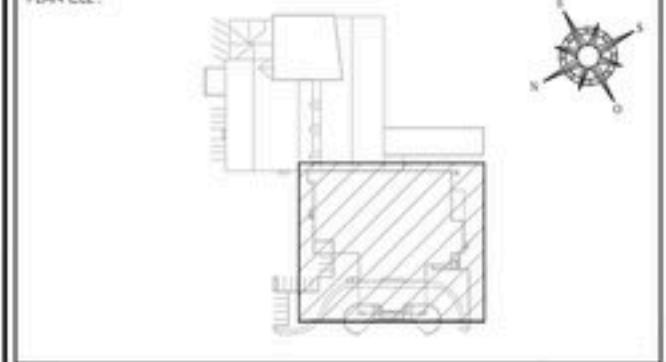


NE PAS UTILISER POUR CONSTRUCTION			
NO.	J - M - A	DESCRIPTION	PAR
1	20-02-26	APPEL D'OFFRES RÉVISION 1	M.S.
2	17-07-25	APPEL D'OFFRES	M.S.
ÉMIS POUR:			

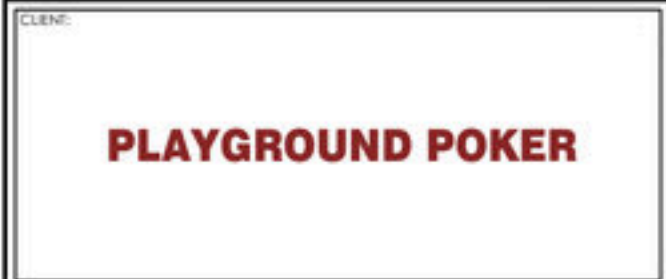


PLAYGROUND HOTEL,
1 500 QC-138 C, KAHNAWAKE,
QC, J0L 1B0


ÉLECTRICITÉ			
ÉCLAIRAGE DES CHAMBRES TYPIQUES			
PRÉPARÉ PAR:	M. SIMARD	ÉCHELLE:	TEL QU'INDIQUÉ
DOSSIER PAR:	G. BLONDIN	PLANCHE NO.:	
NO. DE PROJET:	2024-023		E-400

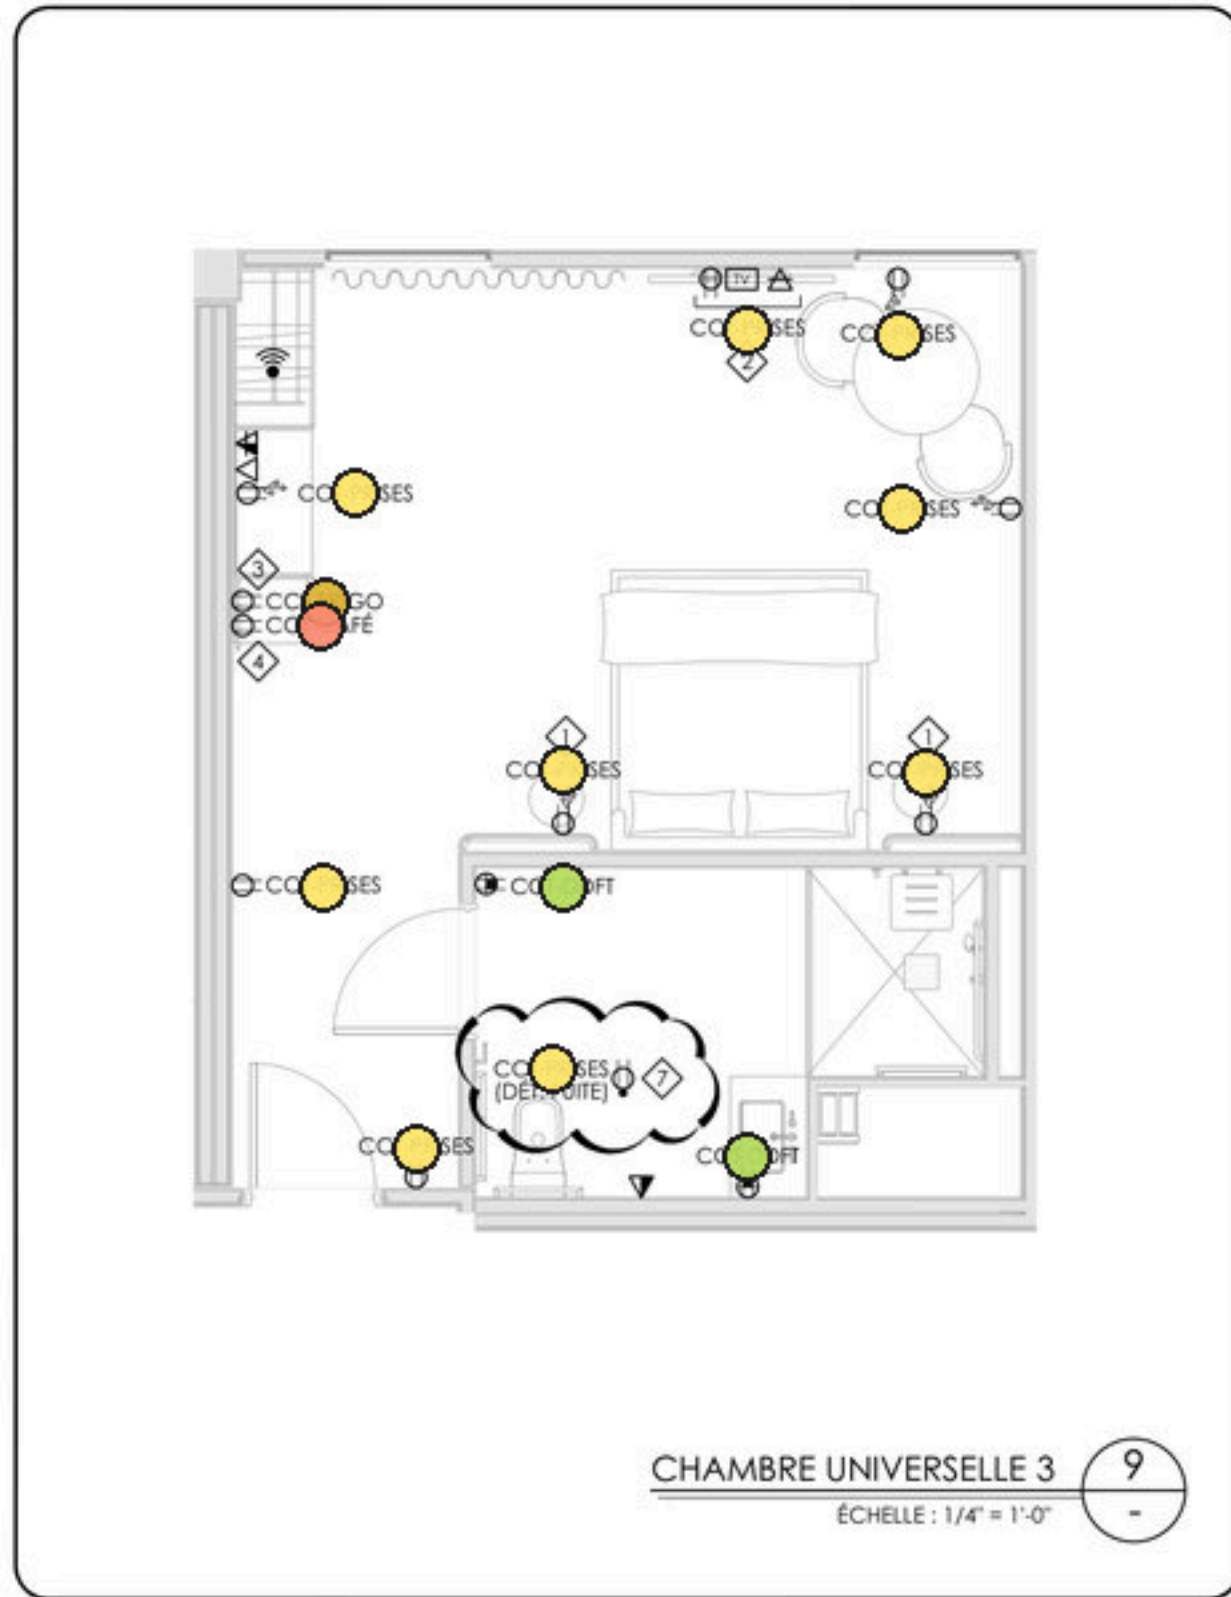


CHAMBRE UNIVERSELLE 3 9
ÉCHELLE : 1/4" = 1'-0"

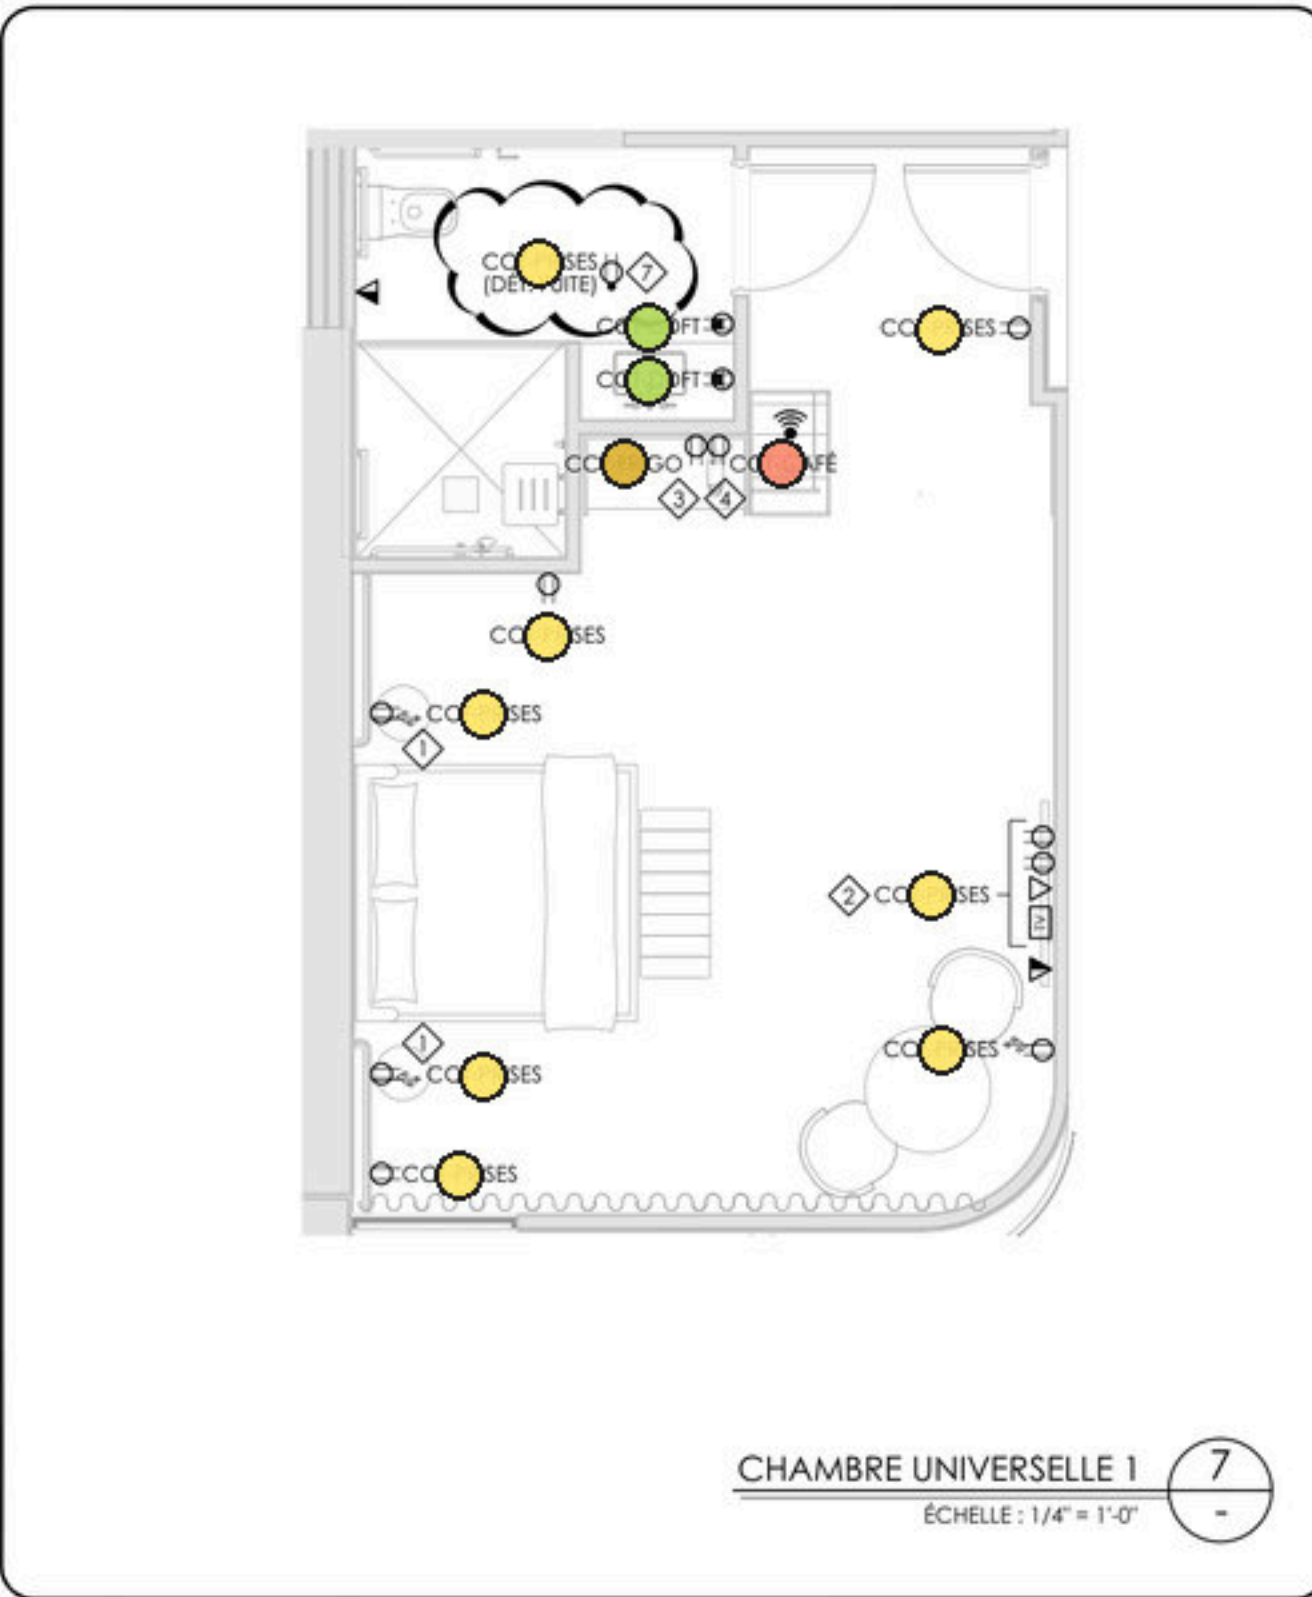


CHAMBRE UNIVERSELLE 1 7
ÉCHELLE : 1/4" = 1'-0"

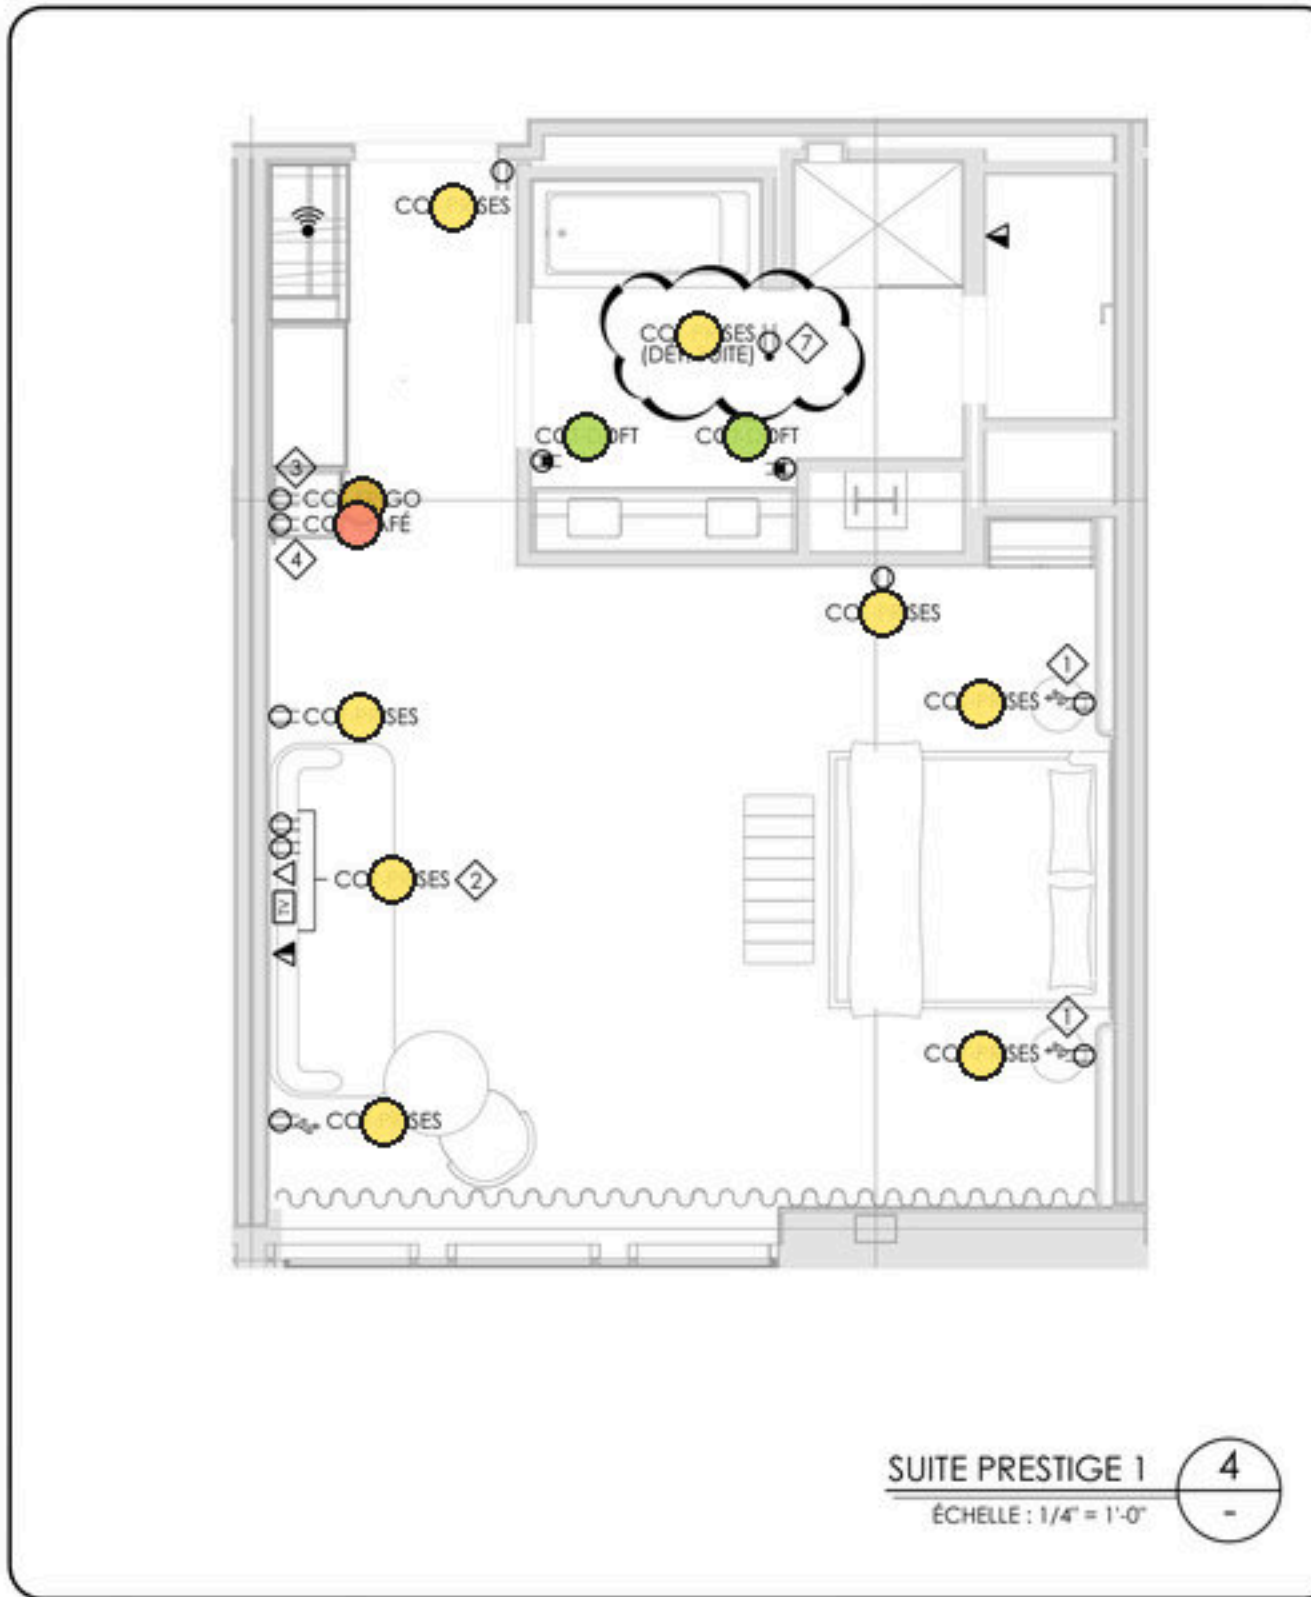


SUITE PRESTIGE 1 4
ÉCHELLE : 1/4" = 1'-0"

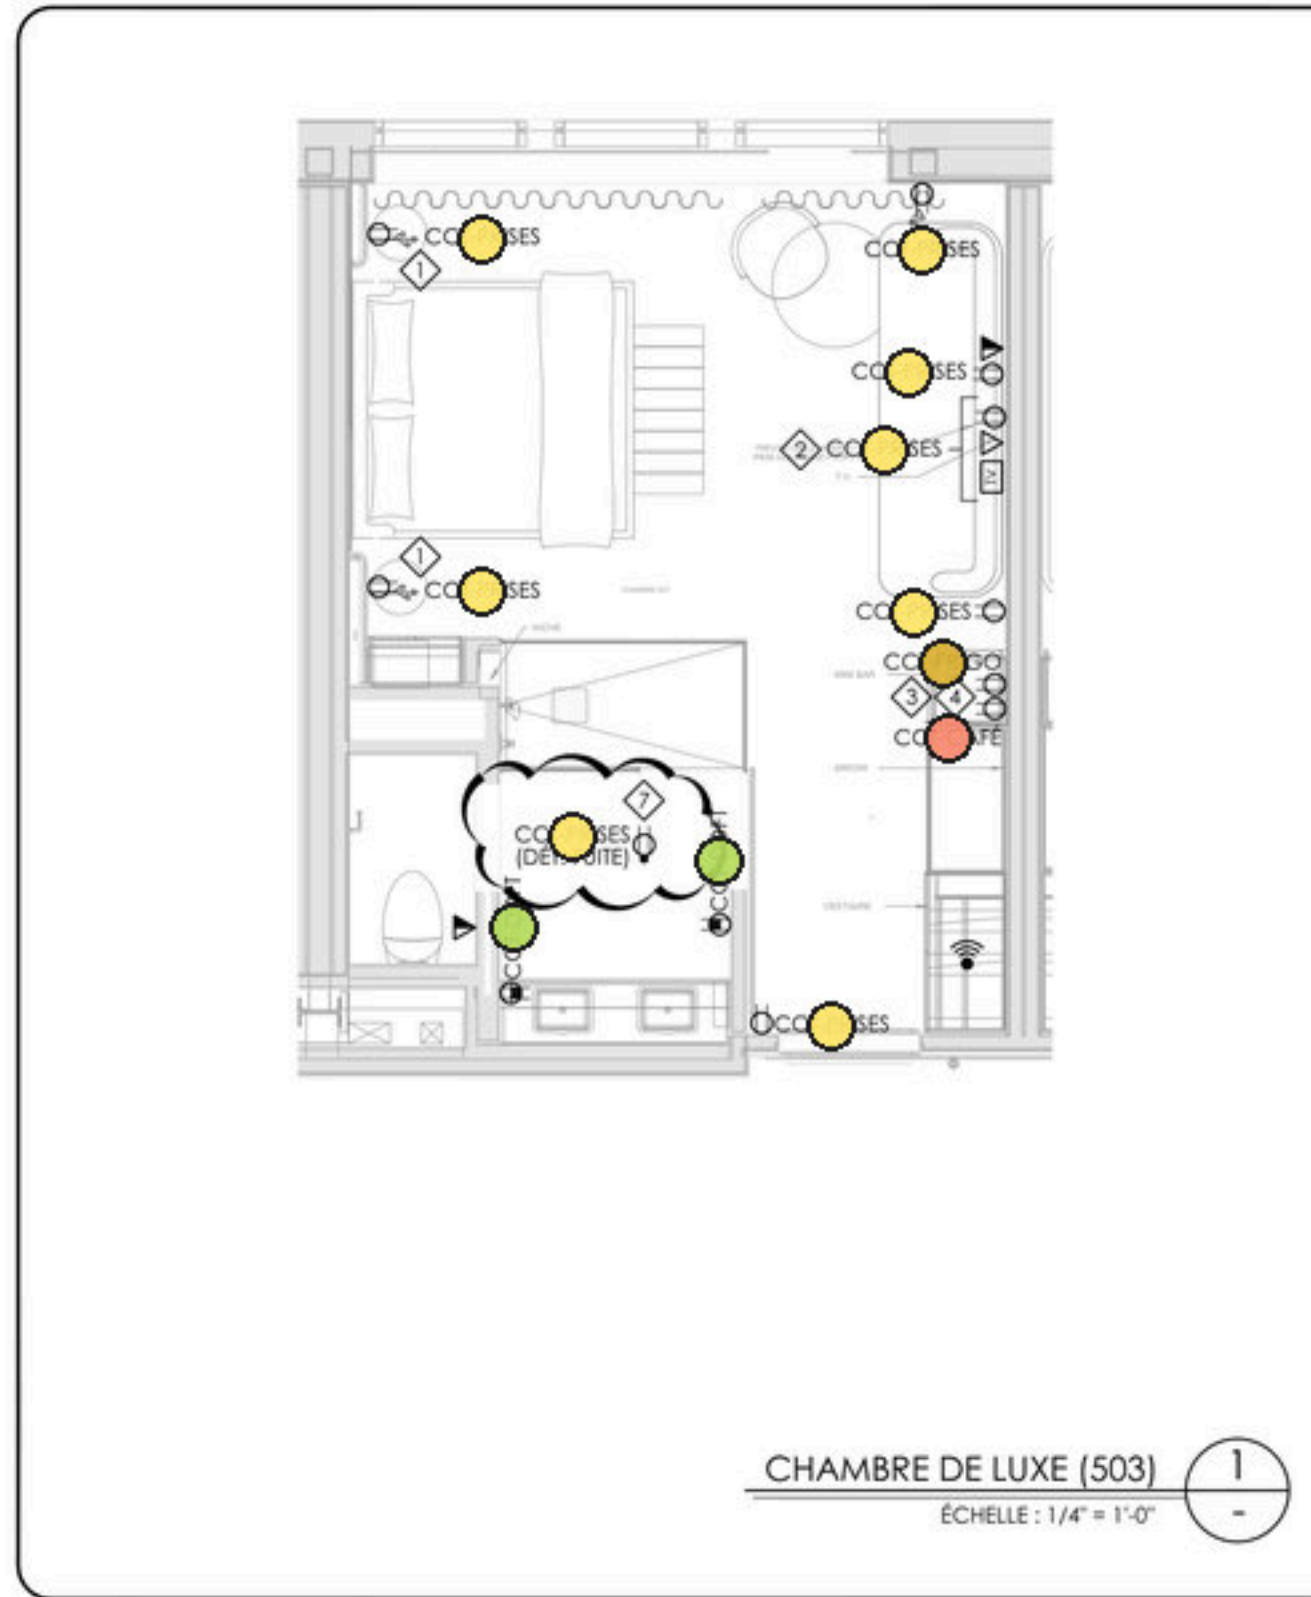


CHAMBRE DE LUXE (503) 1
ÉCHELLE : 1/4" = 1'-0"

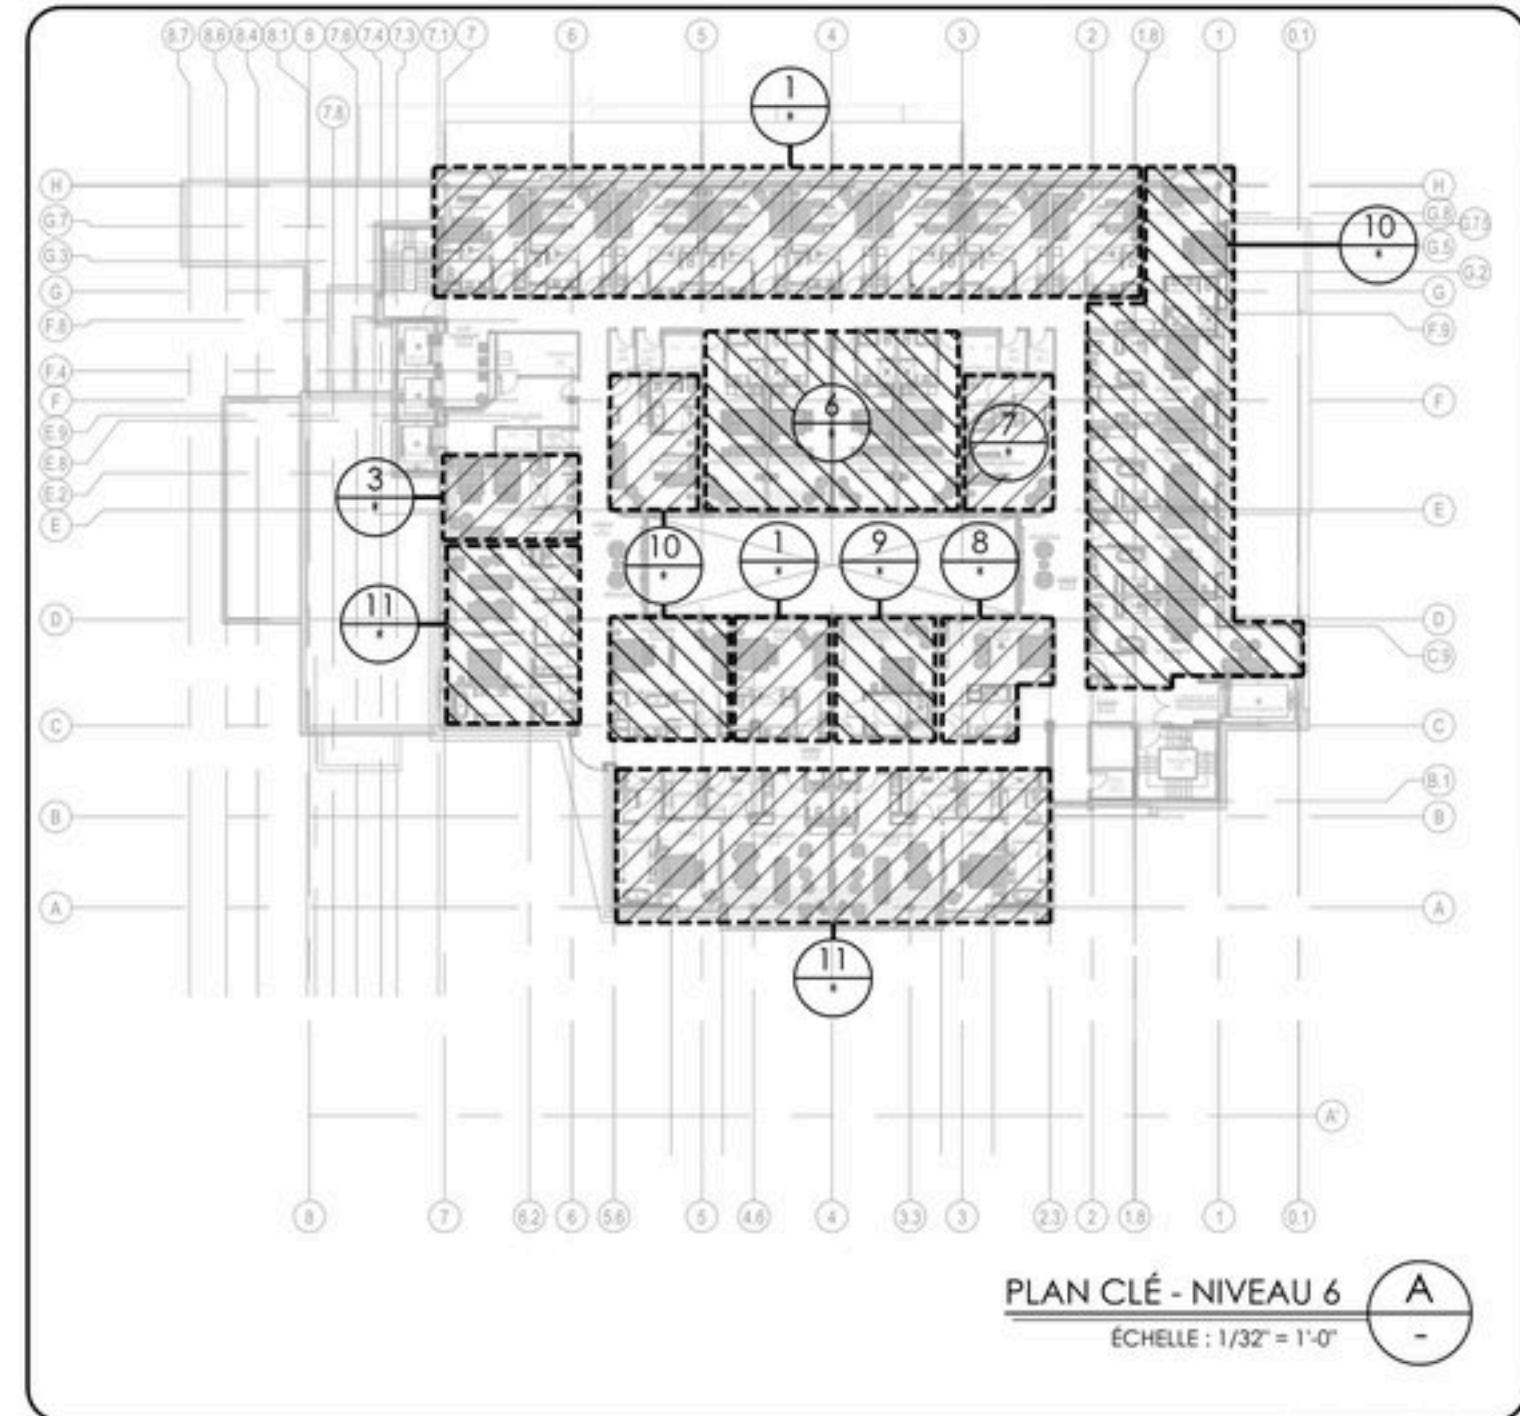


PLAN CLÉ - NIVEAU 6 A
ÉCHELLE : 1/32" = 1'-0"

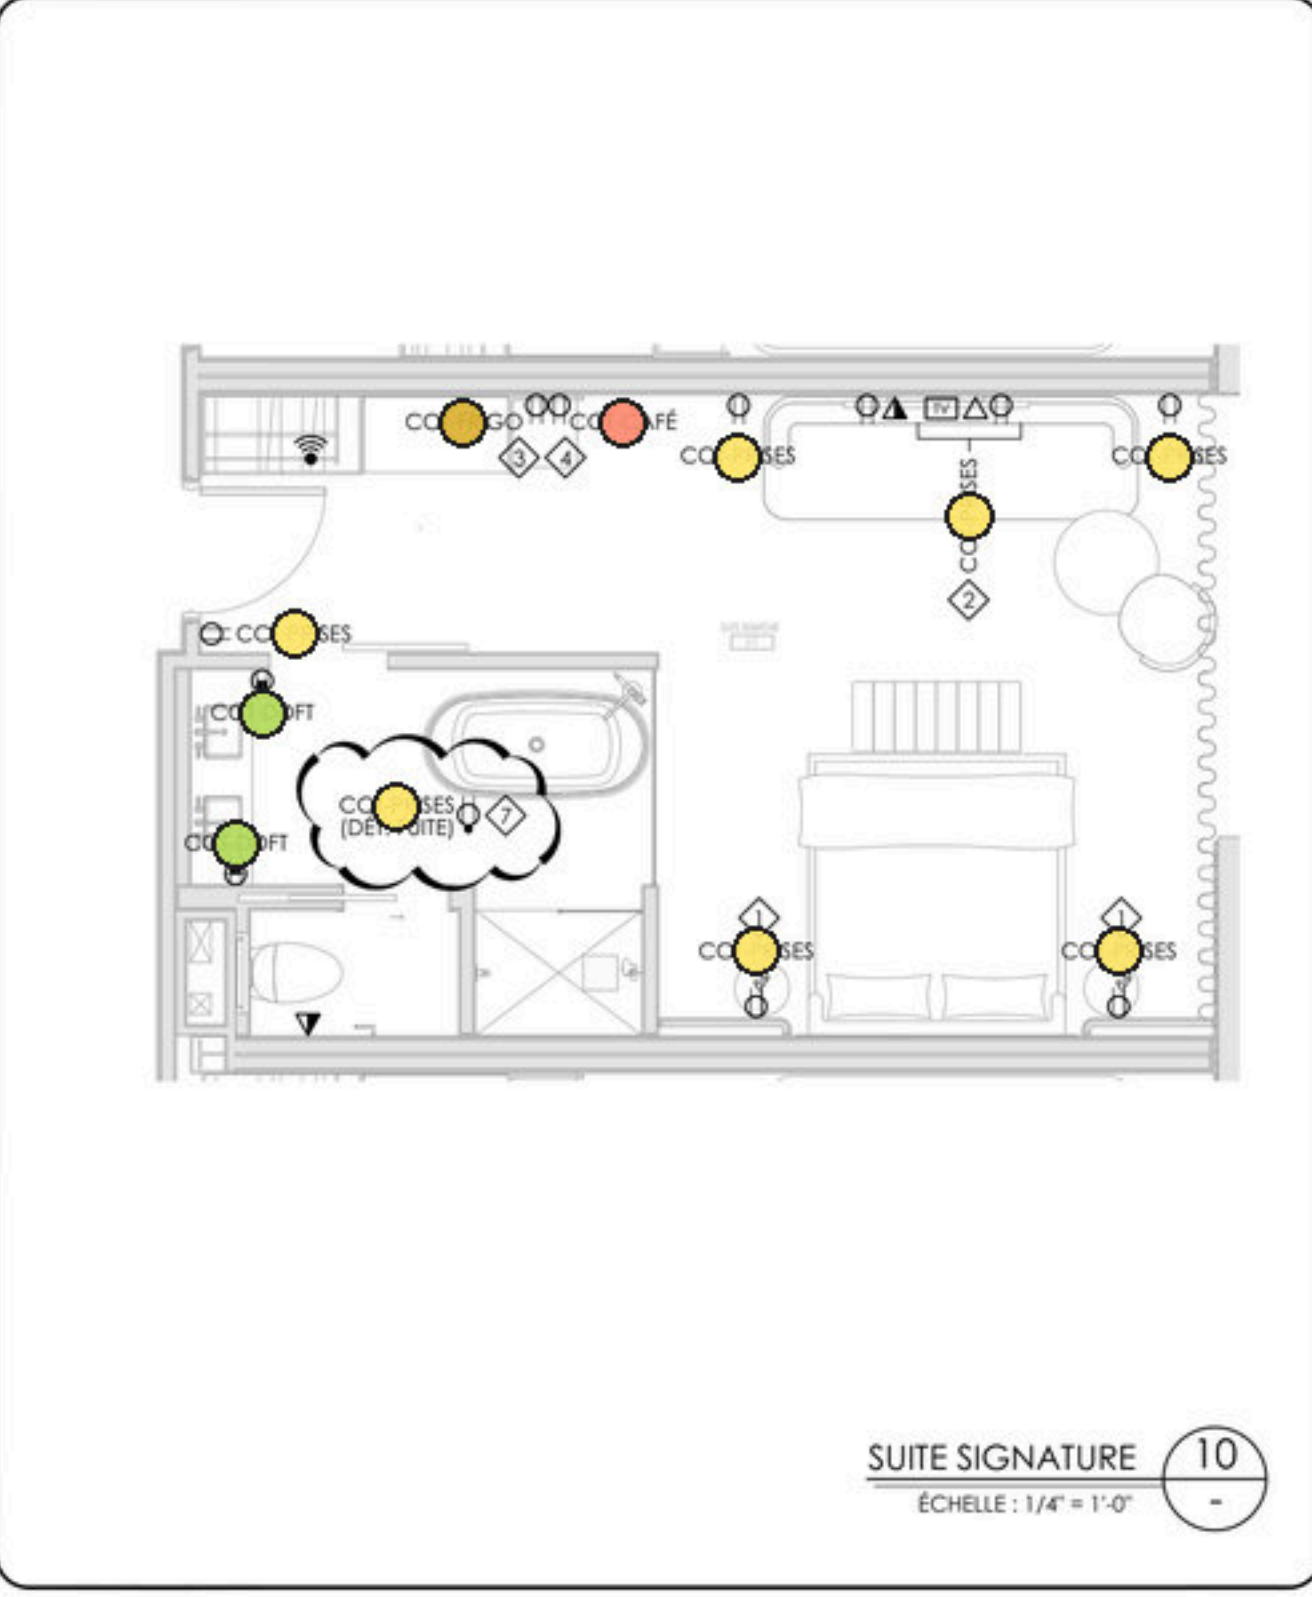


SUITE SIGNATURE 10
ÉCHELLE : 1/4" = 1'-0"

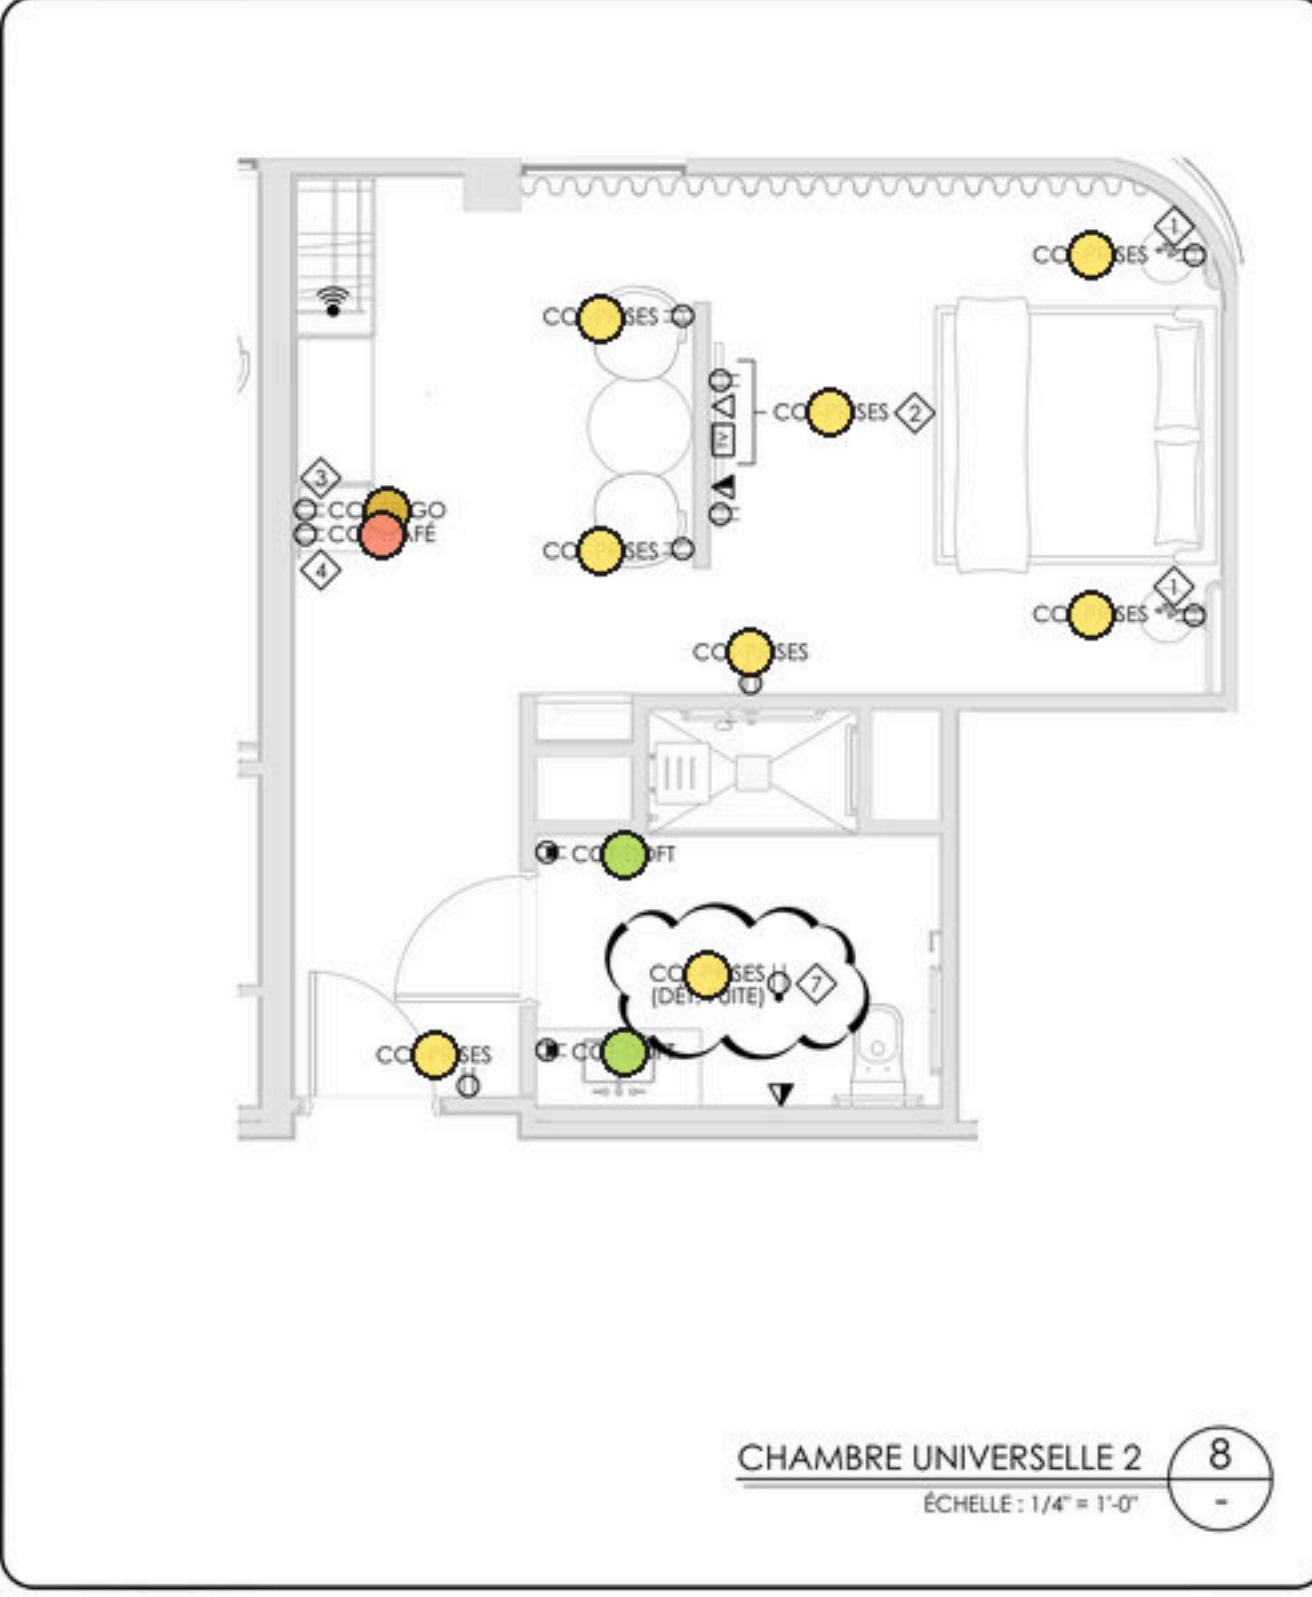


CHAMBRE UNIVERSELLE 2 8
ÉCHELLE : 1/4" = 1'-0"

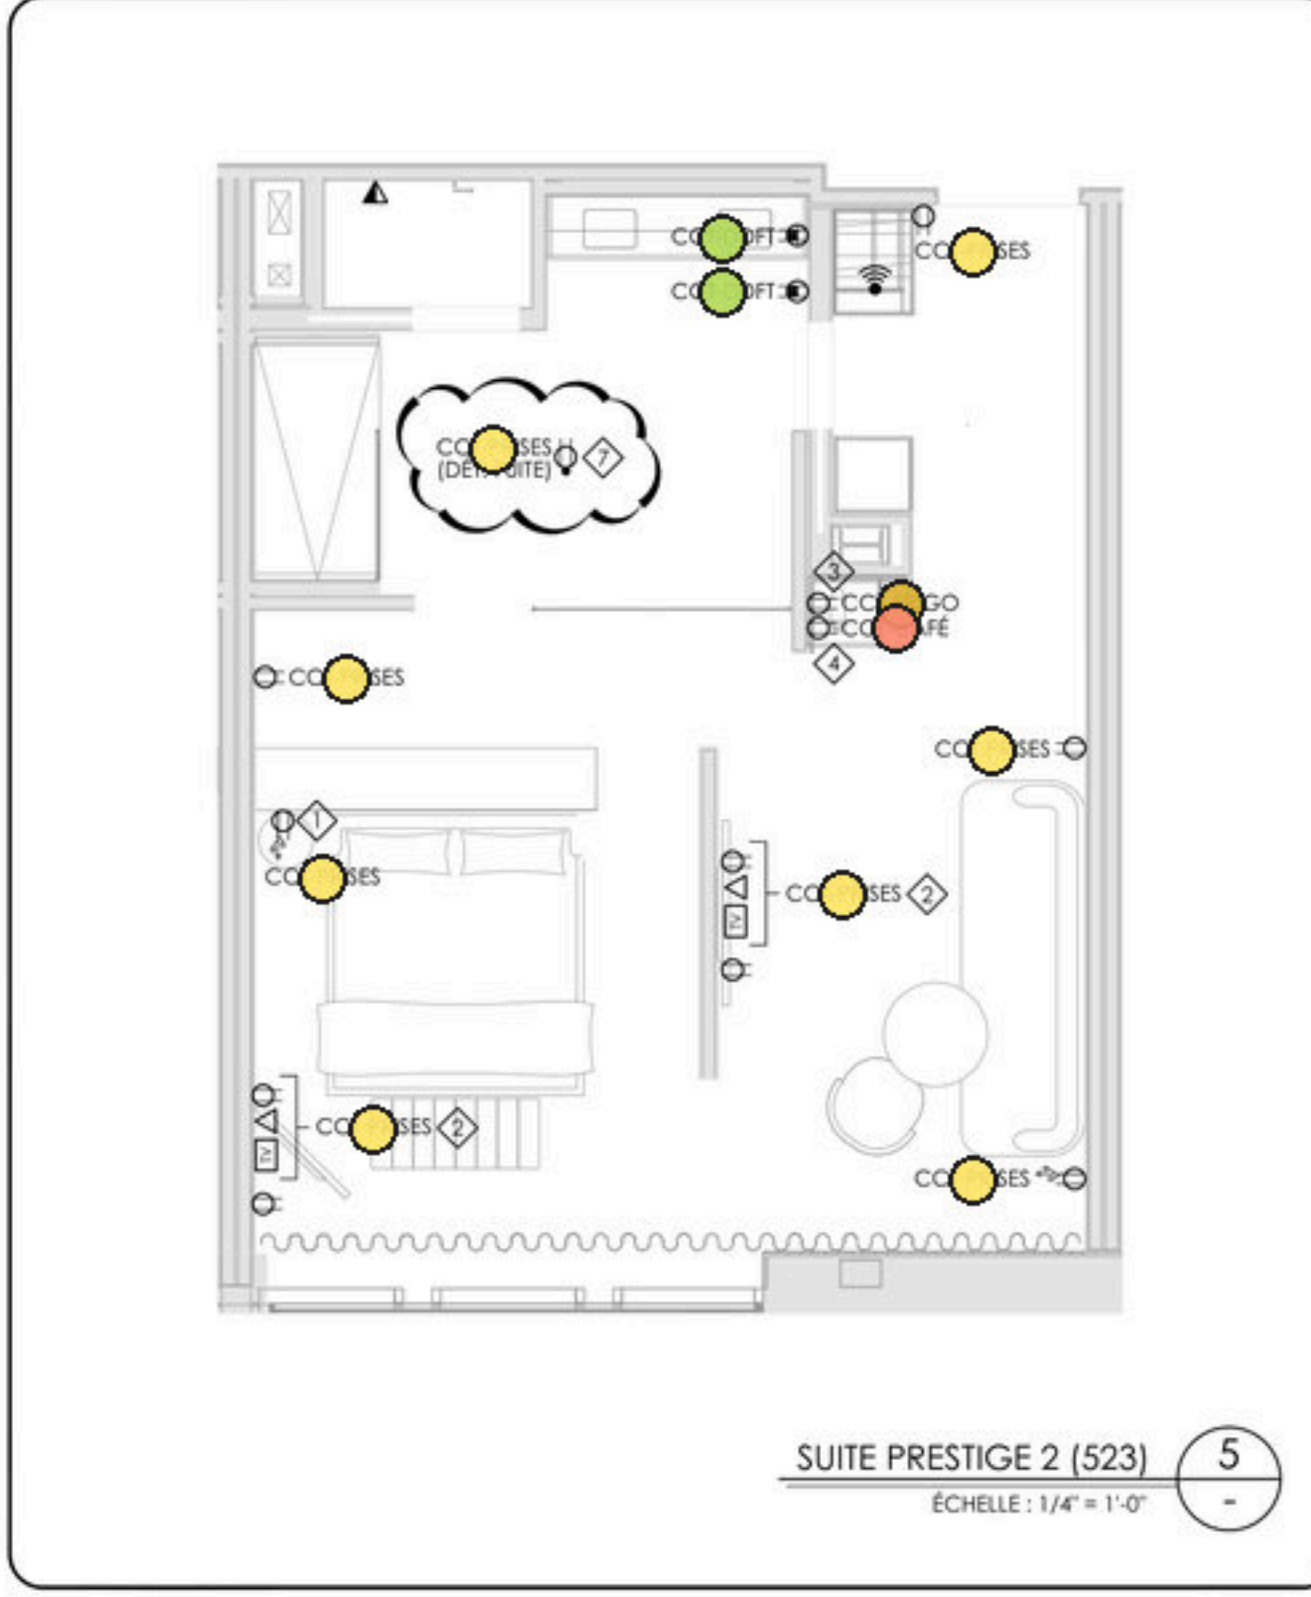

SUITE PRESTIGE 2 (523) 5
ÉCHELLE : 1/4" = 1'-0"

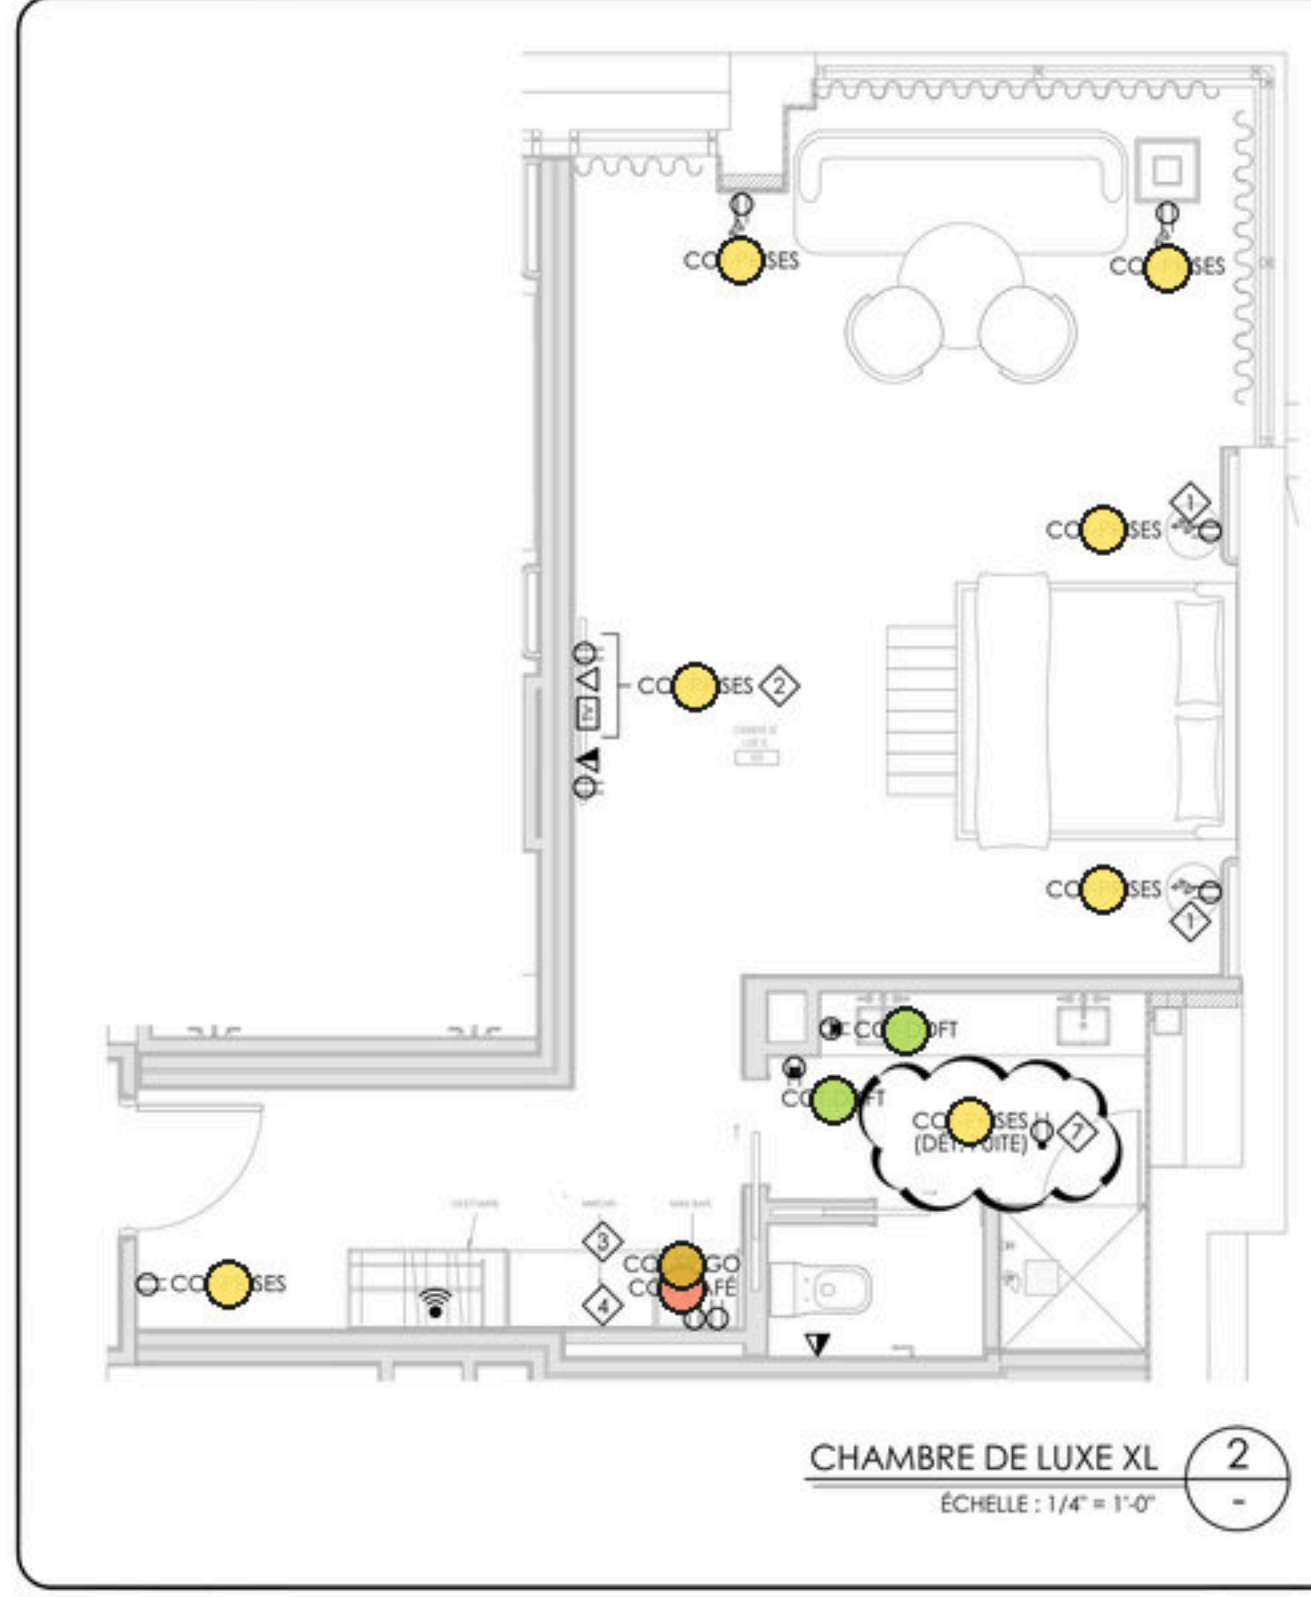


CHAMBRE DE LUXE XL 2
ÉCHELLE : 1/4" = 1'-0"

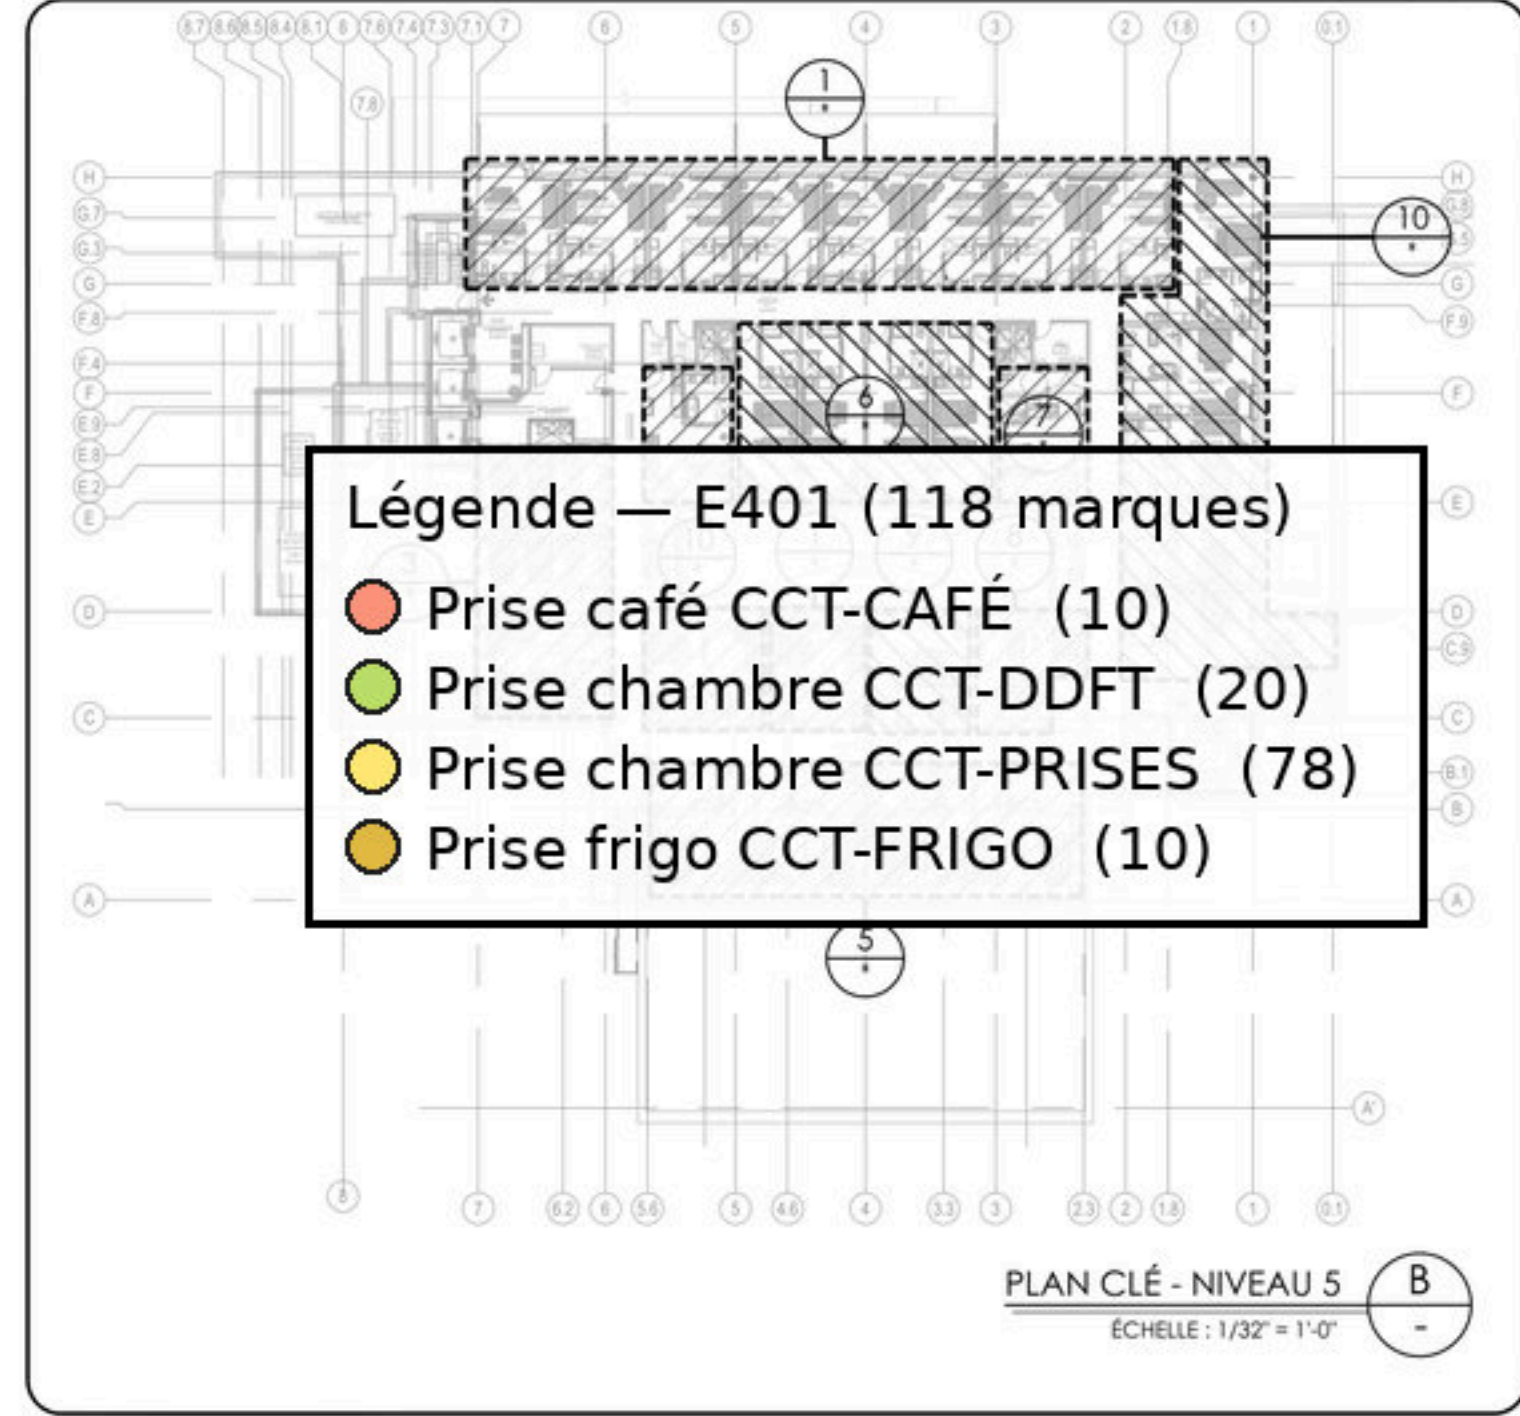

PLAN CLÉ - NIVEAU 5 B
ÉCHELLE : 1/32" = 1'-0"

- Légende — E401 (118 marques)**
- Prise café CCT-CAFÉ (10)
 - Prise chambre CCT-DDFT (20)
 - Prise chambre CCT-PRISES (78)
 - Prise frigo CCT-FRIGO (10)

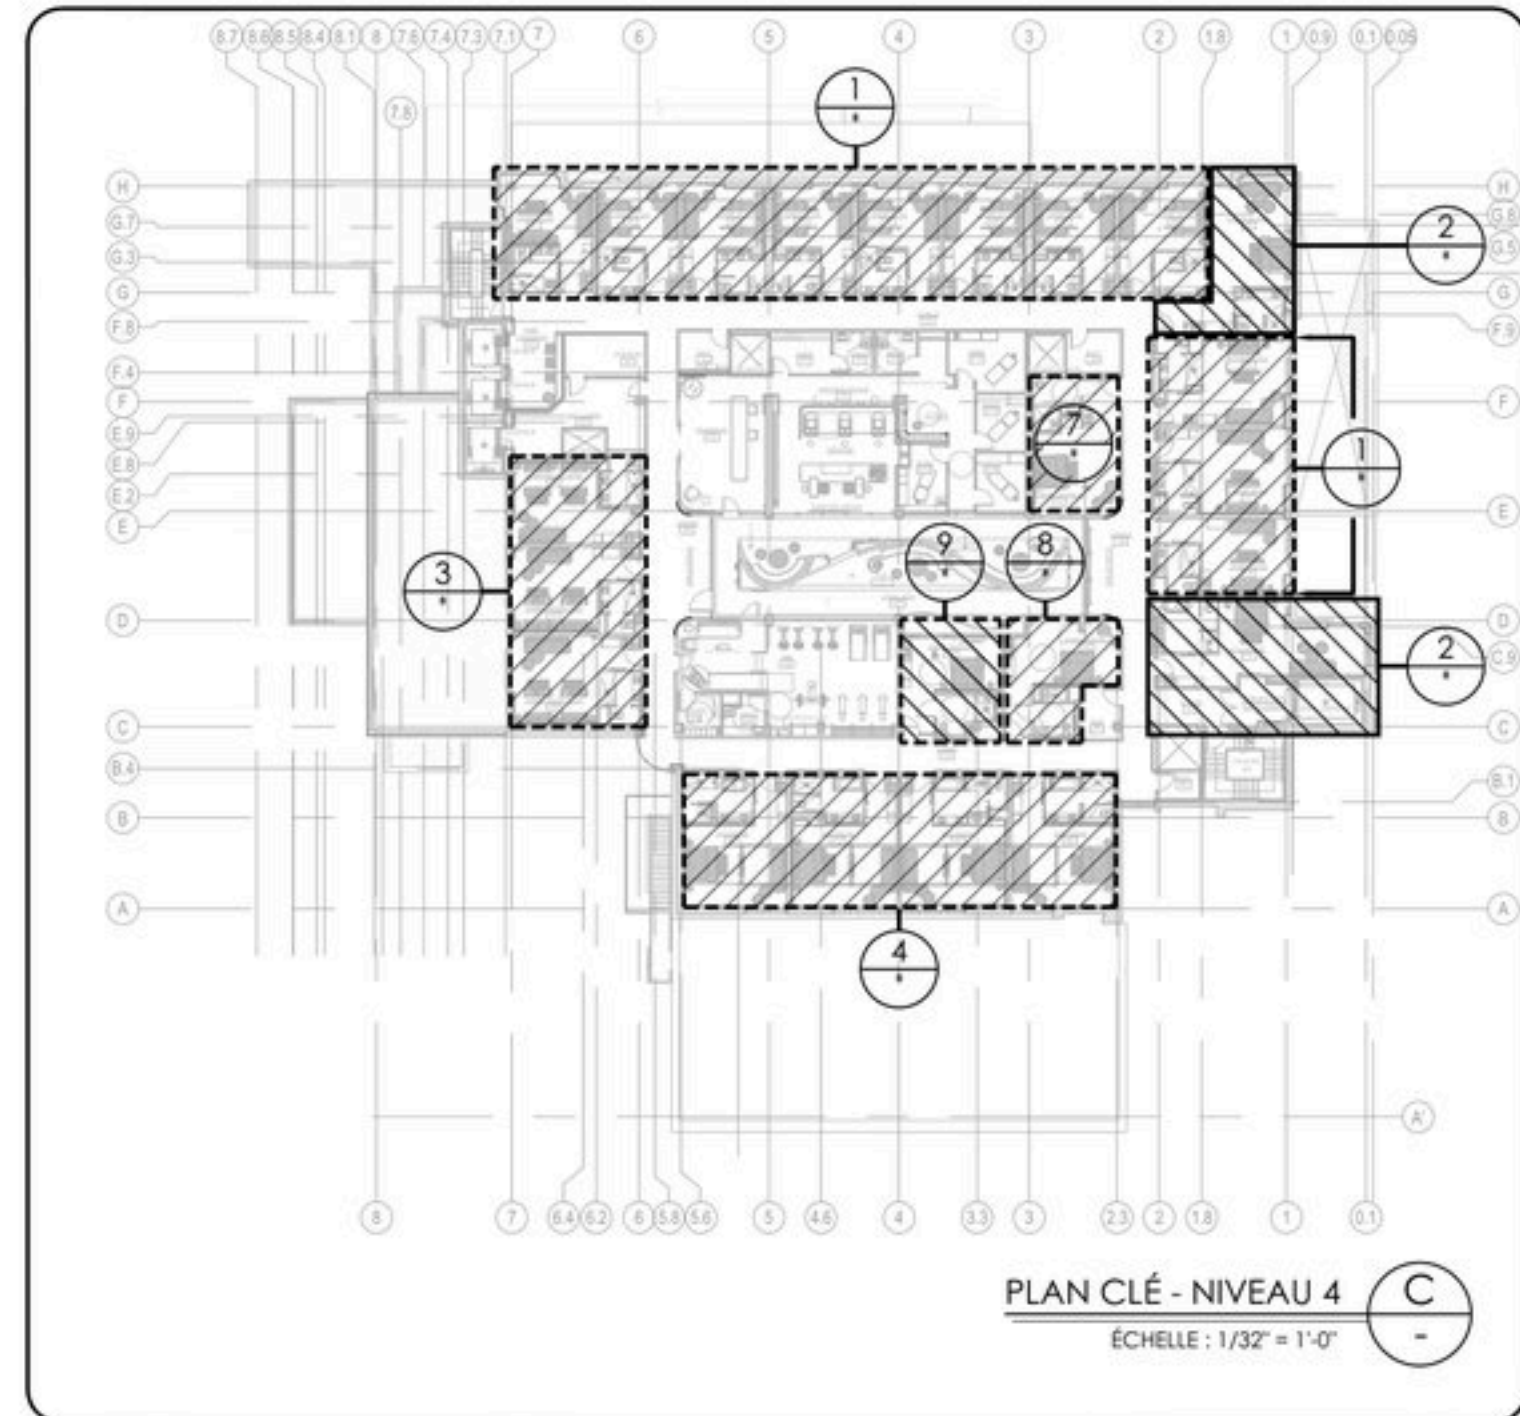


PLAN CLÉ - NIVEAU 4 C
ÉCHELLE : 1/32" = 1'-0"


Panneaux : Logements Type (Couleur Blanc)									
Tronçon : 12/22/23		BARRIÈRES : 100A		PHASE : 1		FILS : 3		CIRCUITS : 30	
DESCRIPTION		VA		A		B		MONTAGE ENCASTRÉ	
LOCAL TOUT USAGE		500		15		150		REC-X, VE-X, SDB	
PRISE CAFÉ		500		15		3		PRISES SERVICES	
REFRIGÉRATEUR		800		15		4		PRISE VANITÉ SDB	
PRISES COMPTOIR		500		20		15		PRISES CHAMBRE	
AUTRES PRISES CUISINE		1000		15		15		ÉCLAIRAGE	
PRISES MICRO-ONDES		1000		15		15		ÉCLAIRAGE	

① DISJONCTEUR COMBINÉ ANTI-ARCS


CALCUL DE CHARGE
SURFACE: 107 m²
CHARGE DE BASE:
PREMIER 45 m².....1 500 W
SECOND 45 m².....1 500 W
SURFACE SUP.....1 000 W
CHARGE SUPÉRIEURE À 1 500 W@25%.....0 W
ALLOCATION DE 6kW (PAS DE CUISINIÈRE).....6 000 W
TOTAL: 10 000W (48.1A@120/208V, 1PH, 3F.)

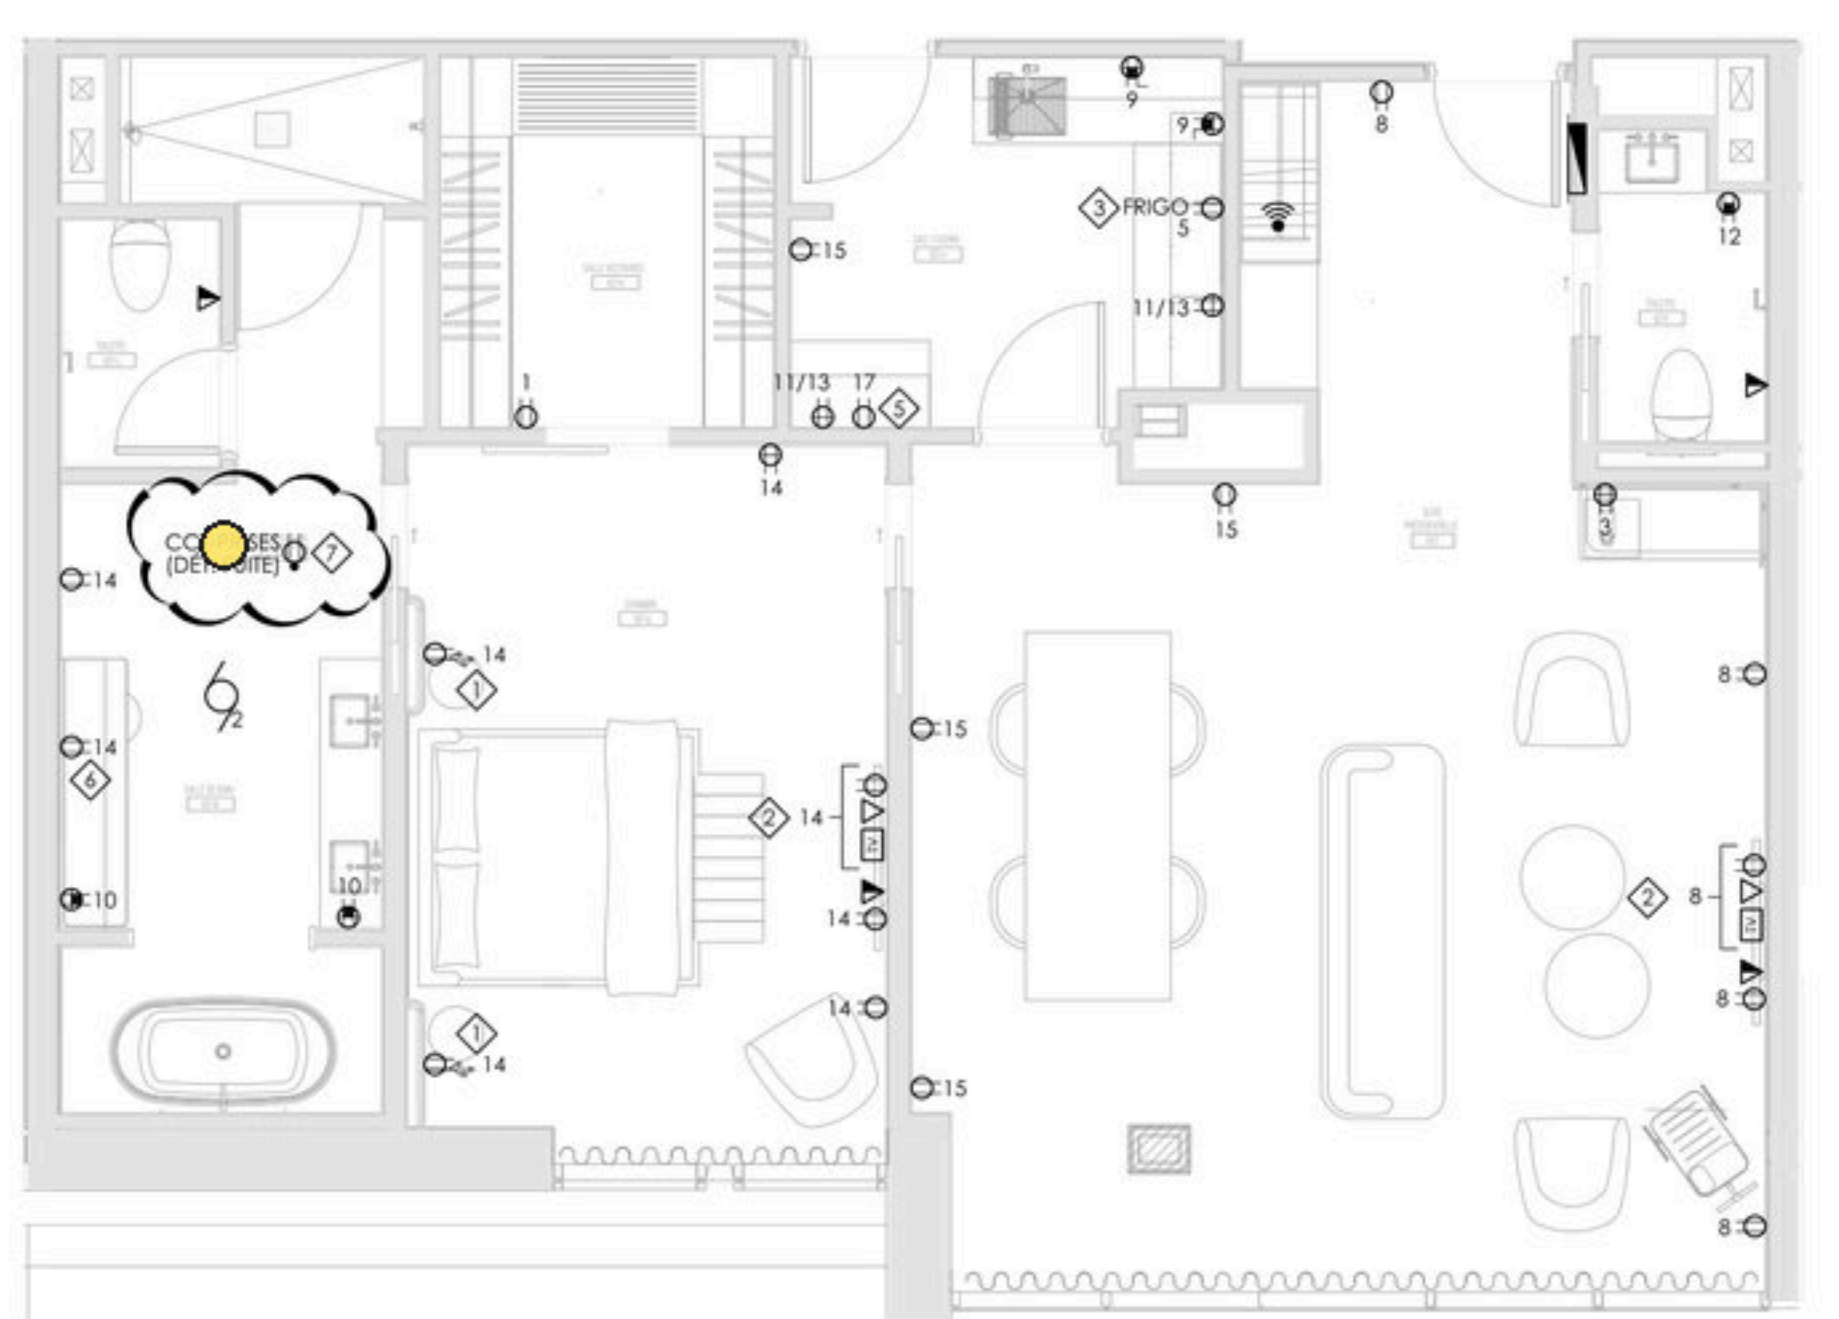

SUITE PRÉSIDENTIELLE 11
ÉCHELLE : 1/4" = 1'-0"

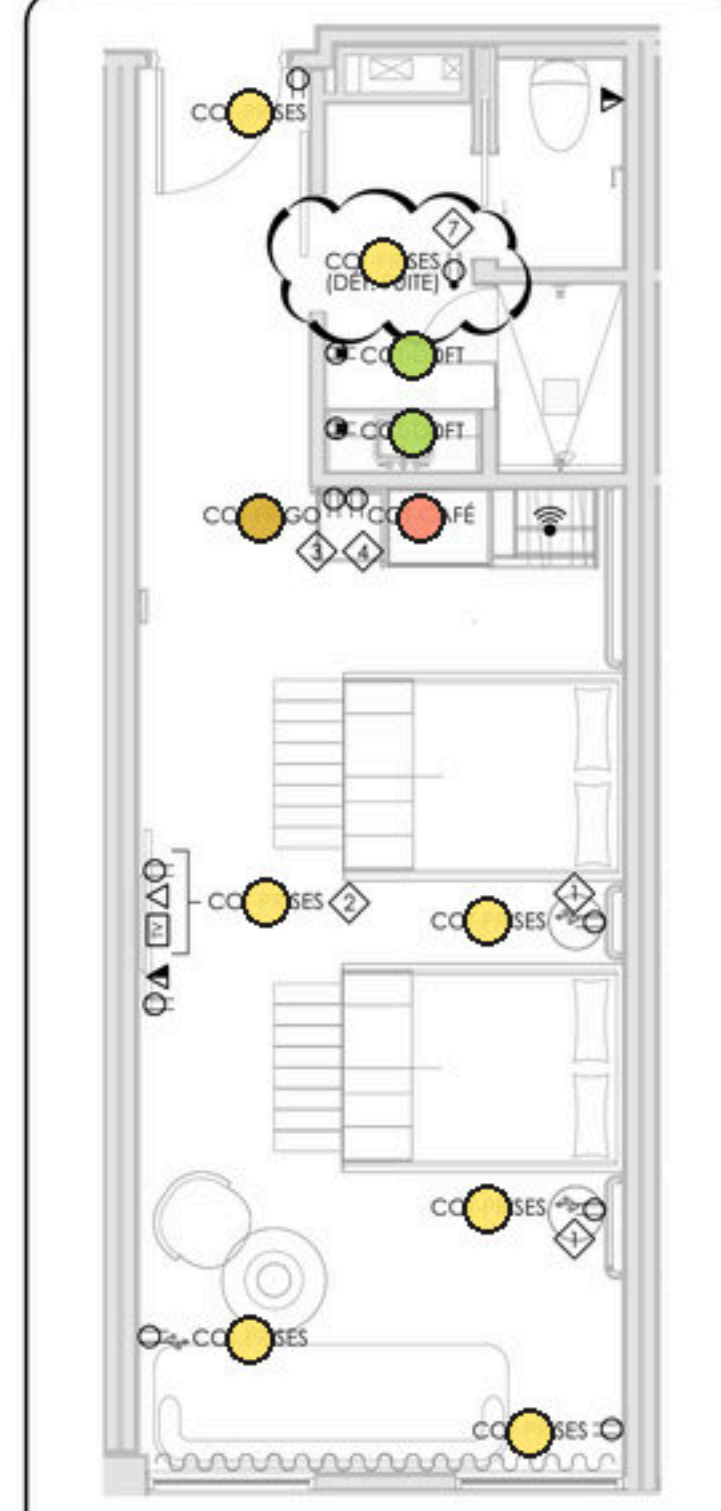

CHAMBRE DOUBLE 2 6
ÉCHELLE : 1/4" = 1'-0"

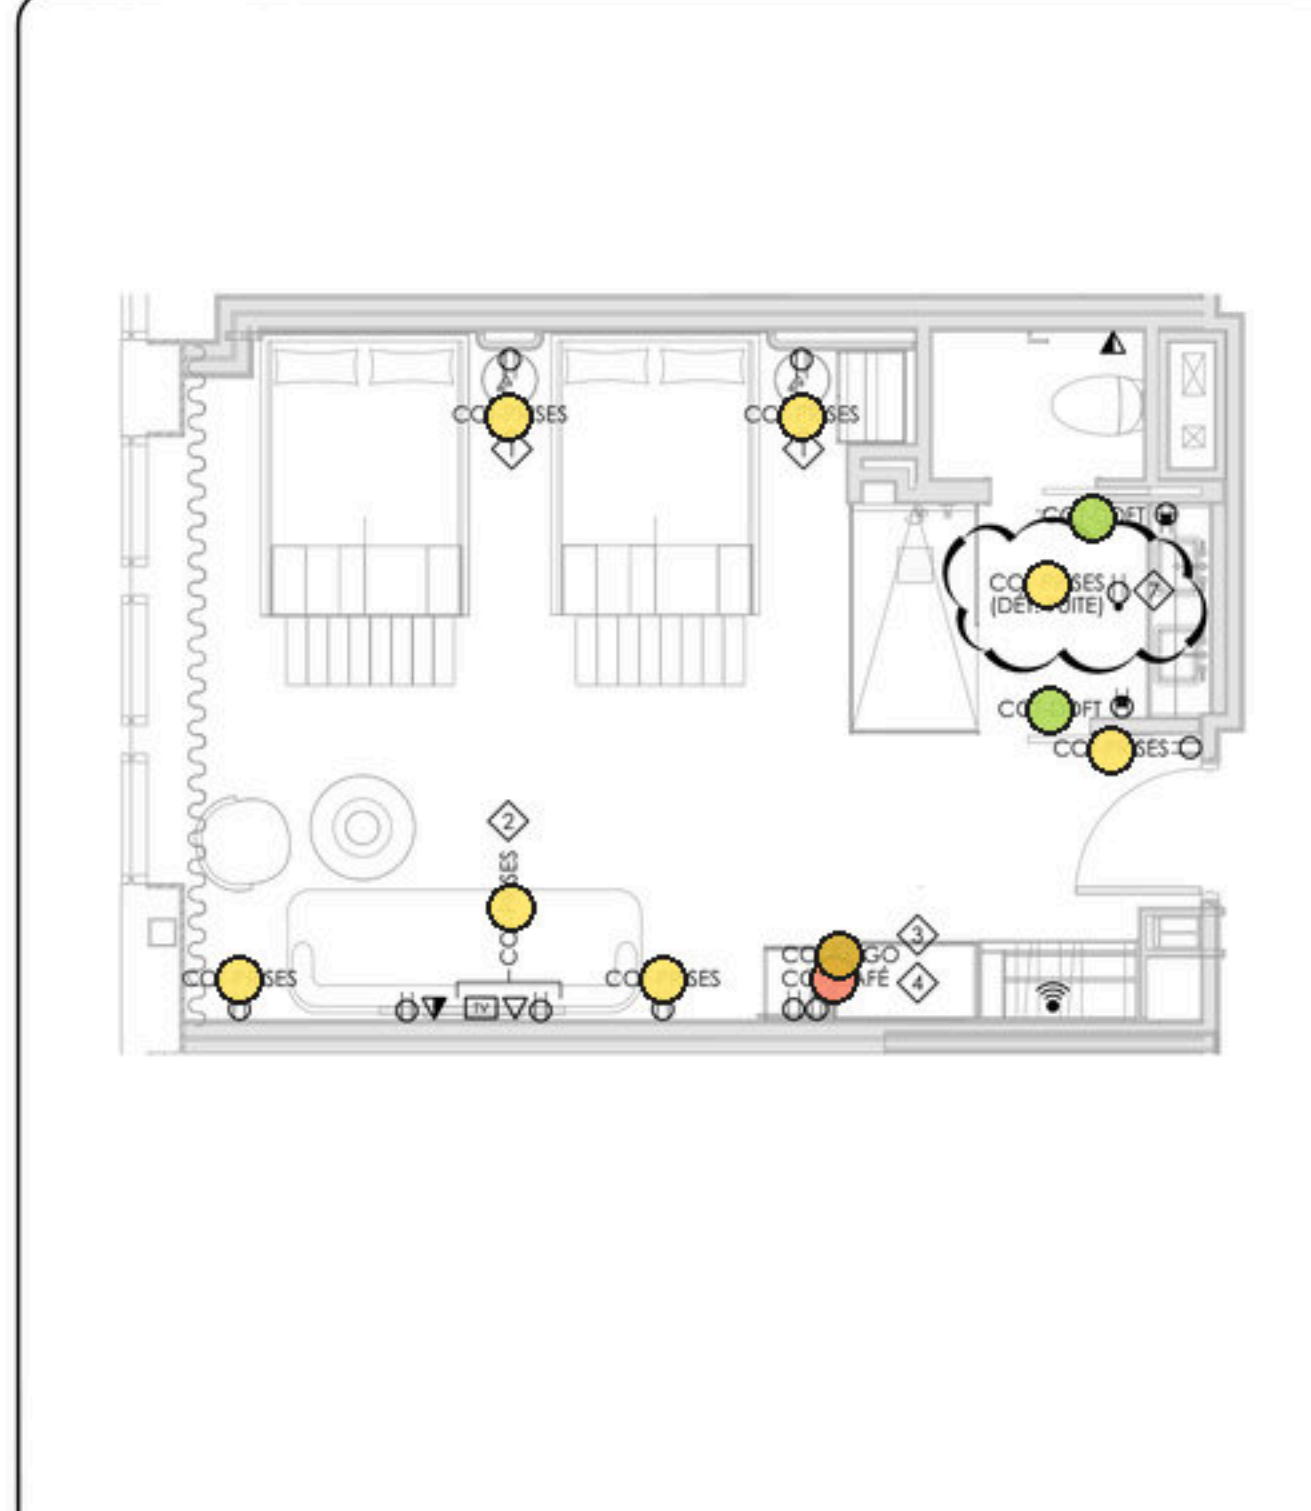

CHAMBRE DOUBLE 1 3
ÉCHELLE : 1/4" = 1'-0"

NOTES SPÉCIFIQUES

- ◇ HAUTEUR D'INSTALLATION À 27" DU PLANCHER FINI.
- ◇ HAUTEUR D'INSTALLATION À 66" DU PLANCHER FINI.
- ◇ HAUTEUR D'INSTALLATION À 18" DU PLANCHER FINI POUR LE FRIGO.
- ◇ HAUTEUR D'INSTALLATION À 40" DU PLANCHER FINI POUR LA MACHINE À CAFÉ.
- ◇ HAUTEUR D'INSTALLATION À 24" DU PLANCHER FINI POUR MICRO-ONDES.
- ◇ HAUTEUR D'INSTALLATION À 36" DU PLANCHER FINI.
- ◇ POSITION À COORDONNER AVEC L'ENTREPRENEUR EN PLOMBERIE.

NOTE GÉNÉRALE

- ◇ INSTALLATION DES TÉLÉVISEURS PAR L'ÉLECTRICIEN OU SON SOUS-TRAITANT EN TÉLÉCOMMUNICATION.

PLAN CLÉ

PROJET

lemay

2024-02-20

NE PAS UTILISER POUR CONSTRUCTION

1 20-02-26 APPEL D'OFFRES RÉVISION 1 M.S.

2 17-07-25 APPEL D'OFFRES M.S.

NO. J - M - A DESCRIPTION PAR

ÉMIS POUR:

2024-02-20

BFA

Blondin Fortin Associés

Experts conseils : mécanique, électrique, drainage

305, boulevard Cuyler-Loiselle
Sudbury, Ontario, Canada
G1P 1Y1
Tél. : 416-488-8000
www.blondinfortin.ca

PROJET

PLAYGROUND POKER

PROJET

PLAYGROUND HOTEL,
1 500 QC-138 C, KAHNAWAKE,
QC, J0L 1B0

PROJET




ÉLECTRICITÉ

SERVICES DES CHAMBRES TYPIQUES

PRÉPARÉ PAR : M. SIMARD ÉCHELLE : TEL QU'INDIQUÉ

COORDONNÉ PAR : G. BLONDIN PLANCHE NO.

NO. DE PROJET : 2024-023 E-401

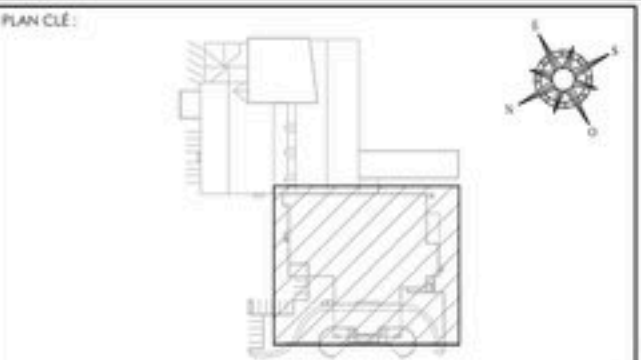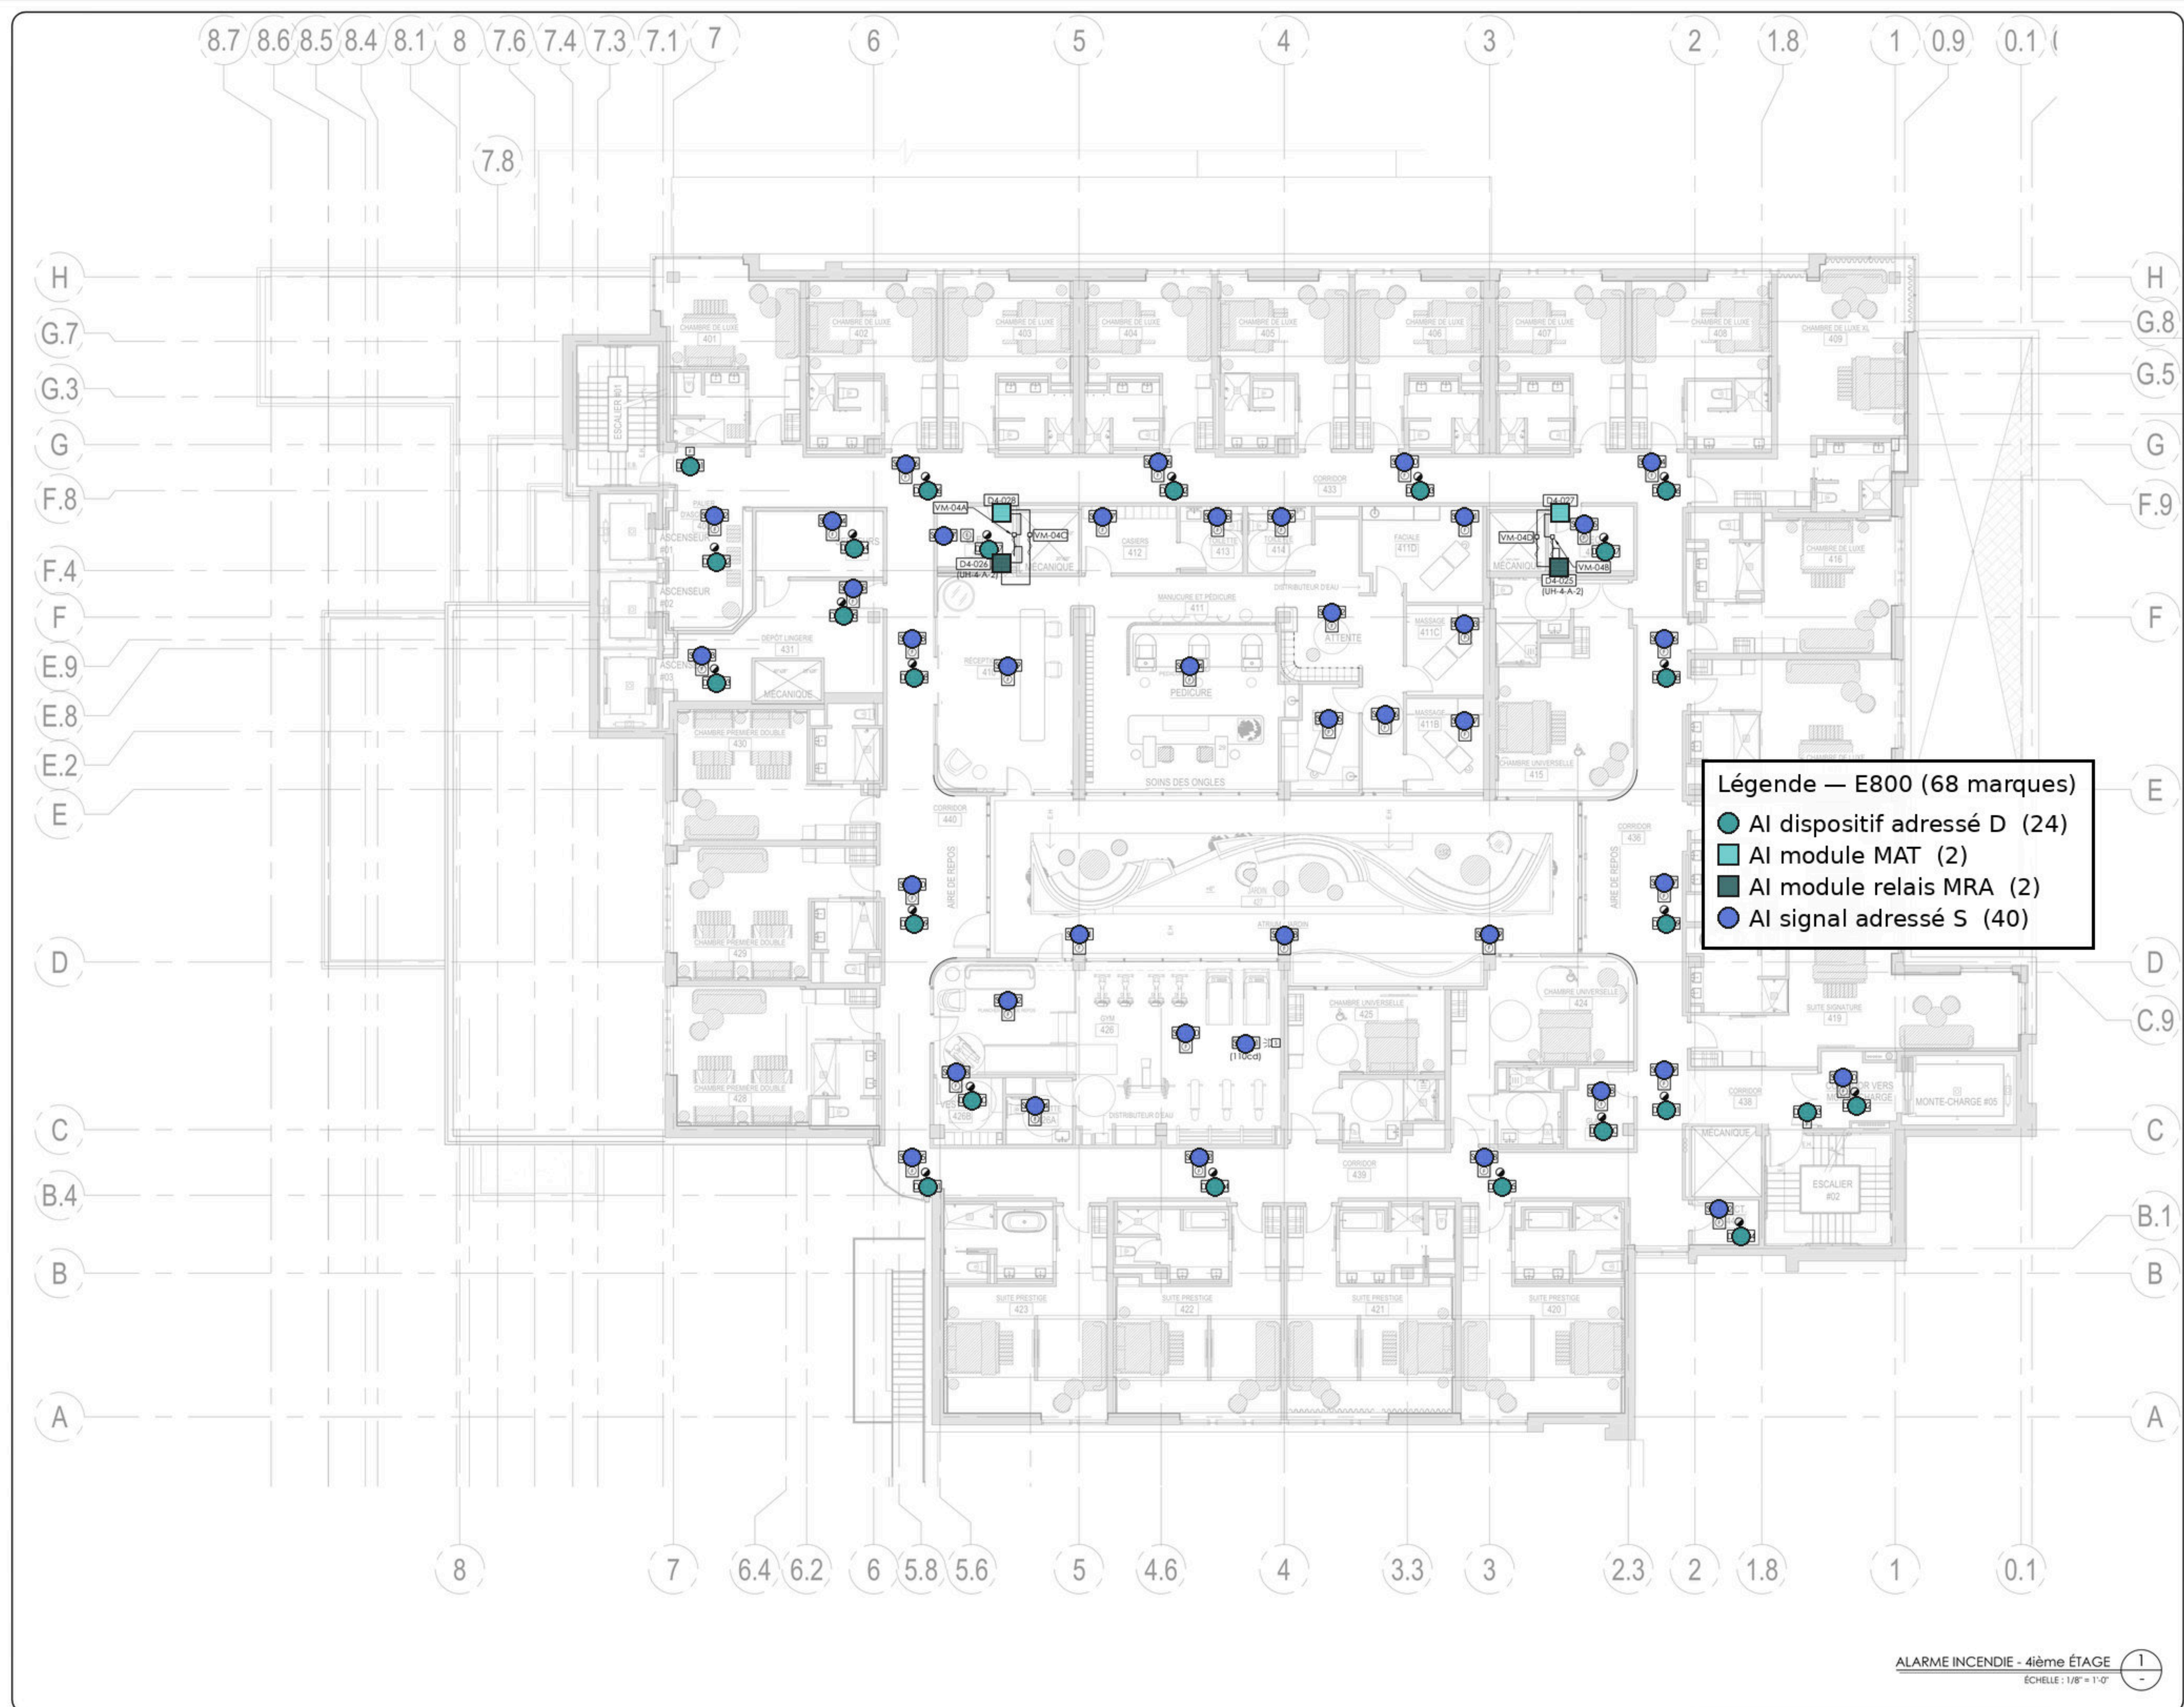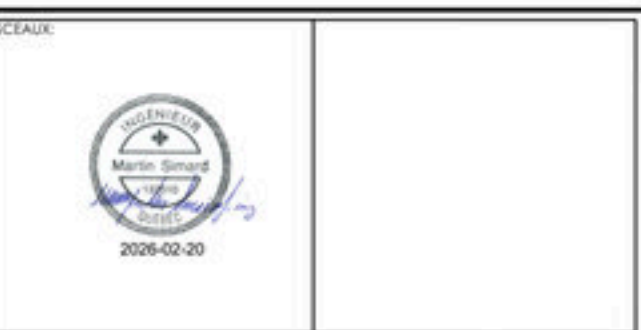[illegible]


PLAYGROUND POKER

PLAYGROUND HOTEL,
1 500 QC-138 C, KAHNAWAKE,
QC, J0L 1B0

OBJET: ÉLECTRICITÉ	
OBJET DU PLAN:	
ALARME INCENDIE 4ième ÉTAGE	
PRÉPARÉ PAR: M. SIMARD	ÉCHELLE TEL QU'INDIQUÉ
ESSINÉ PAR: G. BLONDIN	PLANCHÉ NO:
NO DE PROJET: 2024-023	E-800

NOTE GÉNÉRALE

- ◆ RACCORDER LES ÉQUIPEMENTS DE DÉTECTION ET DE SIGNALISATION SUR LES CIRCUITS PRÉVUS À CET EFFET AUX ÉTAGES.
- ◆ LES CIRCUITS DE SIGNALISATION (HP ET STROBES) DES HAUT PARLEURS ET DES STROBES DES CHAMBRES DOIVENT ÊTRE RACCORDES EN CLASSE.
- ◆ LES CIRCUITS DE SIGNALISATION (HP ET STROBES) DES CORRIDORS ET ZONES COMMUNES DOIVENT ÊTRE RACCORDES EN CLASSE. TERMINER LES CIRCUITS PAR UNE RÉSISTANCE DE LIN DE LIGNE.
- ◆ LE CÂBLAGE DOIT ÊTRE EN CUIVRE DE TYPE FAS-74 :
 - 3/14 TORÇADE POUR
 - 3/14 TORÇADE POUR STROBES
- ◆ INSTALLER LES COMPOSANTES EN CONFORMITÉ AVEC LA NORME CANULC-504 EN VIGUEUR.
- ◆ LE SYSTÈME D'ALARME INCENDIE DOIT ÊTRE VÉRIFIÉ EN CONFORMITÉ AVEC LA NORME CANULC-5537.

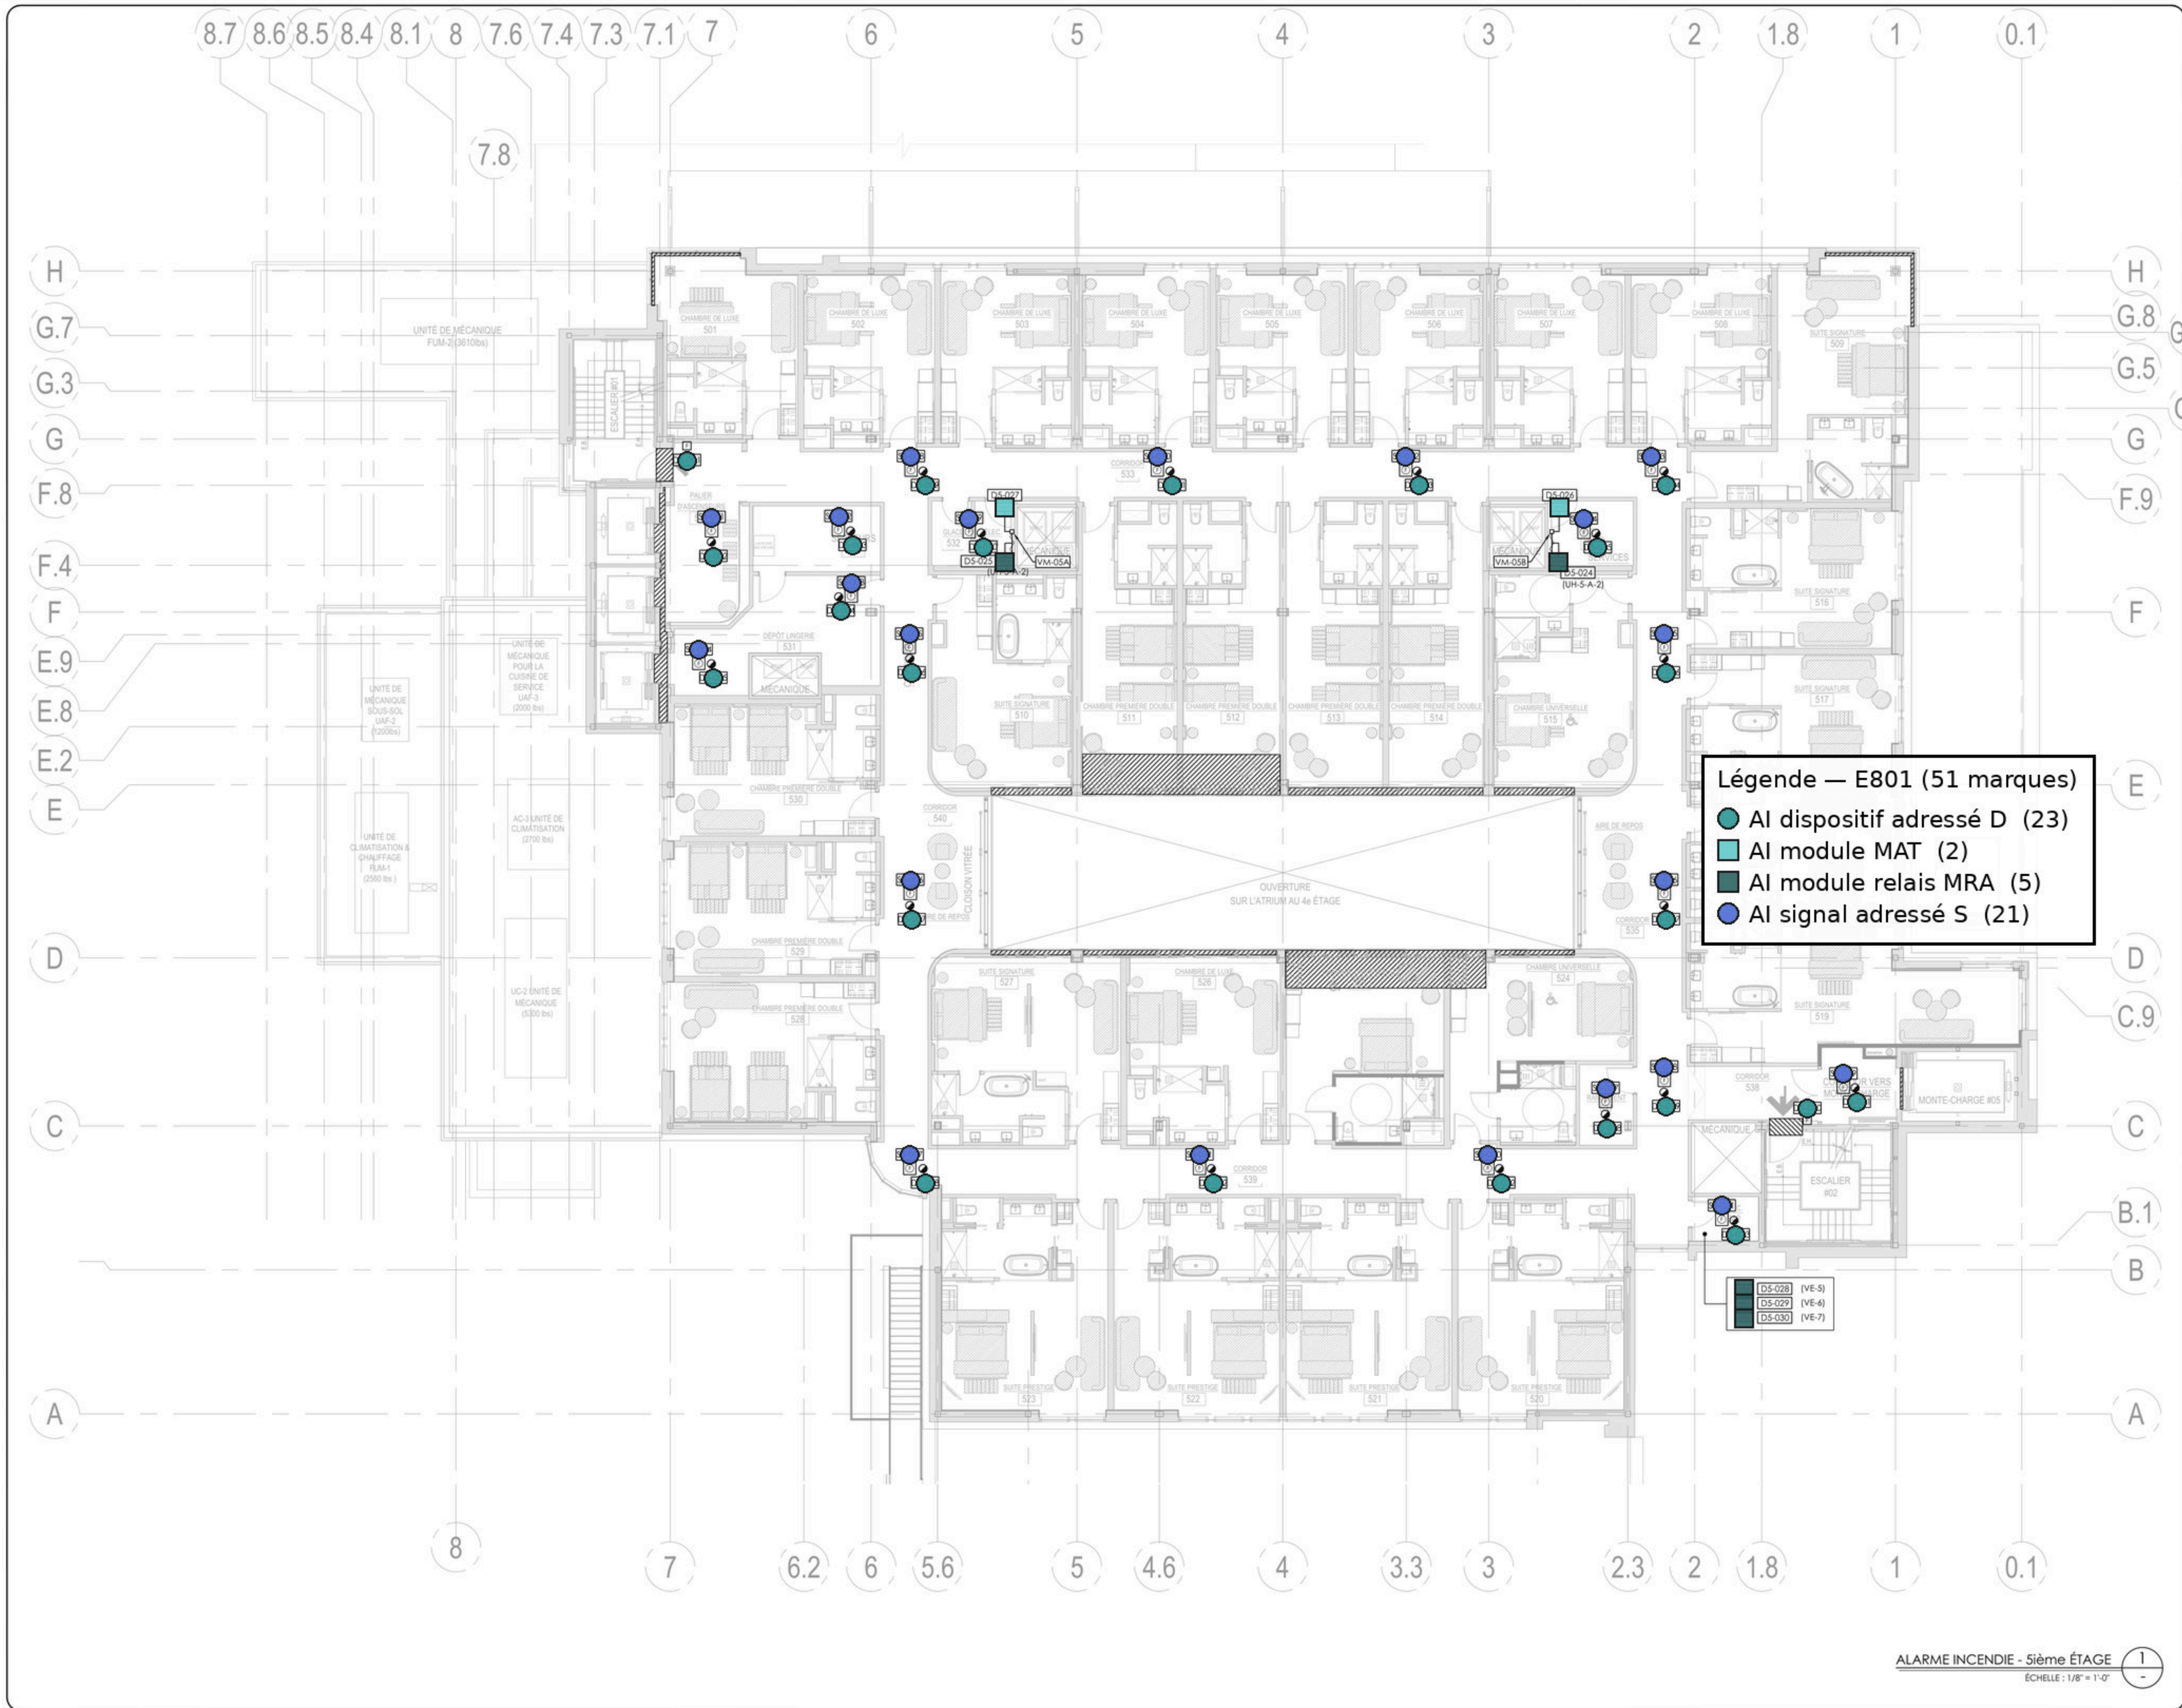

Légende — E801 (51 marques)

- AI dispositif adressé D (23)
- AI module MAT (2)
- AI module relais MRA (5)
- AI signal adressé S (21)

ALARME INCENDIE - 8ème ÉTAGE
ÉCHELLE : 1/8" = 1'-0"

NOTE GÉNÉRALE

- ❖ RACCORDER LES ÉQUIPEMENTS DE DÉTECTION ET DE SIGNALISATION SUR LES CIRCUITS PRÉVUS À CET EFFET AUX ÉTAGES.
- ❖ LES CIRCUITS DE SIGNALISATION (HP ET STROBES) DES HAUT-PARLEURS ET DES STROBES DES CHAMBRES DOIVENT ÊTRE RACCORDÉS EN CLASSE A.
- ❖ LES CIRCUITS DE SIGNALISATION (HP ET STROBES) DES CORRIDORS ET ZONES COMMUNES DOIVENT ÊTRE RACCORDÉS EN CLASSE B. TERMINER LES CIRCUITS PAR UNE RÉSISTANCE DE FIN DE LIGNE.
- ❖ LE CÂBLAGE DOIT ÊTRE EN CUVRE DE TYPE FAS-14:
 - 3/14 TORSADÉ POUR H.P.
 - 3/14 TORSADÉ POUR STROBES
- ❖ INSTALLER LES COMPOSANTES EN CONFORMITÉ AVEC LA NORME CAN/ULC-5524 EN VIGUEUR.
- ❖ LE SYSTÈME D'ALARME-INCENDIE DOIT ÊTRE VÉRIFIÉ EN CONFORMITÉ AVEC LA NORME CAN/ULC-5537.

PLAN GÉNÉRAL

NOTES

lemay

1885, rue Saint-Jacques
Montréal, Québec H3K 2W1
Tél. : 514 399-1111
www.lemay.ca

1885, rue Saint-Jacques
Montréal, Québec H3K 2W1
Tél. : 514 399-1111
www.lemay.ca

NE PAS
UTILISER POUR
CONSTRUCTION

N°	DATE	DESCRIPTION	ÉMIS PAR
2	20-02-26	APPEL D'OFFRES RÉVISION 1	M.S.
1	24-09-25	ADDENDA ME-01	M.S.
0	17-07-25	APPEL D'OFFRES	M.S.

NO. J - M - A

ÉMIS POUR:

2020-02-20

BFA
Blondin Fortin Associés

Experts conseils - mécanique
électrique - électricité

305, boul. Cyrille-Lapointe
Montréal, Québec H3T 2G1
Tél. : 514 399-1111
www.blondinfortin.ca

PLAYGROUND POKER

PROJET:



PLAYGROUND HOTEL,
1 500 QC-138 C, KAHNAWAKE,
QC, J0L 1B0

ÉLECTRICITÉ

ALARME INCENDIE
8ème ÉTAGE

PRÉPARÉ PAR:	ÉCHELLE:	TEL QU'INDIQUE
M. SIMARD	1/8" = 1'-0"	
G. BLONDIN		
NO. DE PROJET:		
2024-023		

E-801

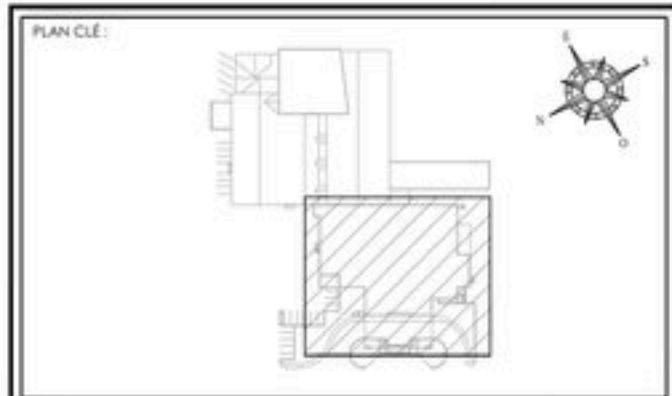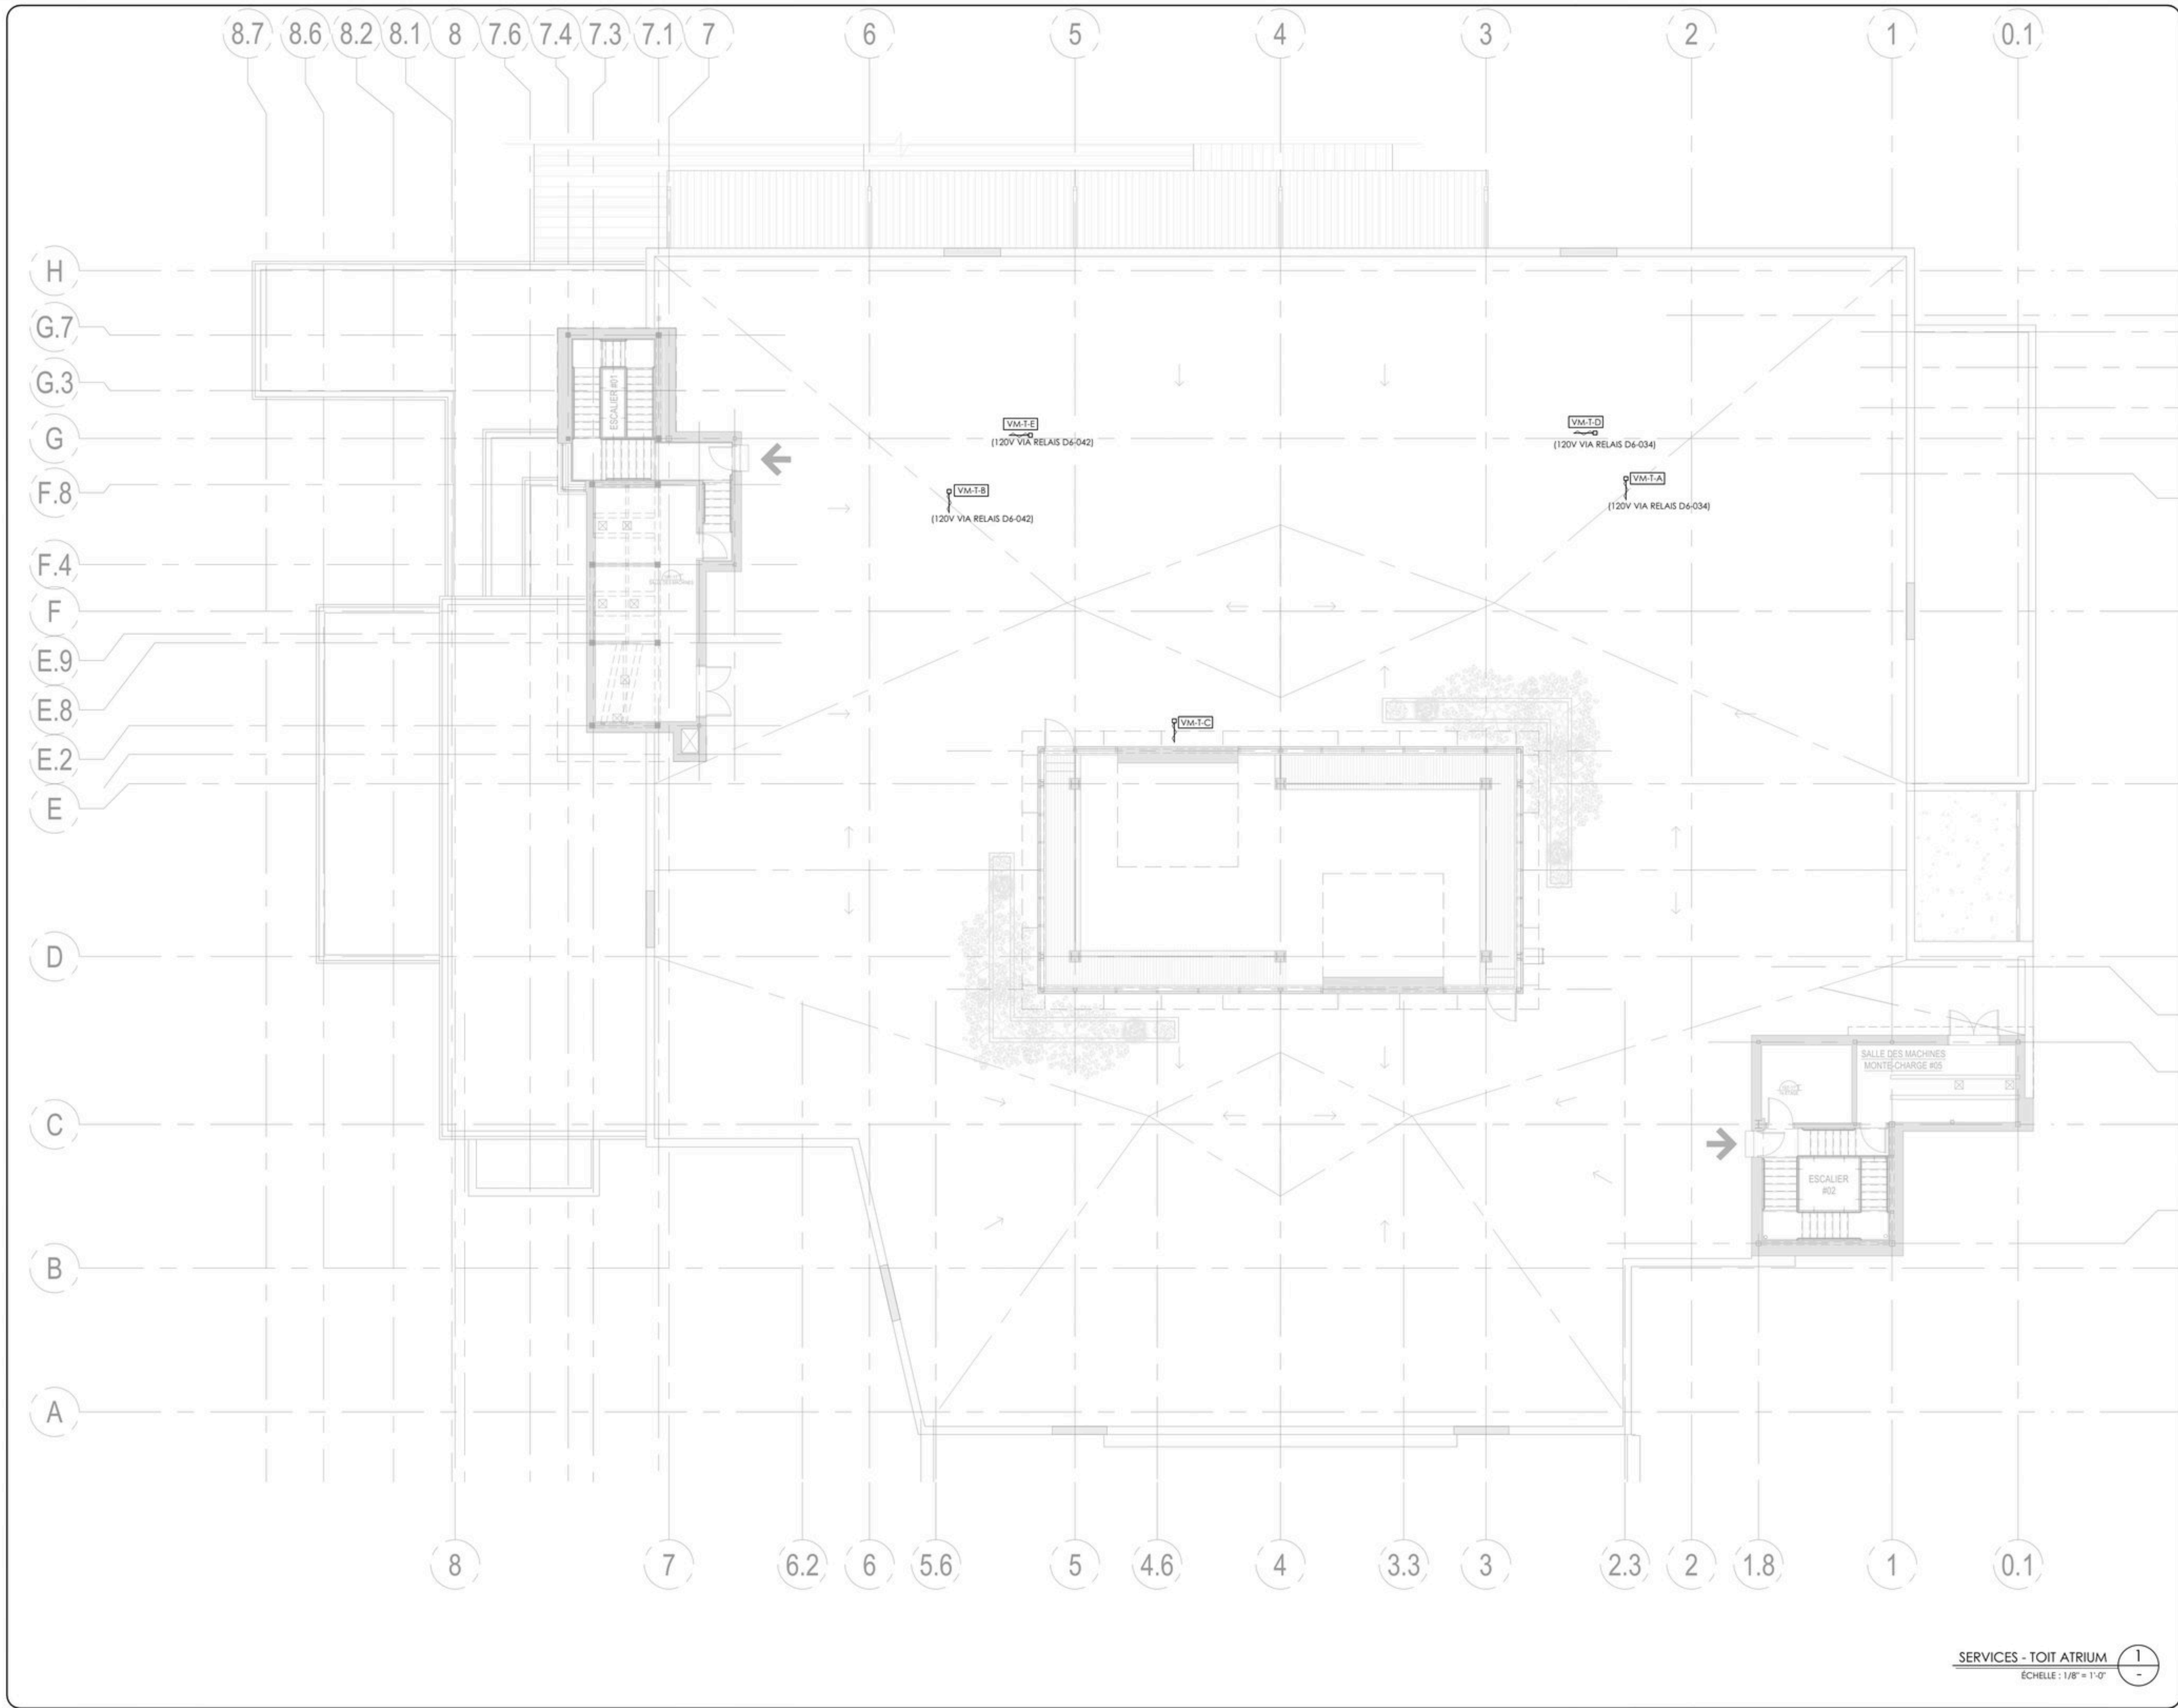

NOTES



NE PAS UTILISER POUR CONSTRUCTION			
2	20-02-26	APPEL D'OFFRES RÉVISION 1	M.S.
1	24-09-25	ADDENDA ME-01	M.S.
0	17-07-25	APPEL D'OFFRES	M.S.
NO.	J - M - A	DESCRIPTION	PAR



PLAYGROUND POKER

PLAYGROUND HOTEL,
1 500 QC-138 C, KAHNAWAKE,
QC, J0L 1B0

ÉLECTRICITÉ	
ALARME-INCENDIE TOIT ATRIUM	
PRÉPARÉ PAR: G. BLONDIN	TEL QU'INDIQUÉ
NO DE PROJET: 2024-023	PLANCHE NO: E-803