


Droit d'auteur

L'entrepreneur doit vérifier toutes les dimensions et en assumer la responsabilité. Prière de ne pas modifier les échelles de dimensions des plans/dessins transmis - toute erreur ou omission doit être rapportée à Stantec sans délai. Les droits d'auteur des plans et dessins demeurent la propriété de Stantec. Toute reproduction ou utilisation pour tout autre motif que celui autorisé par Stantec est strictement interdite.

Notes

Plan c

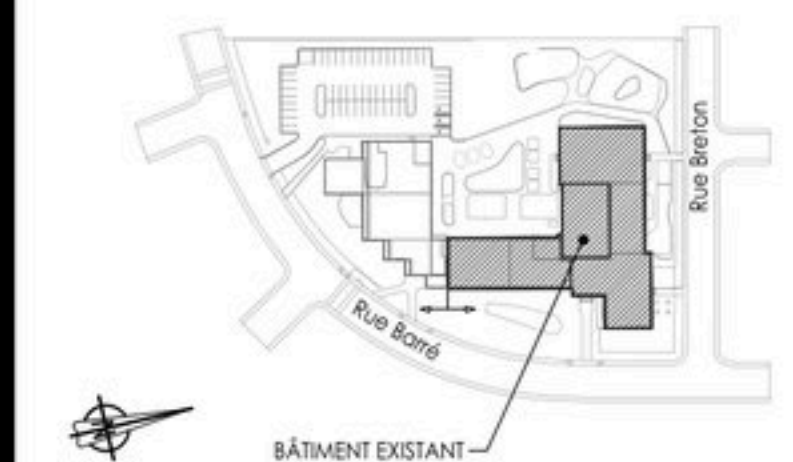

Archit



HÉLOÏSE
THIBODEAU
ARCHITECTE

- INC

360, avenue
McGill 175
T 514-333-
Strath et civil

1) **gbi**

Paysaiste

agence **RELIEFDESIGN**

ELIEFDESIGN

CE DOCUMENT NE DOIT
PAS ÊTRE UTILISÉ À DES FINS

PAS ÊTRE UTILISÉ À DES FINS
DE CONSTRUCTION

D'OFFRES	C.8.	C.5.	2026.06.
révisions	Par	Appr.	AAAA.MM.

103764-300-300-EL-D-101_102_IMP.DWG 2024.04
AAAA.M

our.ing.	Carl Blanchard
	Dessiné

our, ing.	Simon Pelletier, ing.
	Chargé de projet

John St-Amour

0035028
QUÉBEC

026-06-15
/Projet

Dynamilis

Commission scolaire Riverside

† *MISSION ScolaIRE DIVERsIDe (MSD)*

WILLIAM LATTER

DISSEMENT ET RÉAMÉNAGEMENT

Paré, Chambly, QC, J3L 2V4

ENTATION - EXISTANT
NCHEMENT PROVISOIRE

Échelle	
INDIQUÉE	

Feuille
02 de 32

21701

NOTES SPÉCIFIQUES :


- ① IMPLANTATION DES POTEAUX PROVISOIRES À COORDONNER AVEC LES DIVISIONS CIVIL ET PAYSAGISTE.
- ② CÂBLE POSÉ SUR SUPPORTS AU TOIT, À COORDONNER AVEC L'ARCHITECTE.
- ③ INSTALLER UN NÂT DE BRANCHEMENT PROVISOIRE DE TYPE CORNIÈRE SUR LE MUR EXTÉRIEUR POUR LA DESCENTE DU CÂBLE VERS LA SALLE ÉLECTRIQUE. SE RÉFÉRER À L'ILLUSTRATION 2.02 DE LA NORME E.21-10 D'ORTHO-QUÉBEC. À ENLEVER APRÈS LA MISE EN SERVICE DU RACCORDEMENT DÉFINITIF.

Légende — EL101 (4 marques)

- ▼ Démolition poteau client existant (1)
- Mât branchement provisoire (1)
- Poteau branchement provisoire (2)

EXTRAIT DE L'IMPLANTATION – EXISTANT
Echelle: 1:200m

ÉCHELLE: 1:200m

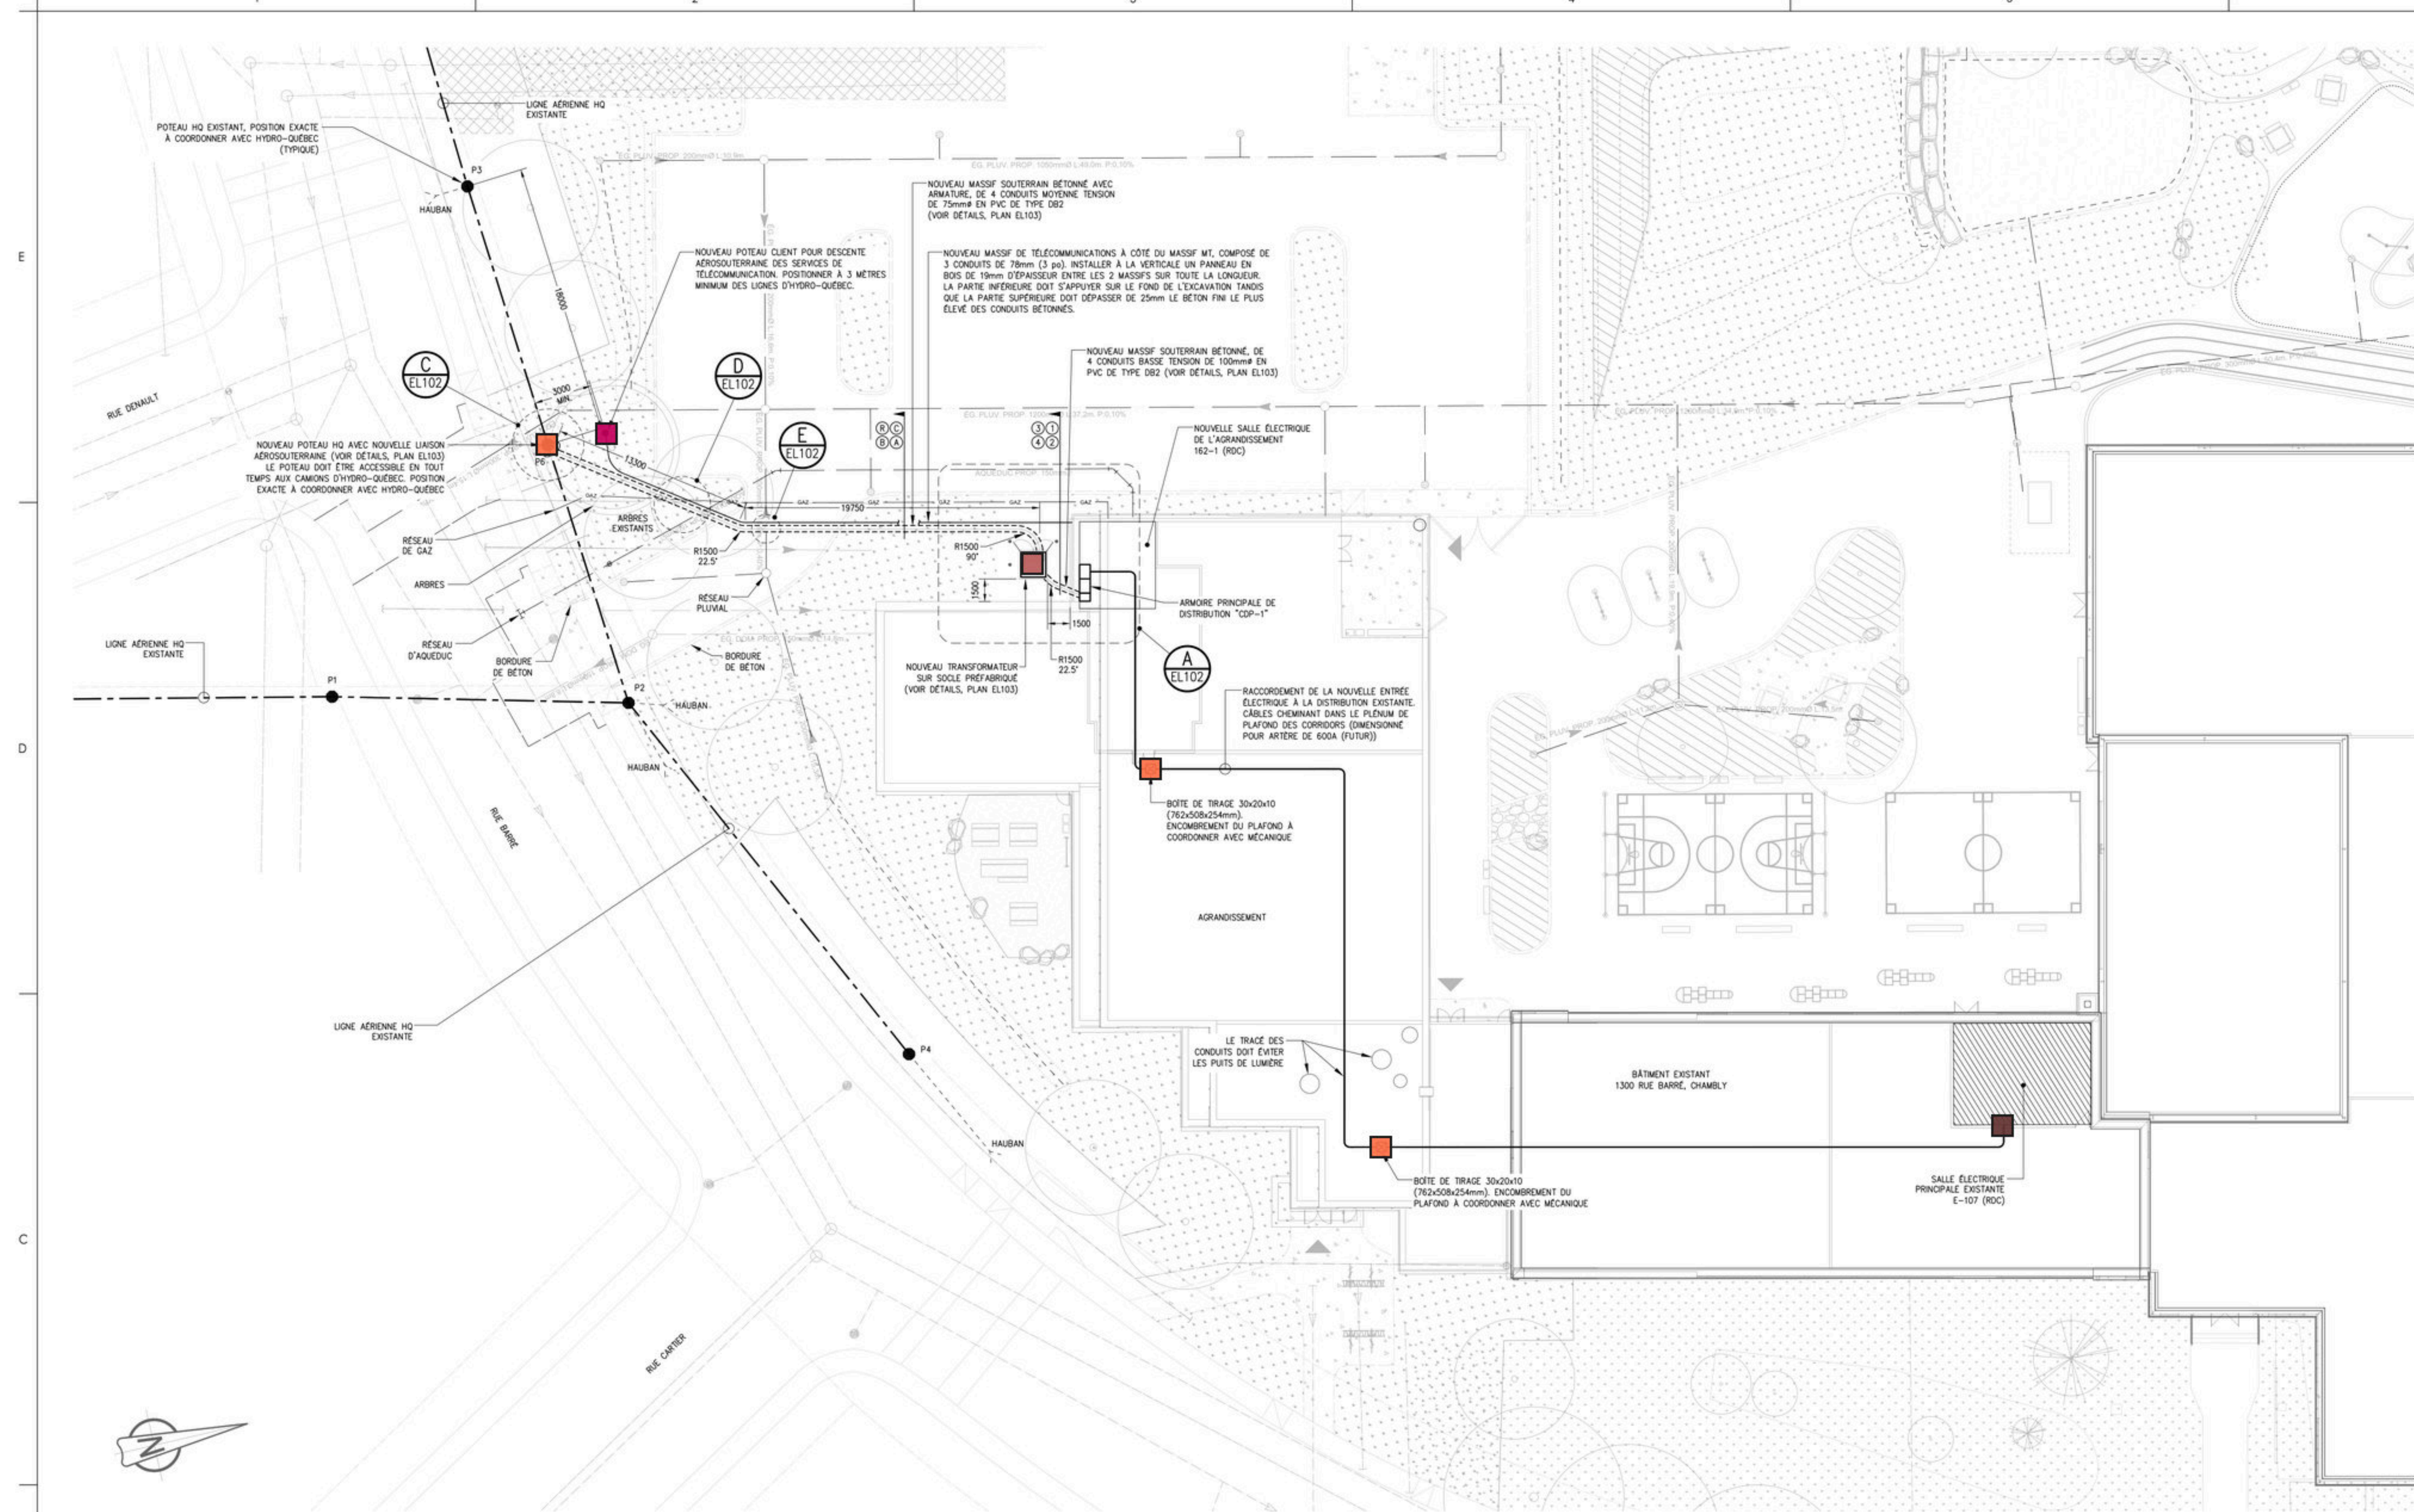

- NOTES GÉNÉRALES :**
- L'ENTREPRENEUR DOIT OUVRIER LES DEMANDES REQUISES POUR LE BRANCHEMENT AVEC LE NUMÉRO DE RÉFÉRENCE HYDRO-QUÉBEC SUIVANT : 03-248843 / RÉSEAU : 61945097.
 - TOUTS LES TRAVAUX DEVONT ÊTRE EXÉCUTÉS SELON LES NORMES DU LIVRE VERT D'HYDRO-QUÉBEC, É.21.11 EN VIGUEUR, INCLUANT LES ADDENDAS.
 - L'ENTREPRENEUR DOIT PRÉSENTER AVANT LE DÉBUT DES TRAVAUX UN PLAN SÛR ET SCÉLÉ PAR UN INGÉNIEUR MEMBRE DE L'ORDRE POUR UN SUPPORT DE SOUTÈNEMENT DE POTEAU ADAPTE À LA SITUATION (RÉFÉRENCE : NORME É.21-11, ARTICLE 7.2.3).
 - L'ENTREPRENEUR EST RESPONSABLE DE POSITIONNER LES STRUCTURES SOUTERRAINES AUX BONS ENDOITS ET AUX ÉLEVATIONS REQUISES. LE NIVEAU DU SOL DOIT ÊTRE FINAL AU MOMENT DE L'IMPLANTATION DU POTEAU. LE SOL DOIT ÊTRE DE NIVEAU, SUR UN RAYON DE 1500mm TOUT AUTOUR DU POTEAU.
 - LE CLIENT CHOISIT CONCOMITAMMENT AVEC HYDRO-QUÉBEC L'EMPLACEMENT DU POSTE DISTRIBUTEUR ET SA VOIE D'ACCÈS. LA CONCEPTION DE LA VOIE D'ACCÈS, Y COMPRIS LA CAPOTE PORTANTE ET LES MATÉRIAUX UTILISÉS DE MÊME QUE TOUT CHANGEMENT ULTÉRIEUREMENT APORTE À SON AMÉNAGEMENT, DOIT ÊTRE ACCEPTÉE PAR HYDRO-QUÉBEC. DE PLUS, CETTE VOIE D'ACCÈS DOIT ÊTRE ENVIRONNEMENT EXTERIEURE ET PERMETTRE EN TOUT TEMPS L'ACCÈS AU POSTE PAR FARDER. LA SURFACE DE ROULEMENT DU CHEMIN D'ACCÈS EST GÉNÉRALEMENT DE 3m DE LARGEUR. ELLE NE DOIT JAMAIS ÊTRE INFÉRIEURE À 4m. SI UN CHEMIN D'ACCÈS PLUS LARGE PEUT ÊTRE CONSTRUIT, IL DOIT SUPPORTER SANS PROBLÈME, AVEC UNE PENTE MAXIMUM DE 5% VERS L'EXTÉRIEUR (RÉFÉRENCE : NORME É.21-11, ARTICLES 4.2.8 ET 6.3).
 - L'AMÉNAGEMENT DU TERRAIN ENVIRONNANT DOIT EMPECHER L'EAU DE S'ACCUMULER AUTOUR DU SOCLE (UNE DENVALLÉE DE 5% VERS L'EXTÉRIEUR AUTOUR DU SOCLE) (RÉFÉRENCE : NORME É.21-11, ARTICLE 6.3).
 - LE SOCLE DU TRANSFORMATEUR DOIT ÊTRE PARFAITEMENT DE NIVEAU. LE NIVEAU FINAL DU SOL DOIT ÊTRE DE 100 À 250mm SOUS LE NIVEAU LE PLUS ÉLEVÉ DU SOCLE.
 - SE RÉFÉRER À L'ILLUSTRATION 6.01 (RÉFÉRENCE : NORME É.21-11) POUR LES DÉGAGEMENTS AUTOUR DU SOCLE. IL NE DOIT Y AVOIR AUCUN OUVRAGE AU-DESSUS DU SOCLE (EX. BALCON).
 - LES CONDUCTEURS DU SYSTÈME DE MALT DOIVENT ÊTRE EN CUIR ÉTAMÉ DE CALIBRE 4/0 ANG. À TORONNAGE STANDARD ET POSSEDER 7 BRINS OU PLUS. LES PROJETS DE TORRE DOIVENT ÊTRE EN ACIER COUVRE DE 19mm DE DIAMÈTRE ET DE 3000mm DE LONGUEUR.
 - SAUF INDICATIONS CONTRAIRES, LA CANTRE RÉGULOTÉRIELLE DOIT ÊTRE ENFOUÏE DIRECTEMENT DANS LE SOL, À UNE DISTANCE DE 1m DU SOCLE ET À UNE PROFONDEUR DE 300mm. ELLE DOIT ÊTRE CONTRAÎNTE ET SANS JOINTURE. LES EXTRÉMITÉS DOIVENT SORTIR PAR LES CAVITÉS DU SOCLE ET EXCÉDER D'AU MOINS 1m DE CE DERNIER (RÉFÉRENCE : NORME É.21-11, ARTICLE 6.7.2).
 - TOUTES LES CONNEXIONS DE LA CANTRE D'ÉQUIPOTENTIALITÉ, CONDUCTEUR-CONDUCTEUR ET CONDUCTEUR-POIQUET DOIVENT ÊTRE FAITES PAR SOUDURE ALUMINOTHERMIQUE (RÉFÉRENCE : NORME É.21-11, ARTICLE 4.3.2).
 - LES OUVRAGES MÉTALLIQUES EXISTANTS OU FUTURS, NON SOULÉS DU SOL ET SITUÉS À MOINS DE 3m DU SOCLE DOIVENT ÊTRE RELIÉS À LA CANTRE D'ÉQUIPOTENTIALITÉ (RÉFÉRENCE : NORME É.21-11, ARTICLE 6.7.3).
 - CHACQUE PHASE DOIT ÊTRE IDENTIFIÉE À SON EXTRÉMITÉ DANS LE SOCLE. PRÉVOIR UNE LONGUEUR MINIMALE DE 2m DE CÂBLE AU-DESSUS DU SOCLE (RÉFÉRENCE : NORME É.21-11, ARTICLE 6.4.1).
 - LES CONDUCTEURS BASSE TENSION DOIVENT DÉPASSER DE 2000mm LE DESSUS DU SOCLE.
 - TOUTS LES COUDS VERTICAUX DOIVENT AVOIR 900mm DE RAYON ET TOUTS LES COUDS HORIZONTAUX 1500mm SAUF INDICATIONS CONTRAIRES AU PLAN.
 - TOUT ÉCART DANS LE TRACÉ DES CONDUITES AMENANT DES ANGLES ADDITIONNELS DEVRA ÊTRE SIGNALÉ AU PRÉALABLE AU REPRÉSENTANT D'HYDRO-QUÉBEC.
 - L'ENTREPRENEUR EST RESPONSABLE DE SCÉLER LES CONDUITS AU POINT D'ENTRÉE DANS LE BÂTIMENT AFIN DE PRÉVENIR TOUTE INFILTRATION D'EAU.
 - LE MANDRINAGE DES CONDUITS DOIT SE FAIRE EN PRÉSENCE D'UN REPRÉSENTANT D'HYDRO-QUÉBEC. UNE CAMERA EST À PASSER EN PRÉSENCE D'UN INSPECTEUR D'HYDRO-QUÉBEC (RÉFÉRENCE : NORME É.21-11, ARTICLE 6.8).
 - VÉRIFIER SUR PLACE TOUTES LES DIMENSIONS AVANT DE PROCÉDER AUX TRAVAUX ET RAPPORTER À L'INGÉNIEUR ET À HYDRO-QUÉBEC TOUTE DIVERGENCE SUSCEPTIBLE DE MODIFIER LES PRINCIPES DE CONCEPTION ET DE CONSTRUCTION VOULUS PAR LES PRÉSENTS PLANS.
 - AU MOINS TROIS (3) JOURS OUVRIABLES AVANT LE DÉBUT DES TRAVAUX CIVILS, TRANSMETTRE LA DEMANDE DE SURVEILLANCE DE TRAVAUX CIVILS DONT TEMPS À L'ADRESSE COURRIER, D'HYDRO-QUÉBEC INSCRITE SUR LE FORMULAIRE.

Légende — EL102 (6 marques)

- Boîte de tirage 30x20x10 (2)
- Poteau client télécom (1)
- Poteau liaison aérosouterraine (1)
- Raccordement entrée existante (1)
- Transformateur sur socle (1)


RÉFÉRENCE		LIVRE VERT - NORMES	
CONSTRUCTION D'UN POSTE DISTRIBUTEUR (RÉFÉRENCE : SECTION 6)			
OUVRAGES DE GÉNIE CIVIL (EXCAVATION) (RÉFÉRENCE : SECTION 7, PAGES 55)			
CONFIGURATIONS GÉNÉRALES D'UNE (RÉFÉRENCE : ARTICLE 7.3.3)			
CONFIGURATIONS GÉNÉRALES D'UNE (RÉFÉRENCE : ARTICLE 7.3)			
COUPE LONGITUDINALE (CANALISATION MULTITUBULAIRE) (RÉFÉRENCE : ARTICLE 7.3.3)			
ARRÊT DE CONDUITS (CANALISATION MULTITUBULAIRE) (RÉFÉRENCE : ARTICLE 7.3.7)			
NETTOYAGE ET VÉRIFICATION DES CONDUITS (MANDRINAGE) (RÉFÉRENCE : ARTICLE 7.3.10)			
QUATRE CONDUITS DE 75, 100 OU 115 mm DE DIAMÈTRE SUR UN POTEAU EN BOIS (LIGNE AÉROSOUTERRAINE) (RÉFÉRENCE : ARTICLE 7.4)			
SOCLE POUR TRANSFORMATEUR TRIPHASE (RÉFÉRENCE : ARTICLE 6.5)			
PROTECTION MÉCANIQUE POUR UN TRANSFORMATEUR SUR SOCLE (RÉFÉRENCE : ARTICLE 6.6)			
INSTALLATION DE MISE À LA TERRE POUR UN SOCLE (RÉFÉRENCE : ARTICLES 4.3.2 ET 6.7)			
PROTÈGE-SORTIE DE CANALISATION DE 1420 mm DE LARGEUR (RÉFÉRENCE : ARTICLE 7.4)			
DISTANCES MINIMALES ENTRE LE SOCLE ET LE BÂTIMENT (RÉFÉRENCE : ARTICLE 6.8.1)			
CELLULE DE MESURAGE (POSTE BLINDÉ ET ARMURE POUR TRANSFORMATEURS) (RÉFÉRENCE : LIVRE BLEU - NORME É.21-10, 10e ÉDITION, ARTICLES 8.1 À 8.4)			
		ILLUSTRATION 6.01	-
		ILLUSTRATION 8.01	-

TABLEAU DE MANDRINAGE HYDRO-QUÉBEC						
NO. DE CONDUIT	TENSION	DÉPART	ARRIVÉE	DIAMÈTRE Ø (mm)	LONGUEUR DE MANDRINAGE ESTIMÉE (m)	LONGUEUR DE MANDRINAGE MESURÉE (m)
A	MT	POTEAU #A LAS	TRANSFO #A TSS	75ø	38	-
B	MT	POTEAU #B LAS	TRANSFO #B TSS	75ø	38	-
C	MT	POTEAU #C LAS	TRANSFO #C TSS	75ø	38	-
R	MT	POTEAU #R LAS	TRANSFO #R TSS	75ø	38	-
1	BT	TRANSFO TSS	ENTRÉE ÉLECTRIQUE	100ø	7	-
2	BT	TRANSFO TSS	ENTRÉE ÉLECTRIQUE	100ø	7	-
3	BT	TRANSFO TSS	ENTRÉE ÉLECTRIQUE	100ø	7	-
4	BT	TRANSFO TSS	ENTRÉE ÉLECTRIQUE	100ø	7	-

NOTE : L'ENTREPRENEUR DOIT MESURER TOUTS LES CONDUITS AU CHANTIER ET INSCRIRE LA MESURE DANS LE TABLEAU DANS LES CAS PRÉVUS À CET EFFET.

EXTRAIT DE L'IMPLANTATION - NOUVEAU

ÉCHELLE : 1:200m

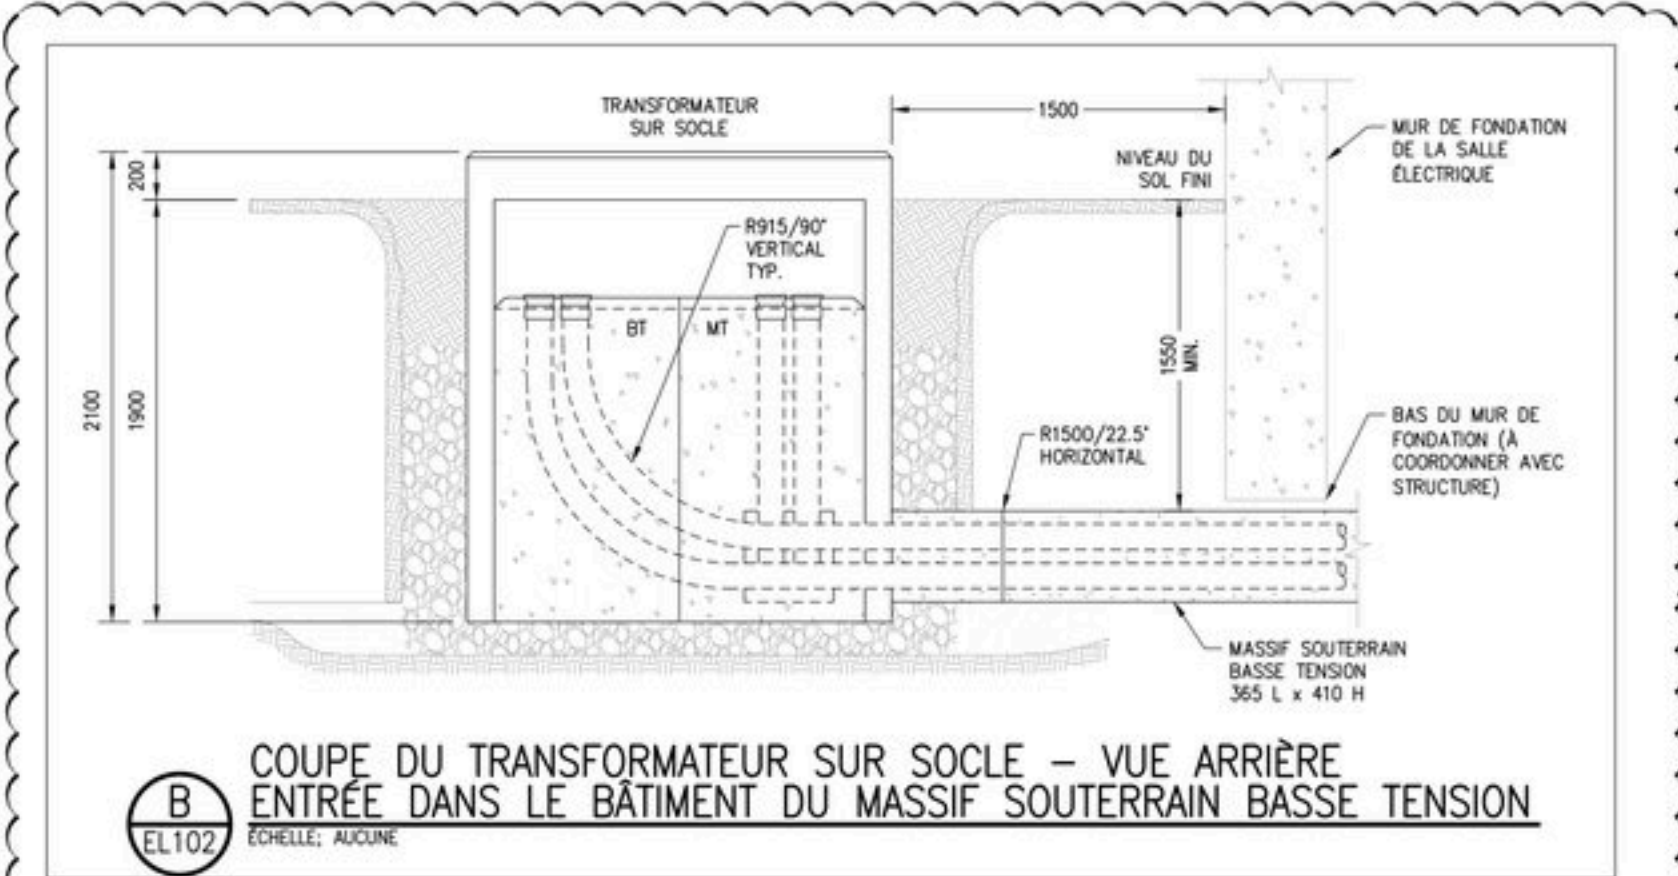

COUPE DU TRANSFORMATEUR SUR SOCLE - VUE ARRIÈRE


ENTRÉE DANS LE BÂTIMENT DU MASSIF SOUTERRAIN BASSE TENSION

ÉCHELLE : AUCUNE




POTEAU DE LIASON AÉROSOUTERRAINE

ÉCHELLE : AUCUNE

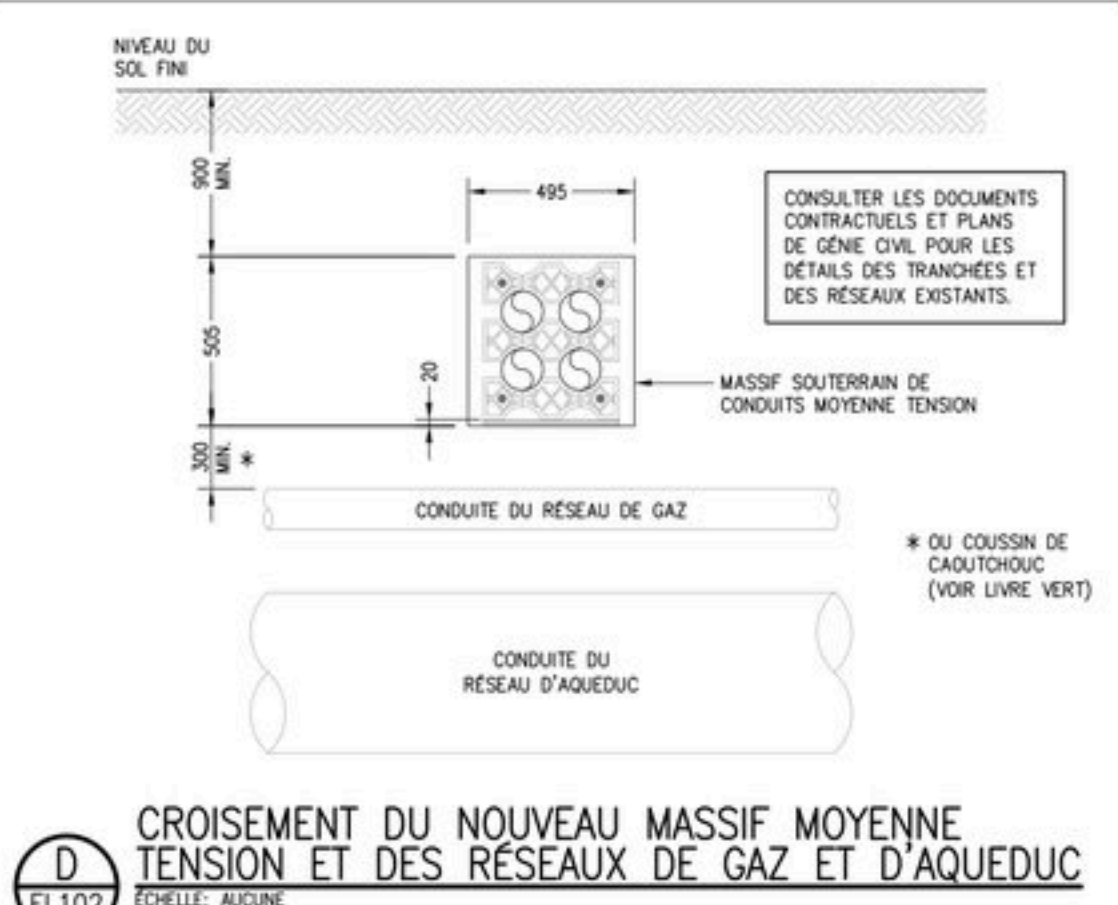


CROISEMENT DU NOUVEAU MASSIF MOYENNE TENSION ET DES RESEAUX DE GAZ ET D'AQUEDUC

ÉCHELLE : AUCUNE

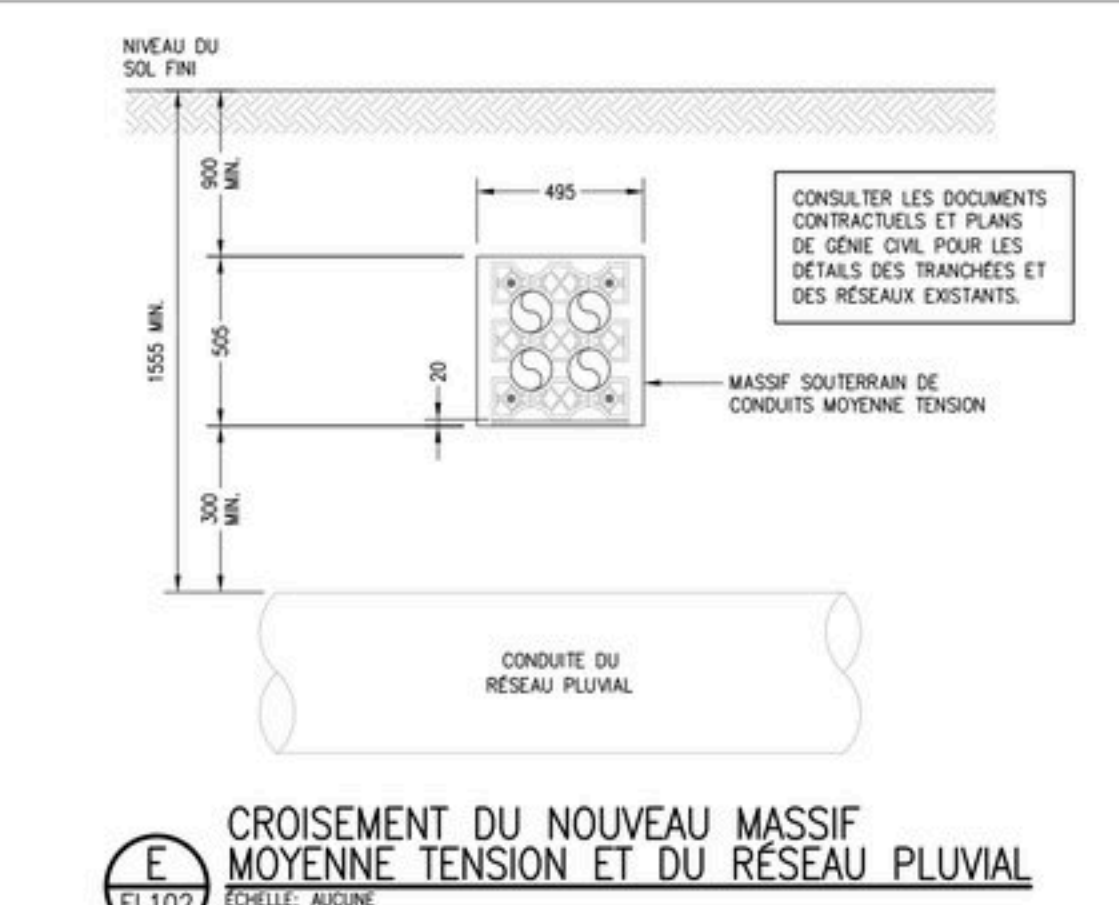

CROISEMENT DU NOUVEAU MASSIF MOYENNE TENSION ET DU RESEAU PLUVIAL

ÉCHELLE : AUCUNE

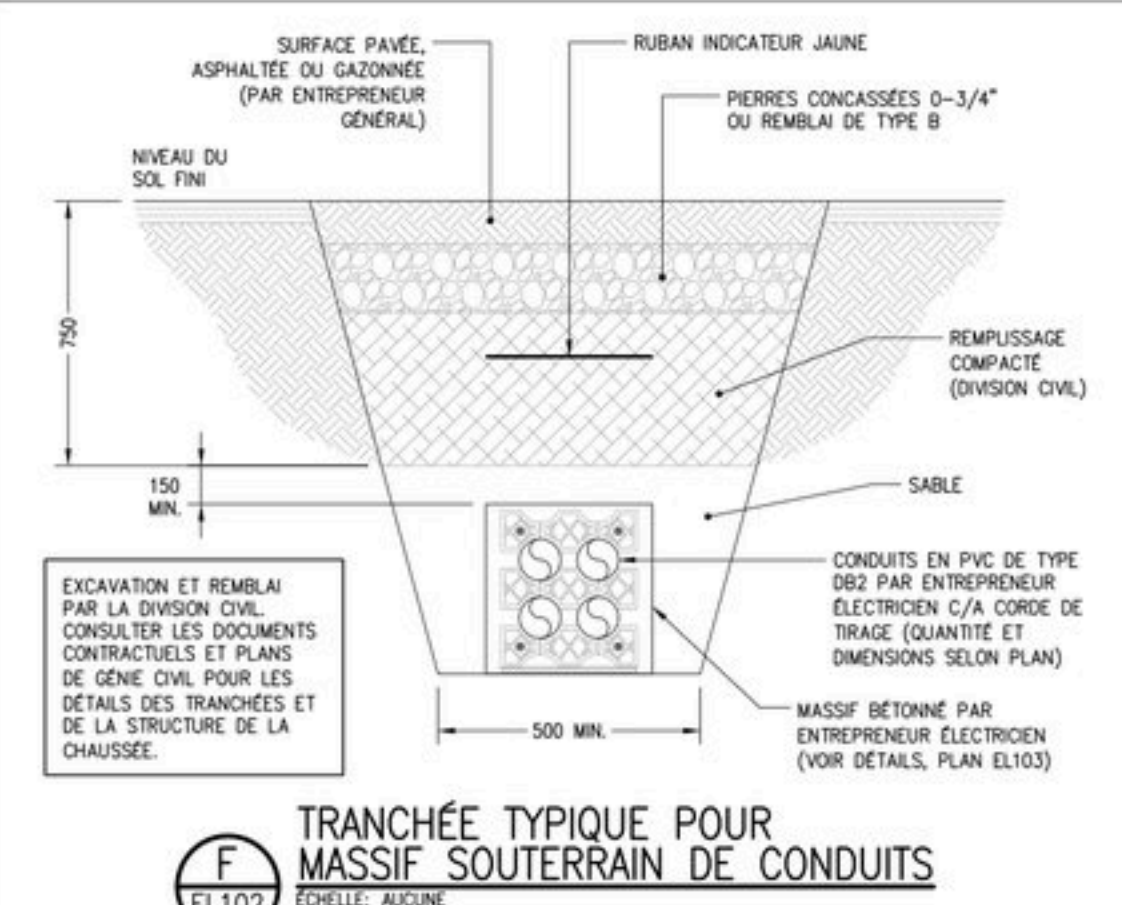

TRANCHÉE TYPIQUE POUR MASSIF SOUTERRAIN DE CONDUITS

ÉCHELLE : AUCUNE




Stantec Experts-conseils Inc.
375, boul. Roland-Thérien, bureau 400
Longueuil (Québec) J4H 4A6
Tél. 514.281.1010
www.stantec.com

Droit d'auteur
L'entrepreneur doit vérifier toutes les dimensions et en assumer la responsabilité. Prière de ne pas modifier les échelles de dimensions des plans/dessins/traçés. Toute erreur ou omission doit être rapportée à Stantec sans délai. Les droits d'auteur des plans et dessins demeurent la propriété de Stantec. Toute reproduction ou utilisation pour tout autre motif autre que celui autorisé par Stantec est strictement interdite.

Notes

Plan clé

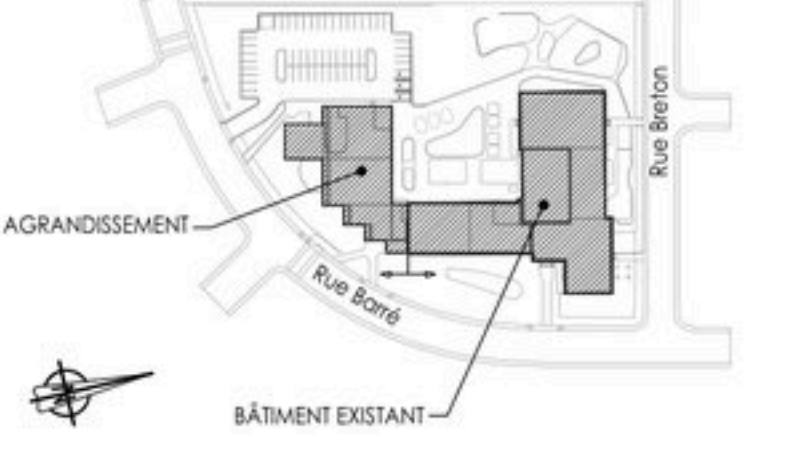

Architecte

HÉLOÏSE THIBODEAU ARCHITECTE
115, rue Saint-Jacques, 10e étage
Montréal, Québec H2Y 1K1
Tél. 514.392.1001

Structure et civil



Logistique



CE DOCUMENT NE DOIT PAS ÊTRE UTILISÉ À DES FINS DE CONSTRUCTION

1	POUR ADDENDA N° 1	C.B.	C.S.	2020.04.26
0	POUR APPEL D'OFFRES	C.B.	C.S.	2020.06.15
Émissions/Révisions		Par	Appr.	AAAA-MM-JJ
Nom fichier : 157103764-300-300-EL-0101_102_AJP-DWG		2020.04.02		
		AAAA-MM-JJ		

Châteaigu St-Amour, ing.	Carl Blanchard
Prépare	Dessiné
Châteaigu St-Amour, ing.	Simon Pellerin, ing.
Vérifie	Chargé de projet

Secours



2020-06-26
Logo Client/Projet

Client/Projet
COMMISSION SCOLAIRE RIVERSIDE (CSR)
ÉCOLE WILLIAM LATTEUR
AGRANDISSEMENT ET RÉAMÉNAGEMENT

1300 rue Barré, Chambly, QC, J3L 2V4

Titre
ÉLECTRICITÉ
IMPLANTATION
NOUVEAU

N° Projet
157103764
Échelle
INDIQUÉE
Émis/Rév. Feuille
1 03 de 32
N° dessin
EL102



NOTES GÉNÉRALES :

- SAUF INDICATION CONTRAIRE, TOUT APPAREILLAGE REPRÉSENTÉ EN TRACÉ CONTINU SUR CE PLAN EST NOUVEAU, EXISTANT MODIFIÉ OU EXISTANT DÉPLACÉ. SE RÉFÉRER AUX INDICES POUR DES DÉTAILS SUR LA NATURE DES TRAVAUX.
- AUCUN PÉRECEMENT N'EST PERMIS DANS LES MURS DES ESCALIERS À MOINS QUE CELA NE DESERVE LES ESCALIERS.
- SE RÉFÉRER AUX PLANS DES SCHÉMAS DE CONTRÔLE D'ÉCLAIRAGE POUR LES DÉTAILS D'INSTALLATION.

NOTES SPÉCIFIQUES :

- BORNE DE RECHARGE DE NIVEAU 2. MODÈLE DE RÉFÉRENCE: CORE+ DE PLO/ADNÉRIQUE, COMPRIS AVEC PASSERELLE DE COMMUNICATION (VOIR DÉTAILS).
- PASSERELLE DE COMMUNICATION À INSTALLER À MOINS DE 50 MÈTRES DES BORNES. FOURNIR ET INSTALLER UN BOÎTIER DE 12 x 12 COMPLÈTEMENT ÉTANCHE.
- LUMINAIRE SUR POTEAU C/A DÉTECTEUR DE MOUVEMENT. RÉDUCTION AUTOMATIQUE DE L'INTENSITÉ LUMINEUSE DE 50% PENDANT LA PLAGE HORAIRE COMPRISE ENTRE MINUIT ET 6 HEURES DU MATIN (00h-06h). LE TOUT DÔTÊTRE PAR UNE MANUTÈRE DOTÉE D'UNE HORLOGE ASTRONOMIQUE. SE RÉFÉRER AU SCHÉMA DE DISTRIBUTION POUR LA CIRCUITERIE.
- LUMINAIRE ARCHITECTURAL COMMANDÉ PAR UNE MANUTÈRE DOTÉE D'UNE HORLOGE ASTRONOMIQUE ET CELLULE PHOTOÉLECTRIQUE QUI L'ÉTEINDRA DE MANIÈRE AUTOMATIQUE POUR LA PÉRIODE COMMENÇANT À MINUIT (OU À LA FERMETURE DU BÂTIMENT) ET FINISSANT AU PLUS TÔT À 6 HEURES DU MATIN (OU À L'HEURE D'OUVERTURE DU BÂTIMENT). HAUTEUR D'INSTALLATION À COORDONNER AVEC L'ARCHITECTE. SE RÉFÉRER AU PLAN EL305 POUR LA POSITION EXACTE DU LUMINAIRE.

Légende — EL104 (17 marques)

- Bollard protection (6)
- Borne recharge VE double (3)
- Luminaire M (3)
- Luminaire P1 (2)
- Luminaire P2 (2)
- Passerelle communication bornes (1)

CE DOCUMENT NE DOIT PAS ÊTRE UTILISÉ À DES FINS DE CONSTRUCTION

0	POUR APPEL D'OFFRES	C.B.	C.S.	2024.06.15
1	Émissions/Révisions	Par	Appr.	AAAAA.MMM.JJ
Nom fichier: 157103764.300.300-EL-01-04_EXT.DWG				
2024.04.02				
AAAAA.MMM.JJ				
Châteaigu St-Amour, ing.	Car Blanchard			
Préparé	Designé			
Châteaigu St-Amour, ing.	Simon Pellerin, ing.			
Vérifié	Chargé de projet			



Logo Client/Projet



Client/Projet
COMMISSION SCOLAIRE RIVERSIDE (CSR)
ÉCOLE WILLIAM LATTEUR
AGRANDISSEMENT ET RÉAMÉNAGEMENT

1300 rue Barré, Chambly, QC, J3L 2V4







Titre
ÉLECTRICITÉ
EXTÉRIEUR
ÉCLAIRAGE ET SERVICES

N° Projet
157103764

Échelle
1:200

Émis./Rév. Feuille
0 05 de 32

EL104

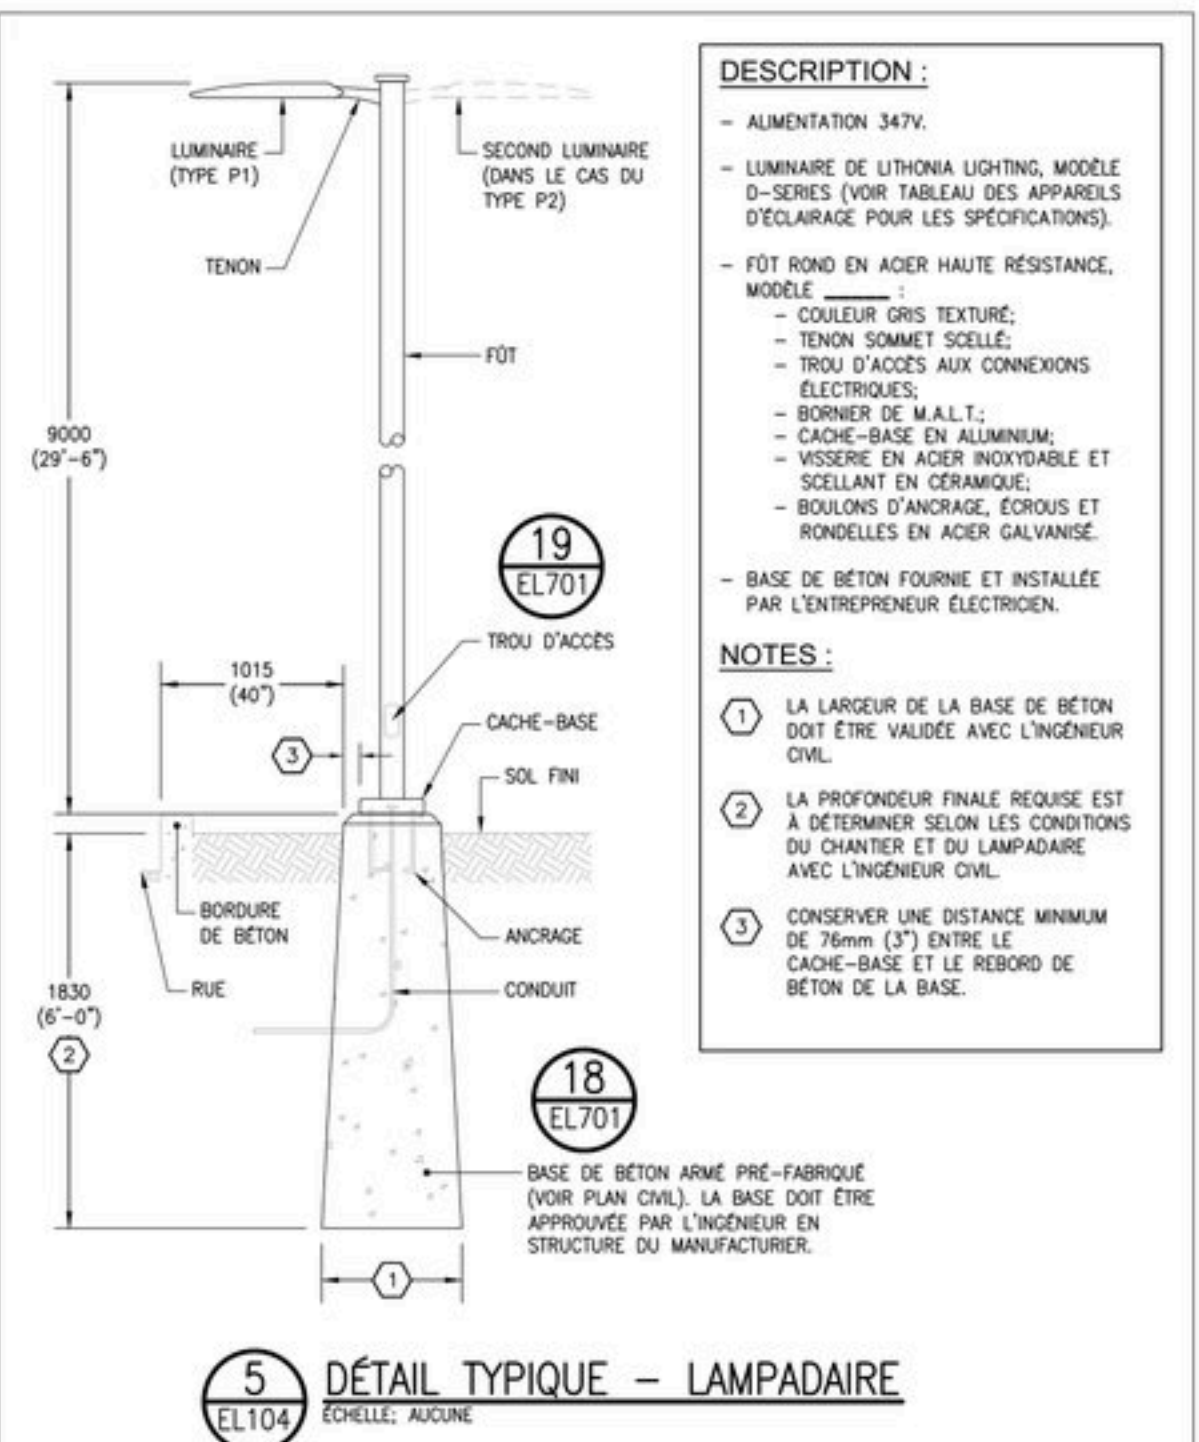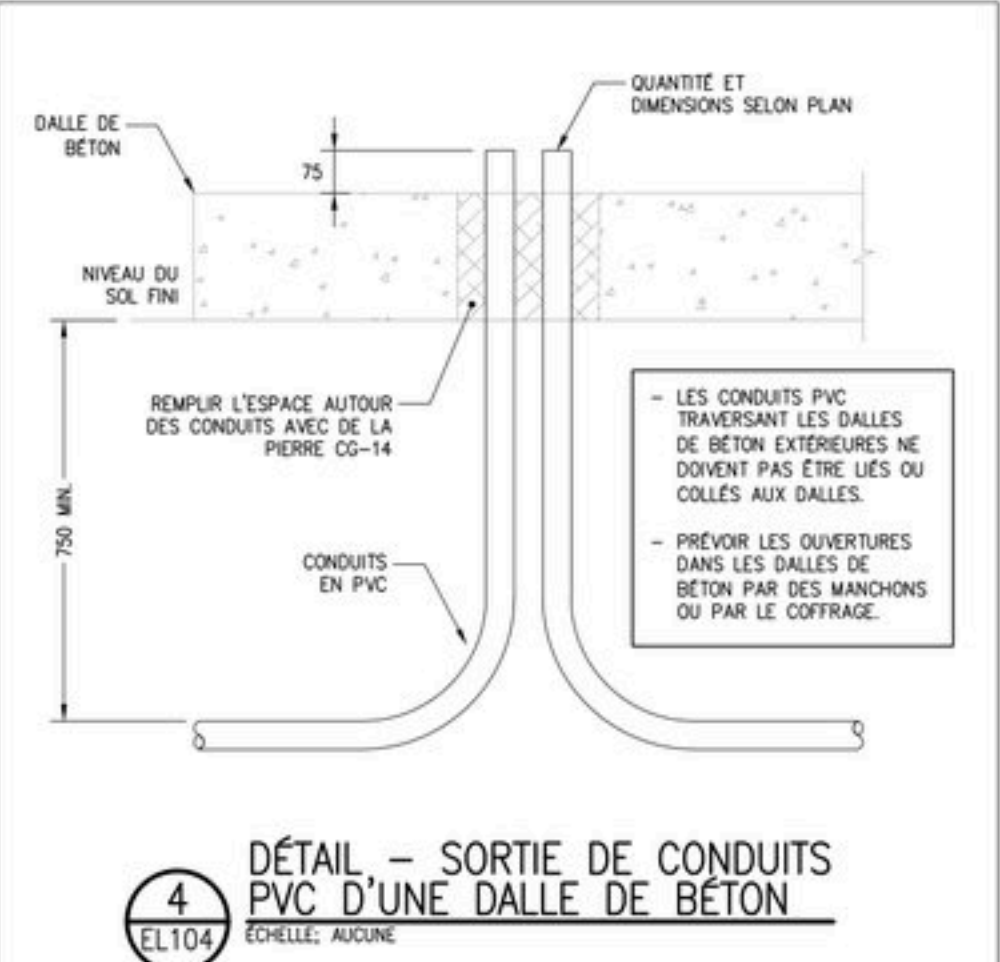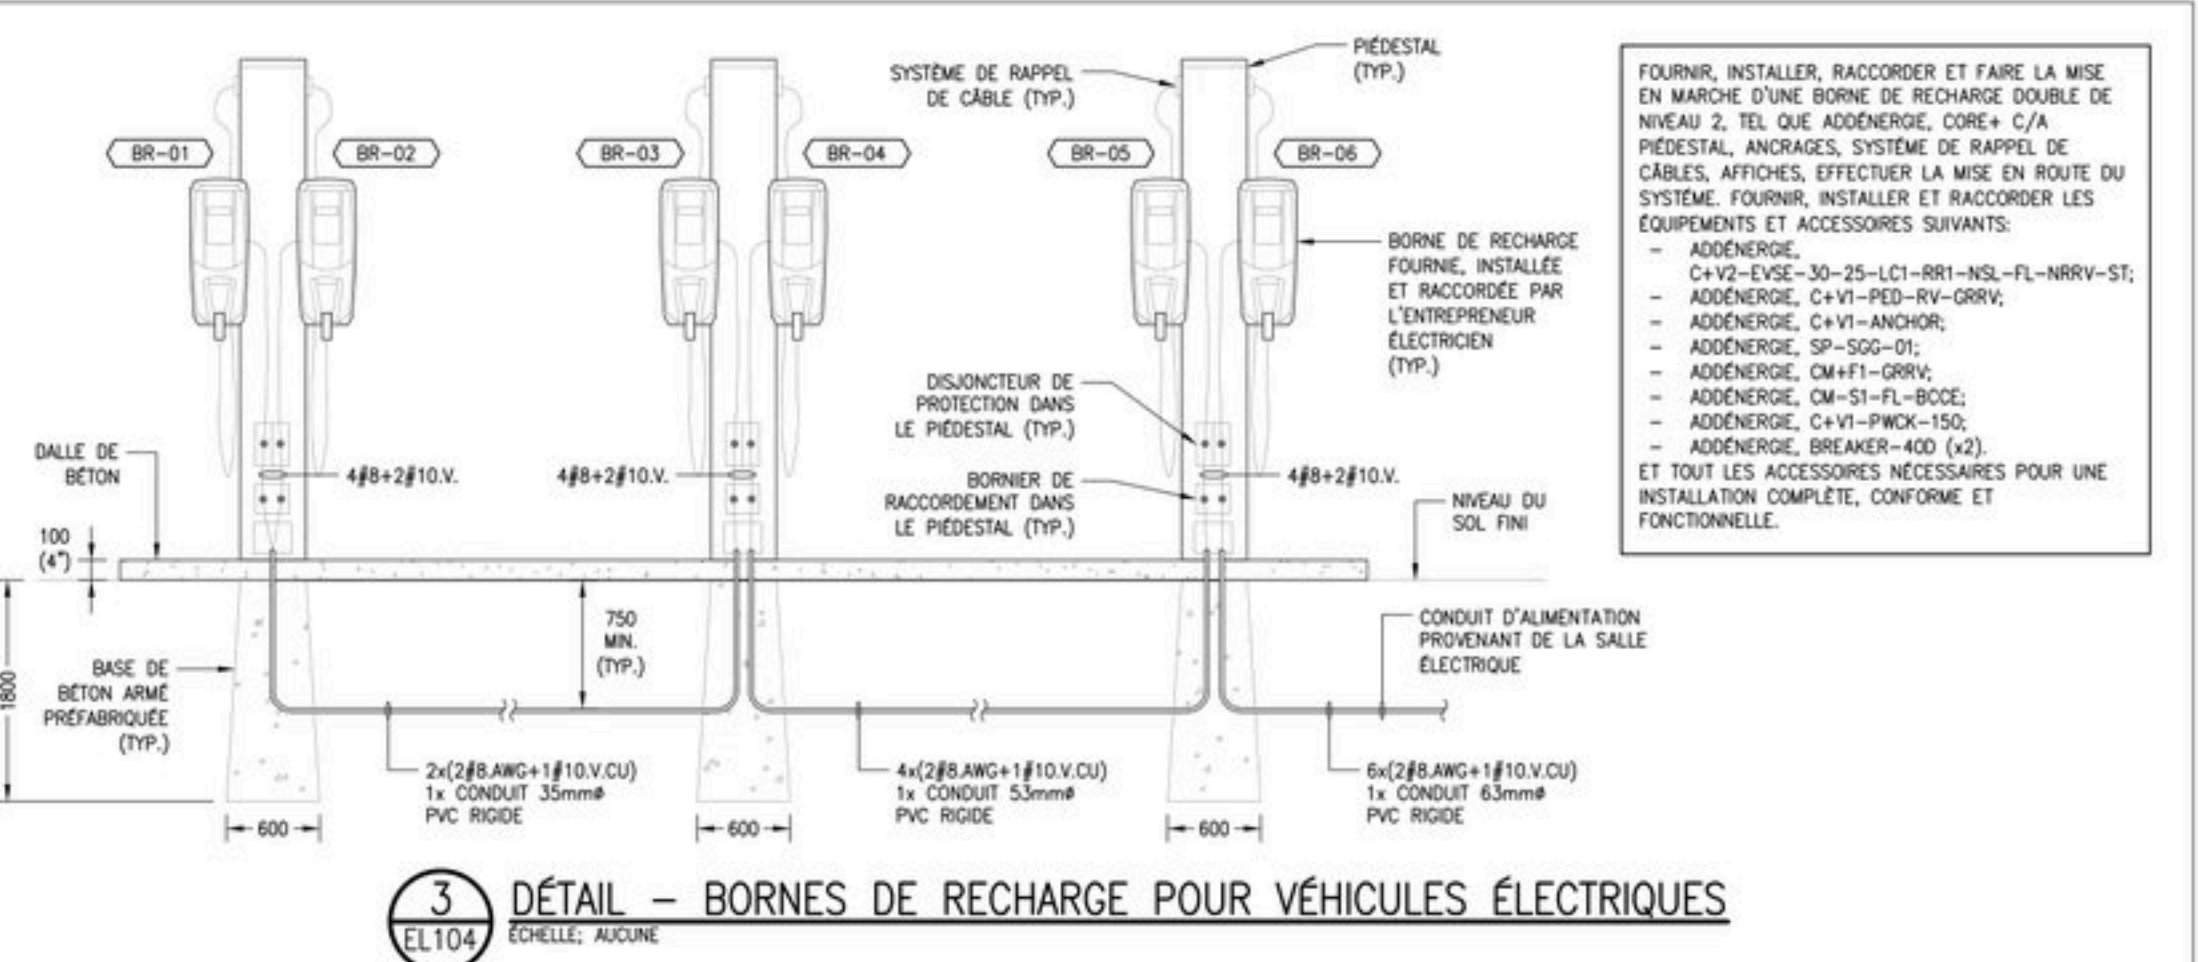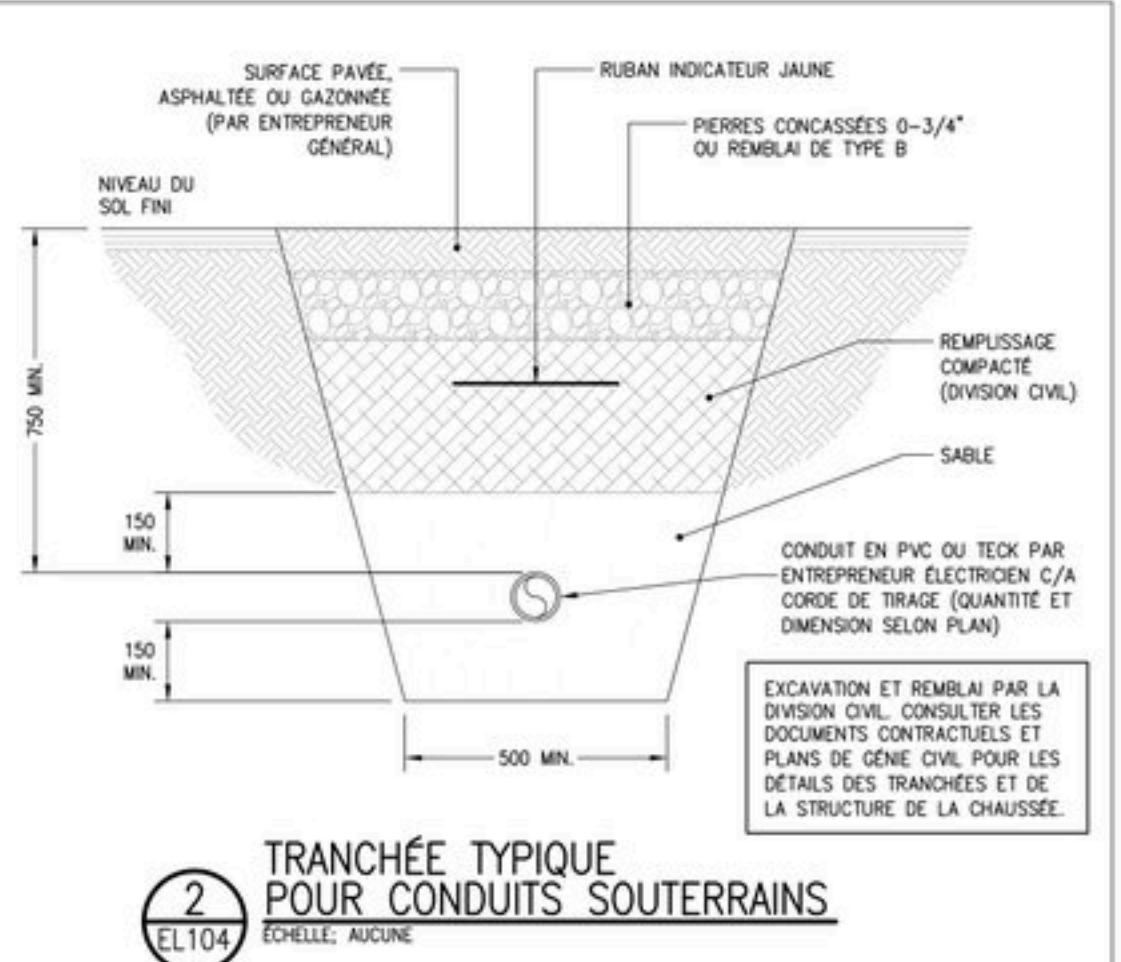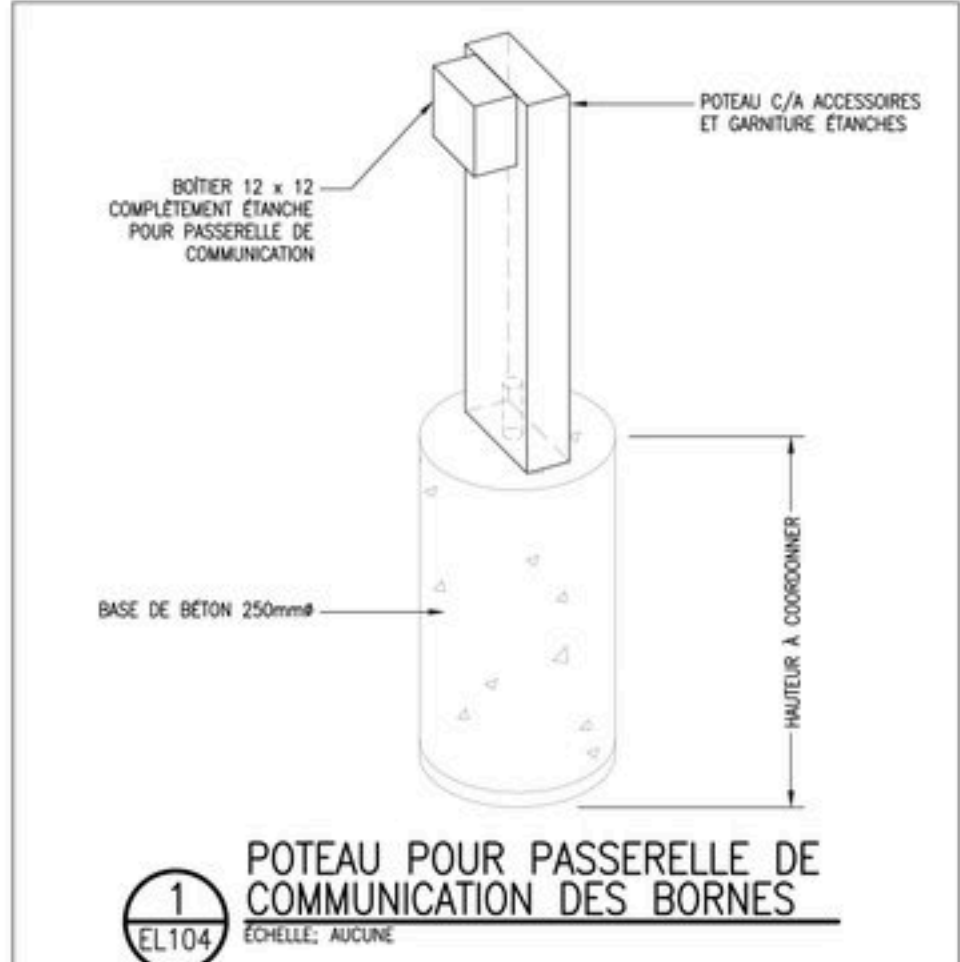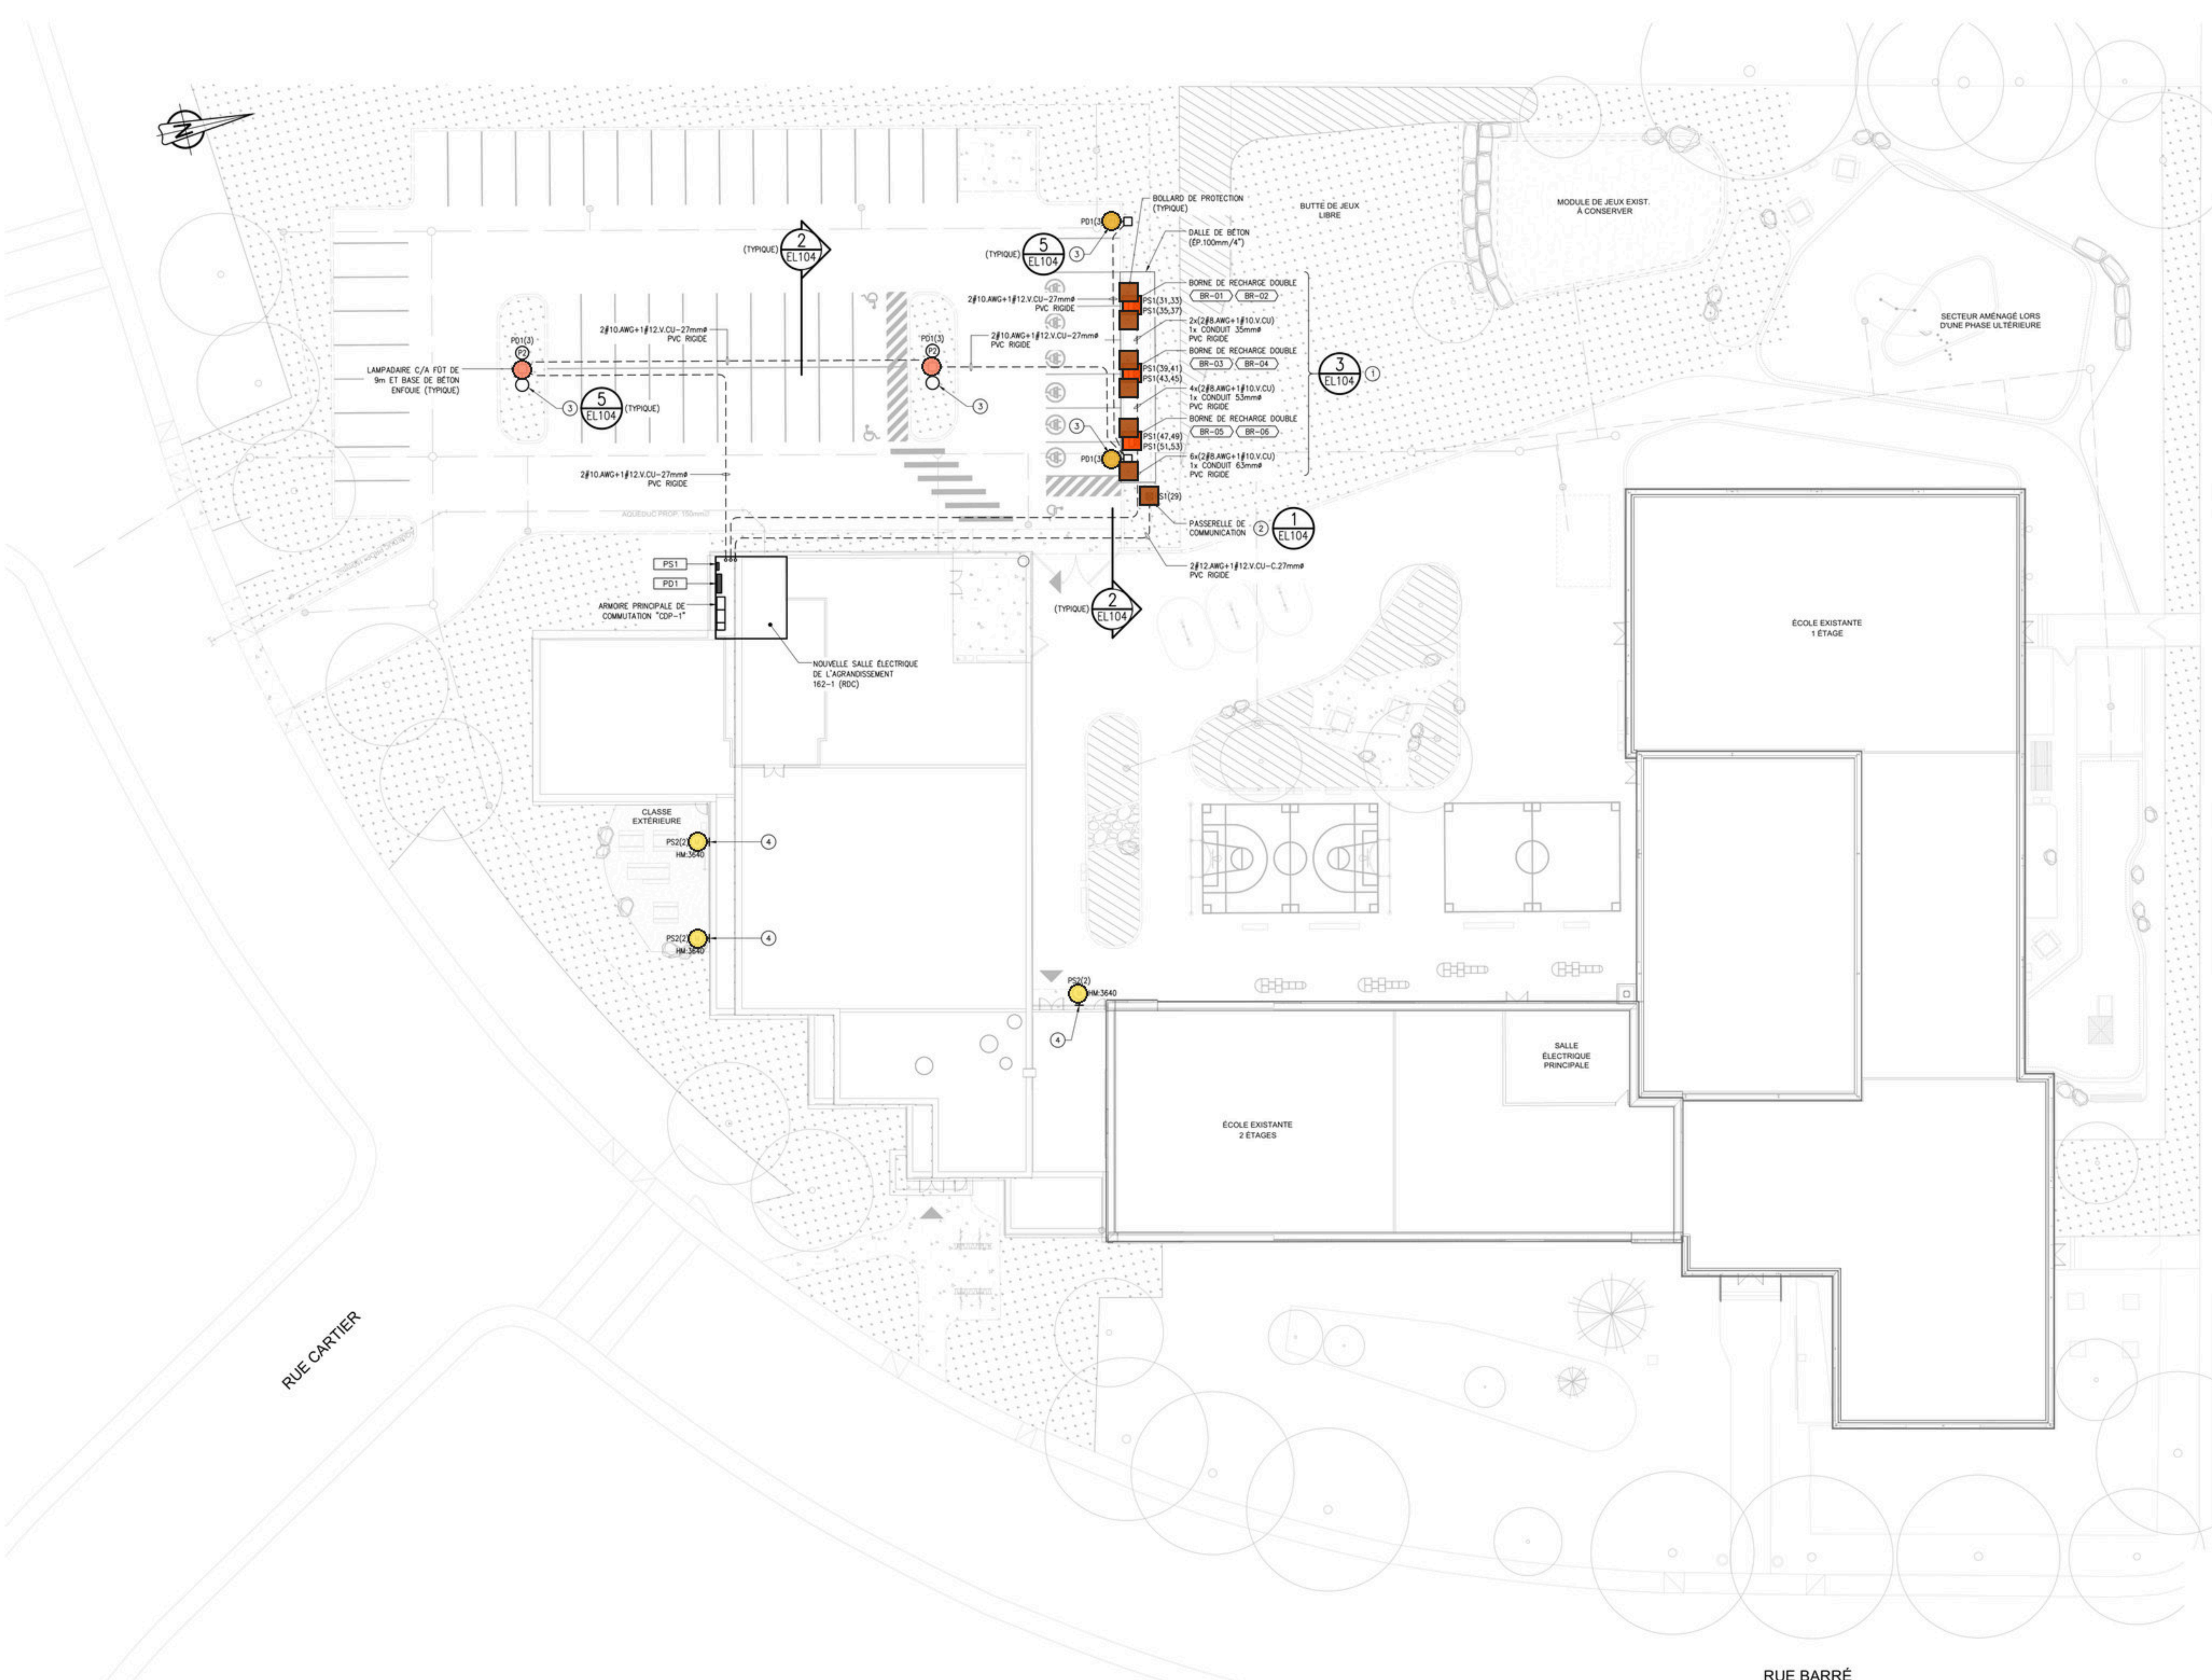

DESCRIPTION :

- ALIMENTATION 347V.
- LUMINAIRE DE LITHONIA LIGHTING, MODÈLE 0-SERIES (VOIR TABLEAU DES APPARELS D'ÉCLAIRAGE POUR LES SPÉCIFICATIONS).
- FÔT ROND EN AÇIER HAUTE RÉSISTANCE, MODÈLE :
- COULEUR GRIS TEXTURE;
- TENDU SANS TÊTE;
- TROU D'ACCÈS AUX CONNEXIONS ÉLECTRIQUES;
- BORNIER DE M.A.L.T.;
- CACHE-BASE EN ALUMINIUM;
- VISSERIE EN AÇIER INOXYDABLE ET SCELLANT EN CÉRAMIQUE;
- BOLLETS D'ANCRAGE, CROUS ET RONDELLES EN AÇIER GALVANISÉ;
- BASE DE BÉTON FOURNIE ET INSTALLÉE PAR L'ENTREPRENEUR ÉLECTRIQUE.

NOTES :

- LA LARGEUR DE LA BASE DE BÉTON DOIT ÊTRE VALIDÉE AVEC L'INGÉNIEUR CIVIL.
- LA PROFONDEUR FINALE REQUISE EST À DÉTERMINER SELON LES CONDITIONS DU QUANTIFIER ET DU LAMPADAIRE AVEC L'INGÉNIEUR CIVIL.
- CONSERVER UNE DISTANCE MINIMUM DE 76mm (3") ENTRE LE CACHE-BASE ET LE REBORD DE BÉTON DE LA BASE.

E



D

C

B

A

Calcul du branchement principal				
Basé sur le Code de construction - Chapitre V - Électricité 2018, article 9-204				
Puissance appelée bâtiment existant (facture Hydro février 2022)	Facteur de demande	W/m²	Superficie (m²)	Puissance (kW)
Superficie du bâtiment (existent et extension)			4926	48700
Charge de base des salles de classes - selon article 9-204, paragraphe 1-a)				
Salles de classe niveau 1 (bâtiment existant)	50		1 995	49 490
Salles de classe niveau 1 (extension du bâtiment)	50	0	0	0
Salles de classe niveau 2 (bâtiment existant)	50		486,8	24 340
Salles de classe niveau 2 (extension du bâtiment)	50		658,7	21 655
Charge de base du reste du bâtiment - selon article 9-204, paragraphe 1-b)				
Reste du bâtiment existant (niveau 1 et 2)	10		1390,4	15 904
Reste de l'extension du bâtiment (niveau 1 et 2)	10		1423,3	14 233
Charge de base totale du bâtiment (nouveau et existant)				
Chauffage électrique (généralisé aérothermique) - Extension				31 000
Chauffage électrique (généralisé aérothermique) - Existant (réaménagé)				9 400
Chauffage électrique - Existant non réaménagé (provision pour futur)				125 000
Serpentins électriques				105 000
Pompes				23 779
Chauffe-eau				24 000
Unité d'eau fra				28 200
Pompe refroidisseur liquide				9 500
Thermopompe eau/air				36 965
Thermopompe VHV				21 655
Ventilation mécanique				1 872
Climatisation (VRF)				260 000
Ventilateurs d'alimentation				56 118
Ventilateurs d'évacuation				9 353
Humidificateurs				21 600
Tableaux de contrôle				1 000
Ascenseur (300)				4 053
Bornes de recharge pour VE				39 956
Charges totales de chauffage	100%			528 621
Total des autres charges (incluant chauffage et climatisation)	100%			199 401
Total des charges de chauffage (selon article 9-204, paragraphe 2-b, i)	75%			396 466
Charge nominale par mètre carré (autres charges excluant chauffage et clim)				
Charges des 300 premiers m² (selon article 9-204, paragraphe 2-b, ii-A)	75%			84561
Charges des 4926 m² restants (selon article 9-204, paragraphe 2-b, ii-B)	50%			132890
Puissance demandée (kW)				
Puissance totale demandée (incluant 10% de charges futures)				623 kW
Transformateur TSS type 1 de 750 kVA (lire vert HQ)				685 A

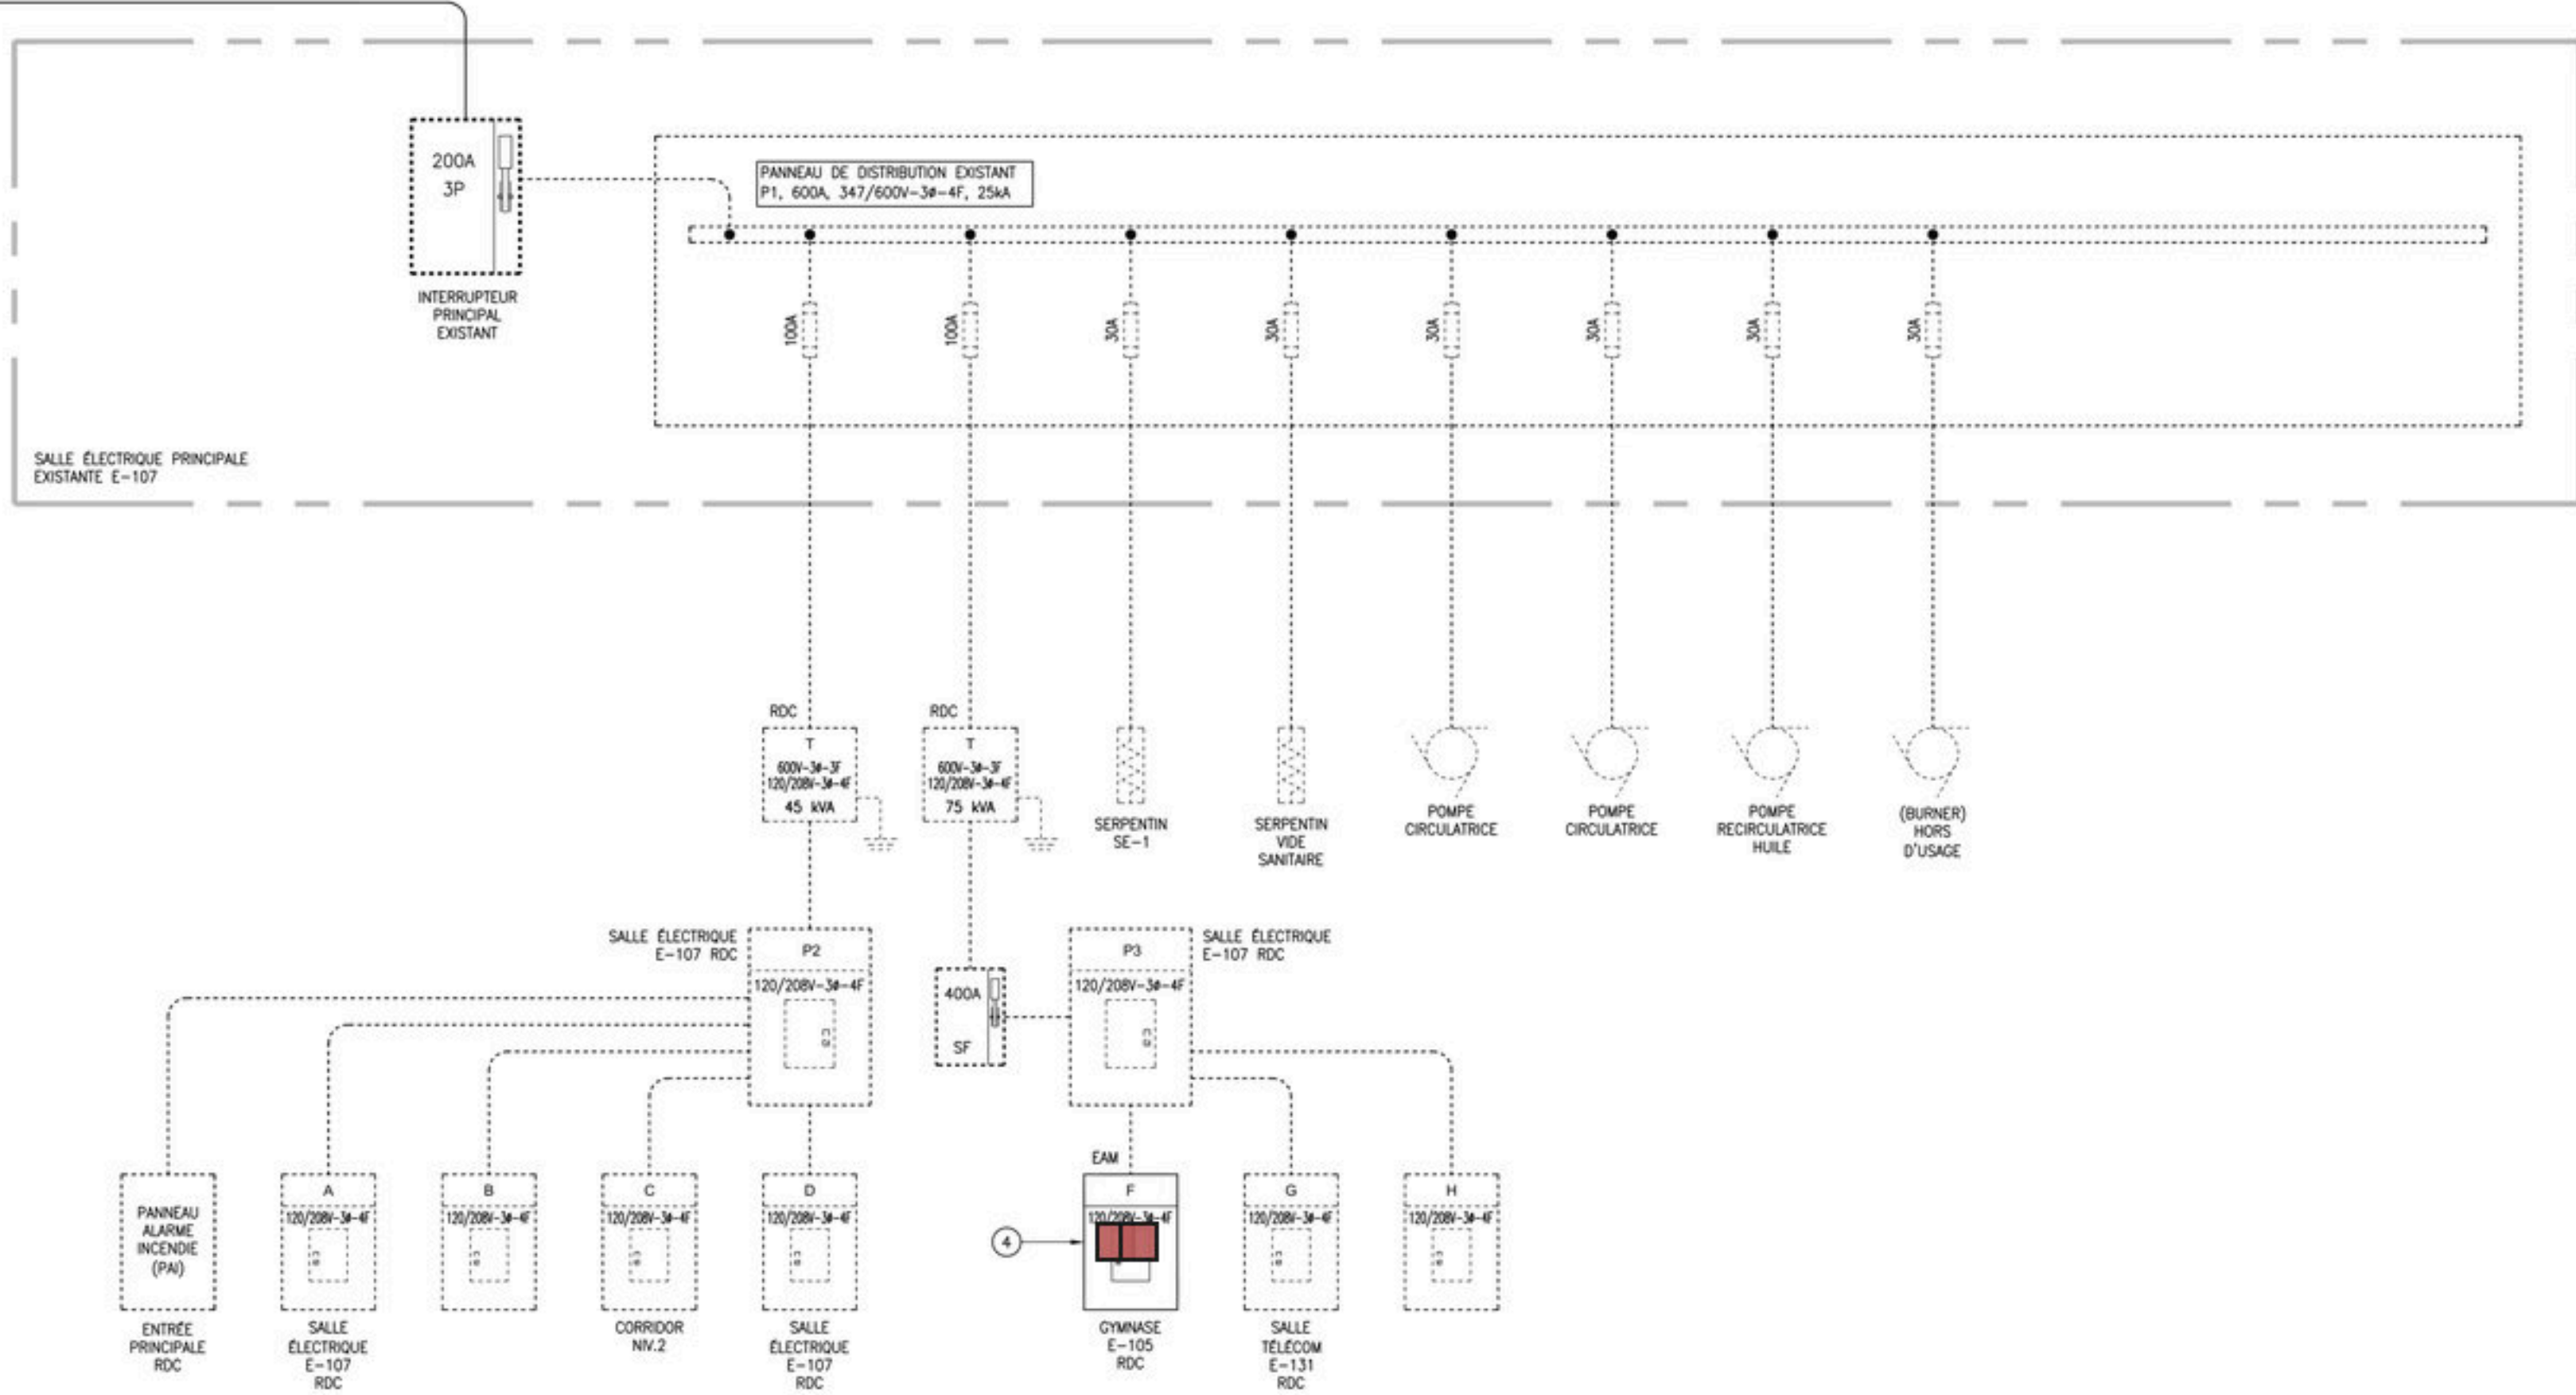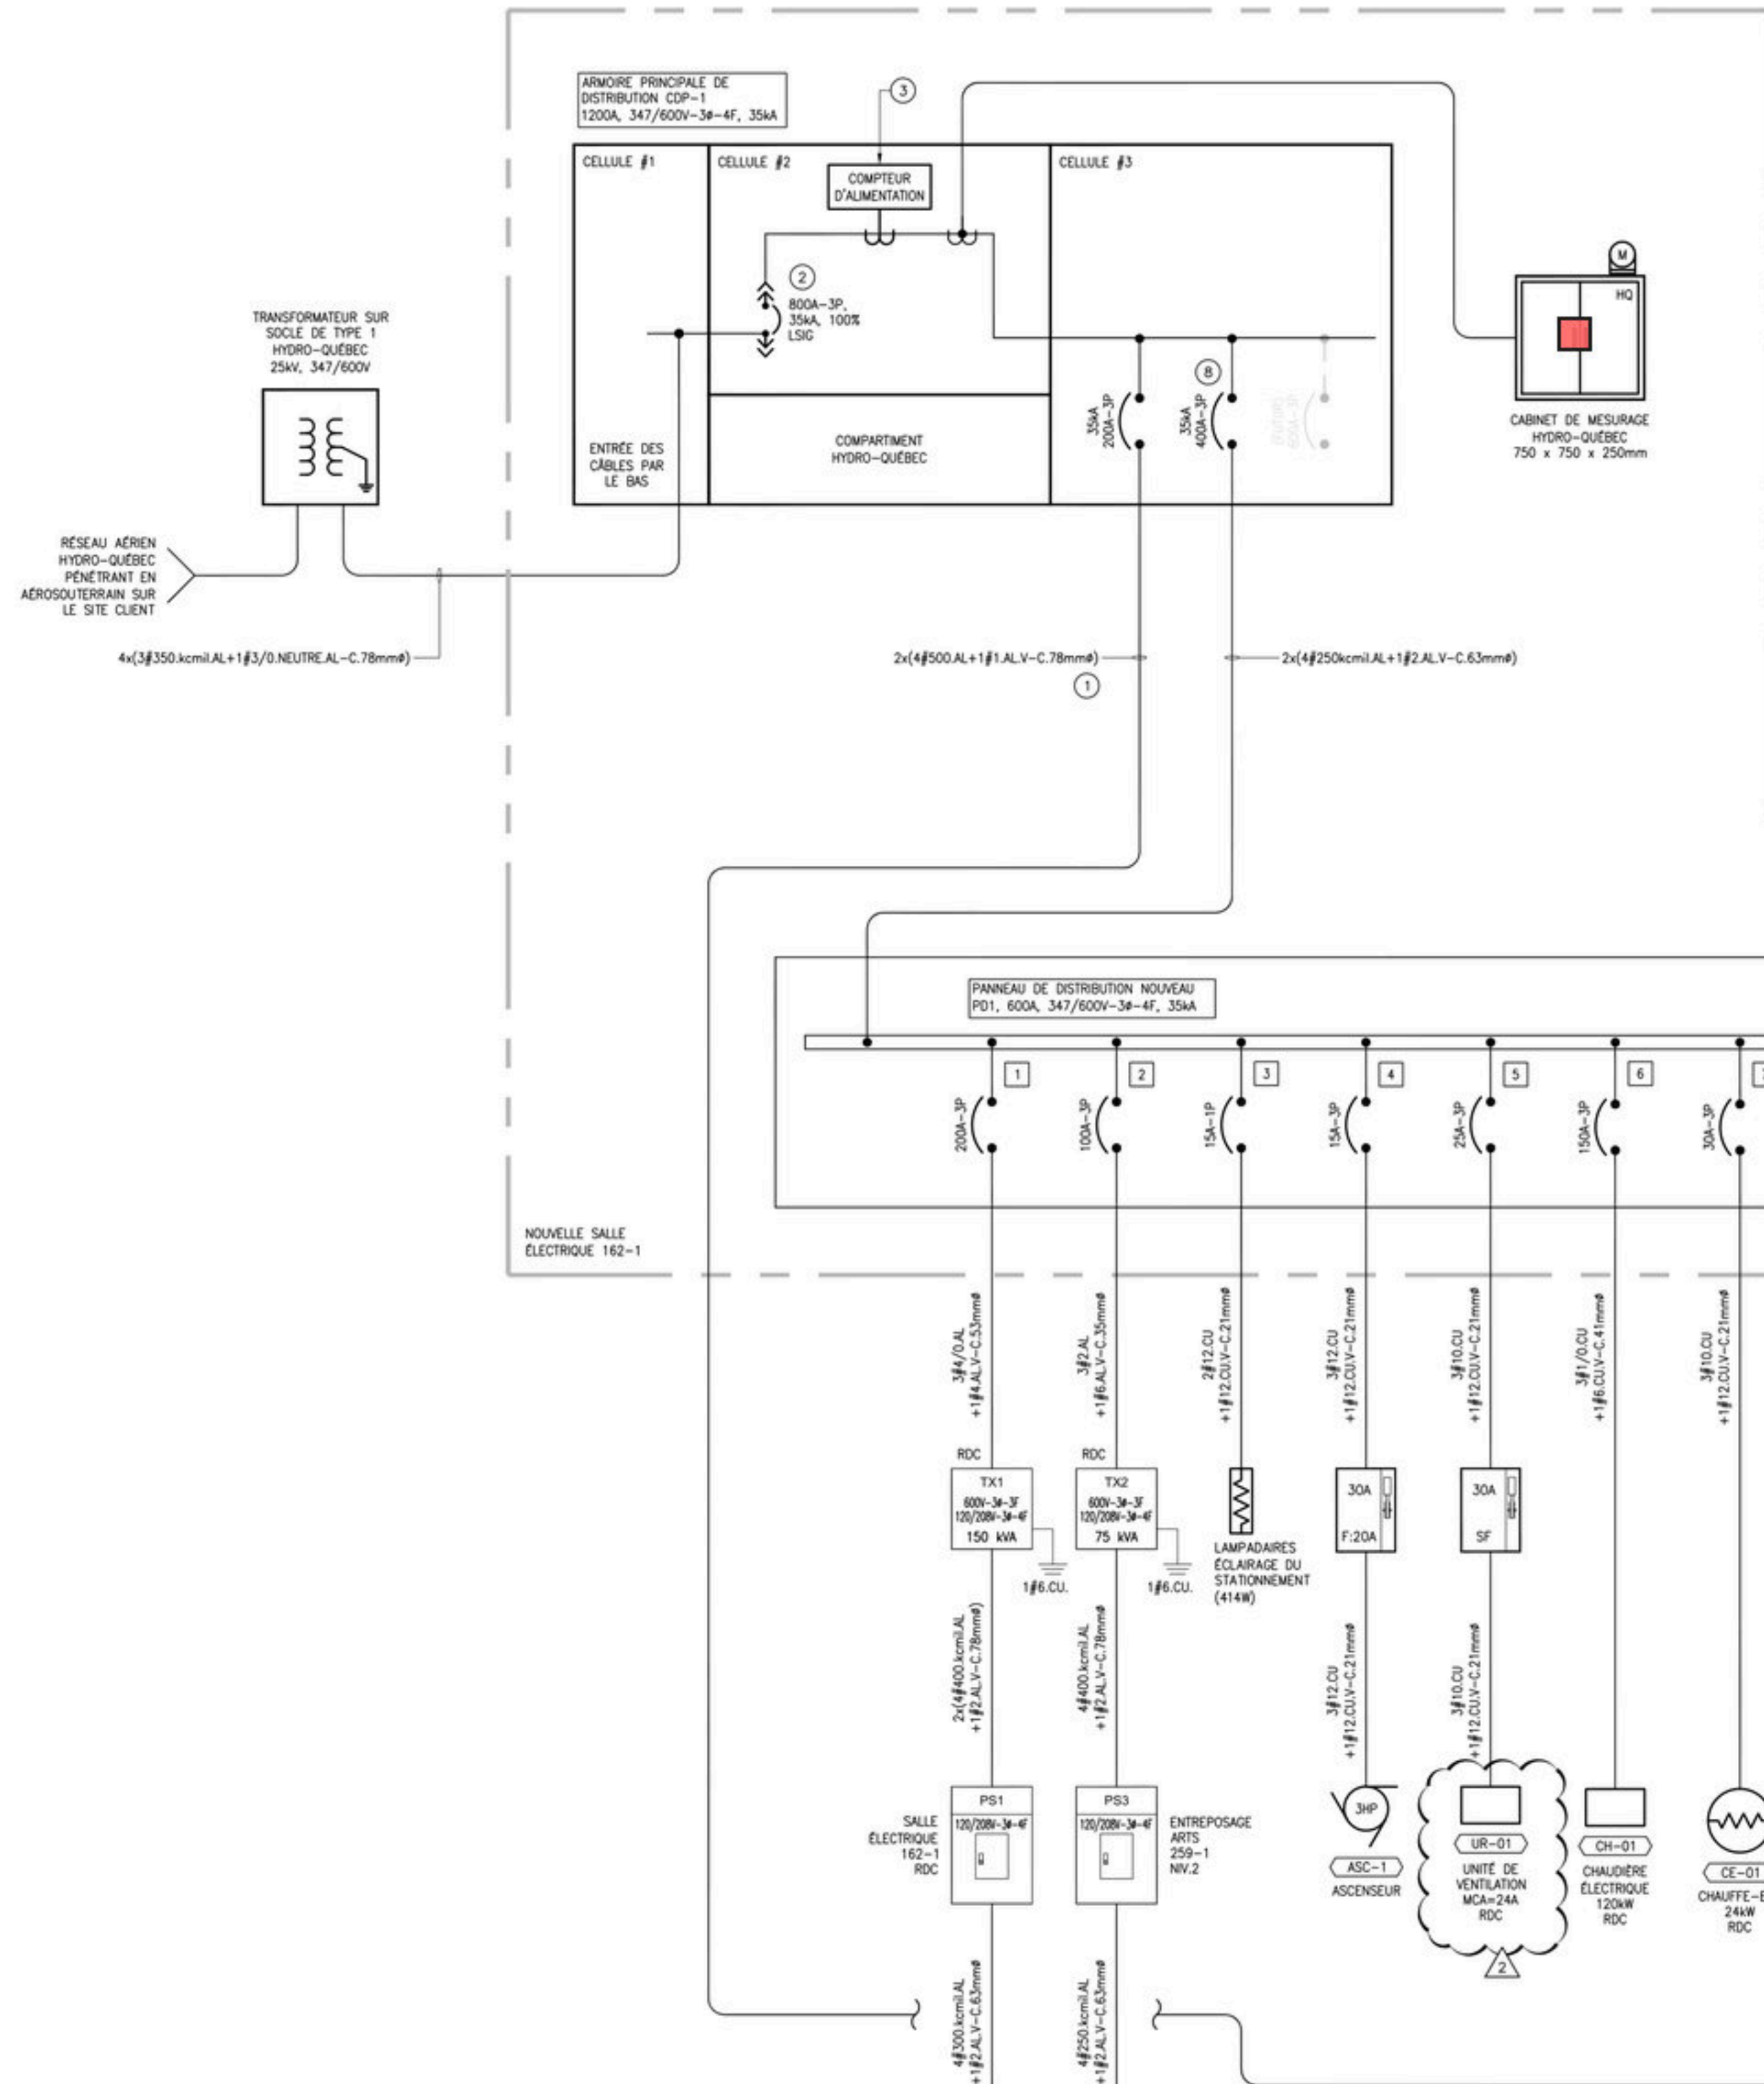

SCHEMA UNIFILAIRE DE DISTRIBUTION ELECTRIQUE - NOUVEAU

NOTES GÉNÉRALES :

- SAUF INDICATION CONTRAIRE, TOUT APPAREILLAGE REPRÉSENTÉ EN TRAIT PORTILLÉ EST EXISTANT. SE RÉFÉRER AUX INDICES DE TRAVAUX POUR PLUS DE DÉTAILS.
- SAUF INDICATION CONTRAIRE, TOUT APPAREILLAGE REPRÉSENTÉ EN TRAIT CONTINU EST NOUVEAU. SE RÉFÉRER AUX INDICES DE TRAVAUX POUR PLUS DE DÉTAILS.
- POUR TOUT NOUVEAU PANNEAU ÉLECTRIQUE DE DISTRIBUTION INSTALLÉ DANS UN NOUVEAU BÂTIMENT, ADAPTER 2 CONDUITS DE 2 POUCES QUI RELIENT LE DESSUS DU PANNEAU À UNE BOÎTE 12"x12" DEVANT LE PANNEAU DANS L'ENTRE-PLAFOND.
- ÉTUDE DE COORDINATION DES PROTECTIONS À FOURNIR PAR LE MANUFACTURIER.
- SI REQUIS, LES REDUCTEURS DE CÂBLES DOIVENT ÊTRE INSTALLÉS SELON LES NORMES EN VIGUEUR EN RESPECTANT LES GROSSEURS REQUISES.

NOTES SPÉCIFIQUES :

- ARTÈRE DIMENSIONNÉE POUR 600A. LASSER UNE MARQUE DE CÂBLE SUFFISANTE POUR LE TRANSFERT FUTUR DE L'ARTÈRE SUR LE DISJONCTEUR DE 600A.
- DISJONCTEUR CARENASSABLE.
- APPAREIL DE MESURAGE PRIVÉ DE LA CONSOMMATION ÉLECTRIQUE INTÈGRE À LA CELLULE C/A FENÊTRE.
- FOURNIR, INSTALLER ET RACCORDER DEUX NOUVEAUX DISJONCTEURS (15A-3P ET 20A-3P) DANS LE PANNEAU ÉLECTRIQUE EXISTANT « F » DU GYMNASIUM POUR LES RACCORDEMENTS DU NOUVEAU RÉSEAU MOTORISÉ.
- FOURNIR PAR DIVISION 22 ET RACCORDER PAR DIVISION 26.
- FOURNIR PAR DIVISION 25 ET RACCORDER PAR DIVISION 26.
- FOURNIR PAR DIVISION 23 ET RACCORDER PAR DIVISION 26.
- DISJONCTEUR ÉLECTRONIQUE LSI 600A AVEC CAPACITÉ DE PROTECTION EN SÉRIE DES DISJONCTEURS EN AVANT À HAUT. COURSE DE COORDINATION DES PROTECTIONS EN SÉRIE À FOURNIR PAR LE MANUFACTURIER.
- PRÉVOIR CONTACT AUXILIAIRE ET CÂBLAGE 2P/2 AWG ENTRE LE VARIATEUR DE FRÉQUENCE ET LE SECTIONNEUR EN AVANT RACCORDER LE CÂBLAGE AU BORNIER DE MISE HORS TENSION DU VARIATEUR DE FRÉQUENCE.

Légende — EL201_2 (3 marques)

- Cabinet mesurage HQ (1)
- Disjoncteur ajouté panneau existant (2)




Stantec Experts-conseils Inc.
375, boul. Roland-Thérien, bureau 400
Longueuil (Québec) J4H 4A6
Tél. 514.281.1010
www.stantec.com

Droit d'auteur

L'entrepreneur doit vérifier toutes les dimensions et en assumer la responsabilité. Toute erreur ou omission doit être rapportée à Stantec sans délai. Les droits d'auteur des plans et dessins demeurent la propriété de Stantec. Toute reproduction ou utilisation pour tout autre motif autre que celui autorisé par Stantec est strictement interdite.

Notes

Plan clé

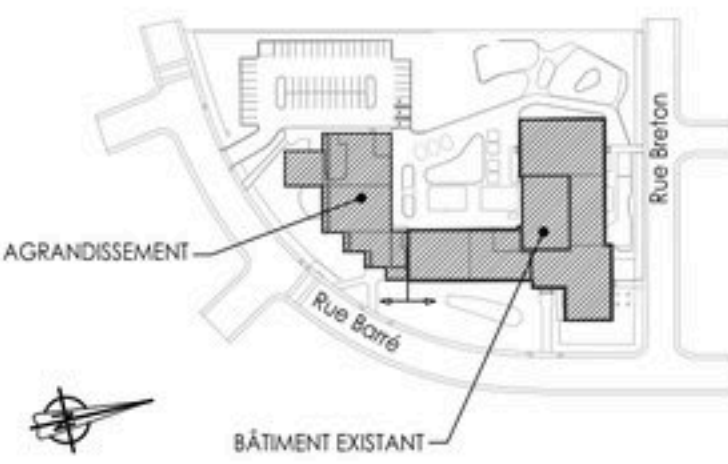

Architecte

HÉLOÏSE
THIBODEAU
ARCHITECTE



Paysagiste

RELIEFDESIGN

CE DOCUMENT NE DOIT PAS ÊTRE UTILISÉ À DES FINS DE CONSTRUCTION

1	POUR ADDENDA N°1	C.B.	C.S.	2024.07.02
2	POUR ADDENDA N°2	C.B.	C.S.	2024.08.26
3	POUR ADDENDA N°3	C.B.	C.S.	2024.08.15
4	POUR APPEL D'OFFRES	C.B.	C.S.	2024.08.15
Émissions/Révisions				Par Appr. AAAAA.M.M.J.J.

Nom fichier: 157103764-300-300-EL-0-201-202-D01-DWG 2024.04.02 AAAAA.M.M.J.J.

Châteaillon St-Amour, ing. Côté Blanchard
Préparé
Châteaillon St-Amour, ing. Simon Pellerin, ing.
Vérifié Chargé de projet

Secours



2008-07-02

Logo Client/Projet




Client/Projet
COMMISSION SCOLAIRE RIVERSIDE (CSR)
ÉCOLE WILLIAM LATIER
AGRANDISSEMENT ET RÉAMÉNAGEMENT

1300 rue Barré, Chambly, QC, J3L 2V4

Titre
ÉLECTRICITÉ
DISTRIBUTION - SCHEMA
NOUVEAU

N° Projet
157103764
Émis/Rév. Feuille
2
Échelle
AUCUNE
N° dessin
06 de 31
EL201

NOUVEAU - REZ-DE-CHAUSSEE									
NOM DU PANNEAU:		TENSION: 120/208V 3Ø 4F				ALIMENTÉ DE:			
PS1		CAPACITÉ: 600A, ICC: 10kA.				TRANSFO TX1			
LOCAL: S.ELECT.162-1		M.A.L.T.: NON		MONTAGE: SURFACE		SPD: NON		DISJ. PRINCIPAL: NON	
DESCRIPTION	IDENT. (*)	CHARGE (VA)	DISJ. (A)	IDENT. (*)	CHARGE (VA)	DISJ. (A)	IDENT. (*)	DESCRIPTION	IDENT. (*)
OPÉRATEURS PORTES 160	D	600	15	1	2	15	1440	ONNEAU/ÉCL. URGENCE RO.	
PORTES 160/ESC.02	D	360	15	3	4	15	72	BATTERIE URGENCE U1 162	
POMPE APPRINT AL. 5A-PA-01	M	250	15	5	6	15	800	ÉCL. CUISINE 156 ESC.	
POMPE PER-01	M	83	15	7	8	15	1014	ÉCL. CUISINE 156 ESC.	
POMPE GLYCOL POL-01	P	265	15	9	10	15	120	ECL. LITTE. MUR01 163, 101	
WETTE H-01	M	120	15	11	12	15	120	PANNEAU RÉGULATION ARIOT	
VENTILATEUR EXTERNE VH-01	M	120	15	13	14	15	1965	TEHMOPANOE TP-10	
VESTIBULE 160	C	5000	30	15	16	2P	--	--	
ESC.02, DÉPOT EXT 159, 163-1	C	5000	30	19	18	15	1965	TEHMOPANOE TP-11	
PUTS + CABINE ASCENSEUR	E/P	600	15	23	20	2P	--	--	
CLIQUE ALARME INCENDIE EXT.	D	120	15	25	22	15	120	TEHMOPANOE TP-22	
SALLE MÉCANIQUE 162	P	240	20	7	28	15	480	DÉPOT EXTERIEUR 159	
PASSERELLE COMM. BORNES	D	120	15	29	30	15	800	DÉPOTS 158 / 161	
BORNE RECHARGE DOUBLE	D	6656	40	31	32	15	800	P FROO CUISINE 158	
BR-01	D	2P 13			34	15	800	P FROO CUISINE 158	
BORNE RECHARGE DOUBLE	D	6656	40	35	36	15	800	MORO-0405 CUISINE 158	
BR-02	D	2P 37			38	15	800	MORO-0405 CUISINE 158	
BORNE RECHARGE DOUBLE	D	6656	40	39	40	15	800	P FROO CUISINE 158	
BR-03	D	2P 41			42	20	2500	MORO-0405 CUISINE 158	
BORNE RECHARGE DOUBLE	D	6656	40	43	44	20	500	P FROO CUISINE 158	
BR-04	D	2P 45			46	40	5000	P FROO CUISINE 158	
BORNE RECHARGE DOUBLE	D	6656	40	47	48	2P	120	TEHMOPANOE TP-10	
BR-05	D	2P 49			50	15	120	TEHMOPANOE TP-10	
BORNE RECHARGE DOUBLE	D	6656	40	51	52	2P	120	TEHMOPANOE TP-10	
BR-06	D	2P 53			54	15	120	TEHMOPANOE TP-10	
VENTILATEUR VA-02 159	M	350	15	25	56	2P	120	TEHMOPANOE TP-10	
POMPE P-03	P	220	15	57	58	15	--	L LIBRE	
ADOUCEUR 162	P	120	15	59	60	15	--	L LIBRE	
VOTIF BR-01 SALLE ÉLECTRIQUE	D/R	100	20	61	62	15	--	L LIBRE	
VOTIF SALLE ÉLECTRIQUE 162	D/R	200	20	63	64	15	--	L LIBRE	
LIBRE	L	20	20	65	66	15	--	L LIBRE	
PANNEAU PS2	D	50900	200	67	68	15	--	L LIBRE	
				69	70	15	--	L LIBRE	
				71	72	15	--	L LIBRE	
				73	74	15	--	L LIBRE	
				389	390	15	--	L LIBRE	

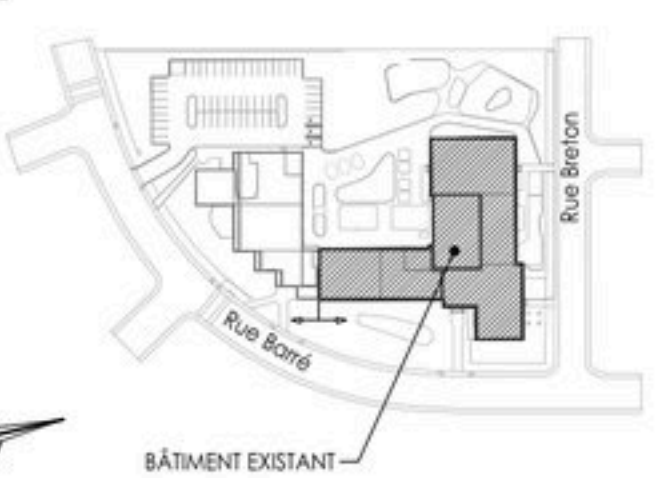

1	POUR ADDENDA N° 1	C.B.	C.E.	2024.04.25
0	POUR APPEL D'OFFRES	C.B.	C.S.	2024.06.15
Émissions/Révisions		Par	Appr.	AAAA.MM.JJ

Nom fichier: 157103764-300-300-EL-0-301-302_ECL1.DWG 2024.04.02

Châteaun St-Amour, inc. Car Blanchard

Préparé Desabé

Châteaun St-Amour, inc. Simon Pellerin, ing.

Vérifié Chargé de projet



2028-06-28

Logo Client/Projet



Client/Projet

COMMISSION SCOLAIRE RIVERSIDE (CSR)
ÉCOLE WILLIAM LATTEUR
AGRANDISSEMENT ET RÉAMÉNAGEMENT

1300 rue Barré, Chambly, QC, J3L 2V4

Titre
ÉLECTRICITÉ
ÉCLAIRAGE - REZ-DE-CHAUSSEE
BÂTIMENT EXISTANT - DÉMOLITION

N° Projet 157103764 Échelle 1:100

Émis/Rév. Feuille 1 N° dessin 08 de 32

NOTES GÉNÉRALES :

- A) SAUF INDICATION CONTRAIRE, TOUT APPAREILLAGE REPRÉSENTÉ EN TRAITS POINTILLÉS SUR CE PLAN EST EXISTANT À CONSERVER. SE RÉFÉRER AUX INDICES POUR DES DÉTAILS SUR LA NATURE DES TRAVAUX.
- B) SAUF INDICATION CONTRAIRE, TOUT APPAREILLAGE REPRÉSENTÉ EN TRAITS CONTINUS SUR CE PLAN EST À DÉMOUR, À MODIFIER OU À DÉPLACER. SE RÉFÉRER AUX INDICES POUR DES DÉTAILS SUR LA NATURE DES TRAVAUX.

NOTES SPÉCIFIQUES :


- 1 INDICATEUR DE SORTIE EXISTANT À RELOCALISER ET À RÉUTILISER POUR L'ISSUE TEMPORAIRE POUR LA DURÉE DU CHANTIER.
- 2 INDICATEUR DE SORTIE EXISTANT RELOCALISÉ ET RÉUTILISÉ POUR L'ISSUE TEMPORAIRE POUR LA DURÉE DU CHANTIER. PROLONGER LE RACCORDEMENT AU CIRCUIT EXISTANT LORS DE LA DÉMOLITION DE L'ISSUE TEMPORAIRE. RETIRER L'APPAREIL ET RETIRER LE FILAGE JUSQU'À LA SOURCE.
- 3 FOURNIR ET INSTALLER UN INDICATEUR DE SORTIE TEMPORAIRE MODÈLE RMC20W-500 DE STANPRO POUR L'ISSUE TEMPORAIRE POUR LA DURÉE DES TRAVAUX. RACCORDER AU MÊME CIRCUIT QUE L'INDICATEUR DE SORTIE EXISTANT LE PLUS PRÈS LORS DE LA DÉMOLITION DE L'ISSUE TEMPORAIRE. RETIRER L'APPAREIL ET RETIRER LE FILAGE JUSQU'À LA SOURCE.
- 4 FOURNIR ET INSTALLER DES PHARES D'ÉCLAIRAGE D'URGENCE TEMPORAIRES MODÈLE N2-06-12V-5W DE STANPRO POUR L'ISSUE TEMPORAIRE POUR LA DURÉE DES TRAVAUX. RACCORDER À LA BATTERIE D'ÉCLAIRAGE D'URGENCE EXISTANTE LA PLUS PRÈS LORS DE LA DÉMOLITION DE L'ISSUE TEMPORAIRE. RETIRER L'APPAREIL ET RETIRER LE FILAGE JUSQU'À LA SOURCE.
- 5 ISSUE TEMPORAIRE CONSTRUITE POUR LA DURÉE DES TRAVAUX D'AGRANDISSEMENT DU BÂTIMENT (VOIR LES PLANS D'ARCHITECTURE). FOURNIR ET INSTALLER LES APPARELS ET CONTRÔLES D'ÉCLAIRAGE TEMPORAIRES INDiqués. FOURNIR ET INSTALLER UN NOUVEAU DISJONCTEUR 15-A DANS UN PANNEAU EXISTANT 120/200V POUR LE RACCORDEMENT ET IDENTIFIER LE CIRCUIT "ÉCLAIRAGE ISSUE TEMPORAIRE" POUR LA DURÉE DES TRAVAUX. LORS DE LA DÉMOLITION DE L'ISSUE TEMPORAIRE, RETIRER LES APPARELS ET LES CONTRÔLES, RETIRER LE FILAGE JUSQU'À LA SOURCE, CONSERVER LE DISJONCTEUR EN POSITION "OFF" ET IDENTIFIER LE CIRCUIT "LIBRE" DANS LE PANNEAU.

Légende — EL301 (8 marques)

- Disjoncteur ajouté panneau existant (1)
- Enseigne existante relocalisée (1)
- Enseigne sortie temporaire (1)
- Interrupteur 3 voies temporaire (2)
- Luminaire T temporaire (2)
- Phare double temporaire (1)

Liste des pièces :

REZ-DE-CHAUSSEE - EXISTANT	E-132-4-1 W.C.
E-101 RÉCEPTION	E-133 DÉPÔT
E-102-1 SALLE DE RÉUNION	E-134 DÉPÔT
E-102-2 SALLE DE RÉUNION	COR. A CORRIDOR A
E-103 SÉCRÉTARIAT	COR. B CORRIDOR B
E-103-1 LOCAL SANTÉ	COR. C CORRIDOR C
E-104 PARTIÈRE	ESC. A ESCALIER A
E-105 GYMNASIUM	ESC. B ESCALIER B
E-105-1 BUREAU GYMNASIUM	HALL HALL D'ENTRÉE
E-105-2 DÉPÔT GYMNASIUM	SAS A-1 VESTIBULE A-1
E-105-3 DÉPÔT GYMNASIUM	SAS A-2 VESTIBULE A-2
E-105-4 VESTIBULE GYMNASIUM	SAS B VESTIBULE B
E-105-5 VESTIBULE GYMNASIUM	SAS C VESTIBULE C
E-107 SALLE ÉLECTRIQUE PRINCIPALE	REZ-DE-CHAUSSEE - AGRANDISSEMENT
E-108 SALLE DU PERSONNEL	150 VESTIBULE 01
E-108-1 DÉPÔT	151 BUREAU ET VESTIAIRE SDG
E-108-2 W.C.	152 ARMOIRES
E-108-3 W.C.	153 PALIER
E-109 W.C.	154 ISSUE
E-110 CLASSE	155 VESTIBULE 02
E-111 CLASSE MATERNELLE	156 CAGÈRES
E-112 TOILETTES GARÇONS	157 ESPACE DINERS - SDG
E-113 TOILETTES FILLES	158 CUISINE
E-114 CLASSE	158-1 DÉPÔT 01
E-115 CLASSE	159 DÉPÔT EXTÉRIEUR
E-116 CLASSE	160 VESTIBULE 03
E-118 MOTOBIKE	DÉPÔT 02
E-118-1 LOCAL D'ENTRETIEN	162 SALLE MÉCANIQUE
E-118-2 RANGEMENT	163 SALLE DE MOTOBIKE
E-118-3 PNE	162-1 SALLE ÉLECTRIQUE
E-119 CLASSE	163 SALLE DE MOTOBIKE
E-120 CLASSE	163-1 DÉPÔT MOTOBIKE
E-121 CLASSE	163-2 VESTIAIRE 01 MOTOBIKE
E-122 CLASSE	163-3 VESTIAIRE 02 MOTOBIKE
E-123 TOILETTES FILLES	164 CUISINE
E-124 CAGÈRES	165 TOILETTES FILLES
E-125 TOILETTES GARÇONS	166 PNE
E-126 CLASSE	167 PNE
E-127 PNE	168 W.C. UNIVERSELLE ET DOUCHE
E-128 CLASSE	169 PNE
E-129 CLASSE	170 SALLE POLYVALENTE - SDG
E-130 DÉPÔT	171 DÉPÔT SALLE POLYVALENTE
E-131 SALLE TÉLÉCOM	172 CORRIDOR 01
E-132-1 DÉPÔT	ASC. MONTE-CHARGE
E-132-2 DÉPÔT	ESC.01 ESCALIER 01
E-132-3 CLASSE MATERNELLE	ESC.02 ESCALIER 02
E-132-3-1 W.C.	
E-132-4 CLASSE MATERNELLE	

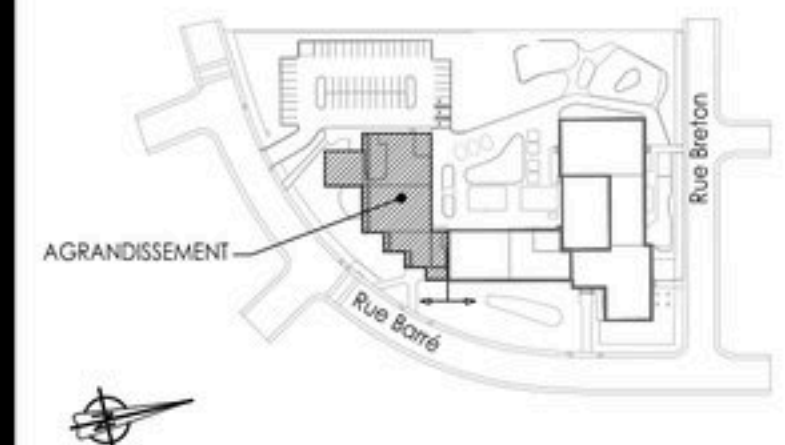

POUR APPRÉHENSION N° 1	C.B.	C.S.	2024.04.25
POUR APPEL D'OFFRES	C.B.	C.S.	2024.06.15
Missions/Révisions	Par	Appr.	AAAA.MMM.JJ

Donnée fichier: 157103764-300-300-EL-0-301-303-EL-1.DWG 2024.04.02

Projet/Client/Projet	Car Bonchard
Dessiné	
Projet/Client/Projet	Simon Pellerin, ing.
Chargé de projet	



NOTES GÉNÉRALES :




- SAUF INDICATION CONTRAIRE, TOUT APPAREILLAGE REPRÉSENTÉ EN TRACÉ POINTILLÉ SUR CE PLAN EST EXISTANT CONSERVÉ. SE RÉFÉRER AUX INDICES POUR DES DÉTAILS SUR LA NATURE DES TRAVAUX.
- SAUF INDICATION CONTRAIRE, TOUT APPAREILLAGE REPRÉSENTÉ EN TRACÉ CONTINU SUR CE PLAN EST NOUVEAU, EXISTANT MODIFIÉ OU EXISTANT DÉPLACÉ. SE RÉFÉRER AUX INDICES POUR DES DÉTAILS SUR LA NATURE DES TRAVAUX.
- AUCUN PERÇEMENT N'EST PERMIS DANS LES MURS DES ESCALIERS À MOINS QUE CELA NE DÉSERVIR LES ESCALIERS.
- SE RÉFÉRER AUX PLANS DE SCHÉMAS DE CONTRÔLE D'ÉCLAIRAGE POUR LES DÉTAILS D'INSTALLATION.


NOTES SPÉCIFIQUES :

- ÉCLAIRAGE SUR RAILS POUR LA ZONE "SIDE" OCCASIONNELLE. COORDONNER L'EMPLACEMENT AVEC L'ARCHITECTURE.
- LUMINAIRE ARCHITECTURAL COMMANDE PAR UNE MINUTERIE DOTÉE D'UNE HORLOGE ASTRONOMIQUE ET PAR UNE CELLULE PHOTOÉLECTRIQUE QUI ÉTEIGNENT LE LUMINAIRE DE MANIÈRE AUTOMATIQUE POUR LA PÉRIODE COMMENÇANT À MINUIT (OU À LA FERMETURE DU BÂTIMENT) ET FINISSANT AU PLUS TÔT À 6 HEURES DU MATIN (OU À L'HEURE D'OUVERTURE DU BÂTIMENT).
- MINUTERIE ET CONTACTEUR POUR LE CONTRÔLE DES APPARELS D'ÉCLAIRAGE EXTÉRIEUR.
- CELLULE PHOTOÉLECTRIQUE INTERFACÉE AVEC MINUTERIE DOTÉE D'UNE HORLOGE ASTRONOMIQUE POUR LE CONTRÔLE DES APPARELS D'ÉCLAIRAGE EXTÉRIEUR.
- BLOC D'ALIMENTATION ET RELAIS POUR CONTRÔLE D'ÉCLAIRAGE DU LOCAL 163.

Légende — EL303 (330 marques)

- Batterie urgence UA (2)
- Bloc relais DP1 (17)
- Bloc relais DP3 (1)
- Boîte PS1 — à confirmer (4)
- Cellule photoélectrique (1)
- Contacteur éclairage extérieur (1)
- Détecteur plafond OS2 (12)
- Détecteur plafond OS3 (8)
- Enseigne sortie applique (4)
- Enseigne sortie plafond (8)
- Luminaire A1 (6)
- Luminaire A1 urgence (2)
- Luminaire A2 (3)
- Luminaire B1 (2)
- Luminaire B2 (4)
- Luminaire B3 (8)
- Luminaire C (2)
- Luminaire C urgence (1)
- Luminaire D12 (4)
- Luminaire D18 (3)
- Luminaire D18 urgence (3)
- Luminaire D24 (2)
- Luminaire D24 urgence (4)
- Luminaire D36 (3)
- Luminaire E (7)
- Luminaire F (2)
- Luminaire F urgence (4)
- Luminaire G (7)
- Luminaire G urgence (6)
- Luminaire H urgence (1)
- Luminaire K (10)
- Luminaire L15 (31)
- Luminaire L2 (15)
- Luminaire L25 (9)
- Luminaire L4 (10)
- Luminaire L4 urgence (10)
- Luminaire L5 (3)
- Luminaire L5 urgence (1)
- Luminaire L8 (18)
- Luminaire L8 urgence (3)
- Luminaire N (16)
- Luminaire N urgence (1)
- Luminaire S1 (14)
- Luminaire S1 urgence (3)
- Luminaire T urgence (1)
- Luminaire W (1)

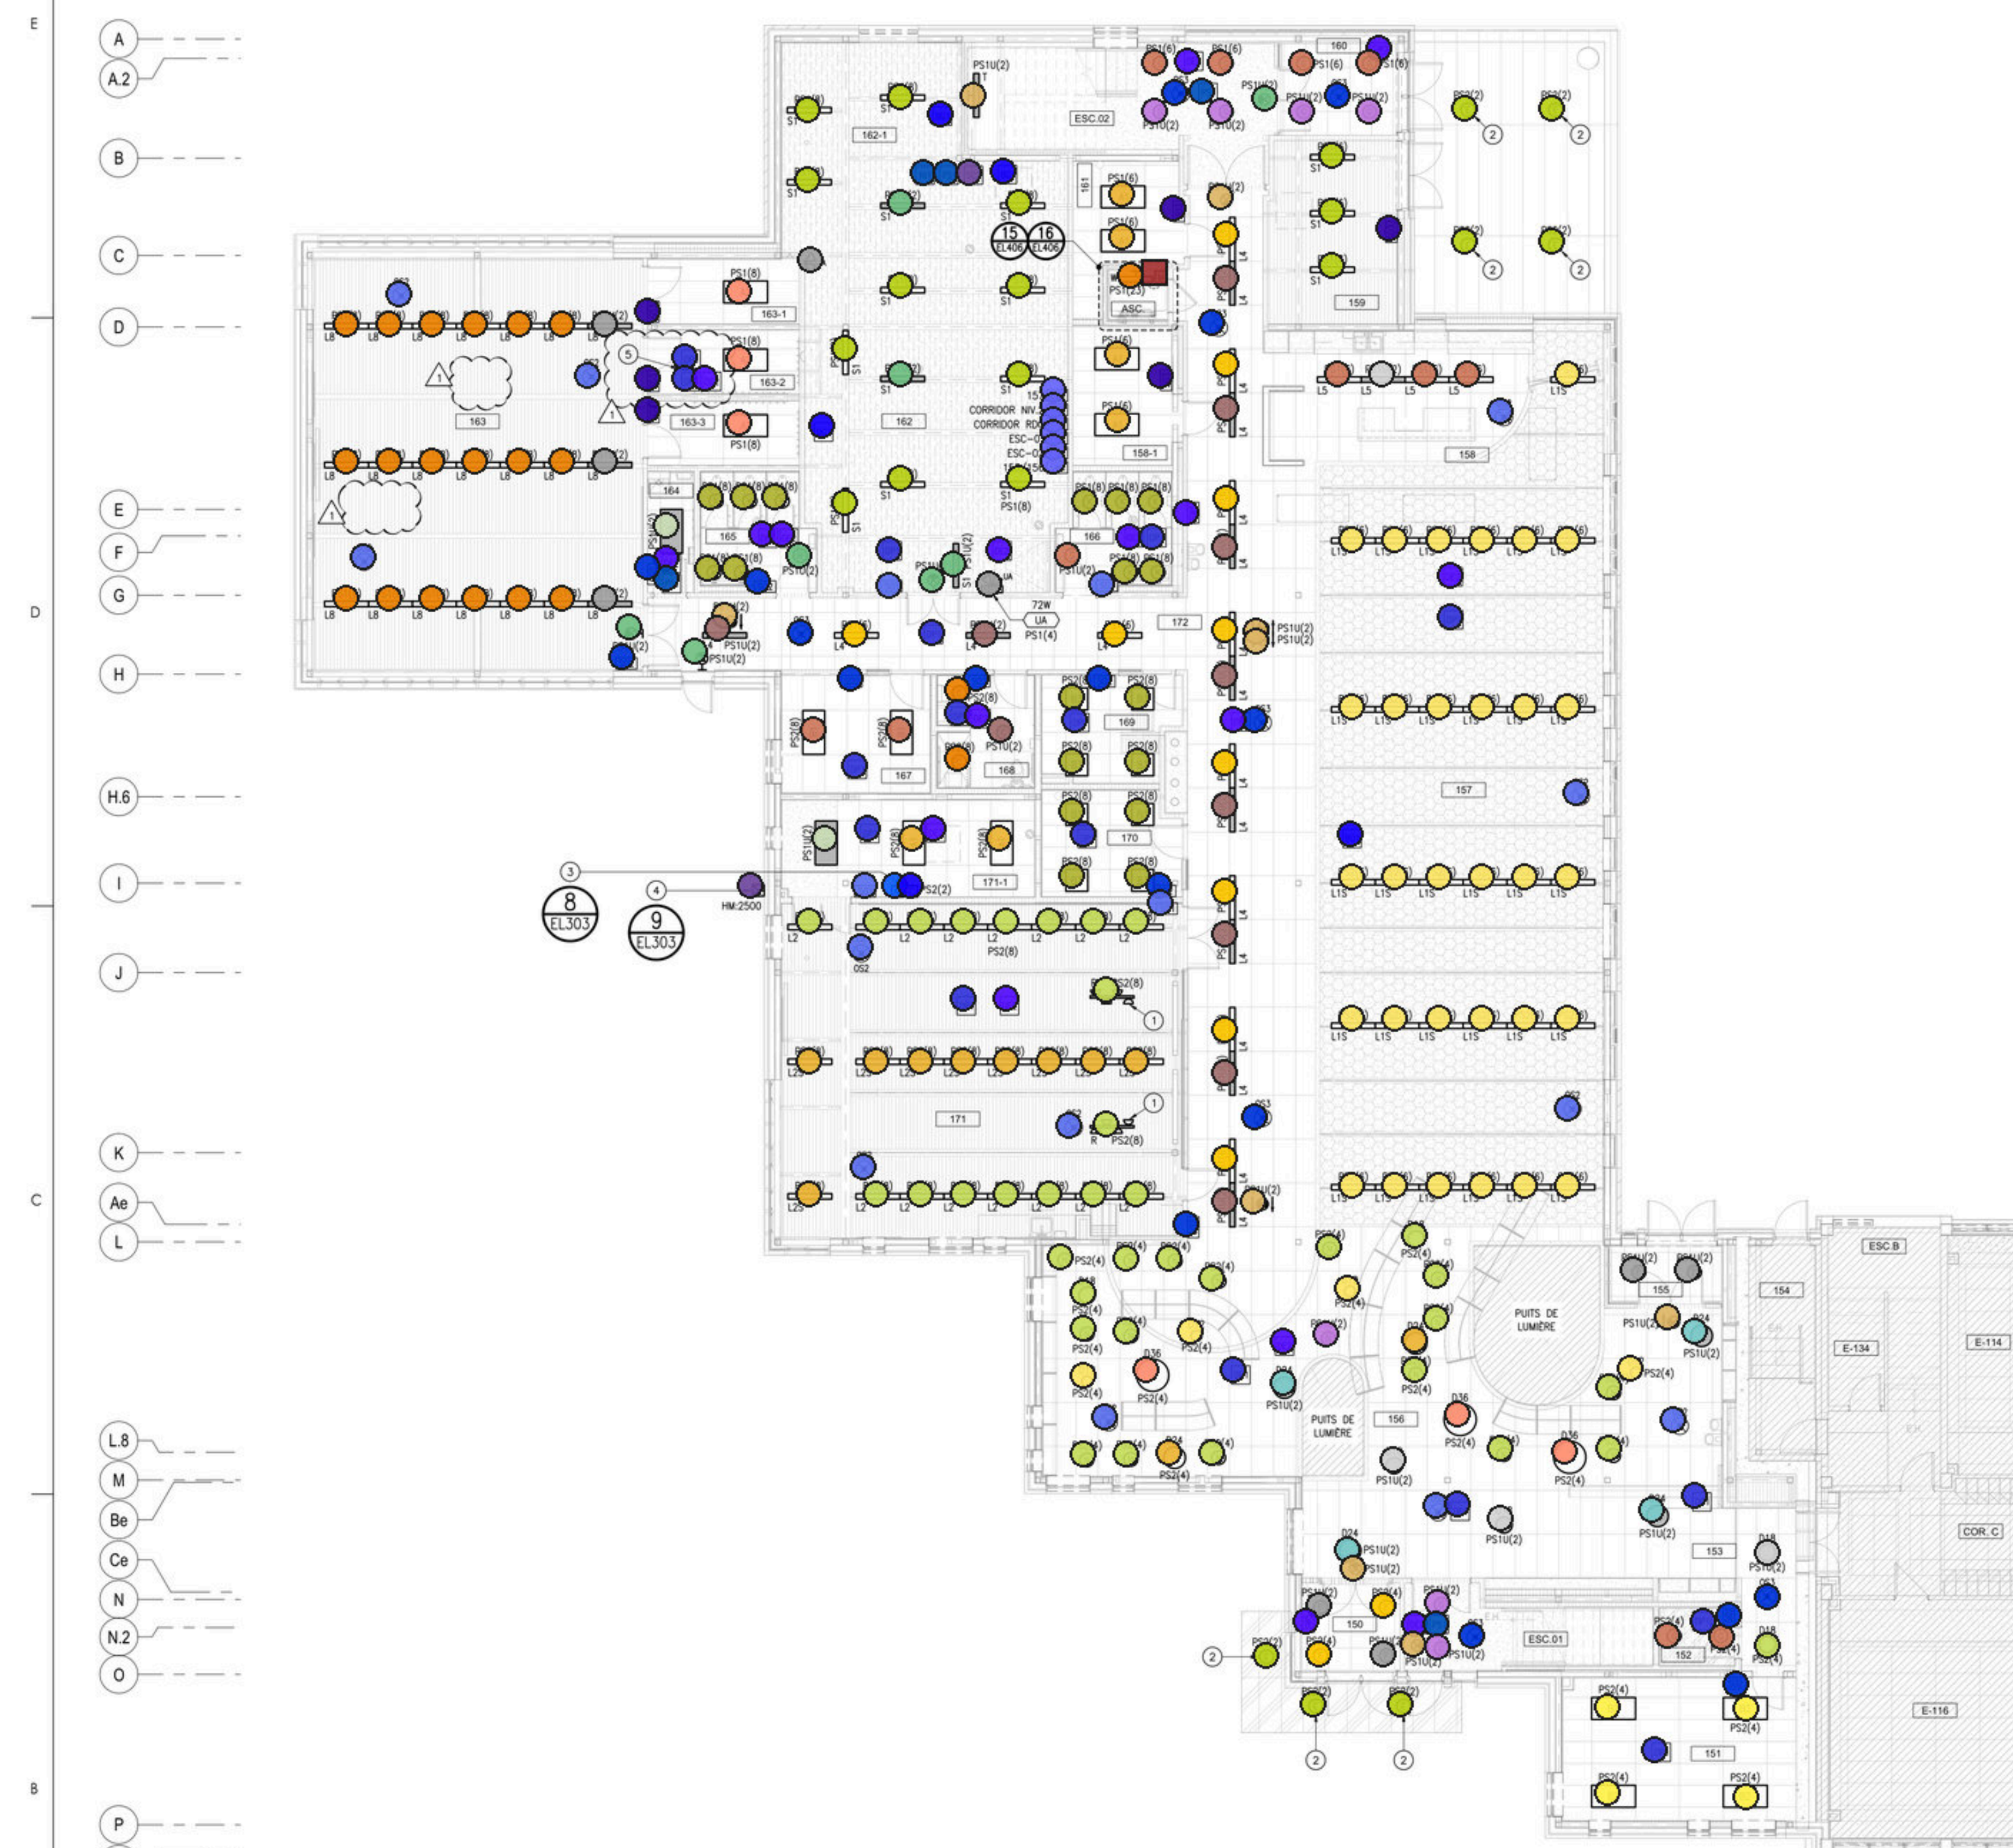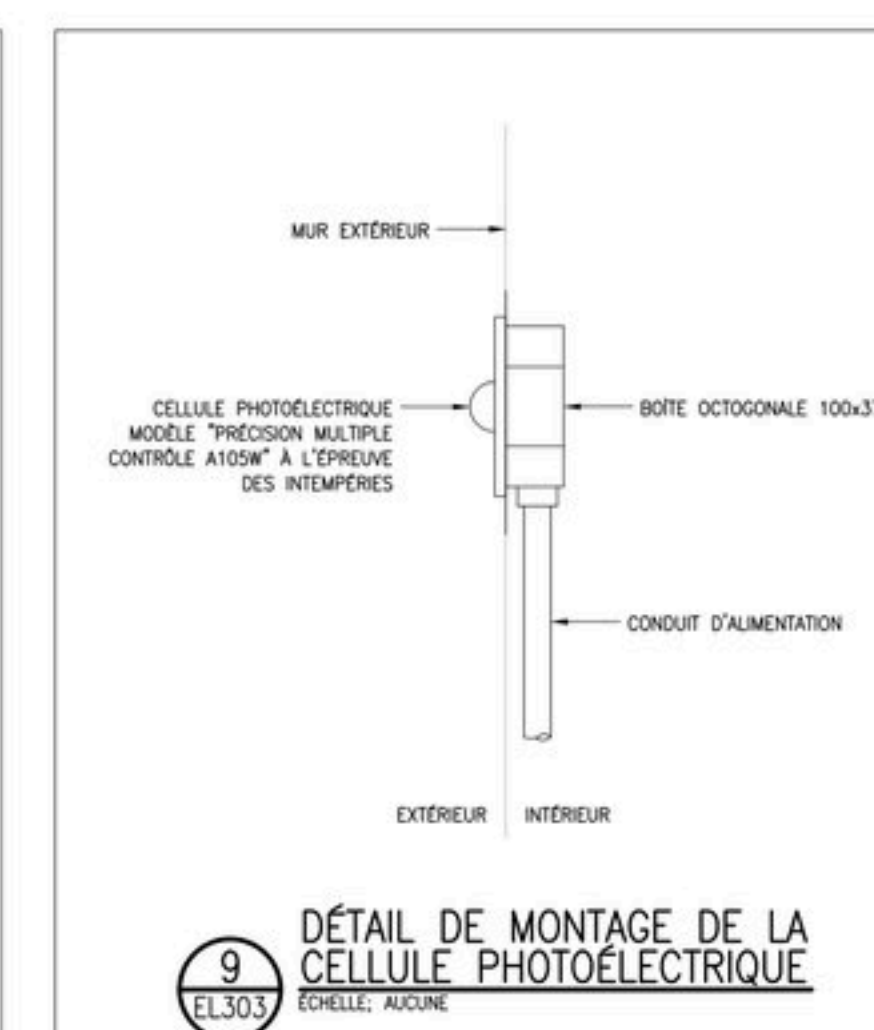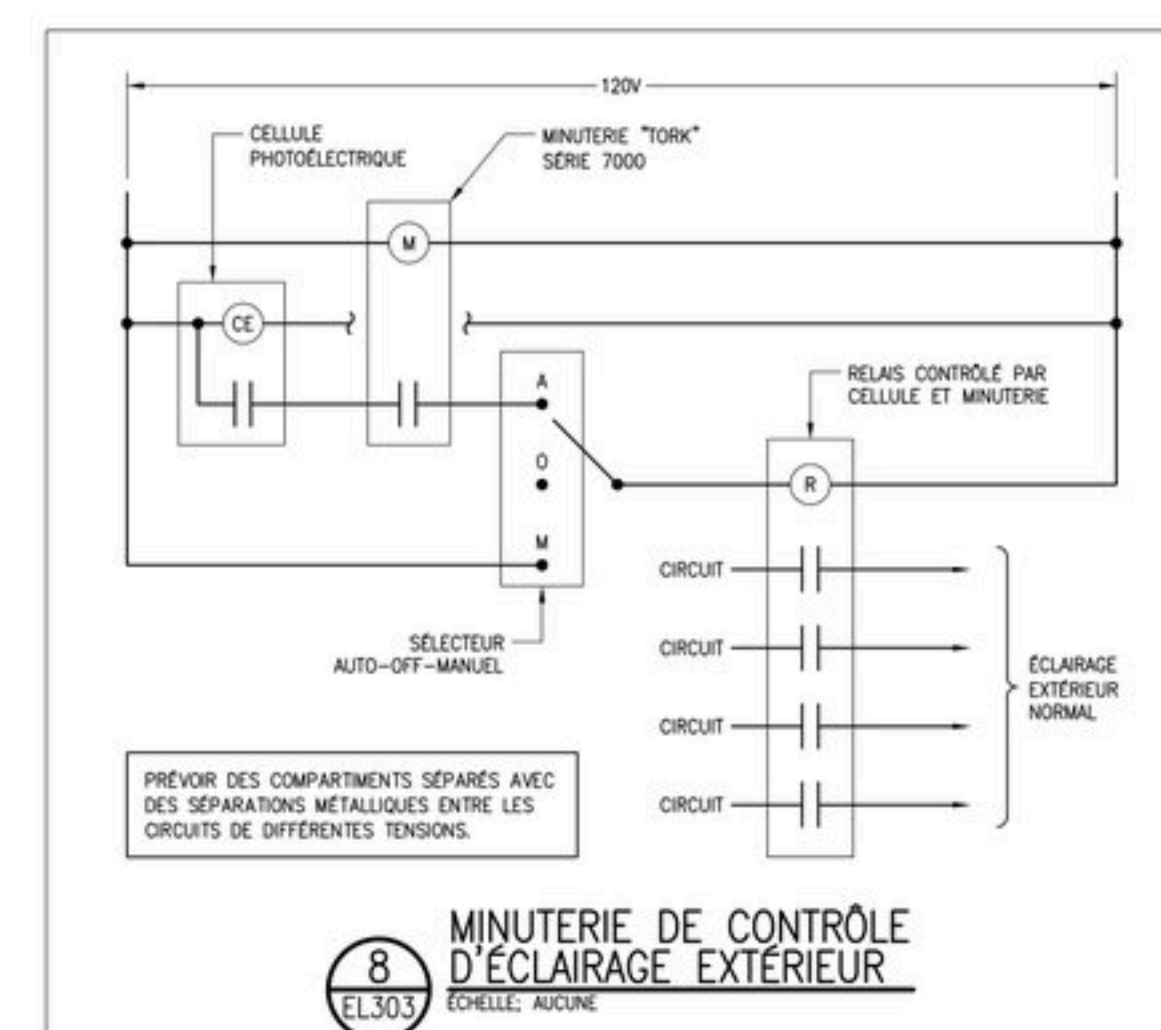

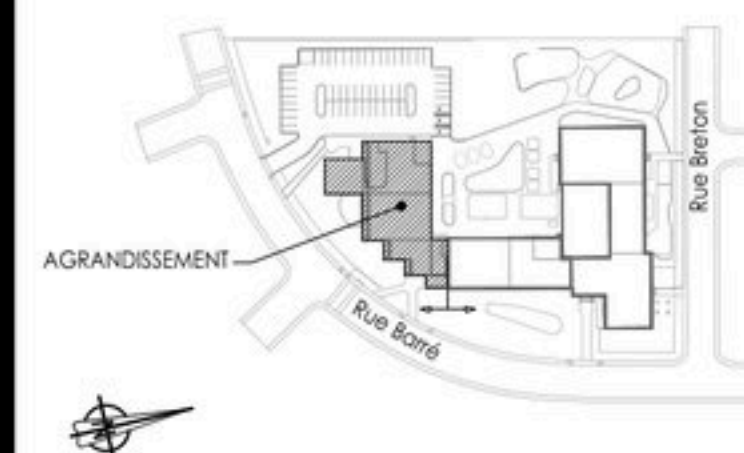

1	POUR ADDENDA N° 1	C.B.	C.S.	2024.04.25
0	POUR APPEL D'OFFRES	C.B.	C.S.	2024.06.15
Émissions/Révisions		Par	Appr.	AAAA.MM.JJ

Nom fichier: 157103764-300-300-EL-0-304-305_ECL2.DWG 2024.04.02 AAAA.MM.JJ

Châteaun St-Amour, inc.	Carl Blanchard
Préparé	Dessiné
Châteaun St-Amour, inc.	Simon Pellerin, ing.
Vérifié	Chargé de projet




NOTES GÉNÉRALES :

- A) SAUF INDICATION CONTRAIRE, TOUT APPAREILLAGE REPRÉSENTÉ EN TRAITS POINTILLÉS SUR CE PLAN EST EXISTANT CONSERVÉ. SE RÉFÉRER AUX INDICES POUR DES DÉTAILS SUR LA NATURE DES TRAVAUX.
- B) SAUF INDICATION CONTRAIRE, TOUT APPAREILLAGE REPRÉSENTÉ EN TRAITS CONTINUS SUR CE PLAN EST NOUVEAU, EXISTANT MODIFIÉ OU EXISTANT DÉPLACÉ. SE RÉFÉRER AUX INDICES POUR DES DÉTAILS SUR LA NATURE DES TRAVAUX.
- C) AUCUN PERÇEMENT N'EST PERMIS DANS LES MURS DES ESCALIERS À MOINS QUE CELA NE DÉSERVIE LES ESCALIERS.
- D) SE RÉFÉRER AUX PLANS DE SCHÉMAS DE CONTRÔLE D'ÉCLAIRAGE POUR LES DÉTAILS D'INSTALLATION.

Légende — EL305 (275 marques)

- Bloc relais DP1 (14)
- Détecteur plafond OS2 (12)
- Détecteur plafond OS3 (8)
- Enseigne sortie applique (1)
- Enseigne sortie plafond (3)
- Luminaire A1 (2)
- Luminaire A2 (1)
- Luminaire A3 (1)
- Luminaire A4 (1)
- Luminaire A4 urgence (1)
- Luminaire B1 (3)
- Luminaire D18 (1)
- Luminaire D18 urgence (2)
- Luminaire D24 (2)
- Luminaire D24 urgence (1)
- Luminaire D36 (3)
- Luminaire F (2)
- Luminaire G (30)
- Luminaire G urgence (6)
- Luminaire H (2)
- Luminaire H urgence (1)
- Luminaire J urgence (2)
- Luminaire L1 (5)
- Luminaire L1 urgence (2)
- Luminaire L3 (68)
- Luminaire L3 urgence (7)
- Luminaire L3S (20)
- Luminaire L3S urgence (3)
- Luminaire L4 (4)
- Luminaire L4 urgence (5)
- Luminaire L6 (2)
- Luminaire L6 urgence (1)
- Luminaire L7 (3)
- Luminaire N (7)
- Luminaire N urgence (1)
- Luminaire S2 (1)
- Luminaire S3 (1)
- Luminaire T urgence (2)
- Luminaire V (10)
- Module gradation DE2 (11)
- Pont nLight BG1 (3)
- Poste mural SO1 (6)
- Poste mural SO2 (3)
- Poste mural SO3 (4)
- Poste mural SW2 (1)
- Poste mural SW3 (6)

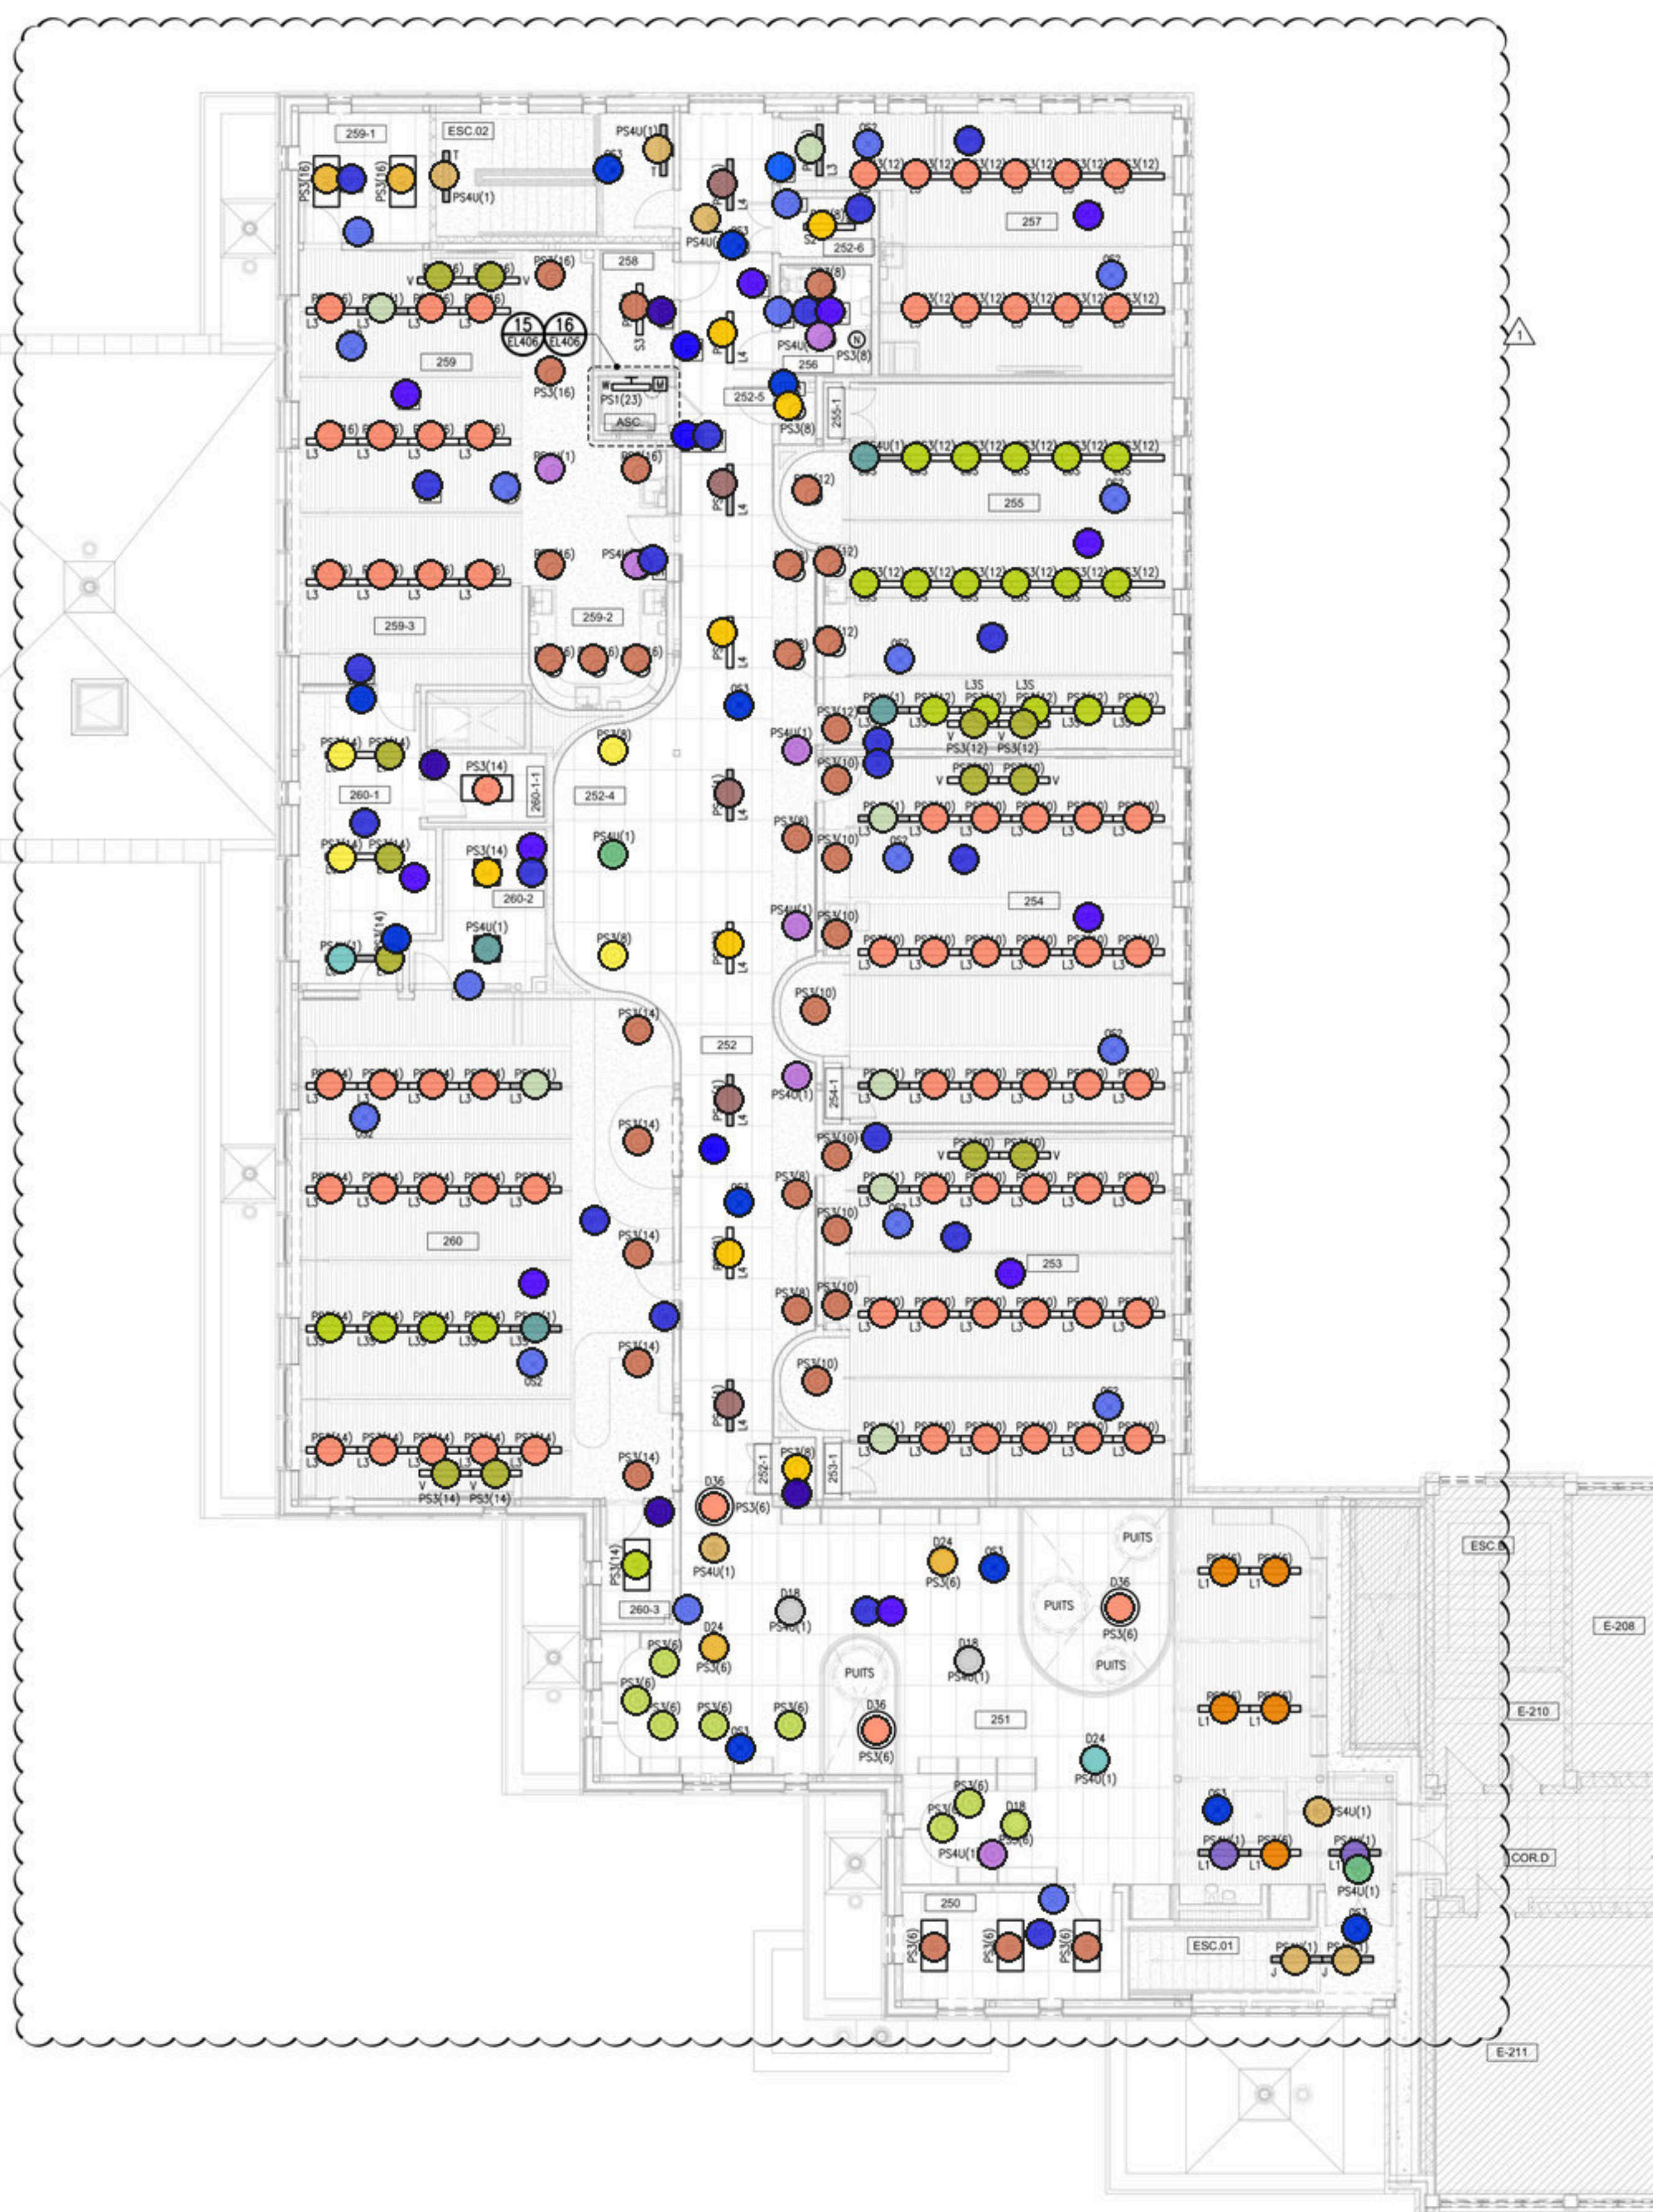

- A
- A.2
- B
- C
- D
- E
- F
- G
- H
- H.6
- I
- J
- K
- Ae
- L
- L.8
- M
- Be
- Ce
- N
- N.2
- O
- P
- De

L'entrepreneur doit vérifier toutes les dimensions et en assumer la responsabilité. Prière de ne pas modifier les échelles de dimensions des plans/dessins transmis - toute erreur ou omission doit être rapportée à Stantec sans délai. Les droits d'auteur des plans et dessins demeurent la propriété de Stantec. Toute reproduction ou utilisation pour tout autre motif autre que celui autorisé par Stantec est strictement interdite.

Notes

 HÉLOÏSE
THIBODEAU
ARCHITECTE
— I N C —
395, avenue Beaumont Montréal (Ouest)
H2B 1T9

gbi

agency **RELIEFDESIGN**

CE DOCUMENT NE DOIT
PAS ÊTRE UTILISÉ À DES FINS
DE CONSTRUCTION

[illegible]

0	POUR APPEL D'OFFRES	C.B.	C.S.	2026.06.15
	Emissions/Révisions	Par	Appr.	AAAA.MM.

Chatelein St-Amour, ing.	Carl Blanchard
--------------------------	----------------

Préparé	Dessiné
---------	---------

Chatelain St-Amour, inc.
Simon Pelletier, inc.

Sceaux



2026-06-
Logo Client/Project



Client/Project

COMMISSION SCOLAIRE RIVERSIDE (CSR)
ÉCOLE WILLIAM LATTER
AGRANDISSEMENT ET RÉAMÉNAGEMENT

1300 rue Barré, Chambly, QC J3L 2V4

Titre
ÉLECTRICITÉ
SERVICES - REZ-DE-CHAUSSÉE
BÂTIMENT EXISTANT - DÉMOLITION


N° Projet	Échelle
-----------	---------

157103764 1:100

Émis./Rév. Feuille	N° dessin
--------------------	-----------

0 13 de 32

EL401

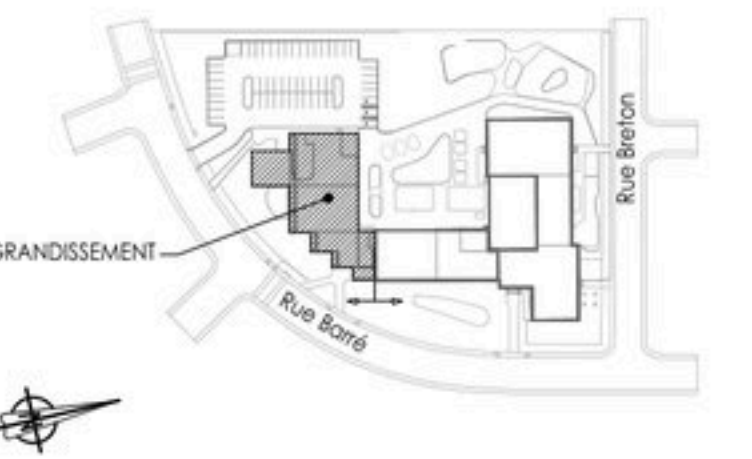

POUR ADDENDA N° 4	C.B.	C.B.A.	2024.07.18
POUR ADDENDA N° 2	C.B.	C.S.	2024.07.02
POUR ADDENDA N° 1	C.B.	C.S.	2024.06.26
POUR APPEL D'OFFRES	C.B.	C.S.	2024.06.15
Missions/Révisions	Par	Appr.	AAAA.MM.JJ

Données de base : 157103764 300 300-EL-0-401-404 58H1 DWG

Projet	St-Amour, ing.	Car Blanchard
Site		Desautels
Projet	St-Amour, ing.	Simon Pellerin, ing.
Site		Chargé de projet



NOTES GÉNÉRALES :

- SAUF INDICATION CONTRAIRE, TOUT APPAREILLAGE REPRÉSENTÉ EN TRAITS POINTILLÉS SUR CE PLAN EST EXISTANT. SE RÉFÉRER AUX INDEXES POUR DES DÉTAILS SUR LA NATURE DES TRAVAUX.
- SAUF INDICATION CONTRAIRE, TOUT APPAREILLAGE REPRÉSENTÉ EN TRAITS CONTINUS SUR CE PLAN EST NOUVEAU, EXISTANT MODIFIÉ OU EXISTANT DÉPLACÉ. SE RÉFÉRER AUX INDEXES POUR DES DÉTAILS SUR LA NATURE DES TRAVAUX.
- AUCUN PERÇEMENT N'EST PERMIS DANS LES MURS DES ESCALIERS À MOINS QUE CELA NE DÉSERVIR LES ESCALIERS.

NOTES SPÉCIFIQUES :



- POSITION ET HAUTEUR DE MONTAGE À COORDONNER AVEC L'ARCHITECTURE.
- SÈCHE-MAINS HAUTE VÉLOCITÉ XLERATOR AVEC CHAUFFAGE, MODÈLE XL-C-111110-120V. COORDONNER L'EMPLACEMENT EXACT AVEC L'ARCHITECTURE.
- ALIMENTATION ÉLECTRIQUE VIA DES CONDUITS INTÉGRÉS DANS LA DALLE DU PLANCHER.
- MINI-ONDULEUR DE 1440W, MODÈLE DM-1440/60 DE EMPO-UTE, POUR L'ALIMENTATION DES APPAREILS D'ÉCLAIRAGE DE SÉCURITÉ ET DE SIGNALISATION. DIMENSIONS 24" x 40.75" x 14.5". CIRCUIT D'ENTRÉE PS1(2), CIRCUIT DE SORTIE PS1(2).
- PRISE ÉLECTRIQUE POUR L'ALIMENTATION DE L'ADOUCEUR D'EAU. À INSTALLER À 48" MAXIMUM DE L'APPAREIL. COORDONNER LA HAUTEUR D'INSTALLATION DE LA PRISE AVEC SELON LES RÉGLES DU MÉCANICIEN.
- ALIMENTATION POUR CÂBLE CHAUFFANT AUTORÉGULANT DE TYPE IEC-TP DE INVENT/RYCHOM FOURNI PAR L'ENTREPRENEUR ÉLECTRIEN, MODÈLE DM-147 à 120 V POUR LA GARDOUILLE DANS LE PARAPET. TROUSSE DE CONNEXION FTS-P ET THERMOSTAT MANI D'UNE PROTECTION DDT : ECH-EP EN MODE AMBIANT. SE RÉFÉRER AUX DÉTAILS D'INSTALLATION DU MANUFACTURIER ET COORDONNER AVEC LES PLANS D'ARCHITECTURE.
- LOCAL SÈCHE-PRÉVOIR RACCORDE ÉTANCHE ET CAPOT ANTI-ÉCOUVILLERMENT AFIN QUE LES ÉQUIPEMENTS (TRANSFORMATEURS, PANNEAU DE DISTRIBUTION, BOÎTE DE MESURAGE, ETC.) SOIENT À L'ÉPREUVE DES GÉLÉES.

Légende — EL403_3 (123 marques)

- Armoire distribution CDP-1 (1)
- ▲ Bouton contrôle d'accès (8)
- ▲ Boîte contrôle de porte (4)
- Boîte de jonction murale (7)
- Boîte mesurage HQ (1)
- Mini-onduleur 1440W (1)
- ▲ Opérateur de porte (4)
- Panneau distribution (3)
- Prise adoucisseur (1)
- Prise congélateur (1)
- Prise double (35)
- Prise double 20A RA (14)
- Prise double DDFT (2)
- Prise double comptoir (7)
- Prise double comptoir 20A (4)
- Prise lave-vaisselle (1)
- Prise micro-onde (5)
- Prise réfrigérateur (3)
- Raccordement cuisinière (1)
- ◆ Raccordement câble chauffant (1)
- Raccordement fontaine d'eau (4)
- ▲ Retenue magnétique (6)
- Sèche-mains (3)
- Transformateur sec (2)
- ▲ Electro-aimant (4)

Liste des pièces :

REZ-DE-CHAUSSEE - EXISTANT	E-132-4-1 W.C.
E-101 RÉCEPTION	E-133 DÉPÔT
E-102-1 SALLE DE RÉUNION	E-134 DÉPÔT
E-102-2 SALLE DE RÉUNION	COR. A CORRIDOR A
E-103 SÉCRÉTARIAT	COR. B CORRIDOR B
E-103-1 LOCAL SANTÉ	COR. C CORRIDOR C
E-104 PARTIERS	ESC. A ESCALIER A
E-105 CUISINE	ESC. B ESCALIER B
E-105-1 BUREAU CUISINE	HALL HALL D'ENTRÉE
E-105-2 DÉPÔT CUISINE	SAS A-1 VESTIBULE A-1
E-105-3 DÉPÔT CUISINE	SAS A-2 VESTIBULE A-2
E-105-4 VESTIBULE CUISINE	SAS B VESTIBULE B
E-105-5 VESTIBULE CUISINE	SAS C VESTIBULE C
E-107 SALLE ÉLECTRIQUE PRINCIPALE	
E-108 SALLE DU PERSONNEL	
E-108-1 DÉPÔT	VESTIBULE 01
E-108-2 W.C.	BUREAU ET VESTIBULE SDO
E-108-3 W.C.	ARROCHES
E-109-1 W.C.	PALIER
E-110 CLASSE	ROSE
E-111 CLASSE MATERNELLE	VESTIBULE 02
E-112 TOILETTES GARÇONS	CASERS
E-113 CLASSE FILLES	ESPACE OMBRES - SDO
E-114 CLASSE	CUISINE
E-115 CLASSE	158-1 DÉPÔT 01
E-116 CLASSE	159 DÉPÔT EXTÉRIEUR
E-117 CLASSE	160 VESTIBULE 03
E-118 CLASSE	161 DÉPÔT 02
E-118-1 LOCAL D'ENTRETIEN	162 SALLE MÉCANIQUE
E-118-2 RANGEMENT	162-1 SALLE ÉLECTRIQUE
E-119 PNE	163 SALLE DE MOTOCYTE
E-120 CLASSE	163-1 DÉPÔT MOTOCYTE
E-121 CLASSE	163-2 VESTIBULE DE MOTOCYTE
E-122 CLASSE	163-3 VESTIBULE 02 MOTOCYTE
E-123 TOILETTES FILLES	164 CUISINE
E-124 CASERS	165 TOILETTES FILLES
E-125 TOILETTES GARÇONS	166 TOILETTES GARÇONS
E-126 CLASSE	167 PNE
E-127 CLASSE	168 W.C. UNIVERSELLE ET DOUCHE
E-128 CLASSE	169 PNE
E-129 CLASSE	170 SALLE POLYVALENTE - SDO
E-130 DÉPÔT	171 DÉPÔT SALLE POLYVALENTE
E-131 SALLE TÉLÉCOM	171-1 DÉPÔT SALLE POLYVALENTE
E-132-1 DÉPÔT	ASC. MONTE-CHARGE
E-132-2 DÉPÔT	ESC. 01 ESCALIER 01
E-132-3 CLASSE MATERNELLE	ESC. 02 ESCALIER 02
E-132-4 CLASSE MATERNELLE	

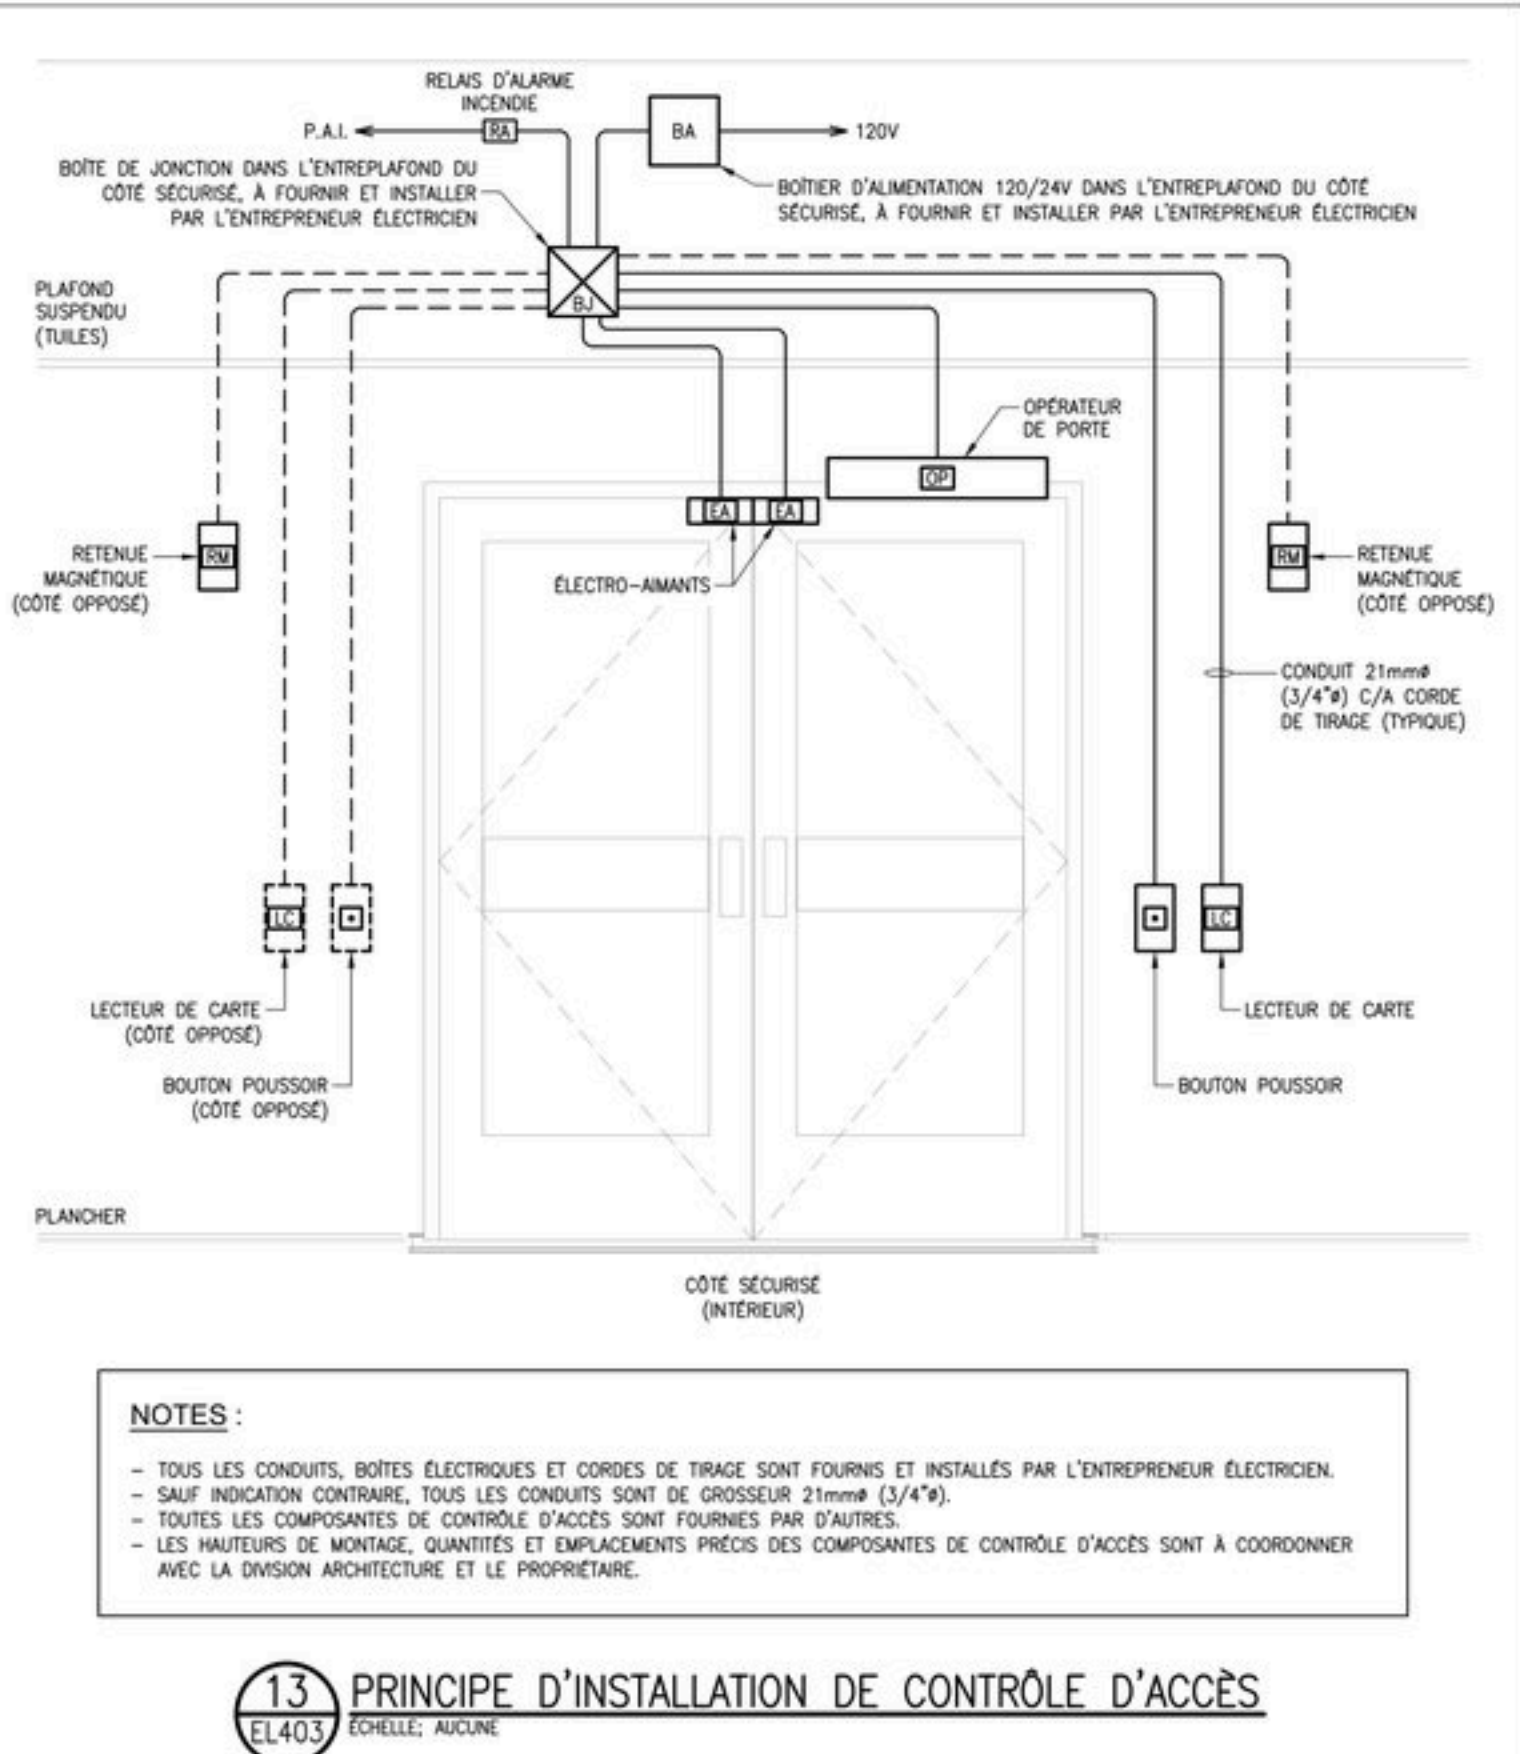
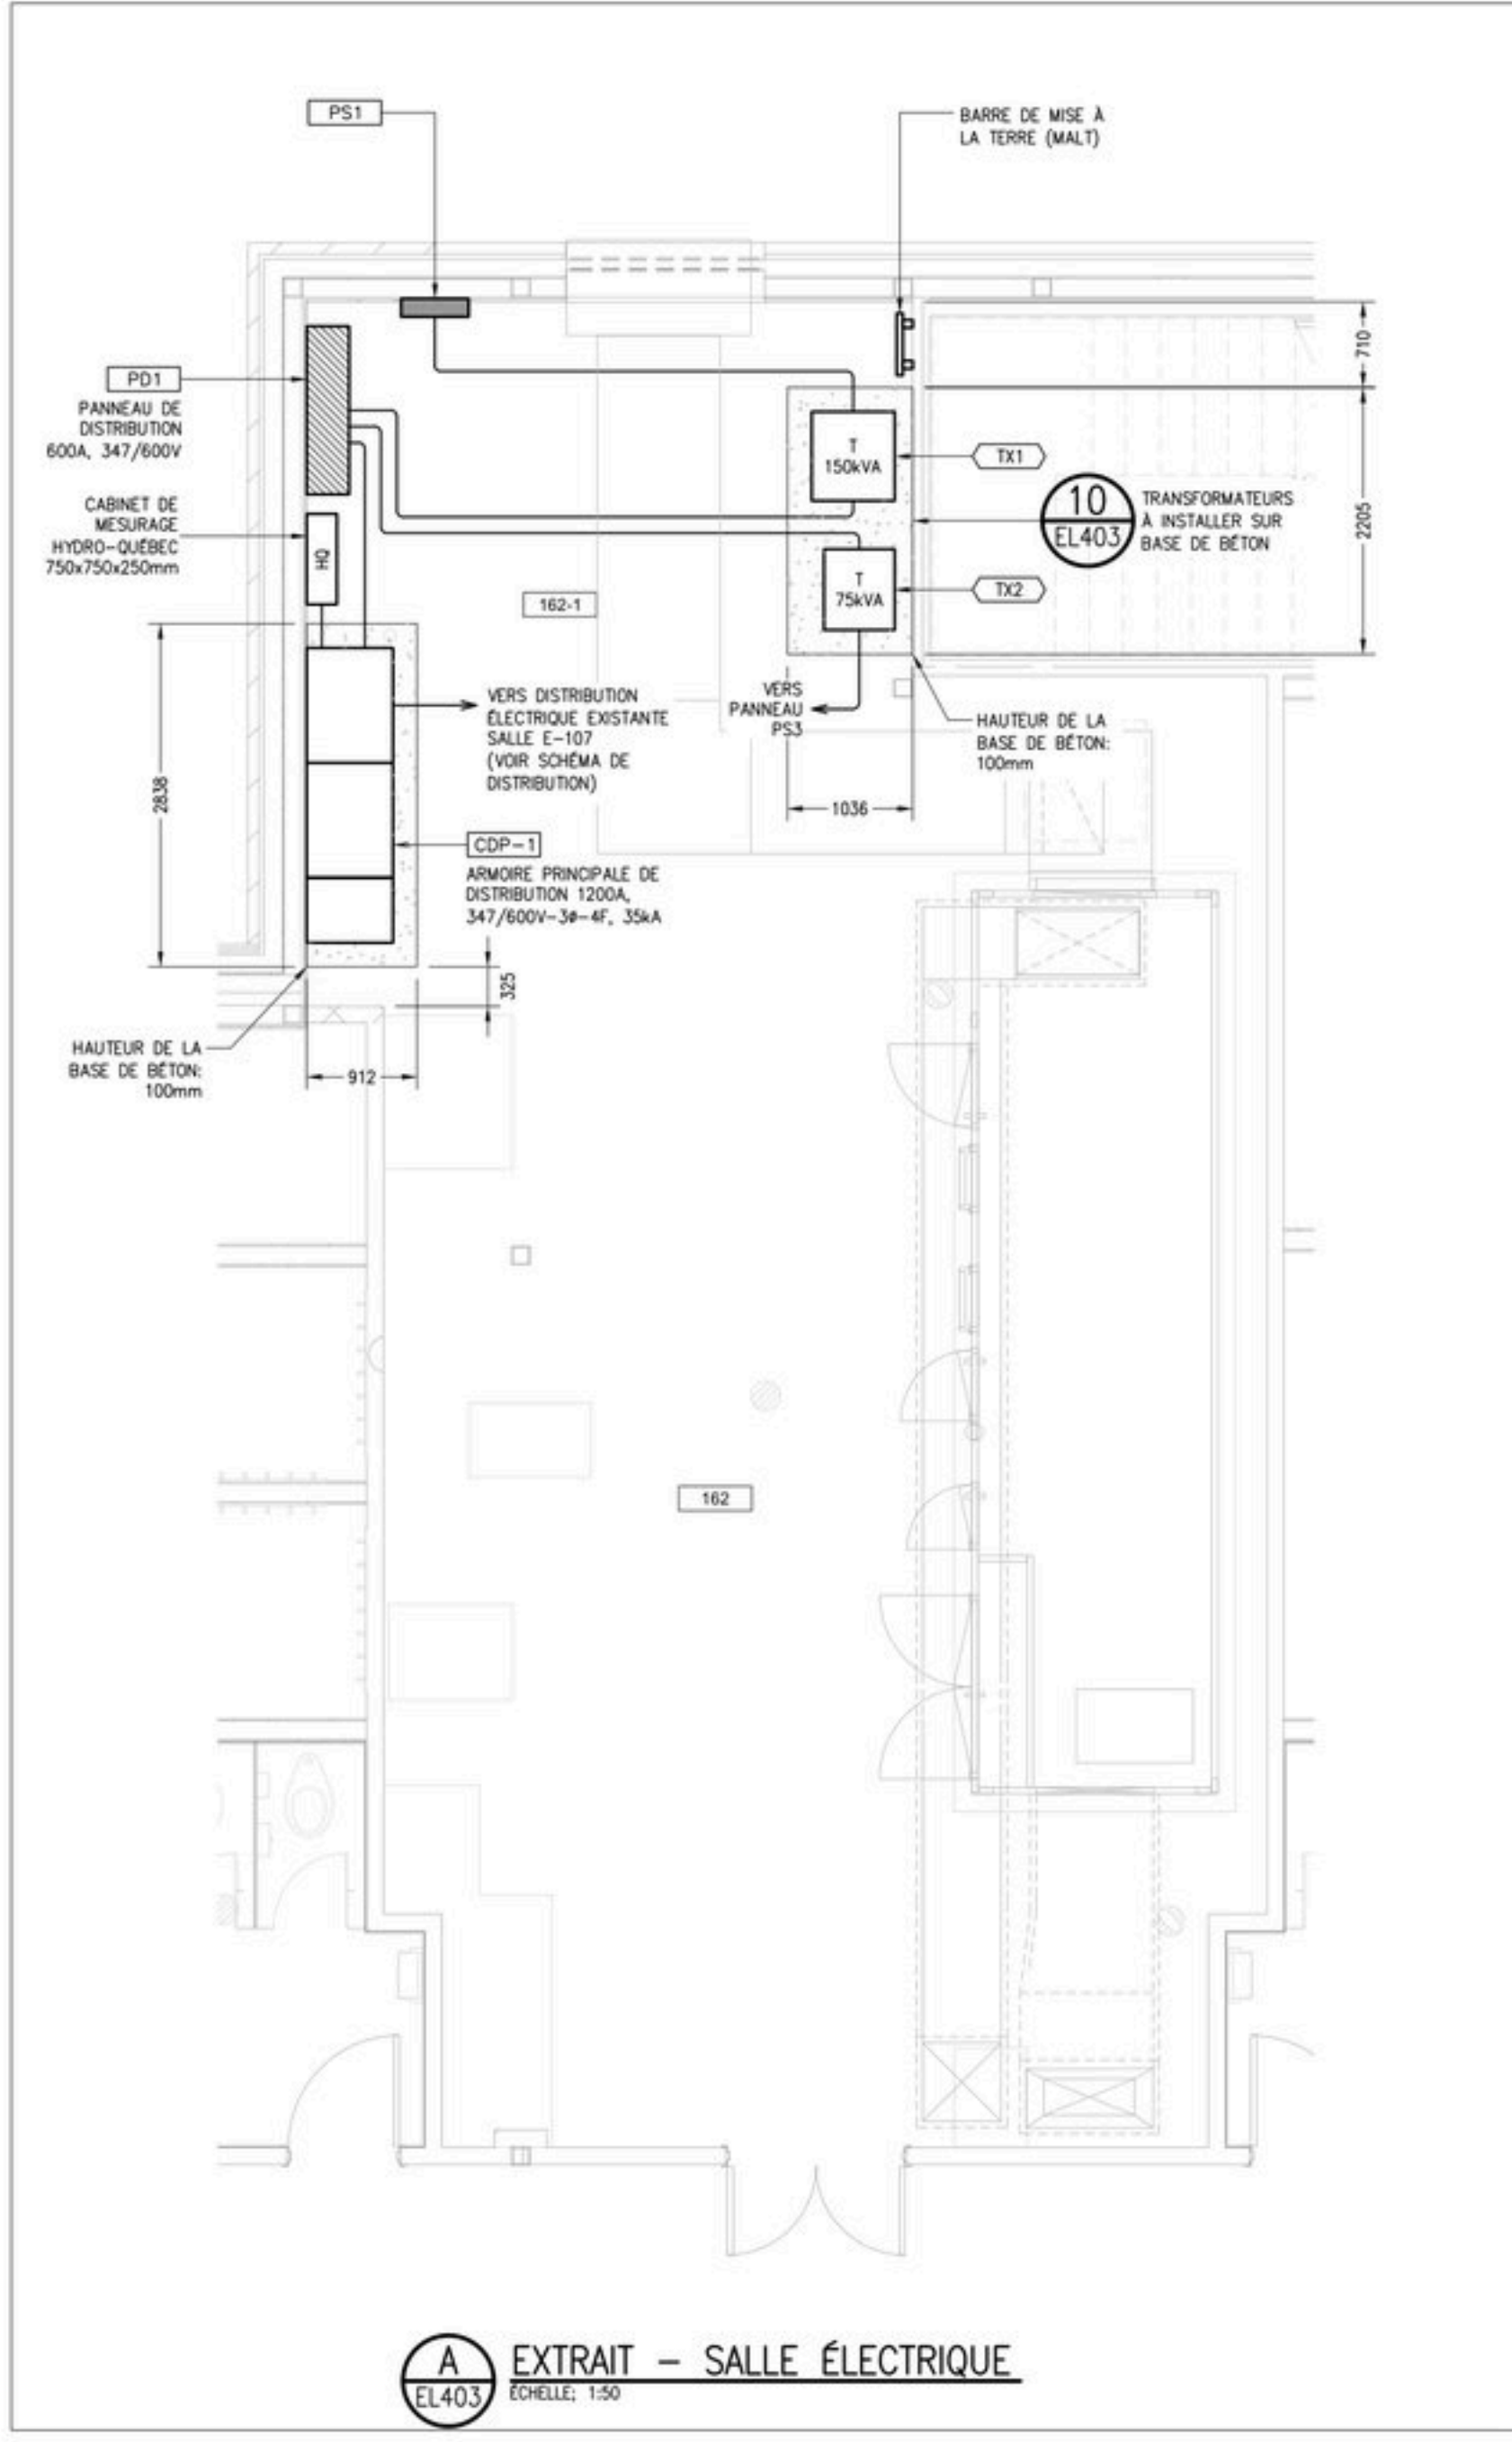


NOTES :

- TOUS LES CONDUITS, BOTES ÉLECTRIQUES ET CORDES DE TRACÉ SONT FOURNIS ET INSTALLÉS PAR L'ENTREPRENEUR ÉLECTRIEN.
- SAUF INDICATION CONTRAIRE, TOUS LES CONDUITS SONT DE GROSSEUR 21mm (3/4").
- TOUS LES COMPOSANTES DE CONTRÔLE D'ACCÈS SONT FOURNIS PAR D'AUTRES.
- LES HAUTEURS DE MONTAGE, QUANTITÉS ET EMBLEMES PRÉCIS DES COMPOSANTES DE CONTRÔLE D'ACCÈS SONT À COORDONNER AVEC LA DIVISION ARCHITECTURE ET LE PROPRIÉTAIRE.


13 PRINCIPÉ D'INSTALLATION DE CONTRÔLE D'ACCÈS

ÉCHELLE : AUCUNE

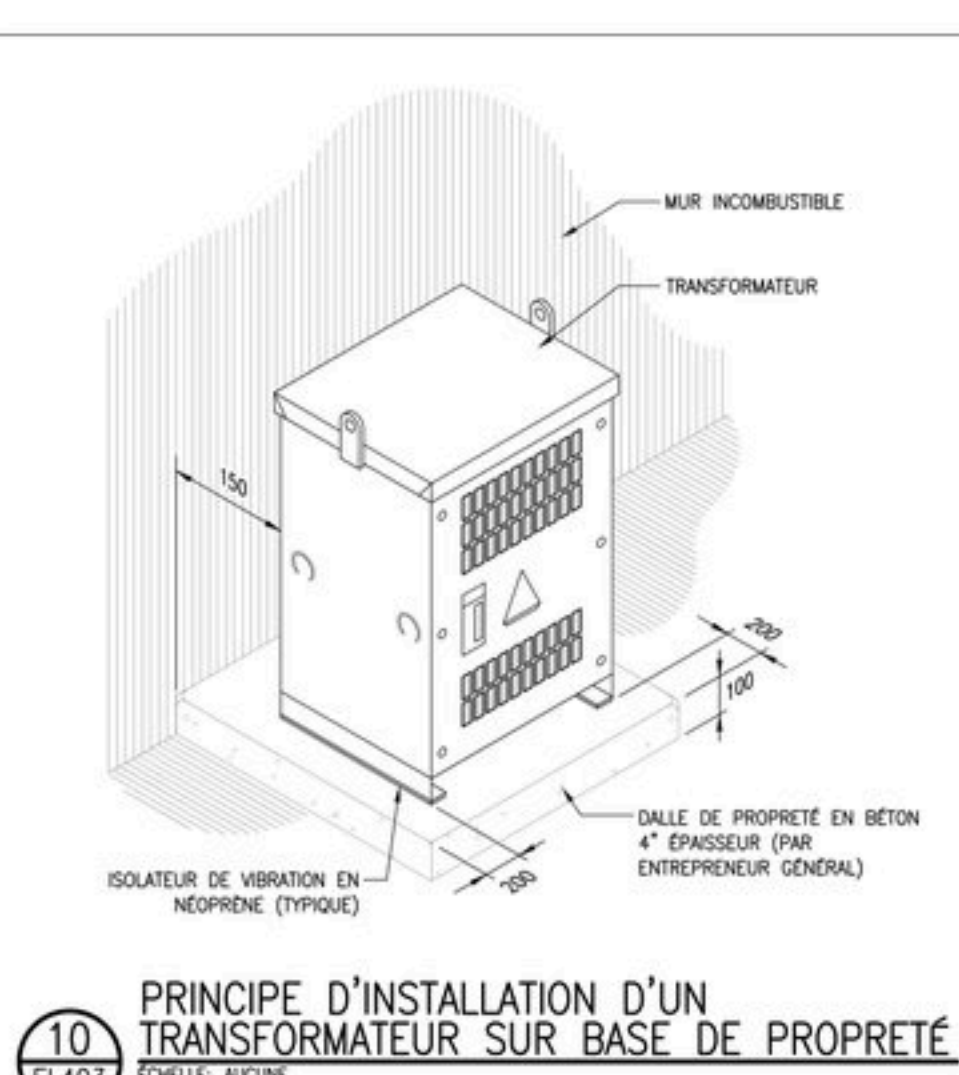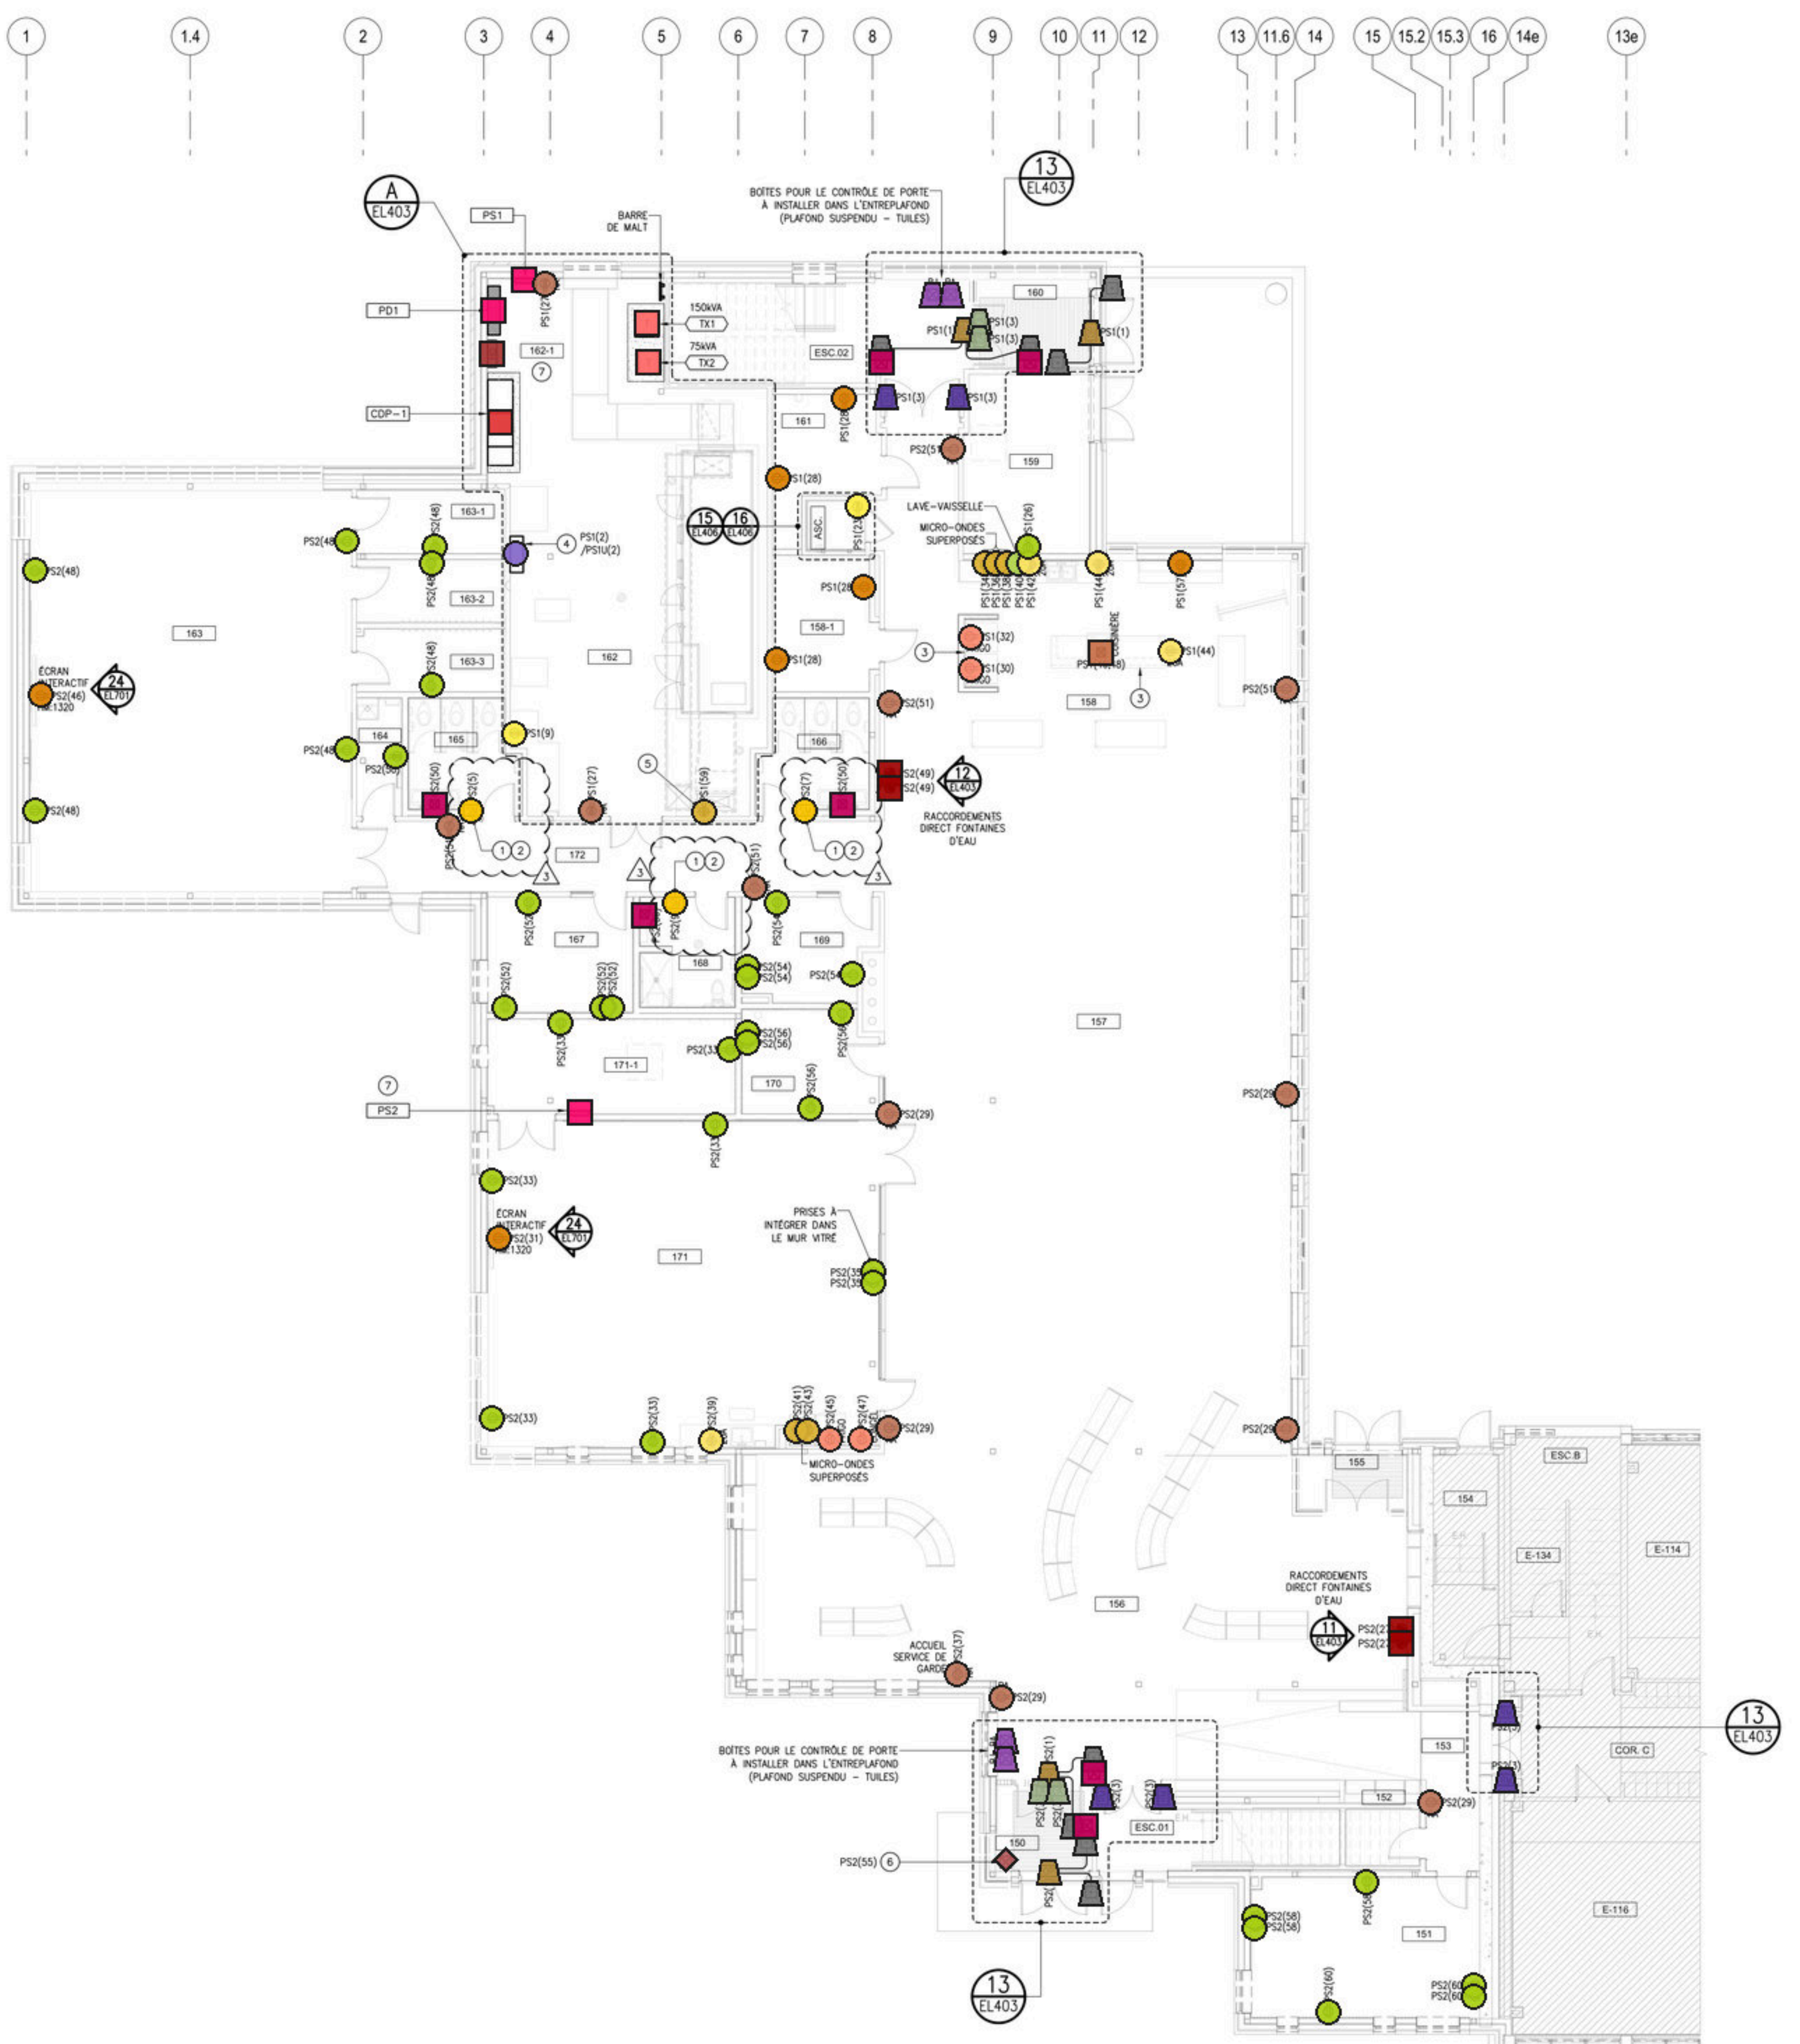


10 PRINCIPÉ D'INSTALLATION D'UN TRANSFORMATEUR SUR BASE DE PROPRIÉTÉ

ÉCHELLE : AUCUNE

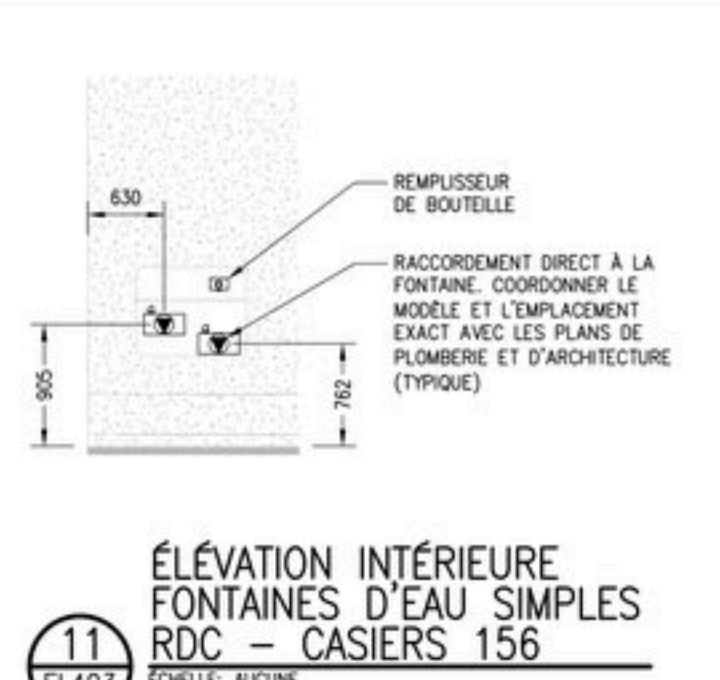

11 ÉLÉVATION INTÉRIEURE FONTAINES D'EAU SIMPLES RDC - CASIERS 156

ÉCHELLE : AUCUNE

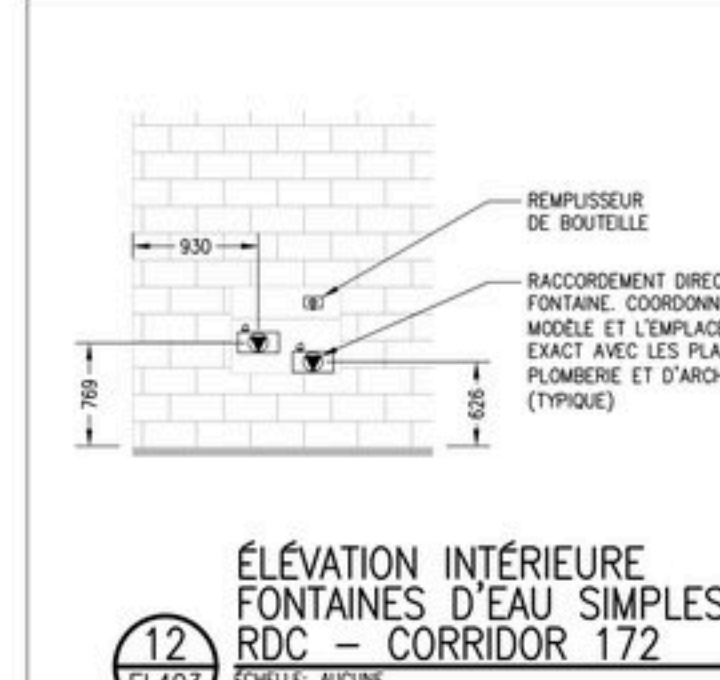

12 ÉLÉVATION INTÉRIEURE FONTAINES D'EAU SIMPLES RDC - CORRIDOR 172

ÉCHELLE : AUCUNE

- A) SAUF INDICATION CONTRAIRE, TOUT APPAREILLAGE REPRÉSENTÉ EN TRAITS POINTILLÉS SUR CE PLAN EST EXISTANT CONSERVÉ. SE RÉFÉRER AUX INDICES POUR DES DÉTAILS SUR LA NATURE DES TRAVAUX.
- B) SAUF INDICATION CONTRAIRE, TOUT APPAREILLAGE REPRÉSENTÉ EN TRAITS CONTINUS SUR CE PLAN EST NOUVEAU, EXISTANT MODIFIÉ OU EXISTANT DÉPLACÉ. SE RÉFÉRER AUX INDICES POUR DES DÉTAILS SUR LA NATURE DES TRAVAUX.
- C) AUCUN PERÇEMENT N'EST PERMIS DANS LES MURS DES ESCALIERS À MOINS QUE CELA NE DÉRIVE DES ESCALIERS.

- ① INTERVERROUILLAGE DU DÉMARRAGE DU VENTILATEUR VH-01 CELUI DE LA HOTTE H-01. LE DÉMARRAGE DE LA HOTTE ET DU VENTILATEUR VH-01 DOIT SE FAIRE À L'AIDE DU BOUTON ACTIONNEUR PRÉSENT SUR LA HOTTE H-01.
- ② PRISE ÉLECTRIQUE POUR L'ALIMENTATION DE L'ADOUCEUR D'EAU, À INSTALLER À 40cm MAXIMUM DE L'APPAREIL. COORDONNER LA HAUTEUR D'INSTALLATION DE LA PRISE AVEC SELON LES BESOINS EN MÉCANIQUE.
- ③ POMPE D'APPONT DU SYSTÈME DE PROTECTION INCENDIE. POSITION EXACTE À COORDONNER AU CHANTIER.

- ◆ Chauffage AC1 5kW (1)
- ◆ Chauffage AC2 2kW (1)
- ◆ Chauffage AC2 3kW (1)
- ◆ Chauffage AC2 4kW (1)
- ◆ Chauffage AC2 5kW (1)
- ◆ Chauffage P3 1kW (3)
- Raccordement boîtier contrôle valves (1)
- Raccordement chaudière électrique (1)
- Raccordement chauffe-eau (1)
- Raccordement moteur (6)
- Raccordement panneau régulation (1)
- Raccordement pompe (8)
- Raccordement thermopompe (14)
- Raccordement ventilateur (6)
- Raccordement éclairage UR-01 (1)
- Sectionneur 30A (21)

HÉLOÏSE
THIBODEAU
ARCHITECTE

gbi

LIEFDESIGN

CE DOCUMENT NE DOIT
PAS ÊTRE UTILISÉ À DES FINS
DE CONSTRUCTION

	C.B.	C.S.	2026.07.02
2 POUR ADDENDA N° 2	C.B.	C.S.	2024.08.24
1 POUR ADDENDA N° 1	C.B.	C.S.	2024.08.24
0 POUR APPEL D'OFFRES	C.B.	C.S.	2026.06.15
Emissions/Révisions	Par	Appr.	A.A.A.M.M.

Norm fichier: 157103764-300-300-El-D-401-404 SER1.DWG

Chatalein St-Amour, ing.	Carl Blanchard
Préparé	Dessiné
Chatalein St-Amour, ing.	Simon Pellerier, ing.
Vérifié	Chargé de projet

Sceaux



2026-07-
Logo Client/Projet



Client/Project

COMMISSION SCOLAIRE RIVERSIDE (CSR)
ÉCOLE WILLIAM LATTER
AGRANDISSEMENT ET RÉAMÉNAGEMENT

1300 rue Barré, Chambly, QC, J3L 2V4

Titre
ÉLECTRICITÉ
RACCORDEMENTS MÉCANIQUES
ET CHAUFFAGE - REZ-DE-CHAUSSIÉE


N° Projet	Échelle
-----------	---------

157103764 1:100

Émis./Rév. Feuille	N° dessin
0 14 de 31	71404

2 16 de 31 **EL404**

EL404

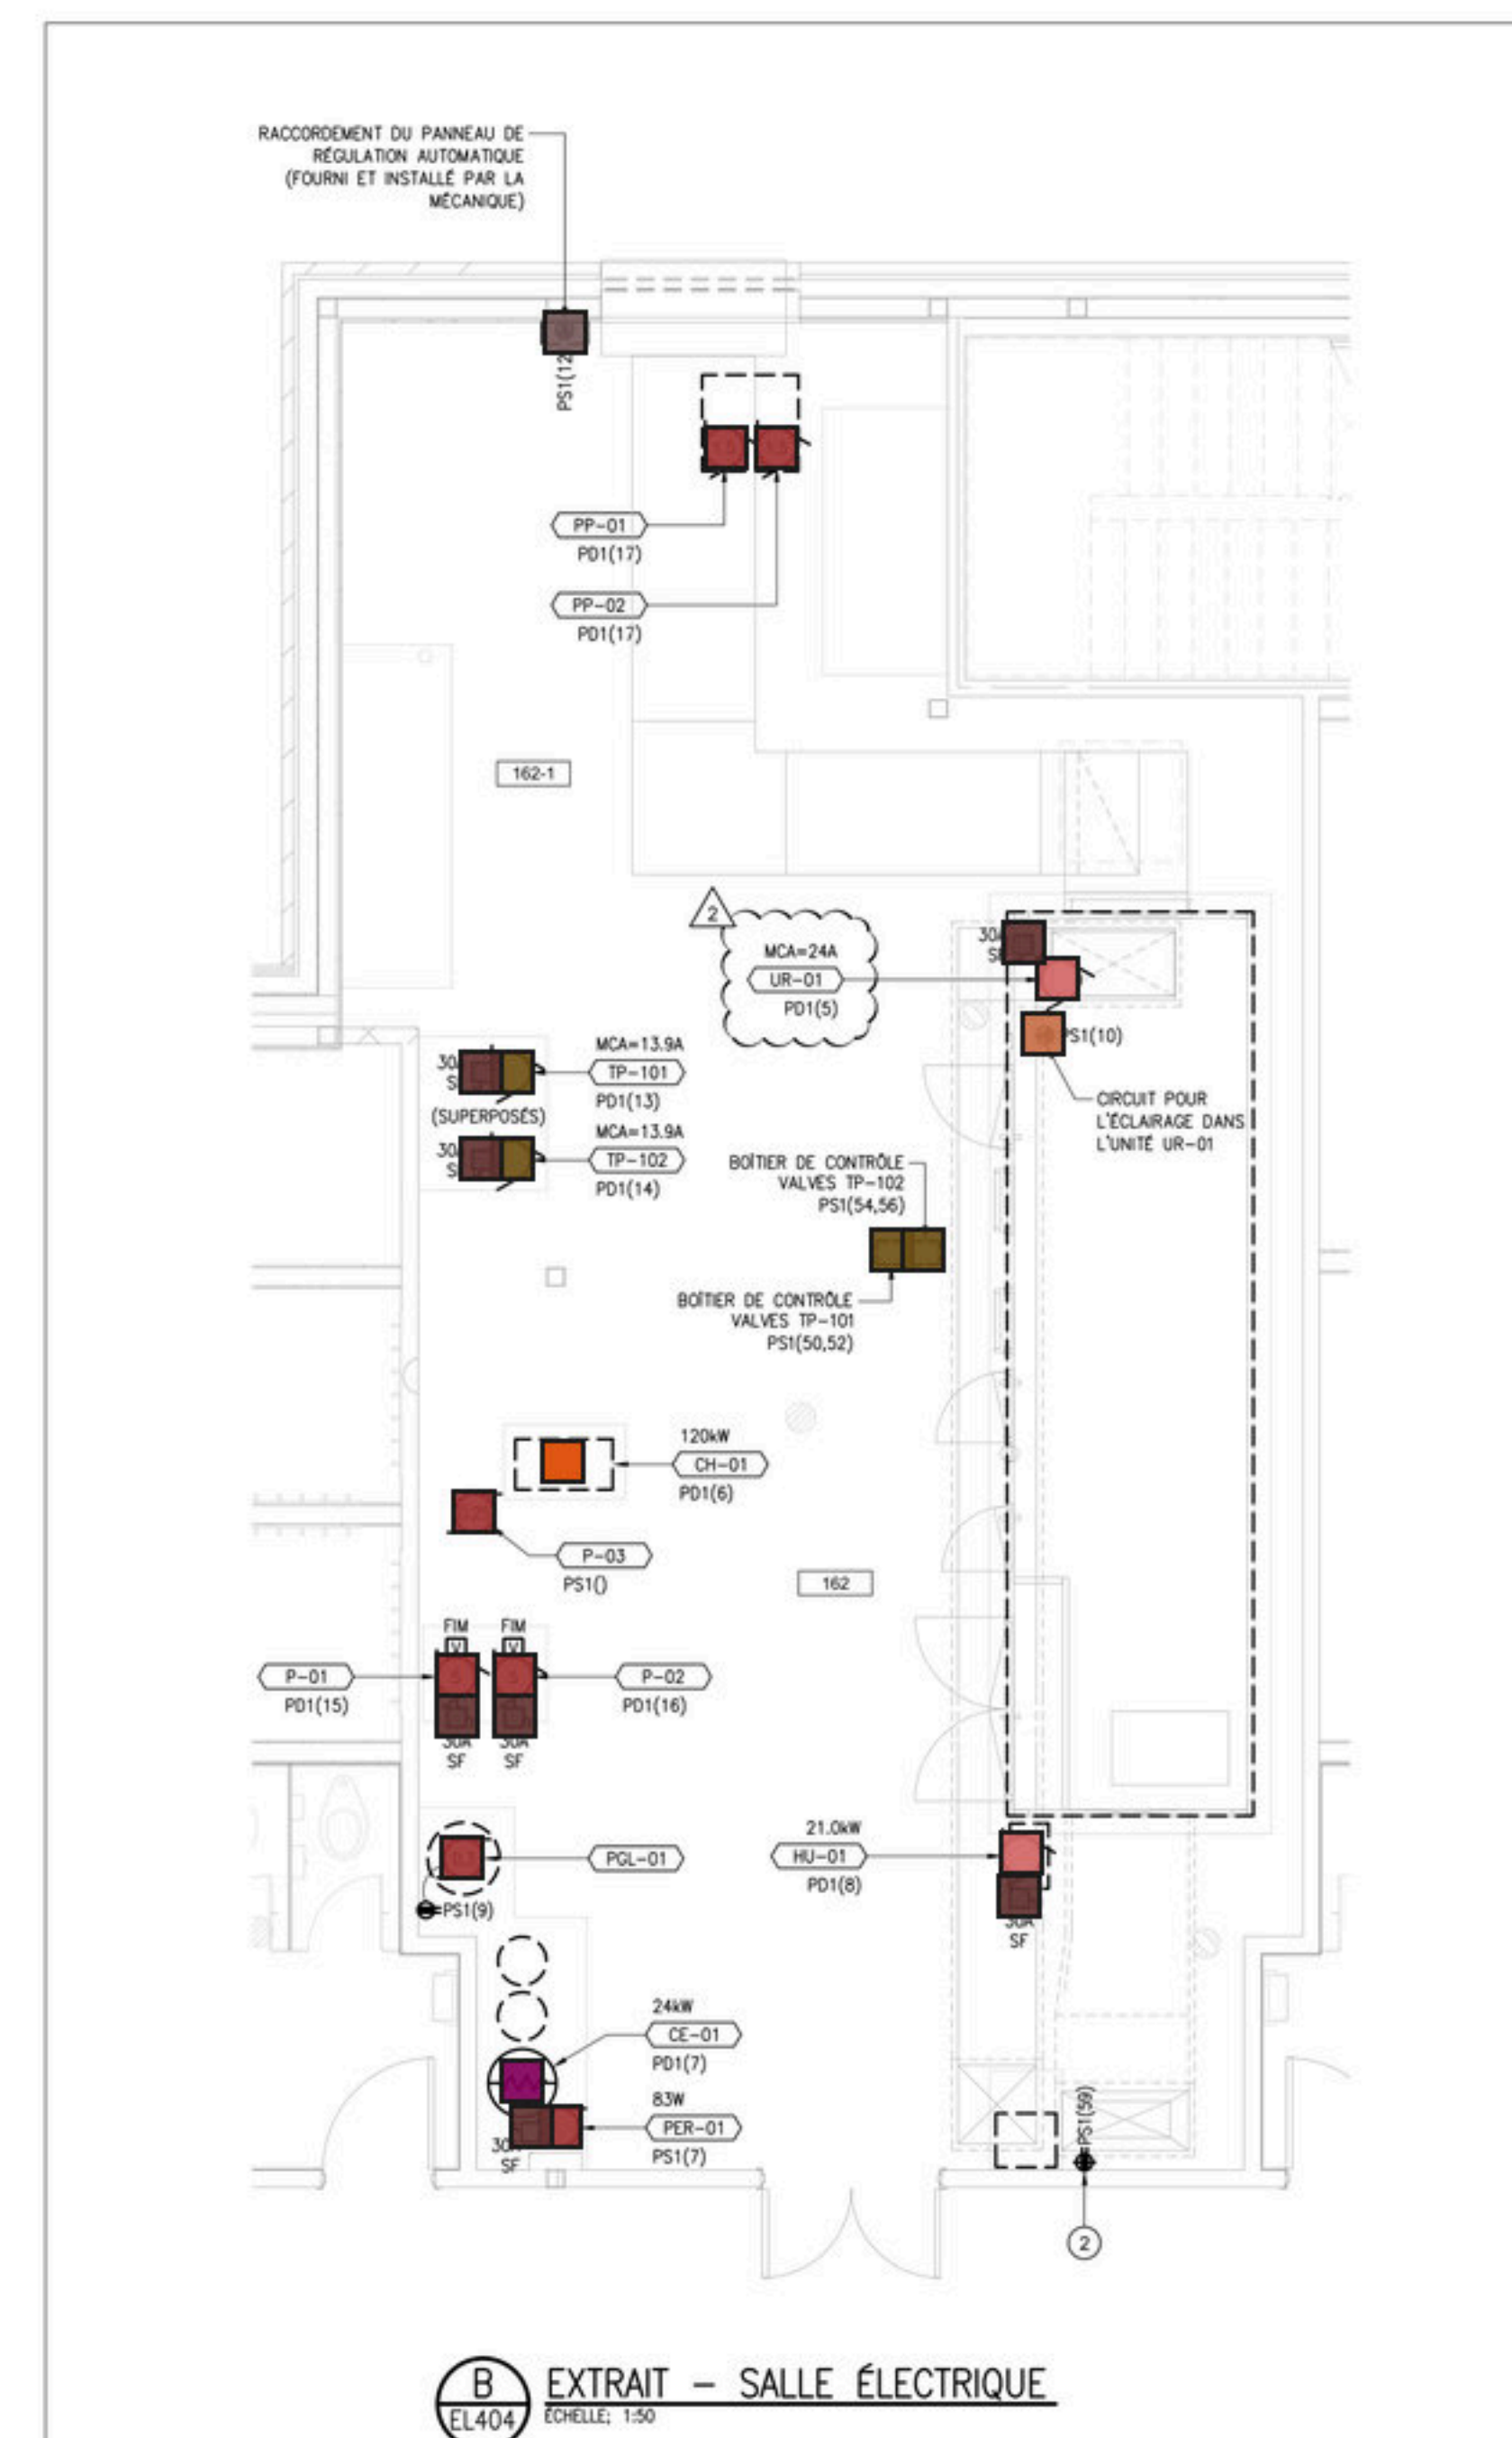


MEZ-de-chaussee - ÉTOIANT

E-101	RECEPTION
E-102-1	DIRECTION DE REUNION
E-102-2	SALE
E-103	SECURITAT
E-103-1	LOCAL SANTE
E-104	REUNION
E-105	DYNAMIE
E-105-1	REUNION
E-105-2	DEPOT CHAMISE
E-105-3	CHAMISE DYNAMIE
E-105-4	VESTIARIE CHAMISE
E-105-5	DYNAMIE CHAMISE
E-106	SALÉ ELECTROQUE PRINCIPALE
E-106-1	PERSONNEL
E-107	DEPOT
E-107-1	CHAMISE
E-108-3	W.C.
E-109	CHAMISE
E-110	CHAMISE
E-111	BURSE MATERNELLE
E-112	TOILETTES GARÇONS
E-113	TOILETTES FILLES
E-114	CLASSE
E-115	CLASSE
E-116	CLASSE
E-117	MUSIQUE
E-118-1	LOCAL D'ENTRETIENMENT
E-118-2	ENTRETIENMENT
E-118-3	PNE
E-119	CLASSE
E-120	CLASSE
E-121	CLASSE
E-122	CLASSE
E-123	TOILETTES FILLES
E-124	CHAMISE
E-125	TOILETTES GARÇONS
E-126	CLASSE
E-127	CLASSE
E-128	CLASSE
E-129	CLASSE
E-130	CLASSE
E-131	SALÉ TELECOM
E-132-1	DEPOT
E-132-2	BURSE MATERNELLE
E-132-3	W.C.
E-133	BURSE MATERNELLE

REZ-DE-CHAUSSEE - AGRANDISSEMENT

150	VESTIBULE 01
151	BUREAU ET VESTIBULE 5
152	ARCHIVES
153	PALIER
154	ISSUE
155	VESTIBULE 02
156	CASIER
157	ESPACE ONIVERS - SDC
158	CUISINE
158-1	DEPOT 01
159	DEPOT EXTÉRIEUR
160	VESTIBULE 03
161	DEPOT 02
162	SALLE MÉCANIQUE
163	SALLE ÉLECTRIQUE
163	SALLE DE MOTRICITÉ
163-1	DEPOT MOTRICITÉ
163-2	VESTIBULE DE MOTRICITÉ
163-3	VESTIBULE 02 MOTRICITÉ
164	CONGÈRES
164	TOLLIETTES ELLES
166	TOLLIETTES GARÇONS
167	PNE
168	W.C. UNIVERSELLE ET D
169	PNE
170	SALLE POLYVALENTE -
171	SALLE SALLE POLYVALENTE
172	CORRIDOR 01
ASC	MONTÉ-CHARGE
ESC.01	ESCAUER 01
ESC.02	ESCAUER 02

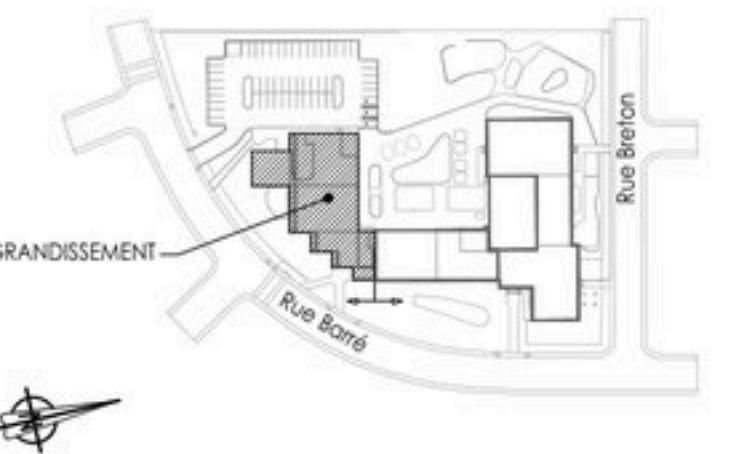

NOTES GÉNÉRALES :

- A) SAUF INDICATION CONTRAIRE, TOUT APPAREILLAGE REPRÉSENTÉ EN TRACÉ POINTILLÉ SUR CE PLAN EST EXISTANT CONSERVÉ. SE RÉFÉRER AUX INDICES POUR DES DÉTAILS SUR LA NATURE DES TRAVAUX.
- B) SAUF INDICATION CONTRAIRE, TOUT APPAREILLAGE REPRÉSENTÉ EN TRACÉ CONTINU SUR CE PLAN EST NOUVEAU, EXISTANT MODIFIÉ OU EXISTANT DÉPLACÉ. SE RÉFÉRER AUX INDICES POUR DES DÉTAILS SUR LA NATURE DES TRAVAUX.
- C) AUCUN PERÇEMENT N'EST PERMIS DANS LES MURS DES ESCALIERS À MOINS QUE CELA NE DÉSERVIR LES ESCALIERS.

NOTES SPÉCIFIQUES :

- ① RACCORDEMENT DE LA BARRE D'ALIMENTATION MULTIPRISE DU RÂTELIER TÉLÉCOM (VOIR PLANS TÉLÉCOM).
- ② SÈCHE-MAINS HAUTE VÉLOCITÉ XLERATOR AVEC CHAUFFAGE, MODÈLE XL-C-111110-120V. COORDONNER L'EMPLACEMENT EXACT AVEC L'ARCHITECTURE.
- ③ MINI-ONDULEUR DE 1440W, MODÈLE EM-1440/60 DE ENERGO-LITE, POUR L'ALIMENTATION DES APPAREILS. DÉTAILS DE SECURITE ET DE SIGNALISATION DIMENSIONS 24" x 40.75" x 14.5". CIRCUIT D'ENTREE PS4(1), CIRCUIT DE SORTIE PS4(1).
- ④ LOCAL DOL. PRÉVOIR RACCORD ÉTANCHE ET CAPOT ANTI-ÉCOUTILLANT AFIN QUE LE PANNEAU SOIT À L'ÉPREUVE DES INTÉRIEURS.
- ⑤ POSITION ET HAUTEUR DE MONTAGE À COORDONNER AVEC L'ARCHITECTURE.

Légende — EL405_2 (88 marques)

- Boîte de jonction murale (1)
- Mini-onduleur 1440W (1)
- Panneau distribution (2)
- Prise double (48)
- Prise double 20A (2)
- Prise double 20A RA (8)
- Prise double DDFT (2)
- Prise double comptoir (11)
- Prise double comptoir 20A (2)
- Prise micro-onde (2)
- Prise réfrigérateur (1)
- Raccordement barre multiprise télécom (1)
- Raccordement fontaine d'eau (2)
- Retenue magnétique (4)
- Sèche-mains (1)


LISTE DES PIÈCES :

NIVEAU 2 - EXISTANT

- E-201 DÉPÔT
- E-202 CLASSE
- E-203 CLASSE
- E-204 CLASSE
- E-205 CLASSE
- E-206 TOILETTES GARÇONS
- E-207 TOILETTES FILLES
- E-208 CLASSE
- E-209 CLASSE
- E-210 CONCERNERIE
- E-211 CLASSE
- COR. D CORRIDOR D
- ESC. A ESCALIER A
- ESC. B ESCALIER B

NIVEAU 2 - AGRANDISSEMENT

- 250 BUREAU DIRECTEUR ADJOINT
- 251 CASIERS
- 252 CORRIDOR 02
- 252-1 DÉPÔT
- 252-4 COLLABO
- 252-5 MÉCANIQUE ASCENSEUR
- 253-6 DÉPÔT
- 253 CLASSE
- 253-1 RANGEMENT CLASSE
- 254 CLASSE
- 254-1 RANGEMENT CLASSE
- 255 CLASSE
- 255-1 RANGEMENT CLASSE
- 256 W.C. DU PERSONNEL
- 257 SALLE DU PERSONNEL
- 258 LOCAL À DÉTERMINER
- 259 ARTS PLASTIQUES
- 259-1 ENTREPOSAGE ARTS
- 259-2 ZONE NETTOYAGE ARTS
- 259-3 ZONE TECHNOLOGIE ARTS
- 260 CARREFOUR D'APPRENTISSAGE
- 260-1 MULTIMÉDIA
- 260-1-1 SALLE TÉLÉCOM
- 260-2 DÉPÔT
- 260-3 LOCAL DE RECHARGE
- 260-4 MONTÉ-CHARGE
- ESC. 01 ESCALIER 01
- ESC. 02 ESCALIER 02

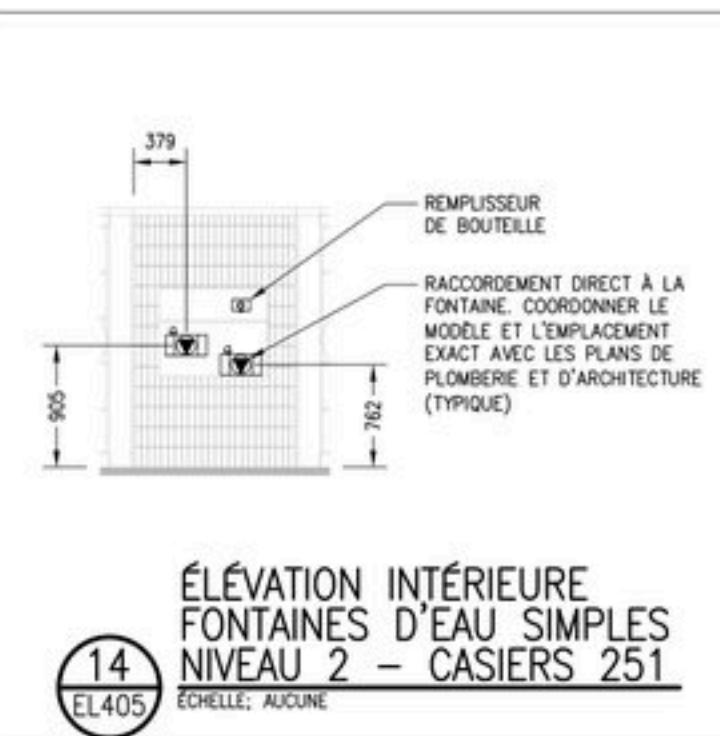

Plan a

Plan c

Archit

 HÉLOÏSE
THIBODEAU
ARCHITECTE

— I N C
395, avenue Beaumont Montréal (Québec)

Structure et civil

gbi

Discussion

agence **RELIEFDESIGN**

CE DOCUMENT NE DOIT
PAS ÊTRE UTILISÉ À DES FINS
DE CONSTRUCTION

[illegible]

Norm fichier: 157103764-300-300-EL-D-501-502 All.DWG 2024.04.0

Chateau St-Amour, Inc.	Carl Blanchard
------------------------	----------------

© 2006 The Authors

Seal



2026-07-0

Logg Client/Proiet



Client/Project

Client/Project _____

ÉCOLE WILLIAM LUTTER

ÉCOLE WILLIAM LUTTER

ÉCOLE WILLIAM LUTTER

1300 rue Barré, Chambly, QC J3L 2V4

Titre
ÉLECTRICITÉ
ALARME INCENDIE - REZ-DE-CHAUSSÉE
AGRANDISSEMENT - CONSTRUCTION

N° Projet	Échelle
-----------	---------


Émis./Rév. Feuille

Émis./Rév. Feuille

2

22 de 31

EL502

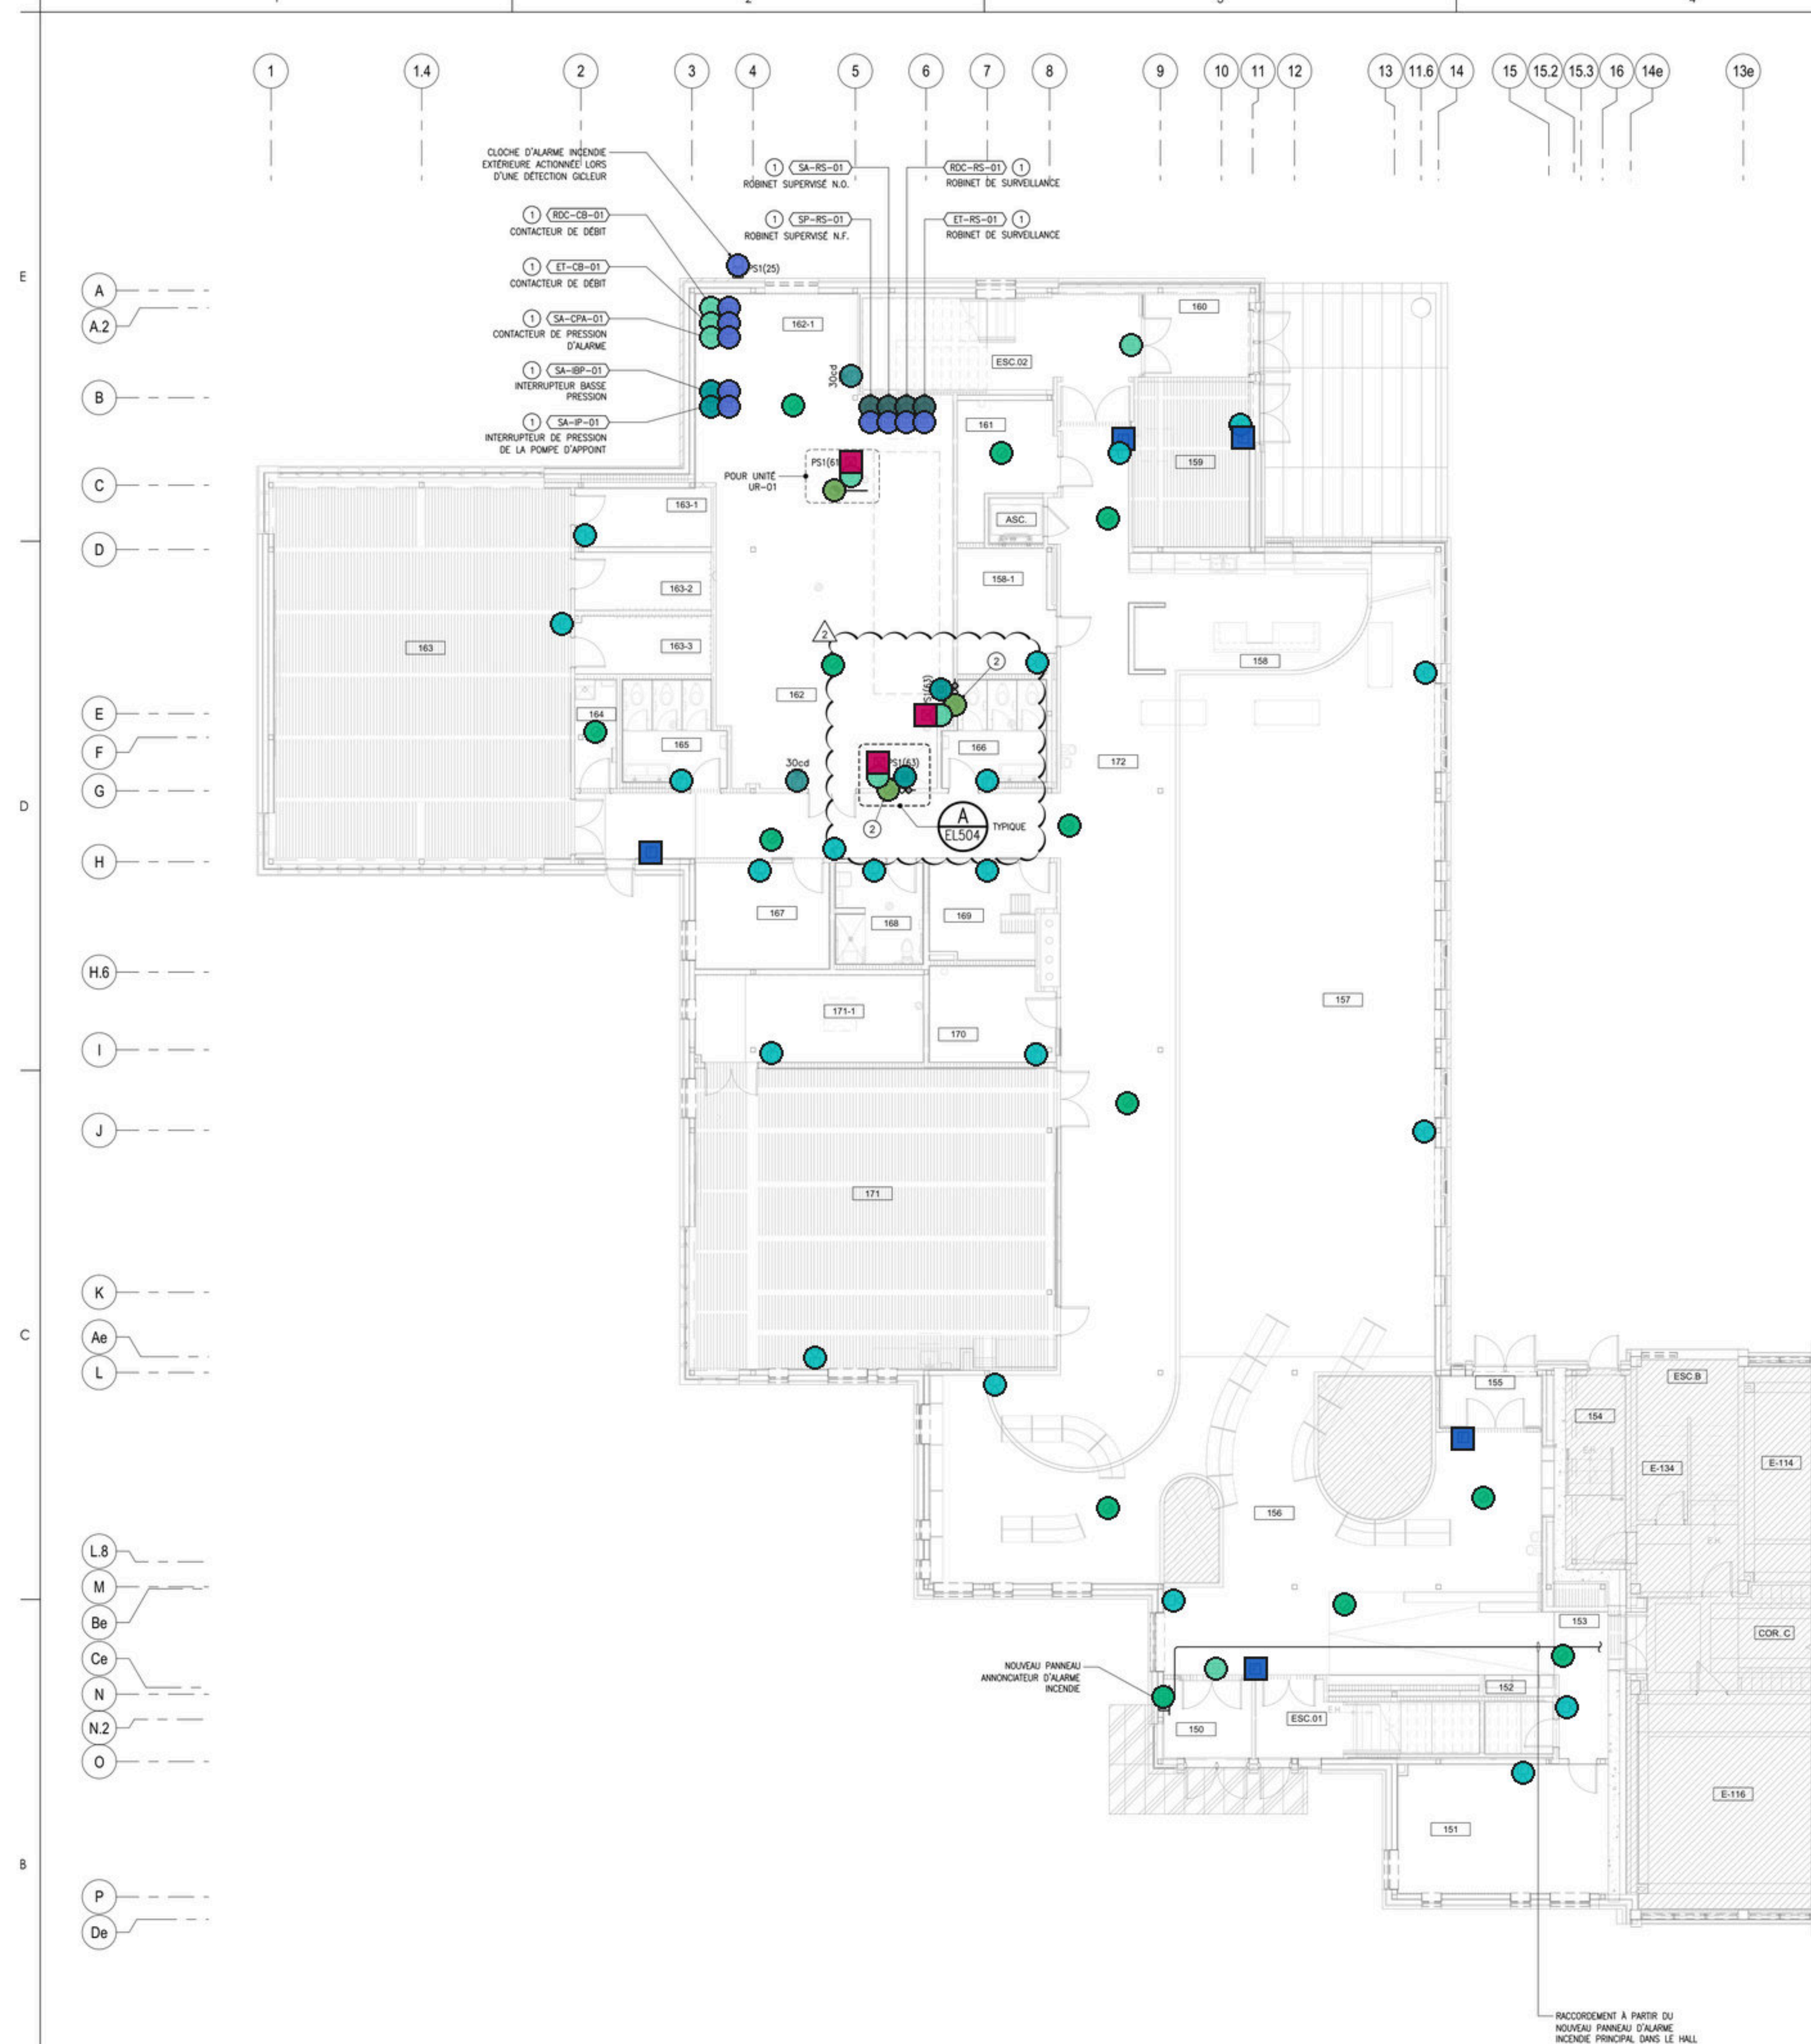

NOTES GÉNÉRALES :

- A) SAUF INDICATION CONTRAIRE, TOUT APPAREILLAGE REPRÉSENTÉ EN TRAITS POINTILLÉS SUR CE PLAN EST EXISTANT CONSERVÉ. SE RÉFÉRER AUX INDICES POUR DES DÉTAILS SUR LA NATURE DES TRAVAUX.
- B) SAUF INDICATION CONTRAIRE, TOUT APPAREILLAGE REPRÉSENTÉ EN TRAITS CONTINUS SUR CE PLAN EST NOUVEAU, EXISTANT, MODIFIÉ OU EXISTANT DÉPLACÉ. SE RÉFÉRER AUX INDICES POUR DES DÉTAILS SUR LA NATURE DES TRAVAUX.
- C) AUCUN PERÇEMENT N'EST PERMIS DANS LES MURS DES FUSCAIERS À MOINS QU'IL N'Y AIT DESSEIN DES FUSCAIERS.

NOTES SPÉCIFIQUES :

- ① L'EMPLACEMENT EXACT DES DIFFÉRENTES COMPOSANTES A COORDONNER AU CHANTIER. SE RÉFÉRER AUX DÉTAILS DE PROTECTION INCENDIE POUR LES ÉLÉMENTS A RACCORDER AU RANNEAU D'ALARME INCENDIE.
- ② LE DÉTECTEUR DE PRODUITS DE COMBUSTION DANS LA GAINÉ DE VENTILATION DOIT ÊTRE INSTALLÉ EN AVANT DU VOILET COUPE-FEU/FUMÉE, SUIVANT LE SENS DE L'ÉCOULEMENT DE L'AIR.

Légende — EL502 2 (72 marques)

- Boîte de jonction murale (3)
- Cloche alarme extérieure (1)
- Détecteur fumée (12)
- Détecteur fumée conduit (3)
- Interrupteur débit gicleurs (3)
- Interrupteur pression gicleurs (2)
- Interrupteur valve surveillée (4)
- Klaxon alarme (20)
- Klaxon-stroboscope (2)
- Module adressable MA (9)
- Panneau annonciateur (1)
- Poste manuel (5)
- Relais adressable RA (5)
- Témoin visuel (2)

LISTE DES PIÈCES :

E-102	REZ-DE-CHAUSSEE - EXISTANT	E-132-1-1	WC
E-101	RECEPTION	E-133	DEPOT
E-102-1	SALLE DE RENONON	E-134	DEPOT
E-103	SECURITE	COR A	CORRIDOR A
E-103-1	SECURITARIAT	COR B	CORRIDOR B
E-104	SECURITE	COR C	CORRIDOR C
E-104-1	SECURITE	ESCA A	ESCALIER A
E-104-2	PARTIERE	ESCA B	ESCALIER B
E-105	SECURITE	HALL	HALL D'ENTREE
E-105-1	BUREAU CUNYASE	SAC A-1	VESTIBULE A-1
E-105-2	DEPOT CUNYASE	SAC B	VESTIBULE A-2
E-105-3	DEPOT CUNYASE	SAC C	VESTIBULE B
E-105-4	VESTIBULES CHAUSSEE	SAC D	VESTIBULE B
E-106	SECURITE		
E-107	SALLE ELECTRIQUE		
E-108	SECURITE DU PERSONNEL		
E-108-1	SECURITE		
E-108-2	SECURITE		
E-108-3	W.C.		
E-109	SECURITE		
E-110	CLASSE		
E-110-1	CLASSE MATERNELLE		
E-111	TOILETTES GARCONS		
E-111-1	TOILETTES FILLES		
E-112	CLASSE		
E-112-1	CLASSE		
E-113	CLASSE		
E-113-1	CLASSE		
E-114	CLASSE		
E-114-1	CLASSE		
E-115	MOISSE		
E-116	LOGICIEL D'ENREGISTREMENT		
E-116-1	LOGICIEL		
E-117	RANGEMENT		
E-118	CLASSE		
E-118-1	CLASSE		
E-119	CLASSE		
E-120	CLASSE		
E-121	CLASSE		
E-122	CLASSE		
E-123	TOILETTES FILLES		
E-124	CLASSE		
E-125	TOILETTES GARCONS		
E-126	CLASSE		
E-127	PNE		
E-128	CLASSE		
E-129	CLASSE		
E-130	CLASSE		
E-131	SALLE TELECOM		
E-132	DEPOT		
E-132-1	DEPOT		
E-132-2	DEPOT		
E-132-70	DEP		

REZ-DE-CHAUSSÉE - AGRANDISSEMENT

MATRICE DE PROGRAMMATION - ALARME INCENDIE							
TYPE DE COMMANDE	SIGNAL TRANSMIS AU SYSTÈME D'ALARME INCENDIE	FONCTIONS AUXILIAIRES					FONCTIONS ADDITIONNELLES
		PORTES AVEC VERROUS ÉLECTROMAGNÉTIQUES	ASCENSEURS ET MONTE-CHARGES POURVUS DE DISPOSITIF AUTOMATIQUE DE RAPPEL	PORTES COUPE-FEU NORMALEMENT OUVERTES	OUVRE-PORTE AUTOMATIQUE INSTALLÉ SUR UNE PORTE DE SÉPARATION COUPE-FEU	REGISTRE COMBINÉ COUPE-FEU/FUMÉE	
Activation d'un poste manuel	ALARME : Signal d'alarme transmis dans l'ensemble du bâtiment. (CCQ 3.2.4.4-1)	Déverrouillage automatique sauf pour les zones de détention cellulaire ou à sortie contrôlée (CCQ 3.4.6.16, 4) et 5) et (ULC-573-20.1.3)	Rappel des ascenseurs au niveau de rappel désigné (CCQ 3.2.4.14-4) et 3.2.4.11-4)	Règlement automatique des portes dans l'ensemble du bâtiment, sauf exception permise au paragraphe 6 (CCQ 3.1.8.14-2a)	Désactivation du détecteur de mouvement et priorisation du système d'alarme incendie (ULC-573-19.2)	-	Service incendie doit être averti selon le type de bâtiment visé par l'article (CCQ 3.2.4.7)
Salle de machine d'ascenseurs, monte-charges et petits monte-charges & puits d'ascenseurs,	ALARME : Signal d'alarme transmis dans l'ensemble du bâtiment. (CCQ 3.2.4.4-1)	Déverrouillage automatique sauf pour les zones de détention cellulaire ou à sortie contrôlée (CCQ 3.4.6.16, 4) et 5) et (ULC-573-20.1.3)	Rappel des ascenseurs au niveau de rappel désigné (CCQ 3.2.4.14-4) et 3.2.4.11-4)	Règlement automatique des portes dans l'ensemble du bâtiment, sauf exception permise au paragraphe 6 (CCQ 3.1.8.14-2a)	Désactivation du détecteur de mouvement et priorisation du système d'alarme incendie (ULC-573-19.2)	-	Service incendie doit être averti selon le type de bâtiment visé par l'article (CCQ 3.2.4.7)
Hall du niveau de rappel d'ascenseurs	ALARME : Signal d'alarme transmis dans l'ensemble du bâtiment. (CCQ 3.2.4.4-1)	Déverrouillage automatique sauf pour les zones de détention cellulaire ou à sortie contrôlée (CCQ 3.4.6.16, 4) et 5) et (ULC-573-20.1.3)	Rappel des ascenseurs au niveau de rappel alternatif désigné (CCQ 3.2.4.14-4) et 3.2.4.11-4)	Règlement automatique des portes dans l'ensemble du bâtiment, sauf exception permise au paragraphe 6 (CCQ 3.1.8.14-2a)	Désactivation du détecteur de mouvement et priorisation du système d'alarme incendie (ULC-573-19.2)	-	Service incendie doit être averti selon le type de bâtiment visé par l'article (CCQ 3.2.4.7)
Porte coupe-feu maintenues ouvertes	ALARME : Signal d'alarme transmis dans l'ensemble du bâtiment. (CCQ 3.2.4.4-1)	Déverrouillage automatique sauf pour les zones de détention cellulaire ou à sortie contrôlée (CCQ 3.4.6.16, 4) et 5) et (ULC-573-20.1.3)	Rappel des ascenseurs au niveau de rappel désigné (CCQ 3.2.4.14-4) et 3.2.4.11-4)	Règlement automatique des portes dans l'ensemble du bâtiment, sauf exception permise au paragraphe 6 (CCQ 3.1.8.14-2a)	Désactivation du détecteur de mouvement et priorisation du système d'alarme incendie (ULC-573-19.2)	-	Service incendie doit être averti selon le type de bâtiment visé par l'article (CCQ 3.2.4.7)
Conduit d'alimentation d'air en ventilation	ALARME : Signal d'alarme transmis dans l'ensemble du bâtiment. (CCQ 3.2.4.4-1)	Déverrouillage automatique sauf pour les zones de détention cellulaire ou à sortie contrôlée (CCQ 3.4.6.16, 4) et 5) et (ULC-573-20.1.3)	Rappel des ascenseurs au niveau de rappel désigné (CCQ 3.2.4.14-4) et 3.2.4.11-4)	Règlement automatique des portes dans l'ensemble du bâtiment, sauf exception permise au paragraphe 6 (CCQ 3.1.8.14-2a)	Désactivation du détecteur de mouvement et priorisation du système d'alarme incendie (ULC-573-19.2)	-	Service incendie doit être averti selon le type de bâtiment visé par l'article (CCQ 3.2.4.7)
Ailleurs dans le bâtiment	ALARME : Signal d'alarme transmis dans l'ensemble du bâtiment. (CCQ 3.2.4.4-1)	Déverrouillage automatique sauf pour les zones de détention cellulaire ou à sortie contrôlée (CCQ 3.4.6.16, 4) et 5) et (ULC-573-20.1.3)	Rappel des ascenseurs au niveau de rappel désigné (CCQ 3.2.4.14-4) et 3.2.4.11-4)	Règlement automatique des portes dans l'ensemble du bâtiment, sauf exception permise au paragraphe 6 (CCQ 3.1.8.14-2a)	Désactivation du détecteur de mouvement et priorisation du système d'alarme incendie (ULC-573-19.2)	-	Service incendie doit être averti selon le type de bâtiment visé par l'article (CCQ 3.2.4.7)
Placé à moins de 1,5 m horizontalement du conduit ou des 2 côtés de l'ouverture de transfert d'air ou dans le conduit en aval du registre coupe-feu/coupe-fumée (CCQ 3.1.8.11-3)	ALARME : Signal d'alarme transmis dans l'ensemble du bâtiment. (CCQ 3.2.4.4-1)	Déverrouillage automatique sauf pour les zones de détention cellulaire ou à sortie contrôlée (CCQ 3.4.6.16, 4) et 5) et (ULC-573-20.1.3)	Rappel des ascenseurs au niveau de rappel désigné (CCQ 3.2.4.14-4) et 3.2.4.11-4)	Règlement automatique des portes dans l'ensemble du bâtiment, sauf exception permise au paragraphe 6 (CCQ 3.1.8.14-2a)	Désactivation du détecteur de mouvement et priorisation du système d'alarme incendie (ULC-573-19.2)	-	Service incendie doit être averti selon le type de bâtiment visé par l'article (CCQ 3.2.4.7)
Intercepteur de débit, gicleurs	ALARME : Signal d'alarme transmis dans l'ensemble du bâtiment. (CCQ 3.2.4.4-1)	Déverrouillage automatique sauf pour les zones de détention cellulaire ou à sortie contrôlée (CCQ 3.4.6.16, 4) et 5) et (ULC-573-20.1.3)	Rappel des ascenseurs au niveau de rappel désigné (CCQ 3.2.4.14-4) et 3.2.4.11-4)	Règlement automatique des portes dans l'ensemble du bâtiment, sauf exception permise au paragraphe 6 (CCQ 3.1.8.14-2a)	Désactivation du détecteur de mouvement et priorisation du système d'alarme incendie (ULC-573-19.2)	-	Service incendie doit être averti selon le type de bâtiment visé par l'article (CCQ 3.2.4.7)
Intercepteur pour valve supervisée, gicleurs	SUPERVISION : Signal visuel de surveillance à l'annunciateur (CCQ 3.2.4.9-3)	-	-	-	-	-	Service incendie doit être averti (CCQ 3.2.4.7 et 3.2.4.9-3)
Intercepteur pour basse ou haute pression	SUPERVISION : Signal visuel de surveillance à l'annunciateur (CCQ 3.2.4.9-3)	-	-	-	-	-	Service incendie doit être averti (CCQ 3.2.4.7 et 3.2.4.9-3)
Eau	SUPERVISION : Signal visuel de surveillance à l'annunciateur (CCQ 3.2.4.9-3)	-	-	-	-	-	Service incendie doit être averti (CCQ 3.2.4.7 et 3.2.4.9-3)
Air (compresseur)	SUPERVISION : Signal sonore de supervision	-	-	-	-	-	Service incendie doit être averti (CCQ 3.2.4.7 et 3.2.4.9-3)
En cas de défaillance (circuit ouvert, court-circuit ou fuite à la terre) du système d'alimentation du panneau d'alarme incendie, du circuit de déclenchement ou de signalisation des alarmes du dispositif anti-surcharge ou de tout autre composante importante	TRIQUE : Signal sonore et visuel de dérangement au poste de contrôle et d'annunciateur (ULC-524-6.2.1)	-	-	-	-	-	Transmission des données au SGB (Facultatif et selon les plans de gestion du bâtiment)
Détecteur de monoxyde de carbone	SUPERVISION : Signal sonore localisé dans la zone touchée et visuel à l'annunciateur et/ou du centre d'arrivage et de contrôle (ULC-524-32.1)	-	-	-	-	-	Transmission des données au SGB (Facultatif et selon les plans de gestion du bâtiment)

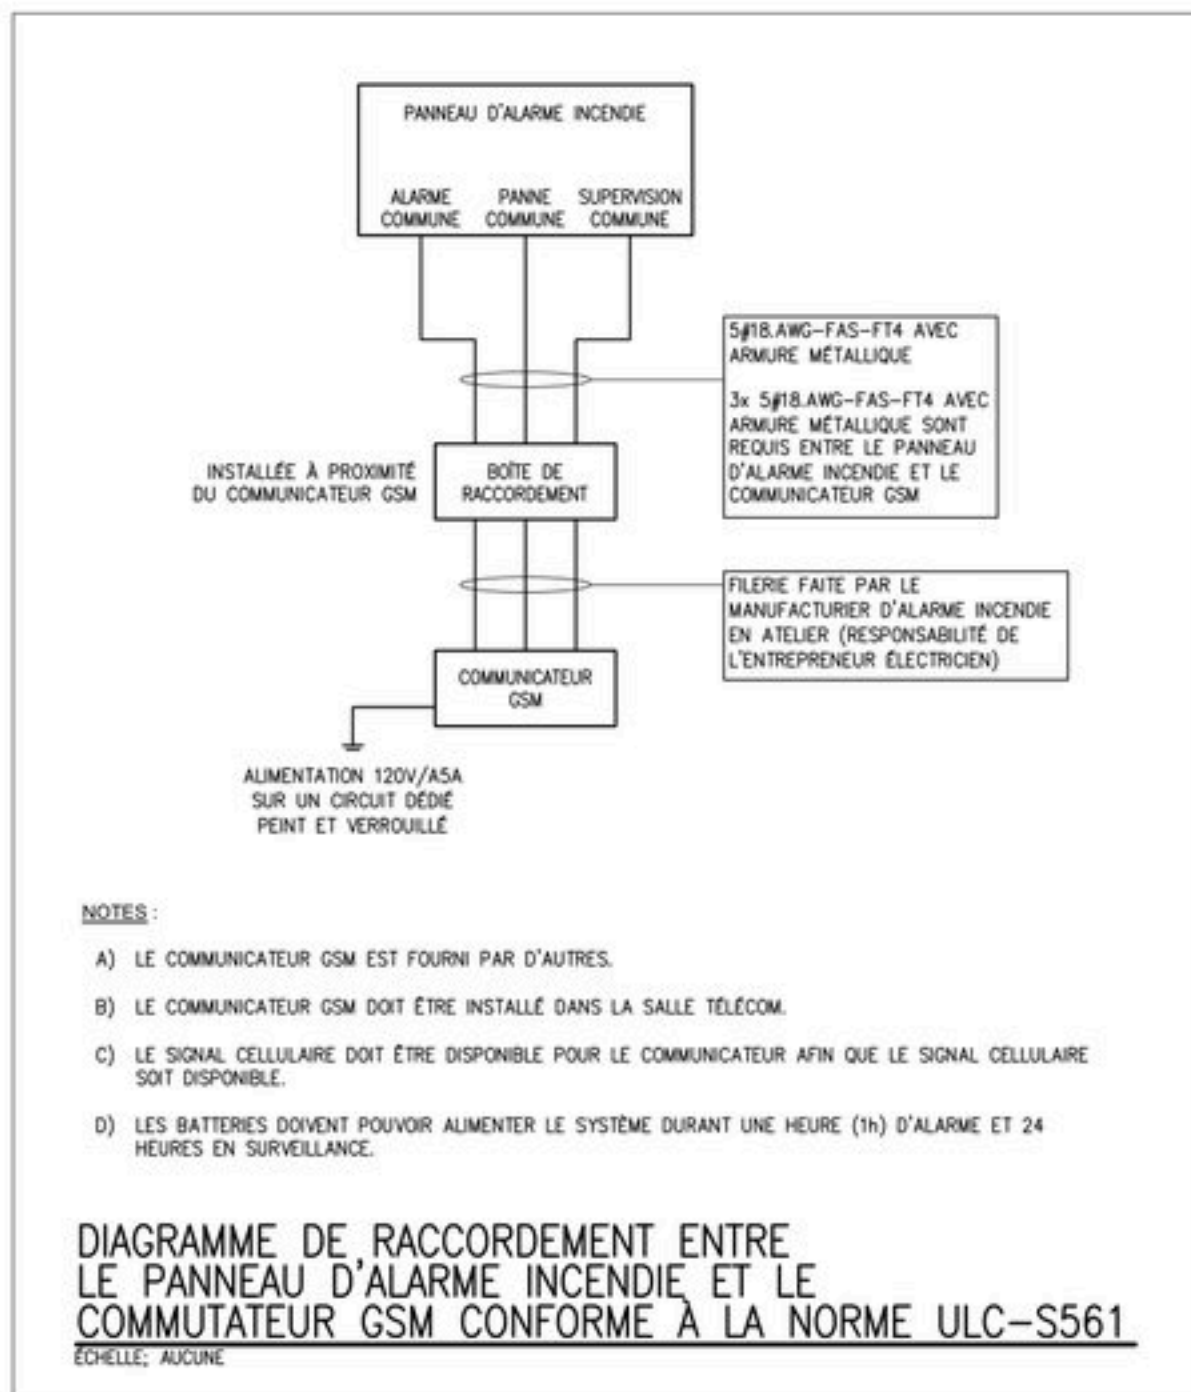
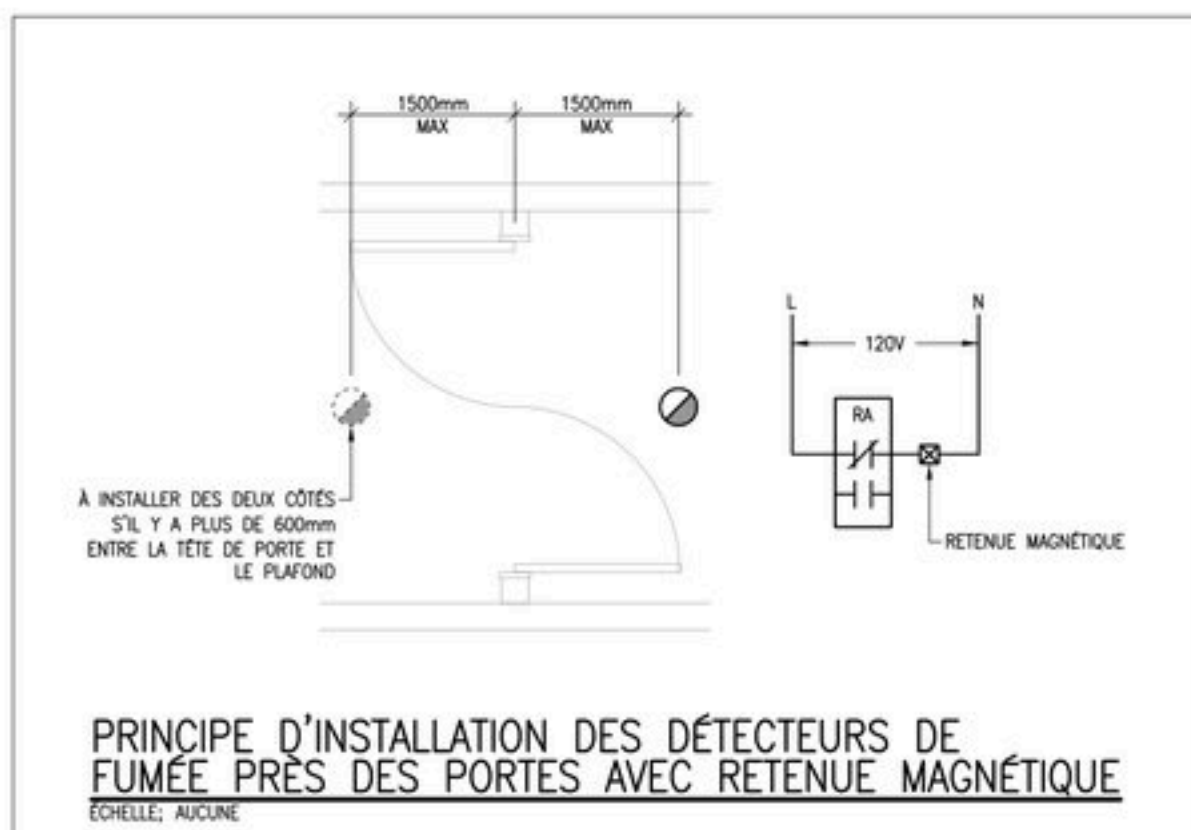
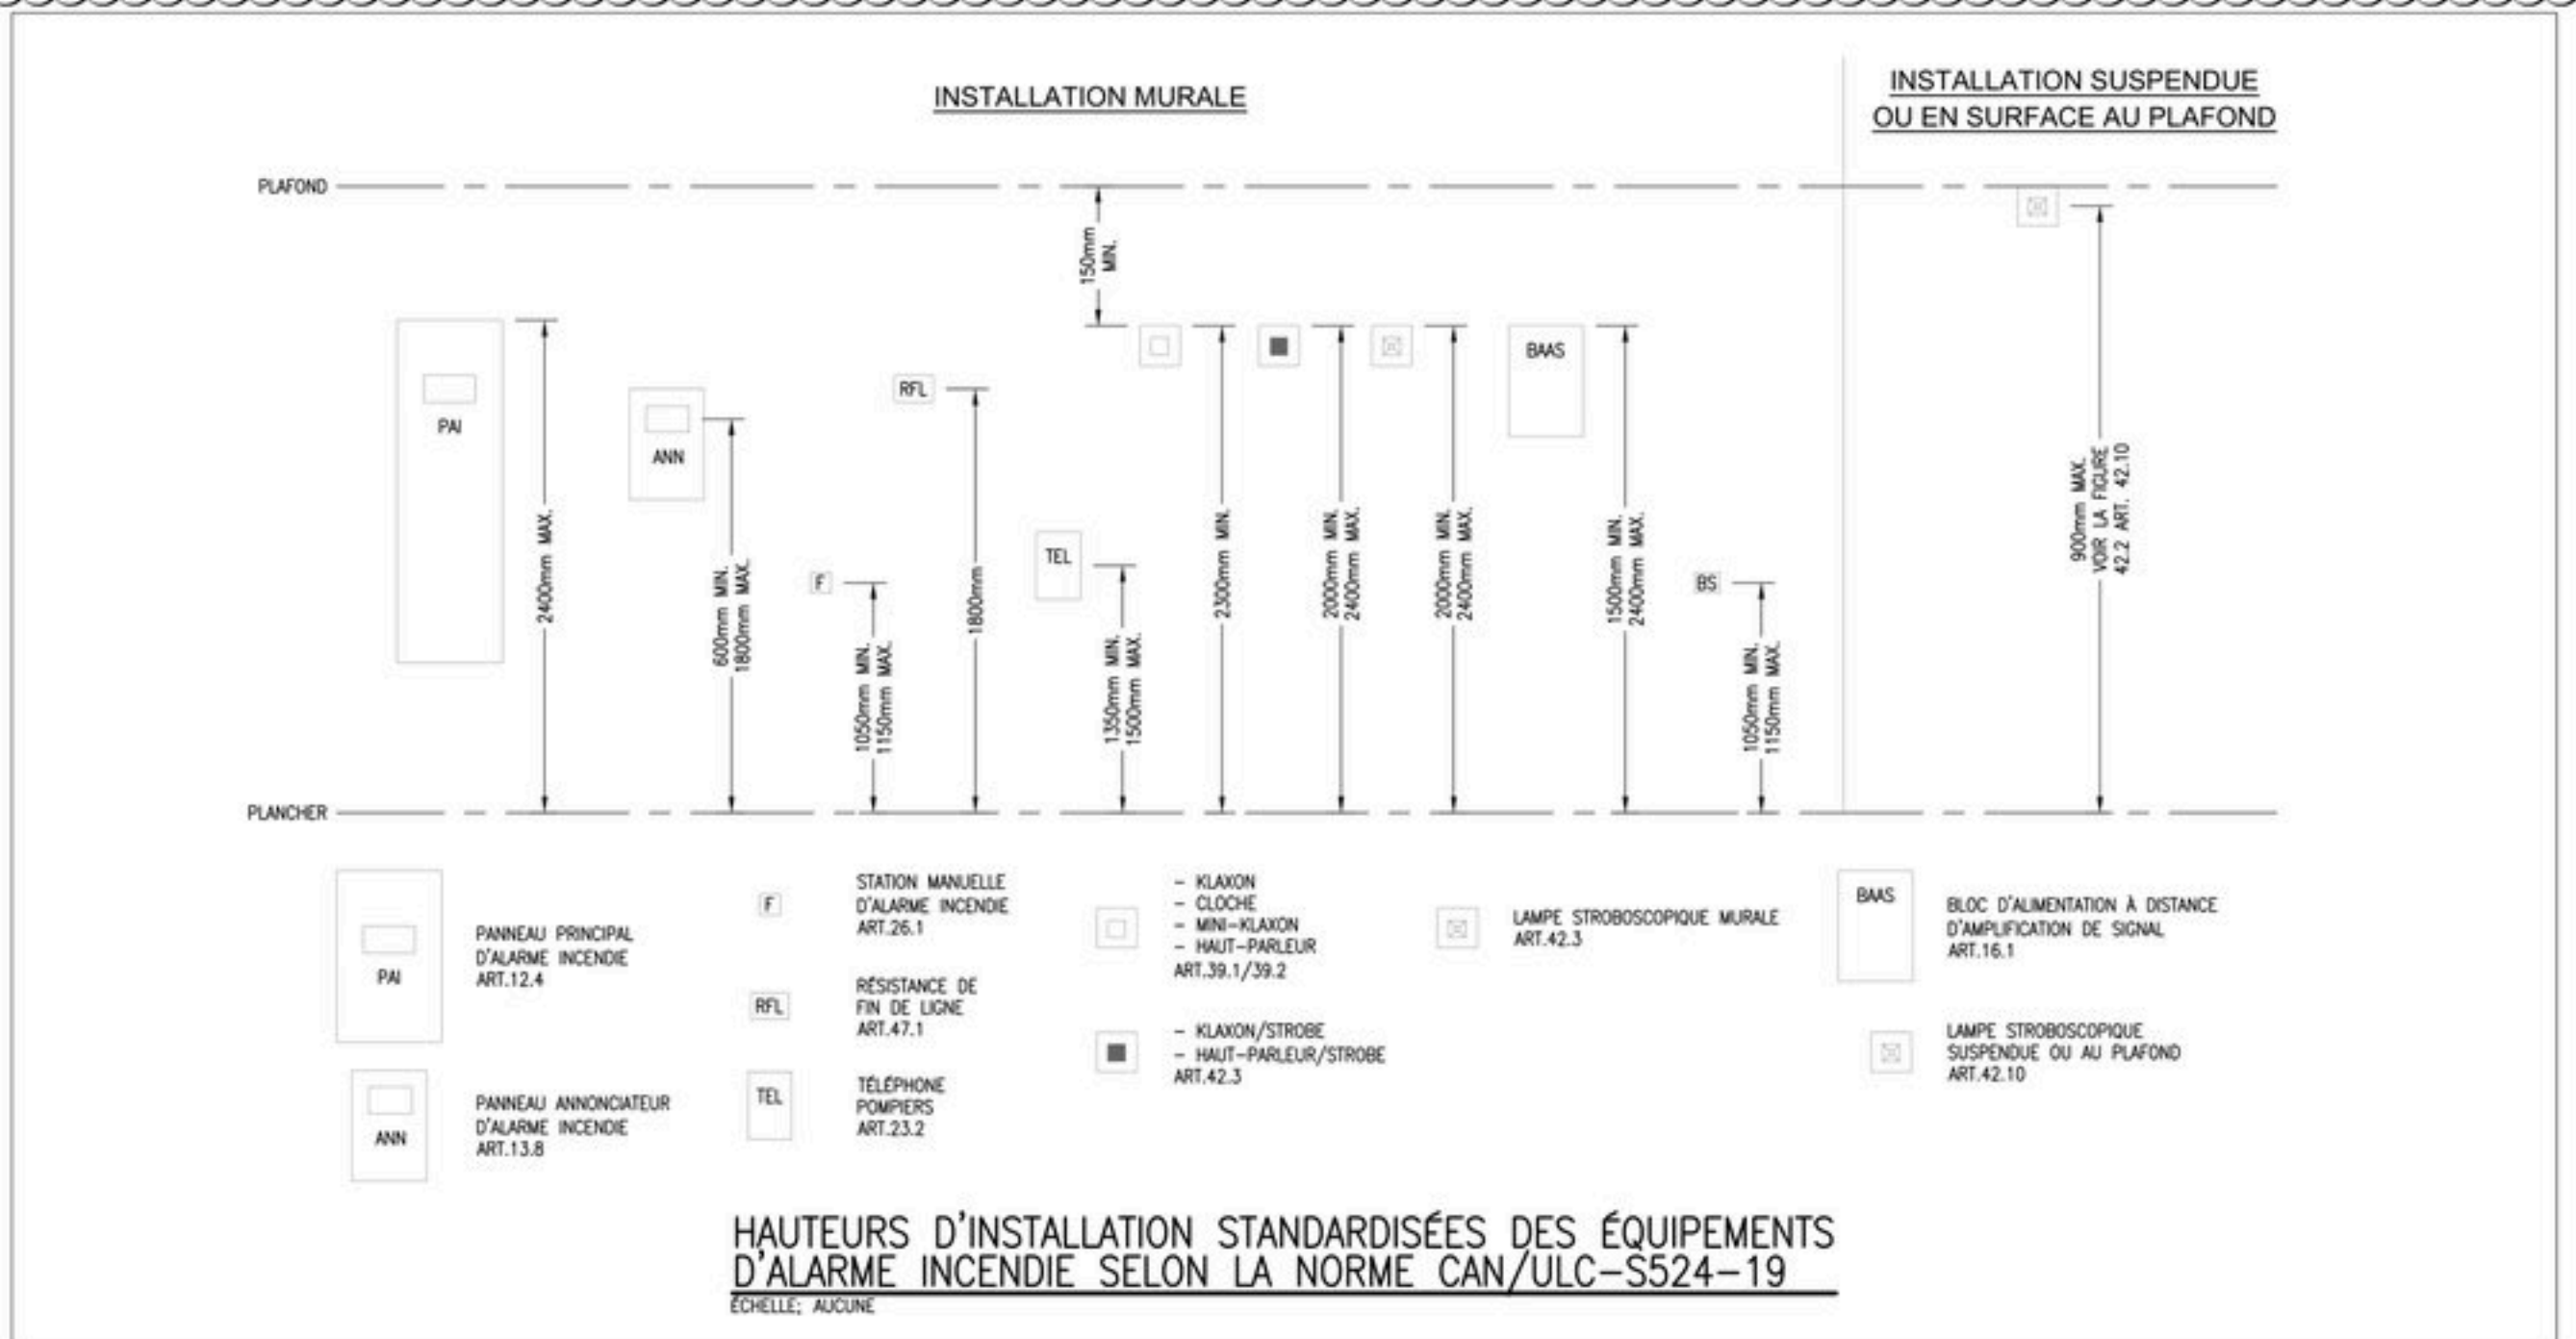
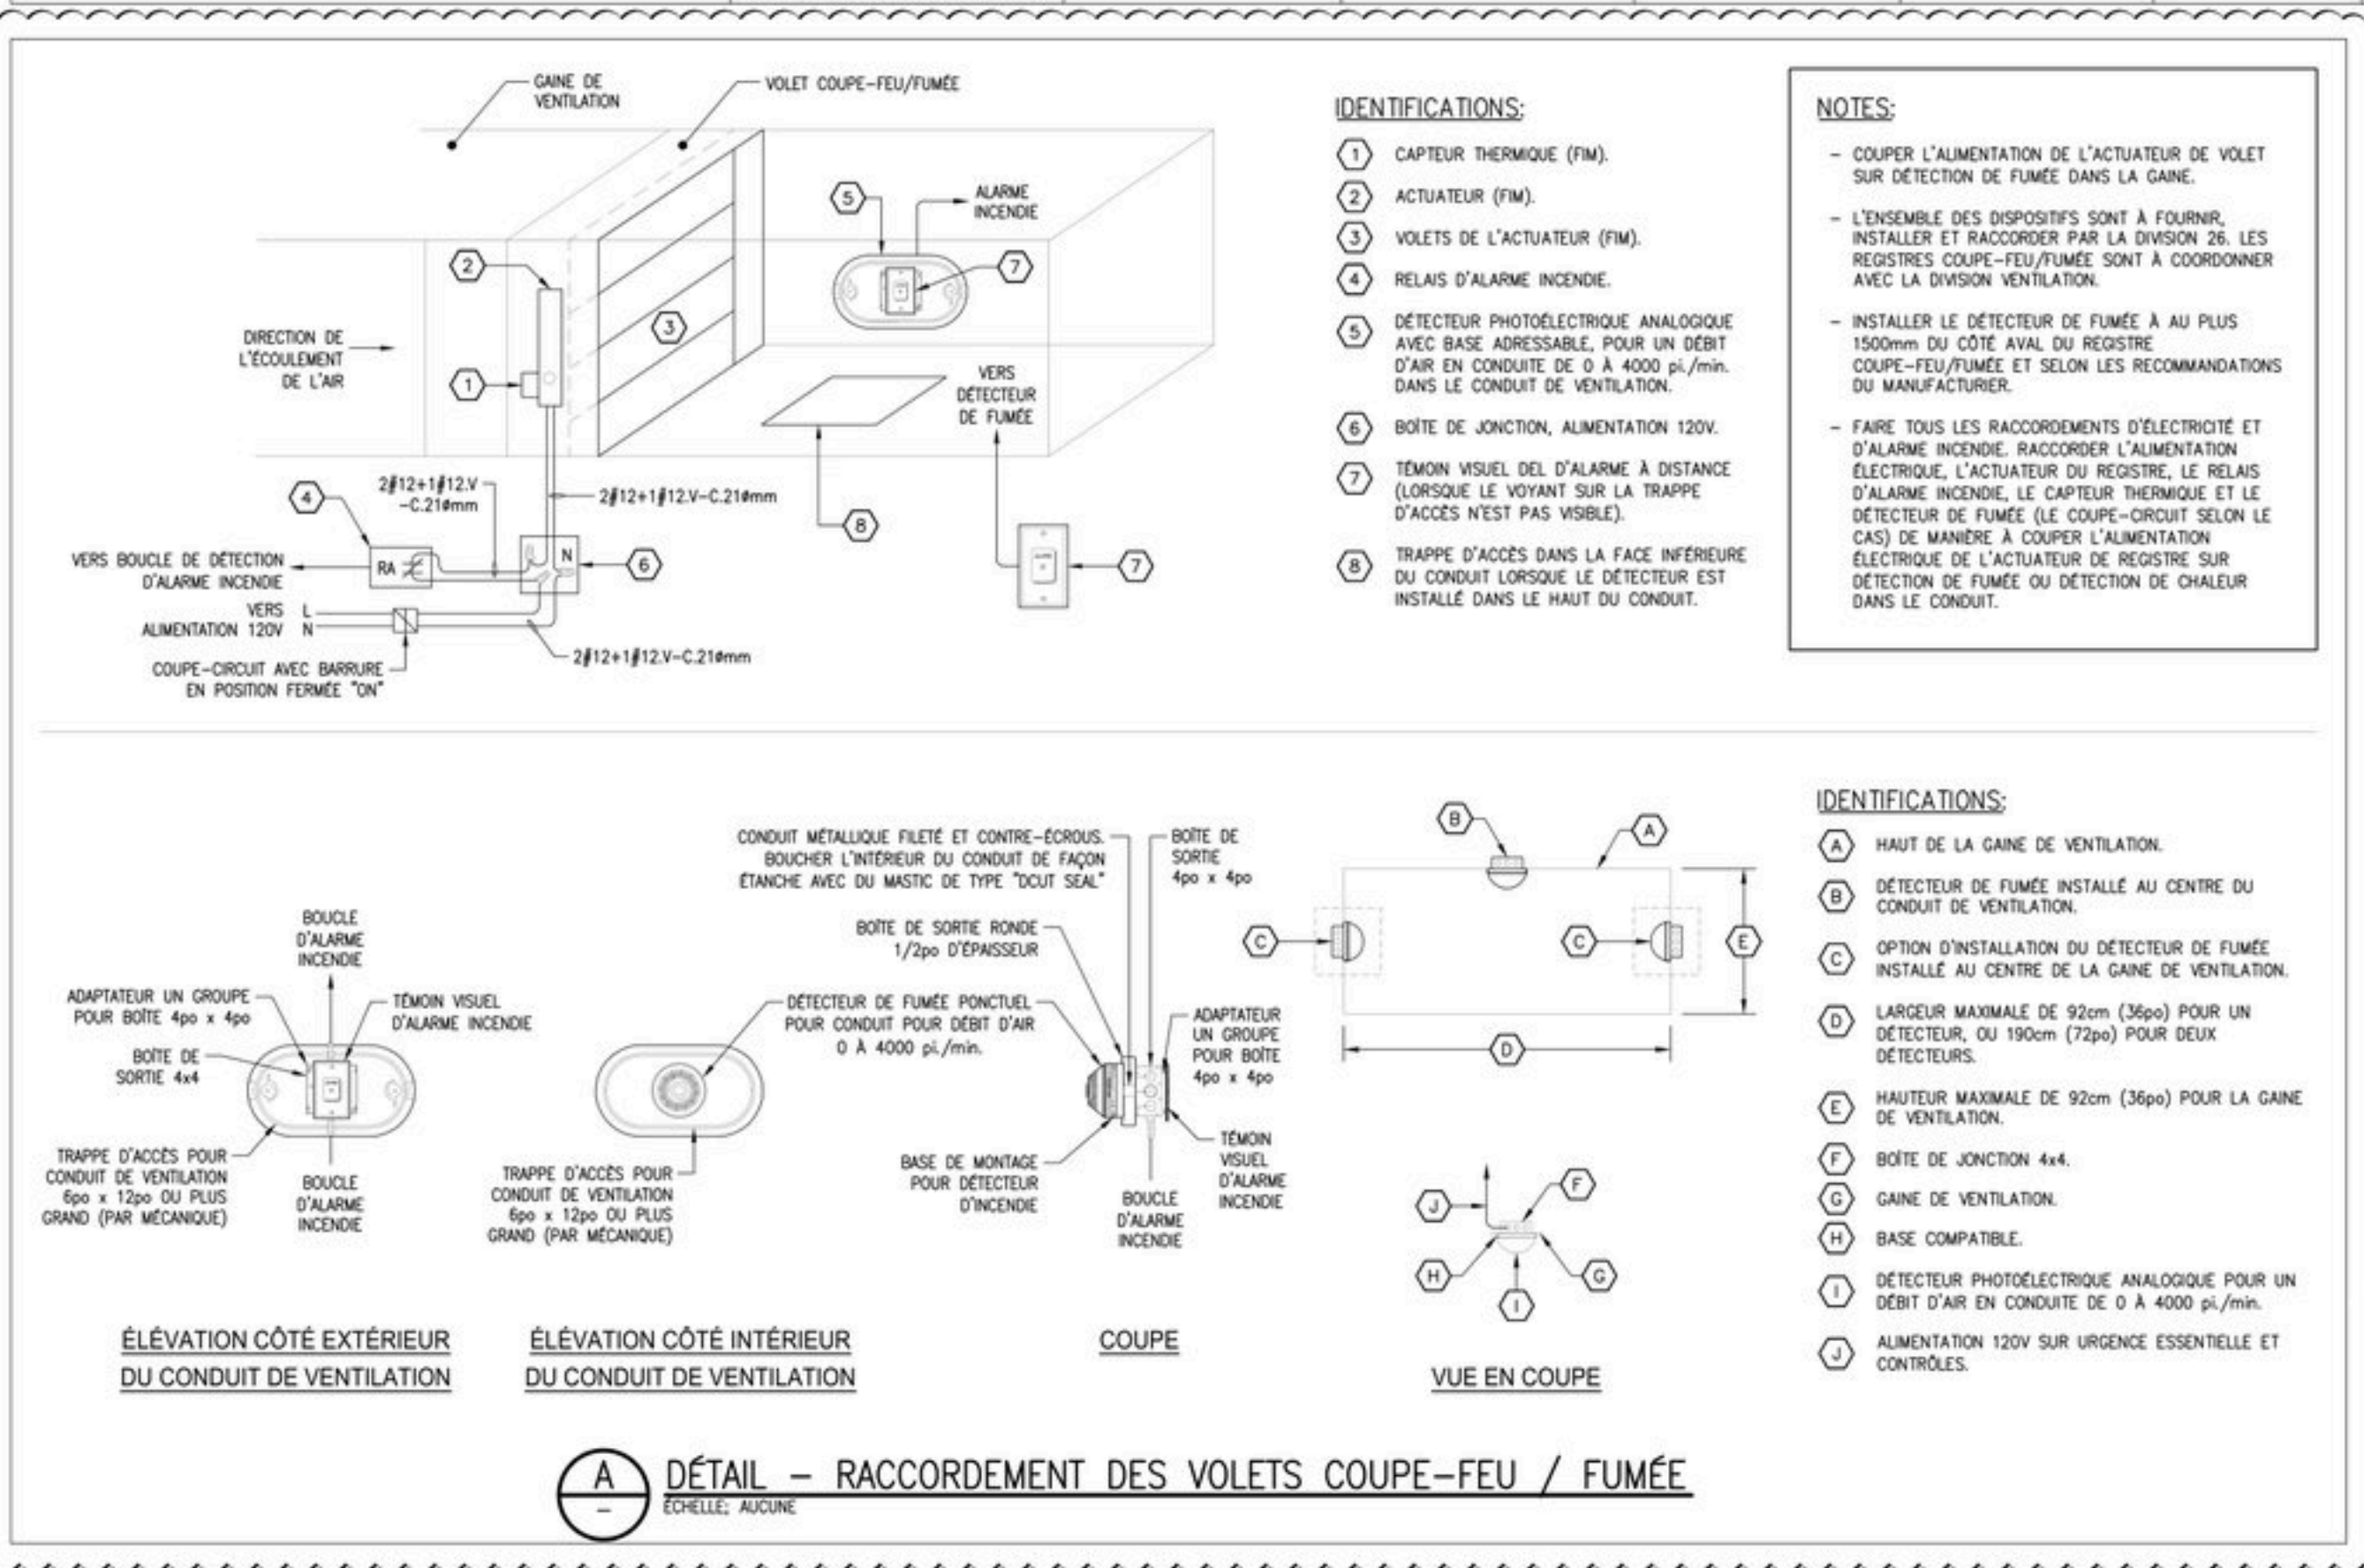





TABLEAU DES LONGUEURS MAXIMALES DES BOUCLES D'ALARME INCENDIE						
LONGUEUR MAXIMALE DU CONDUCTEUR DE LA SOURCE D'ALIMENTATION JUSQU'AU DERNIER APPAREIL - MÉTHODE DE CALCUL « END OF LINE »						
CONDUCTEUR (AWG)	B1	B2	B3	B4	B5	B6
#16	106 MÈTRES	123 MÈTRES	131 MÈTRES	139 MÈTRES	147 MÈTRES	155 MÈTRES
#18	166 MÈTRES	195 MÈTRES	207 MÈTRES	217 MÈTRES	227 MÈTRES	237 MÈTRES
#14	269 MÈTRES	313 MÈTRES	333 MÈTRES	353 MÈTRES	373 MÈTRES	393 MÈTRES
#12	426 MÈTRES	495 MÈTRES	527 MÈTRES	557 MÈTRES	587 MÈTRES	617 MÈTRES
#10	675 MÈTRES	784 MÈTRES	835 MÈTRES	885 MÈTRES	935 MÈTRES	985 MÈTRES

NOTES GÉNÉRALES :

- LES DIAGRAMMES D'ALARME INCENDIE SONT À TITRE INDICATIF SEULEMENT. LA QUANTITÉ DE COMPOSANTES MONTRE PEUT VARIER EN FONCTION DES AMÉNAGEMENTS. SE RÉFÉRER AUX PLANS DES ÉTAGES ET AU DEVIS POUR LA QUANTITÉ EXACTE À INSTALLER.
- LES BOUCLES D'ISOLATION DOIVENT ÊTRE UTILISÉES À L'ENTRÉE ET À LA SORTIE DE CHAQUE ZONE D'ALARME INCENDIE TEL QU'INDIQUÉ PAR LE DB.
- CONSULTER LES PLANS D'ARCHITECTURE ET PRÉVOIR LES ISOLATEURS DE DÉFAUT POUR LIASON DE DONNÉE DE CHAQUE CÔTÉ DES SÉPARATIONS COUPE FEU.
- LA CAPACITÉ DES CÂBLES DOIT ÊTRE CONFORME AUX RECOMMANDATIONS DU MANUFACTURIER.
- LA FILIÈRE ENTRE LE PANNEAU D'ALARME INCENDIE ET LE PANNEAU ANNONCIATEUR DOIT ÊTRE COORDONNÉE AVEC LE MANUFACTURIER.
- LA DISTANCE ENTRE LES BOTES DE JONCTIONS D'UNE BOUCLE DE CLASSE A DOIT ÊTRE AU MINIMUM DE 300mm À LA VERTICALE ET DE 1500mm À L'HORIZONTALE.
- TOUTS LES CONDUCTEURS DU RÉSEAU D'ALARME INCENDIE DOIVENT ÊTRE INSTALLÉS DANS DES CONDUITS ENT OU INCORPORÉS À DES CÂBLES RECOVERTS D'ANIMURE DU GÂNE MÉTALLIQUE.
- LE MANUFACTURIER DOIT FOURNIR UN DIAGRAMME COMPLET D'ALARME INCENDIE, REPRÉSENTANT LE SYSTÈME PROPOSÉ.
- LE MANUFACTURIER DOIT FOURNIR DES COMPOSANTES COMPATIBLES AVEC LE SYSTÈME INSTALLÉ PAR D'AUTRES POUR L'ENSEMBLE DU SITE.
- LE CALIBRE DES CÂBLES MONTRE DANS LES DIAGRAMMES REPRÉSENTE LE CALIBRE MINIMAL.

NOTES SPÉCIFIQUES :

- RÉUTILISER LE CIRCUIT ÉLECTRIQUE DE L'ANCIEN PANNEAU D'ALARME INCENDIE.

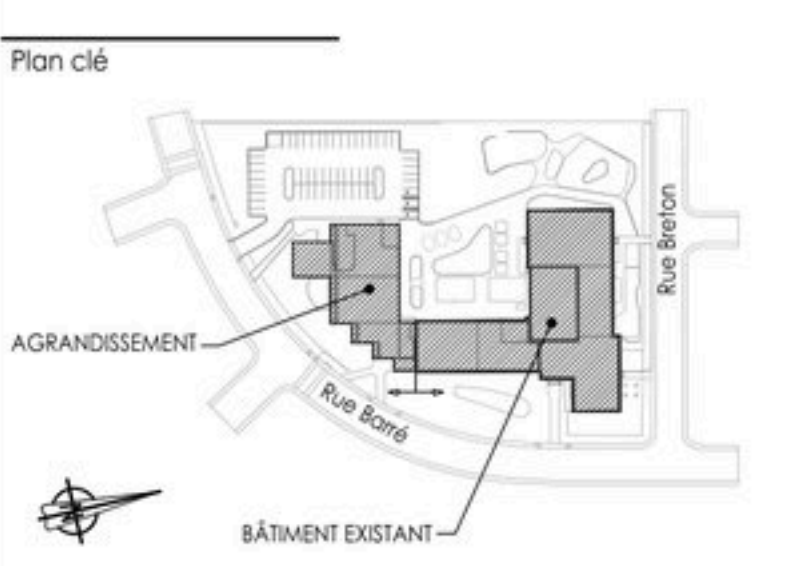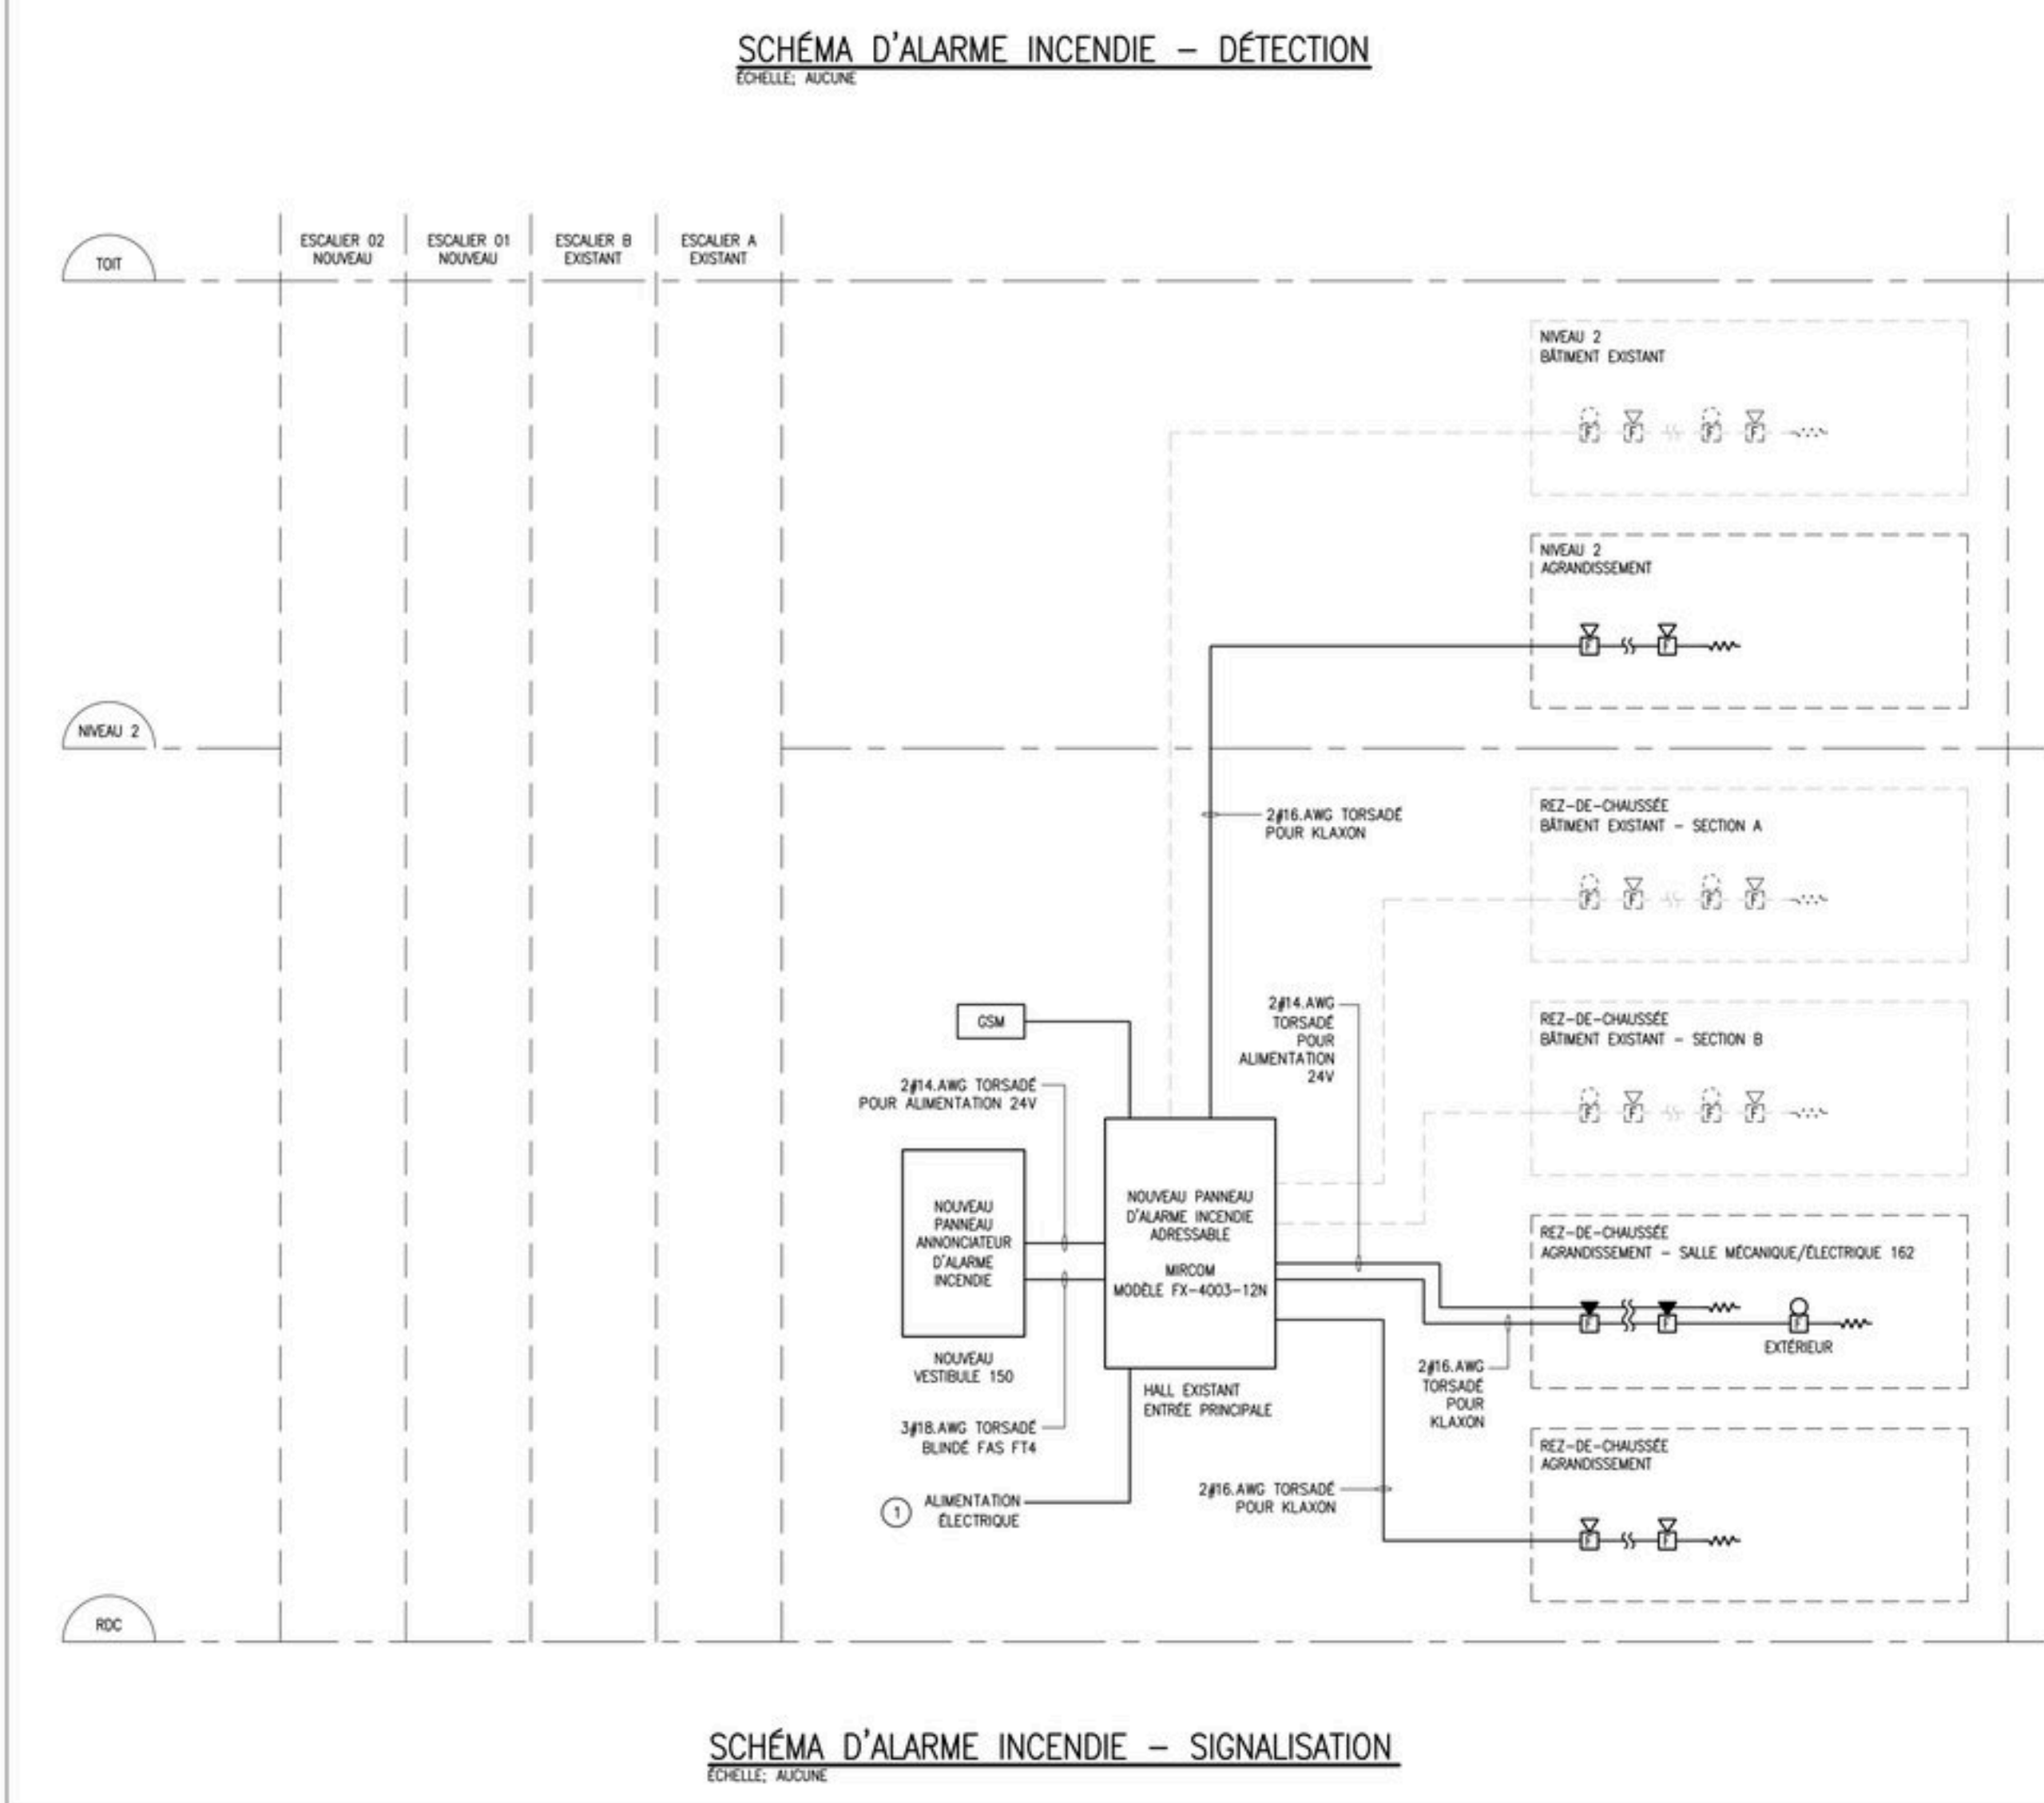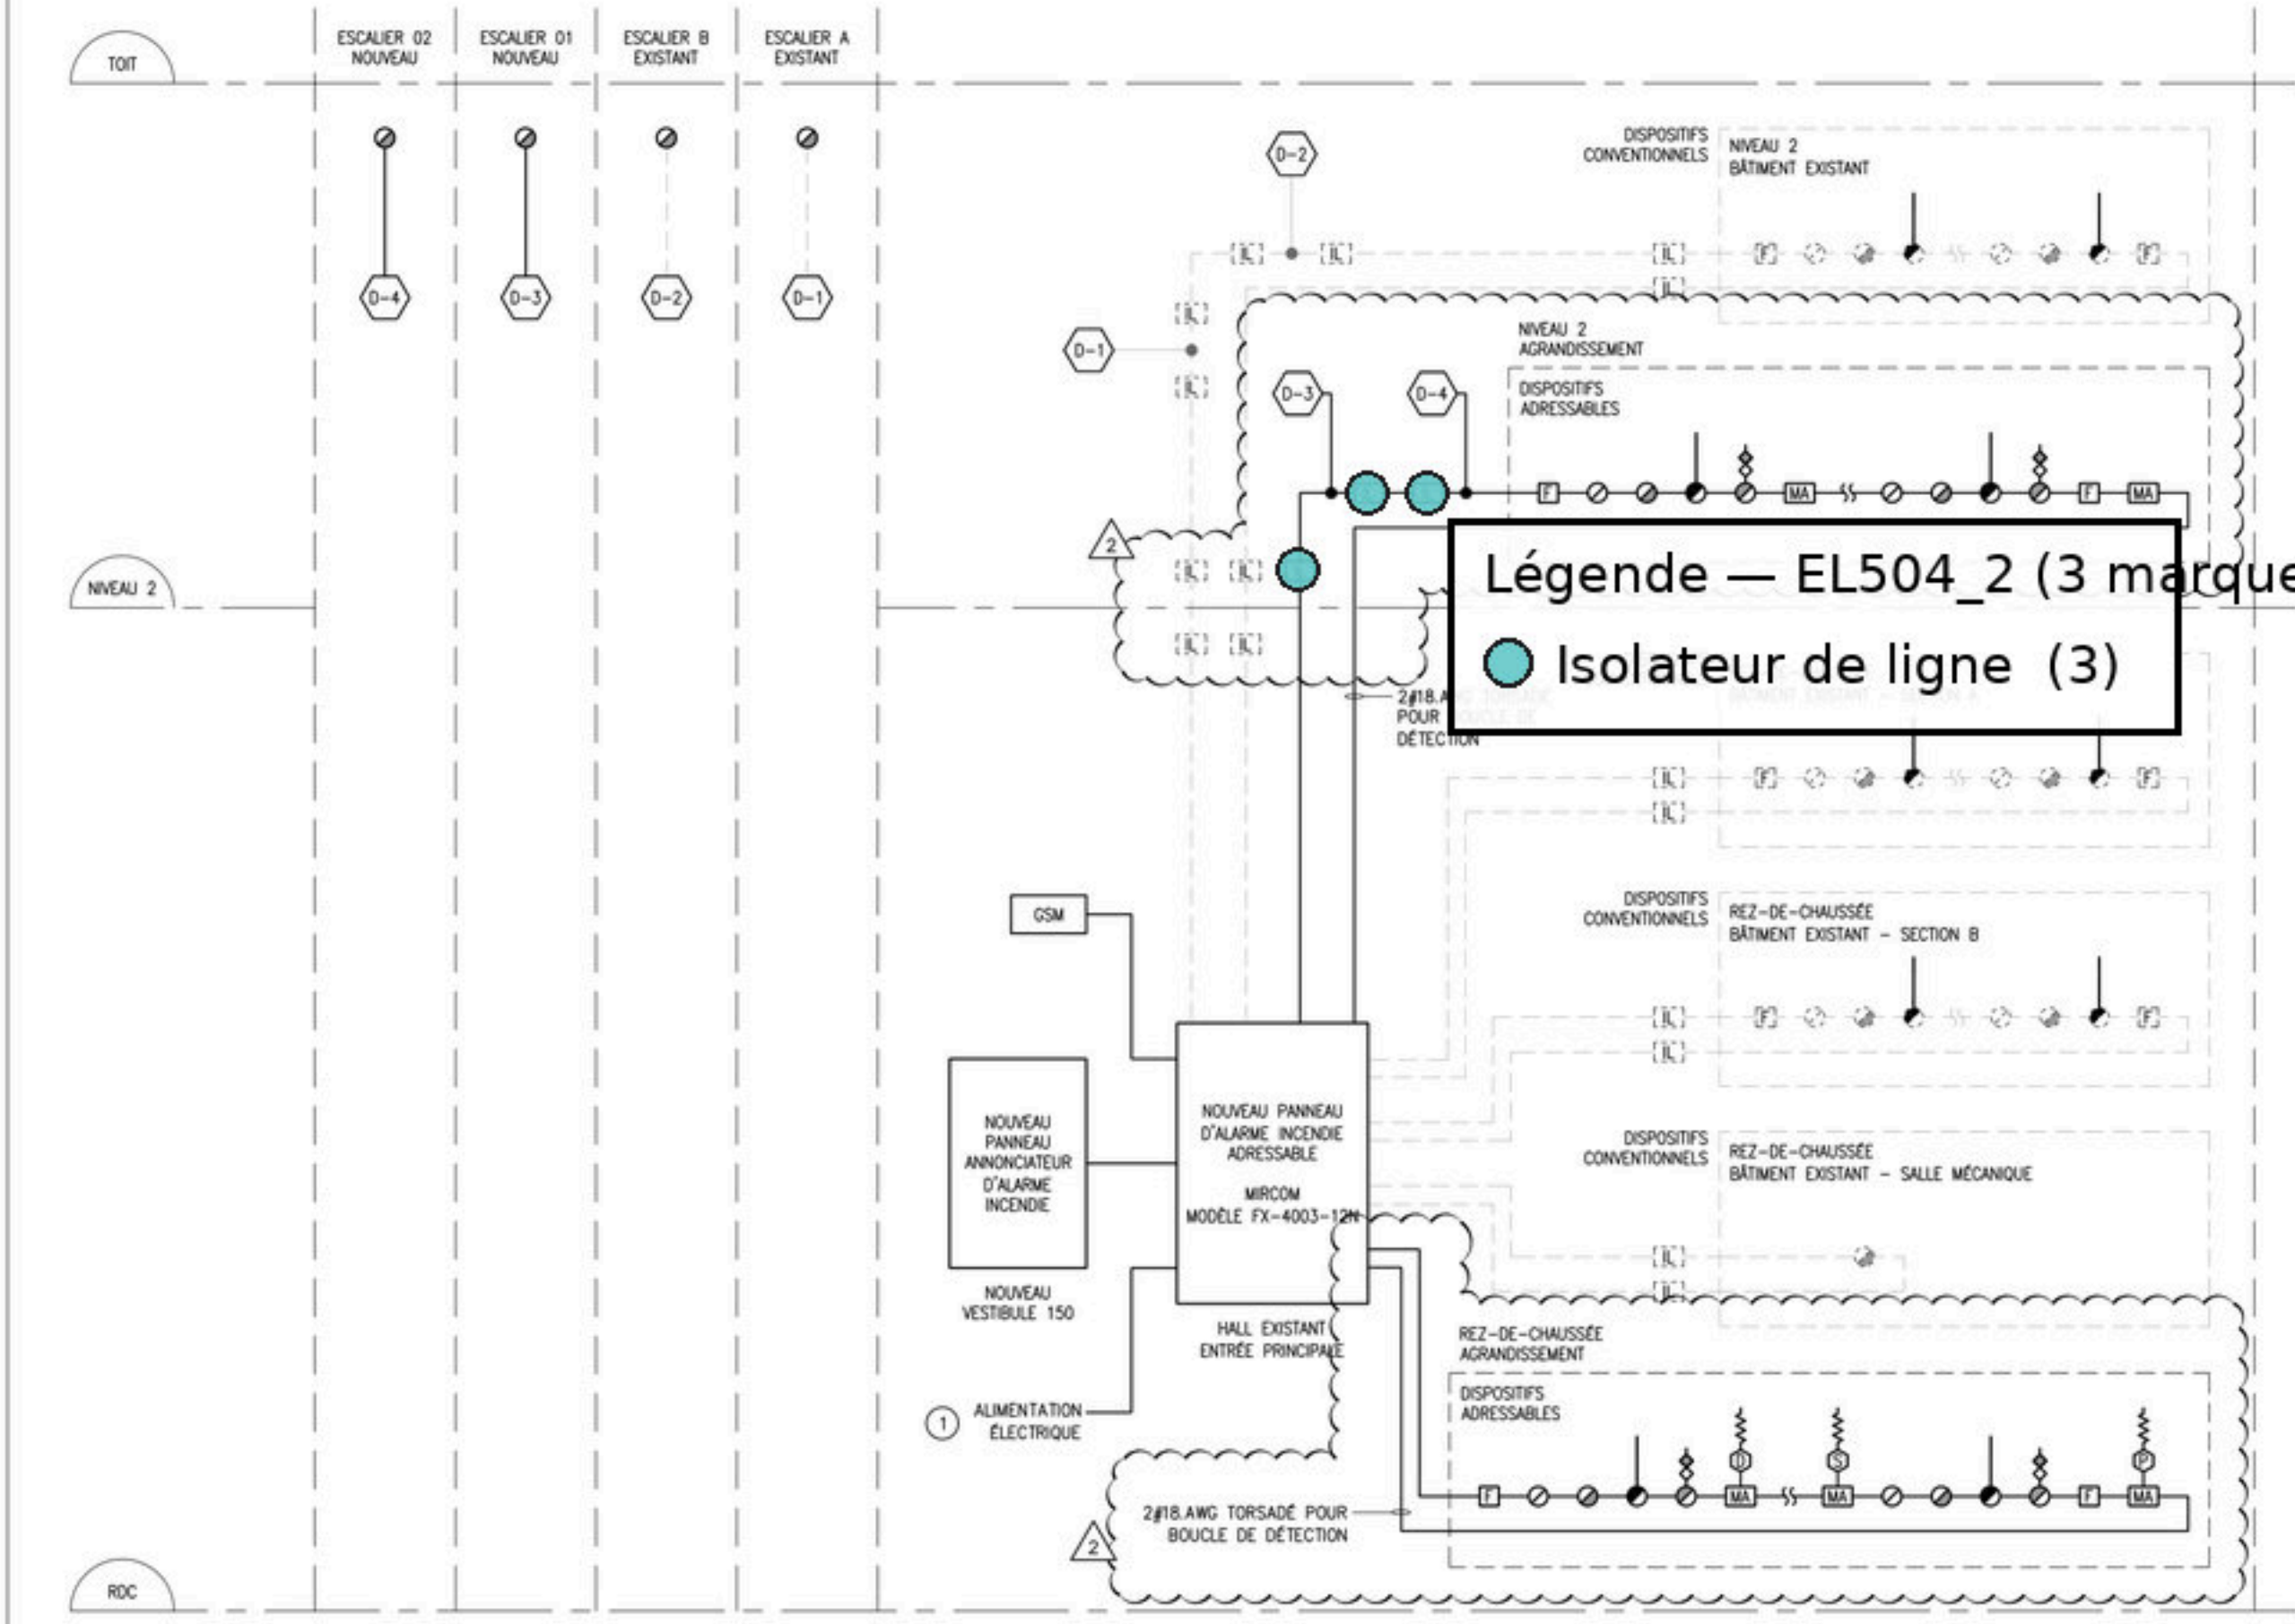

Nom	Prénom	Date
1	POUR APPRENDRE N°2	C.B. C.S. 2024.07.02
2	POUR APPRENDRE N°1	C.B. C.S. 2024.06.26
3	POUR APPRENDRE N°1	C.B. C.S. 2024.06.15
4	POUR APPRENDRE N°1	C.B. C.S. 2024.06.15
5	POUR APPRENDRE N°1	C.B. C.S. 2024.06.15
6	POUR APPRENDRE N°1	C.B. C.S. 2024.06.15
7	POUR APPRENDRE N°1	C.B. C.S. 2024.06.15
8	POUR APPRENDRE N°1	C.B. C.S. 2024.06.15
9	POUR APPRENDRE N°1	C.B. C.S. 2024.06.15
10	POUR APPRENDRE N°1	C.B. C.S. 2024.06.15

