

Eclairage (E) : 0	Moteurs (M) : 2611	ph A	ph B	ph C	Total en Watts
Prises (P) : 0	Chauffe-eau (CE) : 63000	107871	107770	106371	Total en Amps.
Climatisation (CL) : 1800	Divers (D) : 112698	179.8	179.6	177.3	Puissance Totale
Chauffage (CH) : 141903			322012.0		Ampérage Total phase
			179.8		Ampérage Total
			310.2		

* = Disjoncteur Verrouillable
GF = Disjoncteur Différentiel
AFI = Disjoncteur Anti-Arc

Eclairage (E) : 0	Moteurs (M) : 0	ph A	ph B	ph C	Total en Watts
Prises (P) : 37550	Chauffe-eau (CE) : 0	11400	15325	11825	Total en Amps.
Climatisation (CL) : 0	Divers (D) : 0	54,8	73,7	56,9	Puissance Totale
Chauffage (CH) : 0			38550,0		Ampérage Total phase
			73,7		Ampérage Total
			107,1		

* = Disjoncteur Verrouillable
GF = Disjoncteur Différentiel
AFI = Disjoncteur Anti-Arc

Éclairage (E) : 2963	Moteurs (M) : 860	ph A	ph B	ph C	Total en Watts Total en Amps Puissance Totale Ampréage Total phase Ampréage Total
Prises (P) : 21200	Chauffe-eau (CE) : 0	10433	8555	7096	
Climatisation (CL) : 360	Divers (D) : 1100	50,2	42,6	34,1	
Chauffage (CH) : 0		26383,0			
		50,2			
		73,3			

* = Disjoncteur Verrouillable
GF = Disjoncteur Différentiel
AFI = Disjoncteur Anti-Arc

Éclairage (E) : 3125	Moteurs (M) : 3978	ph A	ph B	ph C	Total en Watts	
Prises (P) : 14000	Chauffe-eau (CE) : 0	31558	28099	30543		
Climatisation (CL) : 2766	Divers(D) : 66231	151,7	135,1	148,8		Total en Amps.
Chauffage (CH) : 0			90200,0			Puissance Totale
			151,7		Amperage Total phase	
			250,7		Amperage Total	

* = Disjoncteur Verrouillable
GF = Disjoncteur Différentiel
AFI = Disjoncteur Anti-Arc

ration VRF (2)

ARCHITECTE:



Bâtir pour l'enfance

CPE LES COPAINS D'ABORD

PROJET:

CPE LES COPAINS D'ABORD
PROJET DE REMPLACEMENT

2310 AVENUE BENNY MONTRÉAL, QC, H4B 2R4

TITRE DU PLAN
PANNEAUX

NO DE DOSSIER	25-64		
DESSINÉ PAR:	A. DESJARDINS		
PRÉPARÉ PAR:	A. DESJARDINS		
VÉRIFIÉ PAR:	R. HADDAD		
ÉCHELLE:	AUCUNE	FORMAT	841X594
DATE:	DÉCEMBRE 2025		


01	2026-06-23	POUR SOUMISSION REV01
00	2026-05-26	POUR SOUMISSION
No.	DATE:	ÉMISSION:



CLIENT:
CPE LES COPAINS D'ABORD
PROJET:
CPE LES COPAINS D'ABORD PROJET DE REMPLACEMENT
2310 AVENUE BENNY MONTRÉAL, QC, H4B 2R4

TITRE DU PLAN
SCHÉMA UNIFILAIRE


No DE DOSSIER	25-64		
DESSINÉ PAR:	A. DESJARDINS		
PRÉPARÉ PAR:	A. DESJARDINS		
VÉRIFIÉ PAR:	R. HADDAD		
ÉCHELLE:	AUCUNE	FORMAT	841X594
DATE:	DÉCEMBRE 2025		

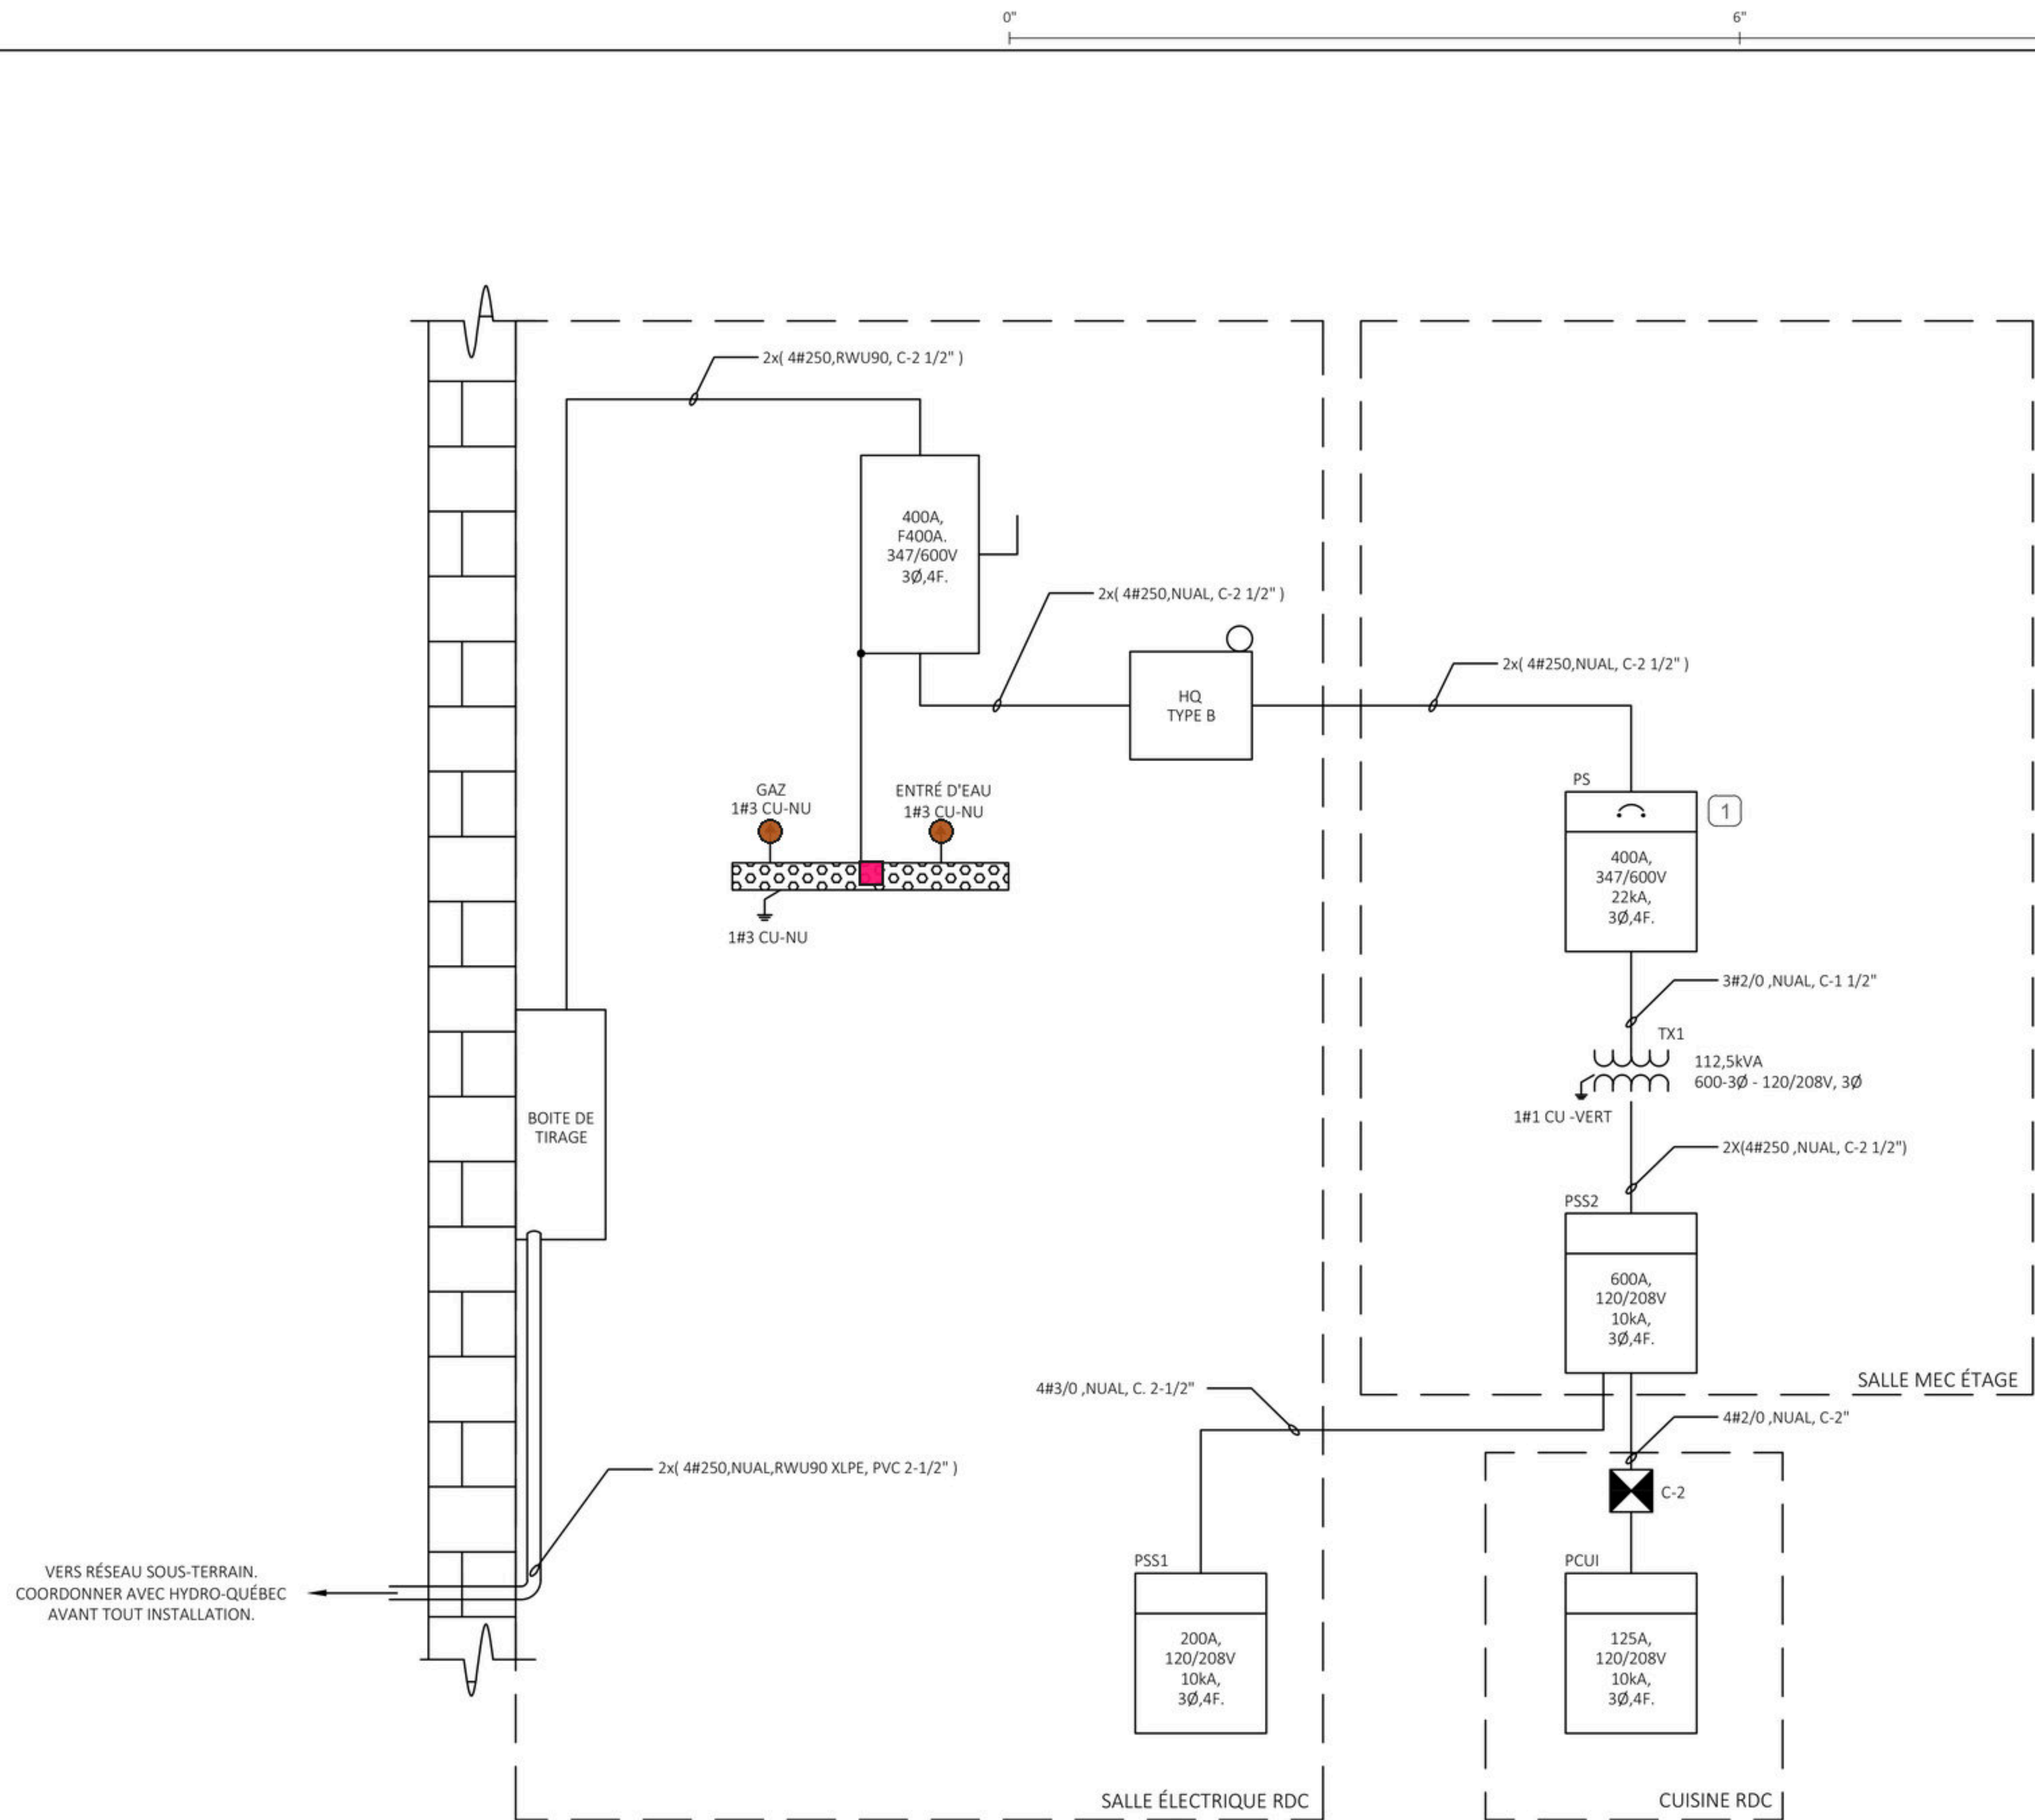


VERS RÉSEAU SOUS-TERRAIN.
COORDONNER AVEC HYDRO-QUÉBEC
AVANT TOUT INSTALLATION.

Légende — E010 (9 marques)


- Barre de mise à la terre (1)
- Conduit vide entrée télécom (2)
- Contacteur (1)
- Contreplaqué télécom (1)
- Liaison MALT gaz/eau (2)
- Minuterie astronomique (1)
- Sélecteur 3 positions (1)

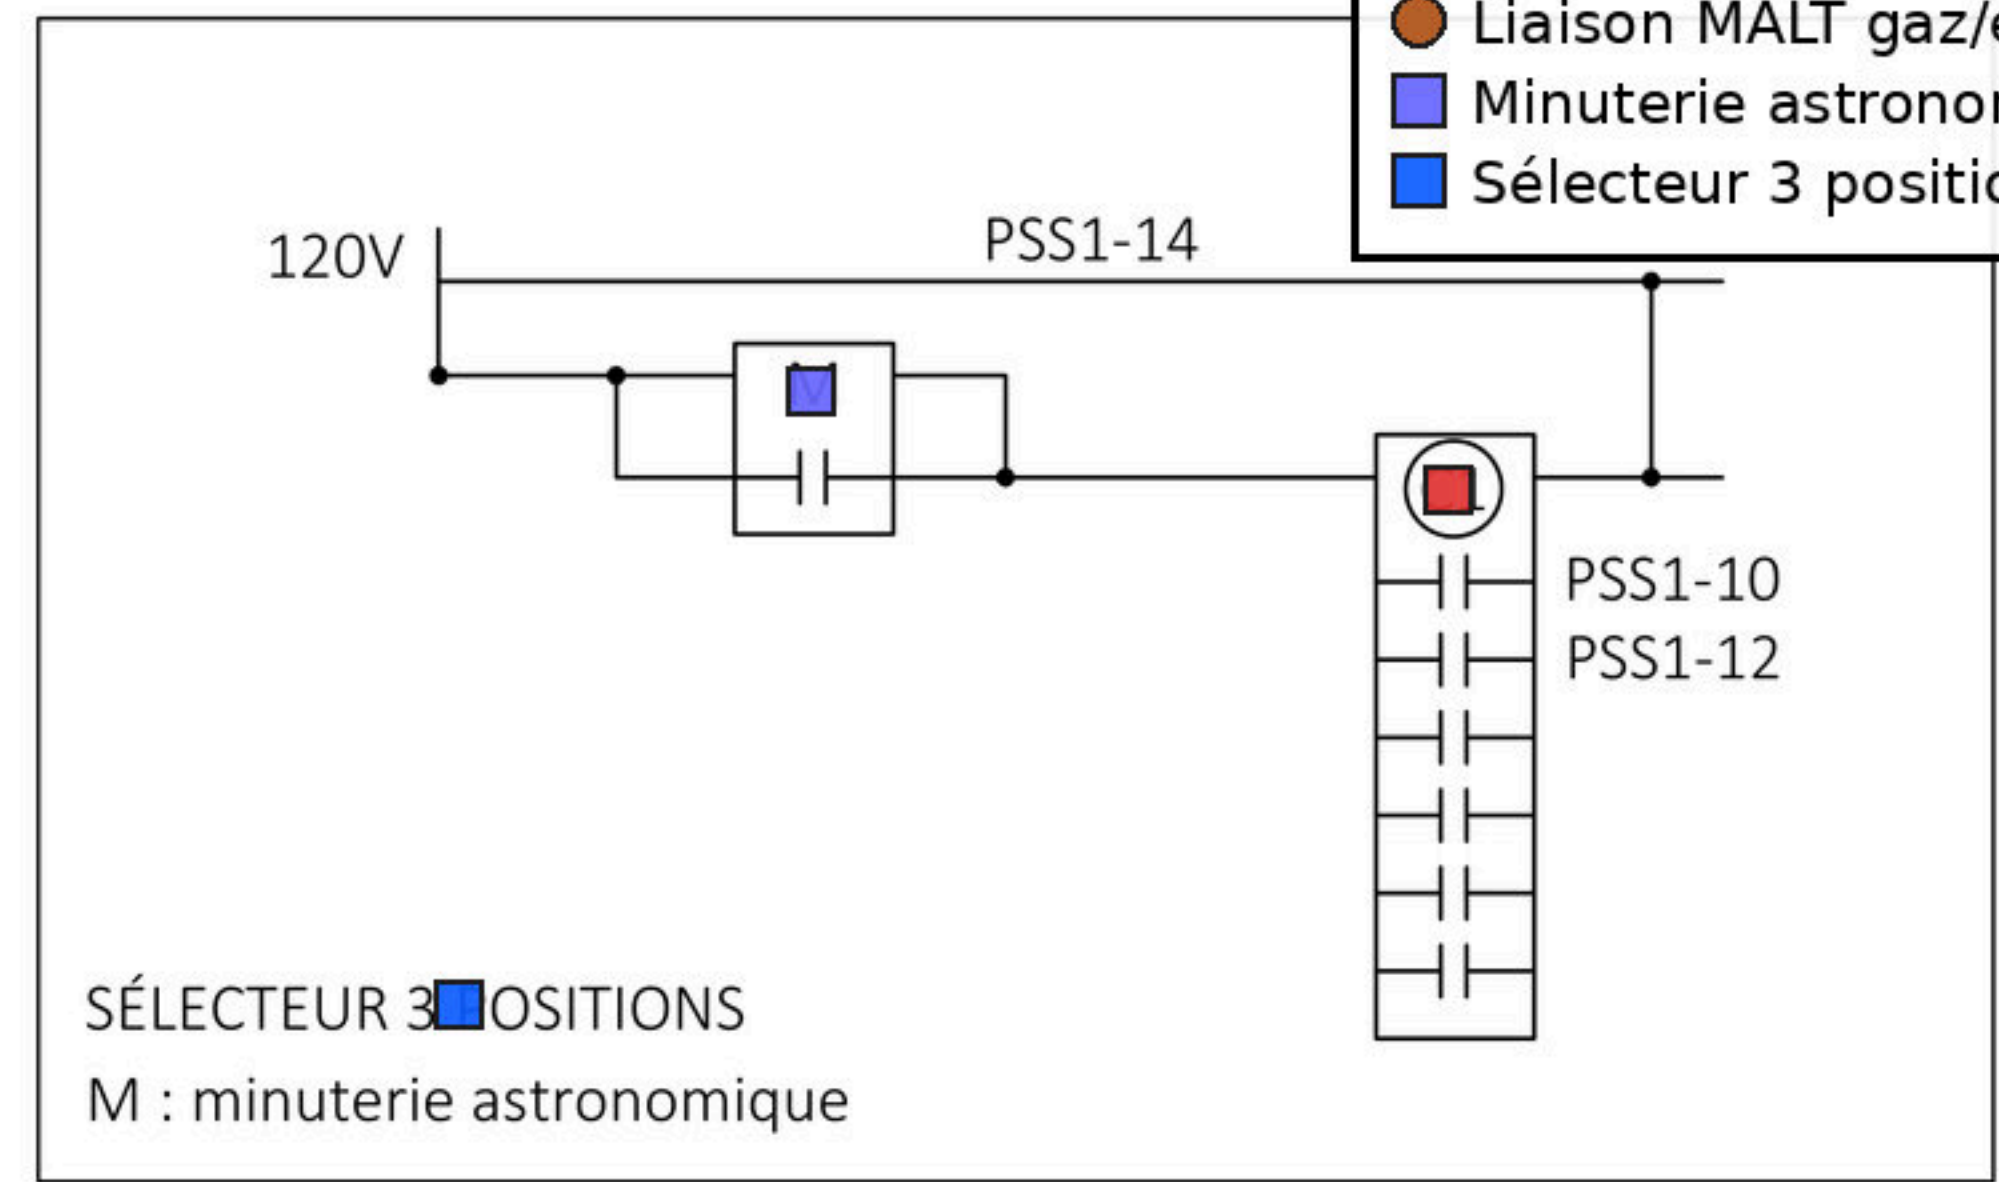

CONTACTEUR POUR ÉCLAIRAGE EXTÉRIEUR - C1
ÉCHELLE: AUCUNE

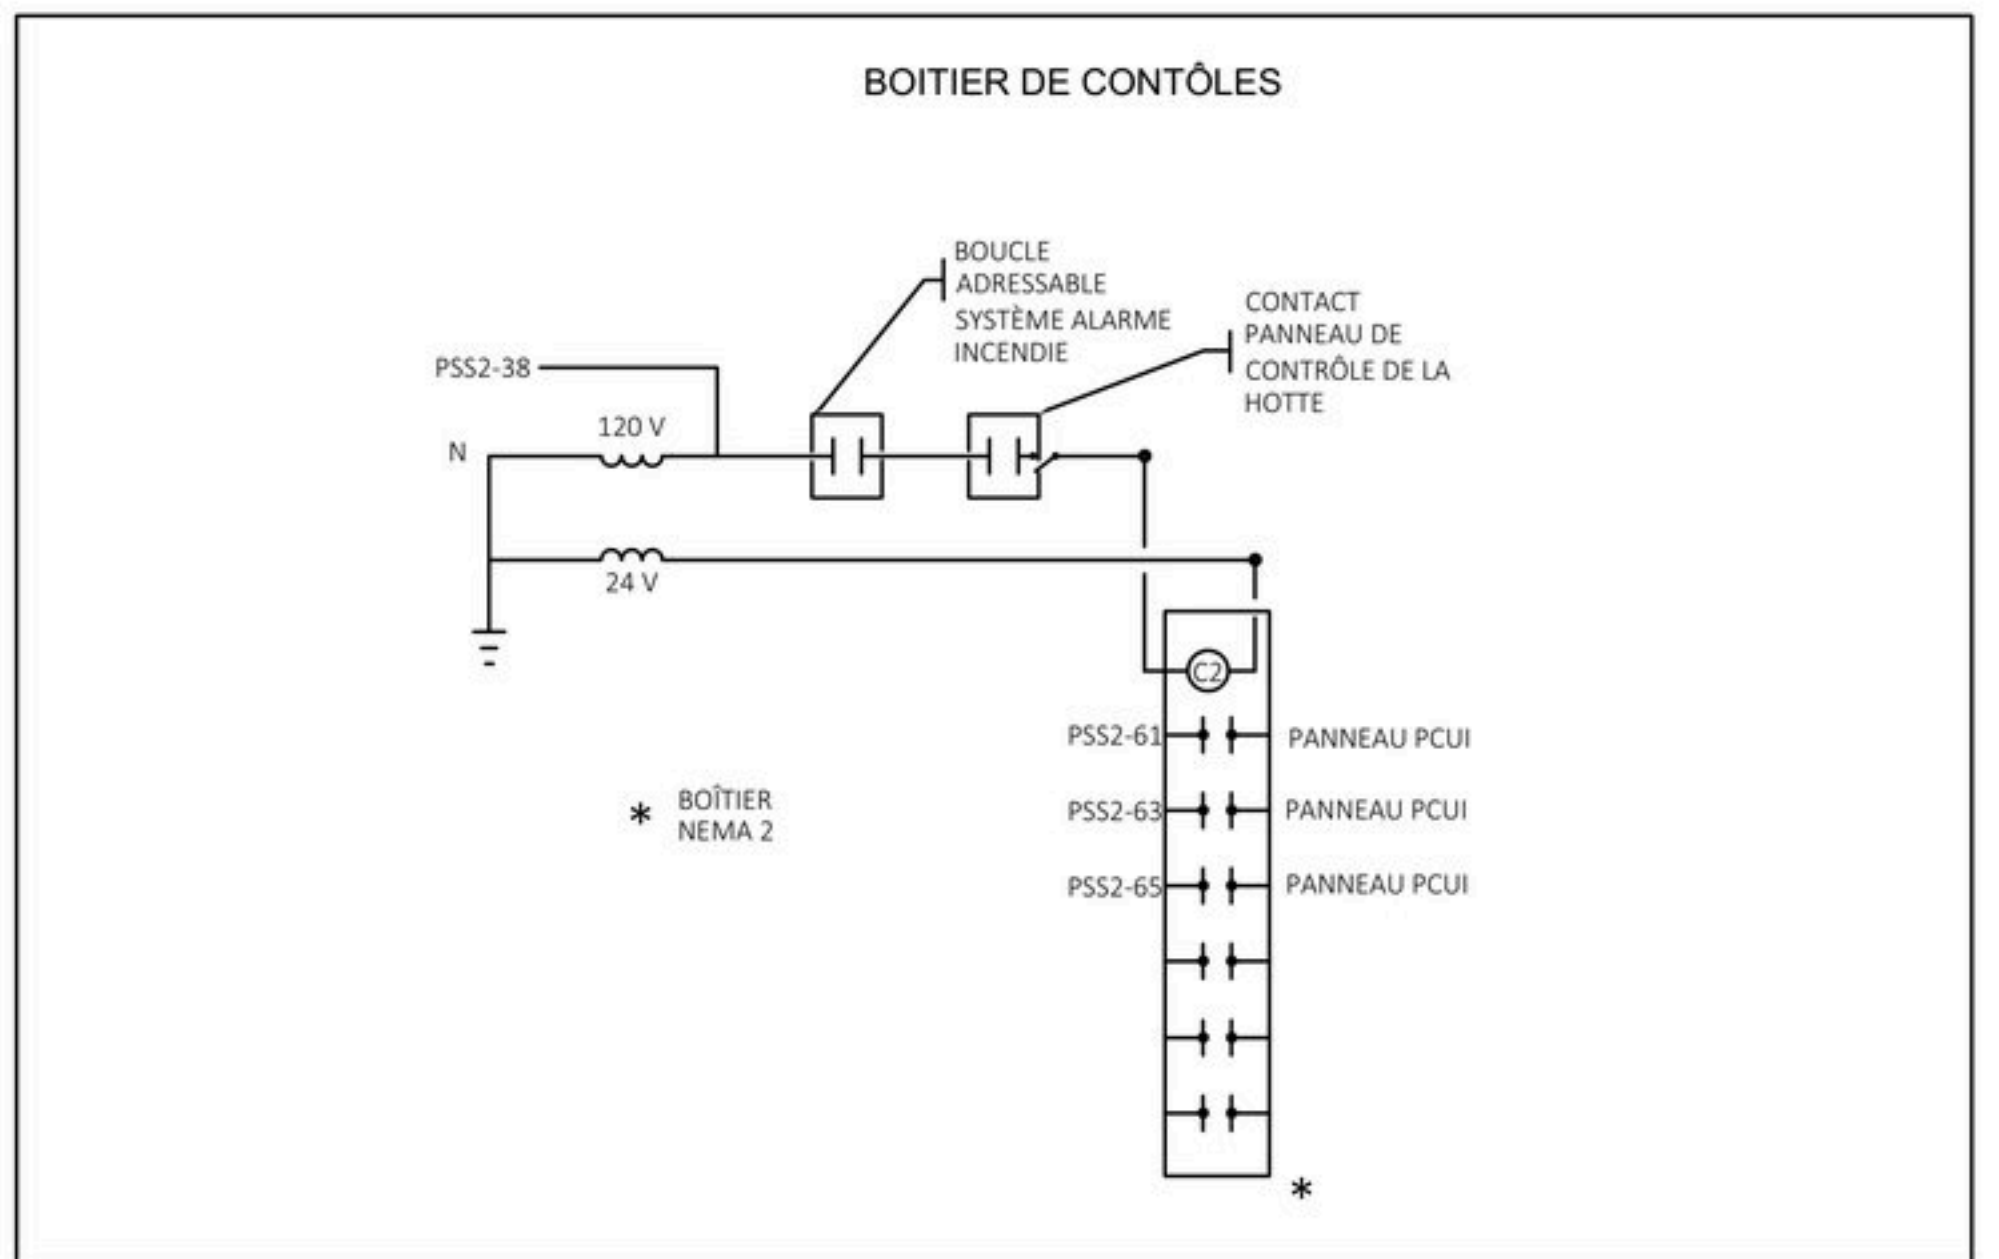

CONTACTEUR POUR CUISINE - C2
ÉCHELLE: AUCUNE

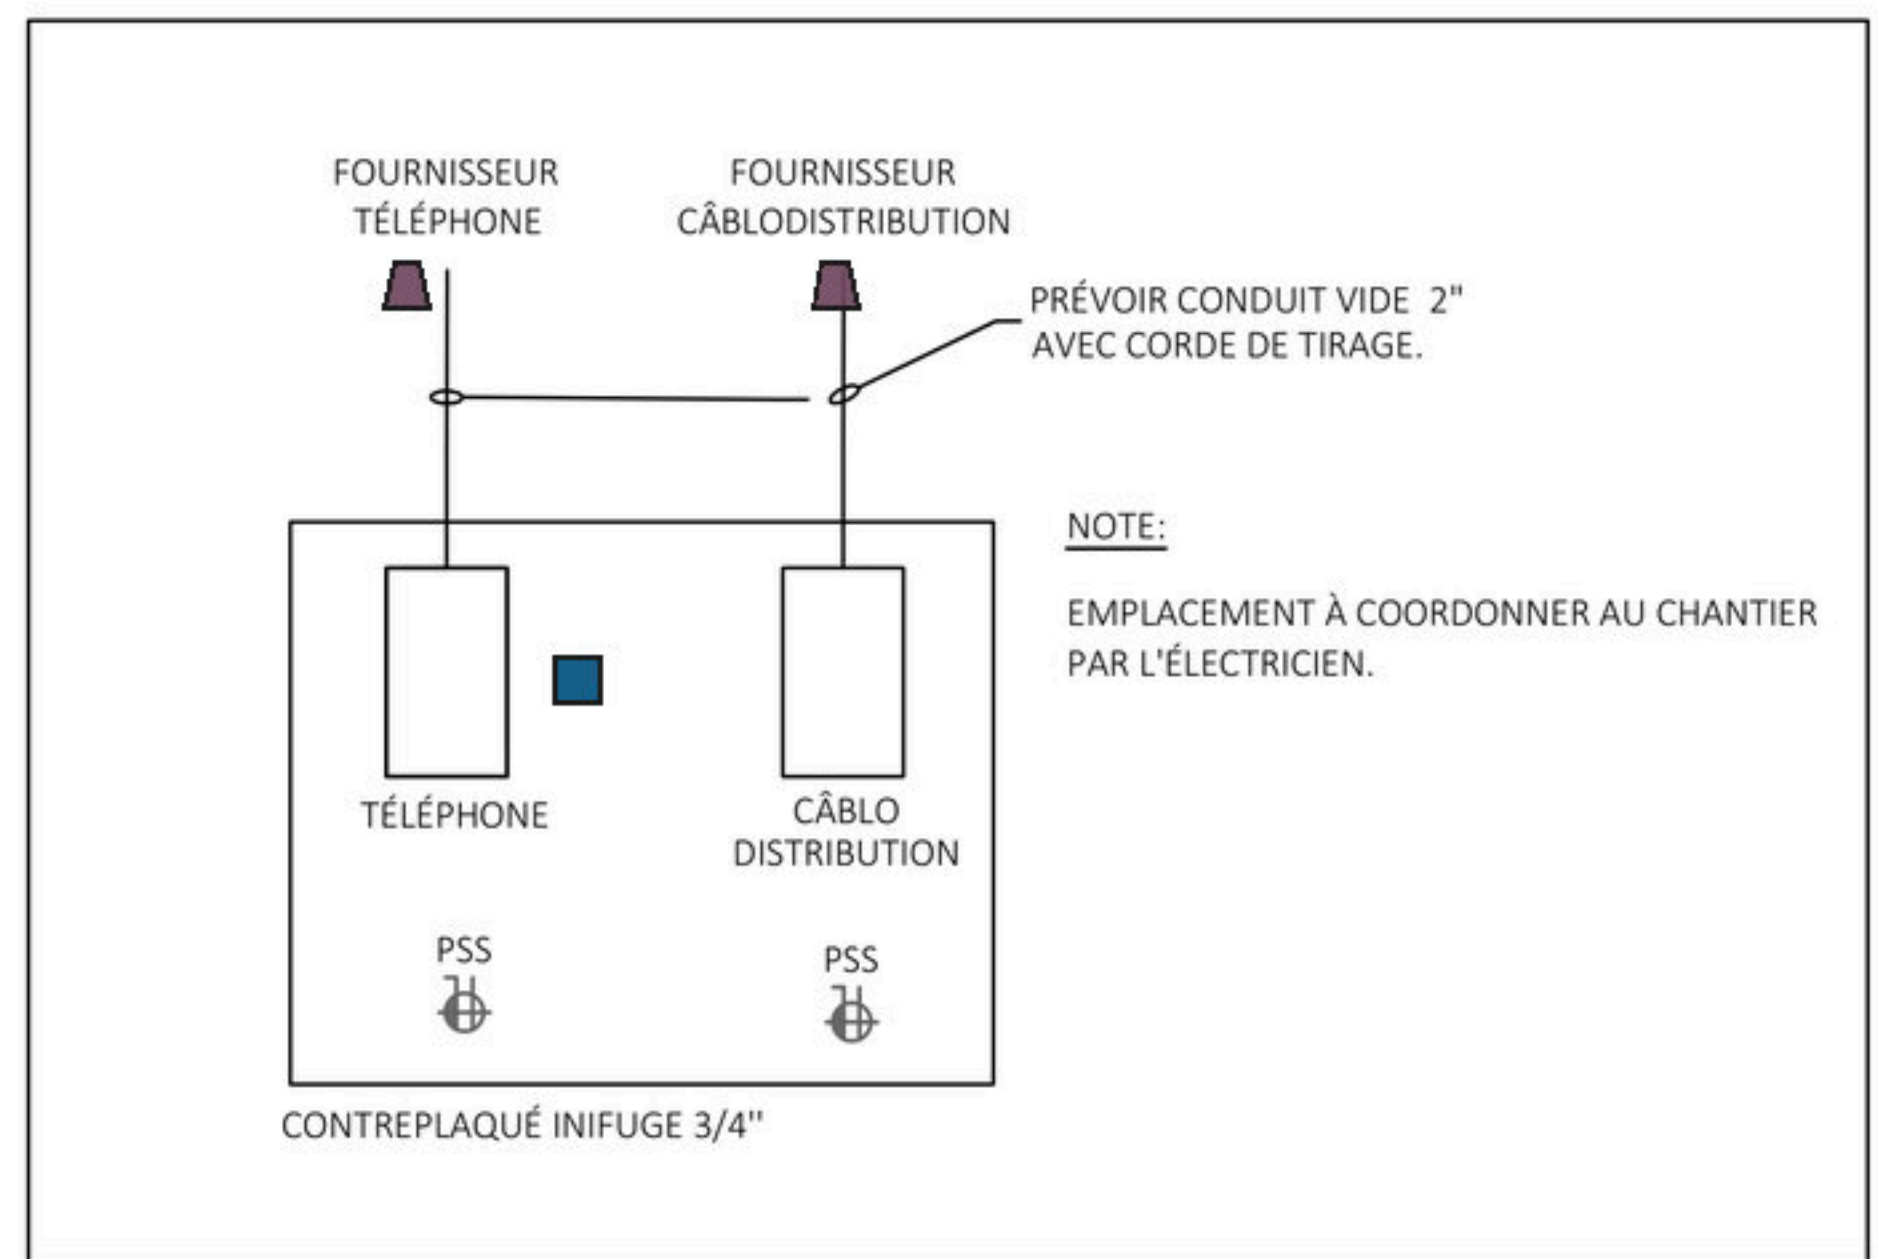

INSTALLATION TYPIQUE CONTREPLAQUÉ CABLODISTRIBUTION
ÉCHELLE: AUCUNE

NOTE SPÉCIFIQUE

1 - MUNI D'UN PADLOCK HASP.

01	2026-06-23	POUR SOUMISSION REV01
00	2026-05-26	POUR SOUMISSION
No.	DATE:	ÉMISSION:



CLIENT:

CPE LES COPAINS D'ABORD

PROJET:


CPE LES COPAINS D'ABORD
PROJET DE REMPLACEMENT

2310 AVENUE BENNY MONTRÉAL, QC, H4B 2R4

TITRE DU PLAN

SCHÉMA UNIFILAIRE
D'ALARME INCENDIE

No DE DOSSIER	25-64		
DESSINÉ PAR:	A. DESJARDINS		
PRÉPARÉ PAR:	A. DESJARDINS		
VÉRIFIÉ PAR:	R. HADDAD		
ÉCHELLE:	AUCUNE	FORMAT	841X594
DATE:	DÉCEMBRE 2025		

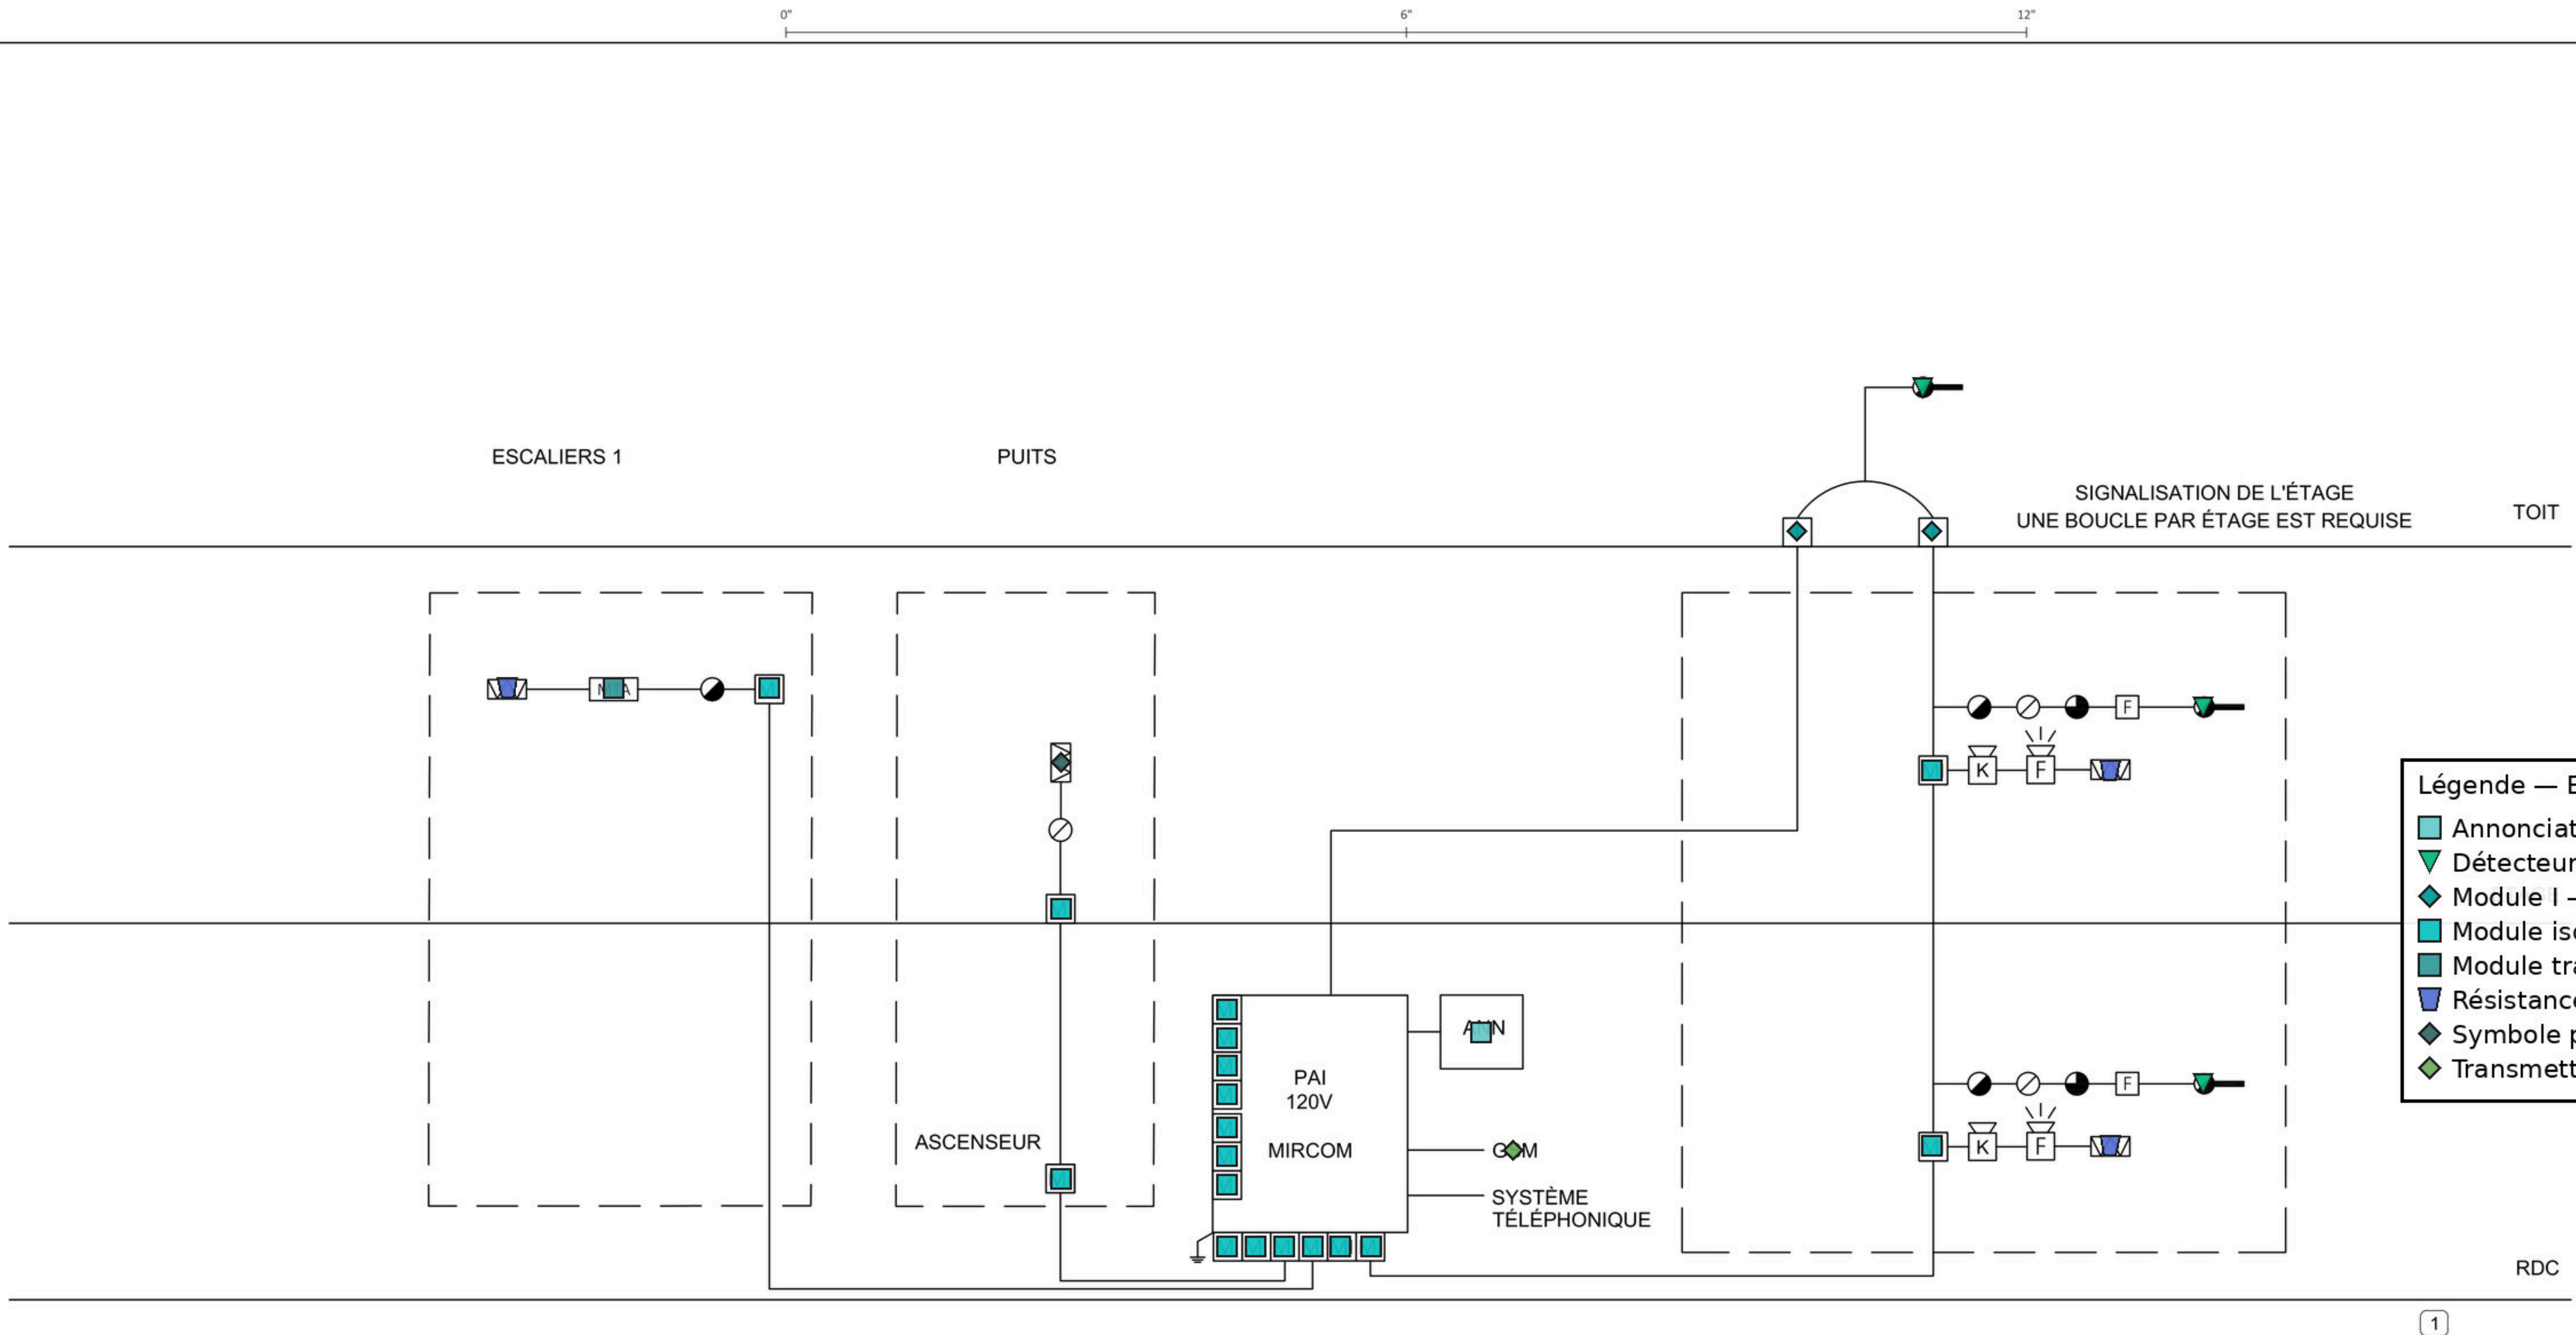

Légende — E020 (30 marques)


- Annonciateur (1)
- Détecteur fumée de gaine (3)
- Module I — à classer (2)
- Module isolateur MI (18)
- Module transmission MTA (1)
- Résistance fin de ligne (3)
- Symbole puits — à classer (1)
- Transmetteur GSM (1)

NOTES SPÉCIFIQUES

- 1 LA HOTTE DE CUISINE H-1 DOIT ÊTRE RACCORDER AU PANNEAU D'ALARME INCENDIE.

NOTES GÉNÉRALES

- LE CONCEPT ILLUSTRÉ AU DIAGRAMME UNIFILAIRE EST BASÉ SUR LES CAPACITÉS ET LES LIMITATIONS D'UN SYSTÈME ADESSABLE. L'ENTREPRENEUR DEVRA ADAPTER SA CONCEPTION SELON LE MANUFACTURIER QU'IL AURA CHOISI ET FOURNI. INSTALLER ET RACCORDER À SES FRAIS TOUS LES ÉQUIPEMENTS SUPPLÉMENTAIRES REQUIS POUR QUE LE SYSTÈME SOIT COMPLET ET FONCTIONNEL.
- LA QUANTITÉ DE DISPOSITIFS MONTREE AUX PLANS PRÉVAUT SUR LA QUANTITÉ INDIQUÉE AU SCHÉMA.
- L'ENTREPRENEUR EST RESPONSABLE DE FOURNIR UN DISPOSITIF DE TRANSMISSION DES DONNÉES CELLULAIRES ET TERRESTRES POUR LE RACCORDEMENT À LA CENTRALE.
- GARDER LIBRE POUR LE FUTUR

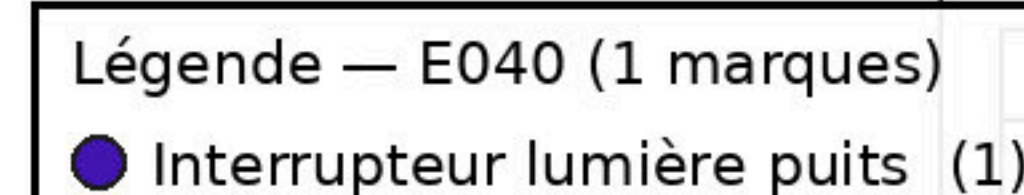

01	2026-06-23	POUR SOUMISSION REV01
00	2026-05-26	POUR SOUMISSION
No.	DATE:	ÉMISSION:



ARCHITECTE:



CLIENT

CPE LES COPAINS D'ABORD

PROJET

CPE LES COPAINS D'ABORD PROJET DE REMPLACEMENT

2310 AVENUE BENNY MONTRÉAL, QC. H4B 2R4

TITRE DU PLAN

DÉTAILS


No DE DOSSIER	25-64		
DESSINÉ PAR:	A. DESIARDINS		
PRÉPARÉ PAR:	A. DESIARDINS		
VÉRIFIÉ PAR:	R. HADDAD		
ÉCHELLE:	AUCUNE	FORMAT	841X594
DATE:	DÉCEMBRE 2025		

PLAN E-040

NOTE GÉNÉRALE

- L'INGÉNIEUR N'EST PAS CONCEPTEUR DES ILLUSTRATIONS, DES EXTRAITS ET TABLEAUX PROVENANT DU CODE DE CONSTRUCTION DU QUÉBEC CHAQUEMENT V. ÉLECTRICITÉ AINSI QUE DES NORMES D'HYDRO-QUÉBEC. IL SE LIMITE SEULEMENT AU CHOIX DES NORMES REQUISE POUR LE PROJET ET NE PEUT ÊTRE TENU RESPONSABLE POUR DES PROBLÈMES RELIÉS À L'APPLICATION DE CES ILLUSTRATIONS, EXTRAITS ET TARI FAUX

No.	DATE:	ÉMISSION:
01	2026-06-23	POUR SOUMISSION REV01
00	2026-05-26	POUR SOUMISSION

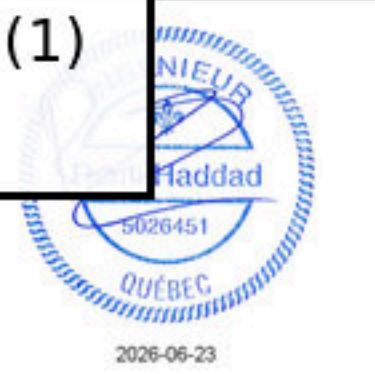

ARCHITECTE:

tracé
l'ère
Bâtir pour l'enfance

CLIENT:

CPE LES COPAINS D'ABORD

PROJET:



CPE LES COPAINS D'ABORD
PROJET DE REMPLACEMENT

2310 AVENUE BENNY MONTRÉAL, QC, H4B 2R4

TITRE DU PLAN:


DÉTAILS (SUITE)

No DE DOSSIER	25-64		
DESSINÉ PAR:	A. DESJARDINS		
PRÉPARÉ PAR:	A. DESJARDINS		
VÉRIFIÉ PAR:	R. HADDAD		
ÉCHELLE:	AUCUNE	FORMAT	841X594
DATE:	DÉCEMBRE 2025		

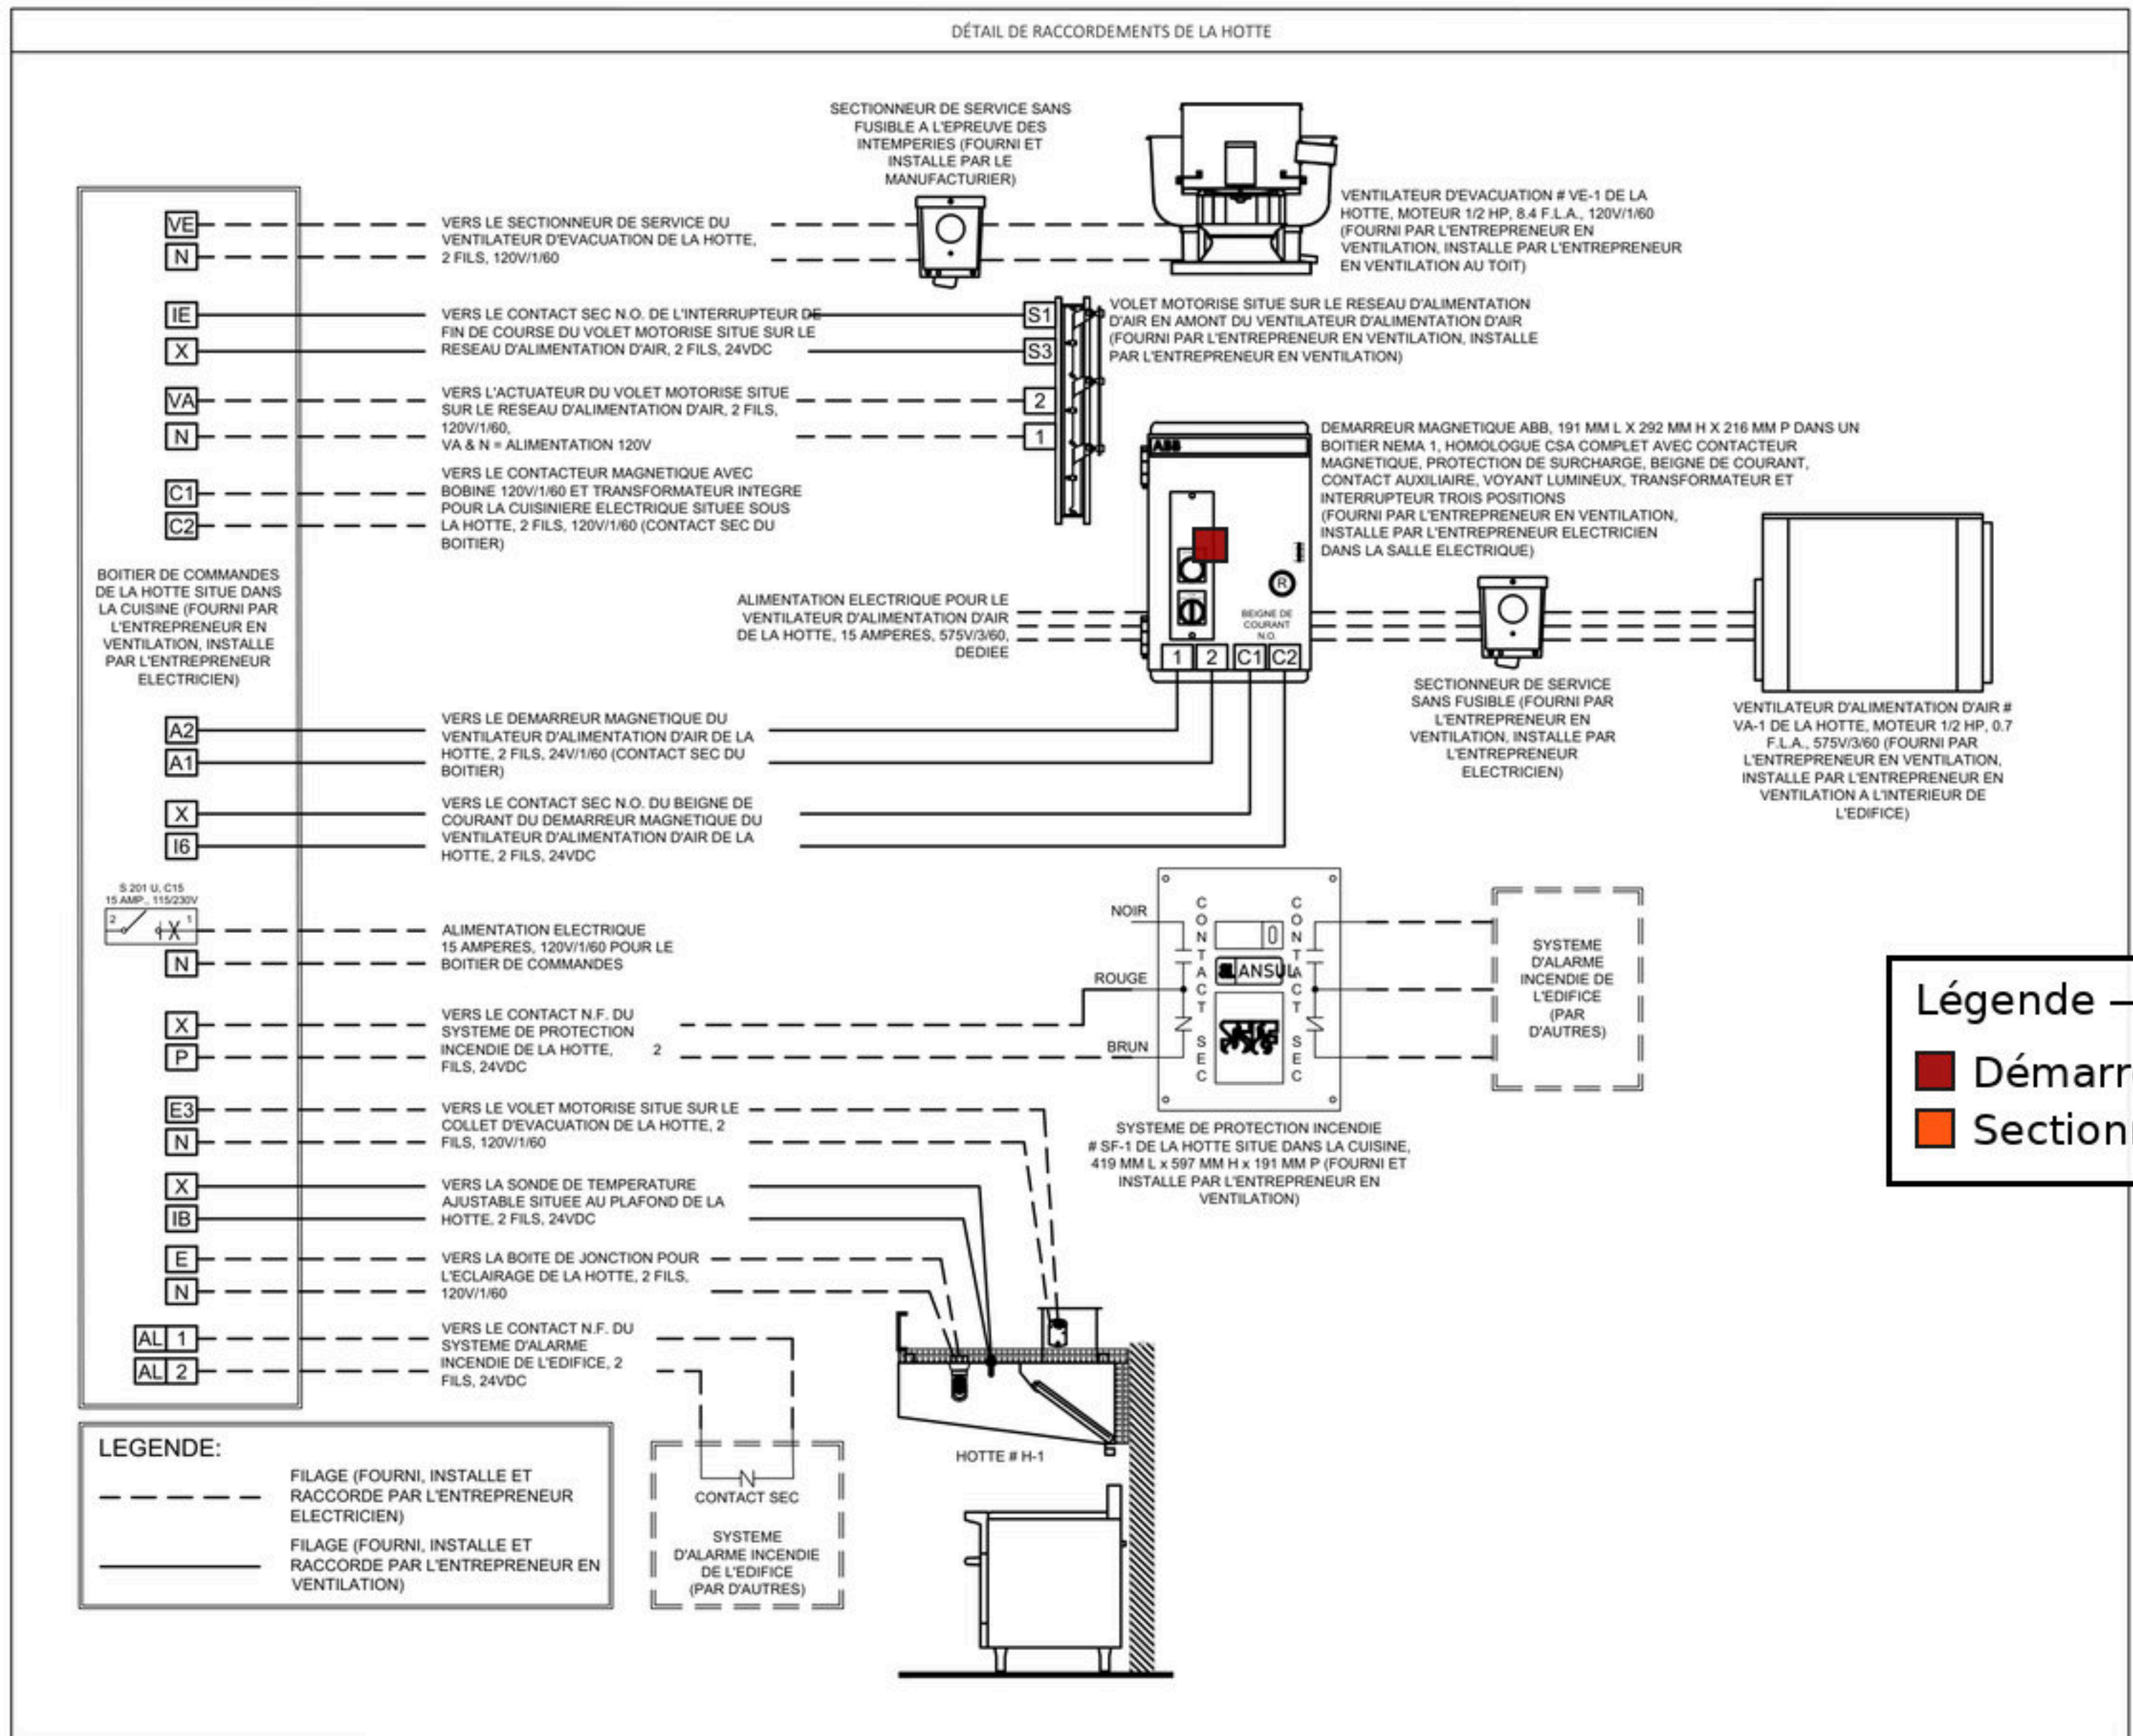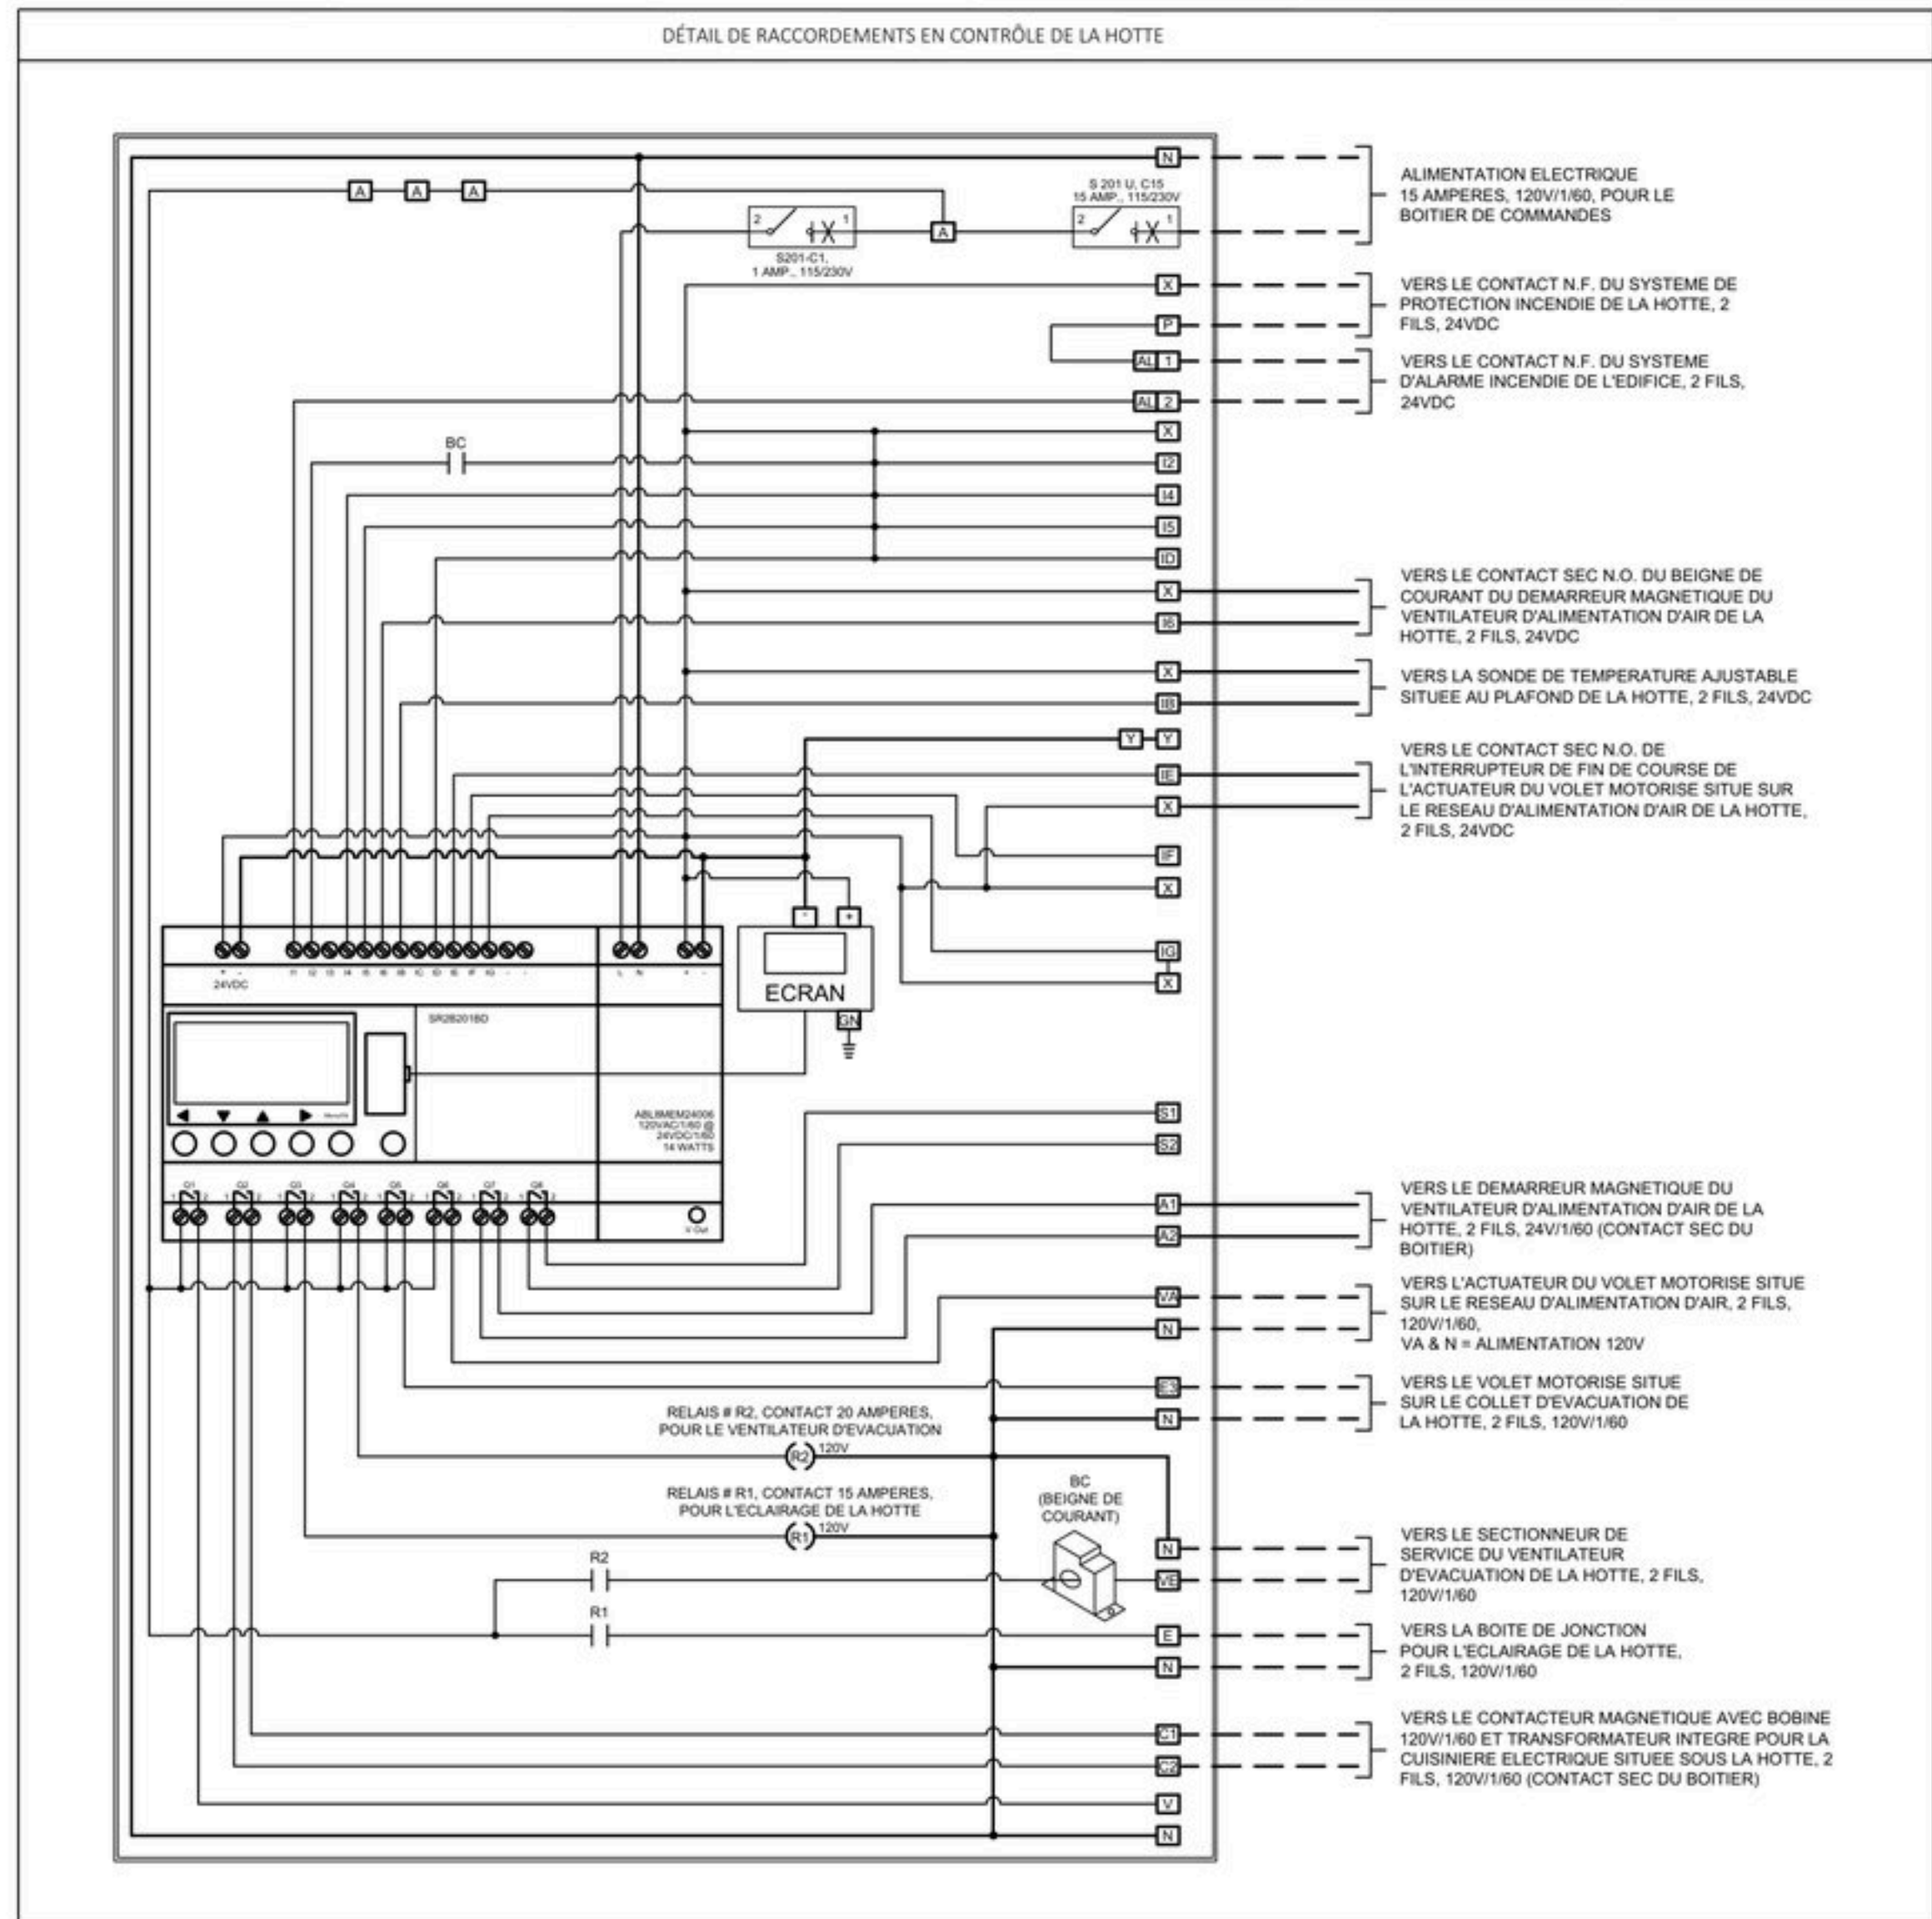

Légende — E041 (2 marques)

- Démarreur hotte — fourni par autres (1)
- Sectionneur à fusibles VA-01 (1)

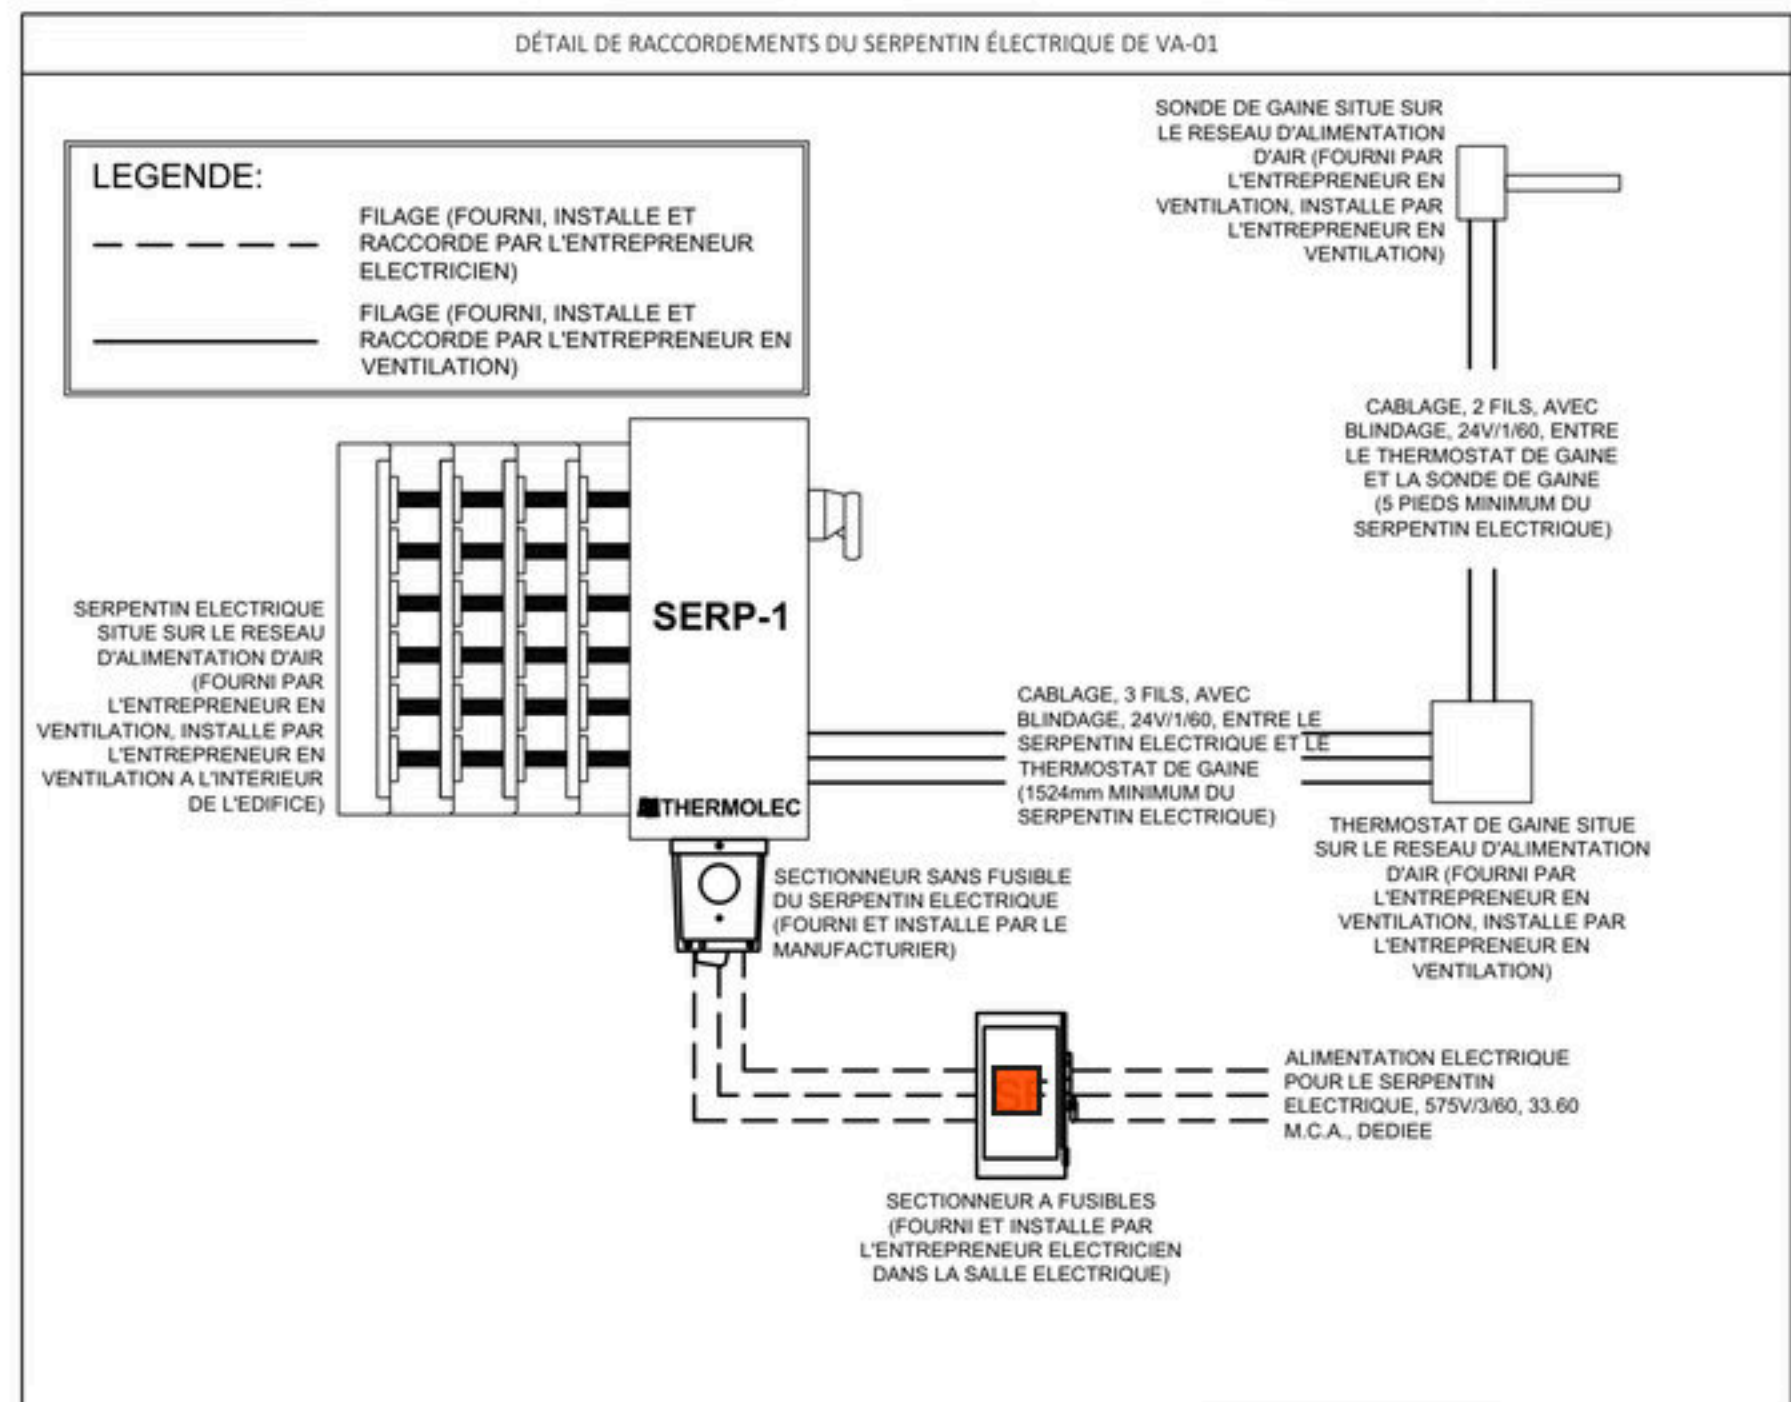

01	2026-06-23	POUR SOUMISSION REV01
00	2026-05-26	POUR SOUMISSION
No.	DATE:	ÉMISSION:

Légende — E050 (1 marques)
■ Point de raccordement HQ (1)



ARCHITECTE:

tracé
l'ère
Bâtir pour l'enfance

CLIENT:

CPE LES COPAINS D'ABORD


PROJET:

CPE LES COPAINS D'ABORD
PROJET DE REMPLACEMENT
2310 AVENUE BENNY MONTRÉAL, QC, H4B 2R4

TITRE DU PLAN

IMPLANTATION

No DE DOSSIER	25-64		
DESSINÉ PAR:	A. DESJARDINS		
PRÉPARÉ PAR:	A. DESJARDINS		
VÉRIFIÉ PAR:	R. HADDAD		
ÉCHELLE:	1:100	FORMAT	841X594
DATE:	DÉCEMBRE 2025		

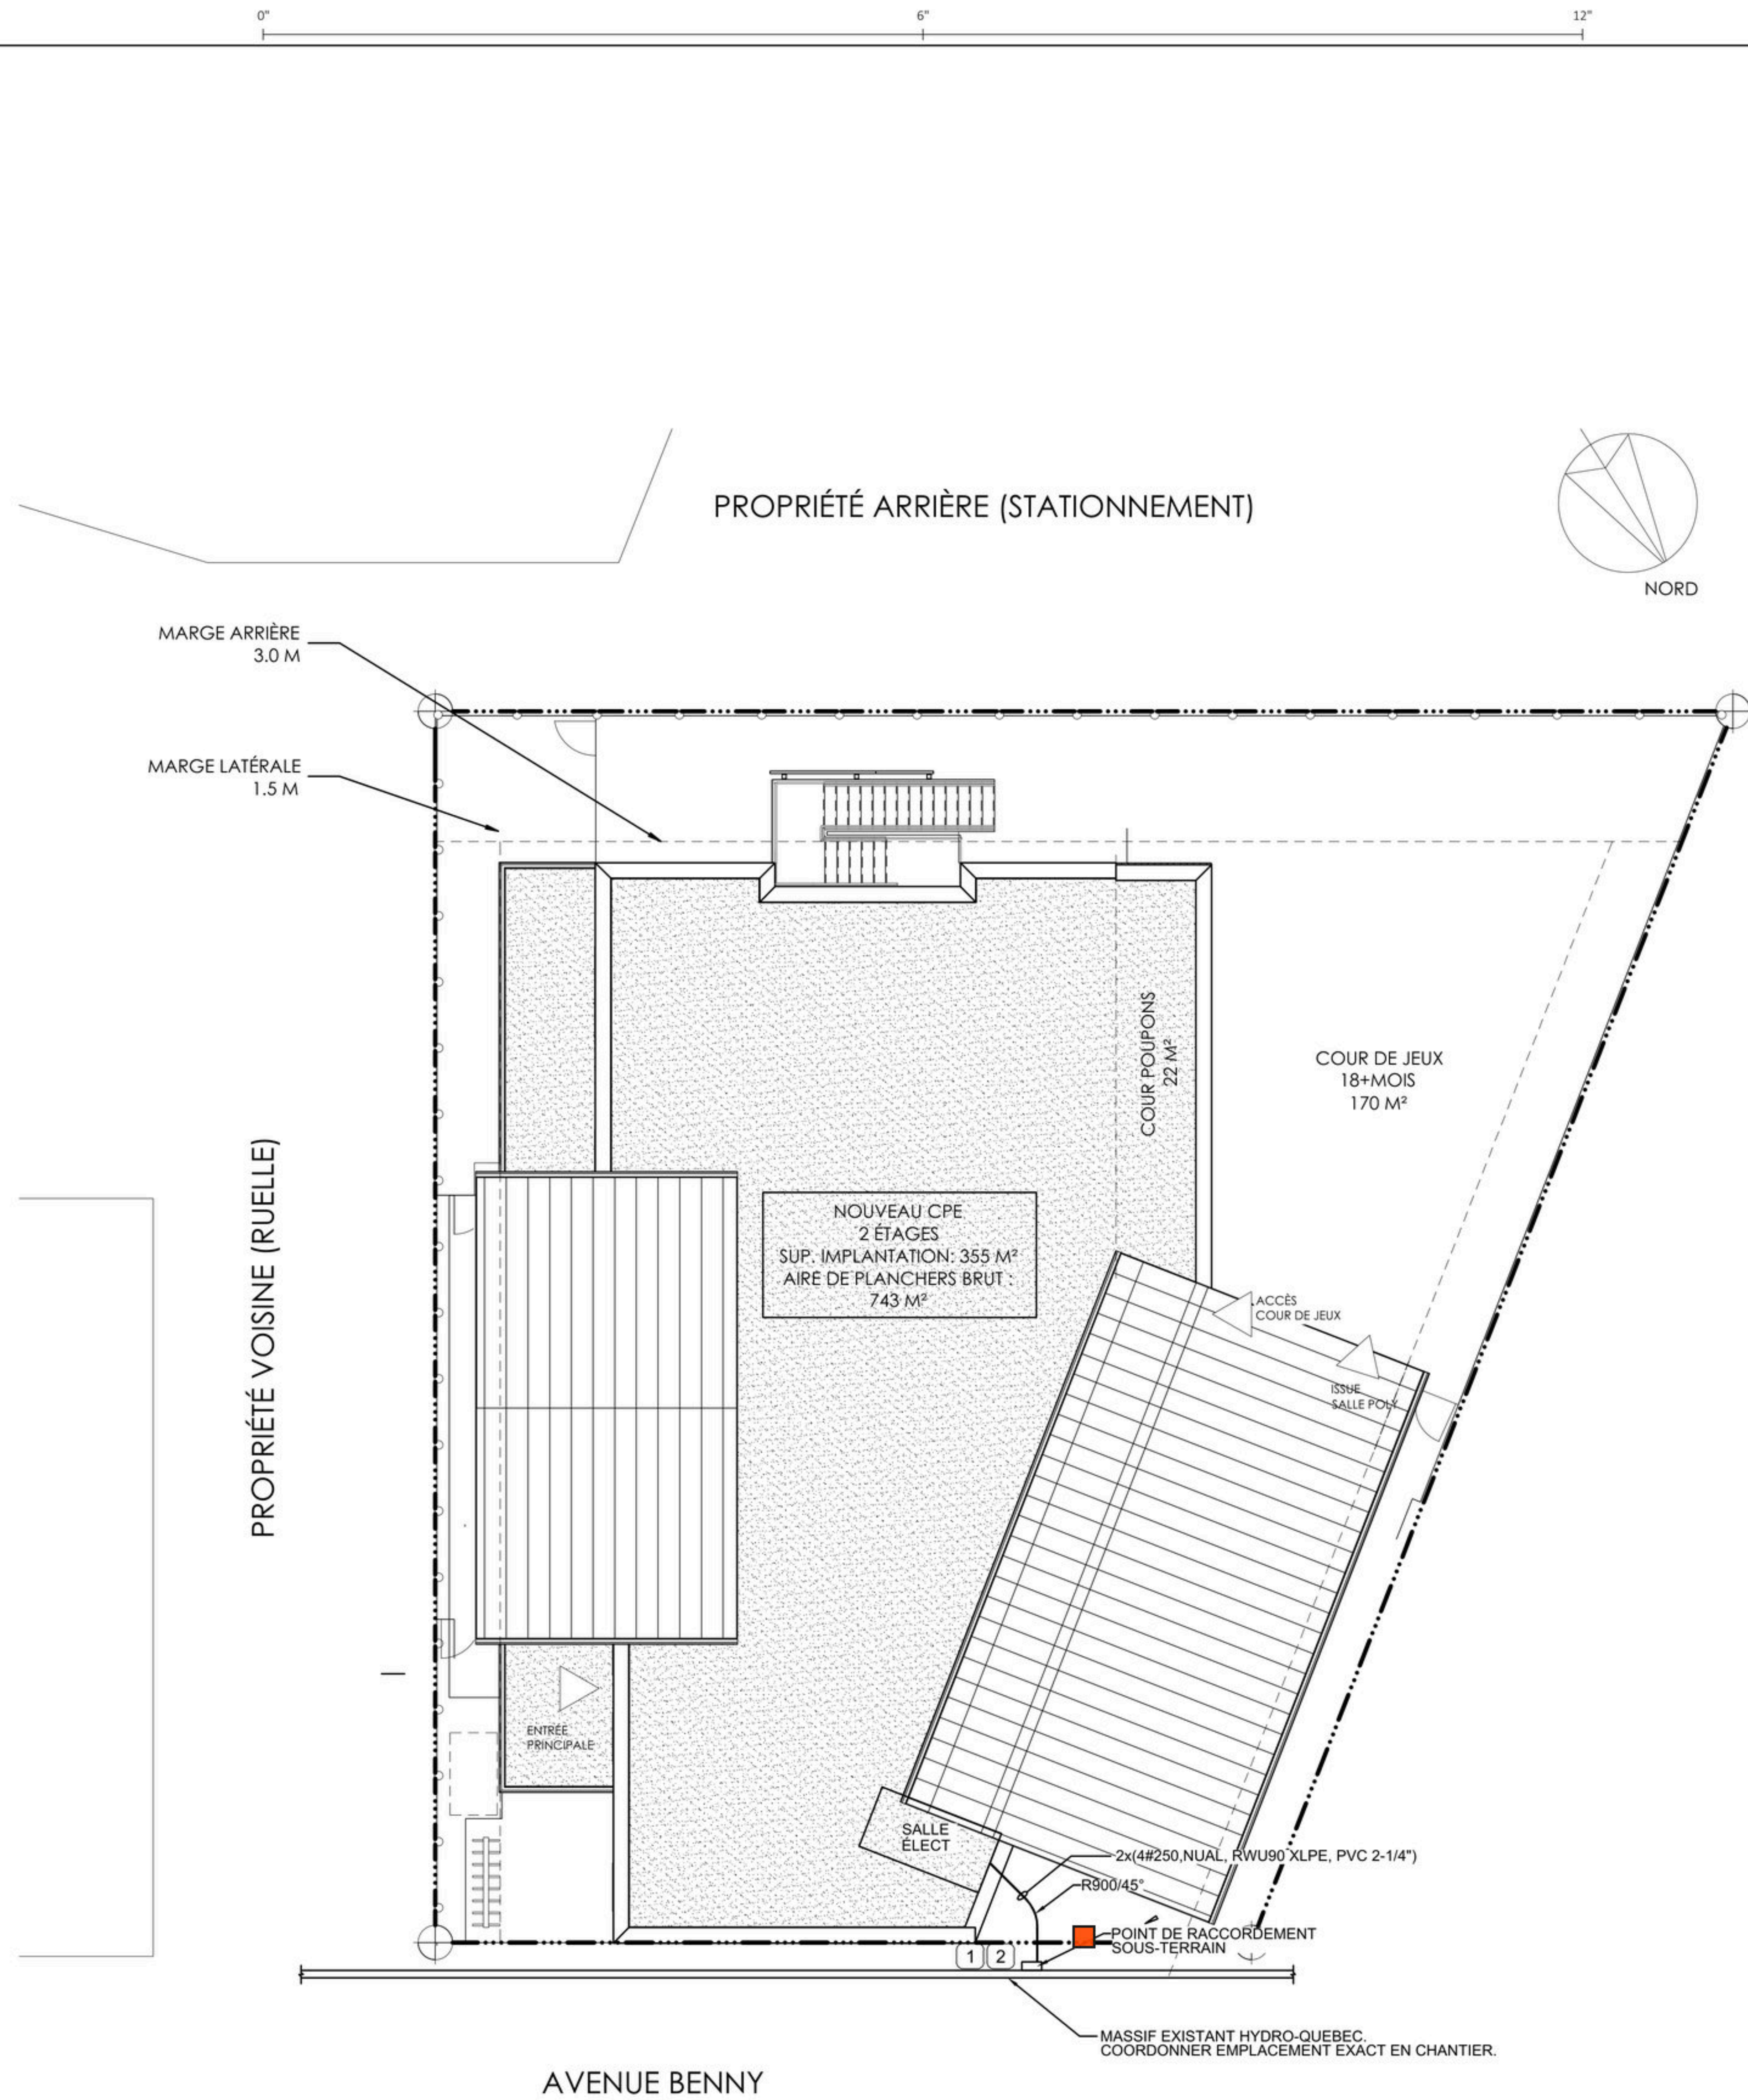


NOTES SPÉCIFIQUES

- CHUTE DE TENSION LIMITÉ À 3% TEL QUE L'ARTICLE (8-102-1-C) POUR LES ARTÈRES DE DÉRIVATIONS. PRÉVOIR CALIBRE PLUS ÉLEVÉ POUR LE FILAGE. IL EST DE LA RESPONSABILITÉ DU CONTRACTEUR DE CHOISIR LE BON CALIBRE POUR LE FILAGE.
- COORDONNER EMPLACEMENT FINAL AVEC HYDRO-QUÉBEC AVANT INSTALLATION.
- PRÉVOIR CORDE DE TIRAGE DANS LES CONDUITS VIDES POUR SERVICES CÂBLE/TELEPHONE (BELL/VIDÉOTRON).

01	2026-06-23	POUR SOUMISSION REV01
00	2026-05-26	POUR SOUMISSION
No.	DATE:	ÉMISSION:

SCAU:

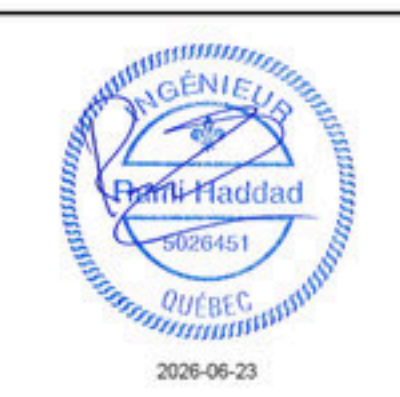

ARCHITECTE:



CLIENT:

CPE LES COPAINS D'ABORD

PROJET:

CPE LES COPAINS D'ABORD
PROJET DE REMPLACEMENT

2310 AVENUE BENNY MONTRÉAL, QC, H4B 2R4

TITRE DU PLAN

ÉLEVATIONS
LATÉRALES NORD ET OUEST


No DE DOSSIER	25-64		
DESSINÉ PAR:	A. DESJARDINS		
PRÉPARÉ PAR:	A. DESJARDINS		
VÉRIFIÉ PAR:	R. HADDAD		
ÉCHELLE:	INDIQUÉE	FORMAT	841X594
DATE:	DÉCEMBRE 2025		



1 ÉLEVATION NORD- FAÇADE AVANT
E-051 1 : 50

Légende — E051 (12 marques)

- Luminaire EX2 (11)
- Luminaire EX3 (1)

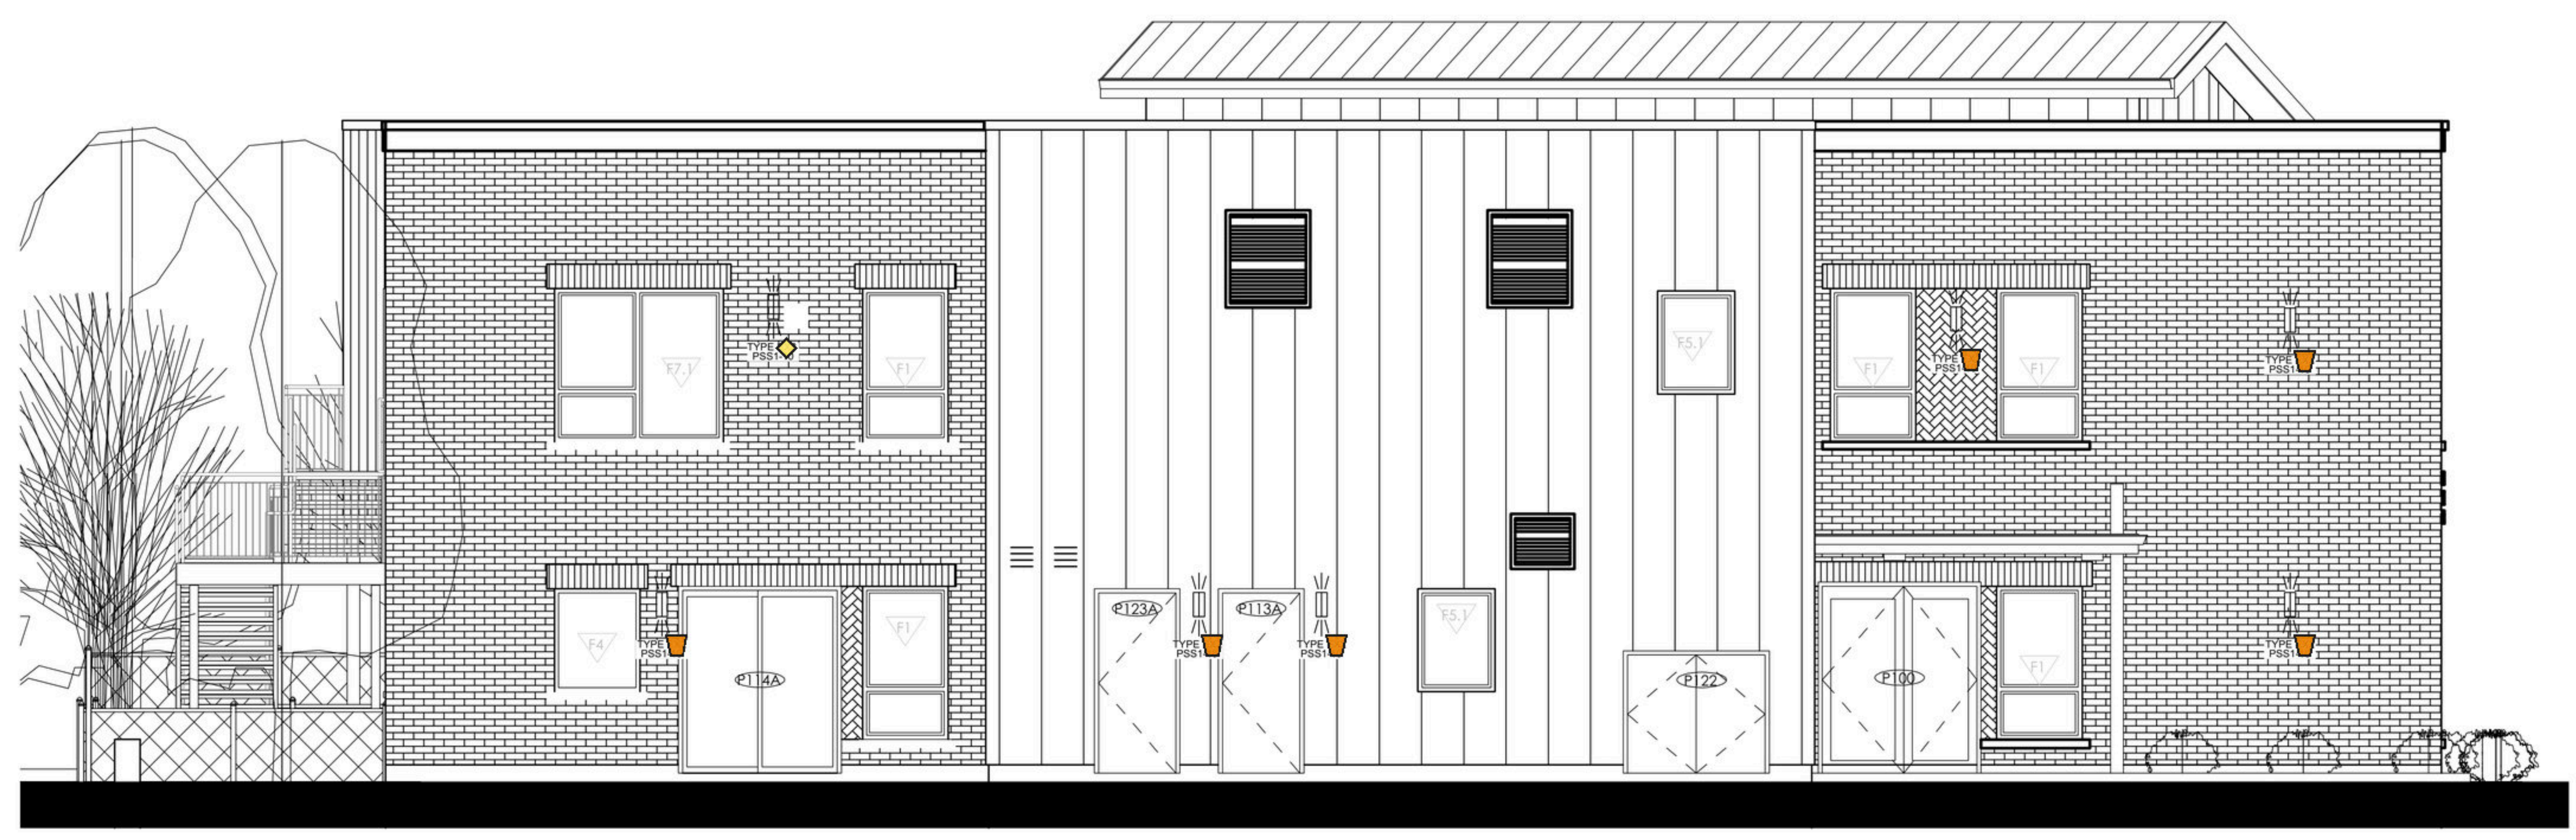

2 ÉLEVATION LATÉRALE OUEST- STATIONNEMENT VOISIN
E-051 1 : 50



Légende — E052 (8 marques)

- Luminaire EX2 (7)
- Luminaire EX3 (1)

1
E-052
ÉLÉVATION ARRIÈRE SUD- COUR
1 : 50



2
E-052
ÉLÉVATION LATÉRALE EST- COUR
1 : 50

No.	DATE:	ÉMISSION:
01	2026-06-23	POUR SOUMISSION REV01
00	2026-05-26	POUR SOUMISSION

SCEAU:

ARCHITECTE:

CLIENT:

PROJET:

TITRE DU PLAN:

No DE DOSSIER	25-64		
DESSINÉ PAR:	A. DESJARDINS		
PRÉPARÉ PAR:	A. DESJARDINS		
VÉRIFIÉ PAR:	R. HADDAD		
ÉCHELLE:	INDIQUÉE	FORMAT	841X594
DATE:	DÉCEMBRE 2025		

PLAN E-052

01	2026-06-23	POUR SOUMISSION REV01
00	2026-05-26	POUR SOUMISSION
No.	DATE:	ÉMISSION:

- Légende — E100 (216 marques)
- ◆ Avertisseur fumée/CO 120V (1)
 - Détecteur de fumée (4)
 - Détecteur mouvement BV (21)
 - Détecteur thermique (17)
 - ▲ Détecteur-gradateur mural (4)
 - ▼ Interrupteur BV 2 scènes (5)
 - ▲ Interrupteur BV 2 scènes grad. (13)
 - Interrupteur simple (2)
 - ▲ Klaxon (7)
 - Luminaire A (55)
 - ◆ Luminaire B (4)
 - Luminaire C (15)
 - ▲ Luminaire D (2)
 - ▲ Luminaire E (6)
 - Luminaire EX1 (8)
 - ▼ Luminaire F (1)
 - Module relais adressable RA (4)
 - Panneau alarme incendie (1)
 - ▲ Piézo-stroboscope (3)
 - ▲ Raccordement hotte H-1 alarme (1)
 - Relais nLight RE (15)
 - Station manuelle (2)
 - Urgence Z1 (4)
 - Urgence Z2 (8)
 - ▲ Urgence Z3 (8)
 - ◆ Urgence Z4 (2)
 - Urgence Z5 (1)
 - Urgence Z6 (2)



LES COPAINS D'ABORD

LES COPAINS D'ABORD
PROJET DE REMPLACEMENT

3310 AVENUE BENNY MONTRÉAL, QC, H4B 2R4

ÉLECTRIQUE
ALARME INCENDIE ET ÉCL.
REZ-DE-CHAUSSÉE

No DE DOSSIER	25-64		
DESSINÉ PAR:	A. DESJARDINS		
PRÉPARÉ PAR:	A. DESJARDINS		
VÉRIFIÉ PAR:	R. HADDAD		
ÉCHELLE:	1:50	FORMAT	841X594
DATE:	DÉCEMBRE 2025		

NOTE SPÉCIFIQUE

- 1 RACCORDER LA HOTTE DE CUISINE H-1 AU PANNEAU D'ALARME INCENDIE, VOIR DÉTAILS PAGE E-041.

01	2026-06-23	POUR SOUMISSION REV01
00	2026-05-26	POUR SOUMISSION
No.	DATE:	ÉMISSION:



CPE LES COPAINS D'ABORD

CPE LES COPAINS D'ABORD
PROJET DE REMPLACEMENT

2310 AVENUE BENNY MONTRÉAL, QC, H4B 2R4

TITRE DU PLAN

ÉLECTRIQUE
ALARME INCENDIE ET ÉCL.
ÉTAGE

No DE DOSSIER	25-64		
DESSINÉ PAR:	A. DESJARDINS		
PRÉPARÉ PAR:	A. DESJARDINS		
VÉRIFIÉ PAR:	R. HADDAD		
ÉCHELLE:	1:50	FORMAT	841X594
DATE:	DÉCEMBRE 2025		

- Légende — E101 (241 marques)
- ◆ Avertisseur fumée/CO 120V (1)
 - Détecteur de fumée (3)
 - Détecteur mouvement BV (22)
 - Détecteur thermique (12)
 - Détecteur-gradateur mural (4)
 - ◆ Gradateur (8)
 - ▼ Interrupteur BV 2 scènes (5)
 - ▲ Interrupteur BV 2 scènes grad. (17)
 - ▲ Klaxon (9)
 - Luminaire A (74)
 - Luminaire C (18)
 - Luminaire D (14)
 - ▲ Luminaire E (6)
 - ▼ Luminaire F (1)
 - ▲ Piézo-stroboscope (1)
 - ▲ Raccordement volet coupe-feu (4)
 - Relais nLight RE (18)
 - Station manuelle (2)
 - Urgence Z1 (7)
 - Urgence Z2 (2)
 - ▲ Urgence Z3 (12)
 - Urgence Z5 (1)

NOTE SPÉCIFIQUE

- 1 RACCORDER LES VOILETS COUPE FEU COUPE FUMÉE AU PANNEAU D'ALARME INCENDIE. SE RÉFÉRER AU PLAN MÉCANIQUE POUR L'EMPLACEMENT EXACT. PRÉVOIR 4 RACCORDEMENTS AU TOTAL POUR L'ÉTAGE.

01	2026-06-23	POUR SOUMISSION REV01
00	2026-05-26	POUR SOUMISSION
No.	DATE:	ÉMISSION:

Légende — E200 (161 marques)

- Aéroconvecteur OAC (2)
- Boîte de tirage (1)
- ◆ Colonne électrique îlot cuisine (1)
- Contacteur (1)
- Contrôle d'accès — porte (4)
- Convecteur SCR (12)
- ◆ Câble chauffant OWC-M (2)
- Embase HQ (1)
- Panneau de distribution (2)
- Plinthe OFM (6)
- ◆ Prise comptoir (4)
- Prise comptoir DDFT (6)
- Prise double (47)
- ▲ Prise double DDFT (3)
- Prise extérieure E.I (8)
- Prise spéciale (2)
- Raccordement AC (11)
- Raccordement AC — à confirmer (1)
- Raccordement VA-01 (1)
- Raccordement four combi (1)
- Raccordement pompe (1)
- ◆ Raccordement serpentín SE (1)
- Raccordement ventilateur VE (3)
- Raccordement évaporateur EVP (1)
- Relais triac RT (17)
- Sectionneur principal 400 A (1)
- ▲ Sortie informatique (5)
- Thermostat AC fourni par autres (11)
- Thermostat intégré TI (3)
- Thermostat plancher chauffant (2)

NOTE GÉNÉRALE

- 1- DANS TOUS LES LOCAUX À L'EXCEPTION DES DORTOIRS, LA SALLE DES EMPLOYÉS, LES BUREAUX ET LES RANGEMENT, LES PRISES DEVRONT ÊTRE INSTALLÉES À UNE HAUTEUR DE 1220mm DE HAUT.
- 2- SAUF INDICATION CONTRAIRE, TOUTES LES PRISES SERONT DE TYPE « TAMPER RESISTANT ».

NOTES SPÉCIFIQUES

- 1 PRÉVOIR ALIMENTATION PAR LE PLAFOND (COLONNE ÉLECTRIQUE POUR PERMETTRE UN OU PLUSIEURS PRISES DANS L'ÎLOT DE LA CUISINE).
- 2 ÉQUIPEMENTS DE CONTRÔLE D'ACCÈS FOURNIS PAR D'AUTRES. L'ÉLECTRICIEN DOIT PRÉVOIR SEULEMENT LES CONDUITS VIDES AINSI QUE L'ALIMENTATION 120V. PRÉVOIR UN RELAIS QUI SERA RACCORDÉ AU PANNEAU D'ALARME INCENDIE. VALIDER, À L'AIDE DES PLANS D'ARCHITECTURE, LES PORTES NÉCESSITANT UNE ALIMENTATION ÉLECTRIQUE DE 120 V.
- 3 PRISE ÉLECTRIQUE 120V, 20A, DDFT, INSTALLÉE À L'HORIZONTALE DANS LE DOSSERET DU COMPTOIR (VOIR PLANS D'ARCHITECTURE POUR RÉFÉRENCE)



CPE LES COPAINS D'ABORD

CPE LES COPAINS D'ABORD
DE REMPLACEMENT

1310 AVENUE BENNY MONTRÉAL, QC, H4B 2R4

ELECTRIQUE
SERVICES
REZ-DE-CHAUSSÉE

No DE DOSSIER	25-64
DESSINÉ PAR:	A. DESJARDINS
PRÉPARÉ PAR:	A. DESJARDINS
VÉRIFIÉ PAR:	R. HADDAD
ÉCHELLE:	1:50
DATE:	DÉCEMBRE 2025

01	2026-06-23	POUR SOUMISSION REV01
00	2026-05-26	POUR SOUMISSION
No.	DATE:	ÉMISSION:

Légende — E201 (133 marques)

- Contrôle d'accès — porte (4)
- Convecteur SCR (18)
- Démarrateur magnétique combiné (1)
- Panneau de distribution (2)
- Plinthe OFM (3)
- Prise comptoir (2)
- Prise comptoir DDFT (9)
- Prise double (40)
- Raccordement AC (9)
- Raccordement ascenseur (1)
- Raccordement chauffe-eau (1)
- Raccordement contrôleur ascenseur (1)
- Raccordement humidificateur (2)
- Raccordement pompe (1)
- Raccordement serpentín SE (3)
- Raccordement ventilateur VE (1)
- Raccordement échangeur d'air (2)
- Relais triac RT (16)
- Sectionneur lumière ascenseur (1)
- Sortie informatique (1)
- Thermostat AC fourni par autres (9)
- Thermostat intégré TI (5)
- Transformateur TX1 (1)

NOTE GÉNÉRALE

- DANS TOUS LES LOCAUX À L'EXCEPTION DES DORTOIRS, LA SALLE DES EMPLOYÉS, LES BUREAUX ET LES RANGEMENT, LES PRISES DEVRONT ÊTRE INSTALLÉES À UNE HAUTEUR DE 1220mm DE HAUT.
- SAUF INDICATION CONTRAIRE, TOUTES LES PRISES SERONT DE TYPE « TAMPER RESISTANT ».

NOTES SPÉCIFIQUES

- ÉQUIPEMENTS DE CONTRÔLE D'ACCÈS FOURNI PAR D'AUTRES. L'ÉLECTRICIEN DOIT PRÉVOIR SEULEMENT LES CONDUITS VIDES AINSI QUE L'ALIMENTATION 120V. PRÉVOIR UN RELAIS QUI SERA RACCORDÉ AU PANNEAU D'ALARME INCENDIE. VALIDER, À L'AIDE DES PLANS D'ARCHITECTURE, LES PORTES NÉCESSITANT UNE ALIMENTATION ÉLECTRIQUE DE 120 V.
- DÉMARRÉUR MAGNÉTIQUE COMBINÉ INSTALLÉ DANS LA SALLE ÉLECTRIQUE.



tracé
l'ère
pour l'enfance

LES COUSINS D'ABORD

LES COUSINS D'ABORD
PROJET DE REMPLACEMENT

2310 AVENUE BENNY MONTRÉAL, QC, H4B 2R4

TITRE DU PLAN

ÉLECTRIQUE
SERVICES
ÉTAGE

No DE DOSSIER	25-64		
DESSINÉ PAR:	A. DESJARDINS		
PRÉPARÉ PAR:	A. DESJARDINS		
VÉRIFIÉ PAR:	R. HADDAD		
ÉCHELLE:	1:50	FORMAT	841X594
DATE:	DÉCEMBRE 2025		

01	2026-06-23	POUR SOUMISSION REV01
00	2026-05-26	POUR SOUMISSION
No.	DATE:	ÉMISSION:

Légende — E202 (9 marques)

▼

Prise service toiture (1)

▼

Prise service toiture — à confirmer (1)

■

Raccordement condenseur (3)

●

Raccordement ventilateur VE (1)

■

Sectionneur E.I toiture (3)

INGÉNIEUR

R. Haddad

2026-05-26

2026-06-23

ARCHITECTE:

tracé

l'ère

Bâtir pour l'enfance

CLIENT:

CPE LES COPAINS D'ABORD

PROJET:


CPE LES COPAINS D'ABORD
PROJET DE REMPLACEMENT

2310 AVENUE BENNY MONTRÉAL, QC, H4B 2R4

TITRE DU PLAN

ÉLECTRIQUE
SERVICES
TOIT

No DE DOSSIER	25-64		
DESSINÉ PAR:	A. DESJARDINS		
PRÉPARÉ PAR:	A. DESJARDINS		
VÉRIFIÉ PAR:	R. HADDAD		
ÉCHELLE:	1:50	FORMAT	841X594
DATE:	DÉCEMBRE 2025		

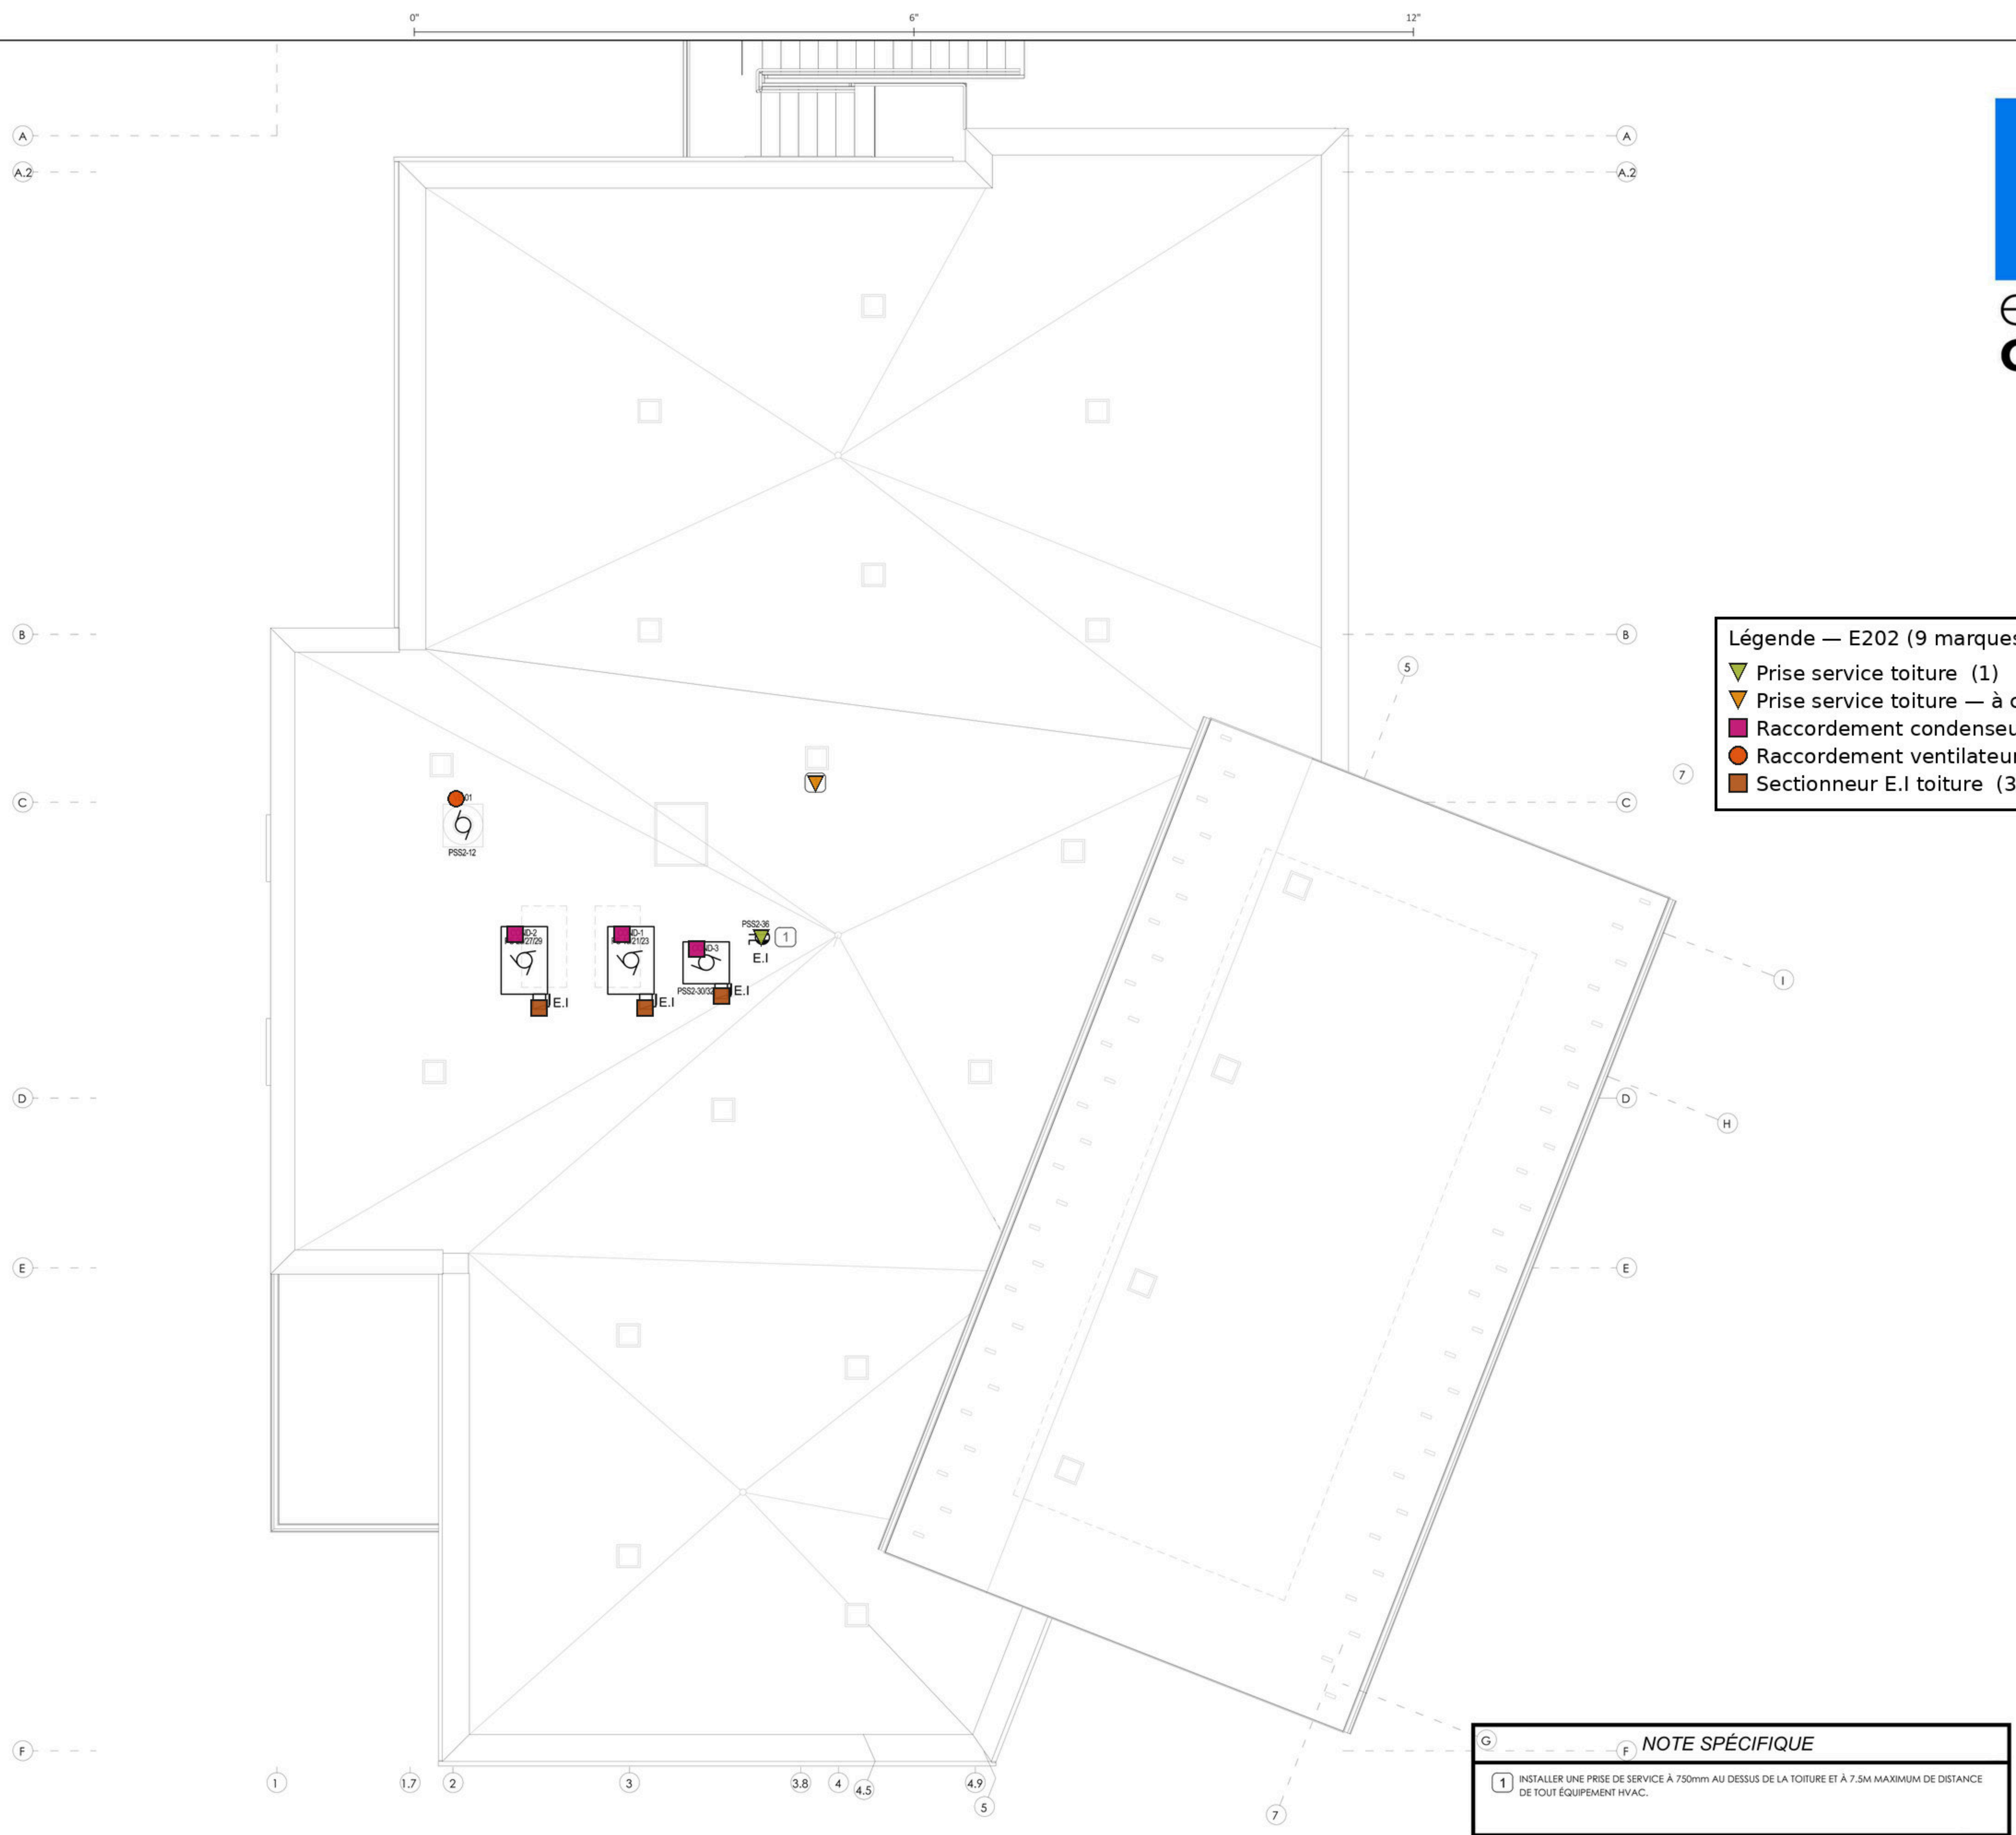

NOTE SPÉCIFIQUE

1 INSTALLER UNE PRISE DE SERVICE À 750mm AU DESSUS DE LA TOITURE ET À 7.5M MAXIMUM DE DISTANCE DE TOUT ÉQUIPEMENT HVAC.