

GENERAL NOTE(S)
NOTE(S) GÉNÉRALE(S):

1- UNLESS OTHERWISE, ALL LIGHTING FIXTURES ARE POWERED BY P1-2P0PMAN-1.
SAUF INDICATION CONTRAIRE, TOUTS LES APPARELS D'ÉCLAIRAGE SONT ALIMENTÉS PAR LE PANNEAU P1-2P0PMAN-1.

2- ALL LIGHTING FIXTURES SHOULD BE POWERED WITH AWG #10 CONDUCTORS TO COMPENSATE THE VOLTAGE DROP.
TOUTS L'ÉCLAIRAGE DEVAIT ÊTRE ALIMENTÉ AVEC DES CONDUCTEURS AWG #10 POUR PALIER À LA CHUTE DE TENSION.

3- THE EMERGENCY LIGHTING IS POWERED FROM 120V BATTERY UNITS. MINI-INVERTERS, M1 AND M2, THE FIXTURES SHOULD BE CONTROLLED AS DESIGNED FOR NORMAL OPERATION OF THE BUILDING, BUT BE POWERED ON AT FULL CAPACITY IN CASE OF A POWER OUTAGE.
L'ÉCLAIRAGE D'URGENCE EST ALIMENTÉ À PARTIR DES DISPOSITIFS À BATTERIES 120V MINI-ONDULEURS M1 ET M2. LES APPARELS DEVONT FONCTIONNER SELON LE CONTRÔLE NORMAL DÉFINI DANS LE BÂTIMENT, MAIS S'ALLUMER À PLEINE CAPACITÉ EN CAS DE PANNE DE COURANT.

IDENTIFICATION(S)
1- MINI-INVERTER AT 120V FOR EMERGENCY LIGHTING.
MINI-ONDULEUR À 120V POUR ÉCLAIRAGE D'URGENCE.

LEVEL OF SECURITY | NIVEAU DE SÉCURITÉ

This design is an instrument of service and is protected by copyright, copyright for the consultant's instrument of service belongs to the consultant. Copies including electronic copies, may only be used for the purpose intended and for a one time use, on the same site, and for the same project and may not be offered for sale or transfer without the express written consent of the consultant.
Le présent dessin est un instrument de service protégé par le droit d'auteur. Le droit d'auteur sur l'instrument de service de l'ingénieur appartient à ce dernier. Les exemplaires de ce dessin, y compris les exemplaires électroniques, ne peuvent servir qu'àux fins prévues, et ce, qu'une fois, sur le même chantier et pour le même projet. Ils ne peuvent être offerts en vente ni transférés sans le consentement écrit exprès de l'ingénieur.

NORR

NORR Architects & Engineers Limited

55 Murray Street, Suite 600
Ottawa, ON, Canada K1N 5M3
NORR.COM

PAGEAU
MOREL
www.pageaumorel.com
Montréal

THIS DRAWING SHALL NOT BE USED FOR
CONSTRUCTION OR INSTALLATION PURPOSE.



CE PLAN NE DOIT PAS ÊTRE UTILISÉ À DES
FINS DE CONSTRUCTION OU D'INSTALLATION.

Légende — S267_ADD_21 (272 marques)

- A1 Troffer 2x4 (53)
- A1 Troffer 2x4 urgence (6)
- B1 Troffer 2x2 (4)
- C1 Spot encastré (24)
- C2 Spot lieux humides (36)
- C3 Spot boîtier 2h (10)
- C3 Spot boîtier 2h urgence (7)
- D1 High bay (29)
- D1 High bay urgence (14)
- Détecteur de présence plafond (2)
- E1 Réglette 4 pi (12)
- E1 Réglette 4 pi urgence (4)
- Gradateur (6)
- Interrupteur avec détecteur de présence (37)
- Interrupteur unipolaire (4)
- Mini-onduleur 12V (2)
- X1 Enseigne d'issue (18)

2 MINI-INVERTER / MINI-ONDULEUR

SCALE: 1:50
ÉCHELLE: 1:50

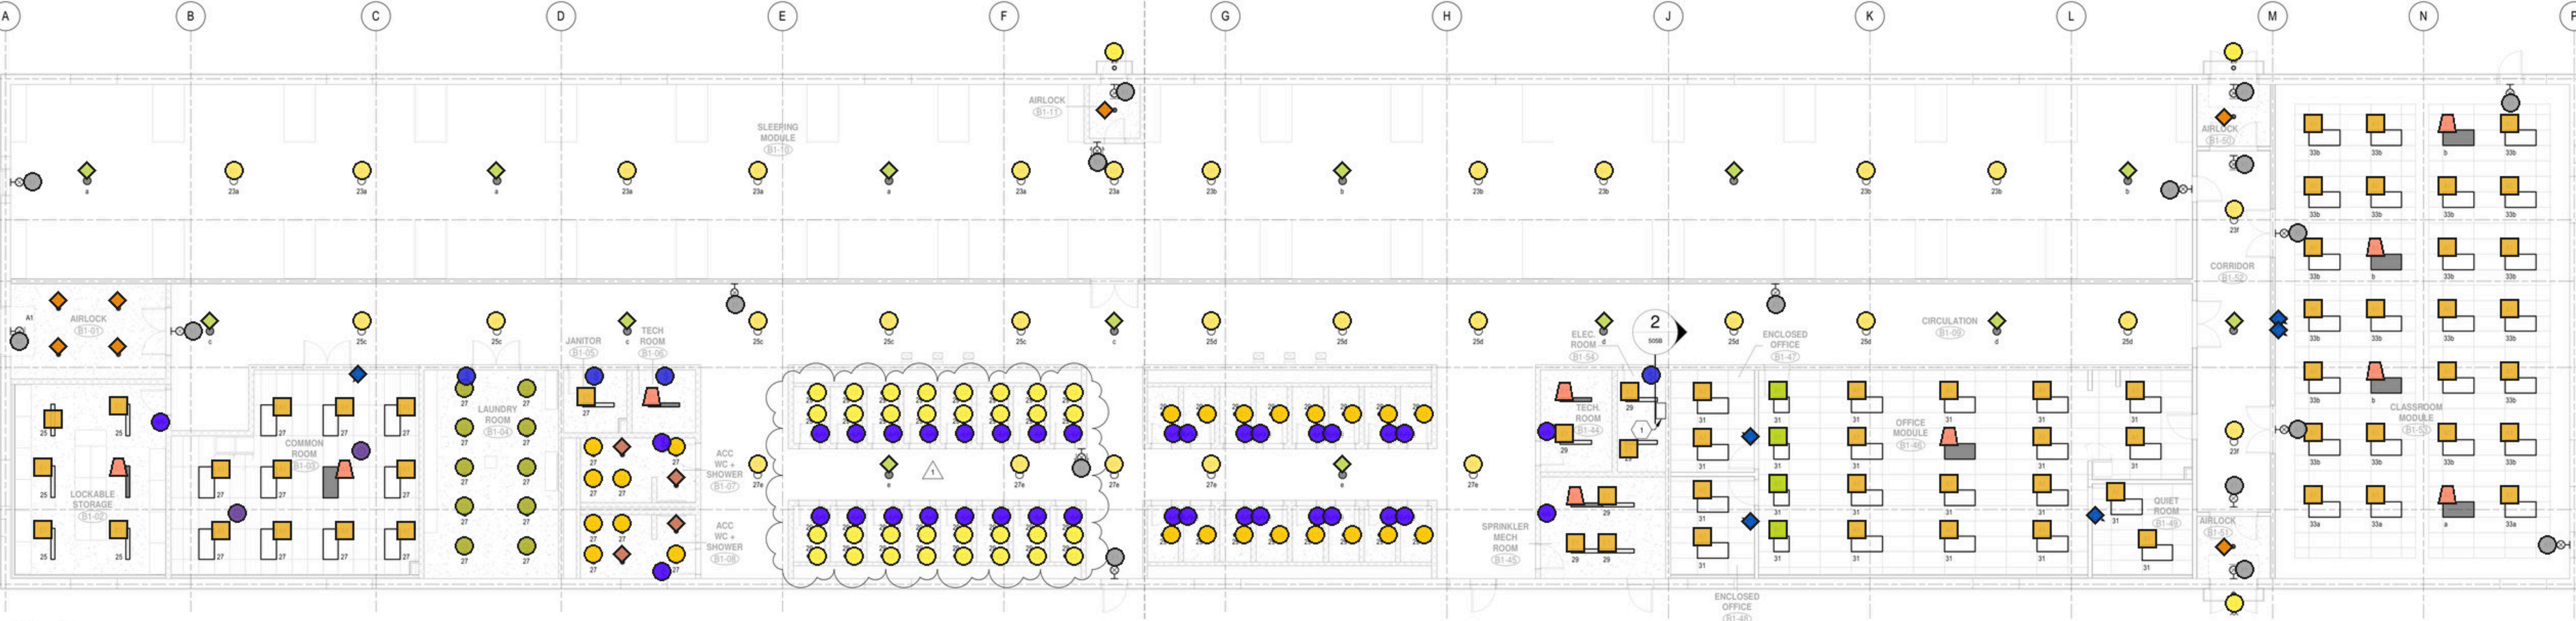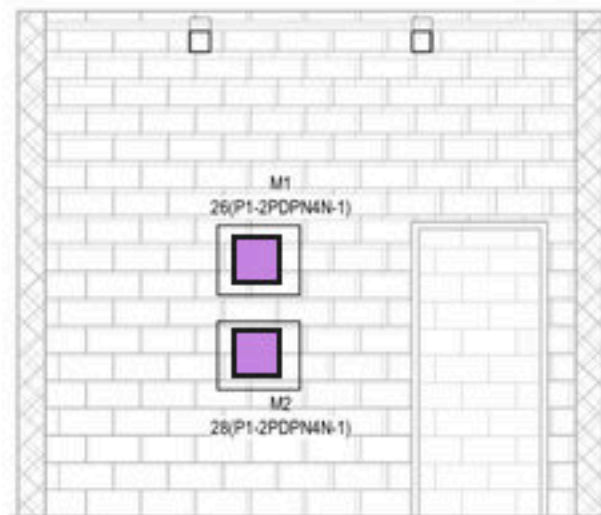

1 ÉCLAIRAGE/ LIGHTING - VUE EN PLAN / PLAN VIEW

SCALE: 1:100
ÉCHELLE: 1:100

1	2026-06-16	ADDENDA MEP-01	
0	2026-04-28	FOR TENDER / POUR SOUMISSIONS	
NO.	DATE	REVISION	APPR.
SCALE ÉCHELLE			
AS NOTED ÉCHELLE TELLE QU'ELLE EST ILLUSTRÉE			
LOCATION EMPLACEMENT			
ST. JEAN GARRISON, QC			
GARRISON DE SAINT-JEAN, QC			
PROJECT PROJET			
STJ-CONSTRUCT 6 NEW			
ACCOMODATION BUILDINGS /			
STJ-CONSTRUIRE 6 NOUVEAUX			
BÂTIMENTS D'HÉBERGEMENT			
TRADE MÉTIER		DATE	
ELECTRICAL / ÉLECTRICITÉ		03/06/26	
SUBJECT SUJET			
LIGHTING LVL 1			
ÉCLAIRAGE NIVEAU 1			
PRODUCTION		REVIEWED REVU	
DESIGNED ÉTUDE		DES O AGENT CONC.	
AMUEL LAPRISE, ing		PRO MGR GÉST PROJ.	
DRAWN DESSIN		DES MGR GÉST CONC.	
ANDY BOUCHER		FIRE INCENDIE	
CHECKED VÉRIFIÉ			
AMUEL LAPRISE, ing			
COORDINATION			
WBS NUMBER NO. SRT		PF NUMBER NO. DP	
N.306844.24		QS-000428-B	
DWG. NO. NO. DESSIN		L-S267-1302-01- 505B	



-  Armoire de mesure HQ type B (1)
-  C1.1 Plinthe 500W (34)
-  C2.2 Convecteur 4000W (3)
-  C3.2 Aérotherme 8000W (1)
-  C4.1 Plinthe 1500W (11)
-  C5.1 Convecteur 2000W (2)
-  C5.2 Convecteur 2000W (1)
-  C6.1 Plinthe 1000W (4)
-  Interrupteur principal 400A (1)
-  Panneau 120/208V (2)
-  Panneau 347/600V (1)
-  Point de raccordement panneau de contrôle (1)
-  Point de raccordement plomberie (32)
-  Point de raccordement porte automatique (4)
-  Point de raccordement volet coupe-feu (6)
-  Prise DDFT 5-15R (cercle) (8)
-  Prise DDFT 5-15R (triangle) (2)
-  Prise double 5-15R (108)
-  Prise double 5-15R (triangle) (2)
-  Prise double 5-15R WP (1)
-  Prise double 5-20R (25)
-  Raccordement chauffe-eau WH (3)
-  Raccordement condenseur CS (3)
-  Raccordement humidificateur HU (3)
-  Raccordement pompe PU1 (1)
-  Raccordement ventilateur HVLS CF (4)
-  Raccordement ventilateur TF (2)
-  Raccordement évaporateur EV (2)
-  Sectionneur $\leq 240V$ (8)
-  Sectionneur $\leq 240V$ WP (3)
-  Serpentin EHC1 19 kW (3)
-  Serpentin EHC1-006 500W (3)
-  Serpentin EHC2 15 kW (3)
-  Serpentin EHC3 3 kW douche (1)
-  Sortie télécom (15)
-  Transformateur sec 112.5 kVA (1)

1. 2024-06-26		AGENDA MEETING			
2. 2024-06-28		FOR TENDER			
NO. DATE		NEWSPAPER		OUR SOUMISSIONS	
SOCIÉTÉ / SOCIÉTÉ				APPR.	
(3) IS NOTED / SOCIÉTÉ TELLER				ELLE EST ILLUSTRÉE	
ST. JEAN GARRISON				. QC	
(4) CORNISON DE SAINT				-JEAN. QC	
PROJECT / PROJET					
STJ-CONSTR				UCT 6 NEW	
ACCOMODATION				N BUILDINGS /	
STJ-CONSTRUIRE				E 6 NOUVEAUX	
BÂTIMENTS D'H				BERGEMENT	
TRADE / MÉTIER					
ELECTRICAL / ÉLECTRICIEN		DITÉ		DATE	
SUBJECT / SUJET				03/06/26	
SERVICE				S LVL 1	
SERVICES				NIVEAU 1	
DESIGNED / ÉTUDE		REVIEWED / REVU			
SAMUEL LAPRISE, ing				DES O / GESTION CON	
DRAWN / DESSINE				PRO MGR / GÉST PRO	
SANDY BOUCHER					
CHECKED / VÉRIFIÉ				DES MGR / GÉST CON	
SAMUEL LAPRISE, ing					
COORDINATION				FIRE / INCENDIE	
WBS NUMBER / NO. SRT		PF NUMBER / NO. DP			
N.306844.24		QS-000428-B			
DWG. NO. / NO. DESSIN					

1

IDENTIFICATION(S)

1

ADRESSABLE FIRE ALARM RELAY TO STOP HVAC UNIT ON THE ROOF IN CASE OF A FIRE.
MODULE DE RELAIS ADRESSABLE POUR ARRÊTER LES UNITES DE VENTILATION AU TOIT EN CAS D'ALARME INCENDIE.

Gouvernement du Canada

Gouvernement du Canada

LEVEL OF SECURITY | NIVEAU DE SÉCURITÉ

This design is an instrument of service and is protected by copyright, copyright for the consultant's instrument of service belongs to the consultant. Copies including electronic copies, may only be used for the purpose intended and for a one time use, on the same site, and for the same project and may not be offered for sale or transfer without the express written consent of the consultant.

Le présent dessin est un instrument de service protégé par le droit d'auteur. Le droit d'auteur sur l'instrument de service de l'expert conseil appartient à ce dernier. Les exemplaires de ce dessin, y compris les exemplaires électroniques, ne peuvent servir qu'aux fins prévues, et ce, qu'une fois, sur le même chantier et pour le même projet. Ils ne peuvent être offerts en vente ni transférés sans le consentement écrit exprès de l'expert conseil.

NORR

NORR Architects & Engineers Limited

55 Murray Street, Suite 600
Ottawa, ON, Canada K1N 5M3
NORR.COM

PAGEAU
MOREL

www.pageaumorel.com
Montréal

THIS DRAWING SHALL NOT BE USED FOR CONSTRUCTION OR INSTALLATION PURPOSE.
CE PLAN NE DOIT PAS ÊTRE UTILISÉ À DES FINS DE CONSTRUCTION OU D'INSTALLATION.

Légende — S267_ADD_23 (12 marques)

Module de relais ARM (3)

Raccordement UTA toit RT (3)

Raccordement prise UTA toit (fournie par fabricant) (3)

Raccordement unité HE toit (3)

1

SERVICES / SERVICES PLAN VIEW / VUE EN PLAN

SCALE: 1:100
ÉCHELLE: 1:100

2026-06-16

1

2026-06-16

ADDENDA MEP-01

0

2026-04-28

FOR TENDER / POUR SOUMISSIONS

NO.

DATE

REVISION

APPR.

SCALE | ÉCHELLE

AS NOTED | ÉCHELLE TELLE QU'ELLE EST ILLUSTRÉE

LOCATION | EMPLACEMENT

ST. JEAN GARRISON. QC
GARNISON DE SAINT-JEAN. QC

PROJECT | PROJET

STJ-CONSTRUCT 6 NEW
ACCOMMODATION BUILDINGS /
STJ-CONSTRUIRE 6 NOUVEAUX
BÂTIMENTS D'HÉBERGEMENT

TRADE | MÉTIER

ELECTRICAL / ÉLECTRICITÉ

DATE

03/06/26

SUBJECT | SUJET

SERVICES AND AUXILIARY
SERVICES ROOF
SERVICES ET SERVICES
AUXILIAIRES TOIT

PRODUCTION

DESIGNED | ÉTUDE

SAMUEL LAPRISE .ing

DRAWN | DESSIN

SANDY BOUCHER

CHECKED | VÉRIFIÉ

SAMUEL LAPRISE .ing

COORDINATION

REVIEWED | REVU

DES O-AGENT CONC.

PRO MGR | GÉST PROJ.

DES MGR | GÉST CONC.

FIRE | INCENDIE

WBS NUMBER | NO. SRT

N.306844.24

PF NUMBER | NO. DP

QS-000428-B

DWG. NO. | NO. DESSIN

L-S267-1302-01-507B

Canada

2026-06-16 12:17

LEVEL OF SECURITY / NIVEAU DE SÉCURITÉ

This design is an instrument of service and is protected by copyright, copyright for the consultant's instrument of service belongs to the consultant. Copies including electronic copies, may only be used for the purpose intended and for a one time use, on the same site, and for the same project and may not be offered for sale or transfer without the express written consent of the consultant.

Le présent dessin est un instrument de service protégé par le droit d'auteur. Le droit d'auteur sur l'instrument de service de l'ingénieur appartient à ce dernier. Les exemplaires de ce dessin, y compris les exemplaires électroniques, ne peuvent servir qu'àux fins prévues, et ce, qu'une fois, sur le même chantier et pour le même projet. Ils ne peuvent être offerts en vente ni transférés sans le consentement écrit exprès de l'ingénieur.

NORR

NORR Architects & Engineers Limited

55 Murray Street, Suite 600
Ottawa, ON, Canada K1N 5M3
NORR.COM

PAGEAU MOREL


www.pageaumorel.com
Montréal

THIS DRAWING SHALL NOT BE USED FOR CONSTRUCTION OR INSTALLATION PURPOSE.
CE PLAN NE DOIT PAS ÊTRE UTILISÉ À DES FINS DE CONSTRUCTION OU D'INSTALLATION.

IDENTIFICATION(S)

- 1 POWER SUPPLY
BLOC D'ALIMENTATION
- 2 ADDRESSABLE FIRE ALARM RELAY TO STOP DESTRATIFICATION FANS IN CASE OF A FIRE
MODULE DE RELAIS ADRESSABLE POUR ARRÊTER LES VENTILATEURS DE DESTRATIFICATION EN CAS D'ALARME INCENDIE

- Légende — S267_ADD_24 (150 marques)
- Annonciateur FAAP (1)
 - Bloc d'alimentation AI PS (2)
 - Déclencheur manuel (9)
 - Détecteur de fumée photoélectrique (50)
 - Détecteur faisceau récepteur FL-RX (3)
 - Détecteur faisceau émetteur FL-TX (3)
 - Klaxon/stroboscope (63)
 - Module d'interface AIM (2)
 - Module de relais ARM (10)
 - Panneau d'alarme incendie FAP (1)
 - Stroboscope mural (6)

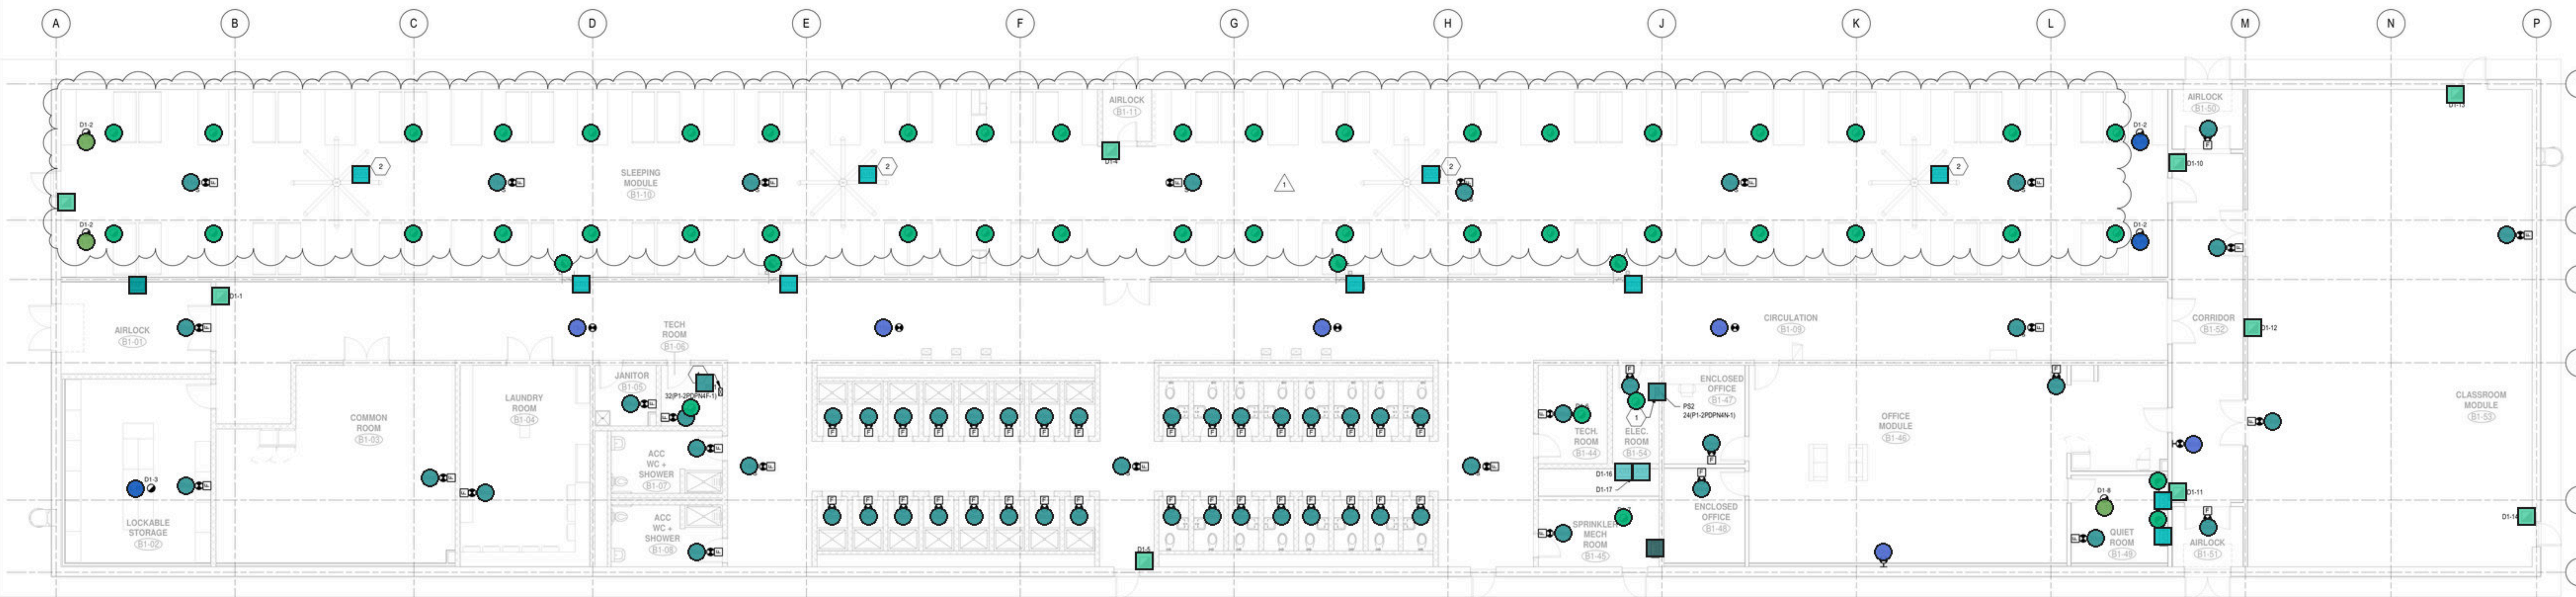

1 AUXILIARY SERVICES / SERVICES AUXILIAIRES PLAN VIEW / VU EN PLAN
SCALE: 1:100
ÉCHELLE: 1:100



1	2026-06-16	ADDENDA MEP-01			
0	2026-04-28	FOR TENDER / POUR SOUMISSIONS			
NO.	DATE	REVISION			APPR.
SCALE / ÉCHELLE					
AS NOTED / ÉCHELLE TELLE QU'ELLE EST ILLUSTRÉE					
LOCATION / EMPLACEMENT					
ST. JEAN GARRISON. QC					
GARRISON DE SAINT-JEAN. QC					
PROJECT / PROJET					
STJ-CONSTRUCT 6 NEW ACCOMMODATION BUILDINGS / STJ-CONSTRUIRE 6 NOUVEAUX BÂTIMENTS D'HÉBERGEMENT					
TRADE / MÉTIER				DATE	
ELECTRICAL / ÉLECTRICITÉ				03/06/26	
SUBJECT / SUJET					
AUXILIARY SERVICES LVL 1 SERVICES AUXILIAIRES NIVEAU 1					
PRODUCTION		REVIEWED / REVU			
DESIGNED / ÉTUDE SAMUEL LAPRISE, ing		DES O AGENT CONC			
DRAWN / DESSIN SANDY BOUCHER		PRO MGR GÉST PROJ			
CHECKED / VÉRIFIÉ SAMUEL LAPRISE, ing		DES MGR GÉST CONC			
COORDINATION		FIRE INCENDIE			
WBS NUMBER NO. SRT N.306844.24			PF NUMBER NO. DP QS-000428-B		
DWG. NO. / NO. DESSIN					
L-S267-1302-01-508B					

SPECIFIC NOTE(S)
NOTE(S) SPECIFIQUE(S):

A- THE DISTRIBUTION FOR EACH BUILDING WILL BE IDENTICAL TO THE BUILDING #1 SHOWN ON THIS PLAN. FOR TENDER, INCLUDE THE DISTRIBUTION FOR THE SIX BUILDING.
LA DISTRIBUTION ÉLECTRIQUE DE CHAQUE BÂTIMENT SUPPLÉMENTAIRE EST IDENTIQUE À LA DISTRIBUTION DU BÂTIMENT #1 DESSINÉ SUR CE PLAN. POUR LA SOUMISSION, PRÉVOIR LA DISTRIBUTION POUR LES SIX (6) BÂTIMENTS.

B- THE MAIN BREAKER SHOULD INCLUDE A MEASURING DEVICE CONNECTED TO THE BUILDING MANAGEMENT SYSTEM. THE MEASURING DEVICE CAN EITHER BE INCLUDED INSIDE THE MAIN BREAKER OR A SEPARATE EQUIPMENT LOCATED IN THE ELECTRICAL ROOM.
LE DISJONCTEUR PRINCIPAL DOIT AVOIR UN DISPOSITIF DE MESURAGE CONNECTÉ AU SYSTÈME DE GESTION DU BÂTIMENT. L'ÉQUIPEMENT DE MESURE PEUT ÊTRE SOIT INTÉGRÉ AU DISJONCTEUR PRINCIPAL OU ÊTRE UN ÉQUIPEMENT INDÉPENDANT LOCALISÉ DANS LA SALLE ÉLECTRIQUE.

IDENTIFICATION(S)

1 HYDRO-QUEBEC TYPE B TRANSFORMATION BOX FOR MEASURING DEVICE.
ARMOIRE DE TRANSFORMATION HYDRO-QUEBEC TYPE B POUR MESURAGE.

LEVEL OF SECURITY / NIVEAU DE SÉCURITÉ

This design is an instrument of service and is protected by copyright, copyright for the consultant's instrument of service belongs to the consultant. Copies including electronic copies, may only be used for the purpose intended and for a one-time use, on the same site, and for the same project and may not be offered for sale or transfer without the express written consent of the consultant.

Le présent dessin est un instrument de service protégé par le droit d'auteur. Le droit d'auteur sur l'instrument de service de l'expert-conseil appartient à ce dernier. Les exemplaires de ce dessin, y compris les exemplaires électroniques, ne peuvent servir qu'aux fins prévues, et ce, au une fois, sur le même chantier et pour le même projet. Ils ne peuvent être offerts en vente ni transférés sans le consentement écrit exprès de l'expert-conseil.

NORR

NORR Architects & Engineers Limited

55 Murray Street, Suite 600
Ottawa, ON, Canada K1N 5M3
NORR.COM


PAGEAU
MOREL
www.pageaumorel.com
Montréal

THIS DRAWING SHALL NOT BE USED FOR CONSTRUCTION OR INSTALLATION PURPOSE.
CE PLAN NE DOIT PAS ÊTRE UTILISÉ À DES FINS DE CONSTRUCTION OU D'INSTALLATION.

Légende — S267_ADD_3 (4 marques)

Barre de mise à la terre (3)

Dispositif de mesurage GTB (1)

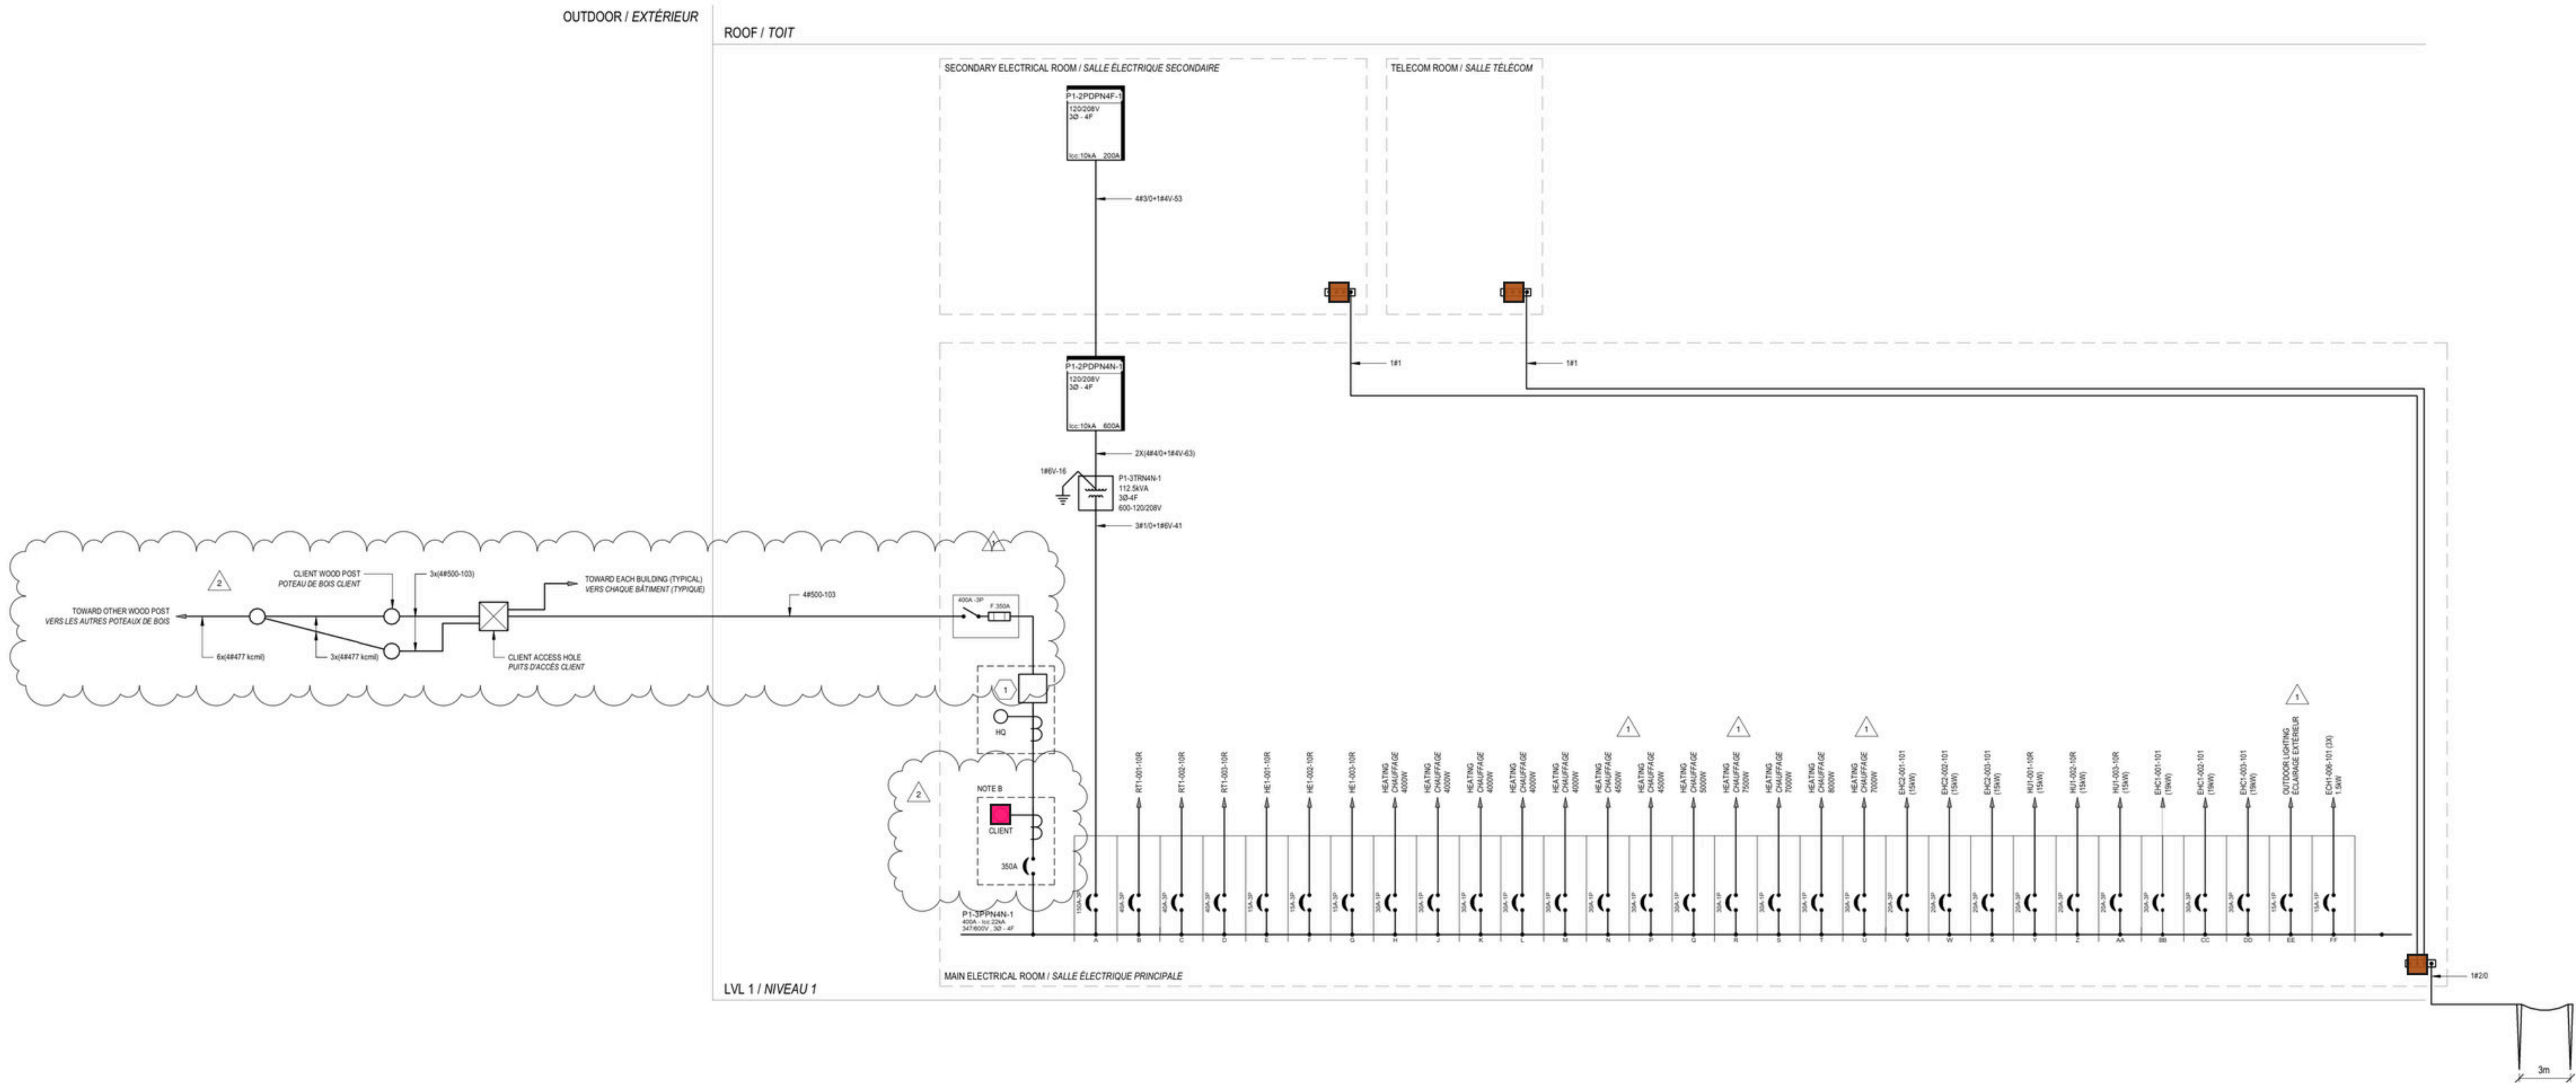

2	2026-07-02	ADDENDA MEP-02	
1	2026-06-16	ADDENDA MEP-01	
0	2026-04-28	FOR TENDER / POUR SOUMISSIONS	

NO.	DATE	REVISION	APPR.
SCALE / ÉCHELLE			

AS NOTED / ÉCHELLE TELLE QU'ELLE EST ILLUSTRÉE

LOCATION / EMPLACEMENT
ST. JEAN GARRISON, QC
GARNISON DE SAINT-JEAN, QC

PROJECT / PROJET
STJ-CONSTRUCT 6 NEW
ACCOMMODATION BUILDINGS /
STJ-CONSTRUIRE 6 NOUVEAUX
BÂTIMENTS D'HÉBERGEMENT



TRADE / MÉTIER ELECTRICAL / ÉLECTRICITÉ	DATE 03/06/26
--	------------------

SUBJECT / SUJET
ELECTRICAL DISTRIBUTION
DISTRIBUTION ÉLECTRIQUE

PRODUCTION	REVIEWED / REVU	DES O / AGENT CONC.
DESIGNED / ÉTUDE SAMUEL LAPRISE, ing		PRO MGR / GÉST PROJ.
DRAWN / DESSINÉ SANDY BOUCHER		DES MGR / GÉST CONC.
CHECKED / VÉRIFIÉ SAMUEL LAPRISE, ing		FIRE / INCENDIE
COORDINATION		

WBS NUMBER / NO. SRT N.306844.24	PF NUMBER / NO. DP QS-000428-B
DWG. NO. / NO. DESSIN	L-S267-1302-01- 502B

Canada

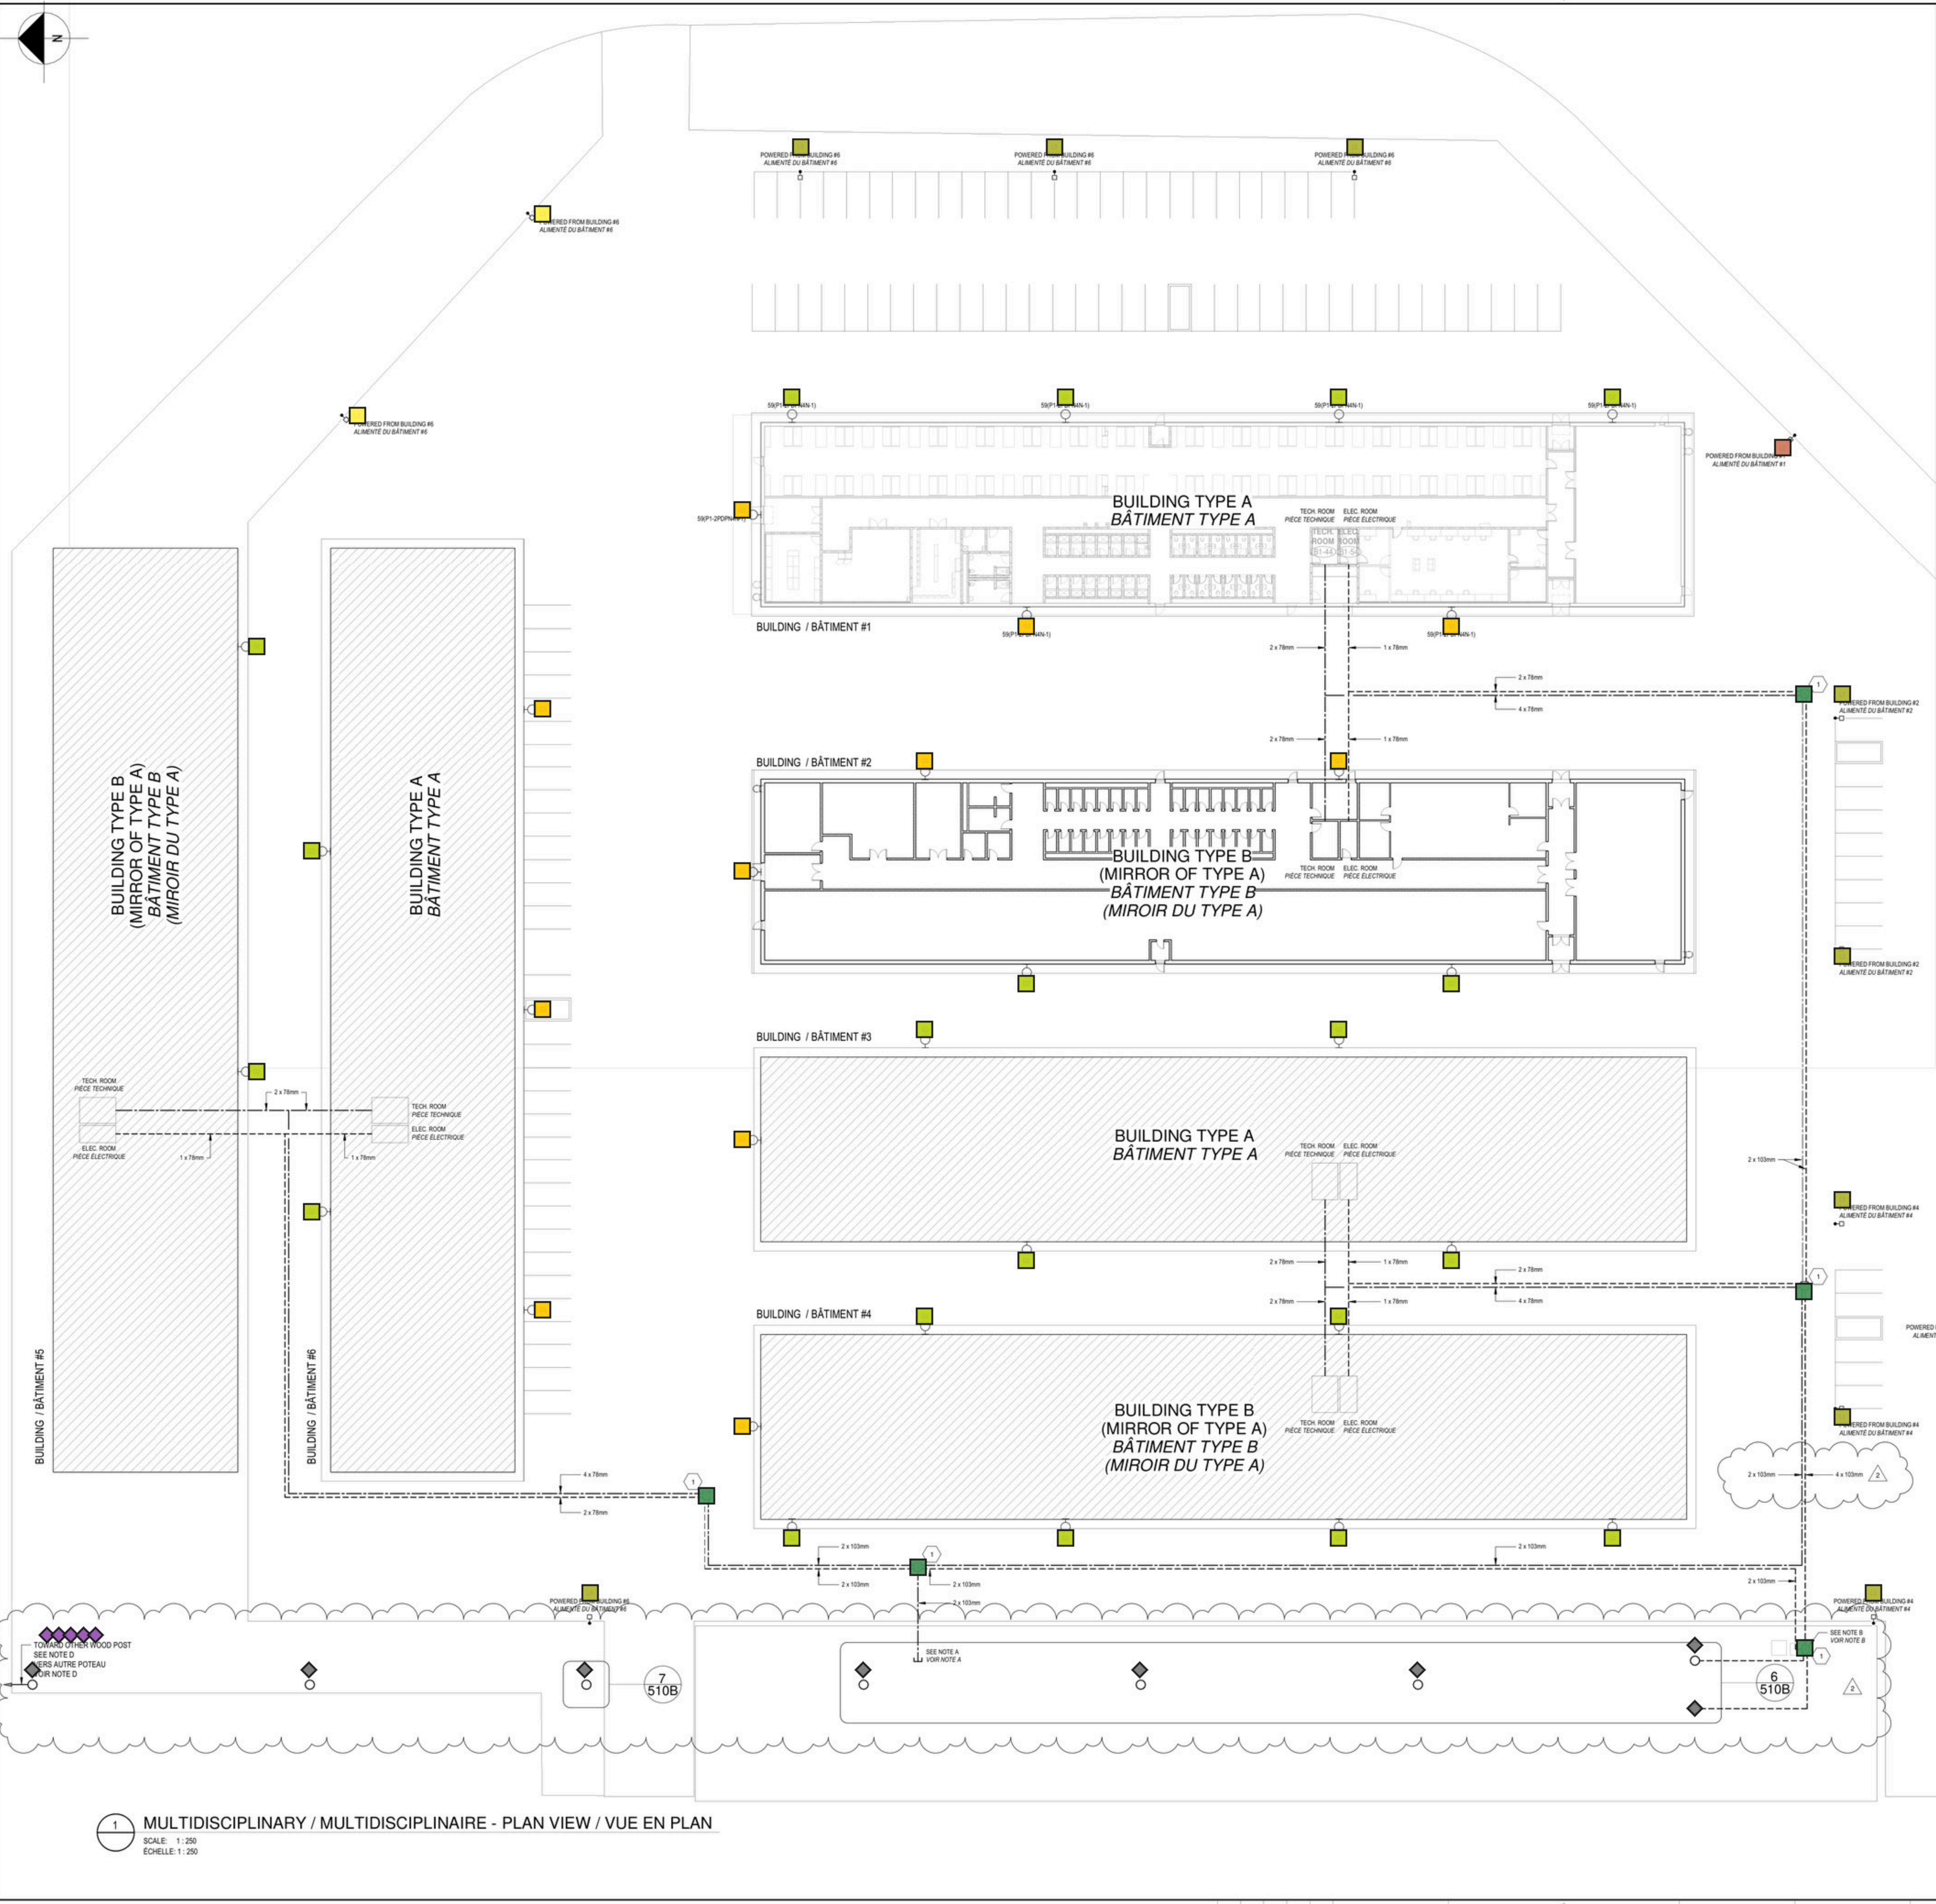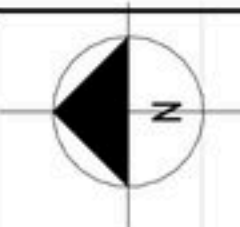

**GENERAL NOTE(S)
NOTE(S) GÉNÉRALE(S):**

1. REFER TO CIVIL PLAN FOR THE PROPOSED COURSE OF THE LAMP POST POWER COMING FROM EACH BUILDING.
SE RÉFÉRER AUX PLANS CIVIL POUR LE PARCOURS PROPOSÉ DE L'ALIMENTATION DES LAMPADAIRES À PARTIR DES BÂTIMENTS.

**SPECIFIC NOTE(S)
NOTE(S) SPÉCIFIQUE(S):**

- A. FINISH THE CONDUITS IN THE GROUND NEAR THE LOCALISATION OF THE FUTURE ACCESS HOLE. REFER TO CIVIL DRAWINGS. INSTALL LIQUID-TIGHT CONDUIT FITTING GULLED TO THE END OF THE CONDUIT.
TERMINER LES CONDUITS DANS LE SOL À PROXIMITÉ DE L'EMPLACEMENT DU FUTUR PUIS D'ACCÈS DE TIRAGE (VOIR PLAN CIVIL). PRÉVOIR DES EMBOUTS ET FANCHES COULÉES AUX EXTRÉMITÉS DES CONDUITS.
- B. ALLOW 5m OF ADDITIONAL CABLE IN THE ACCESS HOLE FOR EACH BUILDING CONNECTION TO ENABLE A FUTURE CONNECTION TO THE CUSTOMER'S POWER LOOP.
PRÉVOIR 5m DE CÂBLE SUPPLÉMENTAIRE DANS LE PUIS D'ACCÈS POUR CHACUN DES RACCORDEMENTS DE BÂTIMENT POUR PERMETTRE UN BRANCHEMENT FUTUR À LA BOUCLE D'ALIMENTATION CLIENT.
- C. AIRBORNE TO UNDERGROUND TRANSITION TO REACH THE ACCESS HOLE AND THE CONCRETE BANK TO POWER EACH BUILDING.
DESCENDRE AÉRODOUTERRAINE POUR REJOINDRE LE PUIS D'ACCÈS ET LE RESEAU DE MASSIF POUR ALIMENTER LES NOUVEAUX BÂTIMENTS.
- D. PROVIDE FIVE (5) ADDITIONAL WOOD POST TO THOSE ALREADY SHOWN ON THE DRAWINGS TO REACH THE HYDRO-QUEBEC LINE. THE EXACT POSITION OF THE POLES MUST BE COORDINATED DURING CONSTRUCTION BASED ON SITE CONSTRAINTS. CONSIDER A STRAIGHT LINE BETWEEN THE CURRENT POSITION AND THE HYDRO-QUEBEC LINE. SEE DETAIL 8 ON 510B PLAN FOR THE LINE PATH.
PRÉVOIR CINQ (5) POTEAUX SUPPLÉMENTAIRES À CEUX DÉJÀ PRÉSENT EN PLAN POUR ATTEINDRE LA LIGNE HYDRO-QUEBEC. LA POSITION EXACTE DES POTEAUX DEVRA ÊTRE COORDONNÉE EN CHANTIER EN FONCTION DES CONTRAINTES DU SITE. PRÉVOIR UNE LIGNE DROITE ENTRE LA POSITION ACTUELLE ET LA LIGNE HYDRO-QUEBEC À REJOINDRE. CONSIDÉRER UNE DISTANCE MOYENNE DE 30m ENTRE LES POTEAUX. VOIR DÉTAIL 8 DU PLAN 510B POUR LE PARCOURS DE LA LIGNE.

IDENTIFICATION(S)

1. ELECTRICAL AND TELECOMMUNICATION SQUARE ACCESS HOLE WITH A MINIMUM OF 4 CONDUITS OF 100mm PER SIDE ON A MINIMUM OF 3 SIDES. THE ACCESS HOLE SHOULD BE PREFABRICATED WITH ARMED CONCRETE WITH A DIMENSIONS OF 815mm X 815mm X 900mm DE HAUTEUR.
PUITS D'ACCÈS CARRÉ ÉLECTRIQUE ET TÉLÉCOMMUNICATION AVEC UN MINIMUM DE 4 CONDUITS DE 100mm PAR CÔTÉ, SUR UN MINIMUM DE 3 FACES. LE PUIS D'ACCÈS DOIT ÊTRE EN BÉTON ARMÉ, PRÉFABRIQUÉ, DE DIMENSION MINIMALE 815mm X 815mm X 900mm DE HAUTEUR.

Légende — S267_ADD_4 (65 marques)

- G2 Applique de zone type 2 (20)
- G3 Applique de zone type 3 (11)
- L2 Lampadaire type 2 (3)
- L3 Lampadaire type 3 (4)
- L5 Lampadaire type 5 (9)
- Poteau de bois (8)
- Poteau de bois additionnel note D (5)
- Puits d'accès électrique/télécom (5)

LEVEL OF SECURITY / NIVEAU DE SÉCURITÉ

This design is an instrument of service and is protected by copyright, copyright for the consultant's instrument of service belongs to the consultant. Copies including electronic copies, may only be used for the purpose intended and for a one-time use, on the same site, and for the same project and may not be offered for sale or transfer without the express written consent of the consultant.

Le présent dessin est un instrument de service protégé par le droit d'auteur. Le droit d'auteur sur l'instrument de service de l'expert-conseil appartient à ce dernier. Les exemplaires de ce dessin, y compris les exemplaires électroniques, ne peuvent servir qu'à une fin prévue, et ce, au même lieu, sur le même chantier et pour le même projet. Ils ne peuvent être offerts en vente ni transférés sans le consentement écrit exprès de l'expert-conseil.

NORR

NORR Architects & Engineers Limited

55 Murray Street, Suite 600
Ottawa, ON, Canada K1N 5M3
NORR.COM

PAGEAU MOREL
www.pageaumorel.com
Montréal

THIS DRAWING SHALL NOT BE USED FOR CONSTRUCTION OR INSTALLATION PURPOSE.

CE PLAN NE DOIT PAS ÊTRE UTILISÉ À DES FINS DE CONSTRUCTION OU D'INSTALLATION.



2	2026-07-02	ADDENDA MEP-02	
1	2026-06-16	ADDENDA MEP-01	
0	2026-04-28	FOR TENDER / POUR SOUMISSIONS	

NO.	DATE	REVISION	APPR.
SCALE ÉCHELLE			

AS NOTED | ÉCHELLE TELLE QU'ELLE EST ILLUSTRÉE

LOCATION | EMPLACEMENT
ST. JEAN GARRISON, QC
GARRISON DE SAINT-JEAN, QC

PROJECT | PROJET
STJ-CONSTRUCT 6 NEW ACCOMMODATION BUILDINGS / STJ-CONSTRUIRE 6 NOUVEAUX BÂTIMENTS D'HÉBERGEMENT

TRADE MÉTIER	DATE
ELECTRICAL / ÉLECTRICITÉ	03/06/26

SUBJECT | SUJET
MULTIDISCIPLINARY SITE
MULTIDISCIPLINAIRE SITE

PRODUCTION	REVIEWED REVU	DES O AGENT CONC.
DESIGNED ÉTUDE SAMUEL LAPRISE, ing		DES O AGENT CONC.
DRAWN DESSIN SANDY BOUCHER		PRO MGR GÉST PRO
CHECKED VÉRIFIÉ SAMUEL LAPRISE, ing		DES MGR GÉST CONC.
COORDINATION		FIRE INCENDIE

WBS NUMBER NO. SRT N.306844.24	PF NUMBER NO. DP QS-000428-B
DWG. NO. NO. DESSIN	L-5267-1302-01- 503B

GENERAL REVISION
REVISION GÉNÉRALE

Autodesk Docs ID: 361-Jean-Garrison-STJ-New-Buildings-5514-000000_MEP_2026-07-02