

$R(X)$ -BS
 $R(X)$ -N
 $R(X)$ -NS

$S(X)$

LISTE DES GRADATEURS /									
INTERRUPTEUR SUR L'INTERFACE GRAPHIQUE NP0D TOUCH									
ZONE	TYPES	#0 RELAIS	TYPES GRADATION	GRADATEUR	RELAIS	INTERRUPTEUR	SCÈNE 1 OUVERTURE	SCÈNE 2 FERMETURE	SCÈNE 3 100%
ILÔTS	S20	#33	0-10V	X	NP16 16 (DP1)	NP0D (SW6)	50%	0%	100%
ILÔTS 24H	S20 24H	#33	0-10V	X	NP16 16 (DP1)	NP0D (SW6)	50%	100%	100%
RAILS CELLIER	D3-N / D4-N	#22	ELV/N/A	X	NP16 CD (P2)	NP0D (SW6)	90%	0%	100%
ENSEIGNE CELLIER	ENSEIGNE CELLIER	#19	N/A	X	NP20 PD (PP1)	NP0D (SW6)	ON	OFF	ON
AU-DESSUS CAISSES LINÉAIRES	OB-N	#27	N/A	X	NP16 (DP1)	NP0D (SW6)	70%	0%	100%
AU-DESSUS CAISSES RAILS	D3-N / D4-N	#16	ELV/N/A	X	NP16 CD (P2)	NP0D (SW6)	90%	0%	100%
MARQUES	T	#31, #29, #30	0-10V	X	NP16 (DP1)	NP0D (SW6)	ON	OFF	ON
VESTIBULE	B-B	#26	0-10V	X	NP16 16 (DP1)	NP0D (SW6)	90%	0%	100%
ARMOIRES VITRÉES	PRISES DUPLEX	#20	N/A	X	NP20 PD (PP1)	NP0D (SW6)	ON	OFF	ON
ENTRÉPÔT	P1 et P2	#35	0-10V	X	NP16 (DP1)	NP0DMA (SW3)	100%	0%	100%
ENTRÉPÔT 24H	P1 ET P2	N/A	N/A		NON CONTRÔLÉ, RACCORDÉ DIRECTEMENT AU PANNEAU				
BUREAU	J1 et K3	#17	0-10V	X		WSXA-G (S03)			
CUISINE	J1	#24	0-10V			WSXA-G (S03)			
ENTRETIEN	G4	#18	N/A			WSXA (S04)			
SALLE DE BAIN	G4	#25, #26	N/A			WSXA (S04)			



NOTES SPÉCIFIQUES

GÉNÉRALITÉS :

LES NOTES GÉNÉRALES SONT COMPLÉMENTAIRES À CE PLAN.

TOUS LES CONDUITS RIGIDES "EMT" OU PVC DESTINÉS À L'ALIMENTATION DE SERVICES INFORMATIQUES DONT IL EST QUESTION DANS LES NOTES CI-BASSES DOIVENT :

- ÊTRE MUNIS DE FICELLE DE TIRAGE BIEN IDENTIFIÉES AUX DEUX EXTRÉMITÉS.
- ÊTRE MUNIS DE BAGUES DE TERMINAISON AUX DEUX EXTRÉMITÉS.
- SE PROLONGER DANS L'ENTRE-PLAFOND JUSQU'À UN ENDOIT FACILEMENT ACCESSIBLE (IE : AU-DESSUS D'UNE TUILE ACOUSTIQUE).

LE RÉSEAU DE CONDUITS CHAUFFANT DÉCRIT EST RÉALISÉ PAR L'ENTREPRENEUR ÉLECTRICIEN MAIS LE CÂBLAGE INFORMATIQUE ET SÉCURITÉ EST RÉALISÉ PAR UN SOUS-TRAITANT MANDATÉ PAR LA SAQ.

TOUS LES CONDUITS RIGIDES "EMT" OU PVC DESTINÉS À L'ALIMENTATION DES SERVICES ÉLECTRIQUES DONT IL EST QUESTION DANS LES NOTES CI-BASSES DOIVENT :

- SE TERMINER, DANS L'ENTRE-PLAFOND, PAR UNE BOÎTE DE JONCTION SITUÉE À UN ENDOIT FACILEMENT ACCESSIBLE (IE : AU-DESSUS D'UNE TUILE ACOUSTIQUE).

SEULEMENT SI LA STRUCTURE DU PLAFOND RESTE APPARENTE, L'ENTREPRENEUR ÉLECTRICIEN DOIT INSTALLER UN RÉSEAU COMPLET DE CONDUITS RIGIDES "EMT" POUR LE CÂBLAGE ÉLECTRIQUE, INFORMATIQUE, TÉLÉPHONIQUE ET SÉCURITÉ. À PARTIR DES SOURCES D'ALIMENTATION JUSQU'ÀUX ENDOITS INDICUÉS AU PLAN OU DE TELS SERVICES SONT REQUIS (BUREAUX, COMPTOIR-CAISSES, ETC.) MUNIS DES CONDUITS DE BOÎTES ET DE FICELLES DE TIRAGE.

SI UN RÉSEAU COMPLET DE CONDUITS RIGIDES N'EST PAS PRÉVU POUR LA DISTRIBUTION ÉLECTRIQUE, AU MINIMUM, L'ÉLECTRICIEN INSTALLERA DES BOÎTES DE JONCTION DANS L'ENTRE-PLAFOND AU-DESSUS DES PANNEAUX DE DISTRIBUTION AVEC UN RÉSEAU DE CONDUITS RIGIDES ENTRE LES DEUX. LES RACCORDS DU CÂBLAGE "BX" DE TOUS LES CIRCUITS S'EFFECTUERONT DANS CES BOÎTES DE JONCTION.

NOTES SPÉCIFIQUES :

[NOTE 1] : CONDUIT RIGIDE EN PVC 1 1/2" Ø (SAUF INDICATION CONTRAIRE AU PLAN), SOUS LA DALLÉ, CE CONDUIT MONTE DANS UN MUR À PROXIMITÉ JUSQU'À UNE BOÎTE DE JONCTION DANS L'ENTRE-PLAFOND. LORSQUE LE PLAFOND EST OUVERT, PROLONGER LE CONDUIT JUSQU'À L'ENTRÉE DU MUR À L'AUTRE EXTRÉMITÉ. IL EST RELIÉ À UNE BOÎTE DE JONCTION FIXÉE À PLAT SUR LA DALLÉ POUR LE RACCORDEMENT DES SERVICES ÉLECTRIQUES REQUIS AUX COMPTOIRS CAISSES, OU ENCORE, IL SE DIRIGE VERS DES PRISES ÉLECTRIQUES AU SOL.

[NOTE 2] : CONDUIT RIGIDE EN PVC 1" Ø, SOUS LA DALLÉ, CE CONDUIT MONTE DANS UN MUR À PROXIMITÉ JUSQU'À L'ENTRÉE DU MUR À L'ENTRÉE DU PLAFOND. LORSQUE LE PLAFOND EST OUVERT, PROLONGER LE CONDUIT JUSQU'À L'ENTRÉE DU MUR À L'AUTRE EXTRÉMITÉ. LE CONDUIT SORTIRA DE 1" AU-DESSUS DE LA DALLÉ (POUR CÂBLAGE INFORMATIQUE, TÉLÉPHONE ET DATA PAR AUTRES).

[NOTE 3] : CONDUIT RIGIDE DE 3/4" Ø RACCORDÉ À UNE BOÎTE DE SORTIE MURALE 2 X 3 ET MONTANT DANS L'ENTRE-PLAFOND. LORSQUE PLAFOND OUVERT, PROLONGER LE CONDUIT DU BUREAU JUSQU'À L'ENTRÉE DU MUR.


[NOTE 4] : 2 CONDUITS RIGIDES DE 2" AVEC BAGUES DE FINITION, DÉBUTANT À 115" DU PLANCHER ET SE TERMINANT DANS L'ENTRE-PLAFOND.

NOTES - PROTECTION IGNIFUGE

FOURNIR ET INSTALLER UNE PROTECTION IGNIFUGE AUTOUR DES BOÎTES DE JONCTION ENCASTRÉES TQ CP 617 DE HLT OU AUTRE PRODUIT ÉQUIVALENT DANS LES DIVISIONS (MURS, PLANCHERS, PLAFONDS) ISOLÉS ET PROTÉGÉS CONTRE LE FEU (LUMINAIRES, INTERRUPTEURS, PRISES ÉLECTRIQUES, ÉCLAIRAGE D'URGENCE, APPARELS DE CHAUFFAGE, ETC.). VEUILLEZ-VOUS RÉFÉRER AUX PLANS D'ARCHITECTURES.

Légende — E200 (79 marques)

- BX 4 pi — à confirmer (1)
- ▲ Contrôle de volume (1)
- Démarreur manuel (1)
- Minuterie évacuation (1)
- Plinthe électrique (5)
- Prise 30A L5-30R (UPS) (1)
- Prise duplex 15A (16)
- Prise duplex BX caisse (11)
- Prise duplex affleurement plancher (1)
- Prise duplex circuit indépendant (4)
- Prise existante relocalisée (4)
- Raccordement boîte à volume BV-01 (1)
- Raccordement chauffe-eau CE-1 (1)
- Raccordement pompe PR-1 (1)
- Raccordement serpentín SE (2)
- Raccordement ventilateur VE-01 — à confirmer (1)
- Raccordement volet motorisé (1)
- Relais basse tension CVC (4)
- ▲ Sortie conduit dalle télécom (5)
- ▲ Sortie haut-parleur (1)
- ▲ Sortie télécom (6)
- Symbole double cercle cyan — à classer (1)
- Sèche-mains SM (2)
- Thermostat action inversée (raccordement) (1)
- Thermostat existant relocalisé (1)
- Thermostat programmable (par CVAC) (2)
- Thermostat électricien (3)

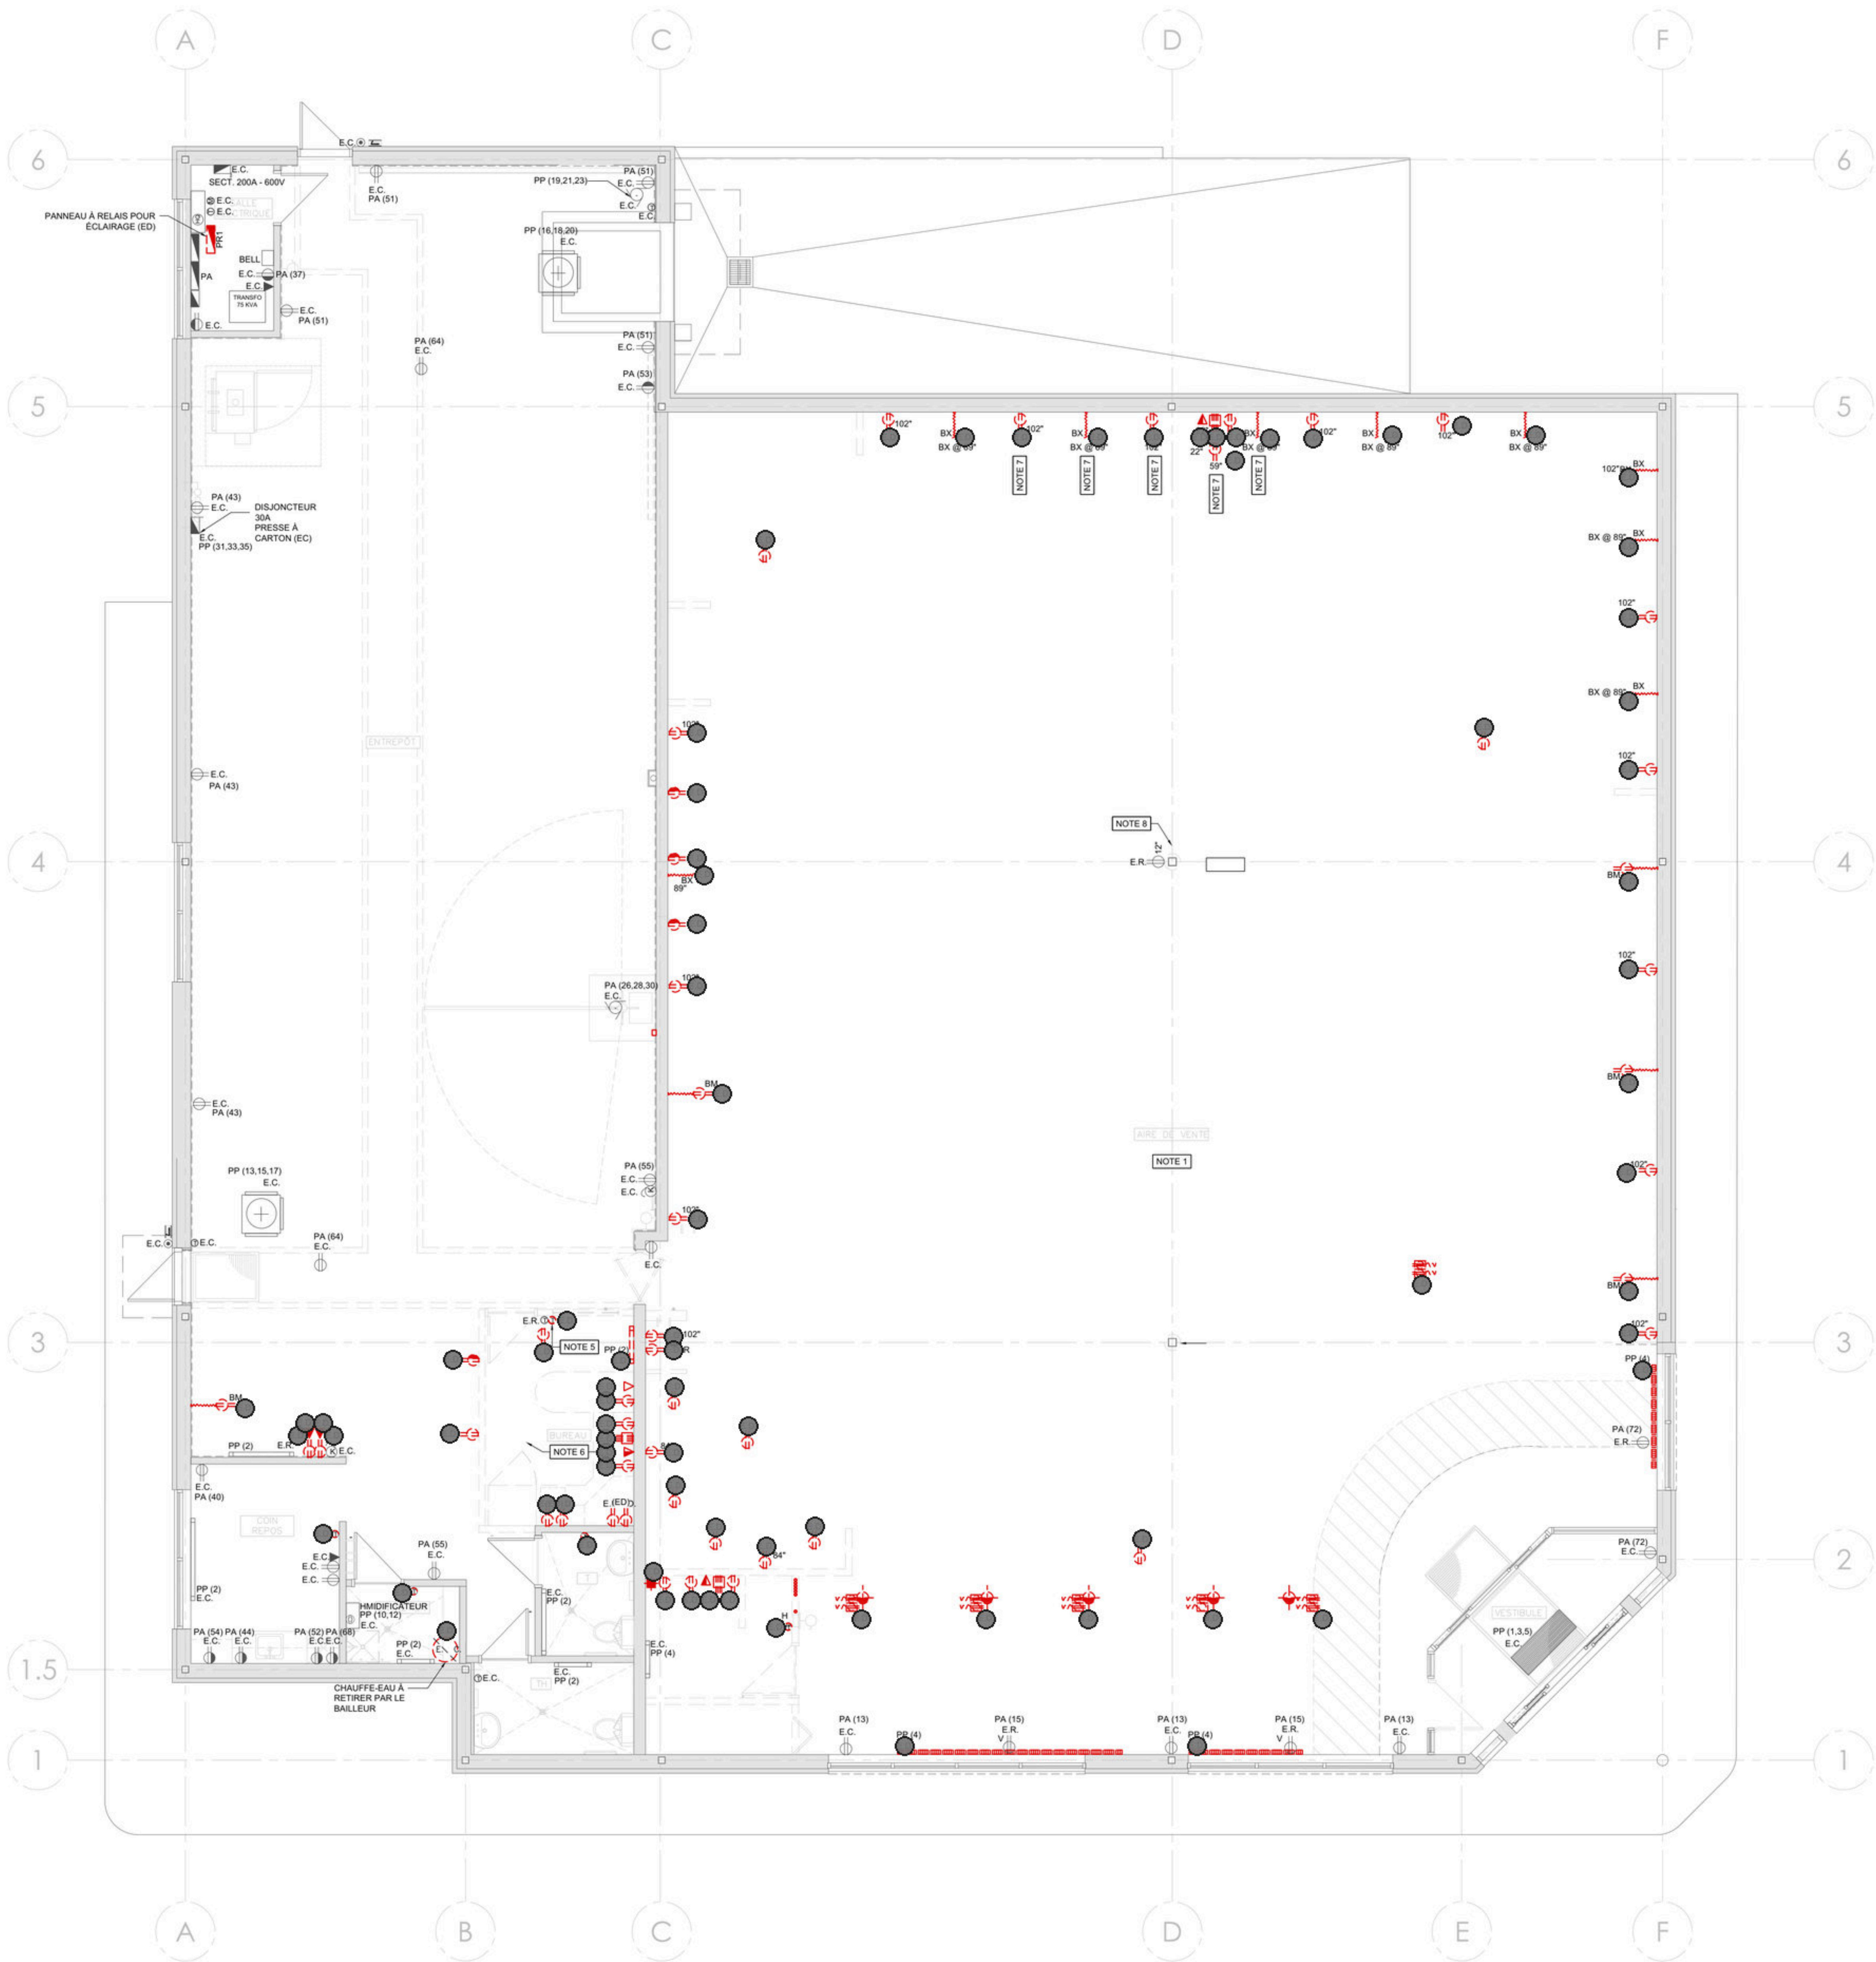

NOTES - DÉMOLITION

IL EST DE LA RESPONSABILITÉ DE L'ENTREPRENEUR D'ÉVALUER LES COÛTS DE DÉMOLITION DURANT LA VISITE DES LIEUX AVANT LA SOUMISSION.

SAUF INDICATION CONTRAIRE ET SI LE CLIENT NE DÉSIRE PAS LES CONSERVER, TOUS LES ÉQUIPEMENTS INDiquÉS SUR LES PLANS DE DÉMOLITION SONT EXISTANTS À ENLEVER ET À DISPOSER HORS DU SITE.

REMETTRE AU PROPRIÉTAIRE TOUS LES ÉQUIPEMENTS QU'IL DÉSIRE CONSERVER ET LES ENTREPOSER À UN ENDROIT DÉSIGNÉ PAR CELUI-CI. CE QUE LE PROPRIÉTAIRE NE DÉSIRE PAS CONSERVER, L'ENTREPRENEUR DEVRA EN DISPOSER À SES FRAIS HORS DU SITE. COORDONNER AU CHANTIER AVEC LE PROPRIÉTAIRE LE CHEMINEMENT DES MATÉRIAUX ENLEVÉS ET LES NOUVEAUX ÉQUIPEMENTS À INSTALLER.

L'ENTREPRENEUR ÉLECTRICIEN DOIT FAIRE UN TRACÉ DES CIRCUITS ET IDENTIFIER LES CIRCUITS DES APPAREILS TOUCHÉS DURANT LES TRAVAUX DANS TOUS LES PANNEAUX ET SOUS-PANNEAUX. TOUS LES CÂBLES ET FILAGE ÉLECTRIQUE ET TÉLÉCOM DÉSAFFECTÉS DOIVENT ÊTRE ENLEVÉS ET DISPOSÉS.

ENLEVER TOUS LES CONDUCTEURS, CONDUITS ET CÂBLES EXISTANTS JUSQU'À LA SOURCE OU JUSQU'À LA DERNIÈRE BOÎTE DE JONCTION TOUJOURS EN FONCTION. BOUCHER LES OUVERTURES FAITES DANS LES BOÎTES ET BOÎTIERS AVEC LES ACCESSOIRES REQUIS.

ALIMENTER ET RACCORDER TOUS LES APPAREILS D'ÉCLAIRAGE EXISTANTS, PRISES OU AUTRES ÉQUIPEMENTS TOUJOURS REQUIS (INCLUANT CEUX HORS DE LA ZONE DES TRAVAUX) ET DONT L'ALIMENTATION ÉLECTRIQUE A ÉTÉ DÉBRANCHÉE DURANT LES TRAVAUX DE DÉMOLITION.

DÉBRANCHER LES ÉQUIPEMENTS MÉCANIQUES POUR LEUR DÉMANTÈLEMENT PAR D'AUTRES (COORDONNER AVEC L'ENTREPRENEUR EN MÉCANIQUE).

LES ÉQUIPEMENTS EXISTANTS DANS LA ZONE DES TRAVAUX SONT INDiquÉS À TITRE INFORMATIF ET POUR DES FINS DE SOUMISSIONS. À MOINS D'INDICATION CONTRAIRE, TOUS LES ÉQUIPEMENTS RACCORDÉS ÉLECTRIQUEMENT SONT EXISTANTS À ENLEVER INCLUANT LES ÉQUIPEMENTS NON MONTRES AU PLANS.

TOUS LES CÂBLES DE TÉLÉCOMMUNICATION EXISTANTS DANS LA ZONE DES TRAVAUX (INCLUANT LES SYSTÈMES INTERCOMS, TÉLÉPHONIQUES, ETC.) SONT À ENLEVER JUSQU'À LA SOURCE.


FOURNIR, INSTALLER ET RACCORDER UN ÉCLAIRAGE TEMPORAIRE DANS LA ZONE DES TRAVAUX.

NOTES GÉNÉRALES - DÉMOLITION

1. PRÉPARER TOUTES LES SURFACES POUR RECEVOIR LES NOUVEAUX FINIS. ENLEVER VIS ET AUTRES DÉBRIS ET RAGRÉER LES SURFACES AU BÉTON.
2. LES TRAVAUX DE DÉMOLITION ET CONTRÔLE DES POUSSIÈRES DÉCRITS AUX PLANS D'ARCHITECTURE NE SONT PAS LIMITATIFS. VOIR LES DOCUMENTS DES AUTRES DISCIPLINES.
3. L'ENTREPRENEUR DOIT SUIVRE LES RECOMMANDATIONS D'UN INGÉNIEUR EN STRUCTURE POUR TOUS LES PERÇEMENTS OU LE RAGRAGE DES OUVERTURES DANS LA DALLE DE BÉTON EXISTANTE. L'ENTREPRENEUR DOIT S'ASSURER DE NE PAS PERÇER AUCUN PERÇEMENT DANS UN ÉLÉMENT STRUCTURAL POUVANT COMPROMETTRE L'INTÉGRITÉ STRUCTURALE ET DE NE PAS PERÇER AUCUN CONDUIT. INCLURE TOUS LES SCANS DE LA DALLE REQUIS PAR UN PROFESSIONNEL.
4. L'ENTREPRENEUR DEVRA VEILLER À NE PAS ENDOMMAGER LA STRUCTURE CONSERVÉE ET L'AMÉNAGEMENT EXTÉRIEUR CONSERVÉ AU PÉRIMÈTRE DU BÂTIMENT.
5. LES TRAVAUX DE DÉMOLITION DEVONT SE FAIRE EN CONFORMITÉ AUX CONDITIONS DES DOCUMENTS DU CONSULTANT EN HYGIÈNE.
6. LE TERME "DÉMOLIR" UTILISÉ DANS CES DOCUMENTS N'IMPLIQUE PAS NÉCESSAIREMENT UNE DESTRUCTION, MAIS IMPLIQUE PLUTÔT, SANS S'Y LIMITER, DÉMANTÉLER, DÉMONTÉ, DÉGARNIR, ENLEVER, DÉCONSTRUIRE OU RETIRER, ET REQUIS POSSIBLEMENT DES PRÉCAUTIONS NÉCESSAIRES POUR ACCUEILLIR LES NOUVEAUX ÉLÉMENTS OU ASSEMBLAGES. PRENDRE NOTE QUE LES COMPOSANTES DÉMOLIES CONTIENNENT OU PEUVENT CONTENIR DE L'AMIANTE. POUR LA DISPOSITION DES MATÉRIAUX CONTAMINÉS, SE RÉFÉRER AUX DOCUMENTS D'HYGIÈNE DU MAÎTRE DE L'OUVRAGE POUR PRENDRE LES MESURES NÉCESSAIRES.
7. PRENDRE NOTE QUE LES COMPOSANTES DÉMOLIES CONTIENNENT OU PEUVENT CONTENIR DES MATÉRIAUX NOCIFS POUR LA SANTÉ ET L'ENVIRONNEMENT. SE RÉFÉRER AUX DOCUMENTS D'HYGIÈNE POUR PRENDRE LES MESURES NÉCESSAIRES.
8. LORSQUE REQUIS POUR LA NATURE DES TRAVAUX INDiquÉS AU PLAN, INCLURE LES ÉTANÇONS TEMPORAIRES POUR SUPPORTER LES MATÉRIAUX EXISTANTS À CONSERVER EN PLACE.
9. TOUT ENTREPOSAGE ET PROTECTION DES ÉLÉMENTS RÉCUPÉRABLES LORS DE LA DÉMOLITION SONT À LA CHARGE DE L'ENTREPRENEUR.

NOTES SPÉCIALES — Légende — E200D (82 marques)

- | | | |
|---------|--|--|
| NOTE 1 | SAUF INDICATIONS À RETIRER ET CONSERVER | ● Démol appareil prises/services (E.D.) (82) |
| NOTE 2 | N/A | |
| NOTE 3 | N/A | |
| NOTE 4 | N/A | |
| NOTE 5 | THERMOSTAT RELIÉ À LA SONDE DE TEMPÉRATURE DE L'AIR DE VENTE À RETIRER ET EN FOURNIR UN NOUVEAU SITUÉ DANS LE BUREAU DE L'AIR DE VENTE | |
| NOTE 6 | N/A | |
| NOTE 7 | EMPLACEMENT EXISTANT À CONSERVER, ALIMENTATION ÉLECTRIQUE À MODIFIER | |
| NOTE 8 | SONDE EXISTANTE À RE-INSTALLER SUR LA COLONNE (VOIR PLAN MÉCANIQUE) | |
| NOTE 9 | N/A | |
| NOTE 10 | N/A | |
| NOTE 11 | N/A | |

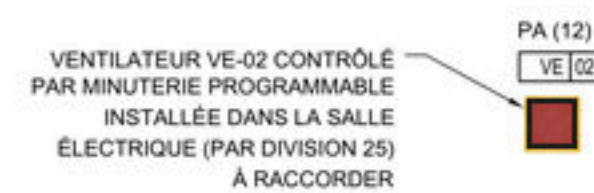

■ Raccordement ventilateur VE-02 (1)

NE PAS UTILISER
POUR CONSTRUCTION

[illegible]

TITRE DU PROJET

SAQ


SAQ VARENNES
VARENNES, QC, J3X 1P7

TITRE DU DESSIN

ÉLECTRICITÉ
PLAN DE TOITURE
EXISTANT /
CONSTRUCTION

14-508-6325

DISCIPLINE	
ÉLECTRIQUE	
CONÇU PAR H. HATTAB, CPI	DATE (AAAA-MM-JJ) 2026-07-13
DESSINÉ PAR F. BÉLAND, tech.	ÉCHELLE INDIQUÉE
VÉRIFIÉ PAR J. BACHKONGI, ING.	NO DE PROJET 26-0094-02
APPROUVÉ PAR J. BACHKONGI, ing.	PLAN NO E201

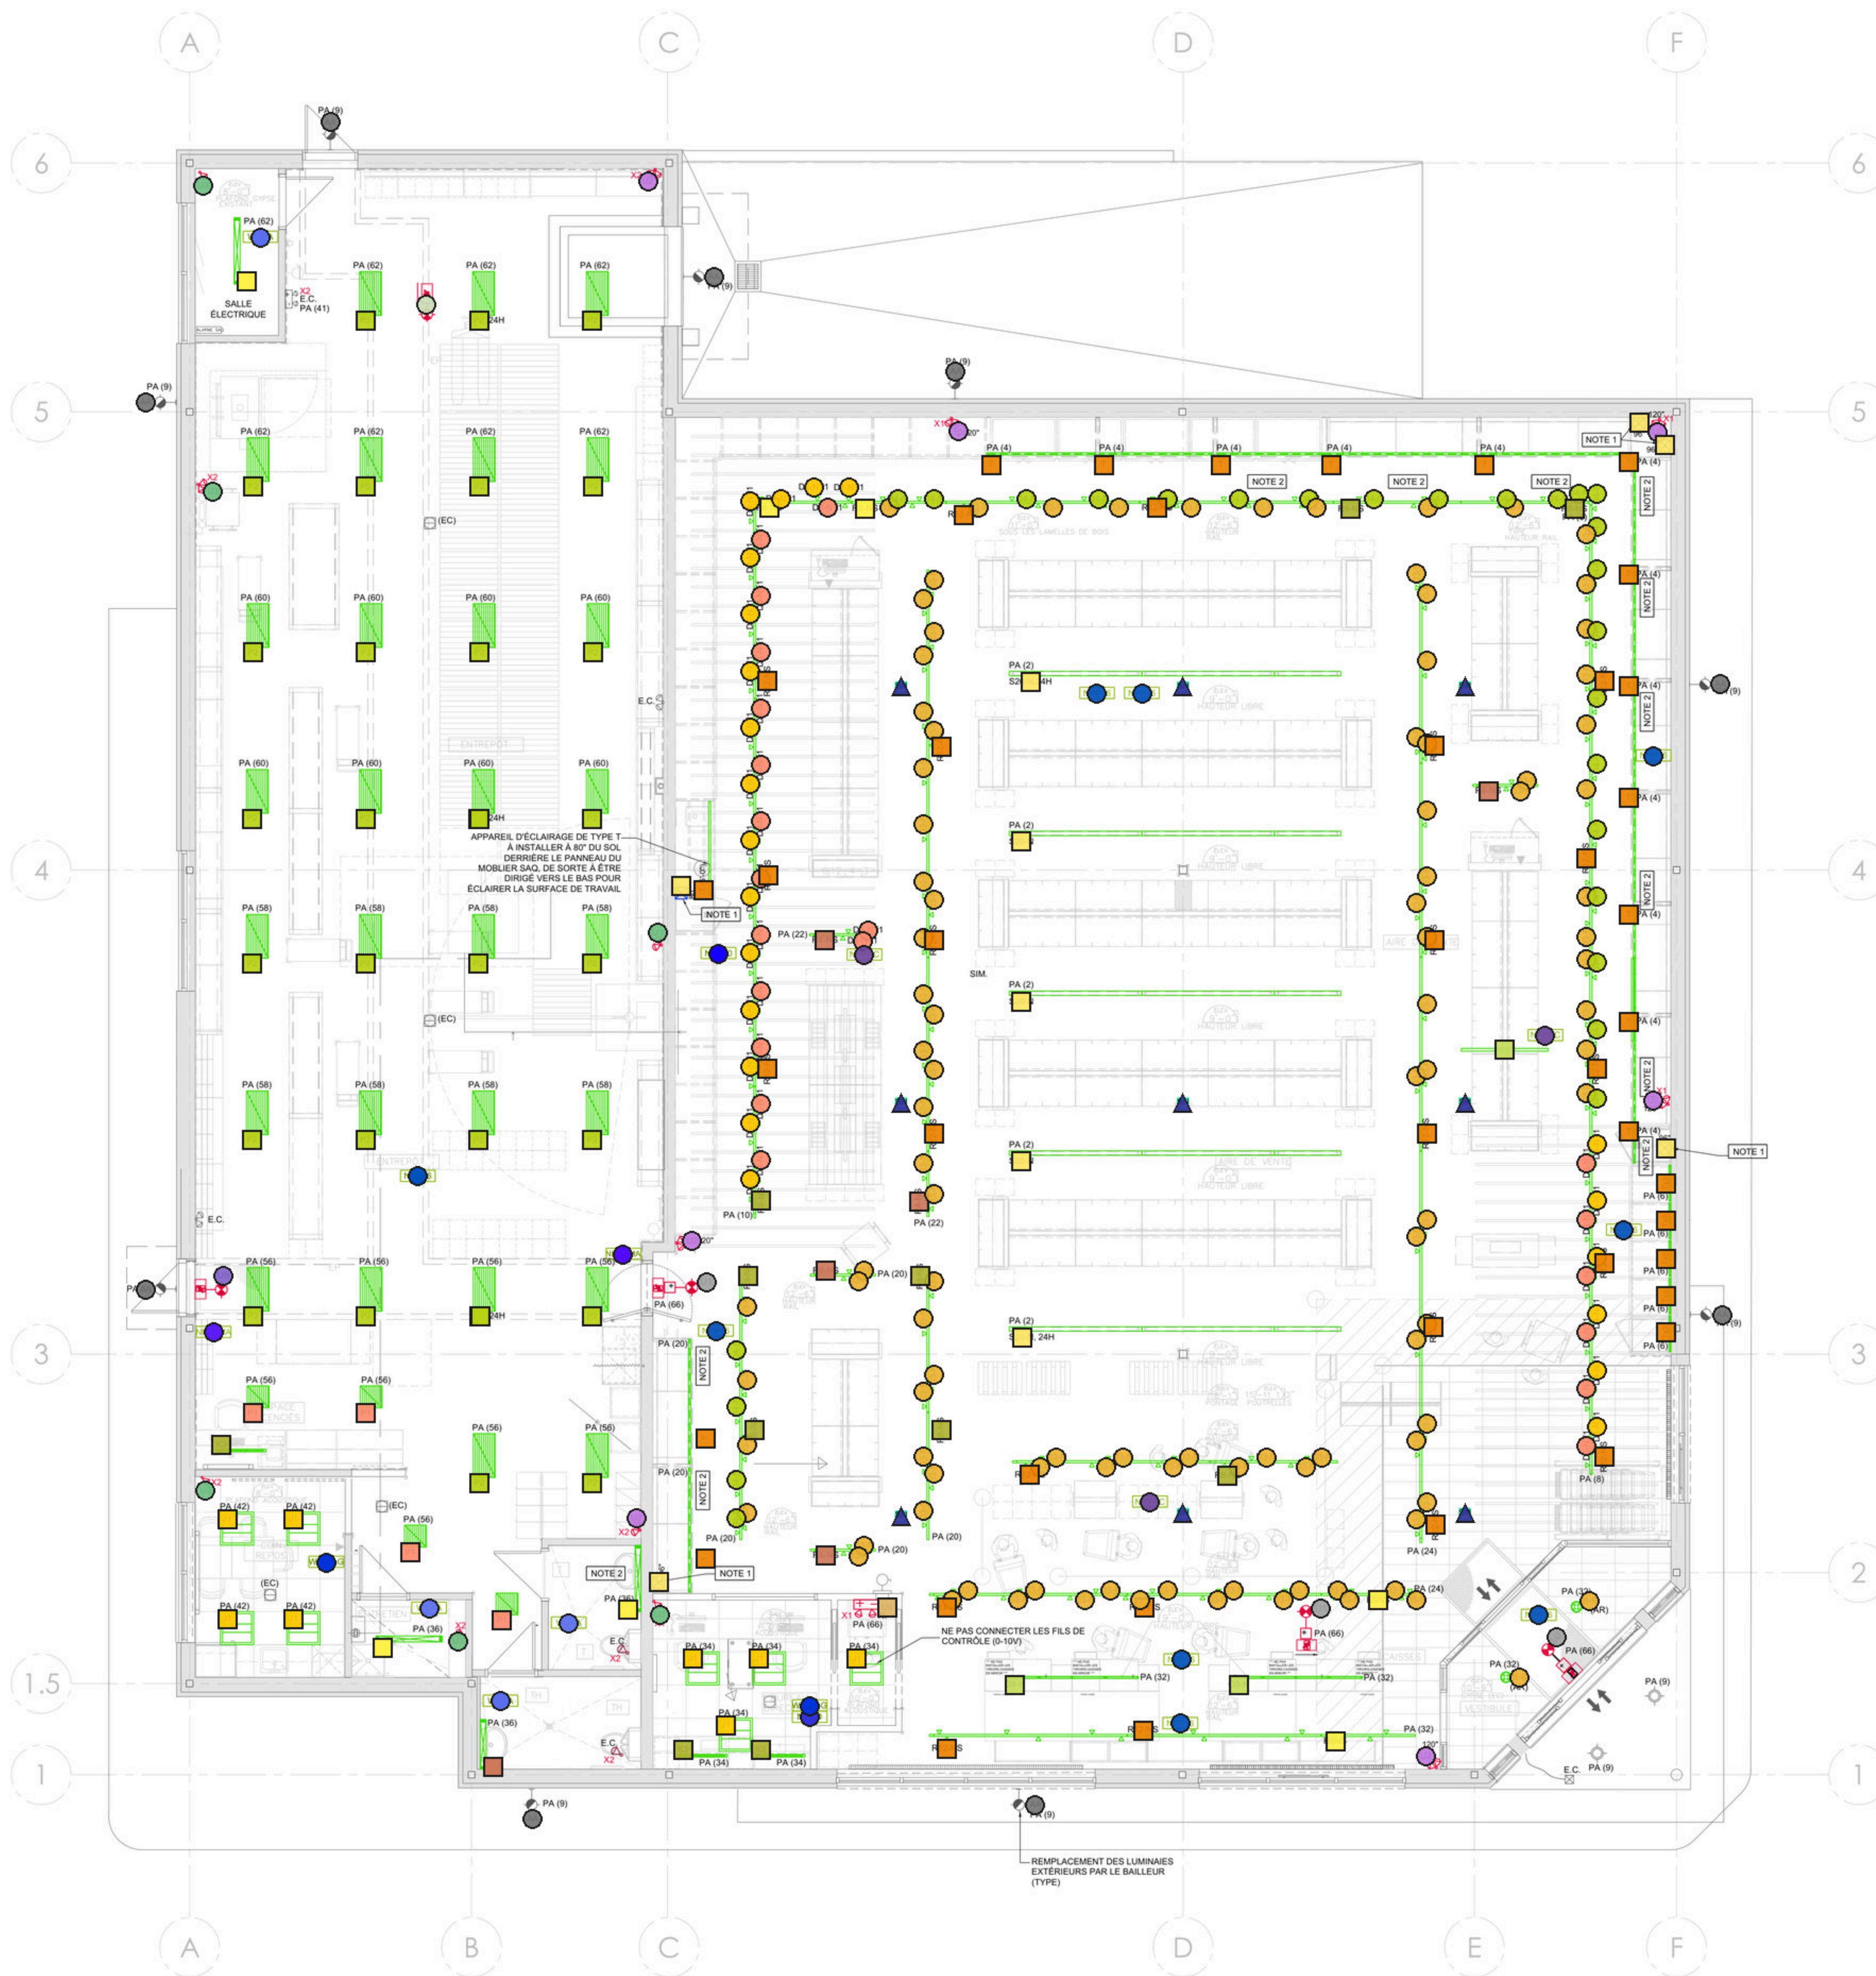

NOTES PLAFOND RÉFLÉCHI

- TOUS LES LUMINAIRES DEVONT ÊTRE APPROUVÉS CSA ET/OU UL ET PARTOUT OÙ C'EST POSSIBLE, ILS AURONT DES BALLASTS ÉLECTRONIQUES.
- REMETTRE AU RESPONSABLE DE PROJET DE LA SAQ UNE DISPOSITION PROPOSÉE DES APPAREILS PERMETTANT D'OBTENIR 50 PIEDS-BOUGIE À 2'-0" DU SOL.
- L'APPELLATION "24H" SIGNIFIE QUE L'APPAREIL DEVRA DEMEURER ALLUMÉ 24 HEURES (ÉCLAIRAGE DE SÉCURITÉ).
- VALIDER LES HAUTEURS D'INSTALLATION AVEC LE RESPONSABLE DE PROJET.
- L'ENTREPRENEUR OU LE SOUS-TRAITANT DOIT TRANSMETTRE UNE COPIE DU PLAN DE PLAFOND AU FOURNISSEUR CHOISI.
- L'ÉLECTRICIEN DEVRA AJUSTER LES FAISCEAUX LUMINEUX DES APPAREILS D'ÉCLAIRAGE DIRIGEABLES AVEC LE MOBILIER SAQ SUITE À SON INSTALLATION.
- DANS LE CAS D'UN PLAFOND À STRUCTURE APPARENTE, L'ÉLECTRICIEN ET L'ÉBÉNISTE DE L'ENTREPRENEUR DEVRONT PRÉVOIR LES CANTRUS NÉCESSAIRES POUR LEURS INSTALLATIONS. LES CANTRUS ET TIGES DE FIXATION DEVRONT ÊTRE PEINTS TEL QUE LE PLAFOND.

NOTES SPÉCIFIQUES - DÉMOLITION

- NOTE 1** BOÎTE DE JONCTION ENCASTRÉE DANS LE MUR POUR RACCORDEMENT DES APPAREILS D'ÉCLAIRAGE DE TYPE T. QUANTITÉ À VALIDER AU CHANTIER, ET LOCALISATION À COORDONNER AVEC LA SAQ. PRÉVOIR UNE PLAQUE DE FINITION À PRENDRE TEL QUE LE MUR.
- NOTE 2** L'ÉLECTRICIEN DEVRA INSTALLER LES APPAREILS D'ÉCLAIRAGE DE TYPE "T" AU DOS DE LA STRUCTURE INFÉRIEURE DU SYSTÈME DE SIGNALISATION MÉTALLIQUE DE L'AMÉNAGEMENT DE LA SAQ. LE FAISCEAU D'ÉCLAIRAGE DOIT ÊTRE ORIENTÉ VERS LE HAUT. CES DERNIERS DEVRONT ÊTRE VISSÉS DANS LA STRUCTURE D'ACIER PAR DERRIÈRE. LES VIS COUPÉS AU RAS DE LA STRUCTURE ET UNE RETOUCHE NOIRE DEVRA ÊTRE FAIT SUR LA VIS. LA DATE EXACTE D'INSTALLATION DEVRA ÊTRE COORDONNÉE AVEC LE RESPONSABLE DE PROJETS DE LA SAQ.

NOTE GÉNÉRALE

EN PLUS DU FILAGE DE PUISSANCE, FOURNIR, INSTALLER ET RACCORDER LES CÂBLES DE CONTRÔLE D'ÉCLAIRAGE BAS VOLTAGE 0-10V. SE RÉFÉRER AUX INSTRUCTIONS DU FABRICANT POUR UNE INSTALLATION COMPLÈTE ET FONCTIONNELLE. INSTALLER LES CÂBLES SOUS CONDUIT EMT ET CÂBLE AC90 C/A CONDUCTEURS BAS VOLTAGE POUR LE RACCORDEMENT FINAL AUX LUMINAIRES.

FOURNIR ET INSTALLER LES CONDUITS EMT REQUIS POUR LE RACCORDEMENT DES CIRCUITS DE CONTRÔLE D'ÉCLAIRAGE.

NOTES - PROTECTION IGNIFUGE


FOURNIR ET INSTALLER UNE PROTECTION IGNIFUGE AUTOUR DES BOÎTES DE JONCTION ENCASTRÉES TAO CP-617 DE 1/2" D'ÉPAISSEUR ÉQUIVALENT DANS LES DIVISIONS (MURS, PLANCHERS, PLAFON, INTERRUPTEURS, PRISES ÉLÉ, ETC.). VEUILLEZ-VOUS RÉFÉRER.

Légende — E300 (368 marques)

- Applique extérieure AA (bailleur) (9)
- Batterie U6 (1)
- Boîte de jonction profilé T (5)
- Contrôleur NPOD (2)
- Détecteur WSXA (6)
- Détecteur WSXA-G (4)
- Encastré B-B (2)
- Enseigne sortie U1 (3)
- Enseigne sortie U9 (1)
- Enseigne sortie — type à confirmer (1)
- ▲ Haut-parleur suspendu SN (9)
- Interrupteur NPODMA (3)
- Linéaire O8-N (2)
- Linéaire S20-N (5)
- Linéaire sans étiquette — à classer (1)
- Panneau P1 (4)
- Panneau P2 (31)
- Phare double U2 (7)
- Phare simple U3 (6)
- Profilé T (20)
- Projecteur D3-N (102)
- Projecteur D3-NT1 (21)
- Projecteur D4-N (27)
- Projecteur D4-NT1 (22)
- Rail R12-NS (23)
- Rail R4-NS (5)
- Rail R6-NS (4)
- Rail R8-NS (8)
- Relais NPP PCD (3)
- Relais NPP16 (10)
- Relais NPP20 (2)
- Réglette G3 (2)
- Réglette G4 (6)
- Réglette K3 (3)
- Troffer J1 (8)

NOTE GÉNÉRALE

IL A ÉTÉ CONVENU AVEC LE CLIENT QUE LES NIVEAUX D'ÉCLAIRAGE SERONT VALIDÉS ENTRE CE DERNIER ET LE FABRICANT. PAR CONSÉQUENT, DIRECTION 360 NE PEUT ÊTRE TENUE RESPONSABLE DES NIVEAUX D'ÉCLAIREMENT OBTENUS À LA FIN DES TRAVAUX.

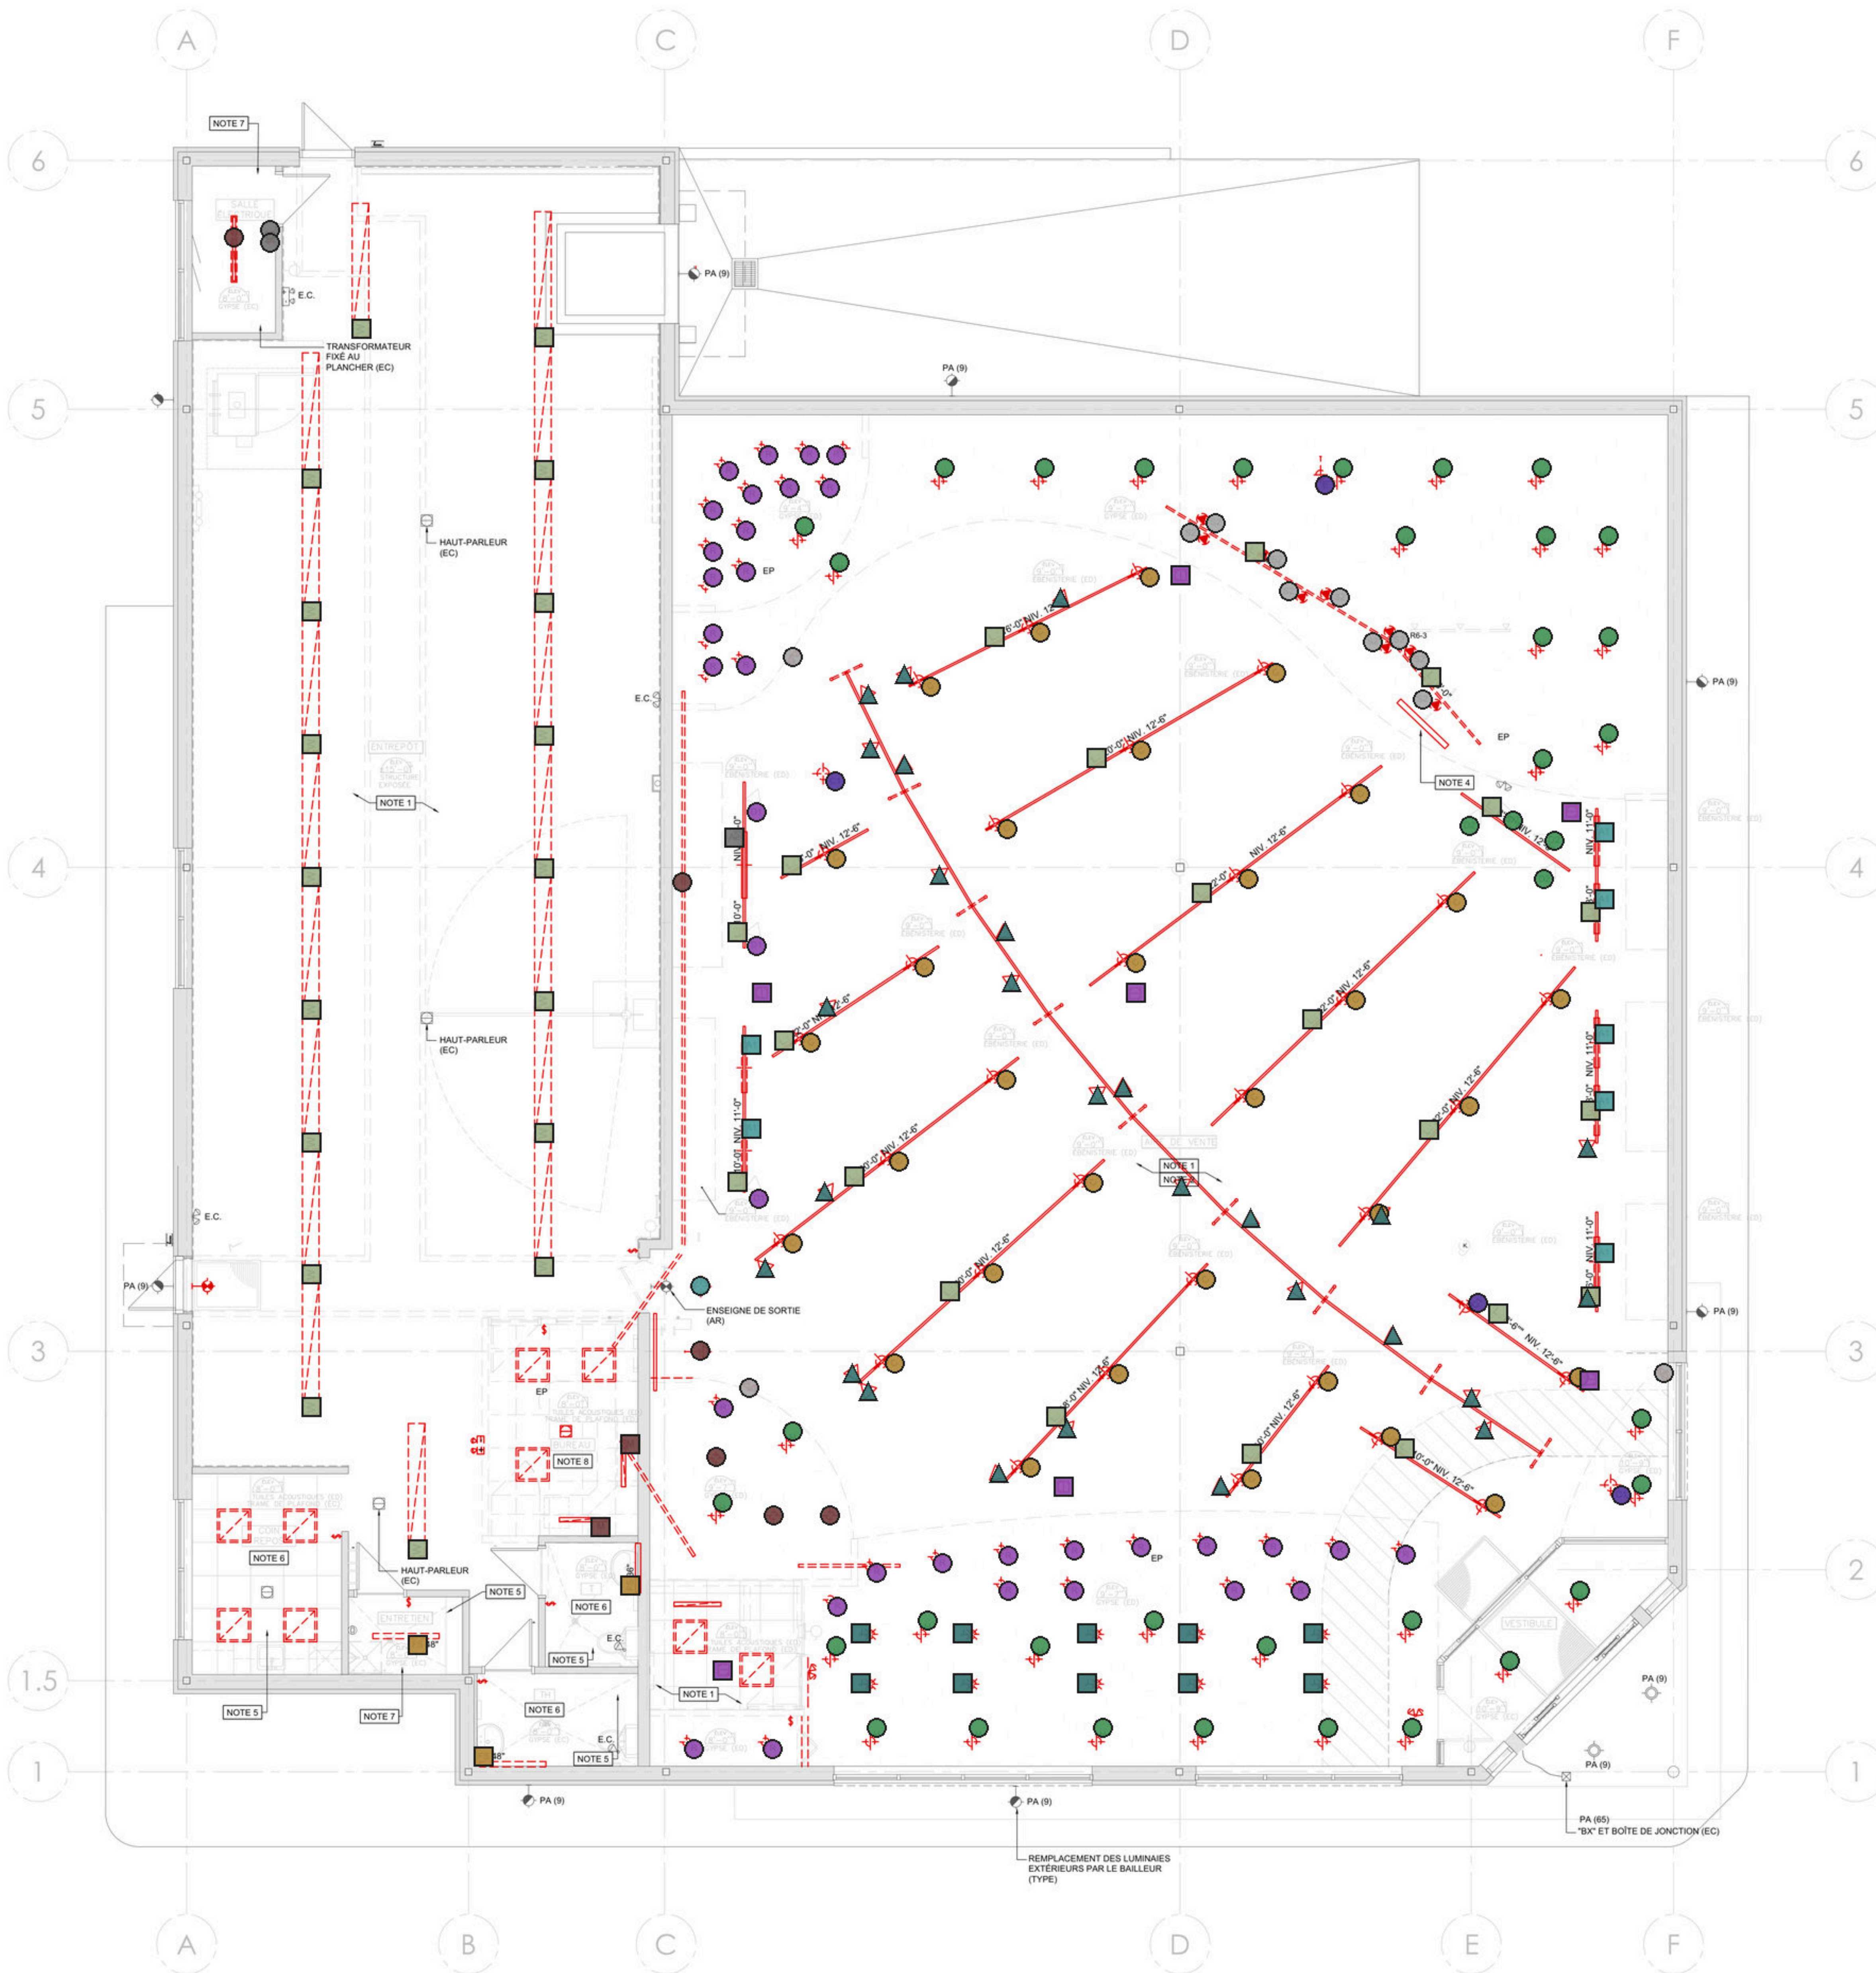

NOTES - DÉMOLITION

IL EST DE LA RESPONSABILITÉ DE L'ENTREPRENEUR D'ÉVALUER LES COÛTS DE DÉMOLITION DURANT LA VISITE DES LIEUX AVANT LA SOUMISSION.

SAUF INDICATION CONTRAIRE ET SI LE CLIENT NE DESIRE PAS LES CONSERVER, TOUS LES ÉQUIPEMENTS INDICÉS SUR LES PLANS DE DÉMOLITION SONT EXISTANTS À ENLEVER ET À DISPOSER HORS DU SITE.

REMETTRE AU PROPRIÉTAIRE TOUS LES ÉQUIPEMENTS QU'IL DESIRE CONSERVER ET LES ENTREPOSER À UN ENDROIT DÉSIGNÉ PAR CELUI-CI. CE QUE LE PROPRIÉTAIRE NE DESIRE PAS CONSERVER, L'ENTREPRENEUR DEVRA EN DISPOSER À SES FRAIS HORS DU SITE. COORDONNER AU CHANTIER AVEC LE PROPRIÉTAIRE LE CHEMINEMENT DES MATÉRIAUX ENLEVÉS ET LES NOUVEAUX ÉQUIPEMENTS À INSTALLER.

L'ENTREPRENEUR ÉLECTRICIEN DOIT FAIRE UN TRAÇAGE DES CIRCUITS ET IDENTIFIER LES CIRCUITS DES APPAREILS TOUCHÉS DURANT LES TRAVAUX DANS TOUS LES PANNEAUX ET SOUS-PANNEAUX. TOUS LES CÂBLES ET FILAGE ÉLECTRIQUE ET TÉLÉCOM DÉSAFFECTÉS DOIVENT ÊTRE ENLEVÉS ET DISPOSÉS.

ENLEVER TOUS LES CONDUCTEURS, CONDUITS ET CÂBLES EXISTANTS JUSQU'À LA SOURCE OU JUSQU'À LA DERNIÈRE BOÎTE DE JONCTION TOUJOURS EN FONCTION. BOUCHER LES OUVERTURES FAITES DANS LES BOÎTES ET BOÎTIERS AVEC LES ACCESSOIRES REQUIS.

ALIMENTER ET RACCORDER TOUS LES APPAREILS D'ÉCLAIRAGE EXISTANTS, PRISES OU AUTRES ÉQUIPEMENTS TOUJOURS REQUIS (INCLUANT CEUX HORS DE LA ZONE DES TRAVAUX) ET DONT L'ALIMENTATION ÉLECTRIQUE A ÉTÉ DÉBRANCHÉE DURANT LES TRAVAUX DE DÉMOLITION.

DÉBRANCHER LES ÉQUIPEMENTS MÉCANIQUES POUR LEUR DÉMÂTELEMENT PAR D'AUTRES (COORDONNER AVEC L'ENTREPRENEUR EN MÉCANIQUE).

LES ÉQUIPEMENTS EXISTANTS DANS LA ZONE DES TRAVAUX SONT INDICÉS À TITRE INFORMATIF ET POUR DES FINS DE SOUMISSIONS. À MOINS D'INDICATION CONTRAIRE, TOUS LES ÉQUIPEMENTS RACCORDÉS ÉLECTRIQUEMENT SONT EXISTANTS À ENLEVER INCLUANT LES ÉQUIPEMENTS NON MONTRES AU PLANS.

TOUS LES CÂBLES DE TÉLÉCOMMUNICATION EXISTANTS DANS LA ZONE DES TRAVAUX (INCLUANT LES SYSTÈMES INTERCOMS, TÉLÉPHONIQUES, ETC.) SONT À ENLEVER JUSQU'À LA SOURCE.

FOURNIR, INSTALLER ET RACCORDER UN ÉCLAIRAGE TEMPORAIRE DANS LA ZONE DES TRAVAUX.


NOTES GÉNÉRALES - DÉMOLITION

1. PRÉPARER TOUTES LES SURFACES POUR RECEVOIR LES NOUVEAUX FINIS. ENLEVER VIS ET AUTRES DÉBRIS ET RAGRÉER LES SURFACES AU BÉTON.
2. LES TRAVAUX DE DÉMOLITION ET CONTRÔLE DES POUSSIÈRES DÉCRITS AUX PLANS D'ARCHITECTURE NE SONT PAS LIMITATIFS. VOIR LES DOCUMENTS DES AUTRES DISCIPLINES.
3. L'ENTREPRENEUR DOIT SUIVRE LES RECOMMANDATIONS D'UN INGÉNIEUR EN STRUCTURE POUR TOUS LES PERÇEMENTS OU LE RAGRÉAGE DES OUVERTURES DANS LA DALLE DE BÉTON EXISTANTE. L'ENTREPRENEUR DOIT S'ASSURER D'EFFECTUER AUCUN NOUVEAU PERÇEMENT DANS UN ÉLÉMENT STRUCTURAL POUVANT COMPROMETTRE L'INTÉGRITÉ STRUCTURALE ET DE NE PAS PERÇER AUCUN CONDUIT. INCLURE TOUS LES SCANS DE LA DALLE REQUIS PAR UN PROFESSIONNEL.
4. L'ENTREPRENEUR DEVRA VEILLER À NE PAS ENDOMMAGER LA STRUCTURE CONSERVÉE ET L'AMÉNAGEMENT EXTÉRIEUR CONSERVÉ AU PÉRIMÈTRE DU BÂTIMENT.
5. LES TRAVAUX DE DÉMOLITION DEVONT SE FAIRE EN CONFORMITÉ AUX CONDITIONS DES DOCUMENTS DU CONSULTANT EN HYGIÈNE.
6. LE TERME "DÉMOLIR" UTILISÉ DANS CES DOCUMENTS N'IMPLIQUE PAS NÉCESSAIREMENT UNE DESTRUCTION, MAIS IMPLIQUE PLUTÔT, SANS SE LIMITER, DÉMANTÉLER, DÉMONTÉ, DÉGARNIR, ENLEVER, DÉCONSTRUIRE OU RETIRER, ET REQUISER POSSIBLEMENT DES PRÉCAUTIONS NÉCESSAIRES POUR ACCUEILLIR LES NOUVEAUX ÉLÉMENTS OU ASSEMBLAGES. PRENDRE NOTE QUE LES COMPOSANTES DÉMOLIES CONTIENNENT OU PEUVENT CONTENIR DE L'AMIANTE. POUR LA DISPOSITION DES MATÉRIAUX CONTAMINÉS, SE RÉFÉRER AUX DOCUMENTS D'HYGIÈNE DU MAÎTRE DE L'OUVRAGE POUR PRENDRE LES MESURES NÉCESSAIRES.
7. PRENDRE NOTE QUE LES COMPOSANTES DÉMOLIES CONTIENNENT OU PEUVENT CONTENIR DES MATÉRIAUX NOCIFS POUR LA SANTÉ ET L'ENVIRONNEMENT. SE RÉFÉRER AUX DOCUMENTS D'HYGIÈNE POUR PRENDRE LES MESURES NÉCESSAIRES.
8. LORSQUE REQUIS POUR LA NATURE DES TRAVAUX INDICÉS AU PLAN, INCLURE LES ÉTANÇONS TEMPORAIRES POUR SUPPORTER LES MATÉRIAUX EXISTANTS À CONSERVER EN PLACE.
9. TOUT ENTREPOSAGE ET PROTECTION DES ÉLÉMENTS RÉCUPÉRABLES LORS DE LA DÉMOLITION SONT À LA CHARGE DE L'ENTREPRENEUR.

NOTES SPÉ

Légende — E300D (226 marques)

- | | | |
|---------|-------------------------------------|-------------------------------------|
| NOTE 1 | SAUF INDICATIONS À RETIRER ET COND | ■ Démo carré-cercle — à classer (7) |
| NOTE 2 | N/A | ● Démo enseigne de sortie (1) |
| NOTE 3 | N/A | ● Démo interrupteur (2) |
| NOTE 4 | N/A | ■ Démo luminaire A1 (7) |
| NOTE 5 | THERMOSTAT RELIÉ LE BUREAU DE L'AIR | ■ Démo luminaire A2 (1) |
| NOTE 6 | N/A | ● Démo luminaire C (32) |
| NOTE 7 | EMPLACEMENT EXIS | ● Démo luminaire C1 (3) |
| NOTE 8 | SONDE EXISTANTE | ● Démo luminaire D1 (3) |
| NOTE 9 | MEULER L'ENSEMBL LA DALLE À RECEVO | ● Démo luminaire D2 (4) |
| NOTE 10 | SAUF INDICATION C MURS DE L'ENTREPR | ● Démo luminaire E (1) |
| NOTE 11 | N/A | ■ Démo luminaire FS (3) |
| | | ● Démo luminaire H (34) |
| | | ■ Démo luminaire J (10) |
| | | ■ Démo luminaire M (2) |
| | | ● Démo luminaire R (32) |
| | | ● Démo luminaire S2 (9) |
| | | ■ Démo luminaire W (18) |
| | | ● Démo luminaire sans type (6) |
| | | ● Démo phare d'urgence (3) |
| | | ▲ Démo projecteur sur rail (27) |
| | | ■ Démo rail existant (21) |

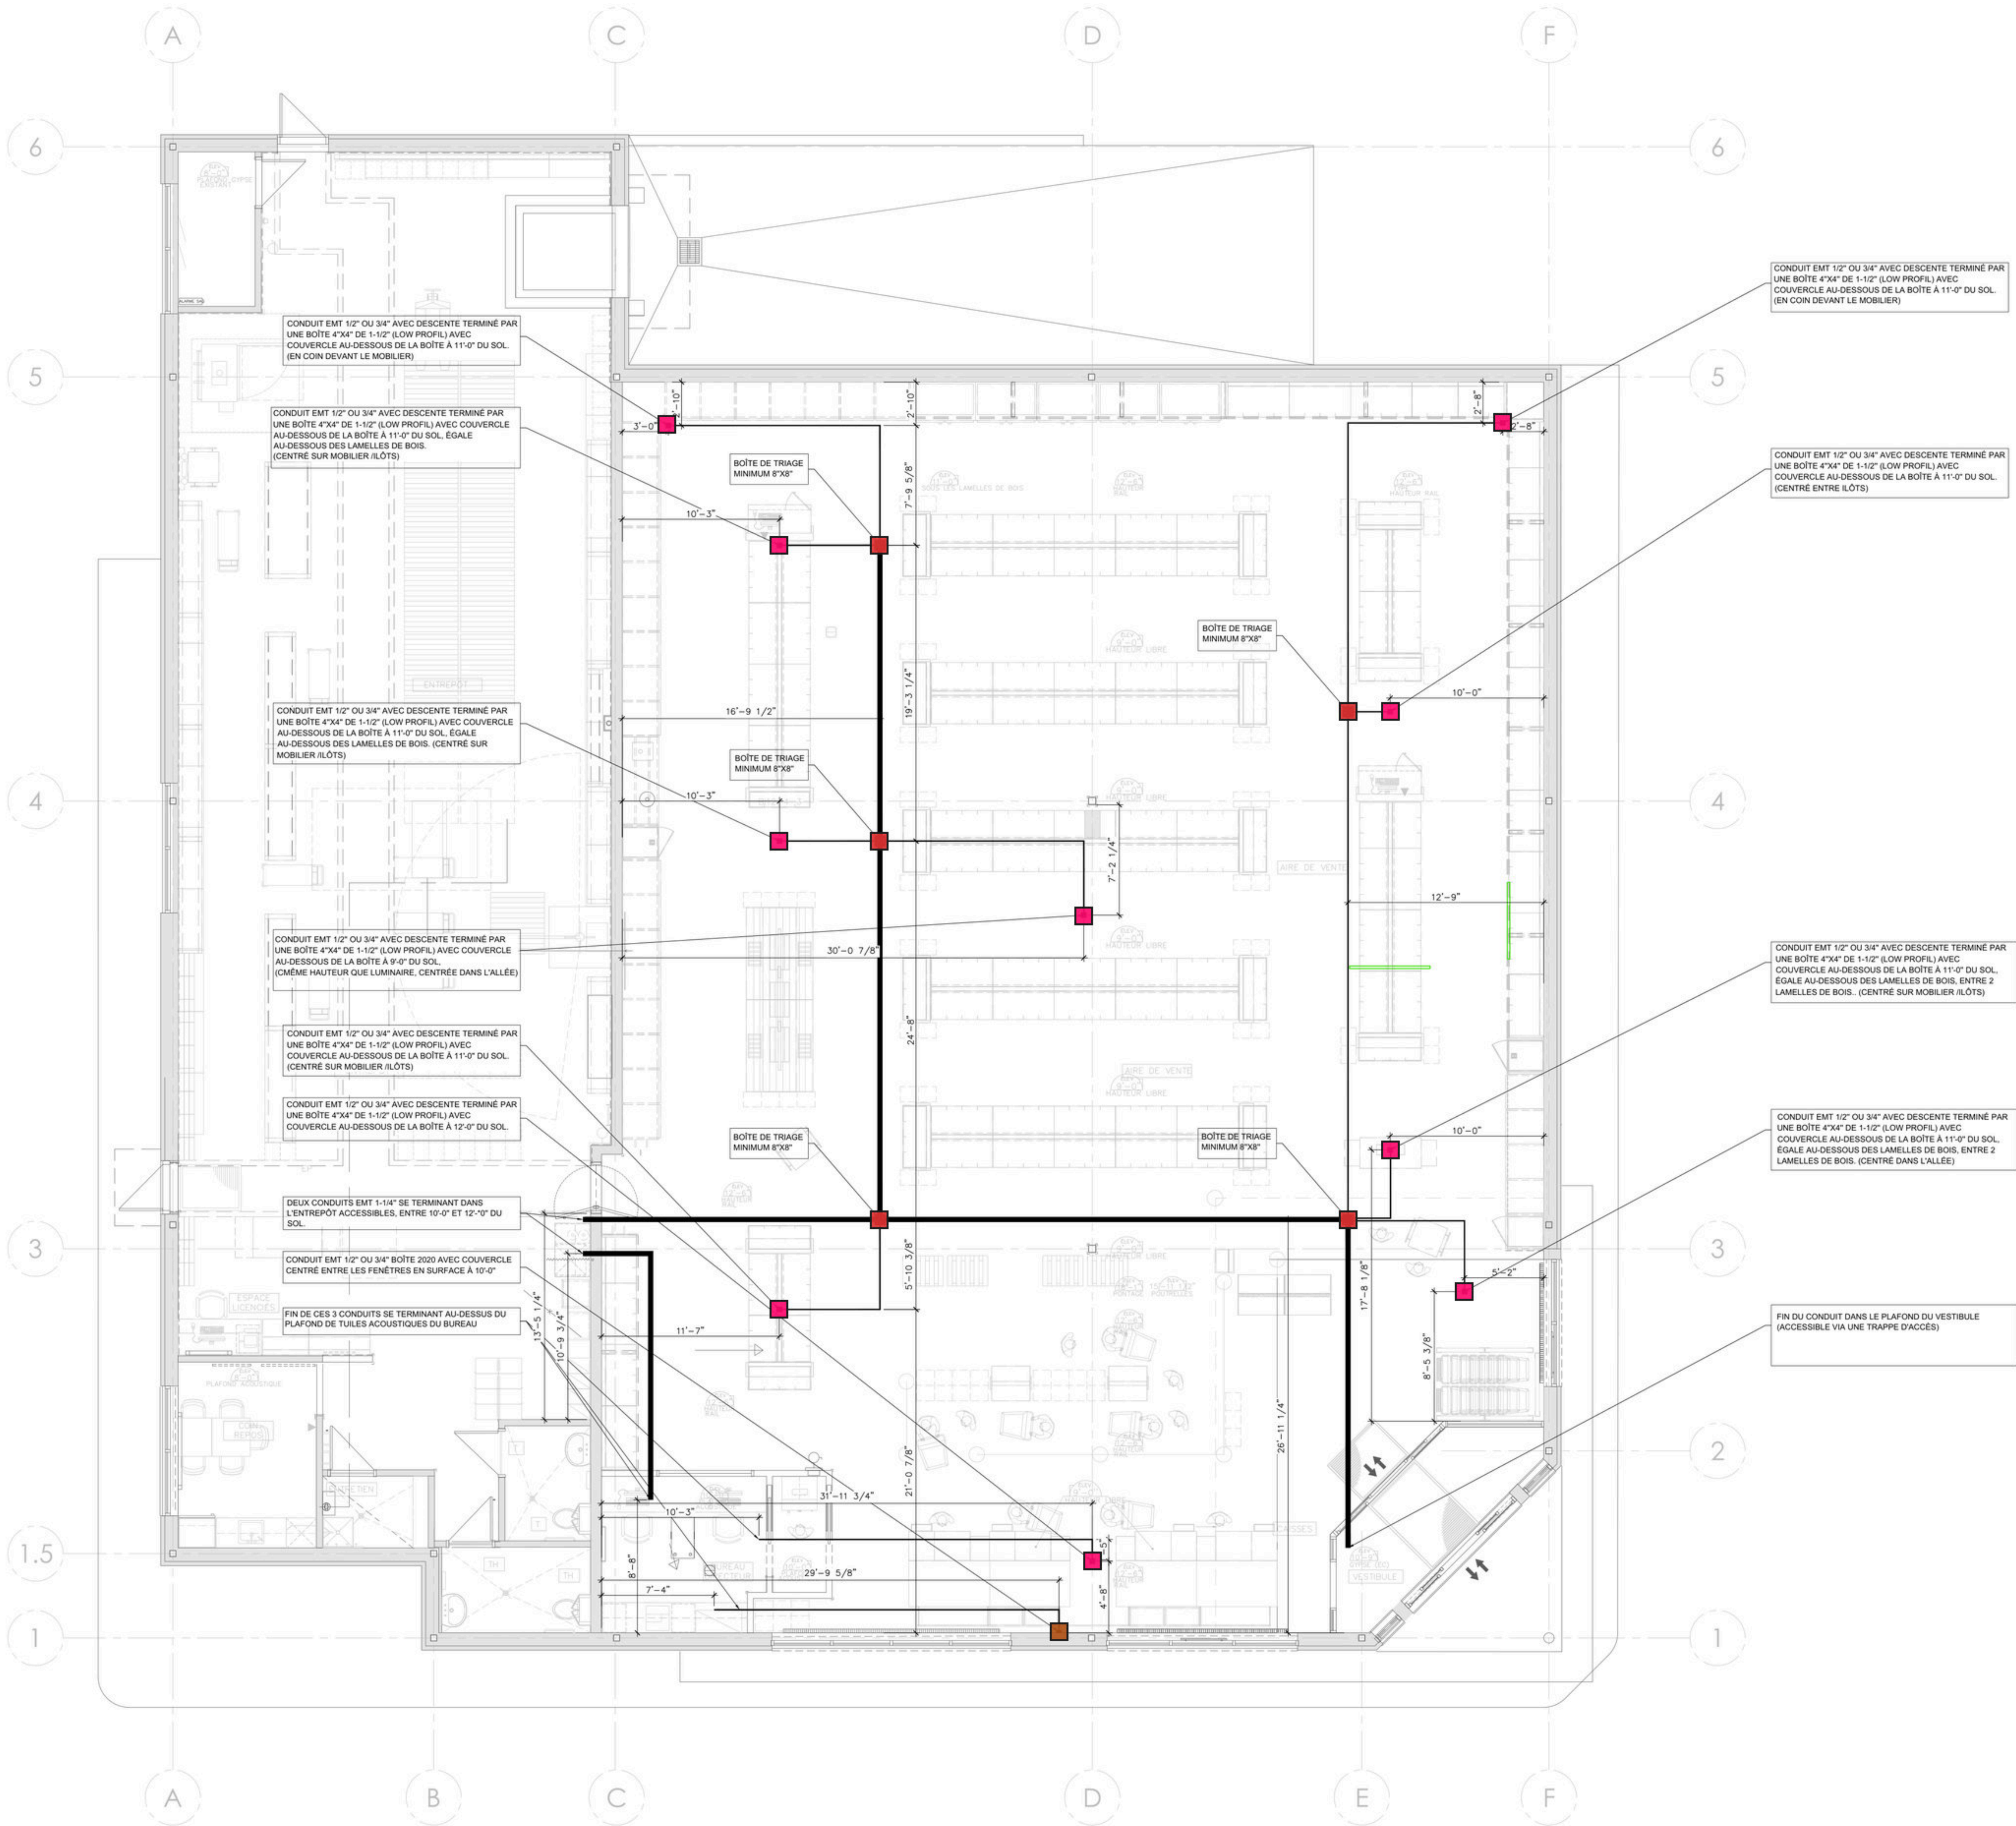

- Légende — E400 (16 marques)
- Boîte 2x2 conduit 3/4 (fenêtres) (1)
 - Boîte de tirage 8x8 (5)
 - Descente EMT + boîte 4x4 (10)

EMT 1-1/4"
EMT 3/4"
TOUS LES CONDUITS DEVONT AVOIR UNE CORDE DE TRIAGE
AUCUNE BOÎTE DE TRIAGE/LS INACCESSIBLE
AU-DESSUS DES LAMELLES

NOTE GÉNÉRALE

CE PLAN EST UN EXTRAIT DU PLAN D'ARCHITECTURE ET EST PRÉSENT À TITRE
INFORMATIF. COORDONNER AVEC LE CLIENT LES DÉTAILS ET L'EMPLACEMENT EXACT DES
COMPOSANTES.

NE PAS UTILISER
POUR CONSTRUCTION

0		2026-08-26	POUR SOUMISSIONS	J.B.
NO	DATE	AAAA-MM-JJ	RÉVISION	PAR



SAQ
SAQ VARENNES
VARENNES, QC, J3X 1P7

ÉLECTRICITÉ
ONDUITS DU SYSTÈME
DE SÉCURITÉ

ÉLECTRIQUE	
Conçu par H. HATTAB, CPI	DATE (AAAA-MM-JJ) 2026-07-13
Évalué par F. BELAND, tech.	ÉCHELLE INDIQUÉE
Vérifié par J. BACHKONGKI, ING.	NOUVEAU PROJET 26-0094-02
Approuvé par J. BACHKONGKI, Ing.	PLAN NO E400