


[illegible]


E150

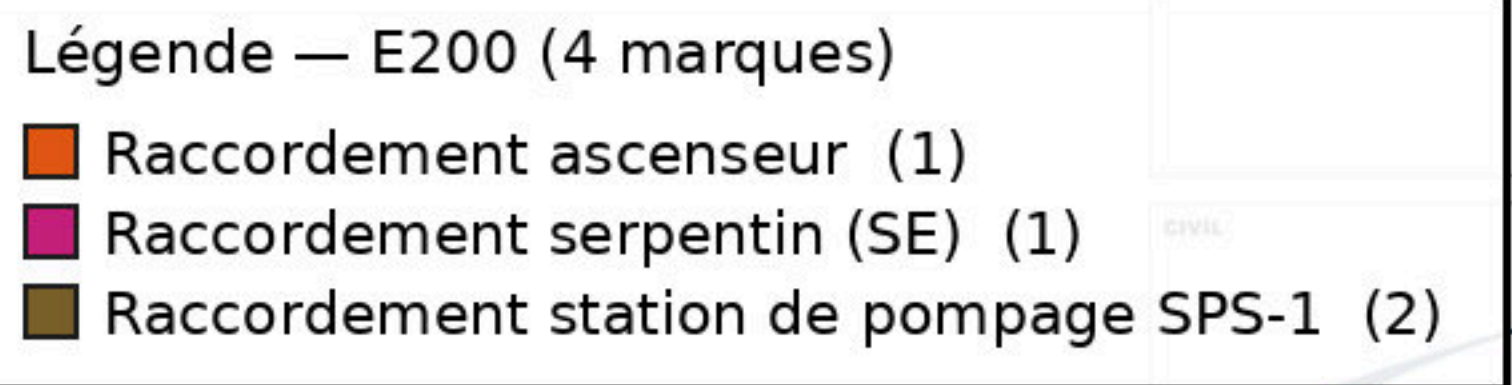

CE PLAN EST LA PROPRIÉTÉ DES PROFESSIONNELS CI-DESSOUS MENTIONNÉS. IL EST PRÊTÉ À CONDITION QU'IL NE SOIT PAS UTILISÉ À L'ENCONTRE DE LEUR INTÉRÊT NI REPRODUIT EN TOUT OU EN PARTIE ET QU'IL LEUR SOIT REMIS SUR DEMANDE.

AVANT DE PROCÉDER À L'INSTALLATION DES COMPOSANTES ET DES SYSTÈMES ELECTROMECANQUES, L'ENTREPRENEUR DOIT CONSULTER LES DERNIERS PLANS EMIS D'ARCHITECTURE. TOUTES LES MESURES DOIVENT ÊTRE PRISES À PARTIR DES DERNIERS PLANS D'ARCHITECTURE.

CE PROJET DOIT SERVIR À LA CONSTRUCTION QUE SI LA MENTION "POUR CONSTRUCTION" FIGURE DANS LA LISTE DES REVISIONS CI-DESSOUS ET QU'IL SOIT DÔMENT SIGNÉ PAR L'INGÉNIEUR.

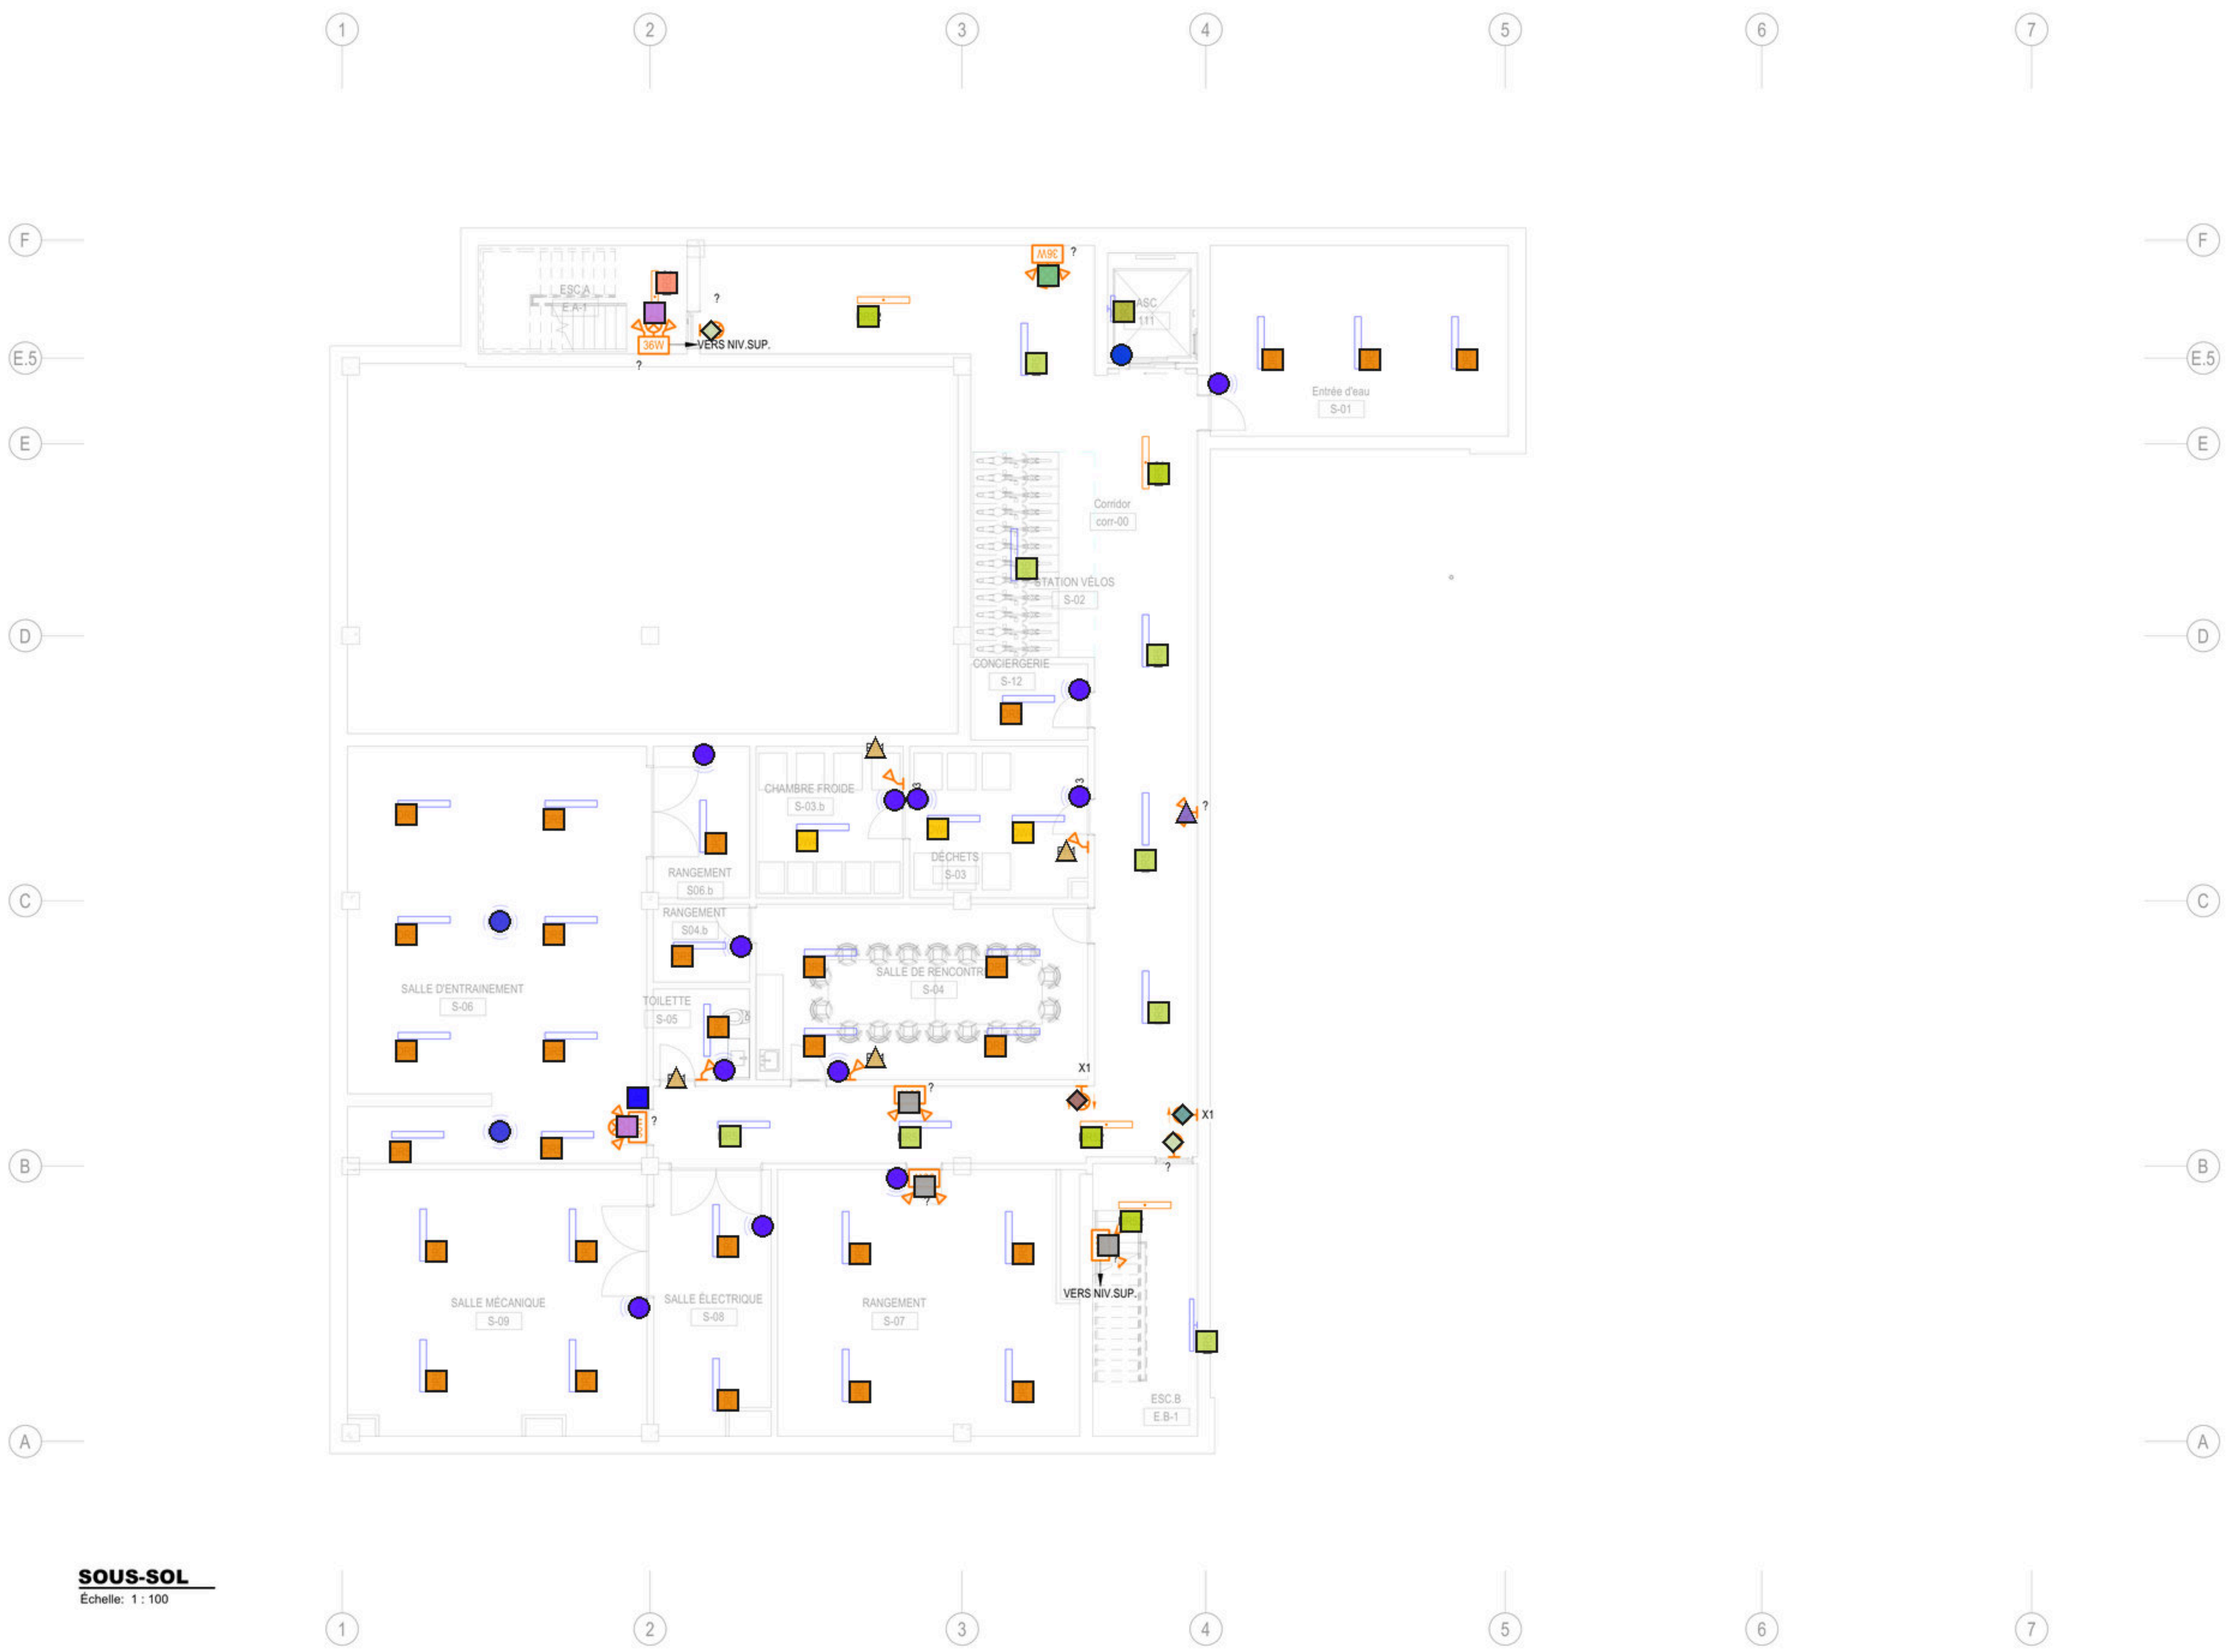

- Légende — E400 (77 marques)
- Accumulateur c/a 2 phares (3)
- Accumulateur c/a 2 phares + enseigne (2)
- Accumulateur c/a 2 phares + enseigne (flèche) (1)
- Bouton-poussoir (B) (1)
- Détecteur inoccupation mural (Do) (12)
- Détecteur inoccupation plafond (Do) (2)
- Ensigne issue 1 face murale (flèche) (1)
- Ensigne issue 1 face murale tout droit (2)
- Ensigne issue 2 faces murale (1)
- Interrupteur unipolaire (1)
- Luminaire DR2 (1)
- Luminaire DR5 (29)
- Luminaire DR51 (8)
- Luminaire DR52 (1)
- Luminaire DR52 service continu (4)
- Luminaire DW4 (3)
- Phare urgence double mural (1)
- Phare urgence simple mural (4)

1	SOUSSION	2026-08-17
A	PERMIS	2026-05-08
NO.	Émis pour	Date

TITRE DU PLAN:

SOUS-SOL - ÉCLAIRAGE

PRÉPARE PAR:

M. BATISTA, ing.

J. GILBERT, tech.

DESSINÉ PAR:

T. CANDU

DATE:

AVRIL 2026

DOSSIER:

25-0810-QC

DISCIPLINE:

ÉLECTRICITÉ

SCEAU



PLAN:

E400

Sous-sol
Echelle: 1 : 100




- | | | |
|-----|-----------|------------|
| 1 | SOUSSION | 2026-08-17 |
| A | PERMIS | 2026-05-08 |
| NO. | Émis pour | Date |

TITRE DU PLAN:	
REZ DE CHAUSSÉE - ÉCLAIRAGE	
PRÉPARE PAR:	SCEAU
M. BATISTE, ing. J. GILBERT, tech.	
DESSINÉ PAR:	
T. CANDU	
DATE:	
AVRIL 2006	
DOSSIER:	
25-0810-QC	
DISCIPLINE:	PLAN:
ÉLECTRICITÉ	E401

CE PLAN EST LA PROPRIÉTÉ DES PROFESSIONNELS CI-DESSOUS MENTIONNÉS. IL EST PRÊTÉ À CONDITION QU'IL NE SOIT PAS UTILISÉ À L'ENCONTRE DE LEUR INTÉRÊT NI REPRODUIT EN TOUT OU EN PARTIE ET QU'IL LEUR SOIT REMIS SUR DEMANDE.

AVANT DE PROCÉDER À L'INSTALLATION DES COMPOSANTES ET DES SYSTÈMES ÉLECTROMÉCANIQUES, L'ENTREPRENEUR DOIT CONSULTER LES DERNIERS PLANS ÉMIS D'ARCHITECTURE. TOUTES LES MESURES DOIVENT ÊTRE PRISES À PARTIR DES DERNIERS PLANS D'ARCHITECTURE.

CE PROJET DOIT SERVIR À LA CONSTRUCTION QUE SI LA MENTION "POUR CONSTRUCTION" FIGURE DANS LA LISTE DES RÉVISIONS CI-DESSOUS ET QU'IL SOIT DÔMENT SIGNÉ PAR L'INGÉNIEUR.

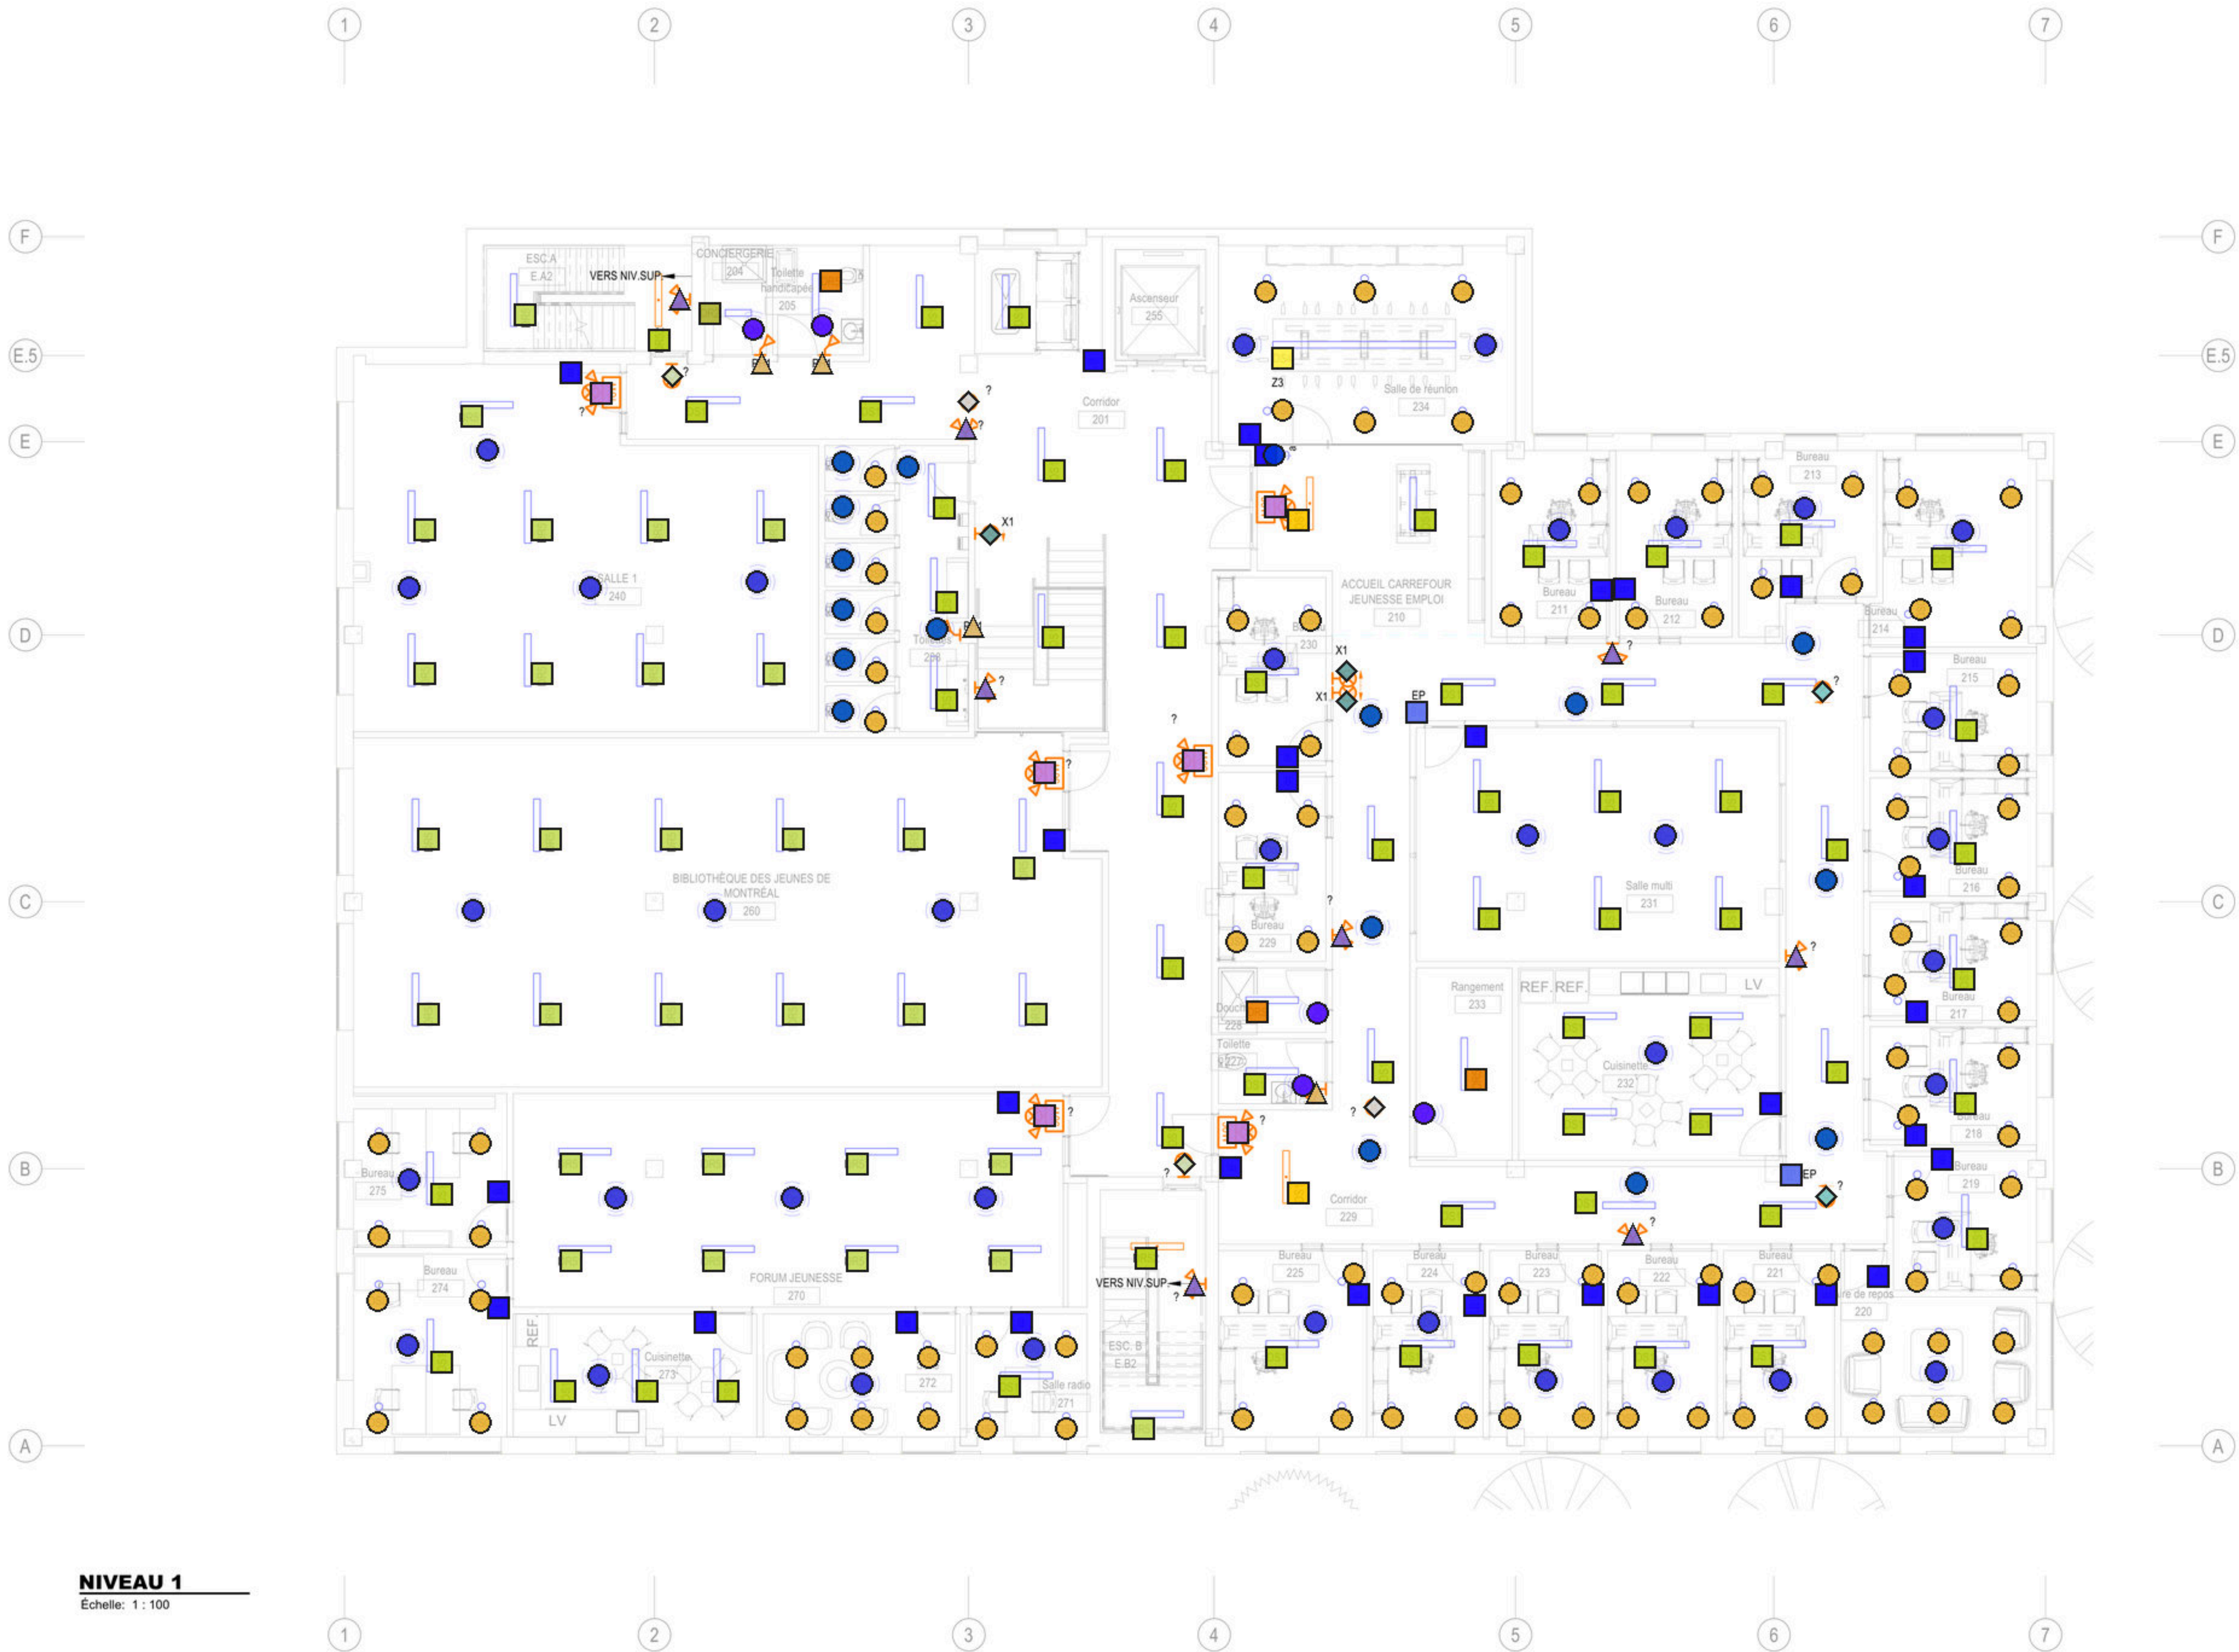

Légende — E402 (317 marques)

■

 Accumulateur c/a 2 phares + enseigne (6)

■

 Bloc d'alimentation (Ba) (2)

■

 Bouton-poussoir (B) (31)

●

 Détecteur infrarouge plafond (Di) (16)

●

 Détecteur inoccupation mural (Do) (5)

●

 Détecteur inoccupation plafond (Do) (37)

◆

 Enseigne issue 1 face murale (flèche) (3)

◆

 Enseigne issue 1 face murale tout droit (2)

◆

 Enseigne issue 1 face plafond (flèche) (2)

◆

 Enseigne issue 1 face plafond tout droit (2)

●

 Interrupteur unipolaire (1)

■

 Luminaire DR2 (1)

■

 Luminaire DR5 (3)

■

 Luminaire DR51 (31)

■

 Luminaire DR52 service continu (2)

●

 Luminaire DS0 (100)

■

 Luminaire DS1 (58)

■

 Luminaire DS1 service continu (2)

■

 Luminaire DS4 (1)

▲

 Phare urgence double mural (8)

▲

 Phare urgence simple mural (4)

1	SOUSSION	2026-08-17
A	PERMIS	2026-05-08
NO.	Émis pour	Date

TITRE DU PLAN:

NIVEAU 1 - ÉCLAIRAGE

PRÉPARÉ PAR:

M. BATISTA, ing.

J. GILBERT, tech.

DESSINÉ PAR:

T. CANDU

DATE:

AVRIL 2026

DOSSIER:

25-0810-QC

DISCIPLINE:

ÉLECTRICITÉ


SCEAU



PLAN:

E402

NIVEAU 1
Echelle: 1 : 100

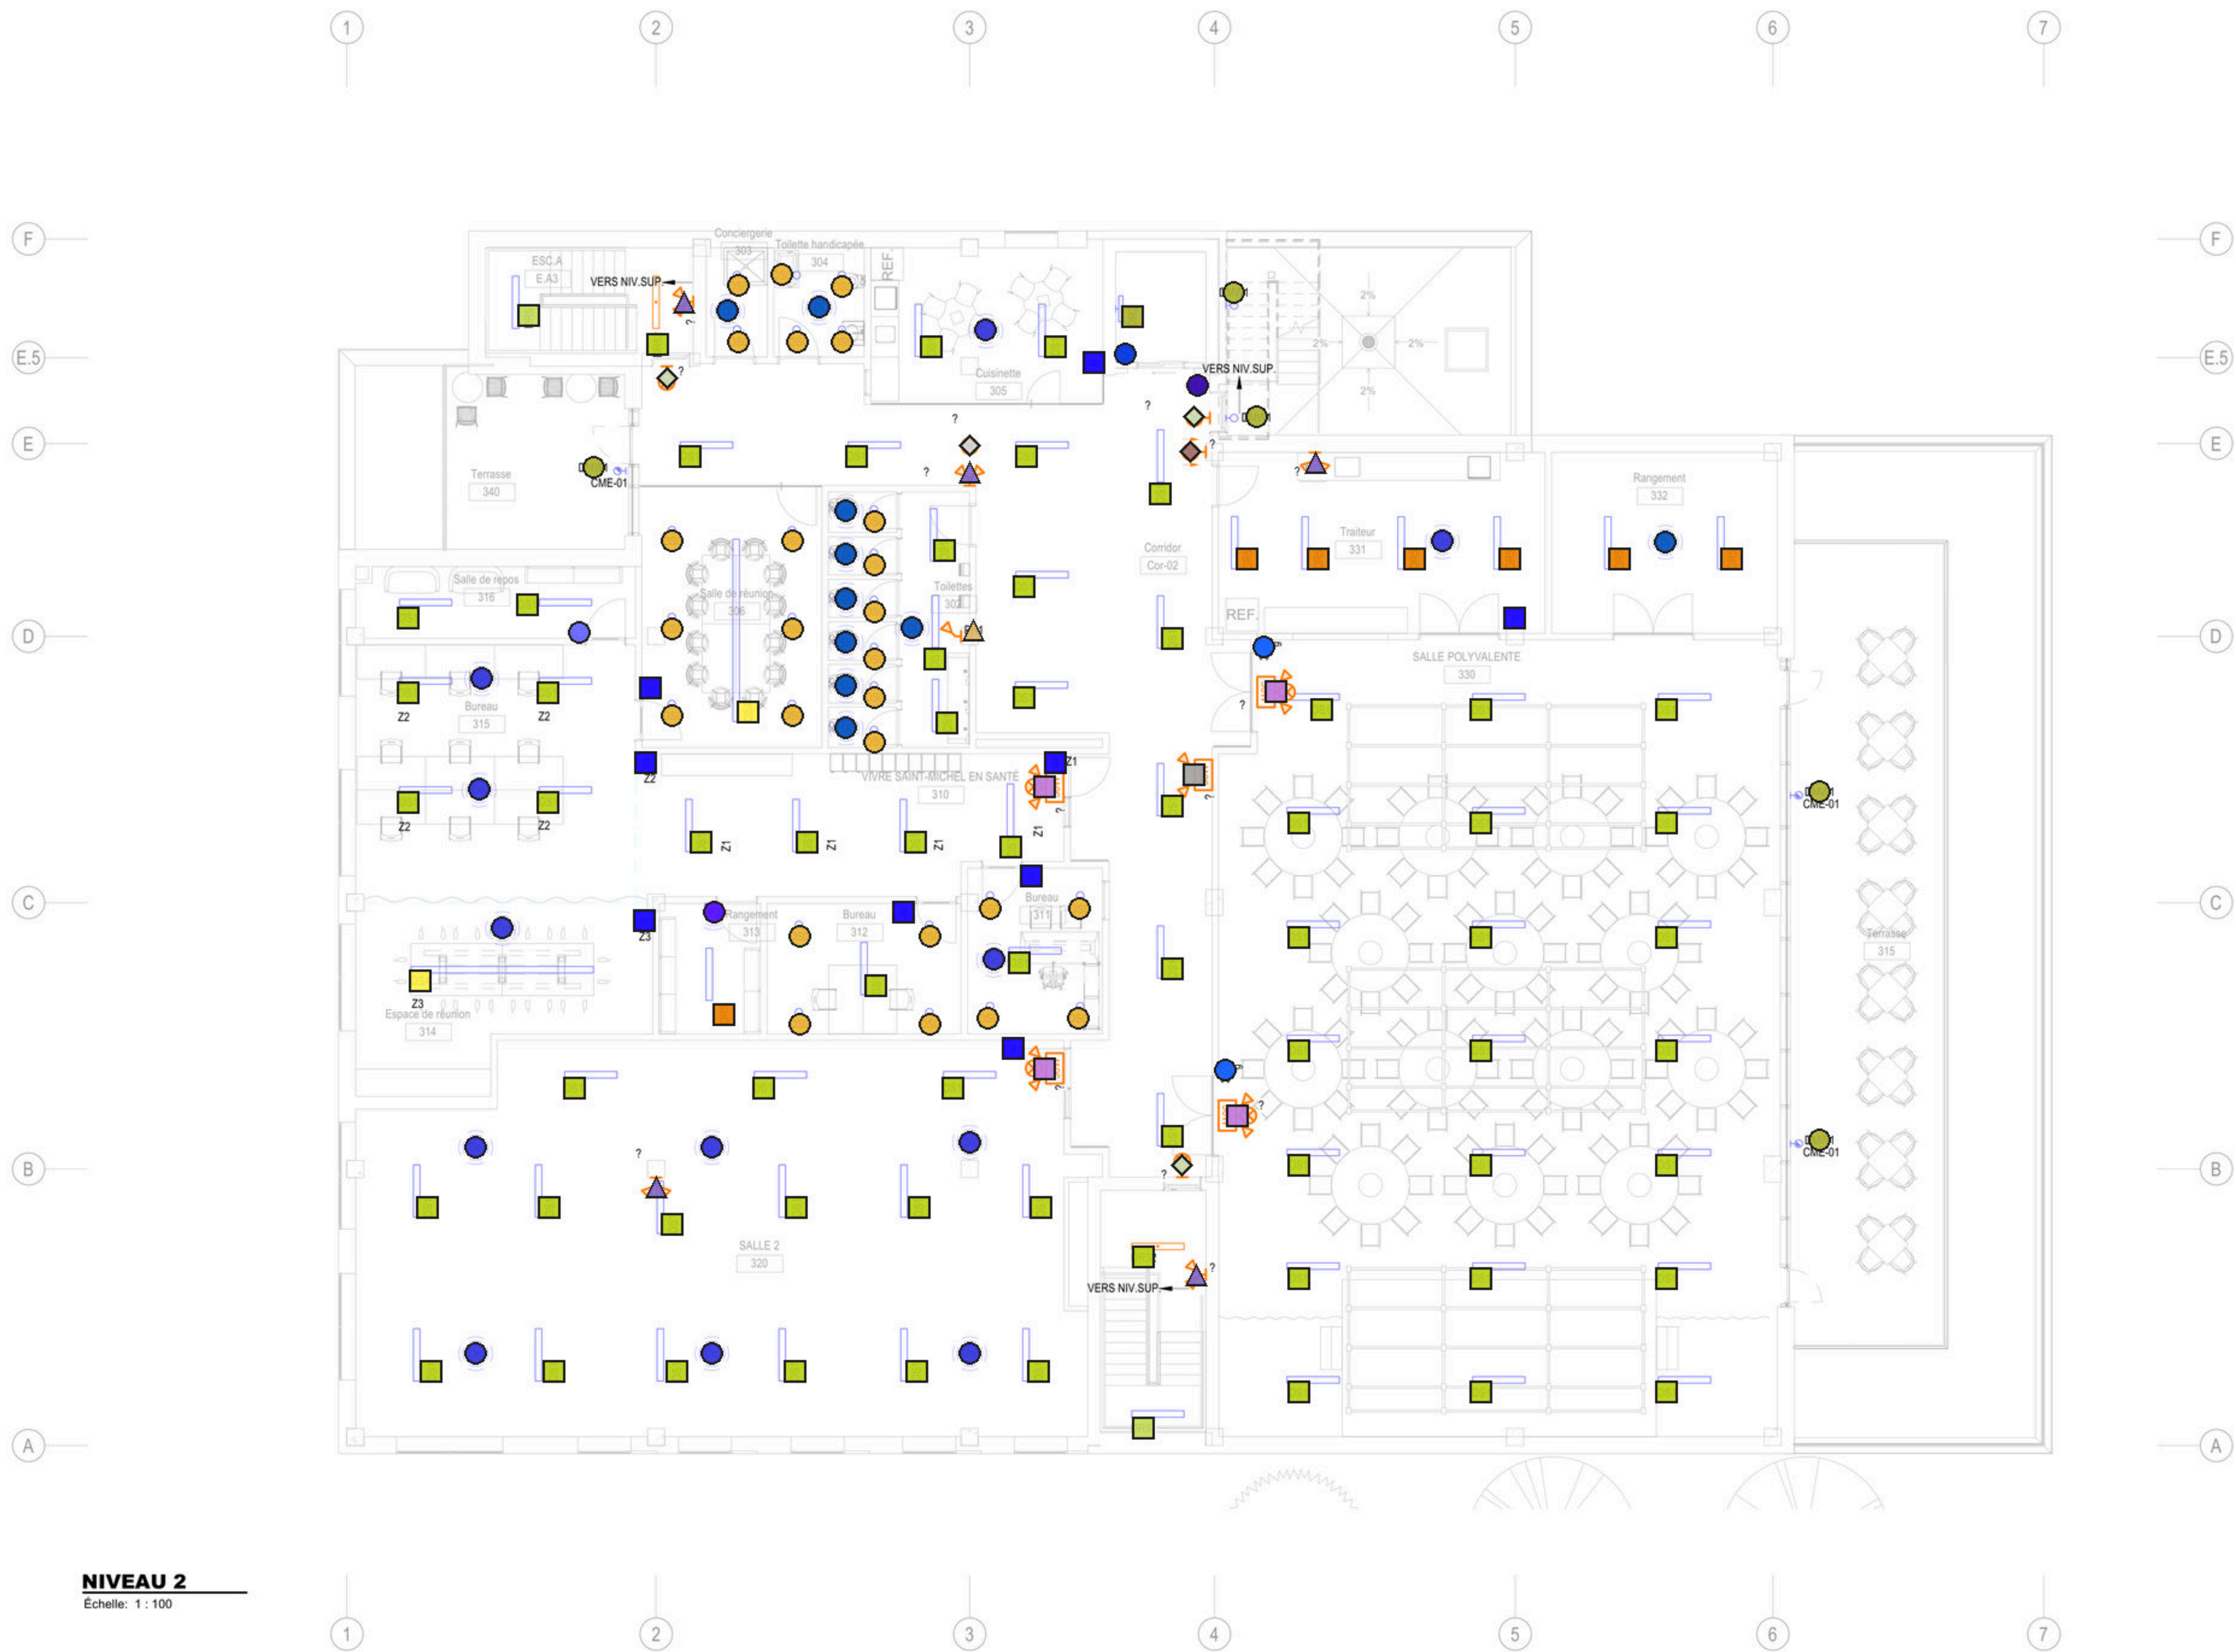

- Légende — E403 (161 marques)
- Accumulateur c/a 2 phares (1)
- Accumulateur c/a 2 phares + enseigne (4)
- Bouton-poussoir (B) (9)
- Détecteur infrarouge plafond (Di) (10)
- Détecteur inoccupation mural (Do) (1)
- Détecteur inoccupation plafond (Do) (12)
- Enseigne issue 1 face murale tout droit (3)
- Enseigne issue 1 face plafond tout droit (1)
- Enseigne issue 2 faces murale (1)
- Gradateur 120V (1)
- Gradateur 3 voies (2)
- Interrupteur c/a lampe témoin (1)
- Interrupteur unipolaire (1)
- Luminaire DMW1 (5)
- Luminaire DR2 (1)
- Luminaire DR5 (7)
- Luminaire DR51 (2)
- Luminaire DR52 service continu (2)
- Luminaire DS0 (26)
- Luminaire DS1 (63)
- Luminaire DS4 (2)
- Phare urgence double mural (5)
- Phare urgence simple mural (1)

1	SOUSSION	2026-08-17
A	PERMIS	2026-05-08
NO.	Émis pour	Date

TITRE DU PLAN:	
NIVEAU 2 - ÉCLAIRAGE	
PRÉPARÉ PAR:	SCEAU
M. BATISTA, ing.	
J. GILBERT, tech.	
DESSINÉ PAR:	
T. CANDU	
DATE:	PLAN:
AVRIL 2026	E403
DOSSIER:	
25-0810-QC	
DISCIPLINE:	
ÉLECTRICITÉ	

[illegible]


PRÉPARÉ PAR:	SCEAU
M. BATISTA, ing. J. GILBERT, tech.	 The seal is circular with a serrated outer edge. Inside the circle, the word "INGÉNIEUR" is written in an arc at the top, and "QUÉBEC" is written in an arc at the bottom. In the center, there is a shield with a fleur-de-lis on top, a scale of justice in the middle, and a gear at the bottom. Below the shield, the text "Membre de l'Ordre des Ingénieurs du Québec" is written in a smaller arc.
DESSINÉ PAR:	
T. CANDU	
DATE:	
AVRIL 2026	PLAN:
DOSSIER:	E404
25-0810-QC	
DISCIPLINE	
ÉLECTRICITÉ	



CE PLAN EST LA PROPRIÉTÉ DES PROFESSIONNELS CI-DESSOUS MENTIONNÉS. IL EST PRÊTÉ À CONDITION QU'IL NE SOIT PAS UTILISÉ À L'ENCONTRE DE LEUR INTÉRÊT NI REPRODUIT EN TOUT OU EN PARTIE ET QU'IL LEUR SOIT REMIS SUR DEMANDE.

AVANT DE PROCÉDER À L'INSTALLATION DES COMPOSANTES ET DES SYSTÈMES ELECTROMECANQUES, L'ENTREPRENEUR DOIT CONSULTER LES DERNIERS PLANS EMIS D'ARCHITECTURE. TOUTES LES MESURES DOIVENT ÊTRE PRISES À PARTIR DES DERNIERS PLANS D'ARCHITECTURE.

CE PROJET DOIT SERVIR À LA CONSTRUCTION QUE SI LA MENTION "POUR CONSTRUCTION" FIGURE DANS LA LISTE DES REVISIONS CI-DESSOUS ET QU'IL SOIT DÔMENT SIGNÉ PAR L'INGÉNIEUR.

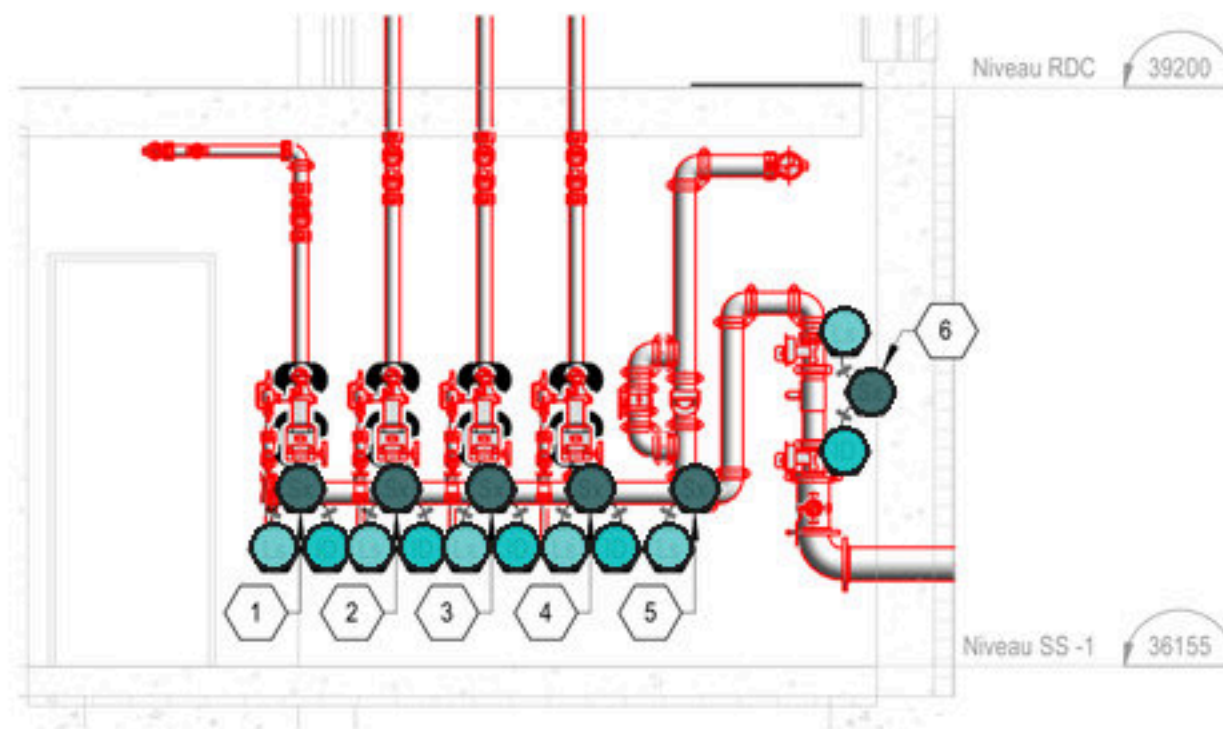


- LÉGENDE
- 1 VALVE ET INTERRUPTEUR DÉBIT SOUS-SOL
 - 2 VALVE ET INTERRUPTEUR DÉBIT NIVEAU RDC
 - 3 VALVE ET INTERRUPTEUR DÉBIT NIVEAU 1
 - 4 VALVE ET INTERRUPTEUR DÉBIT NIVEAU 2
 - 5 VALVE CONTOURNEMENT ESSAI DAR N.F.
 - 6 VALVE DAR GICLEURS N.O.

ENTRÉE D'EAU

Echelle: N.A.E.

Légende — E405 (90 marques)

- Avertisseur sonore/visuel (K) (1)
- Boîte de mesurage HQ (MHQ) (1)
- Détecteur de fumée (F) (1)
- Indicateur de débit (ID) (5)
- Interrupteur fin de course (Ls) (6)
- Klaxon alarme (K) (12)
- Module de supervision (Sx) (6)
- Panneau de dérivation (2)
- Poste manuel (M) (2)
- Prise 20A dans mobilier (2)
- Prise DDFT 20A (3)
- Prise DDFT intempéries (2)
- Prise duplex 20A (25)
- Prise duplex 20A à 1070mm (1)
- Raccord chauffe-eau (CE) (2)
- Raccord direct équipement (▲CC) (10)
- Raccord pompe (▼) — à classer (3)
- Sectionneur 600A (2)
- Sortie data dans mobilier (2)
- Transformateur (Xfo) (2)

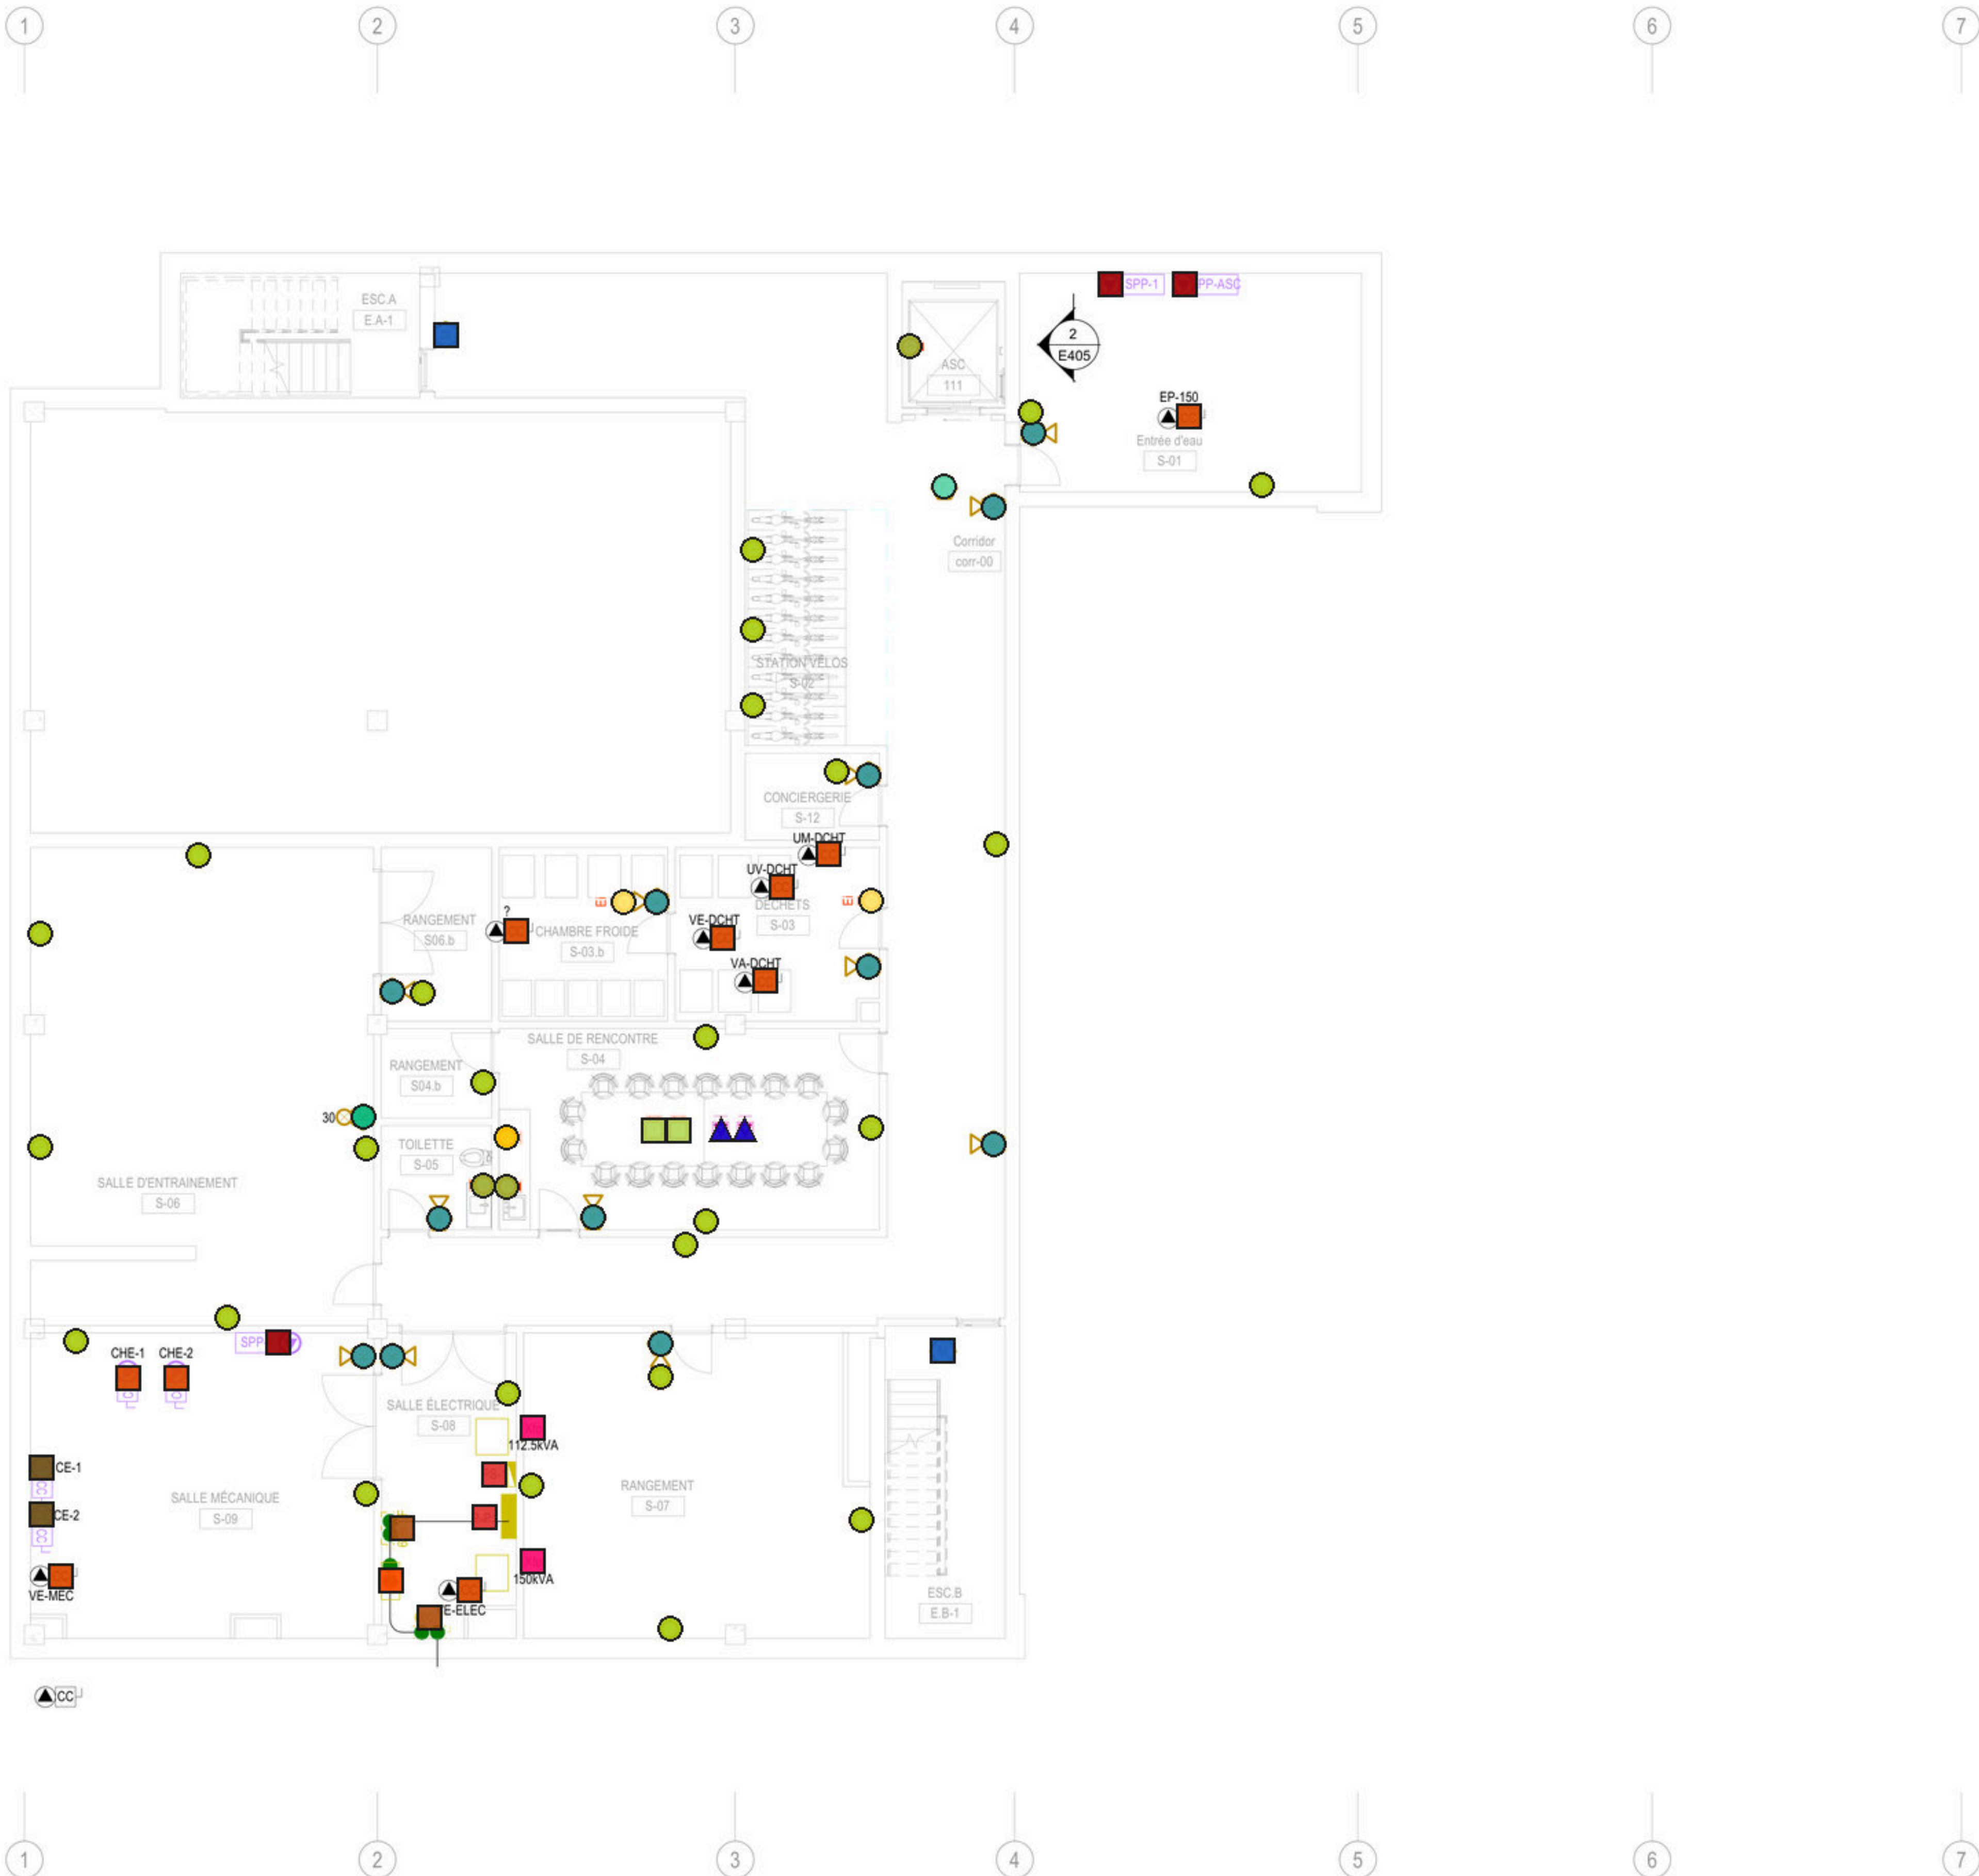

SOUS-SOL

Echelle: 1:100

ARTELIA

POINCARÉ

INGENIERIE

fabg

Architectes

akonovia

ELECTRIQUE


1	SOUSSION	2026-08-17
A	PERMIS	2026-05-08
NO.	Émis pour	Date

TITRE DU PLAN:	
SOUS-SOL - ALARME	
INCENDIE - PRISES ET	
SERVICES	
PRÉPARÉ PAR:	SCEAU
M. BATISTA, ing.	
DESSINÉ PAR:	
T. CANDU	
DATE:	
AVRIL 2026	PLAN:
DOSSIER:	E405
25-0810-QC	
DISCIPLINE	
ÉLECTRICITÉ	

CE PLAN EST LA PROPRIÉTÉ DES PROFESSIONNELS CI-DESSOUS
MENTIONNÉS. IL EST PRÊTÉ À CONDITION QU'IL NE SOIT PAS UTILISÉ À
L'ENCONTRE DE LEUR INTÉRÊT NI REPRODUIT EN TOUT OU EN PARTIE ET
QU'IL LEUR SOIT REMIS SUR DEMANDE.

AVANT DE PROCÉDER À L'INSTALLATION DES COMPOSANTES ET DES
SYSTÈMES ÉLECTROMÉCANIQUES, L'ENTREPRENEUR DOIT CONSULTER LES
DERNIERS PLANS ÉMIS D'ARCHITECTURE. TOUTES LES MESURES DOIVENT
ÊTRE PRISES À PARTIR DES DERNIERS PLANS D'ARCHITECTURE.

CE PROJET DOIT SERVIR À LA CONSTRUCTION QUE SI LA MENTION "POUR
CONSTRUCTION" FIGURE DANS LA LISTE DES RÉVISIONS
CI-DESSOUS ET QU'IL SOIT DÔMENT SIGNÉ PAR L'INGÉNIEUR.

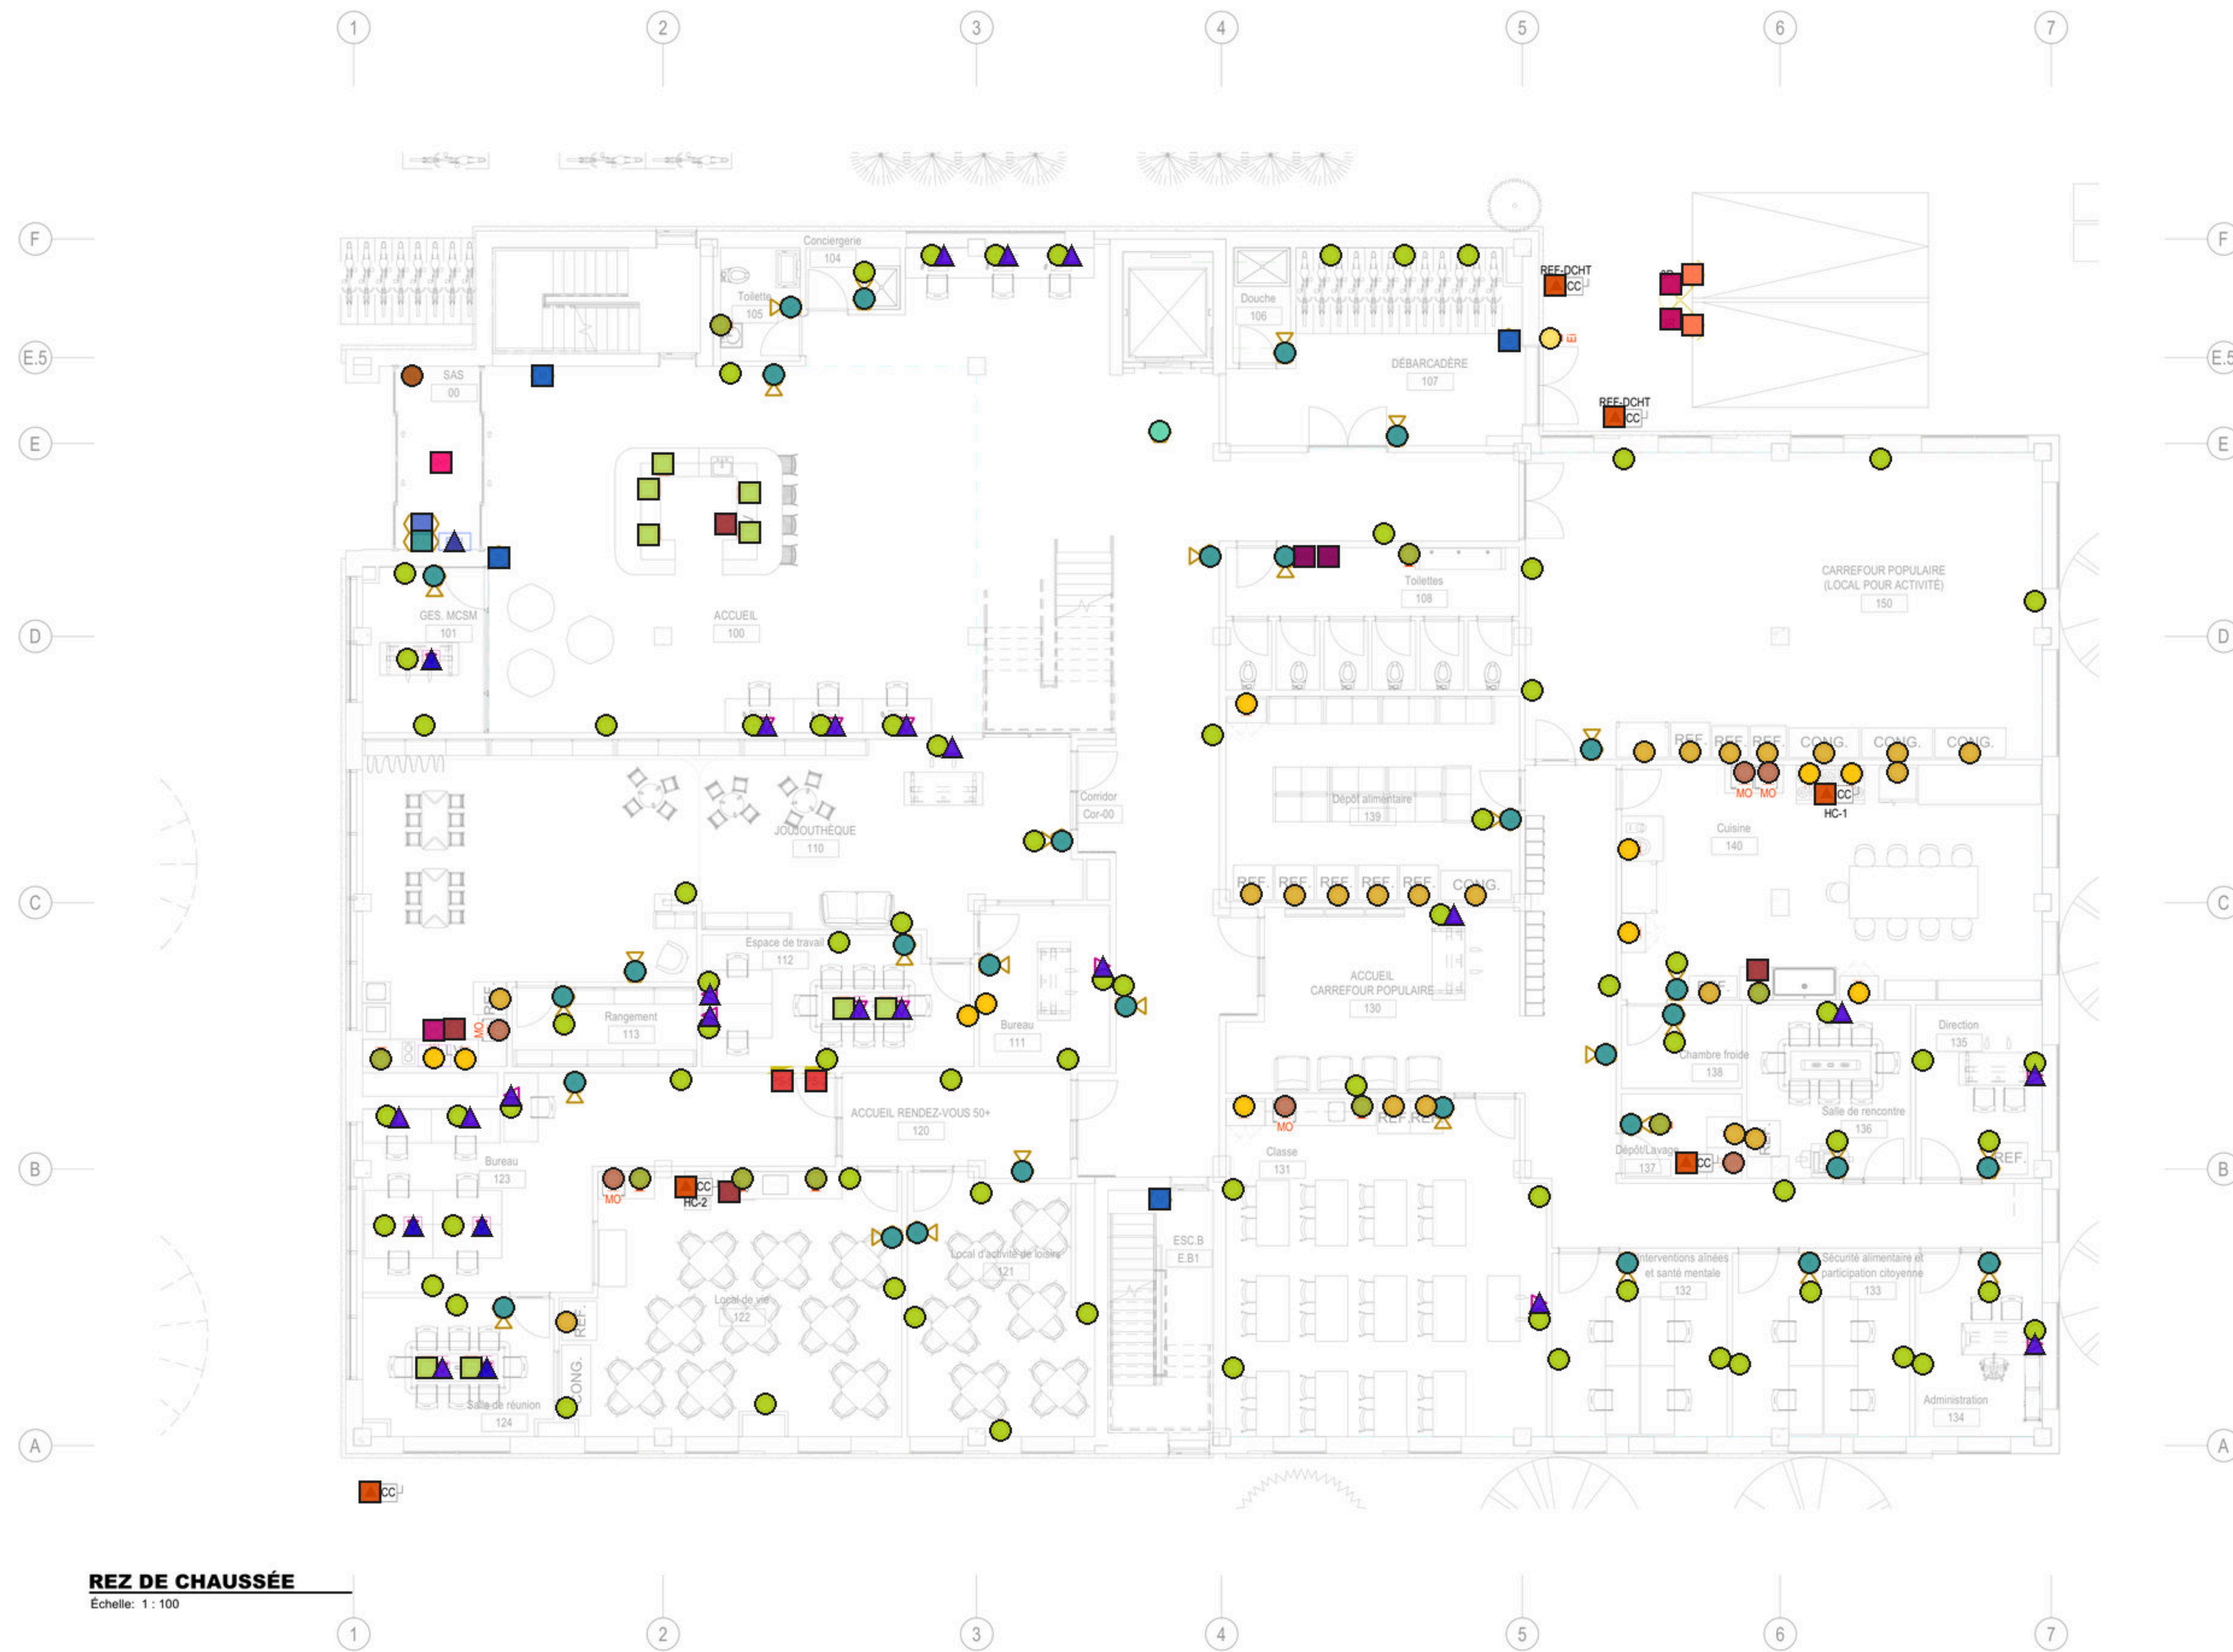

- Légende — E406 (218 marques)**
- Aéroconvecteur plafond (ACP) (1)
 - Borne de recharge VE (2)
 - Coupe-circuit NEMA 3R (CC) (2)
 - Détecteur de fumée (F) (1)
 - Klaxon alarme (K) (31)
 - Module de transmission (TRA) (1)
 - Panneau alarme incendie (PAI) (1)
 - Panneau de dérivation (2)
 - Poste manuel (M) (4)
 - ▲ Poste maître intercom (PMI) (1)
 - Prise 20A au plancher (3)
 - Prise 20A dans mobilier (9)
 - Prise 20A micro-onde (MO) (5)
 - Prise DDFT 20A (9)
 - Prise DDFT intempéries (1)
 - Prise cuisinière 50A (C) (3)
 - Prise duplex 15A (21)
 - Prise duplex 20A (73)
 - Prise duplex 20A à 1070mm (8)
 - Prise sècheuse 30A (S) (1)
 - Raccord direct équipement (▲CC) (6)
 - Raccord hotte (Ht) (1)
 - Raccord lave-vaisselle (LV) (4)
 - ▲ Sortie data (21)
 - ▲ Sortie data dans mobilier (4)
 - Sèche-mains (SM) (2)
 - Thermostat tension secteur (Ts) (1)



1	SOUSSION	2026-08-17
A	PERMIS	2026-05-08
NO.	Émis pour	Date


TITRE DU PLAN:
**REZ DE CHAUSSEE - ALARME
INCENDIE - PRISES ET
SERVICES**

PREPARE PAR: M. BATISTA, ing. J. GILBERT, tech.	SCEAU
DESINE PAR: T. CANDU	INGÉNIEUR Méthy Batista Soto Société Société QUÉBEC
DATE: AVRIL 2026	PLAN: E406
DOSSIER: 25-0810-QC	
DISCIPLINE: ÉLECTRICITÉ	

CE PLAN EST LA PROPRIÉTÉ DES PROFESSIONNELS CI-DESSOUS MENTIONNÉS. IL EST PRÊTÉ À CONDITION QU'IL NE SOIT PAS UTILISÉ À L'ENCONTRE DE LEUR INTÉRÊT NI REPRODUIT EN TOUT OU EN PARTIE ET QU'IL LEUR SOIT REMIS SUR DEMANDE.

AVANT DE PROCÉDER À L'INSTALLATION DES COMPOSANTES ET DES SYSTÈMES ELECTROMECANQUES, L'ENTREPRENEUR DOIT CONSULTER LES DERNIERS PLANS EMIS D'ARCHITECTURE. TOUTES LES MESURES DOIVENT ÊTRE PRISES À PARTIR DES DERNIERS PLANS D'ARCHITECTURE.

CE PROJET DOIT SERVIR À LA CONSTRUCTION QUE SI LA MENTION "POUR CONSTRUCTION" FIGURE DANS LA LISTE DES RÉVISIONS CI-DESSOUS ET QU'IL SOIT DÔMENT SIGNÉ PAR L'INGÉNIEUR.

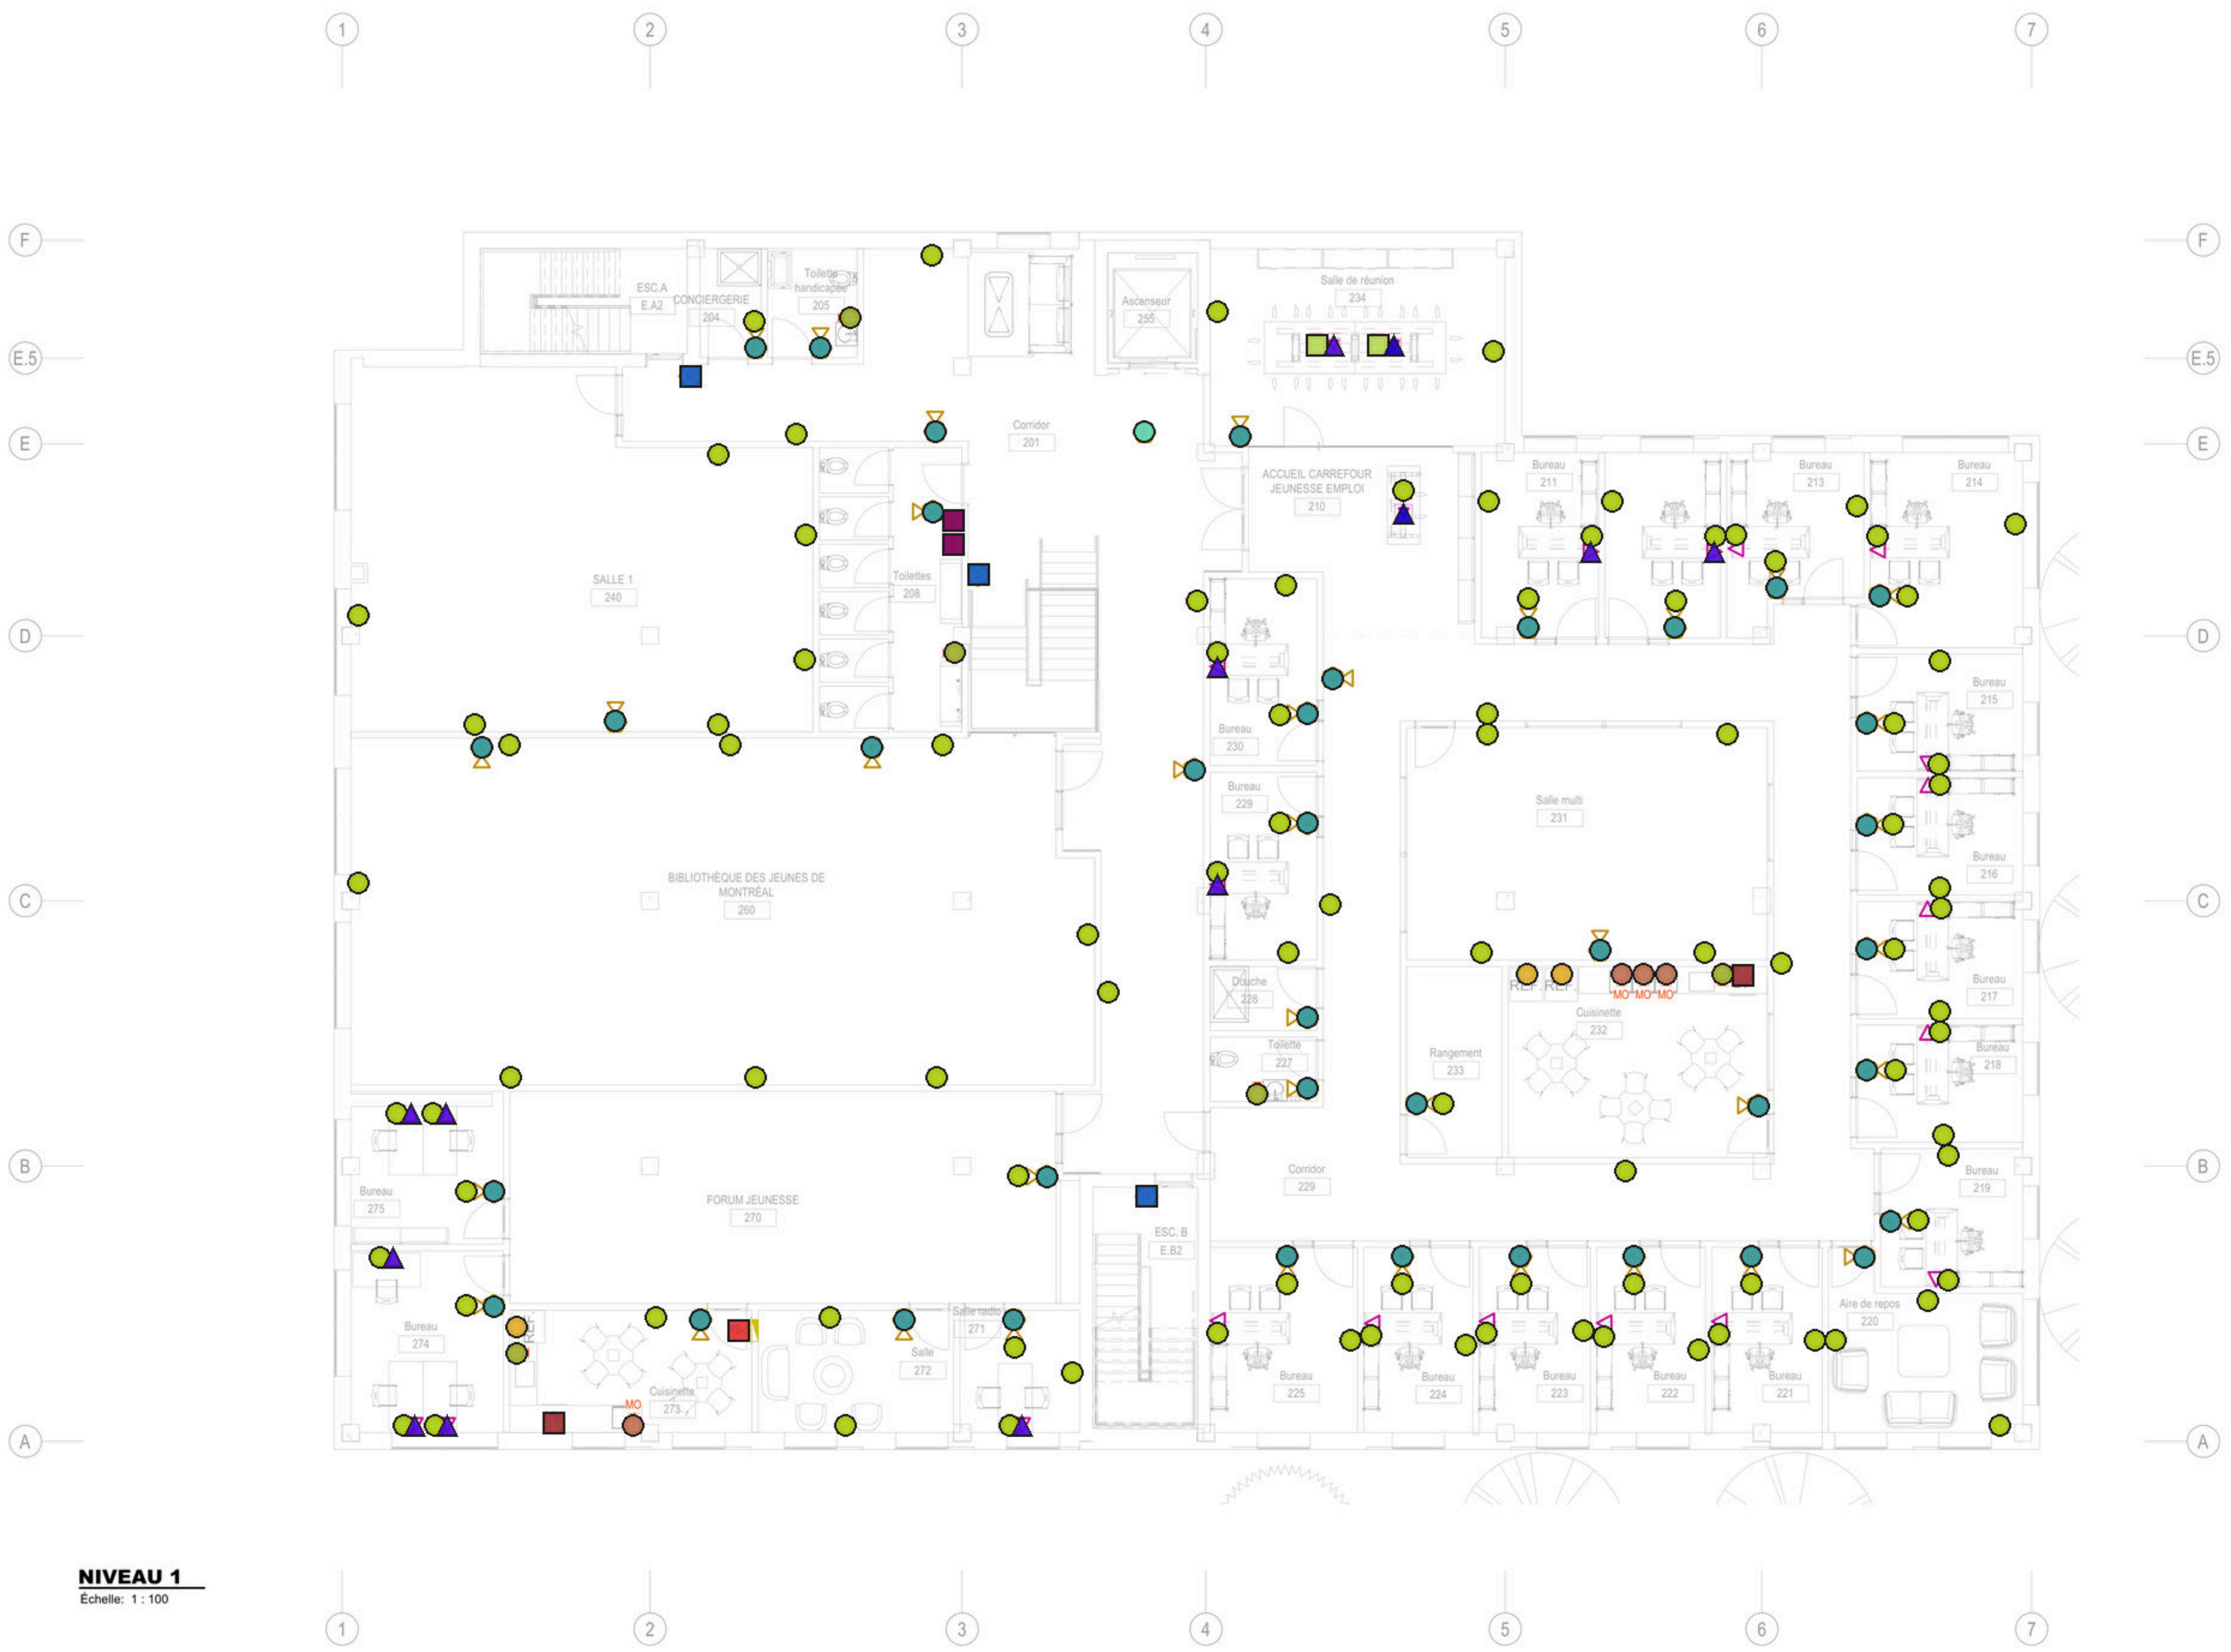

Légende — E407 (170 marques)

- Détecteur de fumée (F) (1)
- Klaxon alarme (K) (38)
- Panneau de dérivation (1)
- Poste manuel (M) (3)
- Prise 20A dans mobilier (2)
- Prise 20A micro-onde (MO) (4)
- Prise DDFT 20A (5)
- Prise duplex 15A (3)
- Prise duplex 20A (96)
- Raccord lave-vaisselle (LV) (2)
- ▲ Sortie data (11)
- ▲ Sortie data dans mobilier (2)
- Sèche-mains (SM) (2)

CIVIL



STRUCTURE



ARCHITECTURE



MÉCANIQUE / ÉLECTRIQUE



1	SOUSSION	2026-08-17
A	PERMIS	2026-05-08
NO.	Émis pour	Date

TITRE DU PLAN:
NIVEAU 1 - ALARME
INCENDIE - PRISES ET
SERVICES

PRÉPARÉ PAR:

M. BATISTA, ing.
J. GILBERT, tech.

DESSINÉ PAR:

T. CANDU

DATE:

AVRIL 2026

DOSSIER:

25-0810-QC

DISCIPLINE

ÉLECTRICITÉ

SCEAU



PLAN:


E407

NIVEAU 1
Echelle: 1 : 100

CE PLAN EST LA PROPRIÉTÉ DES PROFESSIONNELS CI-DESSOUS MENTIONNÉS. IL EST PRÊTÉ À CONDITION QU'IL NE SOIT PAS UTILISÉ À L'ENCONTRE DE LEUR INTÉRÊT NI REPRODUIT EN TOUT OU EN PARTIE ET QU'IL LEUR SOIT REMIS SUR DEMANDE.

AVANT DE PROCÉDER À L'INSTALLATION DES COMPOSANTES ET DES SYSTÈMES ÉLECTROMÉCANIQUES, L'ENTREPRENEUR DOIT CONSULTER LES DERNIERS PLANS ÉMIS D'ARCHITECTURE. TOUTES LES MESURES DOIVENT ÊTRE PRISES À PARTIR DES DERNIERS PLANS D'ARCHITECTURE.

CE PROJET DOIT SERVIR À LA CONSTRUCTION QUE SI LA MENTION "POUR CONSTRUCTION" FIGURE DANS LA LISTE DES RÉVISIONS CI-DESSOUS ET QU'IL SOIT DÔMENT SIGNÉ PAR L'INGÉNIEUR.

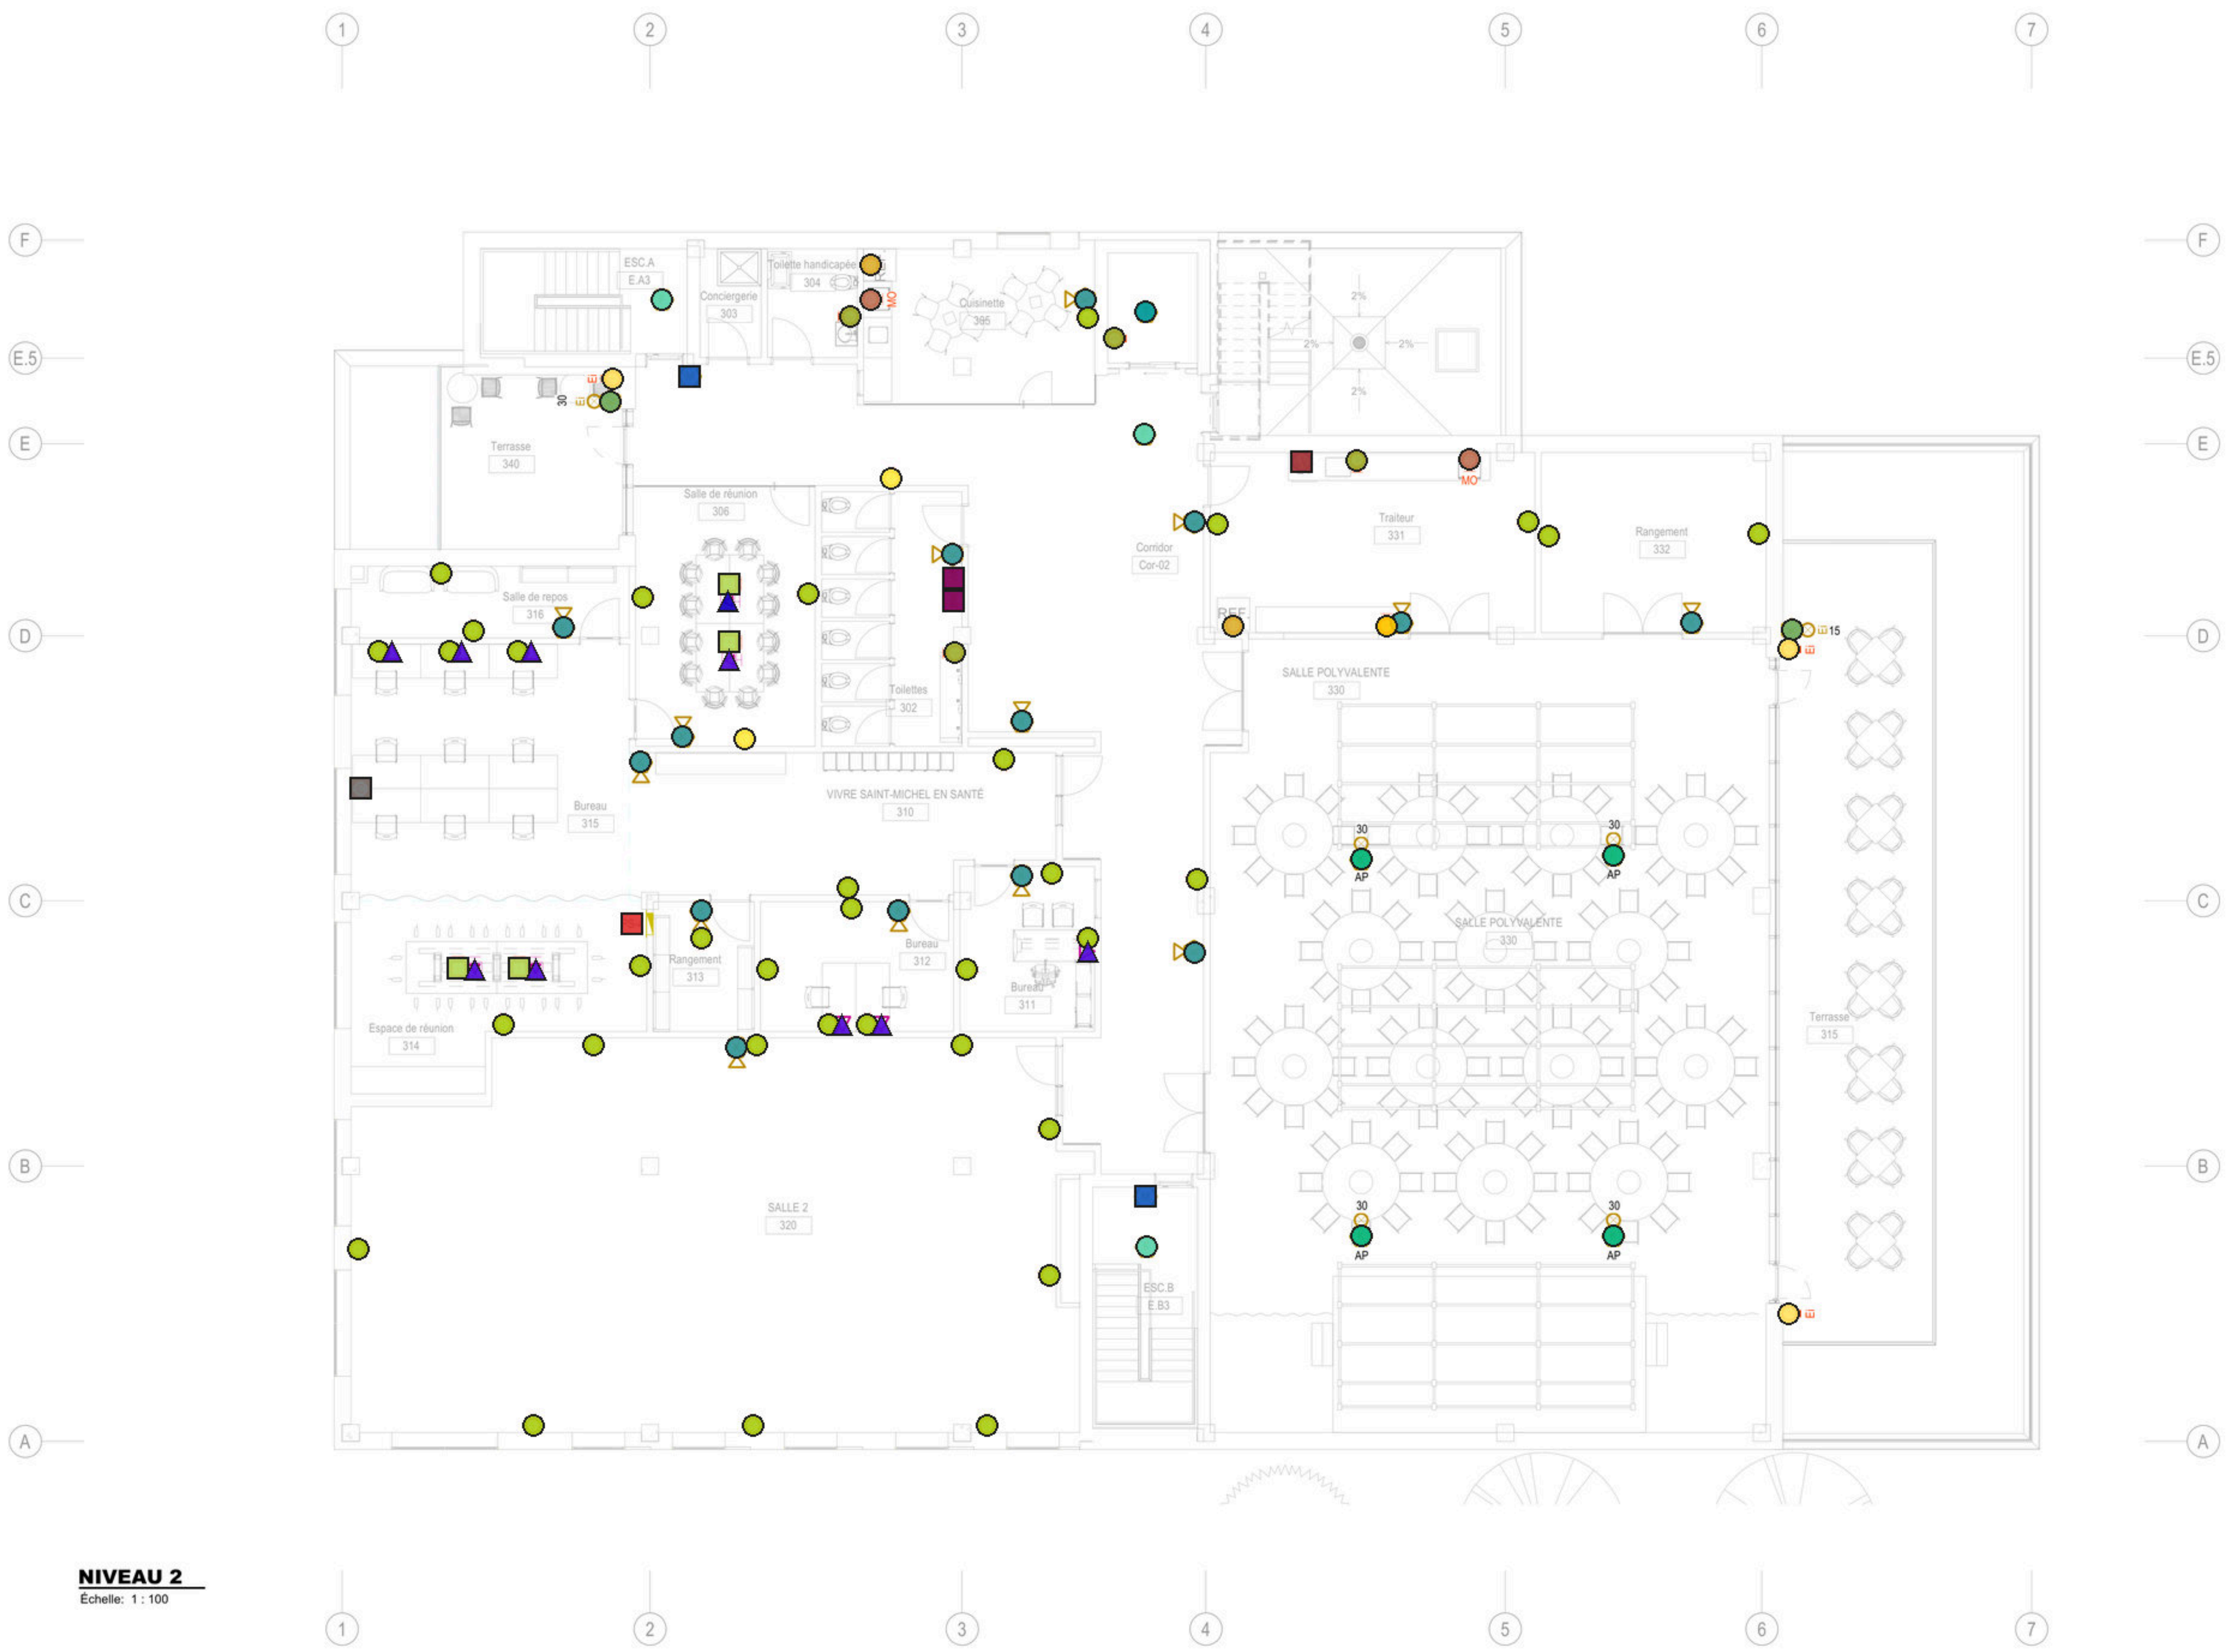

- Légende — E408 (93 marques)
- Avertisseur sonore/visuel (K) (4)
- Avertisseur sonore/visuel intempéries (2)
- Carré plein « C » — à classer (1)
- Détecteur de fumée (F) (3)
- Détecteur thermique (T) (1)
- Klaxon alarme (K) (14)
- Panneau de dérivation (1)
- Poste manuel (M) (2)
- Prise 20A dans mobilier (4)
- Prise 20A micro-onde (MO) (2)
- Prise DDFT 20A (4)
- Prise DDFT intempéries (3)
- Prise duplex 15A (2)
- Prise duplex 20A (34)
- Prise duplex 20A à 1070mm (1)
- Prise — cercle vide à classer (2)
- Raccord lave-vaisselle (LV) (1)
- Sortie data (9)
- Sortie data dans mobilier (1)
- Sèche-mains (SM) (2)



1	SOUSSION	2026-08-17
A	PERMIS	2026-05-08
NO.	Émis pour	Date

TITRE DU PLAN:

NIVEAU 2 - ALARME

INCENDIE - PRISES ET

SERVICES

PRÉPARE PAR:

M. BATISTA, ing.

J. GILBERT, tech.

DESSINÉ PAR:

T. CANDU

DATE:

AVRIL 2026

DOSSIER:

25-0810-QC

DISCIPLINE:

ÉLECTRICITÉ

SCEAU



PLAN:

E408

ARTELIA

STRUCTURE

POINCARÉ
INGÉNIERIE

[illegible]

PRÉPARÉ PAR: M. BATISTA, ing. J. GILBERT, tech.	SCEAU 
Dessinée PAR: T. CANDU DATE: AVRIL 2026 DOSSIER: 25-0810-QC	PLAN: E409
DISCIPLINE ÉLECTRICITÉ	



PANNEAU : PS-1													
TENSION : 120/208V, 3Ø, 4F						BARRE OMNIBUS : 600A							
LOCALISATION : S-08 SALLE ELECTRIQUE						DISJ. MAITRE : NA							
OPTION :						MONTAGE : SURFACE							
BOITER :						ENTREE CABLE :							
FABRICANT : SQUARE D # NQ484L6CMH68-NC68V1													
ABV	DESCRIPTION	DISJ.	#	A	B	C	#	DISJ.	DESCRIPTION	ABV			
E	ASCENSEUR 111	15 A	1	34 / 92			2	15 A	PECD-1	Q			
Q	EP-150 (S-03, S-01)	15 A	3		86 / 114		4	15 A	S-03/03b	E			
E	MINUTERIE (ECL-EXT)	15 A	5			35 / 114	6	15 A	ESCALIER A	E			
EV	S-03/03b/04/05/06/07	15 A	7	144 / 166			8	15 A	VE-MEC (S-09)	Q			
Q	VE-ELEC (S-08)	15 A	9		166 / 218		10	15 A	VA-DCHT (S-01)	Q			
E	ESCALIER B	15 A	11			152 / 174	12	15 A	ÉVIER ELECTR	Q			
E	CORRIDOR-00	15 A	13	228 / 260			14	15 A	ESCALIER B	EV			
EV	ESCALIER A	15 A	15		242 / 360		16	20 A	S-01	P			
P	S-03/03b	20 A	17			240 / 276	18	15 A	CORRIDOR-00	EV			
P	S-02	20 A	19	360 / 750			20	15 A	UV-DCHT (S-01)	Q			
E	S-01/04/04b/05/06/06b/07/08/12	15 A	21		618 / 720		22	20 A	S-06	P			
Q	VC (SS)	20 A	23			408 / 960	24	20 A	110 / 111	P			
P	S-04	20 A	25	840 / 840			26	20 A	S-07/08/09	P			
P	S-05	20 A	27		120 / 120		28	20 A	COMPTOIR (S-04)	Q			
P	121/122	20 A	29			960 / 2000	30	40 A	SPP-ASC, 2HP	Q			
P	CTRASC (S-01)	20 A	31	120 / 19952			32						
			33		0 / 19958		34	125 A	PS-2	QV			
			35			11323 / 19965	36						
QV	PS-4 125 A		37	11207 / 20334			38						
			39		11267 / 20450		40	200 A	PS-3	QV			
P	S-12	20 A	41			120 / 20476	42						
P	ASCENSEUR	20 A	43	120 / 1400			44						
			45		0 / 1400		46	20 A	REF-DCHT (EXT)	Q			
P	COMPTOR (S-04)	20 A	47			120 / 1400	48						
			49				50						
			51				52						
			53				54						
			55				56						
			57				58						
			59				60						
			61				62						
			63				64						
			65				66						
			67				68						
			69				70						
			71				72						
CHARGES RACCORDEES PAR PHASE: 56847 55839 58723													
ABRÉVIATIONS (ABV) A : DISJONCTEUR ANTI-ARC P : PRISE DE COURANT C : CHAUFFAGE R : ROUGE (A) TOTAL DES CHARGES RACCORDEES 171408 WATTS D : DISJONCTEUR D.D.F.T. Q : EQUIPEMENT E : ECLAIRAGE V : VERROUILLAGE MECANIQUE													

PANNEAU : PS-4

TENSION : 120/208V, 3Ø, 4F				BARRE OMNIBUS : 125A							
LOCALISATION :				DISJ. MAÎTRE :							
OPTION :				MONTAGE : ENCASTRE							
BOÎTIER :				ENTRÉE CÂBLE :							
FABRICANT : SQUARE D # NQ484L6CMH68-NC68V1											

ABV	DESCRIPTION	DISJ.	#	A	B	C	#	DISJ.	DESCRIPTION	ABV	
Q	ÉVIER ÉLECTRIQUE (302, 304)	15 A	1	100 / 198			2	15 A	302/310/320/330/331	EV	
P	302	20 A	3		120 / 240		4	20 A	331	P	
EV	CORRIDOR 3 INV.	15 A	5			144 / 240	6	20 A	EXT (315)	P	
E	CORRIDOR 3 INV.	15 A	7	387 / 600			8	15 A	COLONNETTE (310)	P	
P	331/332	20 A	9		480 / 620		10	15 A	REFRIGERATEUR (305)	P	
E	302-309/311/312/313	15 A	11			540 / 720	12	15 A	VC INVEU 2	P	
P	320	20 A	13	720 / 1110			14	15 A	VC INVEU 2	P	
P	310	20 A	15		840 / 1000		16	20 A	MO (305)	P	
P	310/312/313	20 A	17			840 / 946	18	15 A	330/331/332/EXT	E	
P	VC (INVEU 2)	20 A	19	1181 / 500			20	15 A	SÈCHE-MAIN (302)	Q	
P	MO (331)	20 A	21		1000 / 500		22	15 A	SÈCHE-MAIN (302)	E	
P	306	20 A	23			960 / 970	24	15 A	314/315/316/320	E	
Q	SÈCHE-MAIN (302)	15 A	25	500 / 240			26	15 A	EXT TOIT	P	
P	REFRIGERATEUR (331)	15 A	27		500 / 120		28	15 A	LV (331)	P	
P	REFRIGERATEUR (331)	15 A	29			120 / 120	30	20 A	ASCENSEUR	P	
P	304	20 A	31	120 / 5667			32				
P	340	20 A	33		120 / 5667		34	60 A	UAT-2	Q	
			35		0 / 5667		36				
			37				38				
			39				40				
			41				42				
			43				44				
			45				46				
			47				48				
			49				50				
			51				52				
			53				54				
			55				56				
			57				58				
			59				60				
			61				62				
			63				64				
			65				66				
			67				68				
			69				70				
			71				72				
CHARGES RACCORDEES PAR PHASE:				11323	11207	11267					
ABRÉVIATIONS (ABV)				P : PRISE DE COURANT				TOTAL DES CHARGES RACCORDEES 33796 WATTS			
				R : ROUGE (A)							
				Q : EQUIPEMENT							
				V : VERROUILLAGE MECANIQUE							

PANNEAU : PS-2

TENSION : 120/208V, 3Ø, 4F	BARRE OMNIBUS : 125A
LOCALISATION : 123 (BUREAU)	DISJ. MAÎTRE : N/A
OPTION : MONTAGE : ENCASTRE	MONTAGE : ENCASTRE
BOÎTIER : NEMA 2	ENTRÉE CÂBLE : N/A
FABRICANT : SQUARE D # NQ484L6C-MH68-NC68V1	

ABV	DESCRIPTION	DISJ.	#	A	B	C	#	DISJ.	DESCRIPTION	ABV
Q	ÉVIER ÉLECTRIQUE	15 A	1	50 / 100			2	15 A	VE-SECH	Q
Q	ÉVIER ÉLECTRIQUE	15 A	3		50 / 120		4	20 A	108	P
E		100 / 15 A	5			100 / 120	6	20 A	122 (CONGÉLO)	P
P		105, 104	7	240 / 410			8	15 A	101/CORRIDOR RDC	E
EV	SAS/100 CORRIDOR	15 A	9		254 / 458		10	15 A	101/107/108/110/120/122/130/140...	EV
P		100 / 20 A	11			360 / 500	12	15 A	LAVEUSE (137)	P
E		110/111/112/113	13	584 / 720			14	20 A	150	P
P		100 / 20 A	15		600 / 832		16	15 A	120/122/121/123/124	E
P	136/135 CORRIDOR	20 A	17			720 / 835	18	15 A	104-108/137/138/140/150	E
Q	P (123)	20 A	19		960 / 1000		20	15 A	110 (MIO)	P
P	VC (RDC)	25	21		1334 / 120		22	15 A	COMPTOR (122)	P
Q	130/131/132	15 A	23			960 / 1060	24	15 A	130-136/139	E
P	VC (RDC)	25	25	1078 / 500			26	15 A	SECHE-MAIN (108)	Q
Q		150 / 20 A	27		240 / 500		28			Q
Q	HOÏTE CUISINE (137)	15 A	29			3000 / 500	30			Q
P		137 / 15 A	31	120 / 500			32	15 A	SÉCHE-MAIN (108)	Q
Q			33		2000 / 360		34	20 A	107	P
Q	SÉCHEUSE	30 A	35			2000 / 120	36	20 A	EXTÉRIEUR	P
Q			37	4000 / 240			38	20 A	110 (COMPTOR)	P
Q	LV (100)	50 A	39		4000 / 840		40	20 A	123	P
P	COMPTOR (122)	15 A	41			240 / 360	42	20 A	124	P
P		100 / 20 A	43	360 / 840			44	15 A	100/101	P
Q			45		0 / 4000		46	50 A	LV (122)	Q
Q	132/133/134	20 A	47			840 / 4000	48			Q
P	LV (110)	50 A	49	4000 / 250			50			
Q			51		4000 / 250		52	15 A	HC-2 (RDC)	Q
Q	LV (150)	50 A	53			4000 / 250	54			
			55	4000 / 0			56			
			57				58			
			59				60			
			61				62			
			63				64			
			65				66			
			67				68			
			69				70			
			71				72			

CHARGES RACCORDEES PAR PHASE				19952	19958	19965
ABSEVATIONS				P : PRISE DE COURANT		
(ABV)				R : ROUGE (IN)		
				C : CHAUFFAGE		
				Q : EQUIPEMENT		
				V : VERROUILLAGE MECANIQUE		
				D : DISJONCTEUR ANTI-ARC		
				E : ECLARAGE		
				TOTAL DES CHARGES RACCORDEES		
				58875		
				WATTS		