

RC-PDNO-600(600)

0

Local: SALLE ELECTRIQUE 109

Alimenté: HYDRO-QUEBEC

Niveau: NIVEAU 1

Tension: 347/600V

Phases: 3

Fils: 4

Courant Rupture: 220A

Type barre: CUIVRE

Barre: 600 A

Disjoncteur Main: N/A

Note	Description	Disj.	Poles	C	A	B	C	Poles	Description	Note						
	ECLAIRAGE STATIONNEMENT	15A	1	1	164 VA	4000 VA			CHAUFFAGE 101 / 102							
	CHAUFFAGE 103 / 104 - ENTRÉE	15A	1	3		3000 VA	8000 VA	4	1	SE-01 / SE-02						
	CHAUFFAGE 105 / 106 / 109 / 110 - ENTRÉE GARAGE	15A	1	5		4000 VA	10000 VA			CHAUFFAGE GARAGE ZAMBONI						
	CHAUFFAGE VESTIAIRE	15A	1	7	4000 VA	10000 VA		8	1	SE-07						
	CHAUFFAGE SALLE MECANIQUE	15A	1	9		4000 VA	8000 VA	10	1	SE-03 / SE-04						
				11				12								
				13	20000 VA	96000 VA		14	3	SYSTEME RÉGULATION DE LA GLACE						
				15		26720 VA	96000 VA	16								
				17			27374 VA	12000 VA	18							
	RC-TRNO-600	90A	3	15				20	3	60A						
				19	12000 VA	12000 VA		22		CE-01						
				21		12000 VA	12000 VA	22								
	CE-02	60A	3	23		12000 VA	12000 VA	24								
				25	8333 VA	12000 VA		26	3	60A						
				27		8333 VA	12000 VA	28		CE-03						
	SE-05	50A	3	29		8333 VA	10000 VA	30								
				31		10000 VA		32	3	50A						
				33		10000 VA		34		SE-06						
				35				36								
				37				38								
				39				40								
				41				42								
Total Charge:				195250 VA		197728 VA		198074 VA								
Total Courant :				563 A		571 A		568 A								

RC-PSNO-200(200)

Local: SALLE ELECTRIQUE 109
Alimenté: RC-TRNO-600
Niveau: NIVEAU 1

Tension: 120/208V
Phases: 3
Fils: 4



Type barre: CUIVRE
Barre: 400 A
Disjoncteur Main: N/A

Courant Rupture: 150A

Note	Description	Disj.	Poles	C	A	B	C	Poles	Description	Note	
	ECLAIRAGE 109 / 110	15A	1	1	105 VA	167 VA		2	ECLAIRAGE 101 / 102 / 103		
	ECLAIRAGE SALLE MECANIQUE	15A	1	3		132 VA	204 VA	4	ECLAIRAGE GARAGE		
	ECLAIRAGE SALLE MECANIQUE	15A	1	5			132 VA	170 VA	6	ECLAIRAGE EXTÉRIEUR	
	ECLAIRAGE ENTRÉE ET TOILETTES	15A	1	7	289 VA	411 VA		8	ECLAIRAGE PATINOIRE		
	ECLAIRAGE GARAGE	15A	1	9		307 VA	500 VA	10	PRISE FONTAINE RÉFRIGÉRÉE		
	ECLAIRAGE PATINOIRE	15A	1	11			307 VA	500 VA	12		
	ECLAIRAGE PATINOIRE	15A	1	13	764 VA			14			
	ECLAIRAGE PATINOIRE	15A	1	15				16	ECLAIRAGE PATINOIRE		
	PROJECTEURS	15A	1	17		680 VA	917 VA	18	ECLAIRAGE PATINOIRE		
	PRISE PORTE DE GARAGE	15A	1	19	1000 VA	180 VA		20	PRISE ENTRÉE D'EAU 110		
	ECLAIRAGE VESTIAIRE	15A	1	21		800 VA	1176 VA	22	DEV-01		
	VE-03 / VE-04	15A	1	23		1872 VA	180 VA	24	PRISES T1		
	ECH-01	15A	2	25	500 VA	900 VA		26	VC-01		
	PRISE ENTRETIEN GARAGE	20A	1	29		500 VA	500 VA	30			
	VE-01	15A	2	31	812 VA	2058 VA		32	COND-01		
	PRISES VESTIAIRE	15A	1	33		812 VA	536 VA	34	VE-02		
	PRISE AQUISAGE DE PATIN	15A	1	35		360 VA	936 VA	36			
	PRISE SALLE ELECTRIQUE 109	15A	1	37	180 VA	360 VA		38	PRISES T1		
	PRISES GARAGE 108	15A	1	39		180 VA	180 VA	40	PRISE CONCIERGERIE		
	PRISES ENTRETIEN VESTIAIRE	20A	1	43	360 VA	540 VA		44	PRISES SALLE MECANIQUE 111		
	PRISES T1	15A	1	45		360 VA	540 VA	46	PRISES GARAGE 108		
	SÈCHE-MAINS 106	15A	1	47		900 VA	82 VA	48	ECLAIRAGE DE SECOURS		
	SÈCHE-MAINS 104	15A	1	49	800 VA	300 VA		50	PRCA-01		
	PRISES EXTÉRIEURE	15A	1	51		540 VA	800 VA	52	SÈCHE-MAINS 105		
				53		10371 VA	0 VA	54	RÉGLATION		
	BOTIER CABLOCK	200A	3	55	10371 VA	0 VA		56	RÉGLATION		
		15A	1	57	10371 VA	0 VA		58	VA-02		
		15A	2	59		348 VA		60			
		15A	2	63		348 VA		64	ECLAIRAGE MARQUISE		
		15A	2	65		348 VA		66			
				67		348 VA		68			
				69				70			
				71				72			
Total Charge:				25580 VA		26720 VA		27374 VA			
Total Courant :				215 A		224 A		230 A			


Notes:
1 - DISJONCTEUR DE COULEUR ROUGE ET CADENASSABLE

Total du panneau
Charge totale raccordée : 79688 VA
Courant total raccordé : 321 A

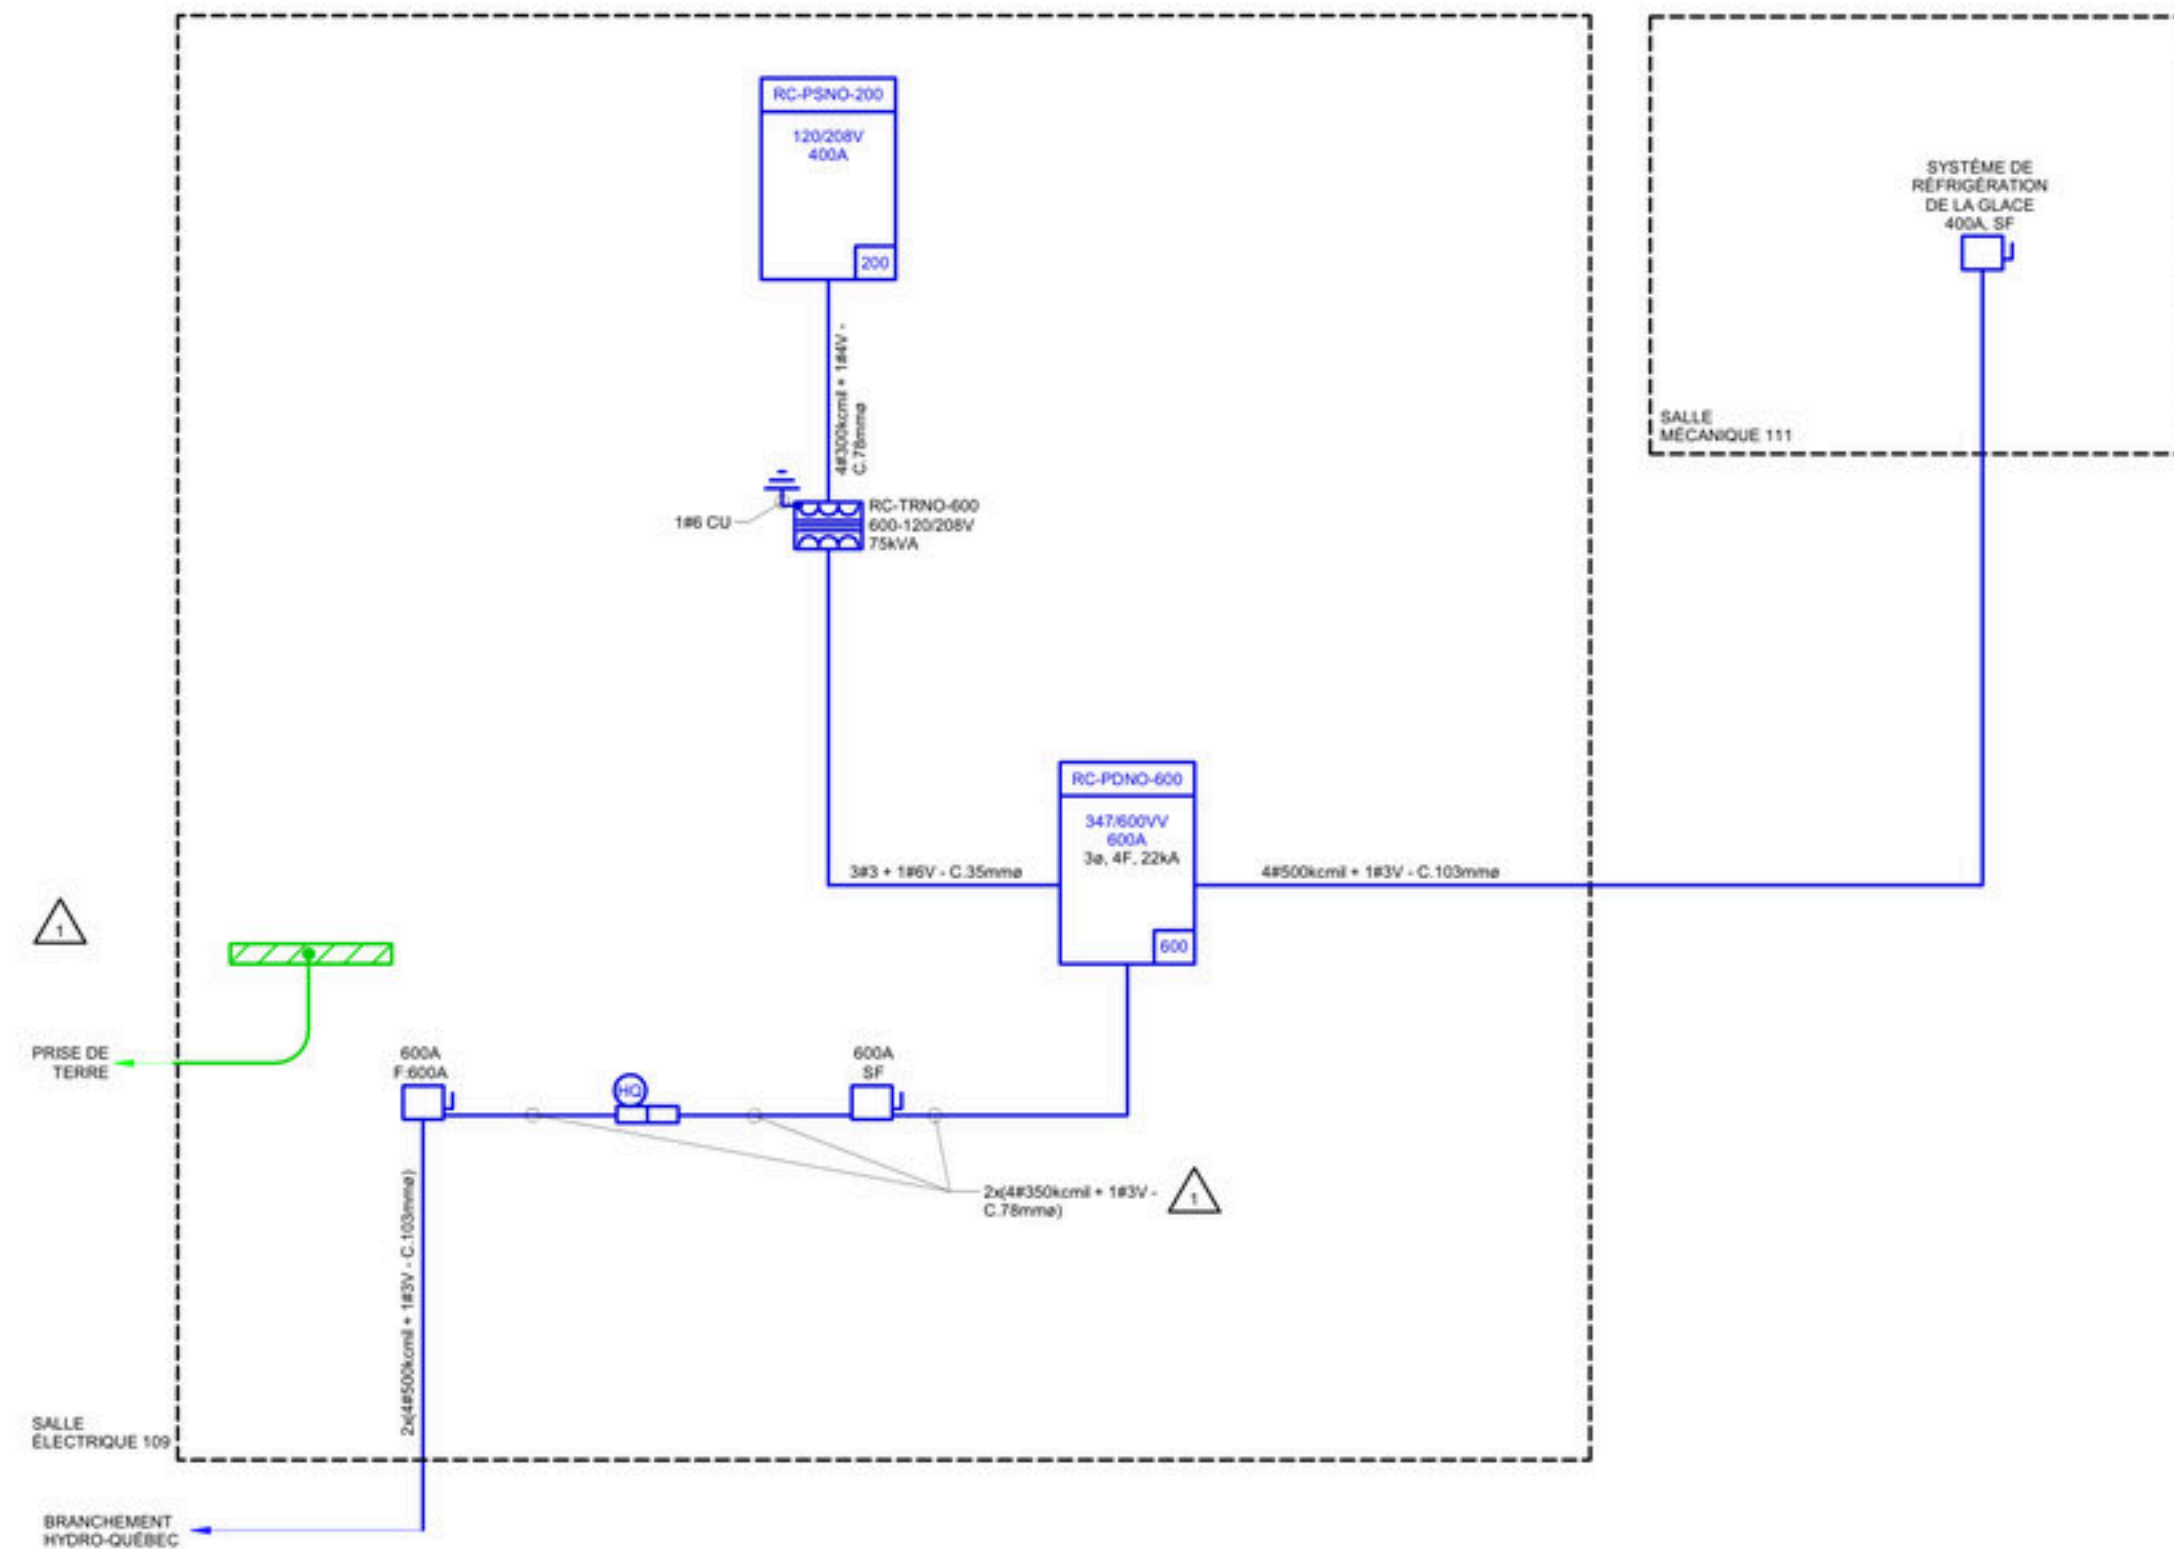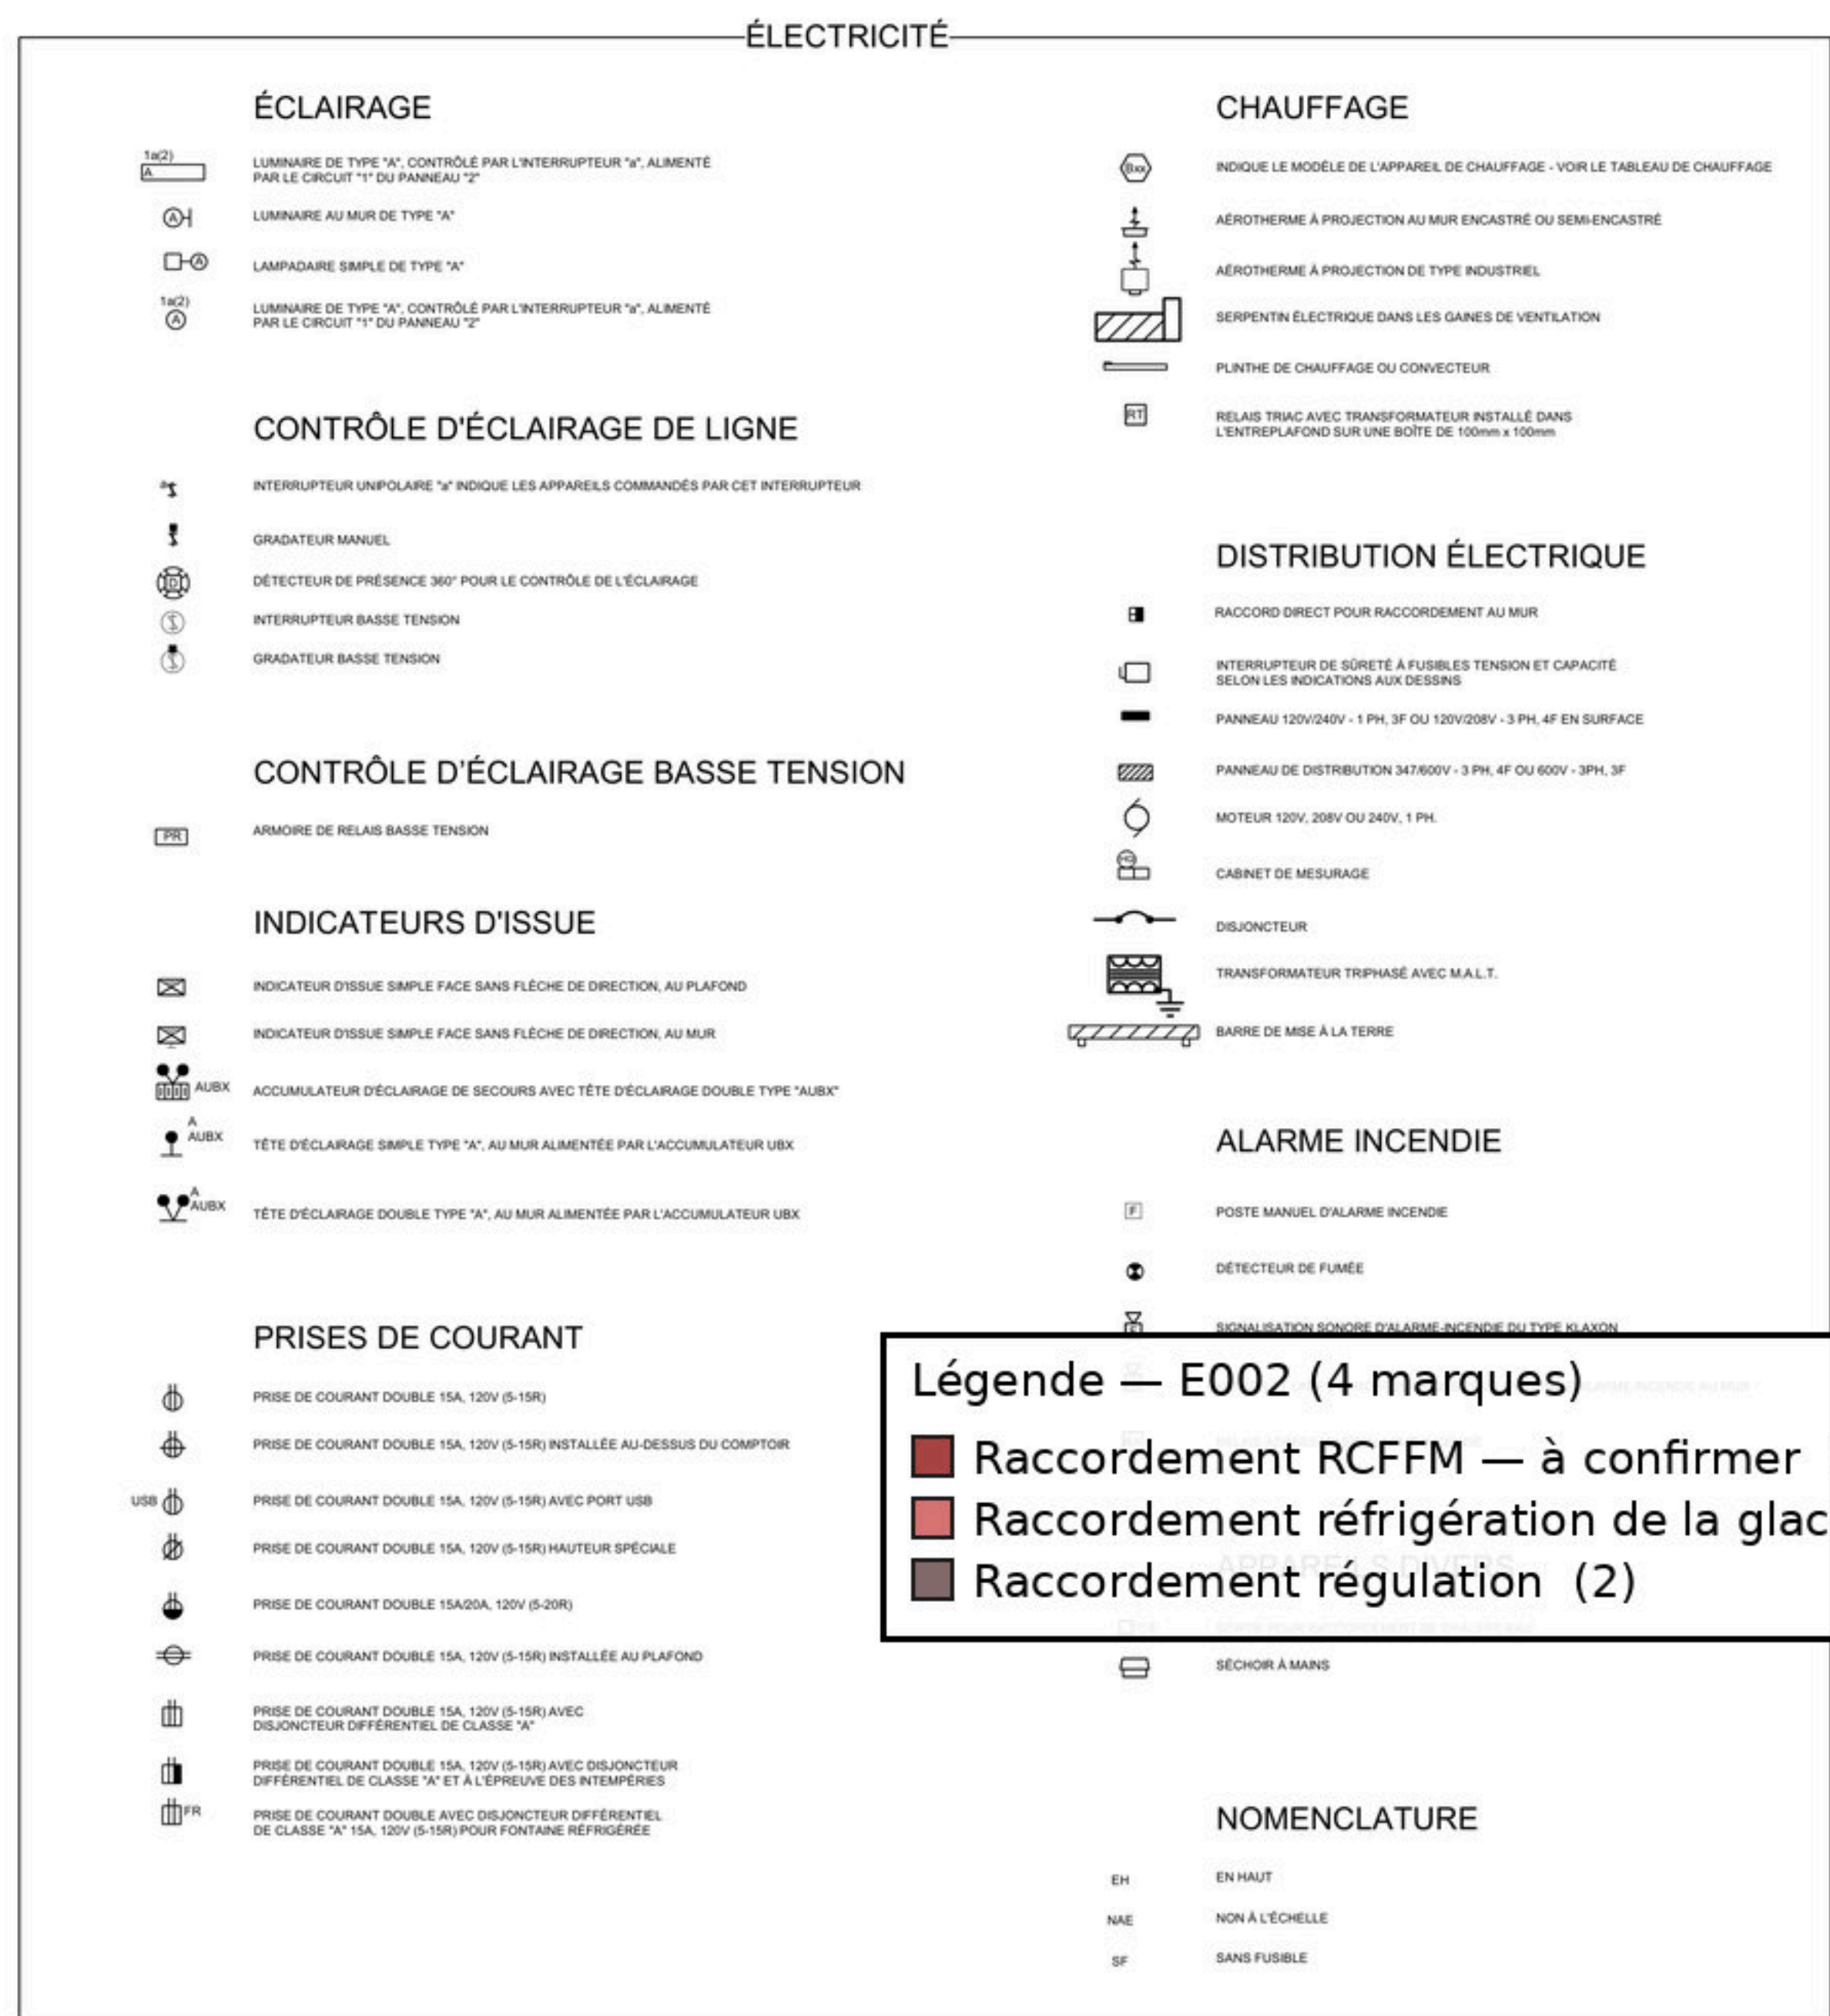

No.	Revisions	Date
1	POUR ADDENDA ELE-002	2026-03-12
2	POUR ADDENDA ELE-001	2026-03-02
3	POUR SOUMISSIONS	2026-02-06


CES DOCUMENTS NE DOIVENT PAS ÊTRE UTILISÉS À DES FINS DE CONSTRUCTION.

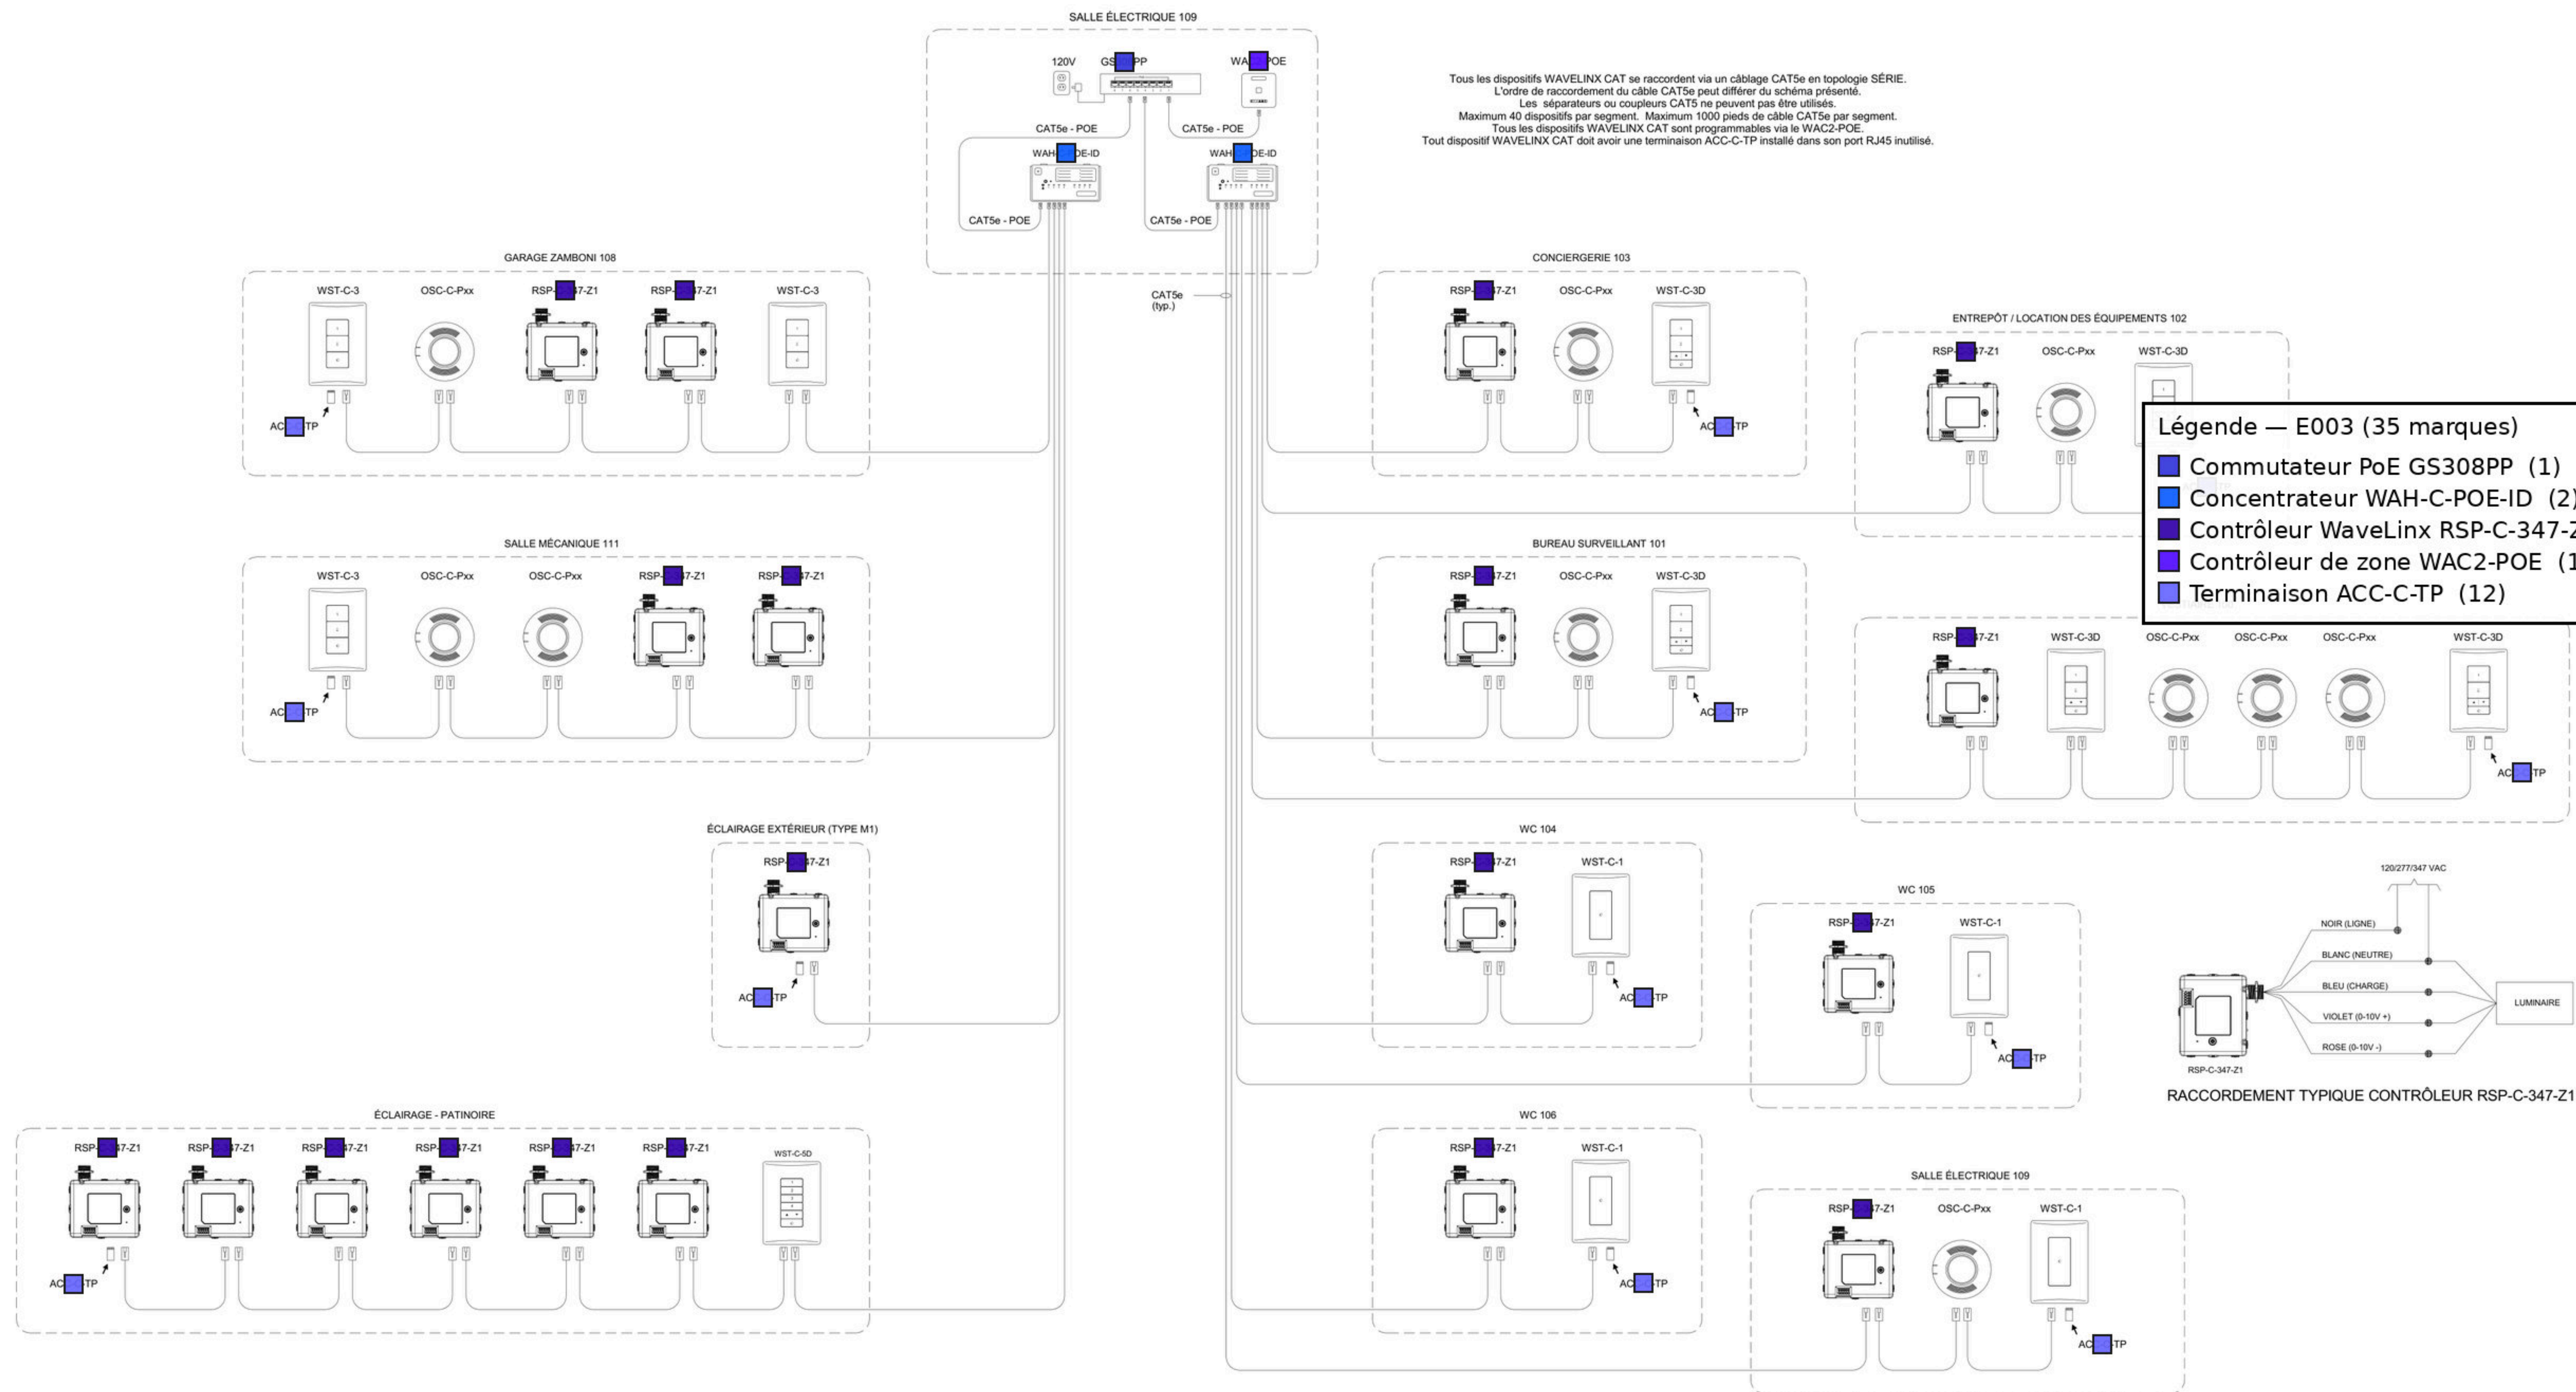

SYSTÈME DE CONTRÔLE D'ÉCLAIRAGE WAVELINX CAT - SCHÉMA DE RACCORDEMENT

No.	Revisions	Date
0	POUR ADDENDA ELE-002	2026-03-12

CES DOCUMENTS NE DOIVENT PAS
ÊTRE UTILISÉS À DES FINS DE
CONSTRUCTION.

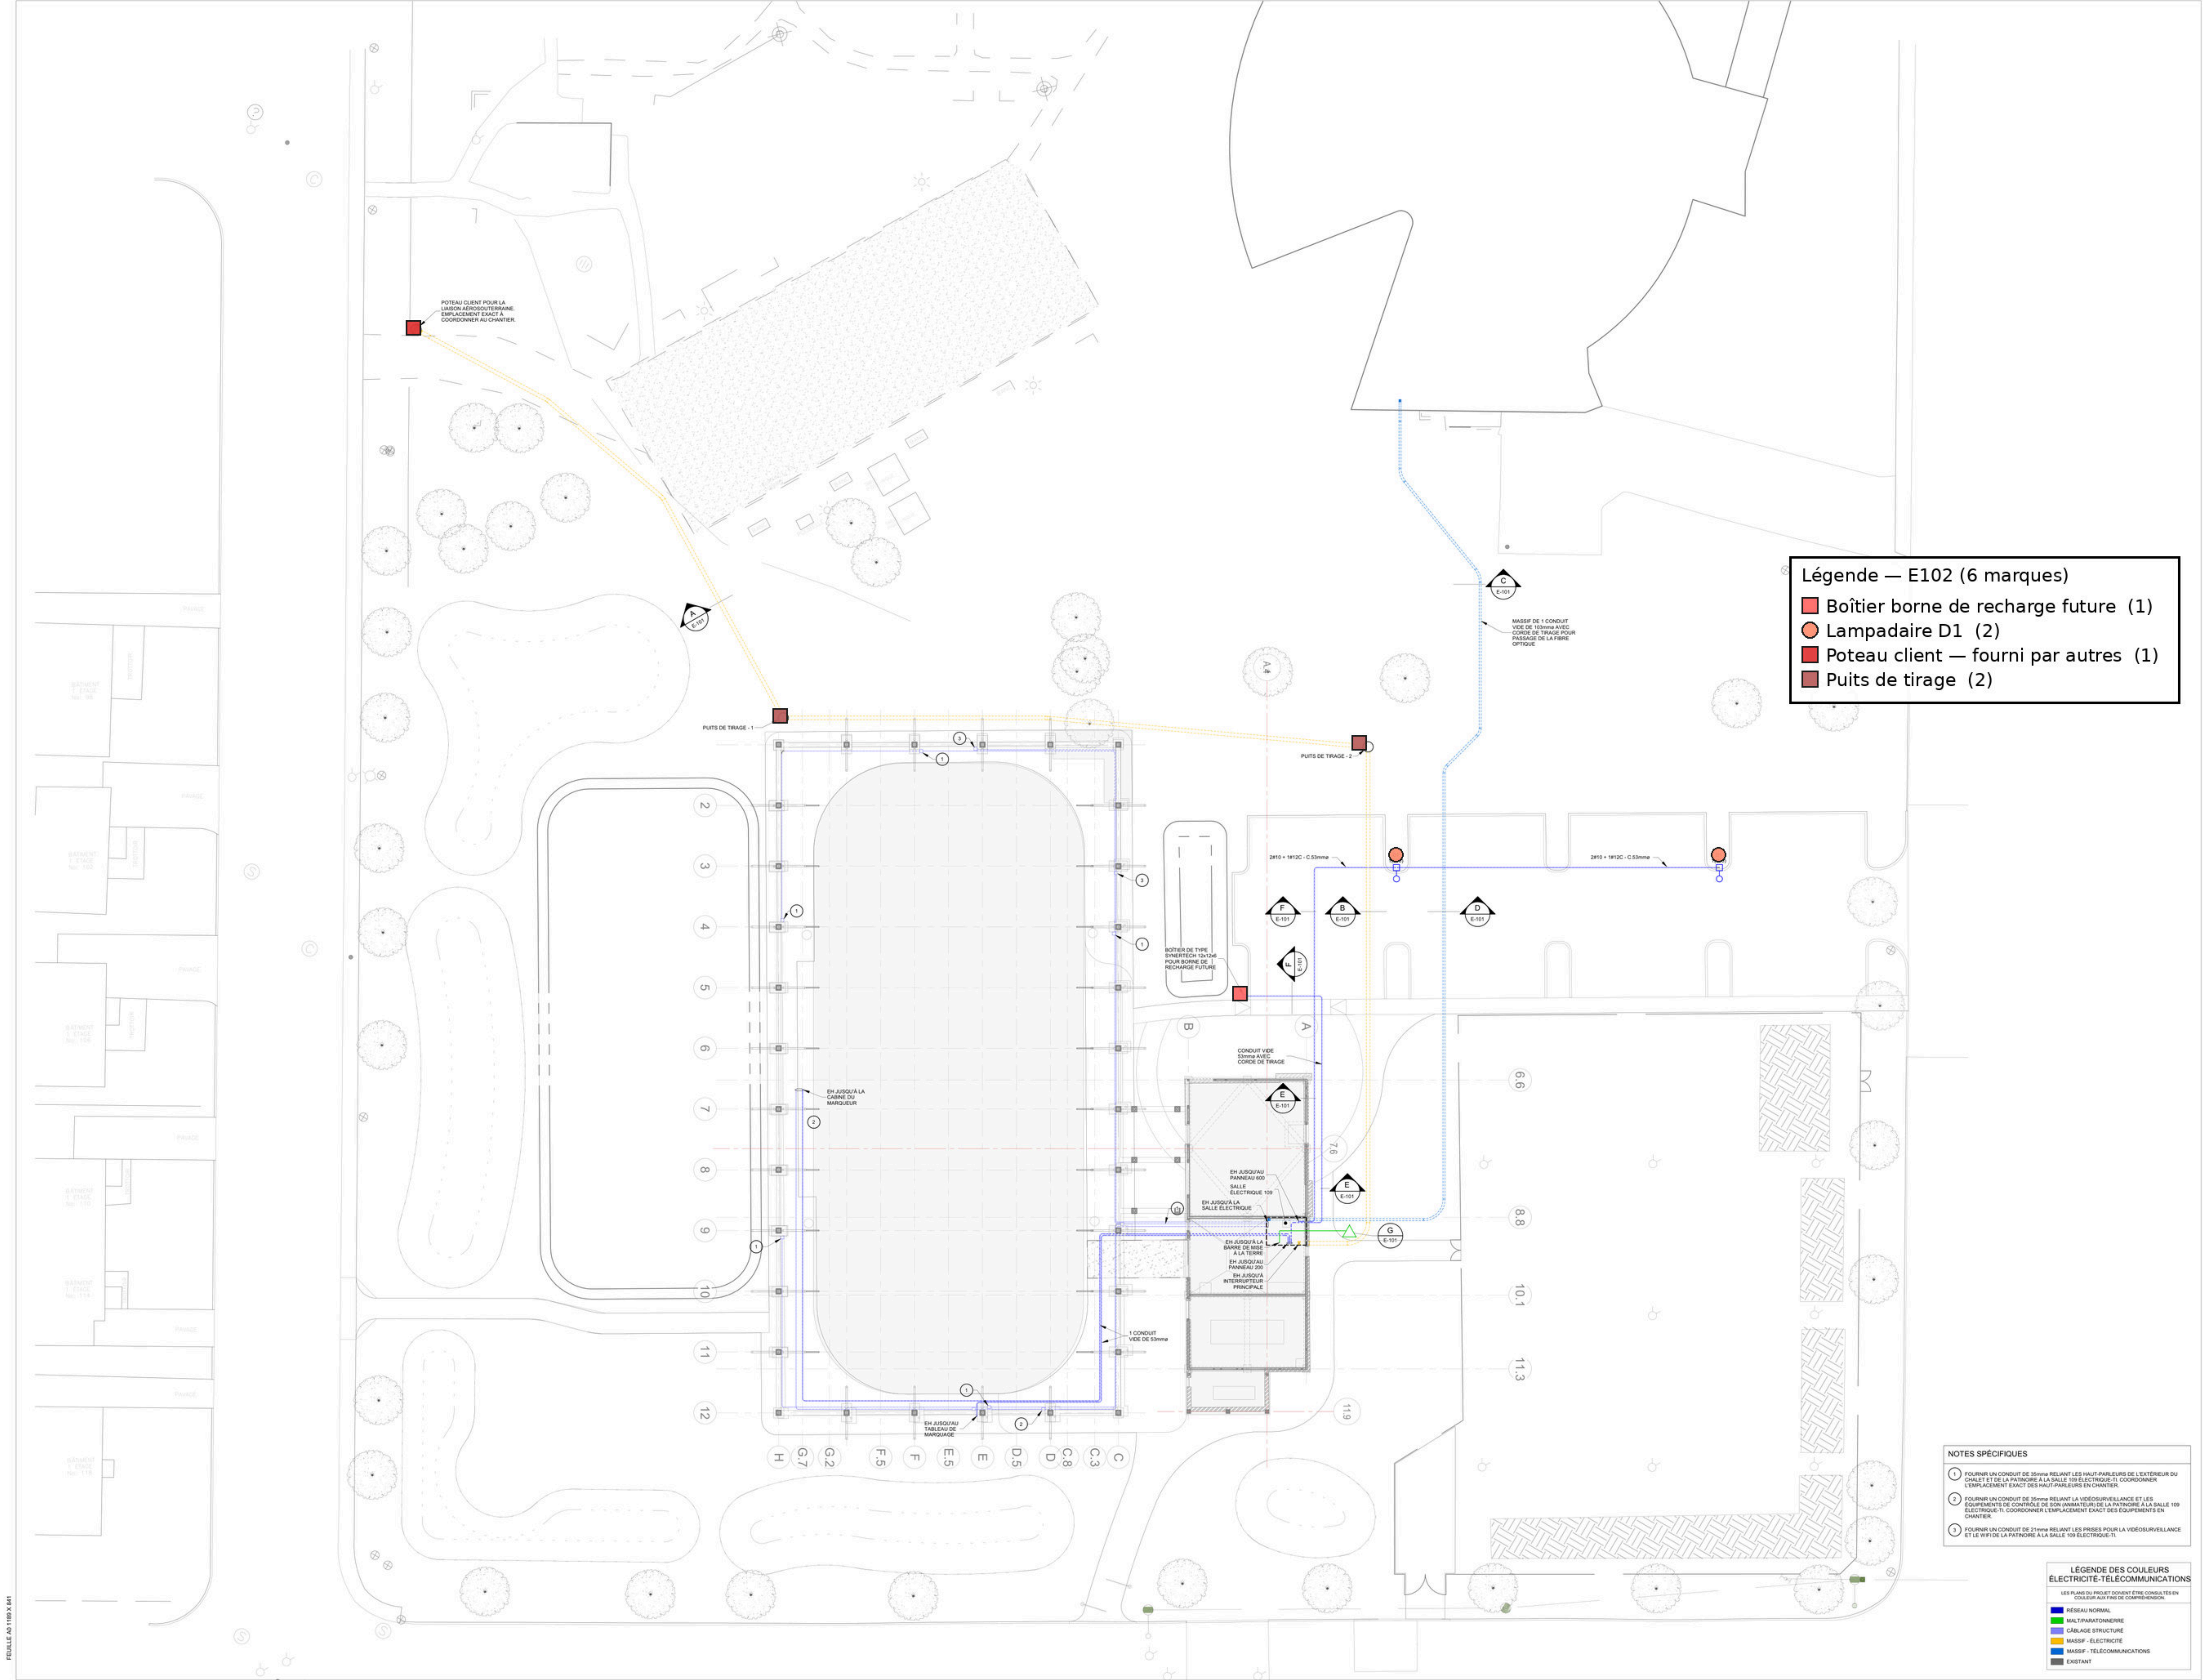

Légende — E102 (6 marques)

- Boîtier borne de recharge future (1)
- Lampadaire D1 (2)
- Poteau client — fourni par autres (1)
- Puits de tirage (2)

NOTES SPECIFIQUES

- Fournir un conduit de 30mm reliant les haut-parleurs de l'extérieur du chalet et de la patinoire à la salle 109 électrique. COORDONNER L'EMPLACEMENT EXACT DES HAUT-PARLEURS EN CHANTIER.
- Fournir un conduit de 20mm reliant la vidéosurveillance et les équipements de contrôle de son ambassadeur de la patinoire à la salle 109 électrique. COORDONNER L'EMPLACEMENT EXACT DES EQUIPEMENTS EN CHANTIER.
- Fournir un conduit de 21mm reliant les prises pour la vidéosurveillance et le Wi-Fi de la patinoire à la salle 109 électrique.

LÉGENDE DES COULEURS ÉLECTRICITÉ-TELECOMMUNICATIONS

LES PLANS DU PROJET DOIVENT ETRE CONSULTEES EN COULEUR AUX FINS DE COMPREHENSION

- RESEAU NORMAL
- MULTIPARATONNERRE
- CABLAGE STRUCTURE
- MASSE - ELECTRONIQUE
- MASSE - TELECOMMUNICATIONS
- EXISTANT

Cliant:

VILLE DE SALABERRY-DE-VALLEYFIELD
81, RUE SAINTÉ-CECILE, SALABERRY-DE-VALLEYFIELD (QUÉBEC), J6T 1L8

CONSTRUCTION D'INFRASTRUCTURES SPORTIVES AU PARC LIONEL-GROULX

118, RUE MATHIAS, SALABERRY-DE-VALLEYFIELD (QUÉBEC), J6T 3L6

CHALET, PATINOIRE ET STATIONNEMENT

POUR SOUMISSIONS

Architectes:

BBC architectes
1535, chemin Sainte-Foy, suite 120
Québec (Québec) G1S 2P1
418 684-5165
architectes@bbcarchitectes.ca

Ingénieurs mécanique / électricité:

BPA

Ingénieurs structure:

wsp
1115, BOULEVARD LEBLANCHEUR
QUÉBEC (QUÉBEC) G1M 1H6
TEL. 418 623-1244 / TEL.ÉC. 418 623-1077 / WWW.WSP.COM

Plan clé:

Sous:

David Dussault
2026-02-09

No.	Revisions	Date
0	POUR SOUMISSIONS	2026-02-06

CES DOCUMENTS NE DOIVENT PAS ETRE UTILISES A DES FINS DE CONSTRUCTION.


ÉLECTRICITÉ

Titre: Échelle: 1 : 200

ÉLECTRICITÉ GÉNÉRALE
PLAN D'IMPLANTATION

Conçu par: D. DUSSAULT Page
Dessiné par: M. GUAY **E-102**
Vérifié par: D. DUSSAULT DE
Dossier BPA: 25-13561 **11**
Dossier BBC: 25-1811

FICHE A3 1180 X 841

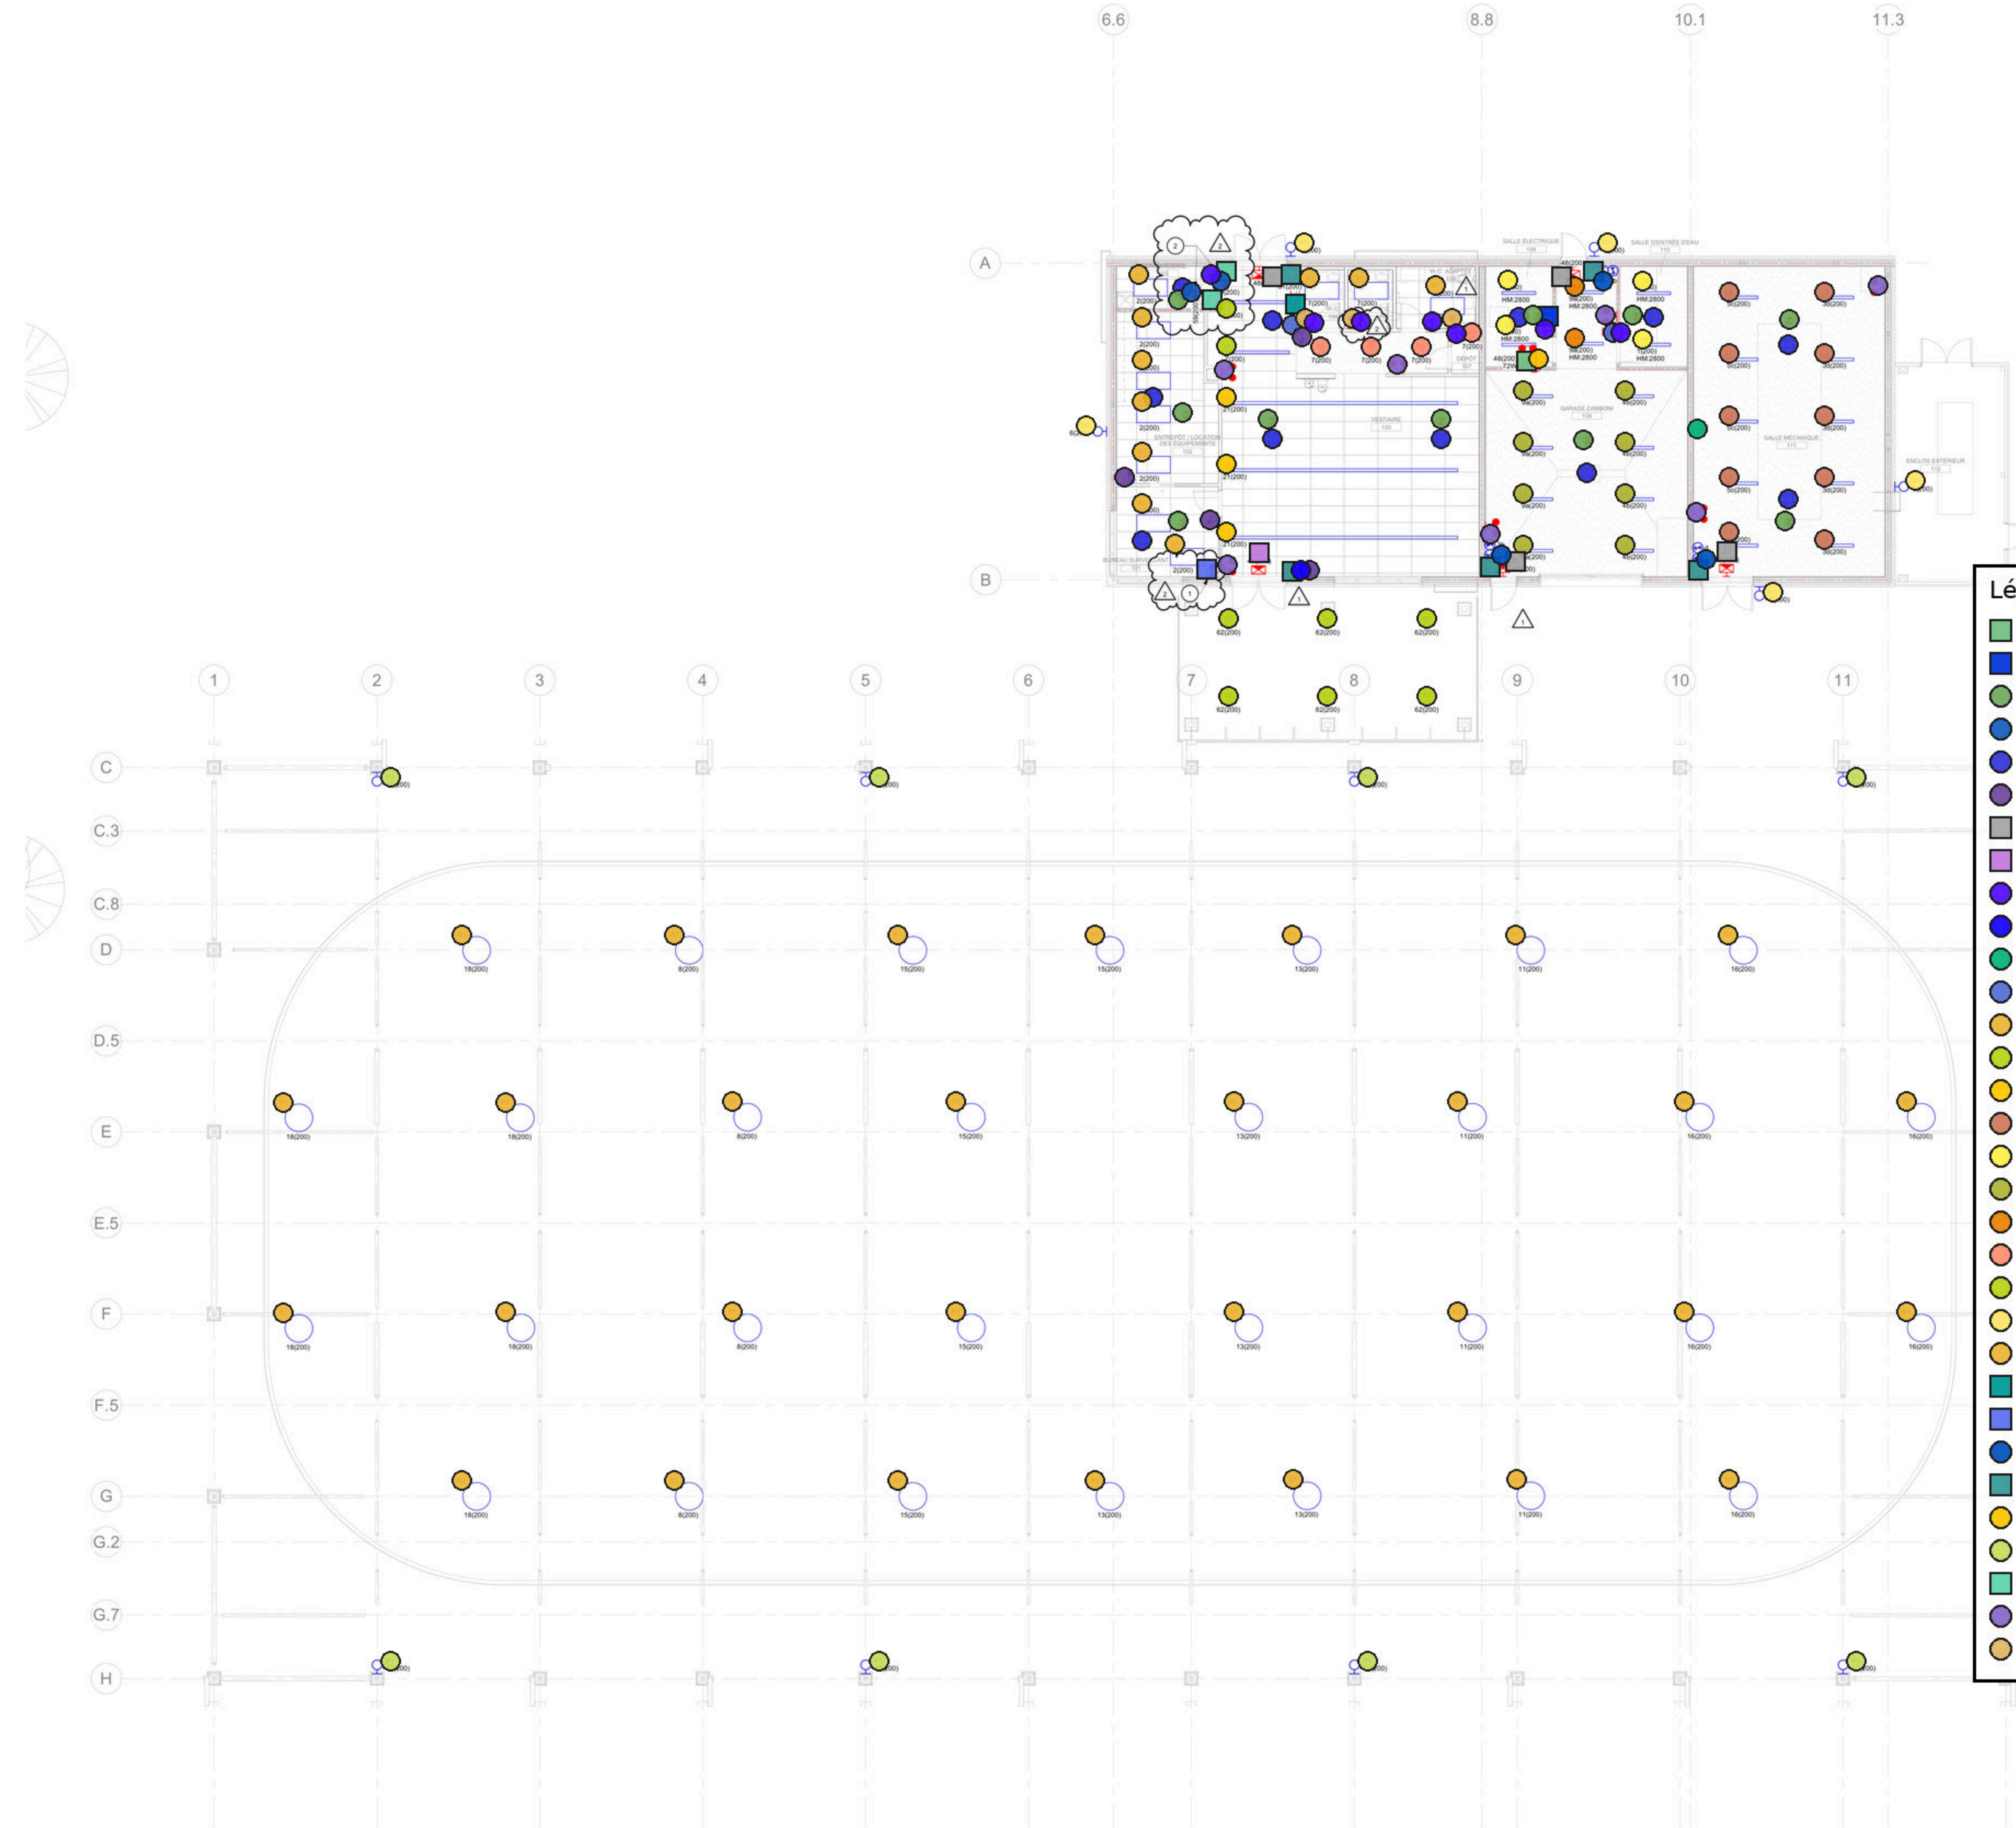

-  Accumulateur AUBX (1)
-  Armoire de relais BT (P.R.) (1)
-  Détecteur de fumée (10)
-  Détecteur de fumée de conduit (note 2) (2)
-  Détecteur de présence 360° (11)
-  Gradateur basse tension (4)
-  Indicateur d'issue Z1 (mur) — à confirmer (4)
-  Indicateur d'issue Z2 (plafond) — à confirmer (1)
-  Interrupteur basse tension (7)
-  Interrupteur unipolaire (1)
-  Klaxon + stroboscope (1)
-  Klaxon alarme incendie (2)
-  Luminaire A1 (10)
-  Luminaire L1 (2)
-  Luminaire L2 (3)
-  Luminaire L3 (10)
-  Luminaire L3A (4)
-  Luminaire L4 (8)
-  Luminaire L4A (2)
-  Luminaire R2 (4)
-  Luminaire R3 (6)
-  Luminaire mural M1 (5)
-  Luminaire suspendu R1 (30)
-  Panneau d'alarme incendie (PAI) (1)
-  Panneau de contrôle P1 (note 1) (1)
-  Poste BT double (a/b) (3)
-  Poste manuel (5)
-  Prise hauteur spéciale (1)
-  Projecteur P1 (8)
-  Relais adressable RA (2)
-  Tête d'éclairage double (7)
-  Tête d'éclairage simple (3)


NOTE(S) SPÉCIFIQUE(S)

1. PANNEAU DE CONTRÔLE D'ÉCLAIRAGE DES APPAREILS DE TYPE P1.
2. DÉTECTEURS DE FUMÉE POUR UNE INSTALLATION DANS UN CONDUIT POUR LES VOLETS COUPE-FEU/COUPE-FUMÉE.

LÉGENDE DES COULEURS ÉLECTRICITÉ

LES PLANS DU PROJET DOIVENT ÊTRE CONSULTÉS EN COULEUR AUX FINS DE COMPRÉHENSION:

	RÉSEAU NORMAL
	SÉCURITÉ DES PERSONNES
	ALARME INCENDIE
	EXISTANT

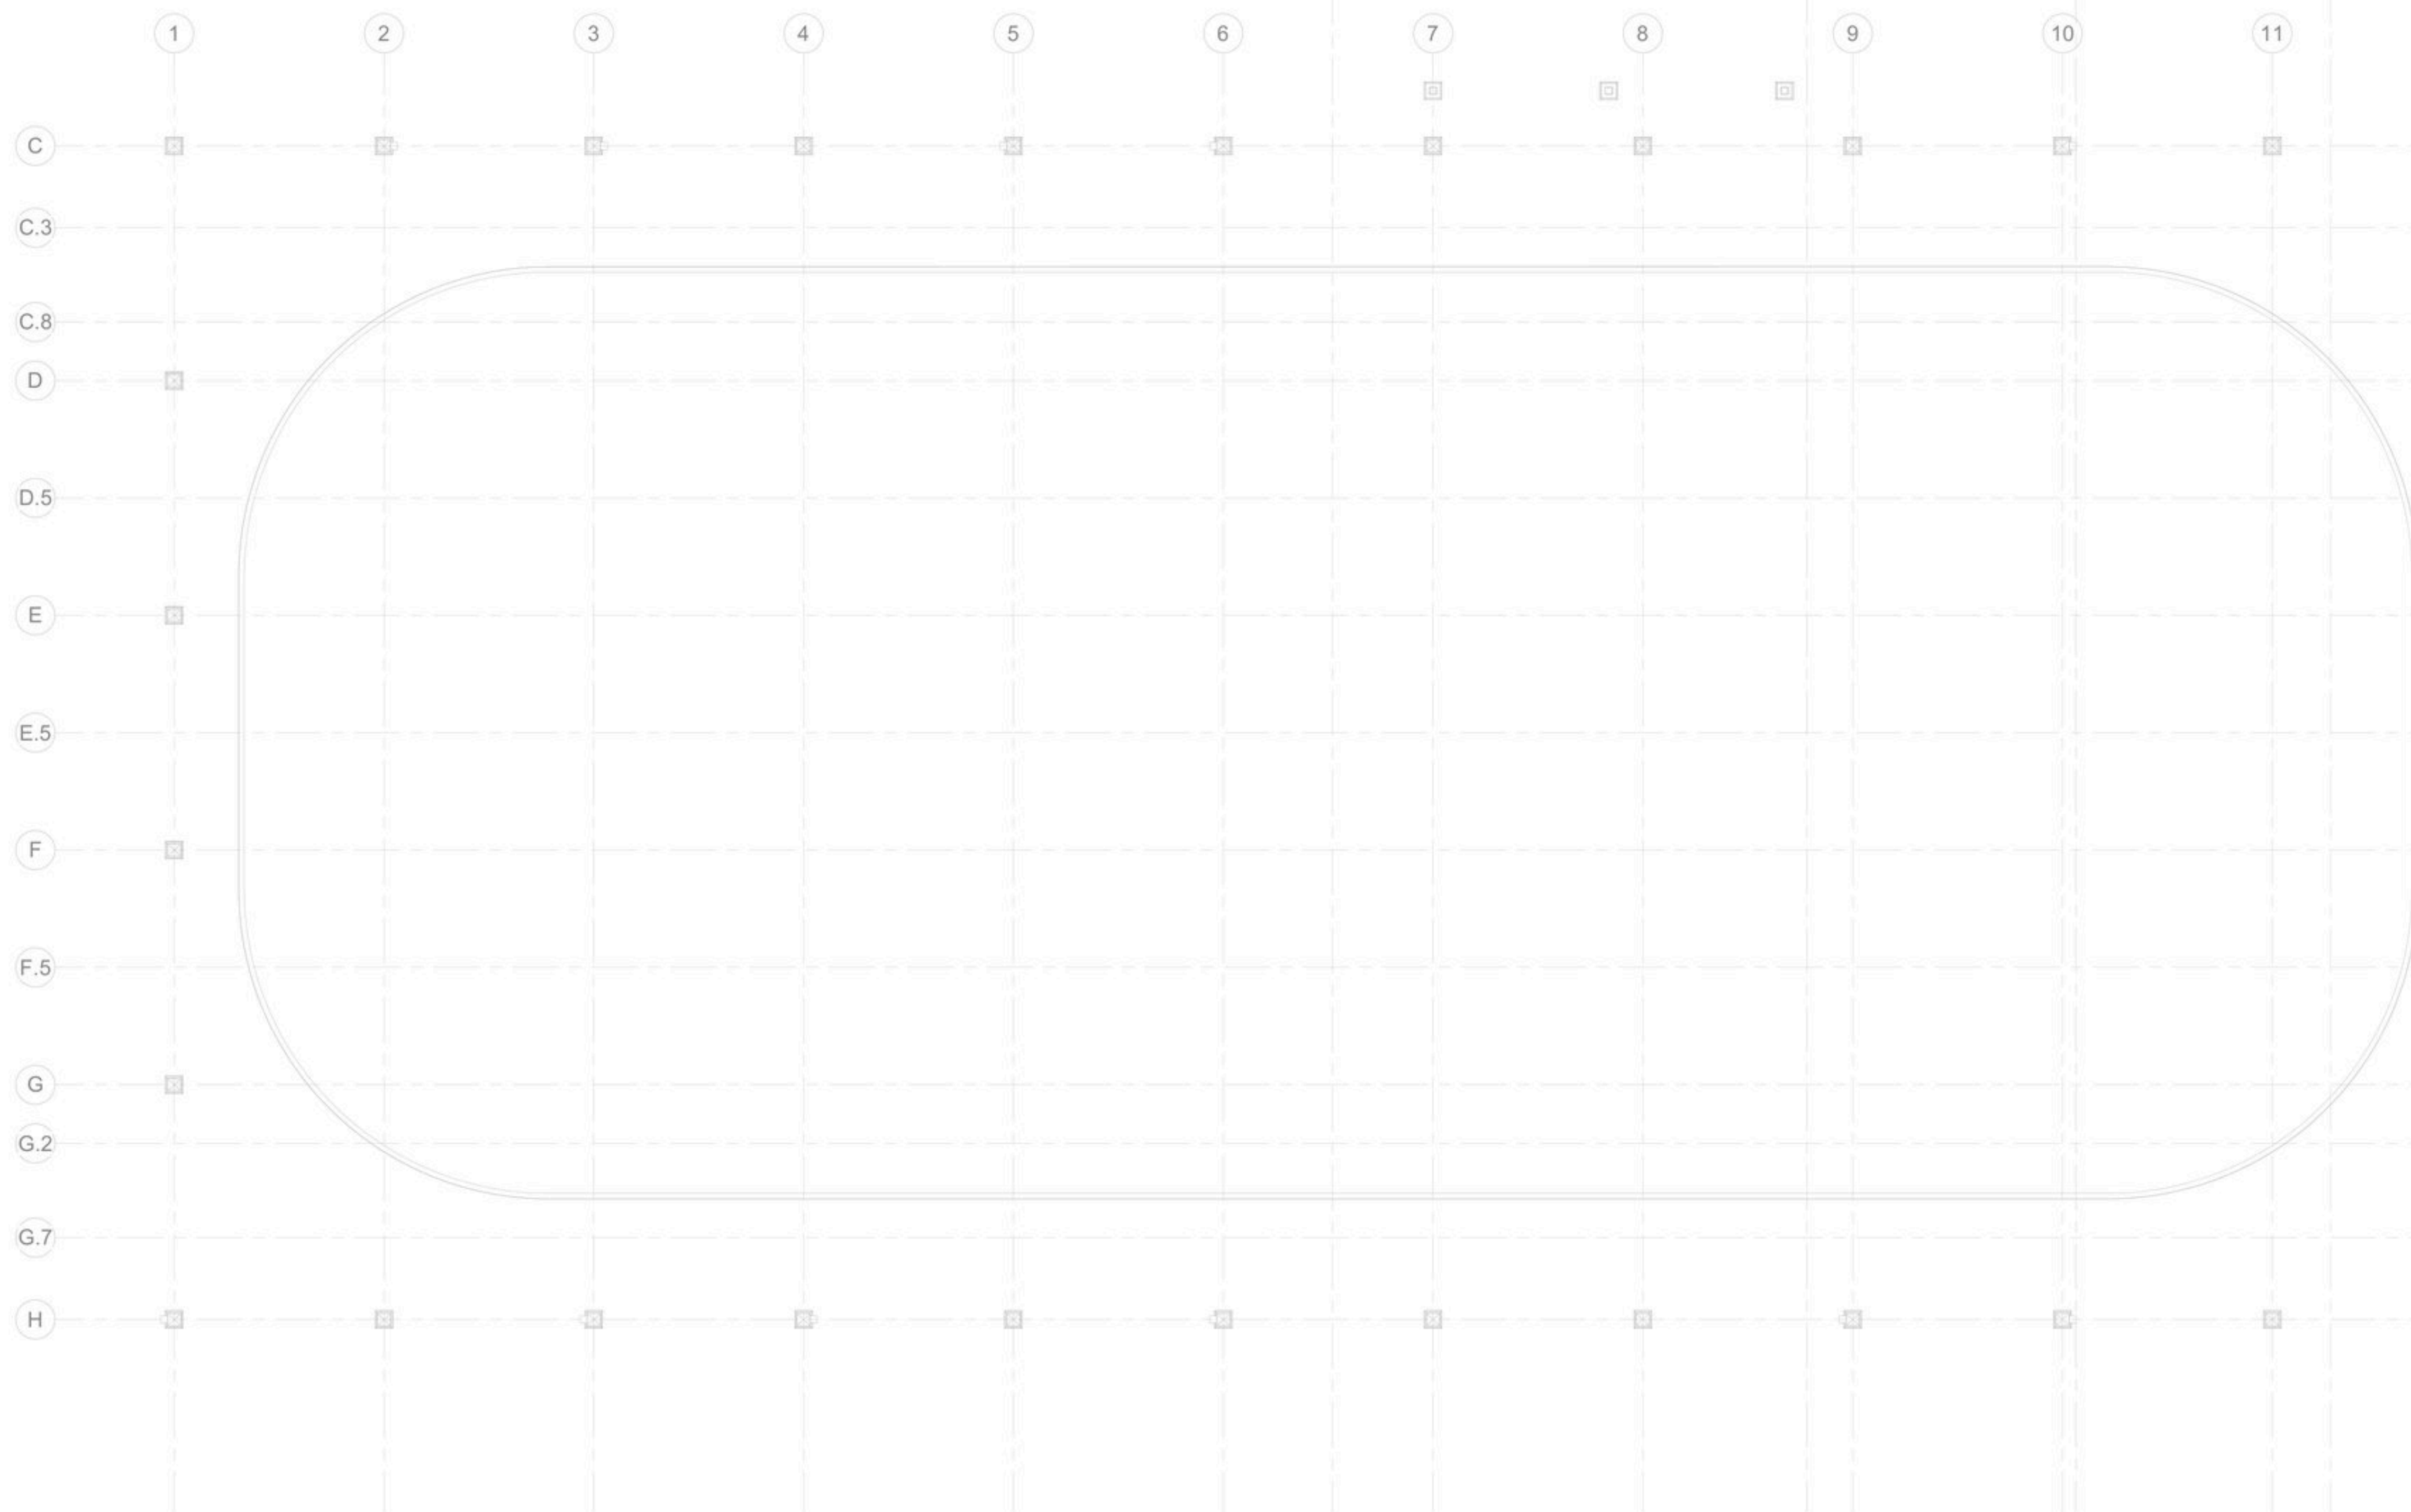

- Légende — E301 (90 marques)**
- ◆ Aérotherme mural A15 (3)
 - ◆ Aérotherme plafond T15 (1)
 - ◆ Aérotherme plafond T4 (1)
 - Barre de mise à la terre (1)
 - Boîtier Camlock 200A (1)
 - Cabinet de mesurage HQ (1)
 - Interrupteur de sûreté 400A SF (réfrigération) (1)
 - Interrupteur de sûreté 600A (2)
 - Interrupteur unipolaire (1)
 - Panneau RC-PDNO-600 (1)
 - Panneau RC-PSNO-200 (1)
 - ◆ Plinthe B10 (1)
 - ◆ Plinthe B12 (2)
 - ◆ Plinthe B15 (1)
 - ◆ Plinthe B25 (1)
 - ◆ Plinthe B5 (5)
 - Prise 15/20A (5-20R) (3)
 - Prise DDFT (5)
 - Prise DDFT fontaine réfrigérée (1)
 - Prise DDFT intempéries (3)
 - Prise au plafond (4)
 - Prise au-dessus du comptoir (6)
 - Prise double 15A (8)
 - Prise double USB (2)
 - Raccordement COND (1)
 - Raccordement DEV (1)
 - Raccordement ECH (1)
 - Raccordement PECR (1)
 - Raccordement VA (2)
 - Raccordement VC (1)
 - Raccordement chauffe-eau CE (36 kW) (3)
 - Raccordement serpentin SE (7)
 - Raccordement ventilateur VE (4)
 - Relais triac RT (9)
 - Sèche-mains (3)
 - Transformateur RC-TRNO-600 (1)

LÉGENDE DES COULEURS ÉLECTRICITÉ	
LES PLANS DU PROJET DOIVENT ÊTRE CONSULTÉS EN COULEUR AUX FINS DE COMPRÉHENSION.	
■	NIVEAU NORMAL
■	NIVEAU TRANSFORMATION
■	NIVEAU URGENCE
■	EXISTANT

ÉLECTRICITÉ


Titre: ÉLECTRICITÉ SERVICES NIVEAU 1

Conçu par: D. DUSSAULT Page
Dessiné par: M. GUAY E-301
Vérifié par: D. DUSSAULT DE
Dossier BPA: 25-13561 11
Dossier BBC: 25-1811

Architectes: 
BEC architects
1000, Avenue de la Paix, suite 120
S 2P1
Salaberry-de-Valleyfield (Québec) J6T 1L8
Tél: 514 333-1111
www.becarchitectes.ca

Électricité: 
BPA
1000, Avenue de la Paix, suite 120
S 2P1
Salaberry-de-Valleyfield (Québec) J6T 1L8
Tél: 514 333-1111
www.bpa.ca

SP
1000, Avenue de la Paix, suite 120
S 2P1
Salaberry-de-Valleyfield (Québec) J6T 1L8
Tél: 514 333-1111
www.sp.ca

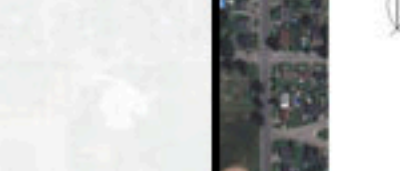
VILLE DE SALABERRY-DE-VALLEYFIELD
81, RUE SAINTÉ-CECILE, SALABERRY-DE-VALLEYFIELD (QUÉBEC), J6T 1L8
CONSTRUCTION D'INFRASTRUCTURES
SPORTIVES AU PARC LIONEL-GROULX
118, RUE MATHIAS, SALABERRY-DE-VALLEYFIELD (QUÉBEC), J6T 3J6
CHALET, PATINOIRE ET STATIONNEMENT



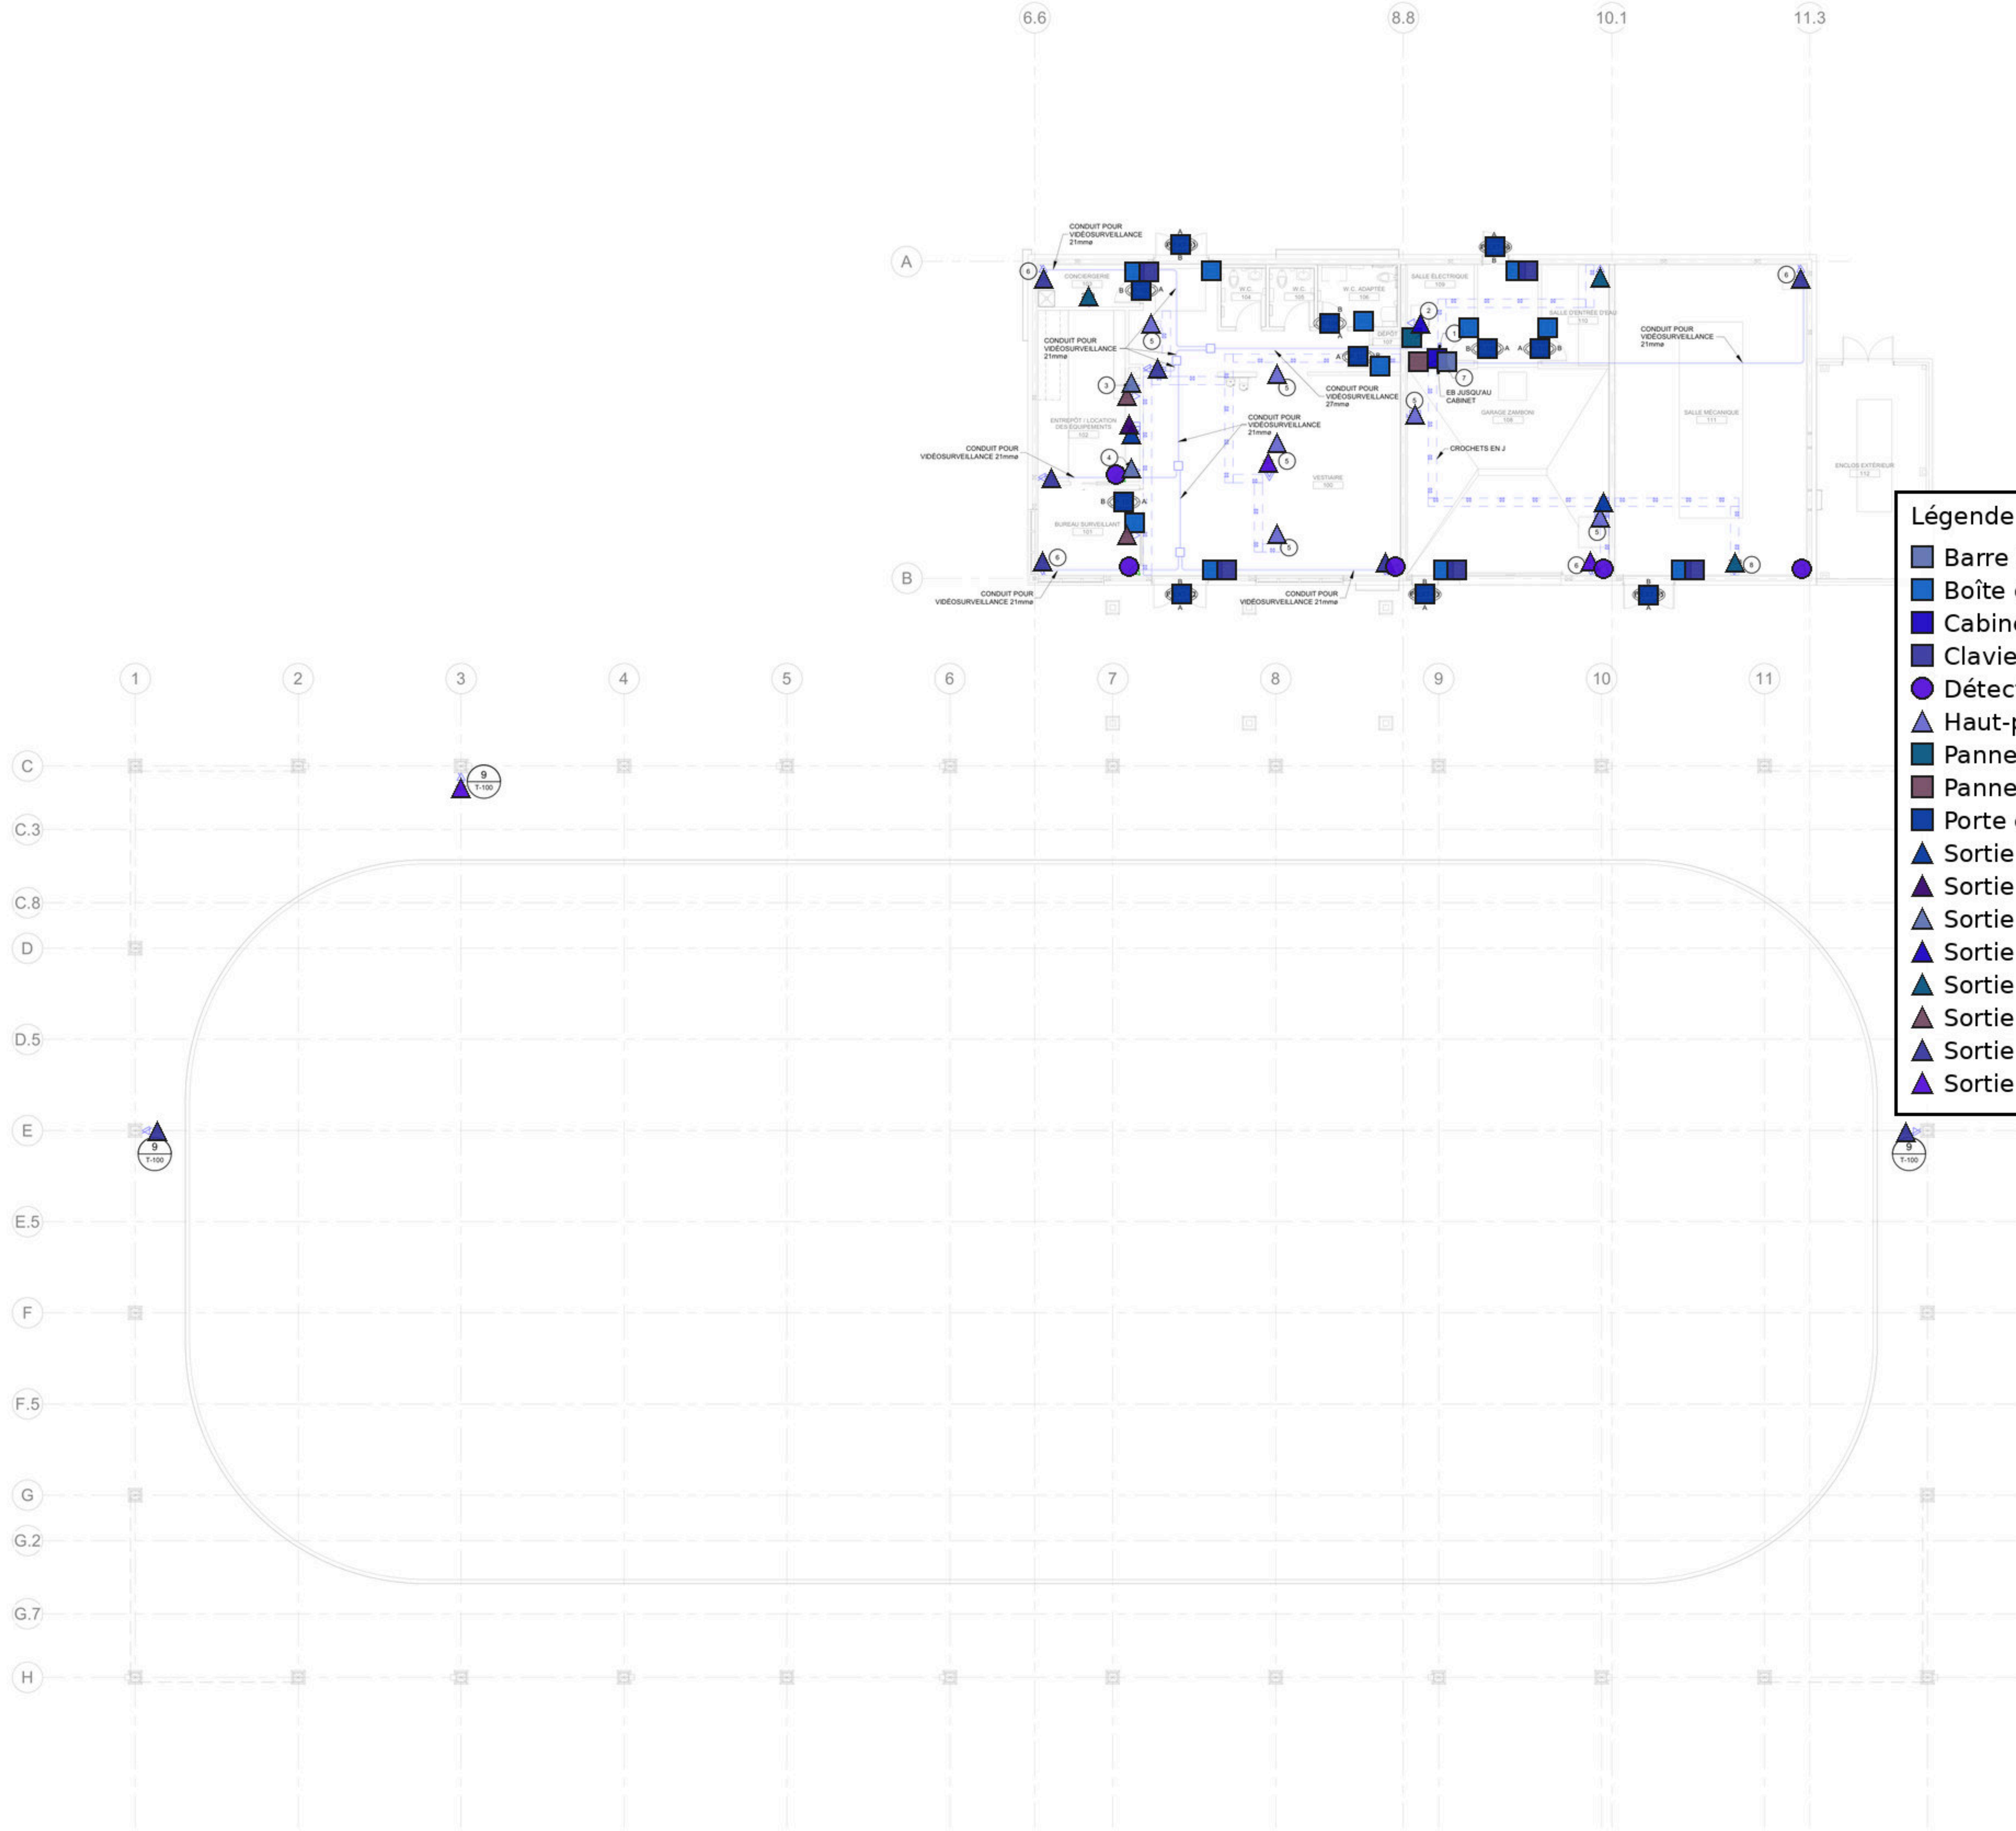

NOTE(S) GÉNÉRALE(S)

A. POUR LES CONDUITS SOUS-TERRAIN, VOIR LES PLANS ÉLECTRIQUES (E-102).

B. FOURNIR ET INSTALLER UN RÉSEAU DE CONDUIT DU PCA JUSQU'ÀUX COMPOSANTES DE CONTRÔLE D'ACCÈS. VOIR TABLEAU 10 (T-101).

C. FOURNIR ET INSTALLER UN RÉSEAU DE CONDUIT DU POI JUSQU'ÀUX COMPOSANTES D'INTRUSION. VOIR TABLEAU 11 (T-101).

D. À MOINS D'INDICATION CONTRAIRE, LES CÂBLES ET LES ÉQUIPEMENTS D'APPEL GÉNÉRAL DE CONTRÔLE D'ACCÈS ET D'INTRUSION SONT FOURNIS ET INSTALLÉS PAR LE CLIENT.

NOTE(S) SPÉCIFIQUE(S)

1. CABINET MURAL FOURNI ET INSTALLÉ PAR LE CLIENT.

2. PANNEAU DE CONTRÔLE D'ACCÈS FOURNI ET INSTALLÉ PAR L'ENTREPRENEUR.

3. FOURNIR LE RÉSEAU DE CONDUIT POUR RACCORDER DU PANNEAU À TOUTES LES PORTES CONTRÔLÉES.

4. PRISE POUR PLAQUE DE CONTRÔLE DE SON TACTILE.

5. PRISE POUR L'ANTENNE BLUETOOTH.

6. FOURNIR UN RÉSEAU DE CROCHETS EN J RELIANT L'HAUT-PARLEUR DANS LE CHALET ET LA SALLE VO ÉLECTRIQUE. COORDONNER L'EMPLACEMENT EXACT DES HAUT-PARLEURS EN CHALET. HAUT-PARLEURS FOURNIS ET INSTALLÉS PAR LE CLIENT.

7. PRÉVOIR UN PERÇEMENT POUR LE RACCORDEMENT PAR LE CLIENT DES CAMÉRAS ET BORNES WIFI EXTÉRIEURES.

8. BARRE CANIVUS SECONDAIRE DE MISE À LA TERRE POUR LES ÉQUIPEMENTS DE TÉLÉCOMMUNICATION. FOURNI ET INSTALLÉ PAR L'ENTREPRENEUR EN ÉLECTRICITÉ. INSTALLER LA BARRE EN DESSOUS DU CABINET MURAL.

9. PRISES POUR LE PANNEAU DE CONTRÔLE DU REPRODUISSEUR. COORDONNER L'EMPLACEMENT EXACT DU PANNEAU AVEC L'ENTREPRENEUR DE RÉFRIGÉRATION.

Légende — T201 (64 marques)

- Barre MALT télécom (note 7) (1)
- Boîte de groupe sécurité BG (11)
- Cabinet mural télécom — fourni par autres (1)
- Clavier d'intrusion CLI (5)
- Détecteur de mouvement (5)
- Haut-parleur — fourni par autres (6)
- Panneau de contrôle d'accès PCA (1)
- Panneau de détection d'intrusion PDI (1)
- Porte contrôlée (11)
- Sortie contrôle de volume (2)
- Sortie microphone (1)
- Sortie télécom (note) (2)
- Sortie télécom CA (1)
- Sortie télécom CB (3)
- Sortie télécom D (2)
- Sortie télécom VS (8)
- Sortie télécom WF (3)

LÉGENDE DES COULEURS
TÉLÉCOMMUNICATIONS

LES PLANS DU PROJET DOIVENT ÊTRE CONSULTÉS EN COULEUR AUX FINS DE COMPRÉHENSION.

- CÂBLAGE STRUCTURE
- CONDUIT D'ACCÈS ET VIDEOSURVEILLANCE
- EXISTANT

No.	Révisions	Date
0	POUR SOUMISSIONS	2026-02-06

CES DOCUMENTS NE DOIVENT PAS
ÊTRE UTILISÉS À DES FINS DE
CONSTRUCTION.

TÉLÉCOMMUNICATION

Titre: Échelle: 1: 100
TÉLÉCOMMUNICATION
CÂBLAGE STRUCTURE
NIVEAU 1