

Les architectes Clermont St-Germain associés
1845 Rue de l'Église
Sainte-Julie, Qc, J3E1E9
t. 450.461.0835
pstgermain@architectescs.com
www.architectescs.com

RELEVÉ A801 - MATERIEL

66 repères / 14 familles / RES 66

RES = réserve source, modèle, position, portée ou reconciliation; * = identification à réviser

- **AF** DETECTEUR DE FUMÉE D.F.E. (HORS LÉGENDE - R-001)
● **C3** INTERRUPTEUR 3 VOIES HAUTEUR STANDARD
● **CI** PRISE ÉLECTRIQUE CONTRÔLÉ PAR INTERRUPTEUR
● **CT** PRISE ÉLECTRIQUE HAUTEUR COMPTEUR

- **CU** INTERRUPTEUR HAUTEUR STANDARD
■ **EV** VENTILATEUR
● **LD** PLAFONNIER DETECTEUR DE MOUVEMENT
● **LE** ENCASTRE SLIM


- 12 / R12 ● **LM** APPLIQUE MURALE - SALLE D'ATTENTE
1 / R1 ● **LS** LUMINAIRE SUSPENDU
4 / R4 ● **PC** PRISE ÉLECTRIQUE HAUTEUR STANDARD
11 / R11 ■ **PL** PLINTE ÉLECTRIQUE

- 3 / R3 ■ **RA** RACCORD DIRECT VRC (HORS LÉGENDE - R-001)
1 / R1 ■ **TH** THERMOSTAT
1 / R1
10 / R10


- 1 / R1
4 / R4

Quantités source et renvois; voir bordereau détaillé.

Calques activables; modèles, prescriptions et réserves complètes page 2

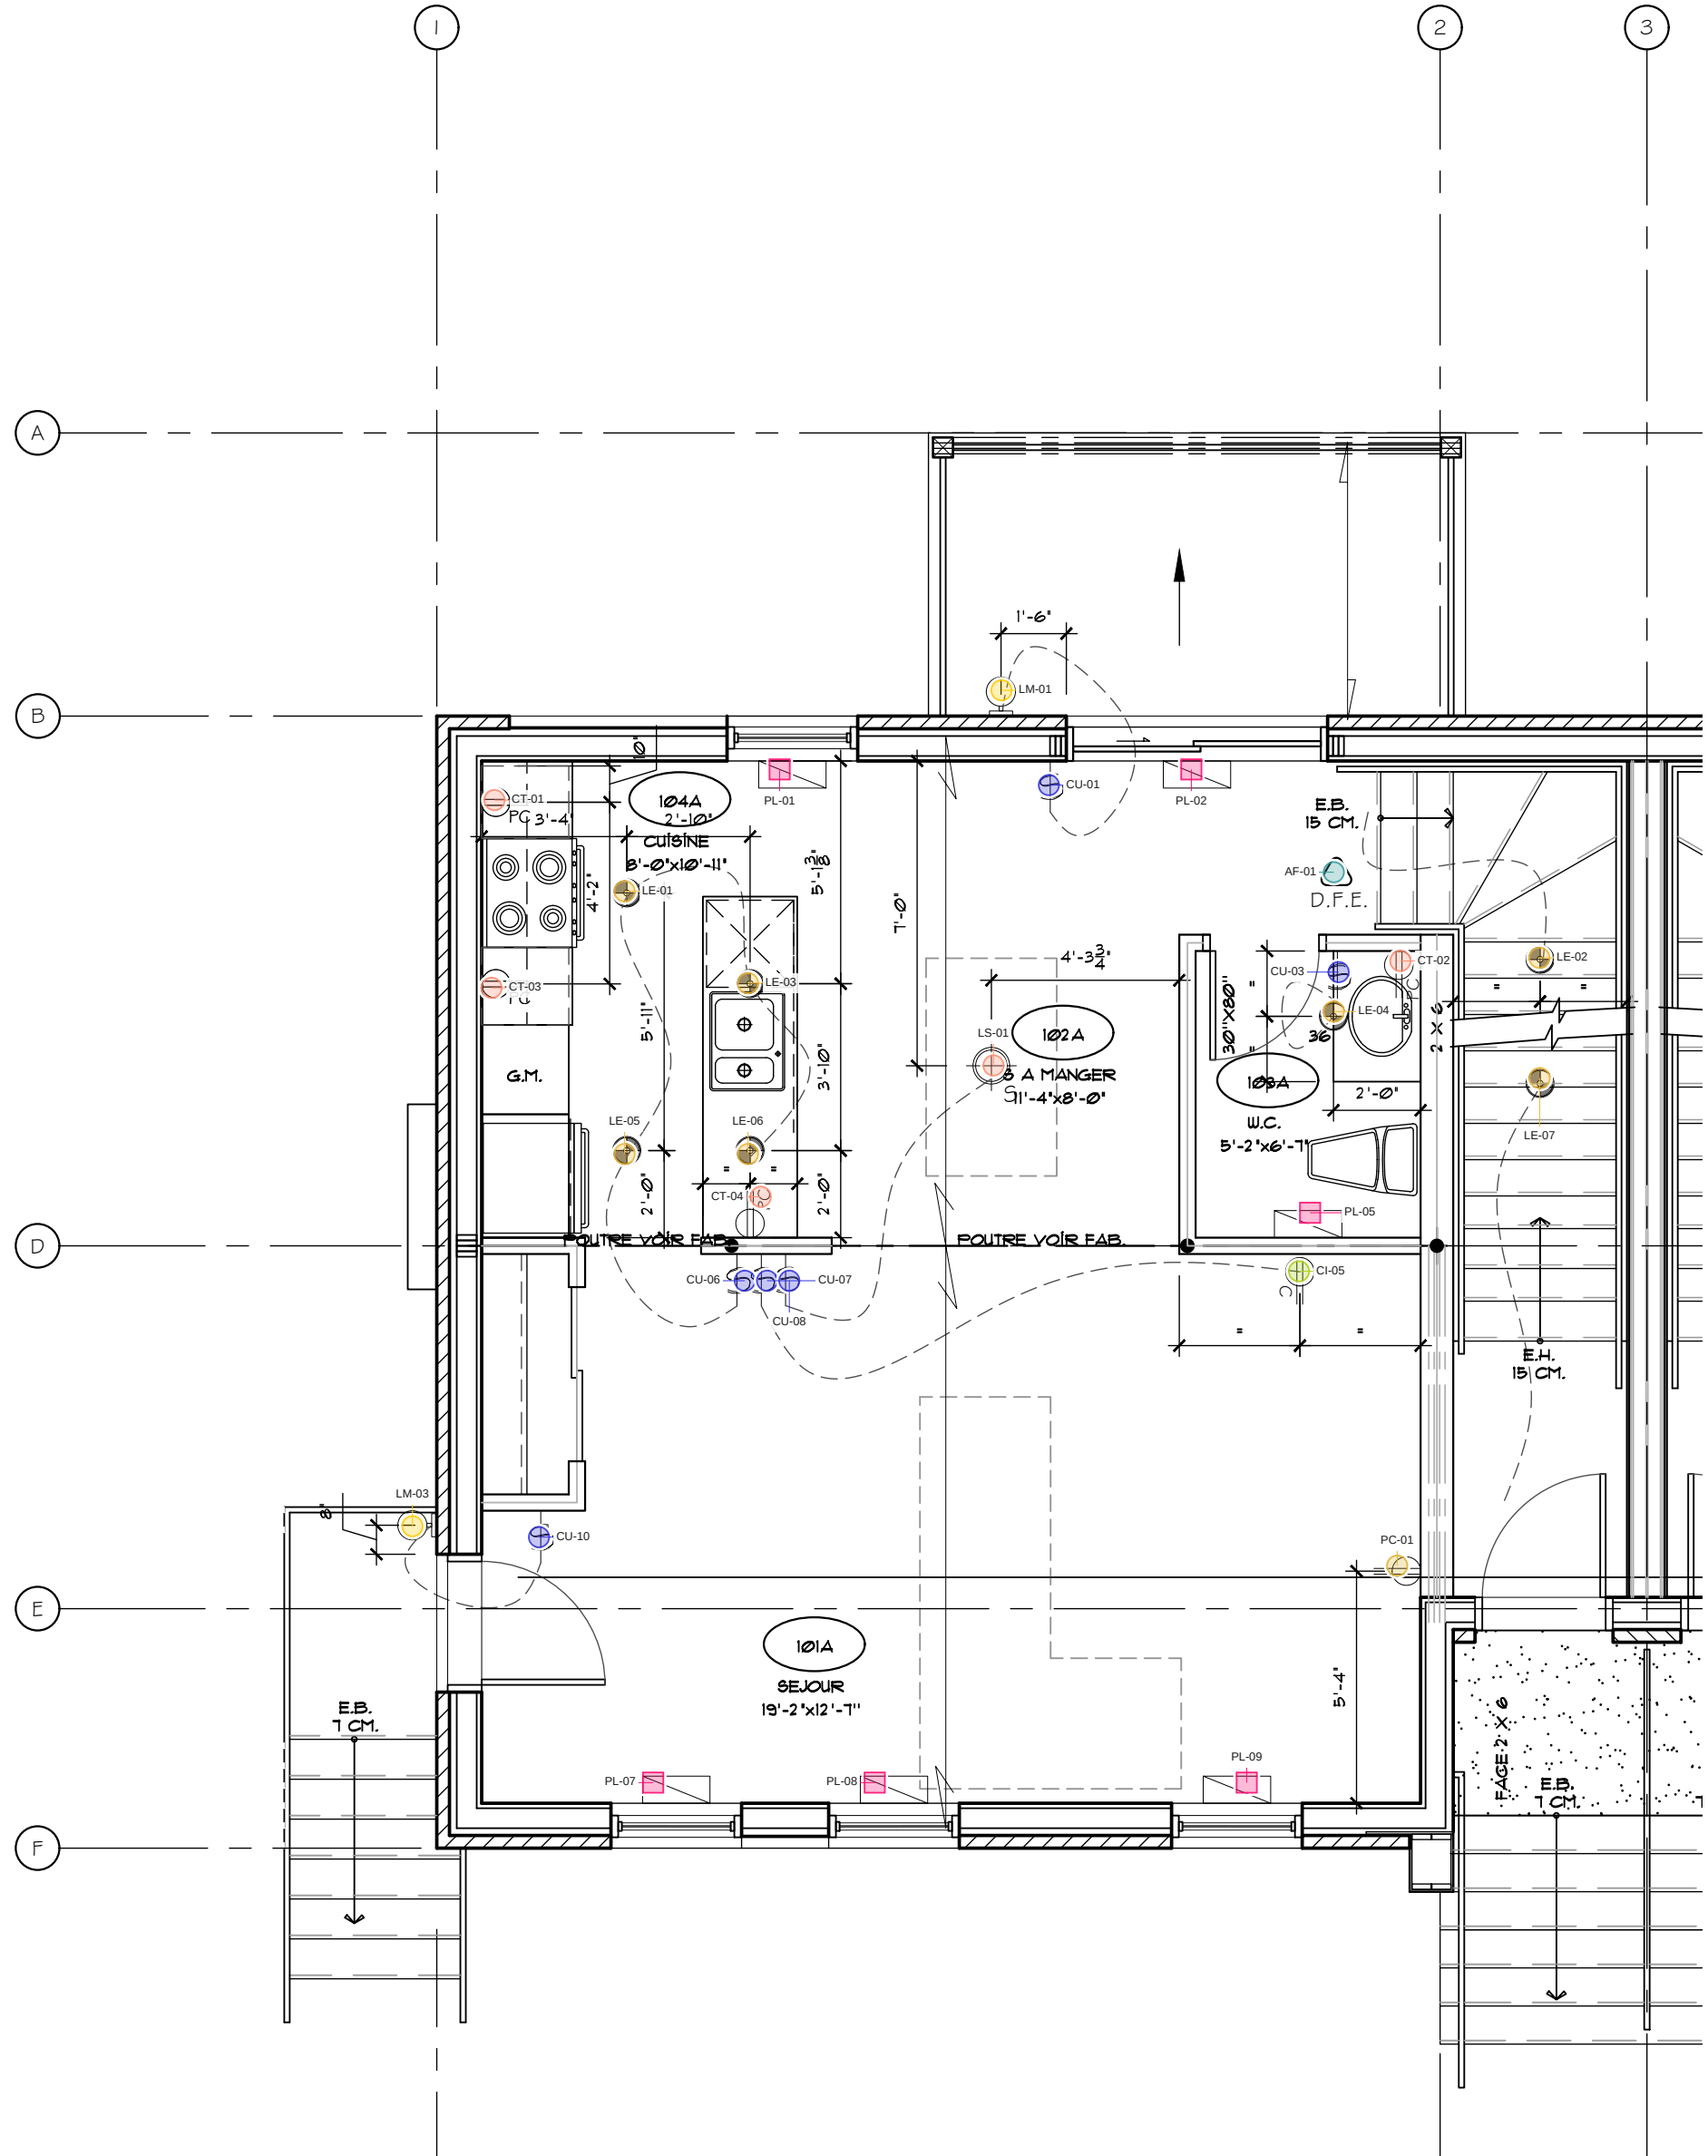

UNITÉ TYPE A - PLAN DU REZ-DE-CHAUSSÉE
NOUVELLE CONDITION
ÉCHELLE 1/4"=1'-0" A-801

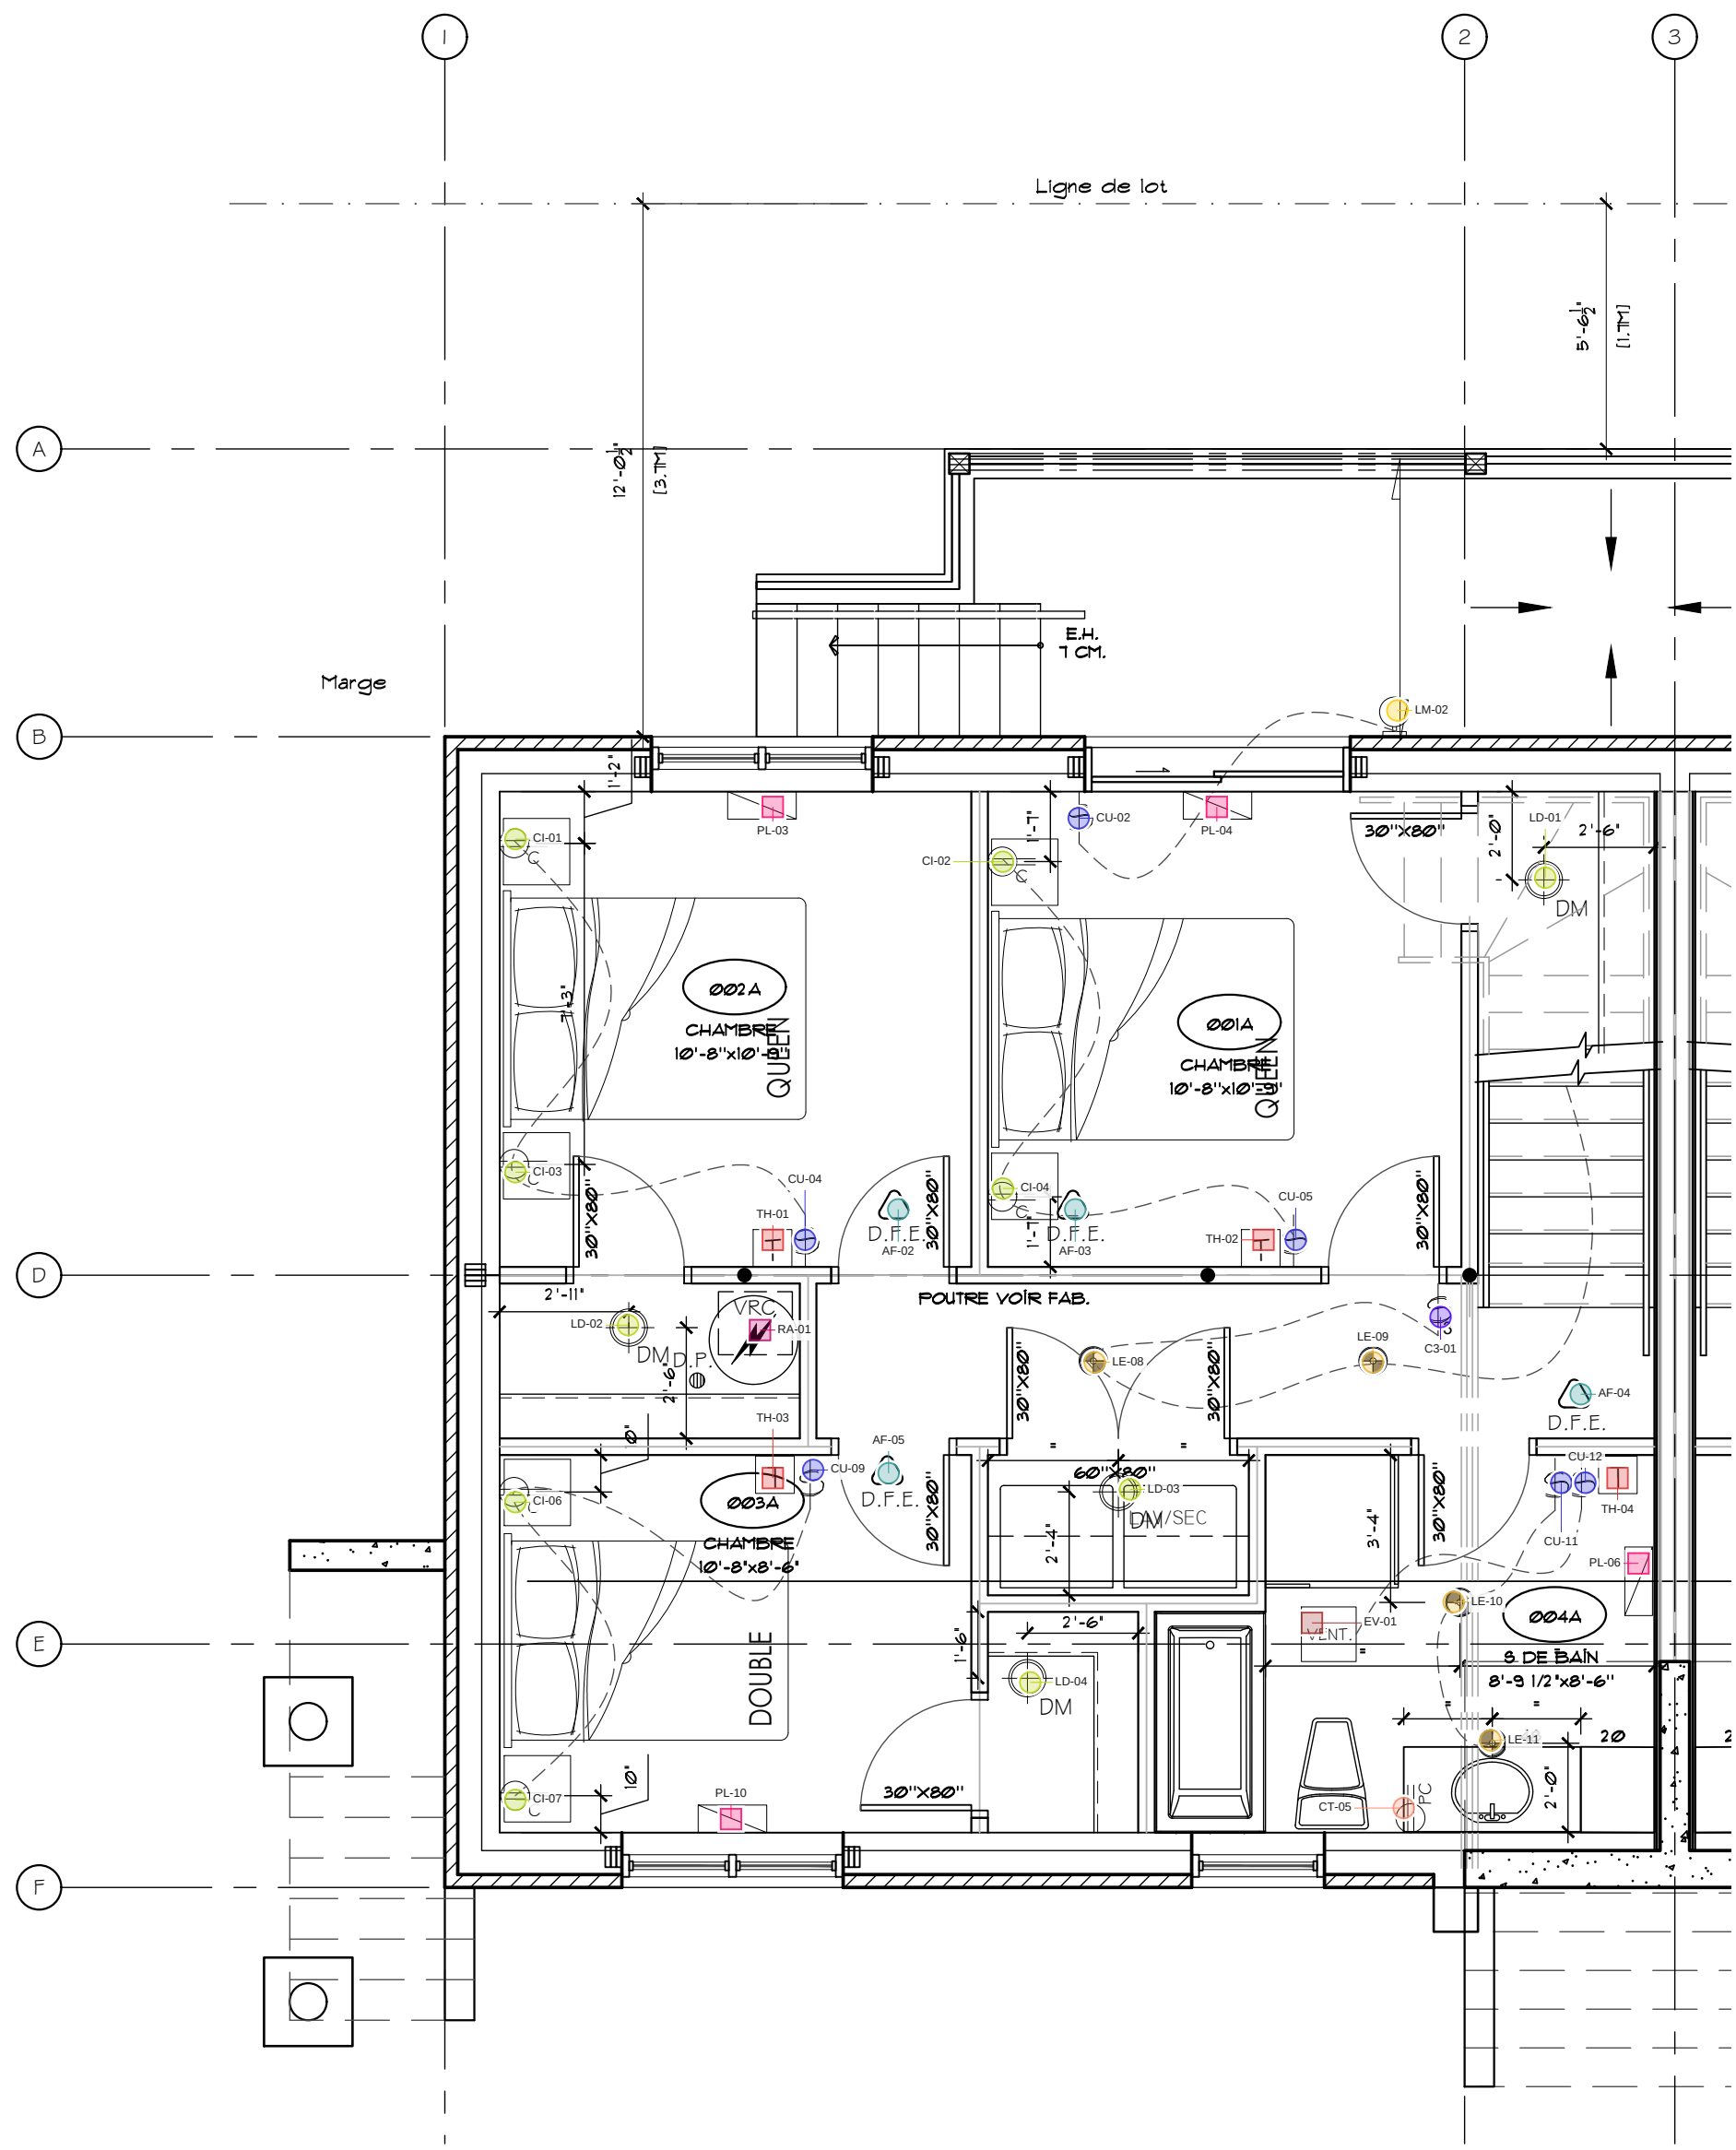

UNITÉ TYPE A - PLAN SOUS-SOL
NOUVELLE CONDITION
ÉCHELLE 1/4"=1'-0" A-801

LÉGENDE D'ÉCLAIRAGE

- ENCASTRÉ SLIM
MODÈLE: XX
CODE: XX
DIM: BLANC
FINI: BLANC
● LUMINAIRE SUSPENDU
MODÈLE: XX
CODE: XX
DIM: BLANC
FINI: BLANC
● PLAFONNIER DETECTEUR DE MOUVEMENT
MODÈLE: JASPER WALL SCONCE
CODE: 4192504
FINI: EBONY
DIM: 4" X 24"

LÉGENDE ÉLECTRIQUE

- PRISE ÉLECTRIQUE HAUTEUR STANDARD
● PRISE ÉLECTRIQUE HAUTEUR COMPTEUR
● PRISE ÉLECTRIQUE SUR CABINET
● PRISE ÉLECTRIQUE CONTRÔLÉ PAR INTERRUPTEUR
● THERMOSTAT
● INTERRUPTEUR HAUTEUR STANDARD
● INTERRUPTEUR 3 VOIES HAUTEUR STANDARD
● VENTILATEUR
MODÈLE À VALIDER AVEC ÉLECTRICIEN, VALIDER SON POSITIONNEMENT SUITE À LA COORDINATION AVEC LES PLANS MÉCANIQUES COMPLET
● PANNÉAU ÉLECTRIQUE
MODÈLE À VALIDER AVEC ÉLECTRICIEN, VALIDER SON POSITIONNEMENT SUITE À LA COORDINATION AVEC LES PLANS MÉCANIQUES COMPLET
● PLINTE ÉLECTRIQUE
WATT À VALIDER PAR ÉLECTRICIEN, SELON LES NORMES EN VIGUEUR

NOTES :

TOUTES LES MESURES ONT ÉTÉ VÉRIFIÉES SUR PLACE EN PRÉSENCE DU CLIENT. LES LOCAUX DU REZ-DE-CHAUSSÉE ET DES ÉTAGES ONT ÉTÉ VALIDÉS.

CES PLANS SONT LA VERSION ABREGÉE POUR LA DEMANDE DE PERMIS ET SOUMISSIONS SEULEMENT ET EN CONFORMITÉ AU CNBQ PR-VIGUEUR 2015 MODIFIÉ.

LE NIVEAU 1000' CORRESPOND AU NIVEAU 16,74m DU PLAN D'ARPEUTEUR (GÉOMÉTRIE) DU 23 MARS 2026.

PLAN PAS POUR CONSTRUCTION

16	EMIS POUR CONSTRUCTION - ESTIMATION FINALE	FSTG 2026/08/26
15	EMIS POUR CONSTRUCTION	FSTG 2026/08/06
14	EMIS COORD/CONSTRUCTION 95% Rev	FSTG 2026/04/30
13	EMIS PERMIS/CONSTRUCTION 95% Rev	FSTG 2026/04/21
12	EMIS PERMIS/CONSTRUCTION 95% Rev	FSTG 2026/04/13
11	EMIS POUR CONSTRUCTION 90%	FSTG 2026/03/30
10	EMIS POUR PERMIS/SOUMISSION REV02	FSTG 2026/03/13
09	EMIS POUR PERMIS/SOUMISSION	FSTG 2026/01/21
08	EMIS POUR PERMIS/SOUMISSION	FSTG 2025/12/11
07	EMIS POUR COMMENTAIRES	FSTG 2025/11/06
06	EMIS POUR COMMENTAIRES	FSTG 2025/10/02
05	EMIS POUR CCU/FI/A	FSTG 2024/10/30
04	EMIS POUR CCU/FI/A	FSTG 2024/10/18
03	EMIS POUR CCU/FI/A	FSTG 2024/10/18
02	EMIS POUR APPROBATION	FSTG 2023/12/14
01	EMIS POUR APPROBATION	FSTG 2023/06/14
No.	REVISION	PAR DATE

PROJET: AGRANDISSEMENT MULTILOGEMENT-ROY
POUR PERMIS
Sorel, QC

CLIENT: IMMEUBLES DE TRACY INC
40 RUE ELIZABETH
SOREL-TRACY, QC
450-701-1998 COURRIEL: dev@tracyrealestate.com
ARCHITECTURE

CONSULTANTS:

STRUCTURE:

MEC/ELEC:

A: No. DU DESSIN
B: No. DE FEUILLE OU LE DESSIN EST DÉTAILLÉ

DESSINE PAR: P.BTG.
VÉRIFIÉ PAR: P.BTG.

TITRE: UNITÉ TYPE A ET TYPE B EN MIROIR

NOUVELLE CONDITION

DOSSIER: 23-2554
DATE: 2024/01
ÉCHELLE: INDICÉE

No.: A-801

NOTE: L'ENTREPRENEUR DEVRA PRENDRE ET VÉRIFIER SUR PLACE LES DIMENSIONS AVANT DE COMMENCER TOUT TRAVAIL.

BORDEREAU MATERIEL - A801

66 reperes sur cette feuille - prescriptions recopiees du devis et du releve verifie.

Les modeles non renseignes restent a preciser. Les circuits divergents exigent une clarification.

ID	Qte	Famille	Modele / type	Prescription du devis	Source / reserve
AF	5	DETECTEUR DE FUMEE D.F.E. (HORS LEGENDE - R-001)	MODELE NON PRECISE	Detecteur de fumee D.F.E. (hors legende - R-001)	A-801 symbole triangle D.F.E. au plan; absent des legendes RESERVES: 5 reperes - modele a confirmer x5 Motifs: RDC Hall escalier ; verifie au zoom 200 dpi ; RESERVE: symbole hors legende electrique - R-001; SS Chambre 002A ; verifie au zoom 200 dpi ; RESERVE: symbole hors legende electrique - R-001; SS Chambre 001A ; verifie au zoom 200 dpi ; RESERVE: symbole hors legende electrique - R-001; SS Corridor ; verifie au zoom 200 dpi ; RESERVE: symbole hors legende electrique - R-001; SS Chambre 003A ; verifie au zoom 200 dpi ; RESERVE: symbole hors legende electrique - R-001
C3	1	INTERRUPTEUR 3 VOIES HAUTEUR STANDARD	MODELE NON PRECISE	Interrupteur 3 voies hauteur standard	A-801 legende electrique ligne 7 RESERVES: 1 reperes - modele a confirmer x1 Motifs: SS Corridor ; verifie au zoom 200 dpi
CI	7	PRISE ELECTRIQUE CONTROLE PAR INTERRUPTEUR	MODELE NON PRECISE	Prise electrique controle par interrupteur C	A-801 legende electrique ligne 4 RESERVES: 7 reperes - modele a confirmer x7 Motifs: SS Chambre 002A ; verifie au zoom 200 dpi; SS Chambre 001A ; verifie au zoom 200 dpi; RDC Salle a manger / sejour ; verifie au zoom 200 dpi ; RESERVE: controlee ou standard a confirmer (*); SS Chambre 003A ; verifie au zoom 200 dpi
CT	5	PRISE ELECTRIQUE HAUTEUR COMPTOIR	MODELE NON PRECISE	Prise electrique hauteur comptoir PC	A-801 legende electrique ligne 2 RESERVES: 5 reperes - modele a confirmer x5 Motifs: RDC Cuisine 104A ; verifie au zoom 200 dpi; RDC W.C. 103A lavabo ; verifie au zoom 200 dpi ; RESERVE: symbole partiellement masque par le lavabo - a revalider (*); RDC Cuisine 104A ilot ; verifie au zoom 200 dpi; SS S. de bain 004A lavabo ; verifie au zoom 200 dpi
CU	12	INTERRUPTEUR HAUTEUR STANDARD	MODELE NON PRECISE	Interrupteur hauteur standard	A-801 legende electrique ligne 6 RESERVES: 12 reperes - modele a confirmer x12 Motifs: RDC Salle a manger 102A ; verifie au zoom 200 dpi; SS Chambre 001A porte ext. ; verifie au zoom 200 dpi; RDC W.C. 103A ; verifie au zoom 200 dpi; SS Chambre 002A ; verifie au zoom 200 dpi; SS Chambre 001A ; verifie au zoom 200 dpi; RDC Cuisine 104A ; verifie au zoom 200 dpi; SS Chambre 003A ; verifie au zoom 200 dpi; RDC Entree sejour ; verifie au zoom 200 dpi; SS S. de bain 004A ; verifie au zoom 200 dpi
EV	1	VENTILATEUR	MODELE NON PRECISE	MODELE A VALIDER AVEC ELECTRICIEN; POSITIONNEMENT A VALIDER SUITE A LA COORDINATION MECANIQUE	A-801 legende electrique ligne 8 RESERVES: 1 reperes - modele a confirmer x1 Motifs: SS S. de bain 004A ; verifie au zoom 200 dpi
LD	4	PLAFONNIER DETECTEUR DE MOUVEMENT	MODELE NON PRECISE	FINIS: BLANC	A-801 legende d'eclairage ligne 3 RESERVES: 4 reperes - modele a confirmer x4 Motifs: SS Hall escalier ; verifie au zoom 200 dpi; SS Rangement D.P. ; verifie au zoom 200 dpi; SS Lav./sech. ; verifie au zoom 200 dpi; SS Rangement ; verifie au zoom 200 dpi
LE	11	ENCASTRE SLIM	MODELE: XX CODE: XX	FINI: BLANC	A-801 legende d'eclairage ligne 1 RESERVES: 11 reperes Motifs: RDC Cuisine 104A ; verifie au zoom 200 dpi; RDC Escalier ; verifie au zoom 200 dpi; RDC Cuisine 104A ilot ; verifie au zoom 200 dpi; RDC W.C. 103A ; verifie au zoom 200 dpi; SS Corridor ; verifie au zoom 200 dpi; SS S. de bain 004A ; verifie au zoom 200 dpi; SS S. de bain 004A lavabo ; verifie au zoom 200 dpi
LM	3	APPLIQUE MURALE - SALLE D'ATTENTE	UNION LIGHTING JASPER WALL SCONCE CODE: 4192584	FINI: EBONY DIM: 4 X 24	A-801 legende d'eclairage ligne 4 RESERVES: 3 reperes Motifs: RDC Exterieur arriere ; verifie au zoom 200 dpi; SS Exterieur sortie sous-sol ; verifie au zoom 200 dpi; RDC Exterieur entree ; verifie au zoom 200 dpi
LS	1	LUMINAIRE SUSPENDU	MODELE NON PRECISE	Luminaire suspendu (legende d'eclairage)	A-801 legende d'eclairage ligne 2 RESERVES: 1 reperes - modele a confirmer x1 Motifs: RDC Salle a manger 102A ; verifie au zoom 200 dpi
PC	1	PRISE ELECTRIQUE HAUTEUR STANDARD	MODELE NON PRECISE	Prise electrique hauteur standard	A-801 legende electrique ligne 1 RESERVES: 1 reperes - modele a confirmer x1 Motifs: RDC Sejour 101A ; verifie au zoom 200 dpi ; RESERVE: type standard a confirmer (*)
PL	10	PLINTHE ELECTRIQUE	MODELE NON PRECISE	WATT A VALIDER PAR ELECTRICIEN SELON LES NORMES EN VIGUEURES	A-801 legende electrique ligne 10 RESERVES: 10 reperes - modele a confirmer x10 Motifs: RDC Cuisine 104A ; verifie au zoom 200 dpi; RDC Salle a manger 102A ; verifie au zoom 200 dpi; SS Chambre 002A ; verifie au zoom 200 dpi; SS Chambre 001A ; verifie au zoom 200 dpi; RDC W.C. 103A ; verifie au zoom 200 dpi; SS S. de bain 004A ; verifie au zoom 200 dpi; RDC Sejour 101A ; verifie au zoom 200 dpi; SS Chambre 003A ; verifie au zoom 200 dpi
RA	1	RACCORD DIRECT VRC (HORS LEGENDE - R-001)	MODELE NON PRECISE	Raccord direct VRC (hors legende - R-001)	A-801 symbole VRC sous-sol; absent des legendes RESERVES: 1 reperes - modele a confirmer x1 Motifs: SS Rangement D.P. ; verifie au zoom 200 dpi ; RESERVE: symbole hors legende electrique - R-001
TH	4	THERMOSTAT	MODELE NON PRECISE	Thermostat T	A-801 legende electrique ligne 5 RESERVES: 4 reperes - modele a confirmer x4 Motifs: SS Chambre 002A ; verifie au zoom 200 dpi; SS Chambre 001A ; verifie au zoom 200 dpi; SS Chambre 003A ; verifie au zoom 200 dpi; SS S. de bain 004A ; verifie au zoom 200 dpi

Notes de reserve source

R-001 - A-801 : symboles D.F.E. (triangle, 5) et VRC (1) présents au plan, absents des légendes électrique et d'éclairage - relevés sous libellé "hors légende", portée A PRECISER ; avertisseur autonome ou détecteur relié au réseau : non tranché par le plan.
R-002 - A-801 RDC W.C. 103A : prise comptoir au lavabo partiellement masquée par le dessin du lavabo - identification à revalider (*).
R-003 - A-801 RDC séjour 101A : prise classée hauteur standard - type à confirmer (*).
R-004 - A-801 RDC sous la poutre (salle à manger / séjour) : prise contrôlée par interrupteur ou standard - glyphe "C" ambigu (*).
R-005 - A-801 : PANNEAU ÉLECTRIQUE (P.E.) et PRISE ÉLECTRIQUE SUR CABINET (M) figurent dans la légende électrique mais aucun symbole n'est dessiné sur les deux plans (RDC, sous-sol) - vérifié tuile par tuile ; non relevés.
R-006 - A-801 : plan électrique "schématique, à titre de coordination et d'information seulement" (note *) : case MÉC./ÉLEC. vide (pas d'ingénieur électrique) ; tampon "PLAN PAS POUR CONSTRUCTION".
R-007 - A-801 : quantités = une unité type A ; l'unité type B est en miroir (titre de la feuille) - aucune multiplication par le nombre d'unités sur cette feuille (renvoi au nombre d'unités du projet, 59 logements selon AN25004E, à confirmer).
R-008 - A-801 : aucun circuit ni puissance (W) indiqué au plan ; plinthes "WATT A VALIDER PAR ÉLECTRICIEN" (légende).
R-009 - Sources : aucun devis électrique dans 01_SOURCES ; la directive dc03 porte sur l'entrée électrique (3030/3020), hors A-801 - aucune prescription ajoutée.