


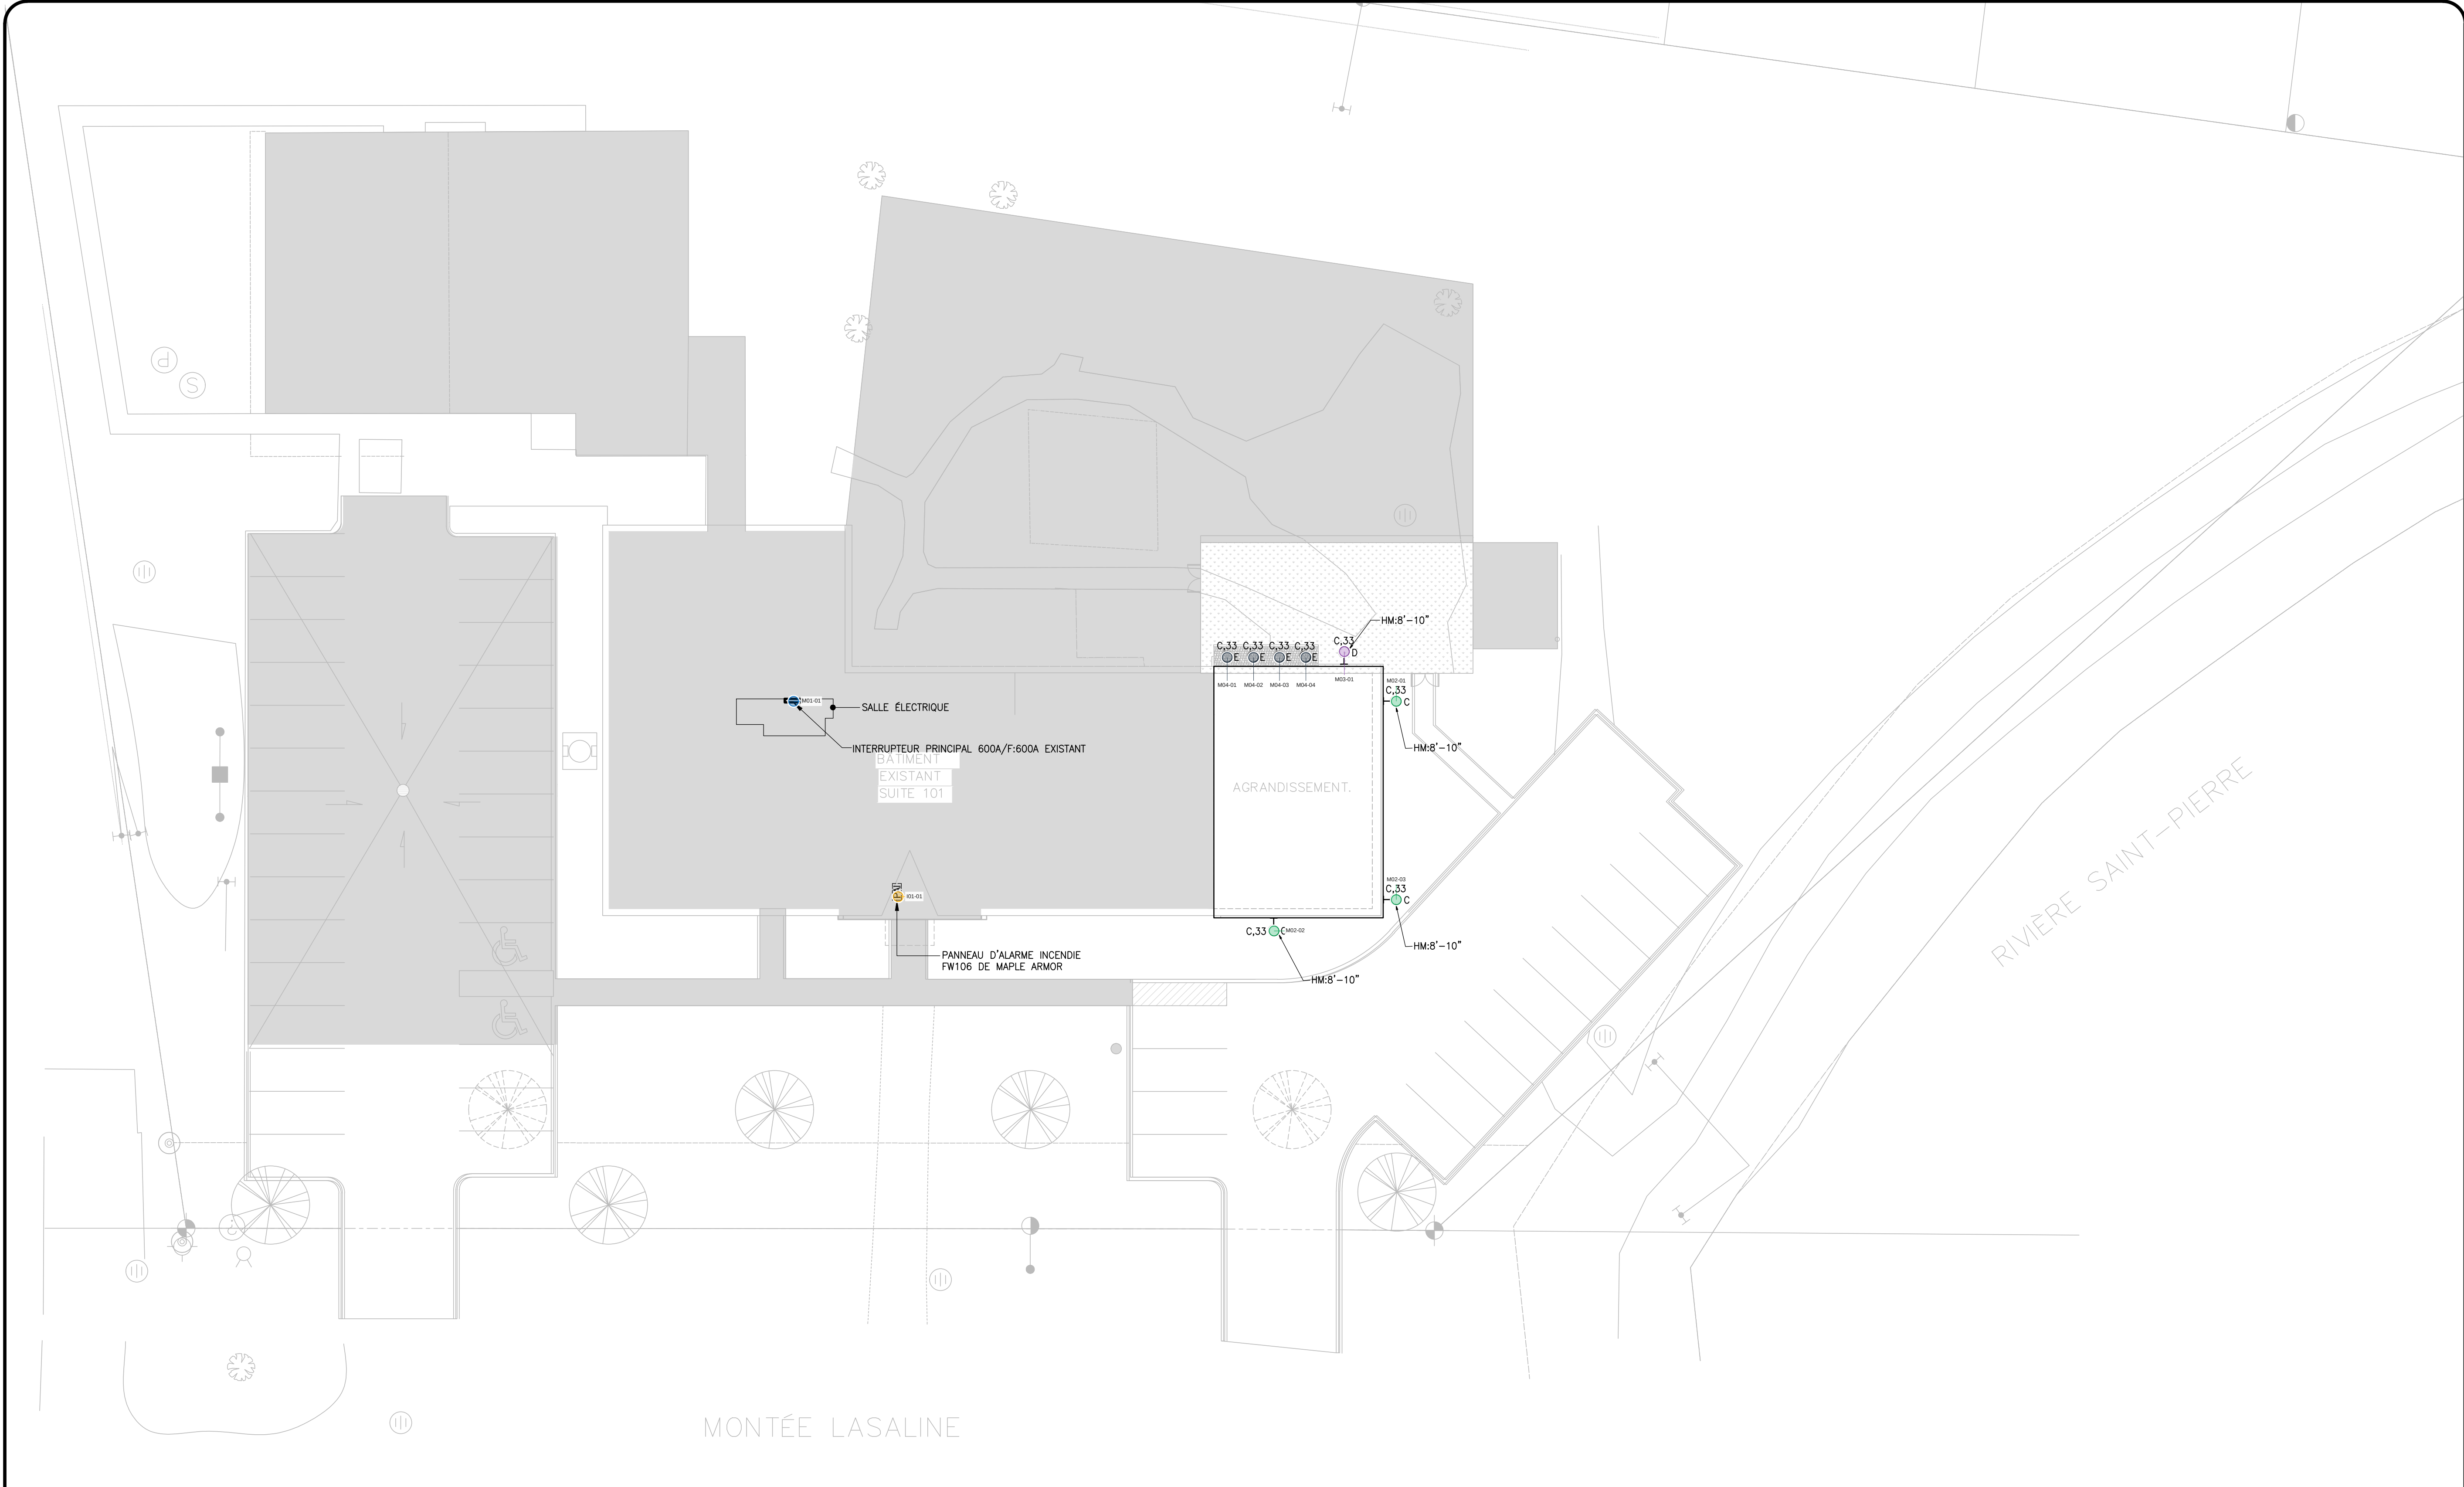

LOCALISATION
ÉCHELLE 1/16" = 1'-0"

RELEVÉ E201 - MATERIEL		10 repères / 5 familles / RES 10		Calques activables; modèles, prescriptions et reserves completes page 2	
RES = reserve source, modele, position, portee ou reconciliation; * = identification a revalider					
I01 PANNEAU D ALARME INCENDIE FW106 DE MAPLE ARMOR 1 / R1	M02 LUMINAIRE EXTERIEUR TYPE C MURAL (C 33) 3 / R3	M04 LUMINAIRE EXTERIEUR TYPE E (CIRCUIT C 33) 4 / R4			
M01 INTERRUPTEUR PRINCIPAL 600 A / F 600 A EXISTANT 1 / R1	M03 LUMINAIRE EXTERIEUR TYPE D SUR PIED MURAL (C 33) 1 / R1				
Quantites source et renvois; voir bordereau detaille.					

PERMIS ET SOUMISSION
7 MAI 2026
CE PLAN NE DOIT PAS SERVIR À LA CONSTRUCTION

plan clé :

No. 8			
No. 7			
No. 6			
No. 5			
No. 4			
No. 3			
No. 2	PERMIS ET SOUMISSION	26-05-07	D.R.P.
No. 1	COORDINATION	26-02-13	D.R.P.
No.	Révisions:	Date:	Par:

ÉMISSIONS

architecte:

ingénieur en **structure, civil, mécanique et électricité**

INGÉNIEURS
**LAROCQUE
COURNOYER**

DRUMMONDVILLE
T. 819 477-0191
LA TUQUE
T. 819 876-7038
SAINT-AMBROISE-
DE-KILDARE
T. 450 752-1106
admin@lc-ing.com
LC-ING.COM

ingénieur en

sceux :

client :

26 MONTÉE LASALINE,
ST-CONSTANT, QC, J5A 2A9

projet :

AGRANDISSEMENT
CPE SOLEIL SOURIANT
26 MONTÉE LASALINE,
ST-CONSTANT

titre :

LOCALISATION

dessiné par : P.ST-AMANT,tech	contrat no. : 25-0075	page : E201
conçu par : P.ST-AMANT,tech	date : 2025-12-15	
vérifié par : D. ROYER-PARENT,ing	échelle: INDIQUÉE	

ÉLECTRICITÉ