
0" 6" 12"

NOTE GÉNÉRALE:

1. Sauf indications contraire, tous les équipements sont existants à conserver.
2. L'entrepreneur en électricité sera responsable d'enlever tout autre équipement non montré en plan lorsque des murs ou des plafonds sont pour démolition. Retirée l'alimentation de ces équipements jusqu'au panneau et la composante à conserver.
3. L'entrepreneur en électricité doit vérifier le bon fonctionnement des prises électrique existante montré aux plans.

NOTE SPÉCIFIQUE:

1. Services et data intégrés au meuble, branchement via boîtes de jonction par des câbles sortant du plancher. À énlever et à refaire dans les nouveaux mobiliérs . Lorsque possible, les câbles et les circuits doivent être conservés.
2. Systéme barrier anti-vol, branchement avec boîte de jonction encastre dans le plancher et conduits EMT de 35mm sous plancher pour chaque porte.

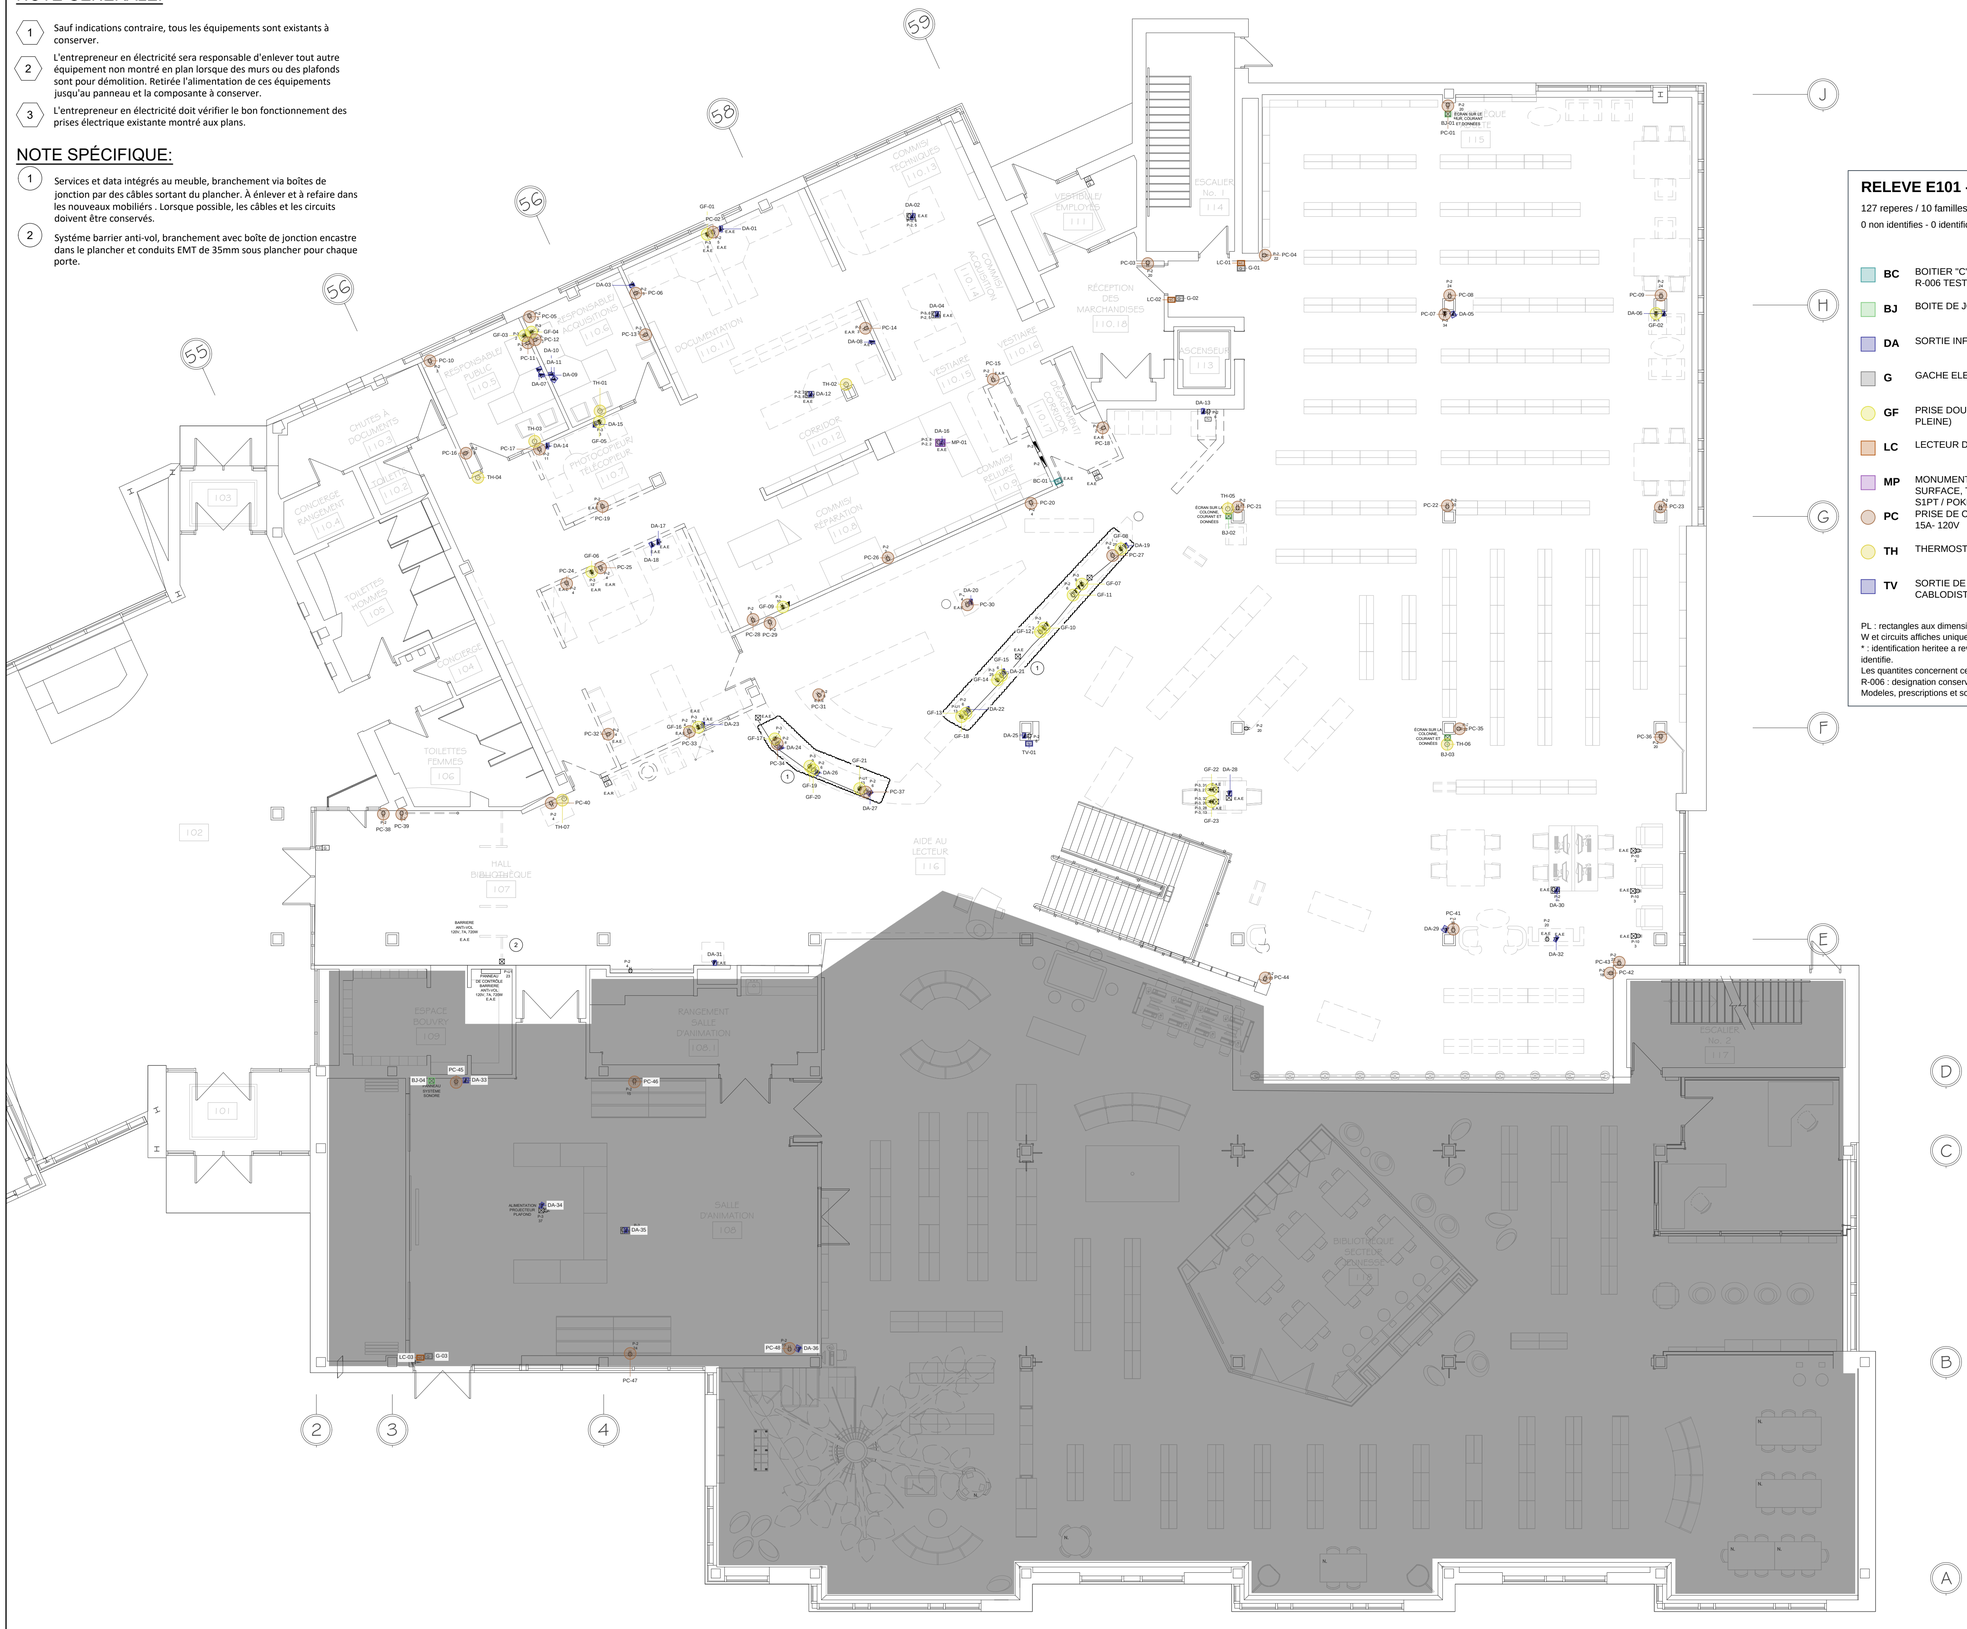

RELEVE E101 - MATERIEL

127 reperes / 10 familles / calques activables

0 non identifies - 0 identifications a revalider (*)

BC	BOITIER "C" (HORS LEGENDE - R-006 TEST-E201)	1
BJ	BOITE DE JONCTION	4
DA	SORTIE INFORMATIQUE/AUDIO	36
G	GACHE ELECTRIQUE	3
GF	PRISE DOUBLE DDFT (MOITIE PLEINE)	23
LC	LECTEUR DE CARTE	3
MP	MONUMENT PLANCHER SURFACE, TYPE HUBBELL S1PT / POKE THROUGH	1
PC	PRISE DE COURANT DOUBLE 15A- 120V	48
TH	THERMOSTAT	7
TV	SORTIE DE CABLODISTRIBUTION AU MUR	1

PL : rectangles aux dimensions graphiques du plan.
W et circuits affiches uniquement si verifies.
* : identification heritee a revalider ; NI : materiel non identifie.
Les quantites concernent cette feuille.
R-006 : designation conservee au registre des reserves.
Modeles, prescriptions et sources : bordereau page 2.

experts conseils

| HF Experts-Conseils - Mécanique et électricité du bâtiment |
| 7375A rue Beaubien Est, Anjou, QC, H1M 3R5 |
| (514).655.9694 |
| hfec-ing.com |

No.	DATE:	ÉMISSION:
01	2026-09-16	ÉMIS POUR APPEL D'OFFRE
A	2026-08-28	ÉMIS POUR COORDINATION PRÉLIM.

SCEAU:

INGÉNIEURS Hamid Haddad 026461 QUÉBEC
2026-09-16

ARCHITECTE:

CLIENT:

Brossard

PROJET:

TECHNOLOGIE RFID

BIBLIOTHÈQUE GEORGETTE-LEPAGE - TRAVAUX D'AMÉNAGEMENT DU REZ-DE-CHAUSSÉE ET DE L'ÉTAGE

NO APPEL D'OFFRES : SP-GTER-26-0080

TITRE DU PLAN

SERVICES EXISTANT/DÉMOLITION REZ-DE-CHAUSSÉE

No DE DOSSIER	26-29		
DESSINÉ PAR:	P. ELISEEV		
PRÉPARÉ PAR:	P. ELISEEV		
VÉRIFIÉ PAR:	R. HADDAD, Ing.		
ÉCHELLE:	1:100	FORMAT	841X594
DATE:	JUILLET 2026		

PLAN E-101

BORDEREAU MATERIEL - E101

127 reperes sur cette feuille - prescriptions recopiees du devis et du releve verifie.

Les modeles non renseignes restent a preciser. Les circuits divergents exigent une clarification.

ID	Qte	Famille	Modele / type	Prescription du devis	Source / reserve
BC	1	BOITIER "C" (HORS LEGENDE - R-006 TEST-E201)	C MODELE NON PRECISE	BOITIER "C" (hors légende - R-006 TEST-E201)	E-001 légende ; bloc S218
BJ	4	BOITE DE JONCTION	ET 20 P-2; T ET LA 24 P-2; T ET LA 22 P-2 MODELE NON PRECISE	BOITE DE JONCTION	E-001 légende ; bloc S107
DA	14	SORTIE INFORMATIQUE/AUDIO	P-2 5 P-3; 4 5; 6 5; 3 P-3; 2 8; P-2 4; 12 P-3 P-2; P-2 22; 20 MODELE NON PRECISE	SORTIE INFORMATIQUE/AUDIO	E-001 légende ; bloc S006
DA	22	SORTIE INFORMATIQUE/AUDIO	P-2 5; P-3 34; TV P-2 6; P-2 11 T; P-3 3 T; P-3 25 P-2 6; 6 P-2 P-3 25; 6 P-2 P-U1 13; 6 P-2 7; 6 P-2 9 P-3; 6 13 P-2 P-U1; 35 P-3; P-3 37; P-2 15; 15 P-2 MODELE NON PRECISE	SORTIE INFORMATIQUE/AUDIO	E-001 légende ; bloc S006
G	3	GACHE ELECTRIQUE	G LC MODELE NON PRECISE	GÂCHE ÉLECTRIQUE	E-001 légende ; bloc S290
GF	4	PRISE DOUBLE DDFT (MOITIE PLEINE)	P-3 P-2 6 5; 12 P-3 P-2 4; 31 27 32 20 28; 20 32 28 13 27 31 MODELE NON PRECISE	PRISE DOUBLE DDFT (moitié pleine)	E-001 légende ; bloc S158
GF	18	PRISE DOUBLE DDFT (MOITIE PLEINE)	P-3 34; P-3 2 P-2 3 P-3 2 P-2 3; P-3 2 P-2 3 3 P-3 P-2 2 P-2; P-3 T 3; 9 P-3 P-2 6; 25 P-3 P-2 6; 10 P-3; 7 P-3 P-2 14; 6 P-2 9; P-2 14 7 P-3; P-U1 6 13 P-2; 25 P-3 6 P-2; 6 P-3 25 P-2; 7 P-2 P-3 6; 13 P-U1 6 P-2; P-2 9 6 P-3; 13 P-U1 P-2 6 MODELE NON PRECISE	PRISE DOUBLE DDFT (moitié pleine)	E-001 légende ; bloc S158
GF	1	PRISE DOUBLE DDFT (MOITIE PLEINE)	P-3 12 P-2 4 MODELE NON PRECISE	PRISE DOUBLE DDFT (moitié pleine)	E-001 légende ; bloc S158
LC	3	LECTEUR DE CARTE	LC G MODELE NON PRECISE	LECTEUR DE CARTE	E-001 légende ; bloc S219
MP	1	MONUMENT PLANCHER SURFACE, TYPE HUBBELL S1PT / POKE THROUGH	2 8 MODELE NON PRECISE	MONUMENT PLANCHER SURFACE, TYPE HUBBELL S1PT / POKE THROUGH	E-001 légende ; bloc S128
PC	37	PRISE DE COURANT DOUBLE 15A- 120V	P-2 20 ET; P-2 20; P-2 22; P-2 3 P-3 2 P-3; P-2 5; P-3 34; 24 P-2; P-2 3; P-2 3 P-3 2 P-2 2 3 P-3; P-2 3 2 P-2 P-3 3 P-3; P-2 T 11; P-2 4; 24 P-2 T LA; 2 P-2; 6 25 P-2 P-3; P-2 6 7 P-3; P-2 22 LA; 6 13 P-2 P-U1; P-2 4 P-2; P-2 T 4; 35 P-3; P-2 18 22 P-2; 22 P-2 P-2; P-2 15; 15 P-2 MODELE NON PRECISE	PRISE DE COURANT DOUBLE 15A- 120V	E-001 légende ; bloc S020
PC	7	PRISE DE COURANT DOUBLE 15A- 120V	P-2 P-3 5 6; 4 P-2; P-2 4; P-2 6; 4 12 P-2 P-3 MODELE NON PRECISE	PRISE DE COURANT DOUBLE 15A- 120V	E-001 légende ; bloc S020
PC	4	PRISE DE COURANT DOUBLE 15A- 120V	P-3 3; 2 P-2; P-2 2; P-2 4 P-3 12 MODELE NON PRECISE	PRISE DE COURANT DOUBLE 15A- 120V	E-001 légende ; bloc S020
TH	7	THERMOSTAT	T P-3; T; T P-2; T LA ET P-2 24; T ET LA; T P-2 4 MODELE NON PRECISE	THERMOSTAT	E-001 légende ; bloc S323
TV	1	SORTIE DE CABLODISTRIBUTION AU MUR	TV P-2 6 MODELE NON PRECISE	SORTIE DE CÂBLODISTRIBUTION AU MUR	E-001 légende ; bloc S293


0" 6" 12"

NOTE GÉNÉRALE:

1. Sauf indications contraire, tous les équipements sont existants à conserver.
2. L'entrepreneur en électricité sera responsable d'enlever tout autre équipement non montré en plan lorsque des murs ou des plafonds sont pour démolition. Retirée l'alimentation de ces équipements jusqu'au panneau et la composante à conserver.
3. L'entrepreneur en électricité doit vérifier le bon fonctionnement des prises électrique existante montré aux plans.

NOTE SPÉCIFIQUE:

1. Services et data intégrés au meuble, branchement via boîtes de jonction par des câbles sortant du plancher. À énlever et à refaire en utilisant des prises murales ou de plancher standard. Lorsque possible, les câbles et les circuits doivent être conservés.

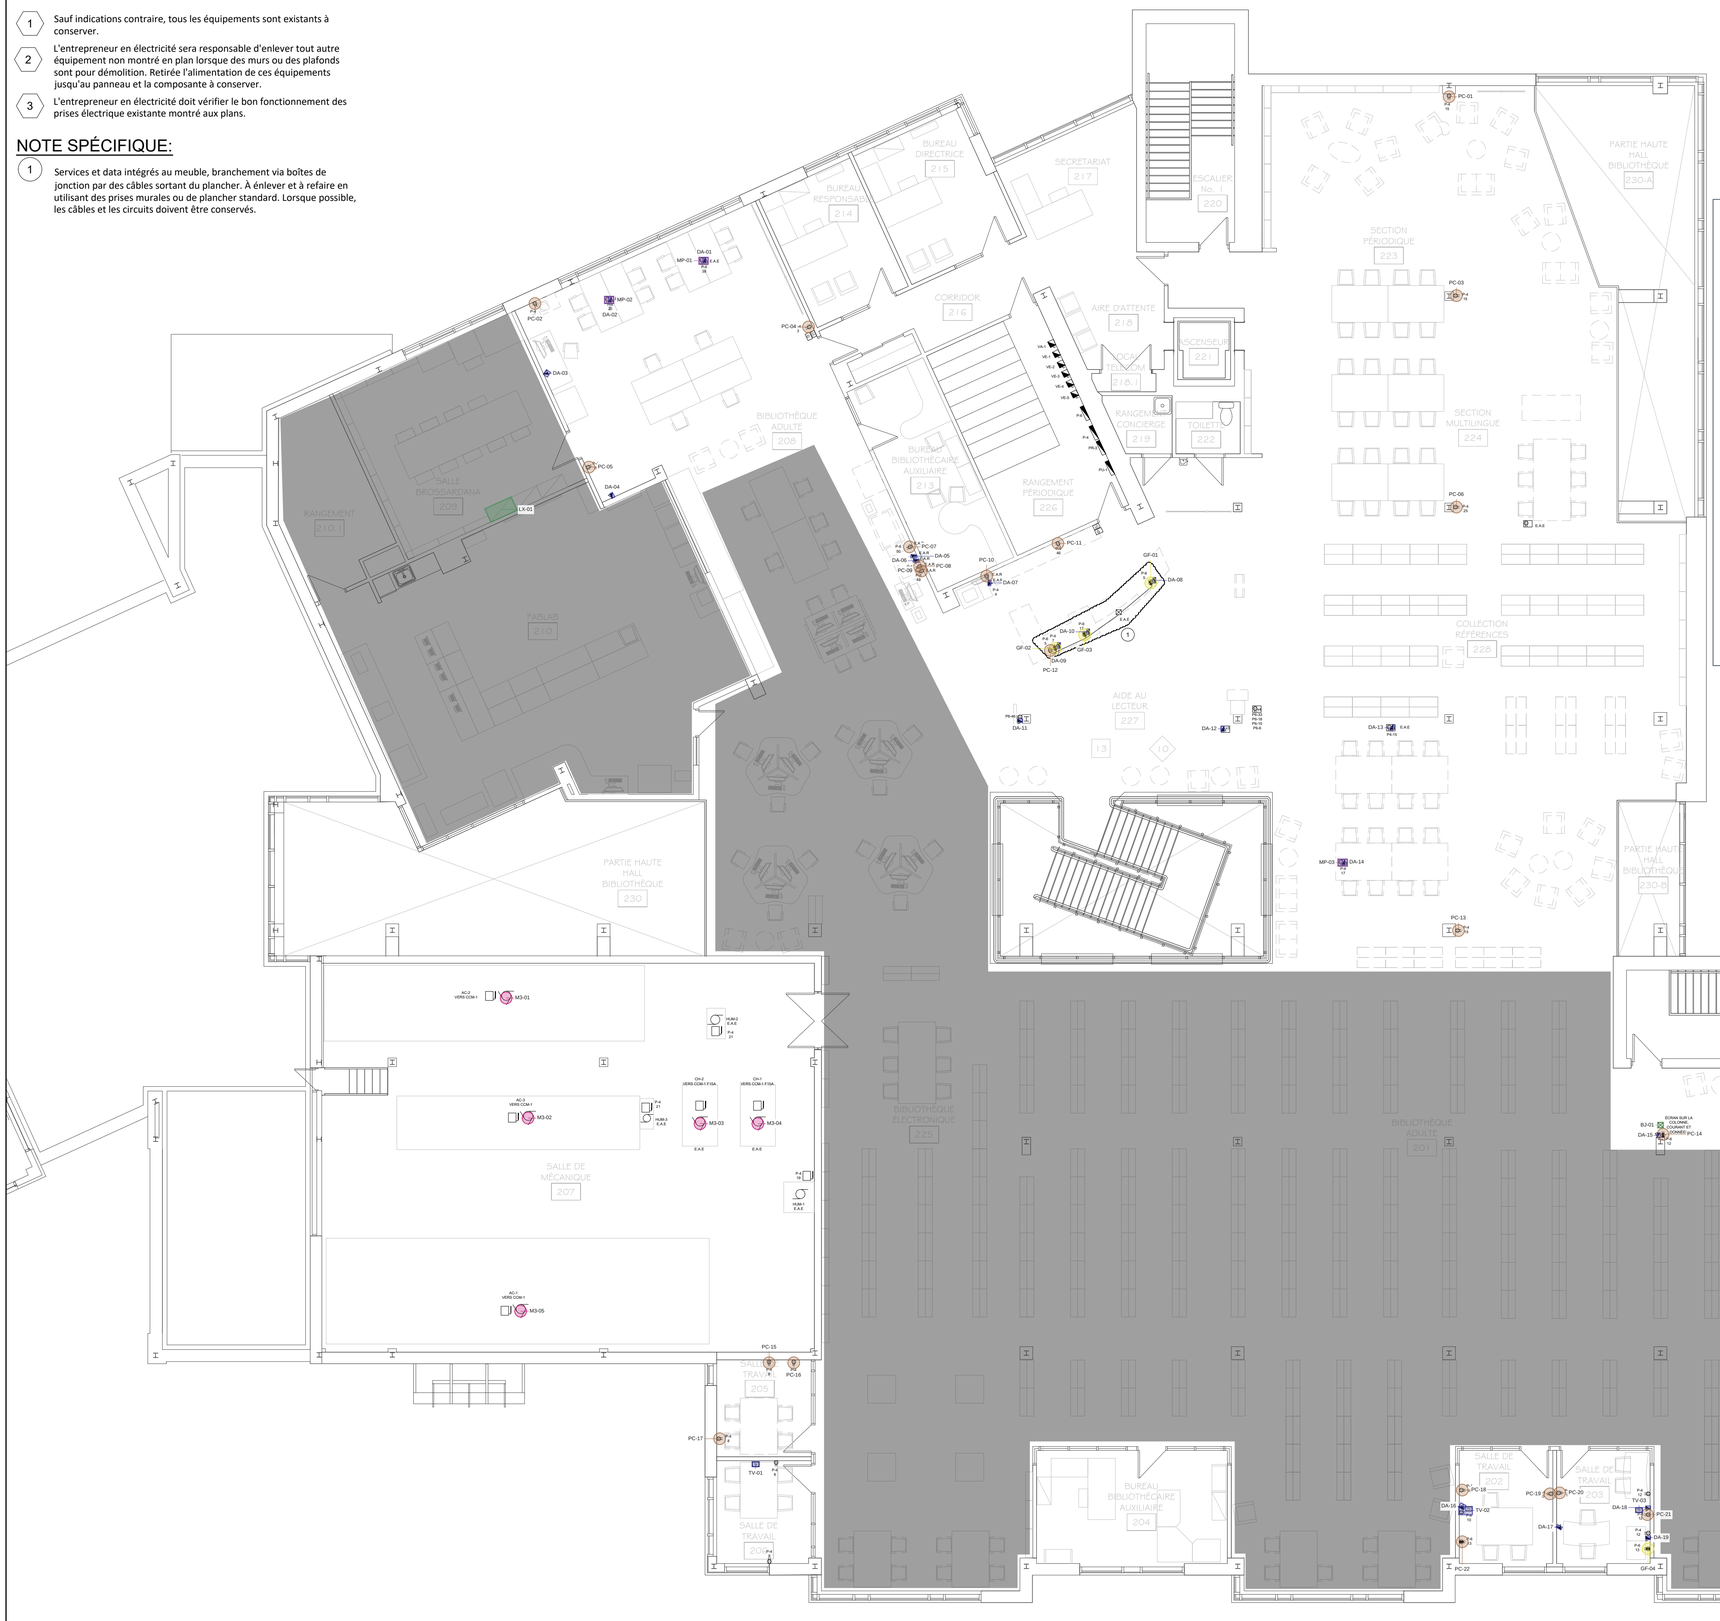

RELEVE E102 - MATERIEL

58 reperes / 8 familles / calques activables

0 non identifies - 0 identifications a revalider (*)

BJ	BOITE DE JONCTION	1
DA	SORTIE INFORMATIQUE/AUDIO	19
GF	PRISE DOUBLE DDFT (MOITIE PLEINE)	4
LX	APPAREIL D'ECLAIRAGE 'X4'	1
M3	MOTEUR TRIPHASE, PUISSANCE SELON LES INDICATIONS	5
MP	MONUMENT PLANCHER SURFACE, TYPE HUBBELL S1PT / POKE THROUGH	3
PC	PRISE DE COURANT DOUBLE 15A- 120V	22
TV	SORTIE DE CABLODISTRIBUTION AU MUR	3

PL : rectangles aux dimensions graphiques du plan.
W et circuits affiches uniquement si verifies.
* : identification heritee a revalider ; NI : materiel non identifie.
Les quantites concernent cette feuille.
Modeles, prescriptions et sources : bordereau page 2.

experts conseils

| HF Experts-Conseils - Mécanique et électricité du bâtiment |
| 7375A rue Beaubien Est, Anjou, QC, H1M 3R5 |
| (514).655.9694 |
| hfec-ing.com |

No.	DATE:	ÉMISSION:
01	2026-09-16	ÉMIS POUR APPEL D'OFFRE
A	2026-08-28	ÉMIS POUR COORDINATION PRÉLIM.

SCEAU:

INGÉNIEURS Hanni Haddad 5026451 QUÉBEC
2026-09-16

ARCHITECTE:

CLIENT:

Brossard

PROJET:

TECHNOLOGIE RFID

BIBLIOTHÈQUE GEORGETTE-LEPAGE - TRAVAUX D'AMÉNAGEMENT DU REZ-DE-CHAUSSÉE ET DE L'ÉTAGE

NO APPEL D'OFFRES : SP-GTER-26-0080

TITRE DU PLAN

SERVICES EXISTANT/DÉMOLITION 2E ÉTAGE

No DE DOSSIER	26-29		
DESSINÉ PAR:	P. ELISEEV		
PRÉPARÉ PAR:	P. ELISEEV		
VÉRIFIÉ PAR:	R. HADDAD, Ing.		
ÉCHELLE:	1:100	FORMAT	841X594
DATE:	JUILLET 2026		

PLAN E-102

BORDEREAU MATERIEL - E102

58 reperes sur cette feuille - prescriptions recopiees du devis et du releve verifie.

Les modeles non renseignes restent a preciser. Les circuits divergents exigent une clarification.


ID	Qte	Famille	Modele / type	Prescription du devis	Source / reserve
BJ	1	BOITE DE JONCTION	P-6 12 MODELE NON PRECISE	BOITE DE JONCTION	E-001 légende ; bloc S107
DA	3	SORTIE INFORMATIQUE/AUDIO	P-6 38; P-6 25 MODELE NON PRECISE	SORTIE INFORMATIQUE/AUDIO	E-001 légende ; bloc S006
DA	13	SORTIE INFORMATIQUE/AUDIO	P-6 5; 7 P-4 P-6 5; 17 P-6; P-4 17; P-6 12; TV P-4 10 10; P-4 TV 12 12 P-4; 12 P-4 P-6 13 MODELE NON PRECISE	SORTIE INFORMATIQUE/AUDIO	E-001 légende ; bloc S006
DA	3	SORTIE INFORMATIQUE/AUDIO	P-6 50 P-6 48; P-6 48 P-6 50; P-4 4 MODELE NON PRECISE	SORTIE INFORMATIQUE/AUDIO	E-001 légende ; bloc S006
GF	4	PRISE DOUBLE DDFT (MOITIE PLEINE)	5 P-6; 7 5 P-6 P-4; 17 P-6; P-6 13 12 MODELE NON PRECISE	PRISE DOUBLE DDFT (moitié pleine)	E-001 légende ; bloc S158
LX	1	APPAREIL D'ECLAIRAGE 'X4'	MODELE NON PRECISE	APPAREIL D'ÉCLAIRAGE 'x4'	E-001 légende ; bloc S035
M3	5	MOTEUR TRIPHASE, PUISSANCE SELON LES INDICATIONS	MODELE NON PRECISE	MOTEUR TRIPHASÉ, PUISSANCE SELON LES INDICATIONS	E-001 légende ; bloc S104
MP	2	MONUMENT PLANCHER SURFACE, TYPE HUBBELL S1PT / POKE THROUGH	P-6 38; P-6 25 MODELE NON PRECISE	MONUMENT PLANCHER SURFACE, TYPE HUBBELL S1PT / POKE THROUGH	E-001 légende ; bloc S128
MP	1	MONUMENT PLANCHER SURFACE, TYPE HUBBELL S1PT / POKE THROUGH	P-4 17 MODELE NON PRECISE	MONUMENT PLANCHER SURFACE, TYPE HUBBELL S1PT / POKE THROUGH	E-001 légende ; bloc S128
PC	18	PRISE DE COURANT DOUBLE 15A- 120V	P-4 15; P-4 3; LC P-4 G 3; P-4 25; P-6 46; 5 7 P-6 P-4; P-6 12; DE P-4 8; P-4 8 DE; P-4 8; P-4 10; P-4 10 P-4 12; P-4 12 P-4 10; P-4 12 TV P-4; P-6 13 MODELE NON PRECISE	PRISE DE COURANT DOUBLE 15A- 120V	E-001 légende ; bloc S020
PC	4	PRISE DE COURANT DOUBLE 15A- 120V	P-6 50; P-6 P-6 48 48; P-6 48 P-6 48; P-4 MODELE NON PRECISE	PRISE DE COURANT DOUBLE 15A- 120V	E-001 légende ; bloc S020
TV	3	SORTIE DE CABLODISTRIBUTION AU MUR	TV P-4; TV P-4 10 10; TV P-4 12 12 MODELE NON PRECISE	SORTIE DE CÂBLODISTRIBUTION AU MUR	E-001 légende ; bloc S293

0" 6" 12"

NOTE GÉNÉRALE:

1. Sauf indications contraire, tous les équipements sont existants à conserver.

2. Dans le cadre des travaux, tous les équipements de ventilation devront être temporairement retirés du toit, puis réinstallés par la suite.
Tous les équipements électriques devront être conservés et réutilisés pour le rebranchement des équipements mécaniques.
Pendant les travaux, tous les sectionneurs et autres équipements amovibles devront être entreposés, et les câbles devront être isolés et couverts.

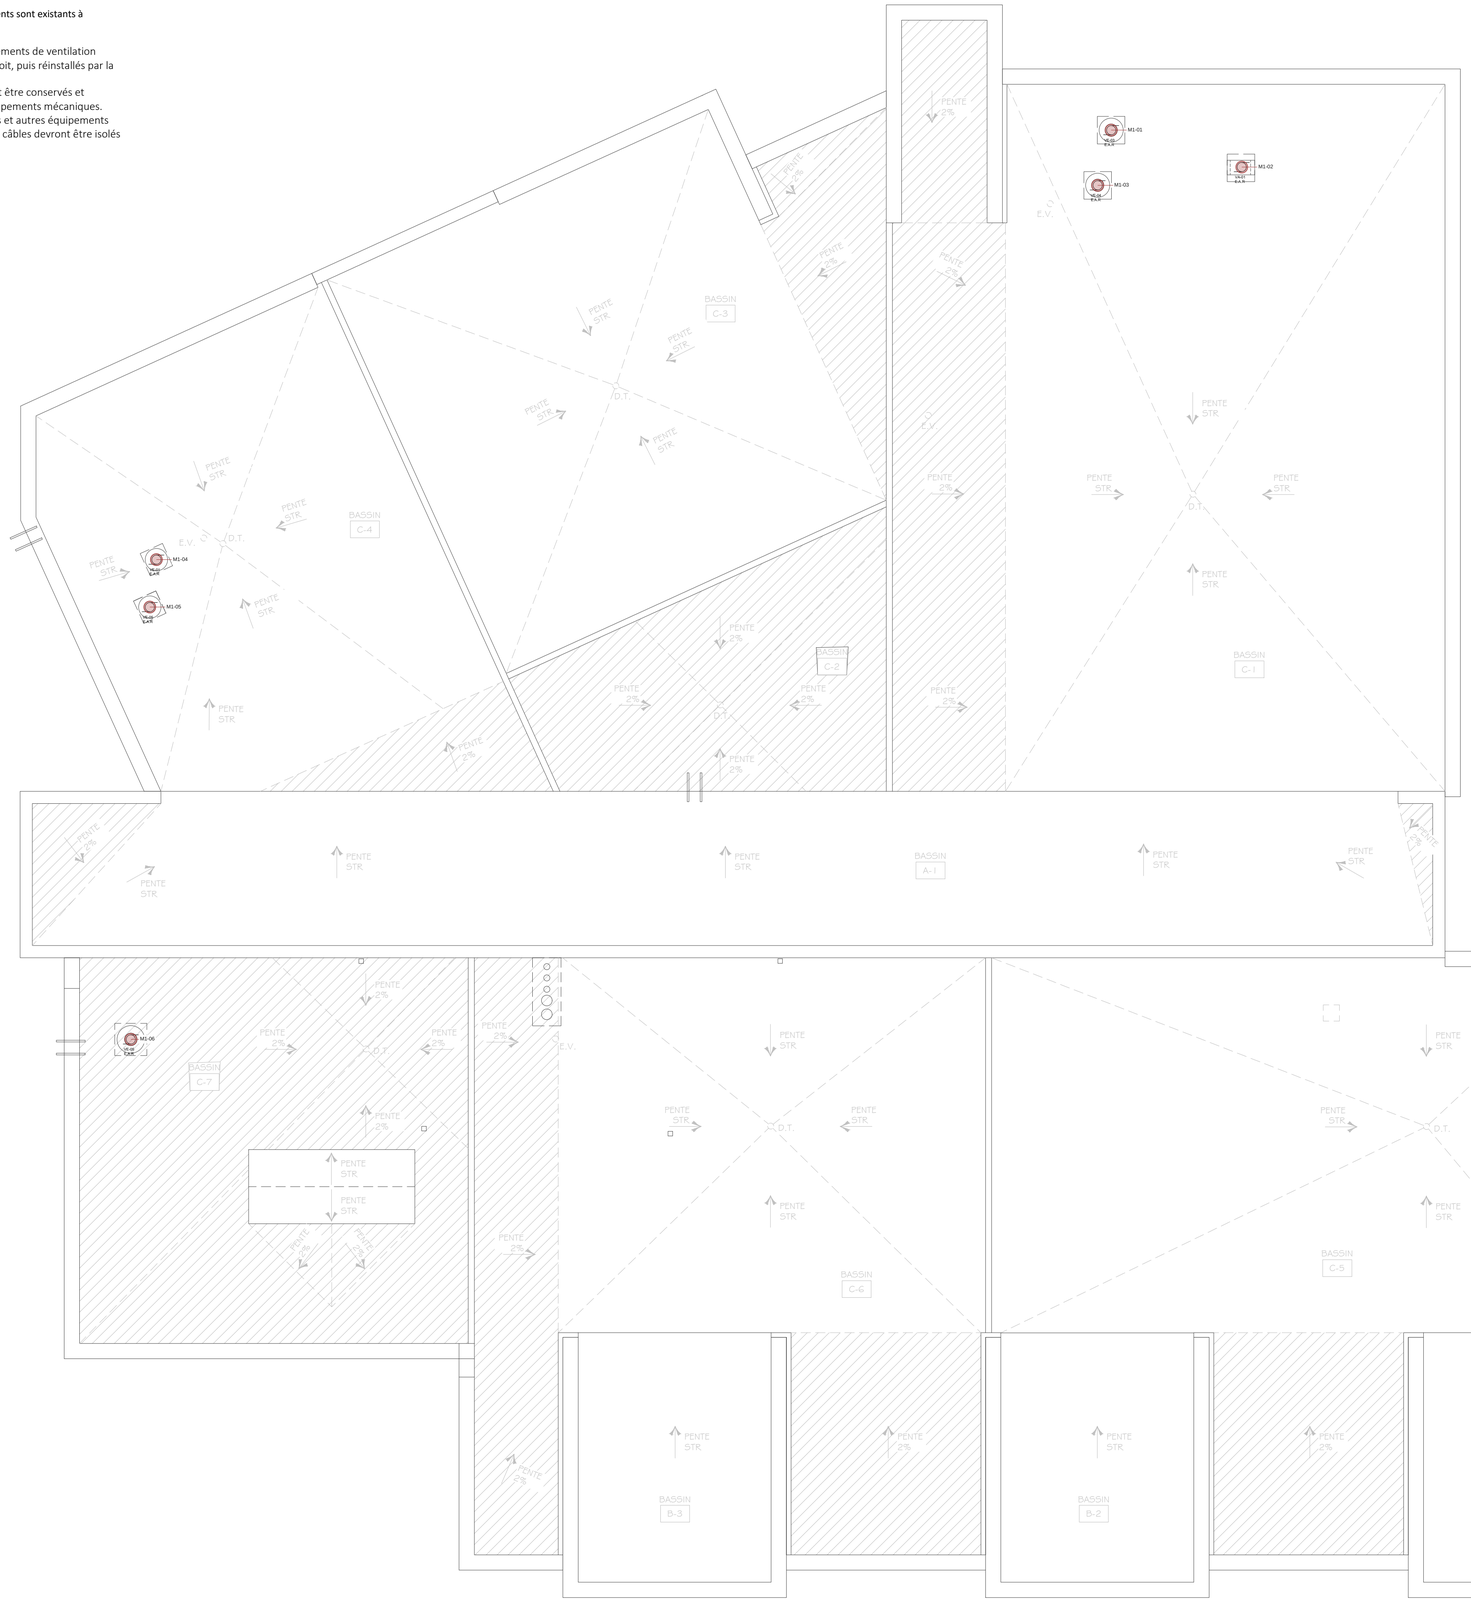

RELEVE E103 - MATERIEL

6 reperes / 1 familles / calques activables

0 non identifies - 0 identifications a revalider (*)

M1	MOTEUR MONOPHASE, PUISSANCE SELON LES INDICATIONS	6

PL : rectangles aux dimensions graphiques du plan.
W et circuits affiches uniquement si verifies.
* : identification heritee a revalider ; NI : materiel non identifie.
Les quantites concernent cette feuille.
Modeles, prescriptions et sources : bordereau page 2.

experts conseils

| HF Experts-Conseils - Mécanique et électricité du bâtiment |
| 7375A rue Beaubien Est, Anjou, QC, H1M 3R5 |
| (514).655.9694 |
| hfec-ing.com |

No.	DATE:	ÉMISSION:
01	2026-09-16	ÉMIS POUR APPEL D'OFFRE
A	2026-08-28	ÉMIS POUR COORDINATION PRÉLIM.

SCEAU:

INGÉNIEURS Hamid Haddad 026451 QUÉBEC
2026-09-16

ARCHITECTE:

CLIENT:

Brossard

PROJET:

TECHNOLOGIE RFID
BIBLIOTHÈQUE GEORGETTE-LEPAGE - TRAVAUX D'AMÉNAGEMENT DU REZ-DE-CHAUSSÉE ET DE L'ÉTAGE

NO APPEL D'OFFRES : SP-GTER-26-0080

TITRE DU PLAN

SERVICES EXISTANT TOIT

No DE DOSSIER	26-29		
DESSINÉ PAR:	P. ELISEEV		
PRÉPARÉ PAR:	P. ELISEEV		
VÉRIFIÉ PAR:	R. HADDAD, Ing.		
ÉCHELLE:	1:100	FORMAT	841X594
DATE:	JUILLET 2026		

PLAN E-103

BORDEREAU MATERIEL - E103

6 reperes sur cette feuille - prescriptions recopiees du devis et du releve verifie.

Les modeles non renseignes restent a preciser. Les circuits divergents exigent une clarification.

ID	Qte	Famille	Modele / type	Prescription du devis	Source / reserve
M1	6	MOTEUR MONOPHASE, PUISSANCE SELON LES INDICATIONS	MODELE NON PRECISE	MOTEUR MONOPHASÉ, PUISSANCE SELON LES INDICATIONS	E-001 légende ; bloc S102


0" 6" 12"

NOTE GÉNÉRALE:

1. Sauf indications contraire, tous les équipements sont existants à conserver.
2. L'entrepreneur en électricité sera responsable d'enlever tout autre équipement non montré en plan lorsque des murs ou des plafonds sont pour démolition. Retirée l'alimentation de ces équipements jusqu'au panneau et la composante à conserver.
3. L'entrepreneur en électricité doit vérifier le bon fonctionnement des prises électrique existante montré aux plans.
4. Valider la position exacte de toute les prises avec le client.
5. Les circuits identifiés aux plans sont à titre indicatif seulement. Afin de conserver les charges actuelles réutiliser les circuits libérés lors du démantèlement et réalimenter lorsque requis les nouveaux besoins.
6. Chute de tension limité à 3% tel que l'article (8-102-1-c) pour les artères de dérivation.Prévoir calibre plus élevé pour le filage. IL est de la responsabilité du contracteur de choisir le bon calibre pour le filage.
7. Coordonner hauteur de montage avec plan d'architecture ou ébénisterie

NOTE SPÉCIFIQUE:

1. Services et data intégrés dans le mobilier. Alimentation via percement de la dalle. Les câbles et les circuits doivent être réutilisés.
2. Prises électriques et data intégrées dans le mobilier. À alimenter à partir d'une boîte de jonction dans le mur adjacent. Réutiliser le câble de données existant.
3. Monument de plancher encastre tel que modele S1R6PTFIT de la serie hubbell (ou equivalent approuve), incluant une prise de courant double 20A, 120V et deux sorties RJ45. Prévoir la fourniture de tous les accesoires neccessaires a l'installtion. Coordonner la localisation exacte au chantier.
4. Prises electriques integrées dans le mobilier. S'assurer d'avoir la boîte d'électrification pour le passe -fil et le trou pour passer deux branchements de deux prises électriques et deux prises USB et s'assurer que le trou de branchement sont au milieu.
5. Conduits sous la dalle: Le passage des conduits est montré à titre indicatif. L'entrepreneur doit valider le passage dans l'entreplafond du niveau en-dessous vers panneau élecrique

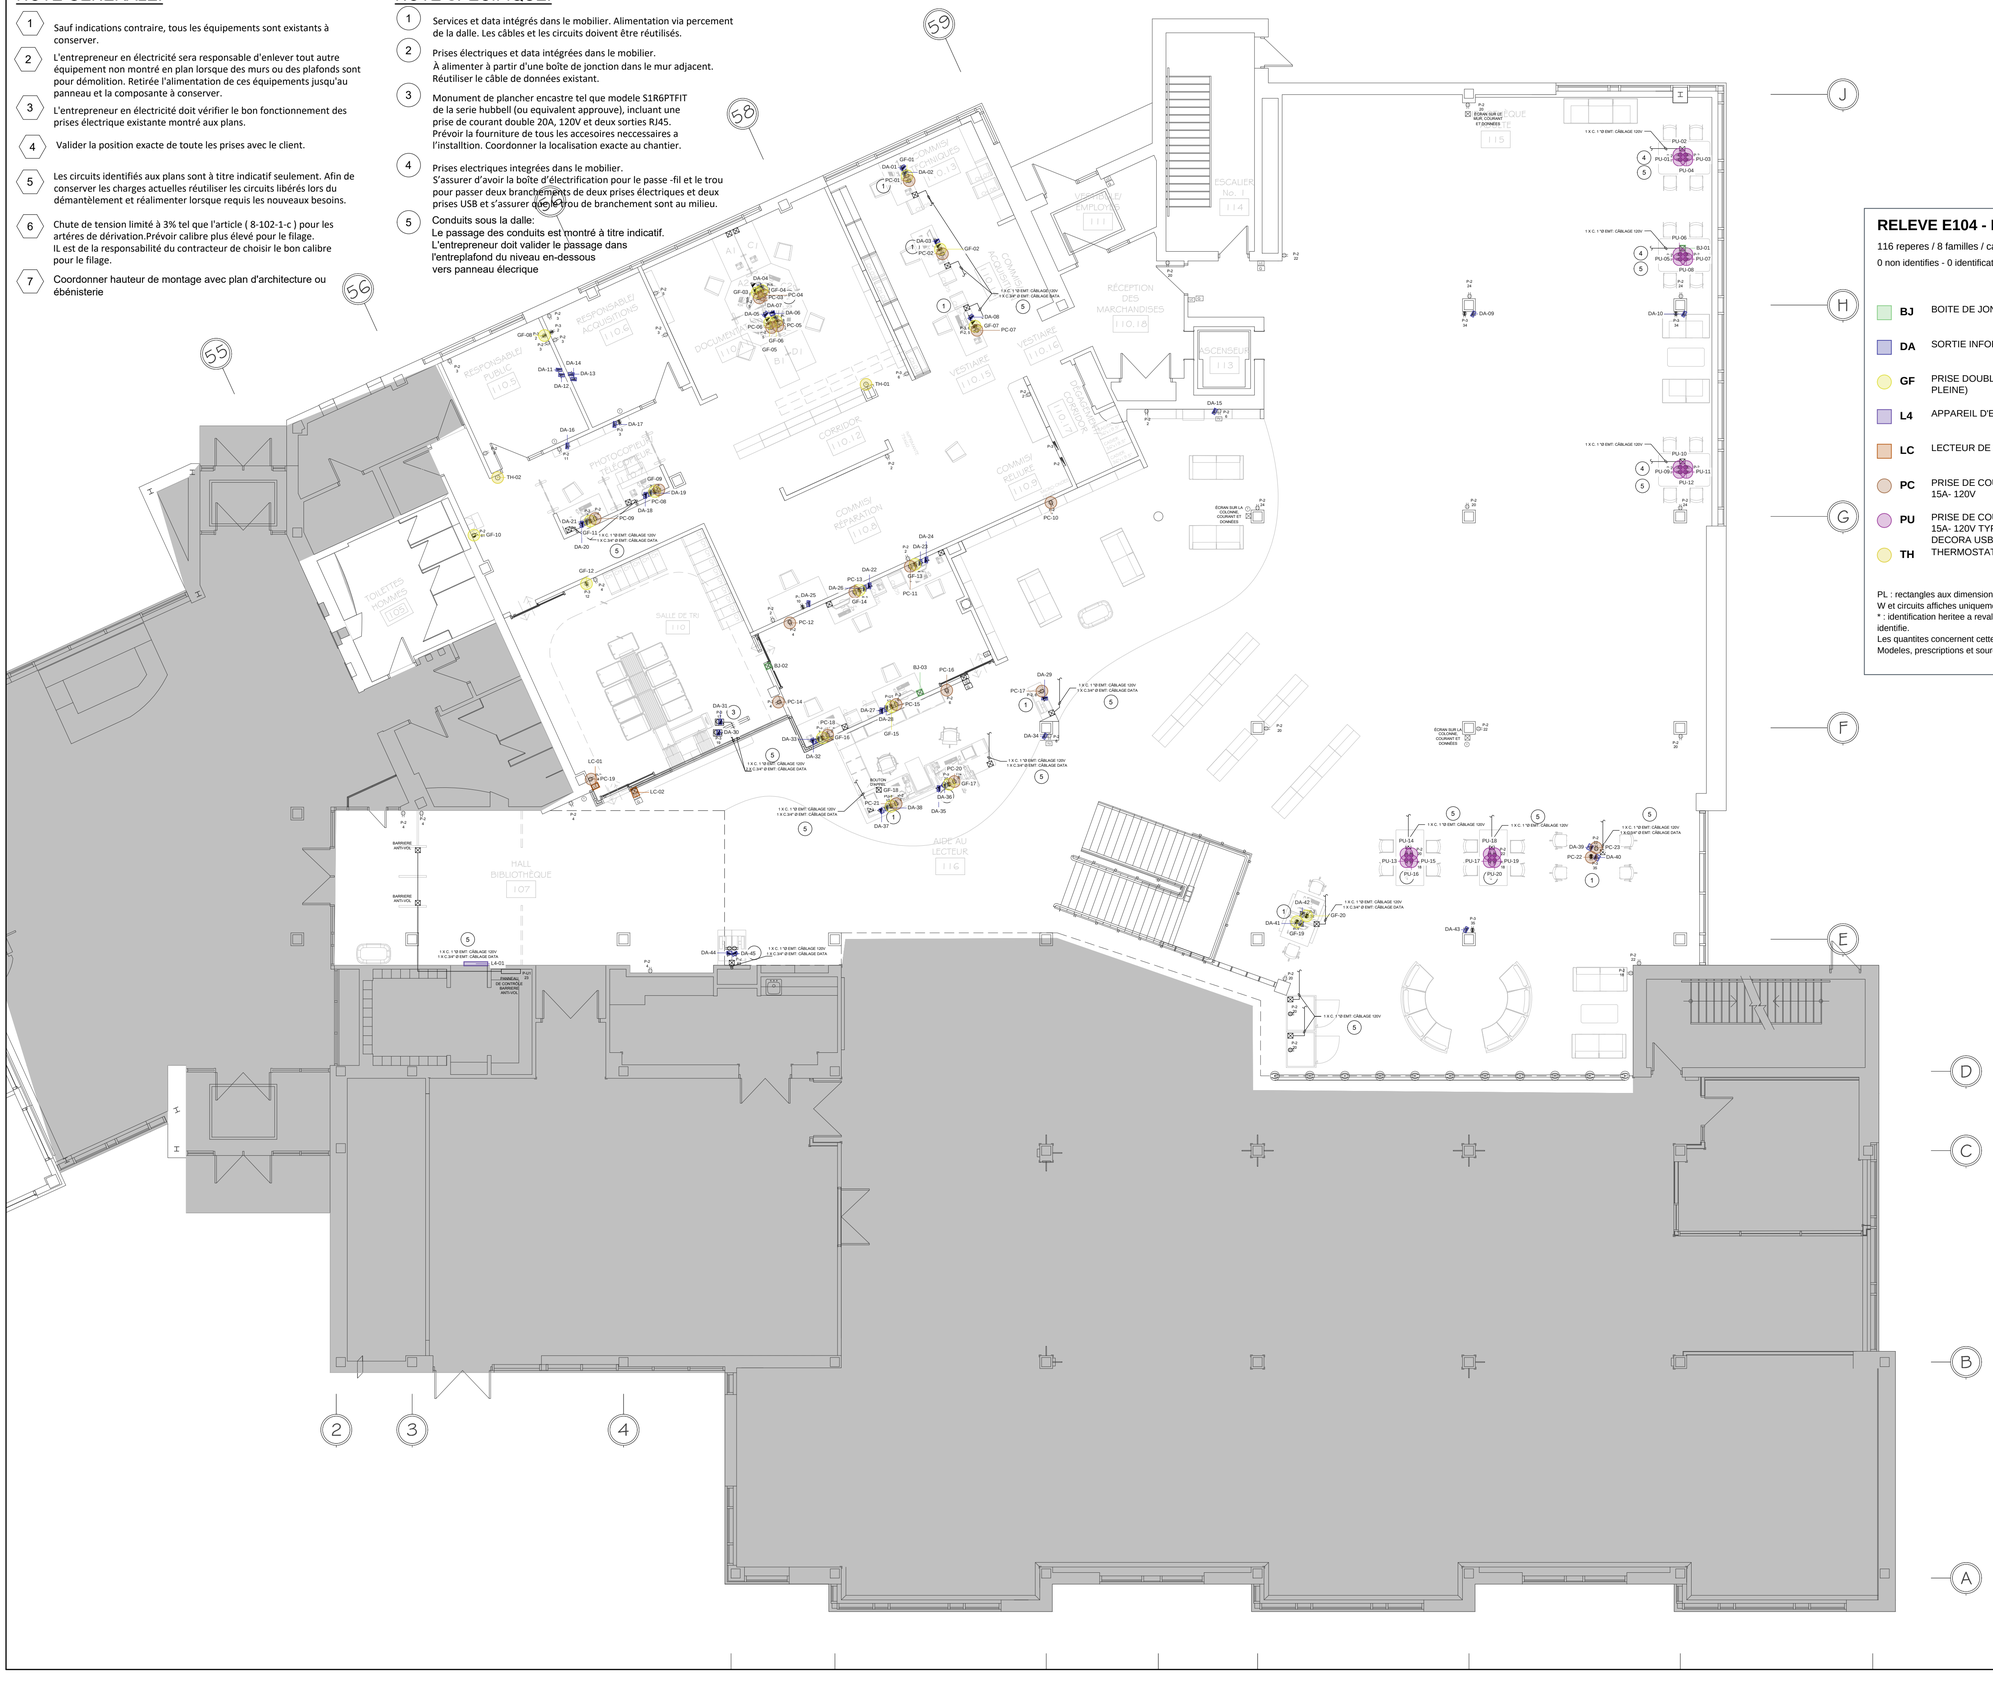
55
56
57
58
59
RESPONSABLE PUBLIC 110.5
RESPONSABLE ACQUISITIONS 110.6
DOCUMENTATION 110.7
COMMIS ACQUISITIONS 110.13
VESTIAIRE EMPLOYÉS 111
ESCALIER No. 1 114
RÉCEPTION DES MARCHANDISES 110.18
VESTIAIRE 110.16
VESTIAIRE 110.15
ASCENSEUR 113
CORRIDOR 110.2
COMMIS RELIURE 110.3
COMMIS RÉPARATION 110.8
PHOTOCOPIEUR TÉLÉCOPIEUR 110.4
TOILETTES HOMMES 109
SALLE DE TRI 110
AIDE AU LECTEUR 116
HALL BIBLIOTHÈQUE 107
BARRIÈRE ANTIVOL
PANNEAU DE CONTRÔLE BARRIÈRES ANTIVOL
ÉCRAN SUR LE COURANT ET DONNÉES
1 X C. 1 "Ø EMT- CÂBLAGE 120V
1 X C.3/4" Ø EMT- CÂBLAGE DATA

BORDEREAU MATERIEL - E104

116 reperes sur cette feuille - prescriptions recopiees du devis et du releve verifie.

Les modeles non renseignes restent a preciser. Les circuits divergents exigent une clarification.

ID	Qte	Famille	Modele / type	Prescription du devis	Source / reserve
BJ	3	BOITE DE JONCTION	P-2 P-2 64 24 MODELE NON PRECISE	BOITE DE JONCTION	E-001 légende ; bloc S107
DA	45	SORTIE INFORMATIQUE/AUDIO	4 5; 6 5; P-3 8 P-2 P-3 2 6 P-2; P-3 6 P-3 2 P-2 5 P-2 8; P-3 8 P-3 P-2 2; 05 6 5 CH; P-3 34; TV P-2 6; P-2 11 T; P-3 3 T; 3 P-3 4 P-2; 3 P-3; 3 P-3 4 P-2 1; CH P-3 05 7; P-3 9 P-2 2; P-3 9; P-3 10; CH P-3 05 7 P-2; 13 05 P-U1 CH; 13 P-U1 6 P-2 05; 6; P-3 19 17; 17 P-3 3 P-3; 7 P-3; 7 P-3 6 P-2; 1 25 P-3; 25 1 P-3 6 P-2; 13 1; 13 1 6 P-2; 22 P-2 P-3; P-3 35 22 P-2; P-3 28 32 P-3; P-3 32 P-3 1; 35 P-3; P-2 63 MODELE NON PRECISE	SORTIE INFORMATIQUE/AUDIO	E-001 légende ; bloc S006
GF	20	PRISE DOUBLE DDFT (MOITIE PLEINE)	4 5; 6 5; P-3 P-2 6 P-3 8 P-2 5 2; P-3 8 P-2 2 P-3 P-2 6 5; P-3 6 P-2 P-3 5 8 P-2 2; 6 5 05; P-3 2 P-2 3 P-3 2 P-2; 3 4 P-3 P-2; P-2 61; 3 4 P-3 P-2 1 X; P-3 12 P-2 4; P-3 P-2 9 2 6 P-2; P-3 P-2 CH 7 14 05; 13 6 P-U1 P-2; 7 P-3 6 P-2; 25 P-3 6 1 P-2; 13 1 6 P-2; P-3 28 1 32 P-3; P-3 32 P-3 MODELE NON PRECISE	PRISE DOUBLE DDFT (moitié pleine)	E-001 légende ; bloc S158
L4	1	APPAREIL D'ECLAIRAGE 4' LED	1 MODELE NON PRECISE	APPAREIL D'ÉCLAIRAGE 4' LED	E-001 légende ; bloc S316
LC	2	LECTEUR DE CARTE	LC 4 P-2 T; LC G MODELE NON PRECISE	LECTEUR DE CARTE	E-001 légende ; bloc S219
PC	23	PRISE DE COURANT DOUBLE 15A- 120V	4 5; 5 6; P-2 P-3 P-2 8 5 6 2 P-3; P-2 8 2 P-3 P-2 P-3 6 5; P-2 P-3 6 5 P-2 8 P-3 2; 4 P-3 3 P-2; 4 3 P-3 P-2 1 X; P-2 4; P-3 P-2 9 6 2 CH; P-3 P-2 7 14 CH; 6 13 P-U1 P-2; P-2 6; 6 1; 6 P-2 P-3 7; P-2 LC 4; 6 25 P-2 P-3 1; 6 13 P-2 1; P-3 35 22 P-2; 22 P-2 P-3 MODELE NON PRECISE	PRISE DE COURANT DOUBLE 15A- 120V	E-001 légende ; bloc S020
PU	20	PRISE DE COURANT DOUBLE 15A- 120V TYPE LEVITON DECORA USB	P-2 64 P-2 24; P-2 24 P-2 64; P-2 18 20 4 P-2; P-2 P-2 20 18; P-2 18 20 P-2 4; P-2 20 P-2 18; P-2 18 22 4 P-2; P-2 P-2 22 18; P-2 18 22 P-2 4; P-2 22 P-2 18 MODELE NON PRECISE	PRISE DE COURANT DOUBLE 15A- 120V TYPE Leviton Decora USB	E-001 légende ; bloc S051
TH	2	THERMOSTAT	T MODELE NON PRECISE	THERMOSTAT	E-001 légende ; bloc S323


0" 6" 12"

NOTE GÉNÉRALE:

1. Sauf indications contraire, tous les équipements sont existants à conserver.
2. L'entrepreneur en électricité sera responsable d'enlever tout autre équipement non montré en plan lorsque des murs ou des plafonds sont pour démolition. Retirée l'alimentation de ces équipements jusqu'au panneau et la composante à conserver.
3. L'entrepreneur en électricité doit vérifier le bon fonctionnement des prises électrique existante montré aux plans.
4. Valider la position exacte de toute les prises avec le client.
5. Les circuits identifiés aux plans sont à titre indicatif seulement. Afin de conserver les charges actuelles réutiliser les circuits libérés lors du démantèlement et réalimenter lorsque requis les nouveaux besoins.
6. Chute de tension limité à 3% tel que l'article (8-102-1-c) pour les artéres de dérivation.Prévoir calibre plus élevé pour le filage.
IL est de la responsabilité du contracteur de choisir le bon calibre pour le filage.
7. Coordonner hauteur de montage avec plan d'architecture ou ébénisterie

NOTE SPÉCIFIQUE:

1. Conduits électriques seront peint au chantier par EG dans le Fablab.
2. Services et data intégrés dans le mobilier. Alimentation via percement de la dalle. Les câbles et les circuits doivent être réutilisés.
3. Conduits sous la dalle:
Le passage des conduits est montré à titre indicatif.
L'entrepreneur doit valider le passage dans l'entreplafond du niveau en-dessous vers panneau élecrique

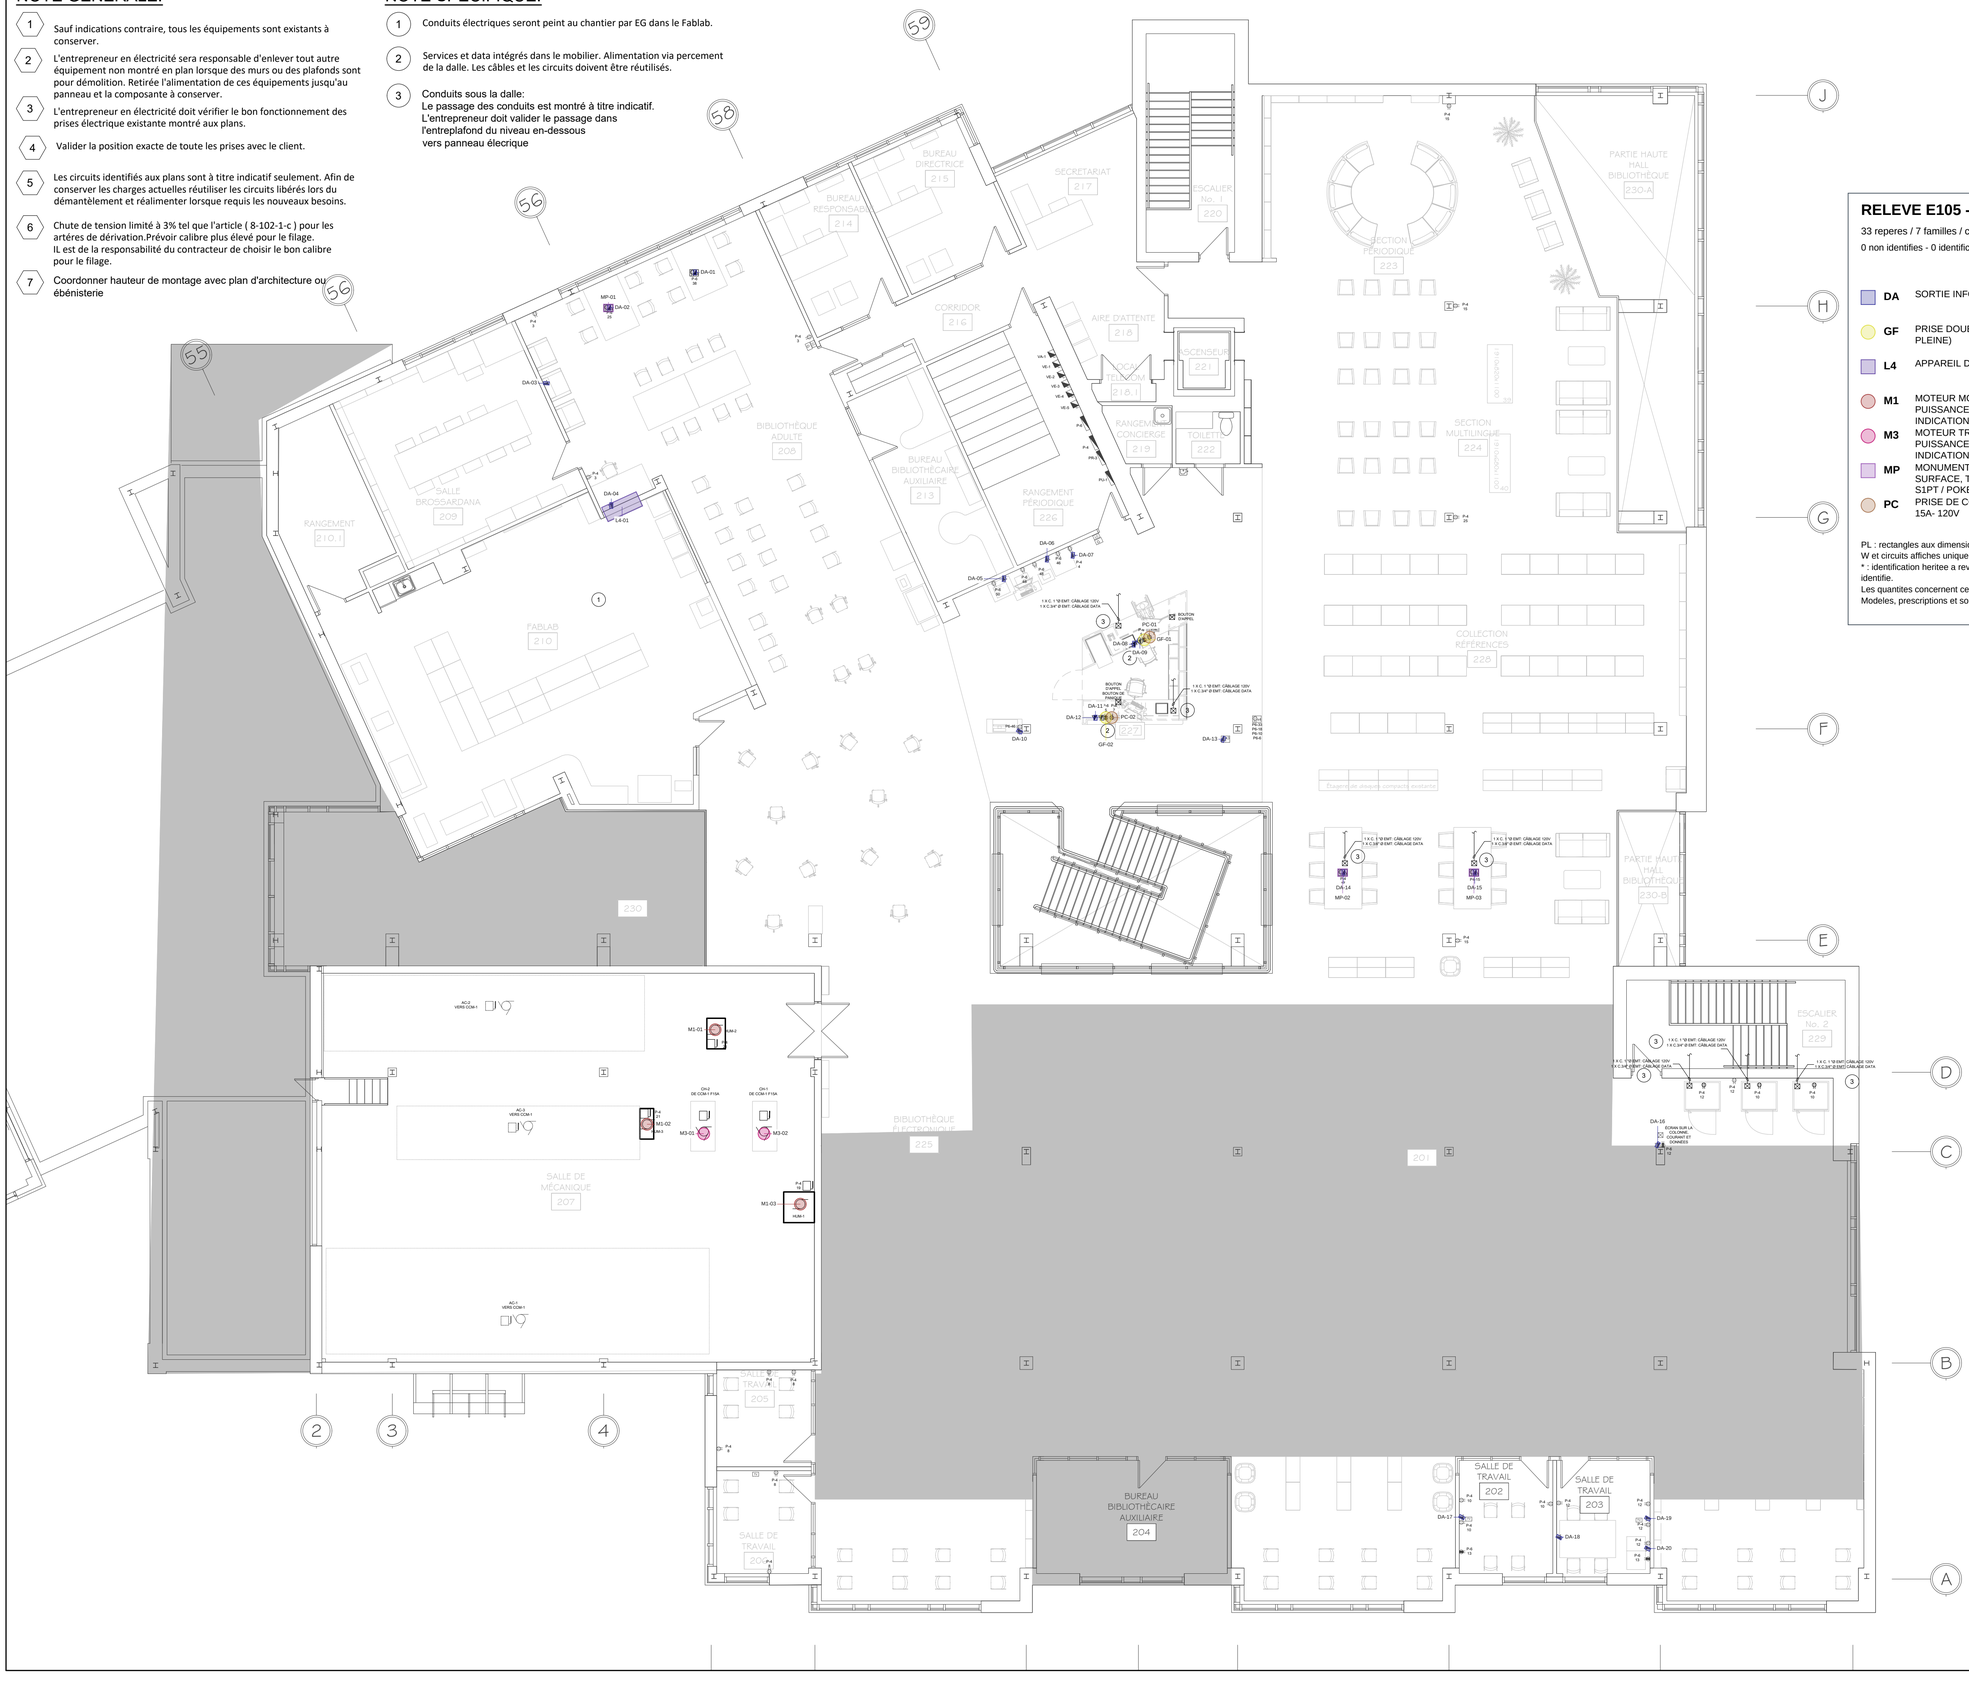

RELEVE E105 - MATERIEL

33 reperes / 7 familles / calques activables

0 non identifies - 0 identifications a revalider (*)

	DA	SORTIE INFORMATIQUE/AUDIO	20
	GF	PRISE DOUBLE DDFT (MOITIE PLEINE)	2
	L4	APPAREIL D'ECLAIRAGE 4' LED	1
	M1	MOTEUR MONOPHASE, PUISSANCE SELON LES INDICATIONS	3
	M3	MOTEUR TRIPHASE, PUISSANCE SELON LES INDICATIONS	2
	MP	MONUMENT PLANCHER SURFACE, TYPE HUBBELL S1PT / POKE THROUGH	3
	PC	PRISE DE COURANT DOUBLE 15A- 120V	2

PL : rectangles aux dimensions graphiques du plan.
W et circuits affiches uniquement si verifies.
* : identification heritee a revalider ; NI : materiel non identifie.
Les quantites concernent cette feuille.
Modeles, prescriptions et sources : bordereau page 2.

experts conseils

| HF Experts-Conseils - Mécanique et électricité du bâtiment |
| 7375A rue Beaubien Est, Anjou, QC, H1M 3R5 |
| (514).655.9694 |
| hfec-ing.com |

No.	DATE:	ÉMISSION:
01	2026-09-16	ÉMIS POUR APPEL D'OFFRE
A	2026-08-28	ÉMIS POUR COORDINATION PRÉLIM.

SCEAU:

INGÉNIEUR Hanni Haddad 2026451 QUÉBEC
2026-09-16

ARCHITECTE:

CLIENT:

Brossard

PROJET:

TECHNOLOGIE RFID
BIBLIOTHÈQUE GEORGETTE-LEPAGE - TRAVAUX D'AMÉNAGEMENT DU REZ-DE-CHAUSSÉE ET DE L'ÉTAGE

NO APPEL D'OFFRES : SP-GTER-26-0080

TITRE DU PLAN

SERVICES
NOUVEAU
2E ÉTAGE

No DE DOSSIER	26-29		
DESSINÉ PAR:	P. ELISEEV		
PRÉPARÉ PAR:	P. ELISEEV		
VÉRIFIÉ PAR:	R. HADDAD, Ing.		
ÉCHELLE:	1:100	FORMAT	841X594
DATE:	JUILLET 2026		

PLAN E-105

BORDEREAU MATERIEL - E105

33 reperes sur cette feuille - prescriptions recopiees du devis et du releve verifie.

Les modeles non renseignes restent a preciser. Les circuits divergents exigent une clarification.


ID	Qte	Famille	Modele / type	Prescription du devis	Source / reserve
DA	20	SORTIE INFORMATIQUE/AUDIO	P-6 38; P-6 25; P-6 50; P-6 P-6 46 48; P-4 4 P-6 46; 5 2 P-6; 5 P-6 2 7 P-4; 5 P-6 2; P-4 17; 3; P-6 12; TV P-4 10 10; P-4 TV 12 12 P-4; 12 P-4 P-6 13 MODELE NON PRECISE	SORTIE INFORMATIQUE/AUDIO	E-001 légende ; bloc S006
GF	2	PRISE DOUBLE DDFT (MOITIE PLEINE)	5 P-6 7 P-4; 5 7 P-6 P-4 2 MODELE NON PRECISE	PRISE DOUBLE DDFT (moitié pleine)	E-001 légende ; bloc S158
L4	1	APPAREIL D'ECLAIRAGE 4' LED	MODELE NON PRECISE	APPAREIL D'ÉCLAIRAGE 4' LED	E-001 légende ; bloc S316
M1	3	MOTEUR MONOPHASE, PUISSANCE SELON LES INDICATIONS	P-4 21; 21 P-4; 19 P-4 MODELE NON PRECISE	MOTEUR MONOPHASÉ, PUISSANCE SELON LES INDICATIONS	E-001 légende ; bloc S102
M3	2	MOTEUR TRIPHASE, PUISSANCE SELON LES INDICATIONS	MODELE NON PRECISE	MOTEUR TRIPHASÉ, PUISSANCE SELON LES INDICATIONS	E-001 légende ; bloc S104
MP	3	MONUMENT PLANCHER SURFACE, TYPE HUBBELL S1PT / POKE THROUGH	P-6 25; P-4 17 3; 3 MODELE NON PRECISE	MONUMENT PLANCHER SURFACE, TYPE HUBBELL S1PT / POKE THROUGH	E-001 légende ; bloc S128
PC	2	PRISE DE COURANT DOUBLE 15A- 120V	7 P-4 P-6 5; 7 5 P-4 P-6 2 MODELE NON PRECISE	PRISE DE COURANT DOUBLE 15A- 120V	E-001 légende ; bloc S020

0" 6" 12"

NOTE GÉNÉRALE:

1. Sauf indications contraire, tous les équipements sont existants à conserver.

2. Dans le cadre des travaux, tous les équipements de ventilation devront être temporairement retirés du toit, puis réinstallés par la suite.
Tous les équipements électriques devront être conservés et réutilisés pour le rebranchement des équipements mécaniques.
Pendant les travaux, tous les sectionneurs et autres équipements amovibles devront être entreposés, et les câbles devront être isolés et couverts.

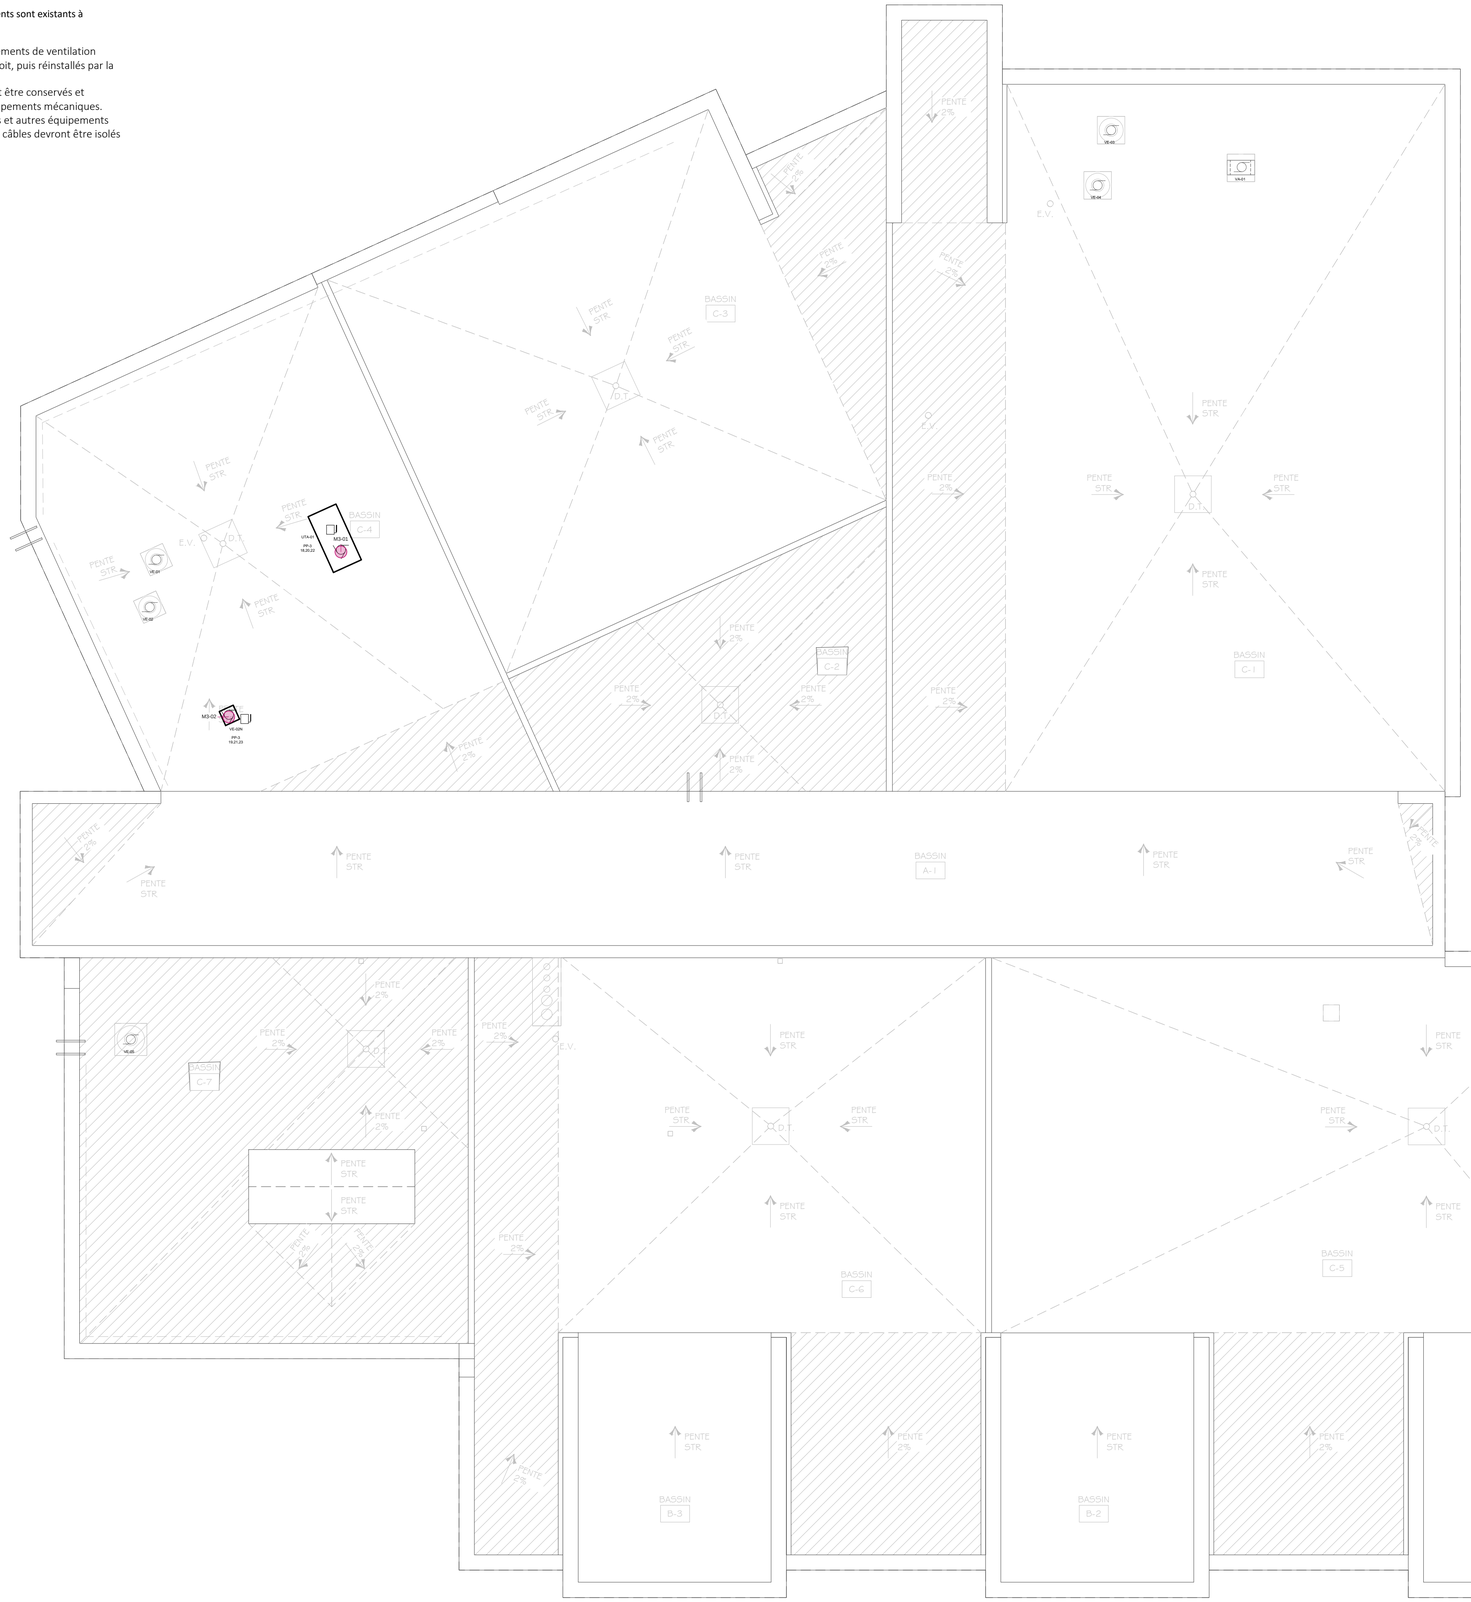

RELEVE E106 - MATERIEL

2 reperes / 1 familles / calques activables

0 non identifies - 0 identifications a revalider (*)

M3	MOTEUR TRIPHASE, PUISSANCE SELON LES INDICATIONS	2

PL : rectangles aux dimensions graphiques du plan.
W et circuits affiches uniquement si verifies.
* : identification heritee a revalider ; NI : materiel non identifie.
Les quantites concernent cette feuille.
Modeles, prescriptions et sources : bordereau page 2.

experts conseils

| HF Experts-Conseils - Mécanique et électricité du bâtiment |
| 7375A rue Beaubien Est, Anjou, QC, H1M 3R5 |
| (514).655.9694 |
| hfec-ing.com |

No.	DATE:	ÉMISSION:
01	2026-09-16	ÉMIS POUR APPEL D'OFFRE
A	2026-08-28	ÉMIS POUR COORDINATION PRÉLIM.

SCEAU:

INGÉNIEURS Hanni Haddad 026461 QUÉBEC
2026-09-16

ARCHITECTE:

CLIENT:

Brossard

PROJET:

TECHNOLOGIE RFID
BIBLIOTHÈQUE GEORGETTE-LEPAGE - TRAVAUX D'AMÉNAGEMENT DU REZ-DE-CHAUSSÉE ET DE L'ÉTAGE

NO APPEL D'OFFRES : SP-GTER-26-0080

TITRE DU PLAN

SERVICES
NOUVEAU
TOIT

No DE DOSSIER	26-29		
DESSINÉ PAR:	P. ELISEEV		
PRÉPARÉ PAR:	P. ELISEEV		
VÉRIFIÉ PAR:	R. HADDAD, Ing.		
ÉCHELLE:	1:100	FORMAT	841X594
DATE:	JUILLET 2026		

PLAN E-106

BORDEREAU MATERIEL - E106

2 reperes sur cette feuille - prescriptions recopiees du devis et du releve verifie.

Les modeles non renseignes restent a preciser. Les circuits divergents exigent une clarification.

ID	Qte	Famille	Modele / type	Prescription du devis	Source / reserve
M3	2	MOTEUR TRIPHASE, PUISSANCE SELON LES INDICATIONS	PP-3 MODELE NON PRECISE	MOTEUR TRIPHASÉ, PUISSANCE SELON LES INDICATIONS	E-001 légende ; bloc S104

0" 6" 12"

NOTE GÉNÉRALE:


1. Sauf indications contraire, tous les équipements sont existants à conserver.
2. L'entrepreneur en électricité sera responsable d'enlever tout autre équipement non montré en plan lorsque des murs ou des plafonds sont pour démolition. Retirée l'alimentation de ces équipements jusqu'au panneau et la composante à conserver.
3. L'entrepreneur en électricité doit vérifier le bon fonctionnement des prises électrique existante montré aux plans.
4. Les travaux d'alarme incendie seront réalisés par l'électricien

NOTE SPÉCIFIQUE:

1. Interrupteurs maitres, à rélocaliser.

   Tout l'éclairage de la zone principale du hall est commandé à partir de ce panneau.

   Système de dénomination : Ma (Main a).

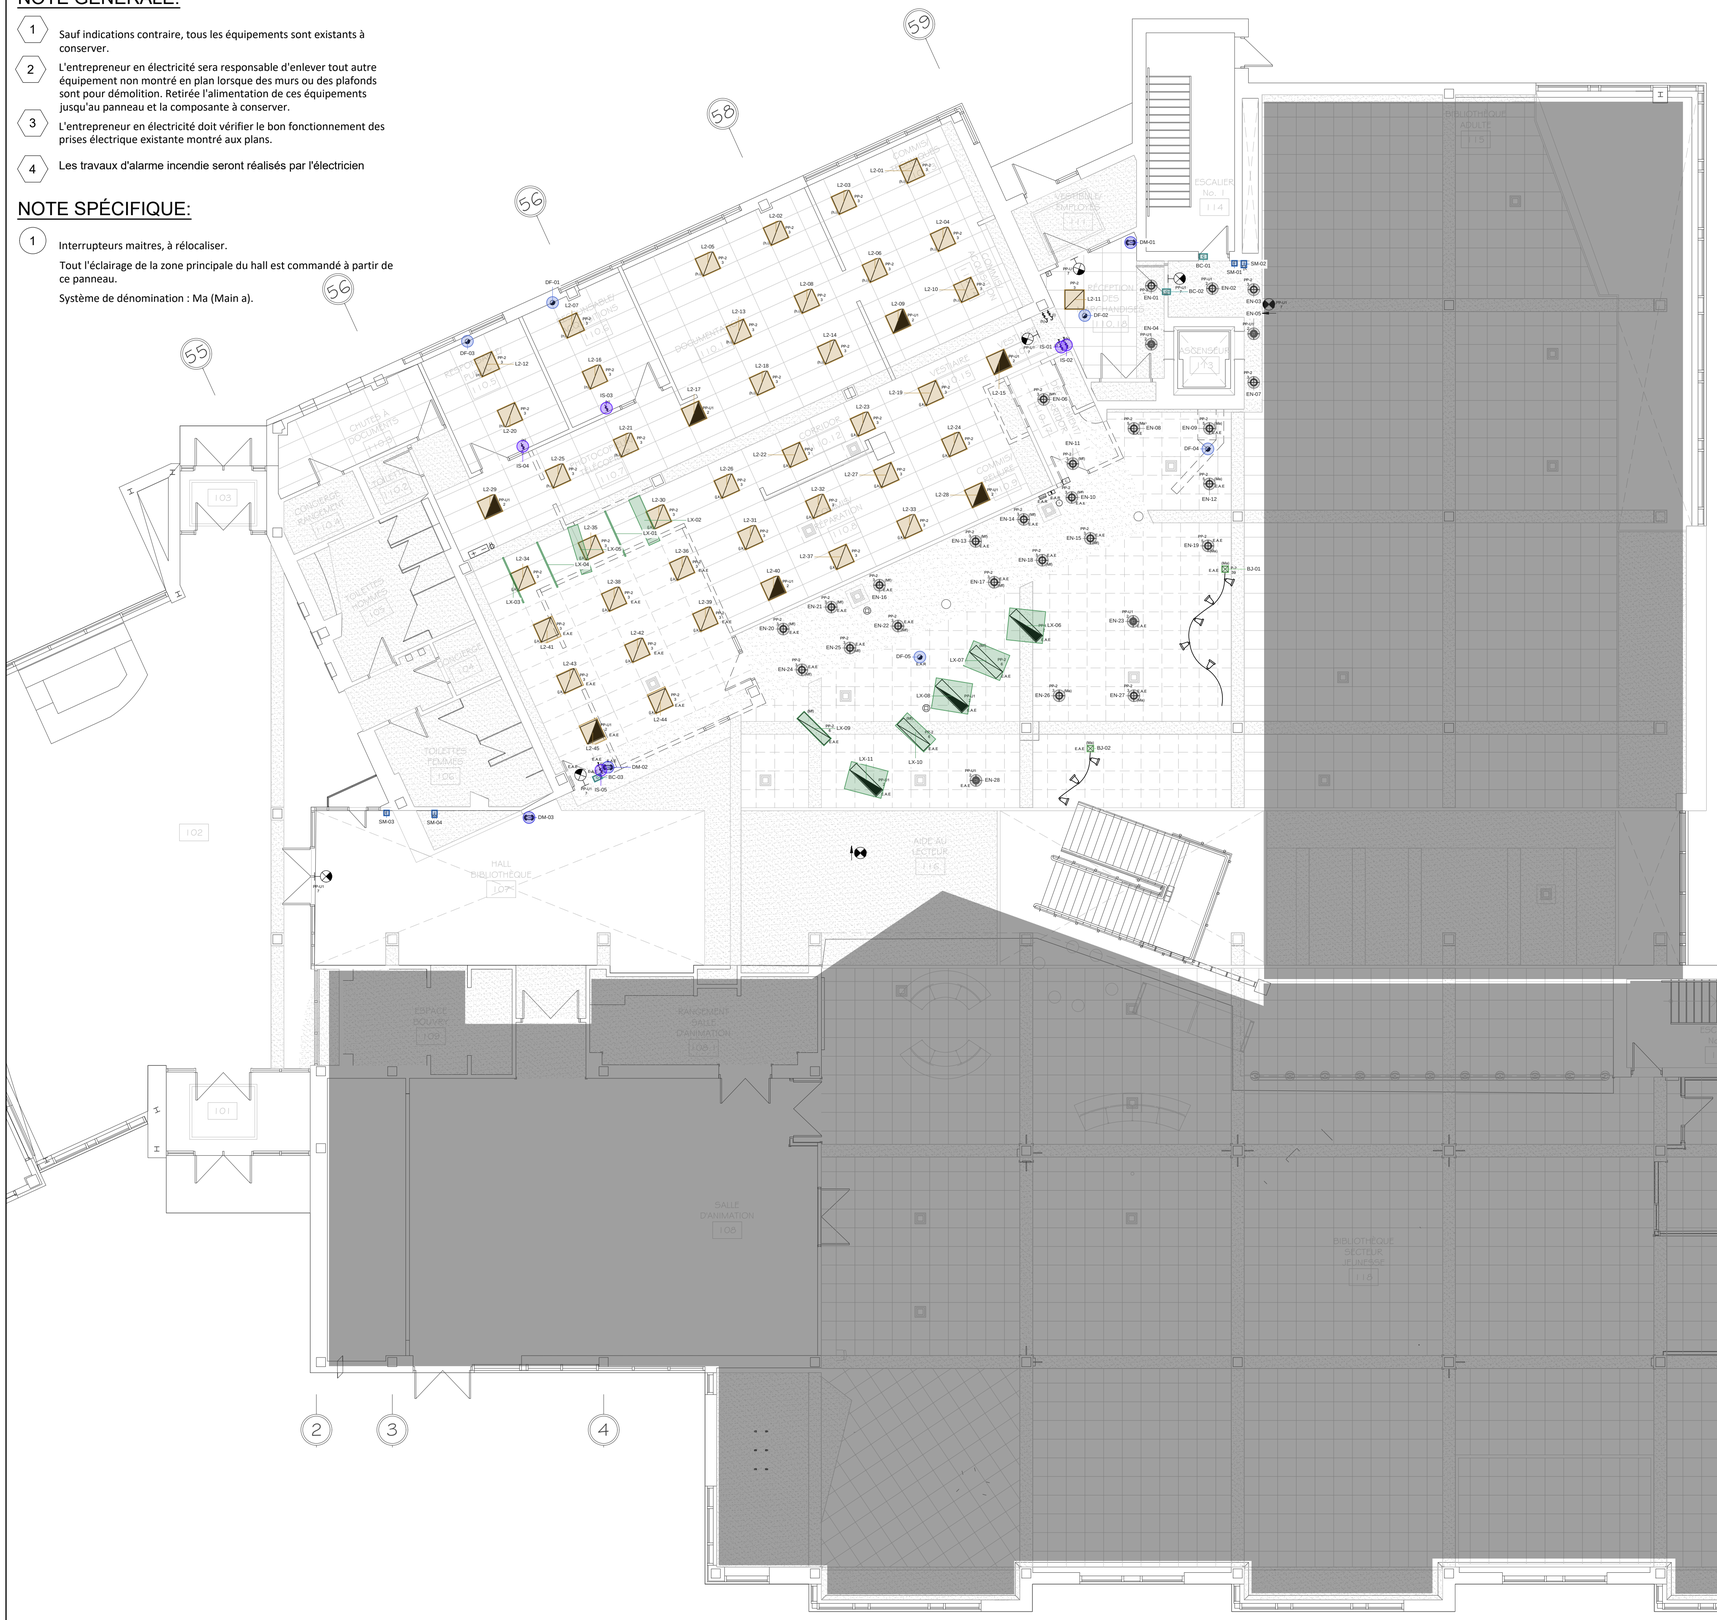

RELEVE E201 - MATERIEL

106 reperes / 9 familles / calques activables

0 non identifies - 0 identifications a revalider (*)

BC	BOITIER "C" (HORS LEGENDE - R-006 TEST-E201)	3
BJ	BOITE DE JONCTION	2
DF	DETECTEUR DE FUMEE	5
DM	DETECTEUR DE MOUVEMENT	3
EN	APPAREIL D'ECLAIRAGE ENCASTRE	28
IS	INTERRUPTEUR SIMPLE	5
L2	APPAREIL D'ECLAIRAGE 2'X2' LED	45
LX	APPAREIL D'ECLAIRAGE 'X4'	11
SM	STATION MANUELLE	4

PL : rectangles aux dimensions graphiques du plan.
W et circuits affiches uniquement si verifies.
* : identification heritee a revalider ; NI : materiel non identifie.
Les quantites concernent cette feuille.
R-006 : designation conservee au registre des reserves.
Modeles, prescriptions et sources : bordereau page 2.

experts conseils

| HF Experts-Conseils - Mécanique et électricité du bâtiment |
| 7375A rue Beaubien Est, Anjou, QC, H1M 3R5 |
| (514).655.9694 |
| hfec-ing.com |

No.	DATE:	ÉMISSION:
01	2026-09-16	ÉMIS POUR APPEL D'OFFRE
A	2026-08-28	ÉMIS POUR COORDINATION PRÉLIM.

SCEAU:

INGÉNIEURS Hamid Haddad 026451 QUÉBEC
2026-09-16

ARCHITECTE:

CLIENT:

Brossard

PROJET:

TECHNOLOGIE RFID

BIBLIOTHÈQUE GEORGETTE-LEPAGE - TRAVAUX D'AMÉNAGEMENT DU REZ-DE-CHAUSSÉE ET DE L'ÉTAGE

NO APPEL D'OFFRES : SP-GTER-26-0080

TITRE DU PLAN

ÉCLAIRAGE ET ALARME INCENDIE EXISTANT/DÉMOLITION REZ-DE-CHAUSSÉE

No DE DOSSIER	26-29		
DESSINÉ PAR:	P. ELISEEV		
PRÉPARÉ PAR:	P. ELISEEV		
VÉRIFIÉ PAR:	R. HADDAD, Ing.		
ÉCHELLE:	1:100	FORMAT	841X594
DATE:	JUILLET 2026		

PLAN E-201

BORDEREAU MATERIEL - E201

106 reperes sur cette feuille - prescriptions recopiees du devis et du releve verifie.

Les modeles non renseignes restent a preciser. Les circuits divergents exigent une clarification.

ID	Qte	Famille	Modele / type	Prescription du devis	Source / reserve
BC	2	BOITIER "C" (HORS LEGENDE - R-006 TEST-E201)	C; C PP-U1 7 PP-2 MODELE NON PRECISE	BOITIER "C" (hors légende - R-006 TEST-E201)	E-001 légende ; bloc S218
BC	1	BOITIER "C" (HORS LEGENDE - R-006 TEST-E201)	C PP-U1 DM (J) 7 MODELE NON PRECISE	BOITIER "C" (hors légende - R-006 TEST-E201)	E-001 légende ; bloc S218
BJ	2	BOITE DE JONCTION	(MA) P-2 39 (MA); (MA) P-2 41 MODELE NON PRECISE	BOITE DE JONCTION	E-001 légende ; bloc S107
DF	3	DETECTEUR DE FUMEE	MODELE NON PRECISE	DÉTECTEUR DE FUMÉE	E-001 légende ; bloc S146
DF	1	DETECTEUR DE FUMEE	MODELE NON PRECISE	DÉTECTEUR DE FUMÉE	E-001 légende ; bloc S146
DF	1	DETECTEUR DE FUMEE	MODELE NON PRECISE	DÉTECTEUR DE FUMÉE	E-001 légende ; bloc S146
DM	2	DETECTEUR DE MOUVEMENT	MODELE NON PRECISE	DETECTEUR DE MOUVEMENT	E-001 légende ; bloc S313
DM	1	DETECTEUR DE MOUVEMENT	(J) DM C MODELE NON PRECISE	DETECTEUR DE MOUVEMENT	E-001 légende ; bloc S313
EN	9	APPAREIL D'ECLAIRAGE ENCASTRE	PP-2 3 C; 2 PP-U1; 3 PP-2; 3 (MF) PP-2; 3 (MF) PP-2 C; 3 (MA) PP-2 MODELE NON PRECISE	APPAREIL D'ÉCLAIRAGE ENCASTRÉ	E-001 légende ; bloc S014
EN	19	APPAREIL D'ECLAIRAGE ENCASTRE	5 (MA) PP-2; 3 (MF) PP-2 1 C; 3 (MF) PP-2; 5 (MA) PP-2 (MA); 2 PP-U1; 3 (MA) PP-2 MODELE NON PRECISE	APPAREIL D'ÉCLAIRAGE ENCASTRÉ	E-001 légende ; bloc S014
IS	4	INTERRUPTEUR SIMPLE	(J) (K); (K) (J); (N) MODELE NON PRECISE	INTERRUPTEUR SIMPLE	E-001 légende ; bloc S098
IS	1	INTERRUPTEUR SIMPLE	(J) C DM MODELE NON PRECISE	INTERRUPTEUR SIMPLE	E-001 légende ; bloc S098
L2	37	APPAREIL D'ECLAIRAGE 2'X2' LED	PP-2 (H,I) 3; PP-2 (N) 3; PP-U1 2; 3 PP-2 (I) 7; PP-U1 2 PP-U1; PP-2 (N) 3 (N); PP-2 (J,K) 3 MODELE NON PRECISE	APPAREIL D'ÉCLAIRAGE 2'x2' LED	E-001 légende ; bloc S024
L2	8	APPAREIL D'ECLAIRAGE 2'X2' LED	PP-2 (J,K) 3; (J,K) PP-2 3; PP-U1 2 MODELE NON PRECISE	APPAREIL D'ÉCLAIRAGE 2'x2' LED	E-001 légende ; bloc S024
LX	5	APPAREIL D'ECLAIRAGE 'X4'	PP-2 3; (J,K) PP-2 3 MODELE NON PRECISE	APPAREIL D'ÉCLAIRAGE 'x4'	E-001 légende ; bloc S035
LX	6	APPAREIL D'ECLAIRAGE 'X4'	PP-U1 2; PP-2 6 (MF) MODELE NON PRECISE	APPAREIL D'ÉCLAIRAGE 'x4'	E-001 légende ; bloc S035
SM	4	STATION MANUELLE	F F PP-2; F MODELE NON PRECISE	STATION MANUELLE	E-001 légende ; bloc S319


0" 6" 12"

NOTE GÉNÉRALE:

1. Sauf indications contraire, tous les équipements sont existants à conserver.
2. L'entrepreneur en électricité sera responsable d'enlever tout autre équipement non montré en plan lorsque des murs ou des plafonds sont pour démolition. Retirée l'alimentation de ces équipements jusqu'au panneau et la composante à conserver.
3. L'entrepreneur en électricité doit vérifier le bon fonctionnement des prises électrique existante montré aux plans.
4. Les travaux d'alarme incendie seront réalisés par l'électricien

NOTE SPÉCIFIQUE:

1. Tous les appareils d'éclairage doivent être temporairement retirés pendant les travaux dans cette pièce, puis réinstallés une fois les travaux terminés. Alimentation par panneaux électiques PP-3 et PPU-1 à 347V et P-4 et PU-1 à 120V.

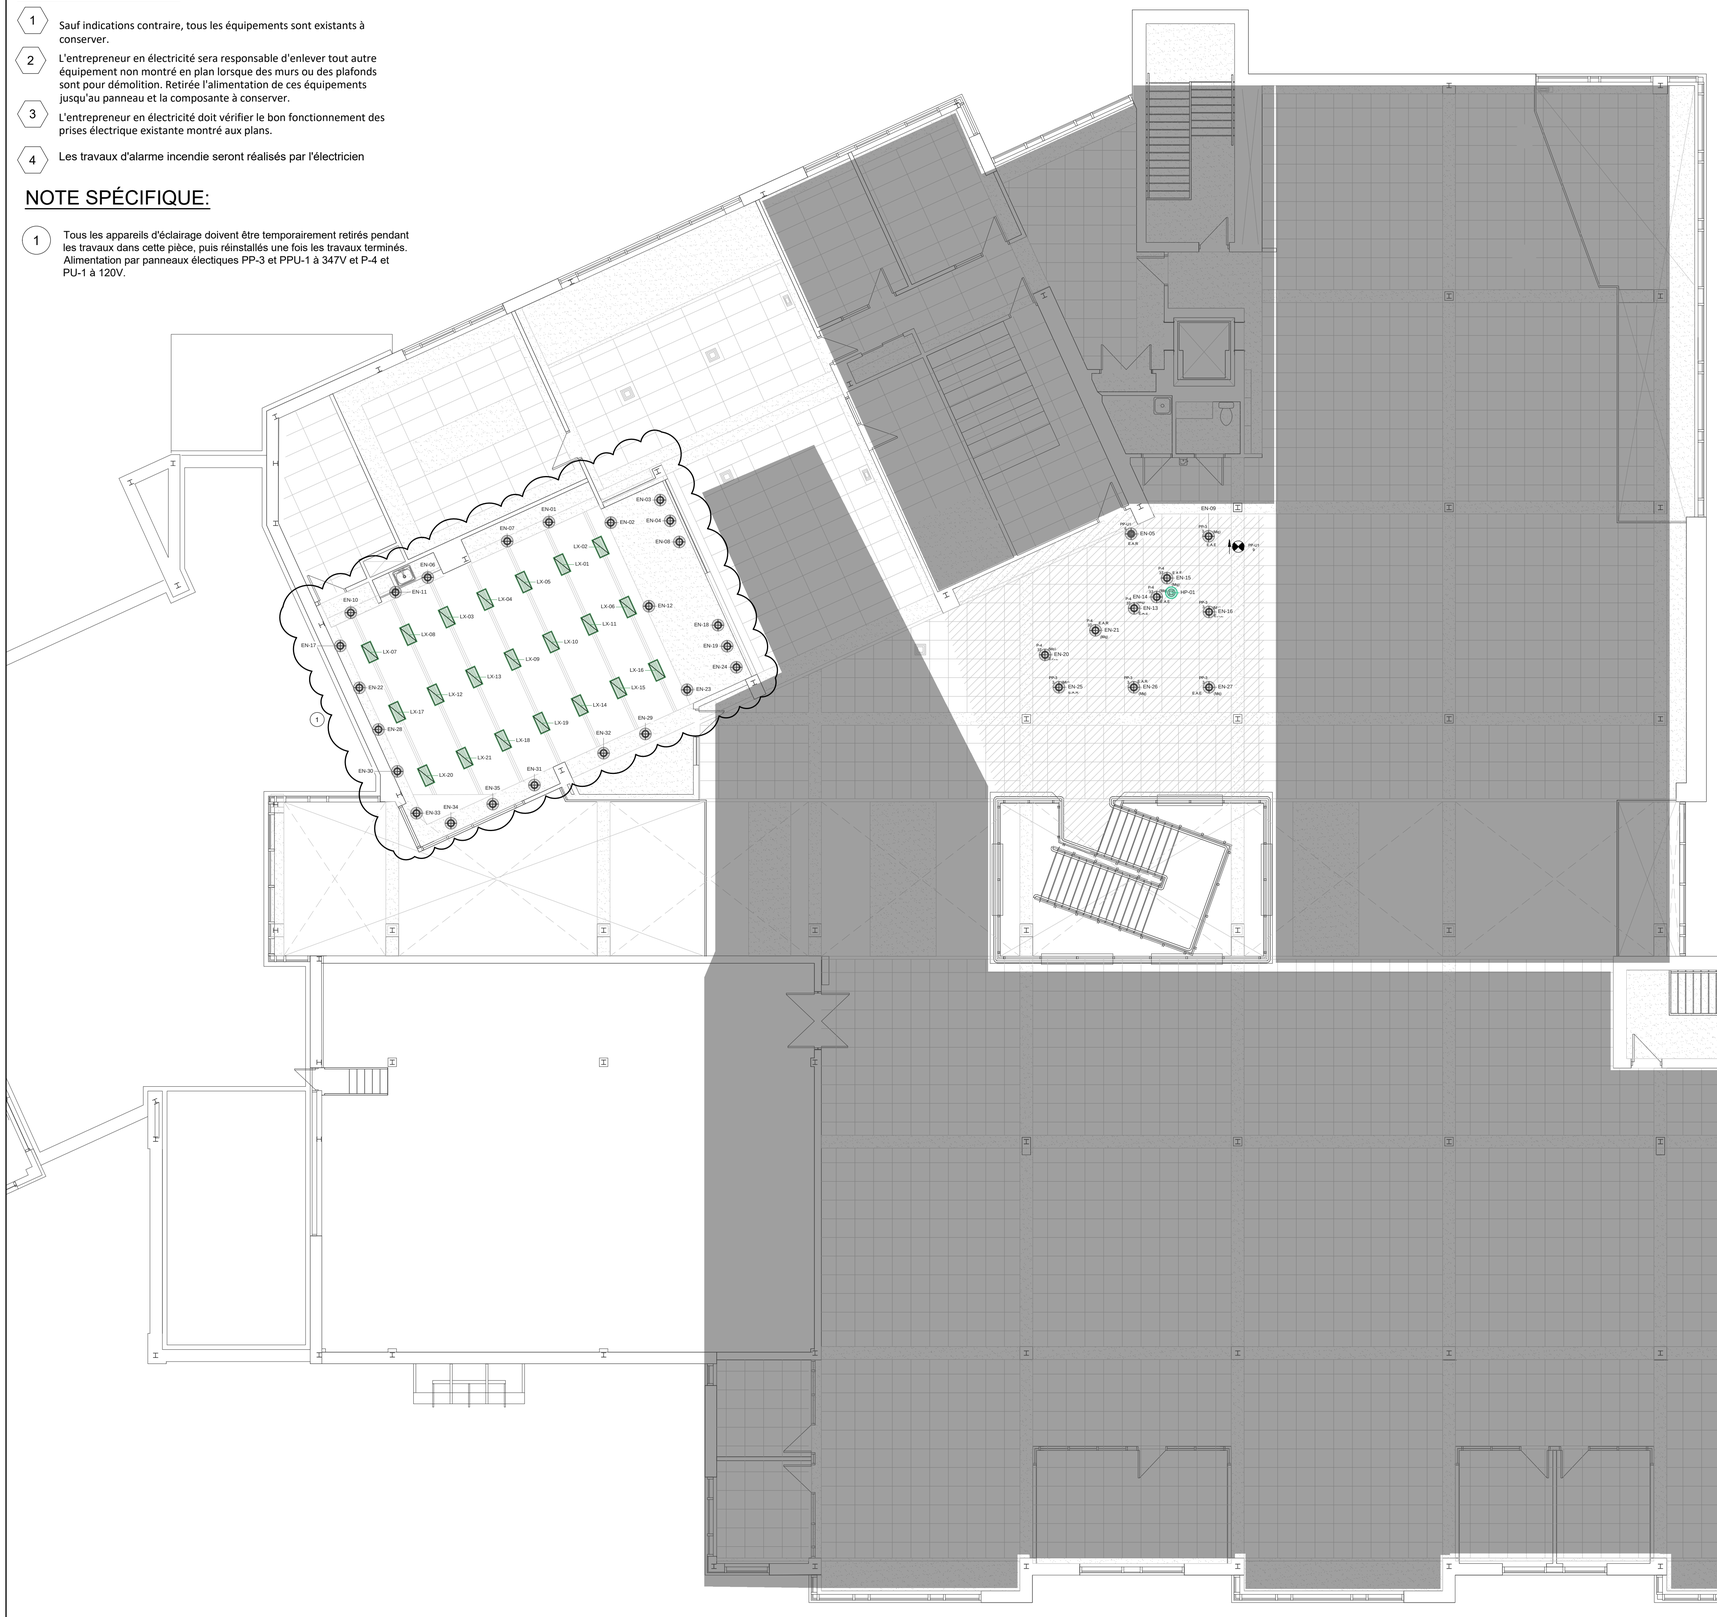

RELEVE E202 - MATERIEL

57 reperes / 3 familles / calques activables

0 non identifies - 0 identifications a revalider (*)

	EN	APPAREIL D'ECLAIRAGE ENCASTRE	35
	HP	HAUT-PARLEUR ENCASTRE AU PLAFOND	1
	LX	APPAREIL D'ECLAIRAGE 'X4'	21

PL : rectangles aux dimensions graphiques du plan.
W et circuits affiches uniquement si verifies.
* : identification heritee a revalider ; NI : materiel non identifie.
Les quantites concernent cette feuille.
Modeles, prescriptions et sources : bordereau page 2.

experts conseils

| HF Experts-Conseils - Mécanique et électricité du bâtiment |
| 7375A rue Beaubien Est, Anjou, QC, H1M 3R5 |
| (514).655.9694 |
| hfec-ing.com |

No.	DATE:	ÉMISSION:
01	2026-09-16	ÉMIS POUR APPEL D'OFFRE
A	2026-08-28	ÉMIS POUR COORDINATION PRÉLIM.

SCEAU:

INGÉNIEURS Hanni Haddad 026451 QUÉBEC
2026-09-16

ARCHITECTE:

CLIENT:

Brossard

PROJET:

TECHNOLOGIE RFID
BIBLIOTHÈQUE GEORGETTE-LEPAGE - TRAVAUX D'AMÉNAGEMENT DU REZ-DE-CHAUSSÉE ET DE L'ÉTAGE

NO APPEL D'OFFRES : SP-GTER-26-0080

TITRE DU PLAN

ÉCLAIRAGE ET ALARME INCENDIE EXISTANT/DÉMOLITION 2E ÉTAGE

No DE DOSSIER	26-29		
DESSINÉ PAR:	P. ELISEEV		
PRÉPARÉ PAR:	P. ELISEEV		
VÉRIFIÉ PAR:	R. HADDAD, Ing.		
ÉCHELLE:	1:100	FORMAT	841X594
DATE:	JUILLET 2026		

PLAN E-202

BORDEREAU MATERIEL - E202


57 reperes sur cette feuille - prescriptions recopiees du devis et du releve verifie.

Les modeles non renseignes restent a preciser. Les circuits divergents exigent une clarification.

ID	Qte	Famille	Modele / type	Prescription du devis	Source / reserve
EN	24	APPAREIL D'ECLAIRAGE ENCASTRE	MODELE NON PRECISE	APPAREIL D'ÉCLAIRAGE ENCASTRÉ	E-001 légende ; bloc S014
EN	4	APPAREIL D'ECLAIRAGE ENCASTRE	6 PP-U1; 37 (MQ) P-4; 3 (MQ) PP-3 MODELE NON PRECISE	APPAREIL D'ÉCLAIRAGE ENCASTRÉ	E-001 légende ; bloc S014
EN	7	APPAREIL D'ECLAIRAGE ENCASTRE	3 (MQ) PP-3; 37 (MQ) P-4 37; 37 (MQ) P-4 (MQ) (MQ); 37 (MQ) P-4 (MQ) P-4 37; 37 (MQ) P-4 MODELE NON PRECISE	APPAREIL D'ÉCLAIRAGE ENCASTRÉ	E-001 légende ; bloc S014
HP	1	HAUT-PARLEUR ENCASTRE AU PLAFOND	(MQ) (MQ) P-4 37 37 MODELE NON PRECISE	HAUT-PARLEUR ENCASTRÉ AU PLAFOND	E-001 légende ; bloc S321
LX	21	APPAREIL D'ECLAIRAGE 'X4'	MODELE NON PRECISE	APPAREIL D'ÉCLAIRAGE 'x4'	E-001 légende ; bloc S035

NOTE GÉNÉRALE:

1. Sauf indication d'une lettre du tableau des appareils d'éclairage, tous les équipements sont existants à conserver.
2. L'entrepreneur en électricité sera responsable d'enlever tout autre équipement non montré en plan lorsque des murs ou des plafonds sont pour démolition. Retirée l'alimentation de ces équipements jusqu'au panneau et la composante à conserver.
3. Sauf indications contraire, tous les systèmes de contrôle d'éclairage sont existants à conserver.
4. Valider la position exacte de toute les appareils d'éclairage avec le client.
5. Réutiliser les circuits des appareils d'éclairage existant pour alimenter les nouveaux appareils d'éclairage.
6. Les circuits identifiés aux plans sont à titre indicatif seulement. Afin de conserver les charges actuelles réutiliser les circuits libérés lors du démantèlement et réalimenter lorsque requis les nouveaux besoins.
7. Chute de tension limité à 3% tel que l'article (8-102-1-c) pour les artères de dérivation.Prévoir calibre plus élevé pour le filage. Il est de la responsabilité du contracteur de choisir le bon calibre pour le filage.

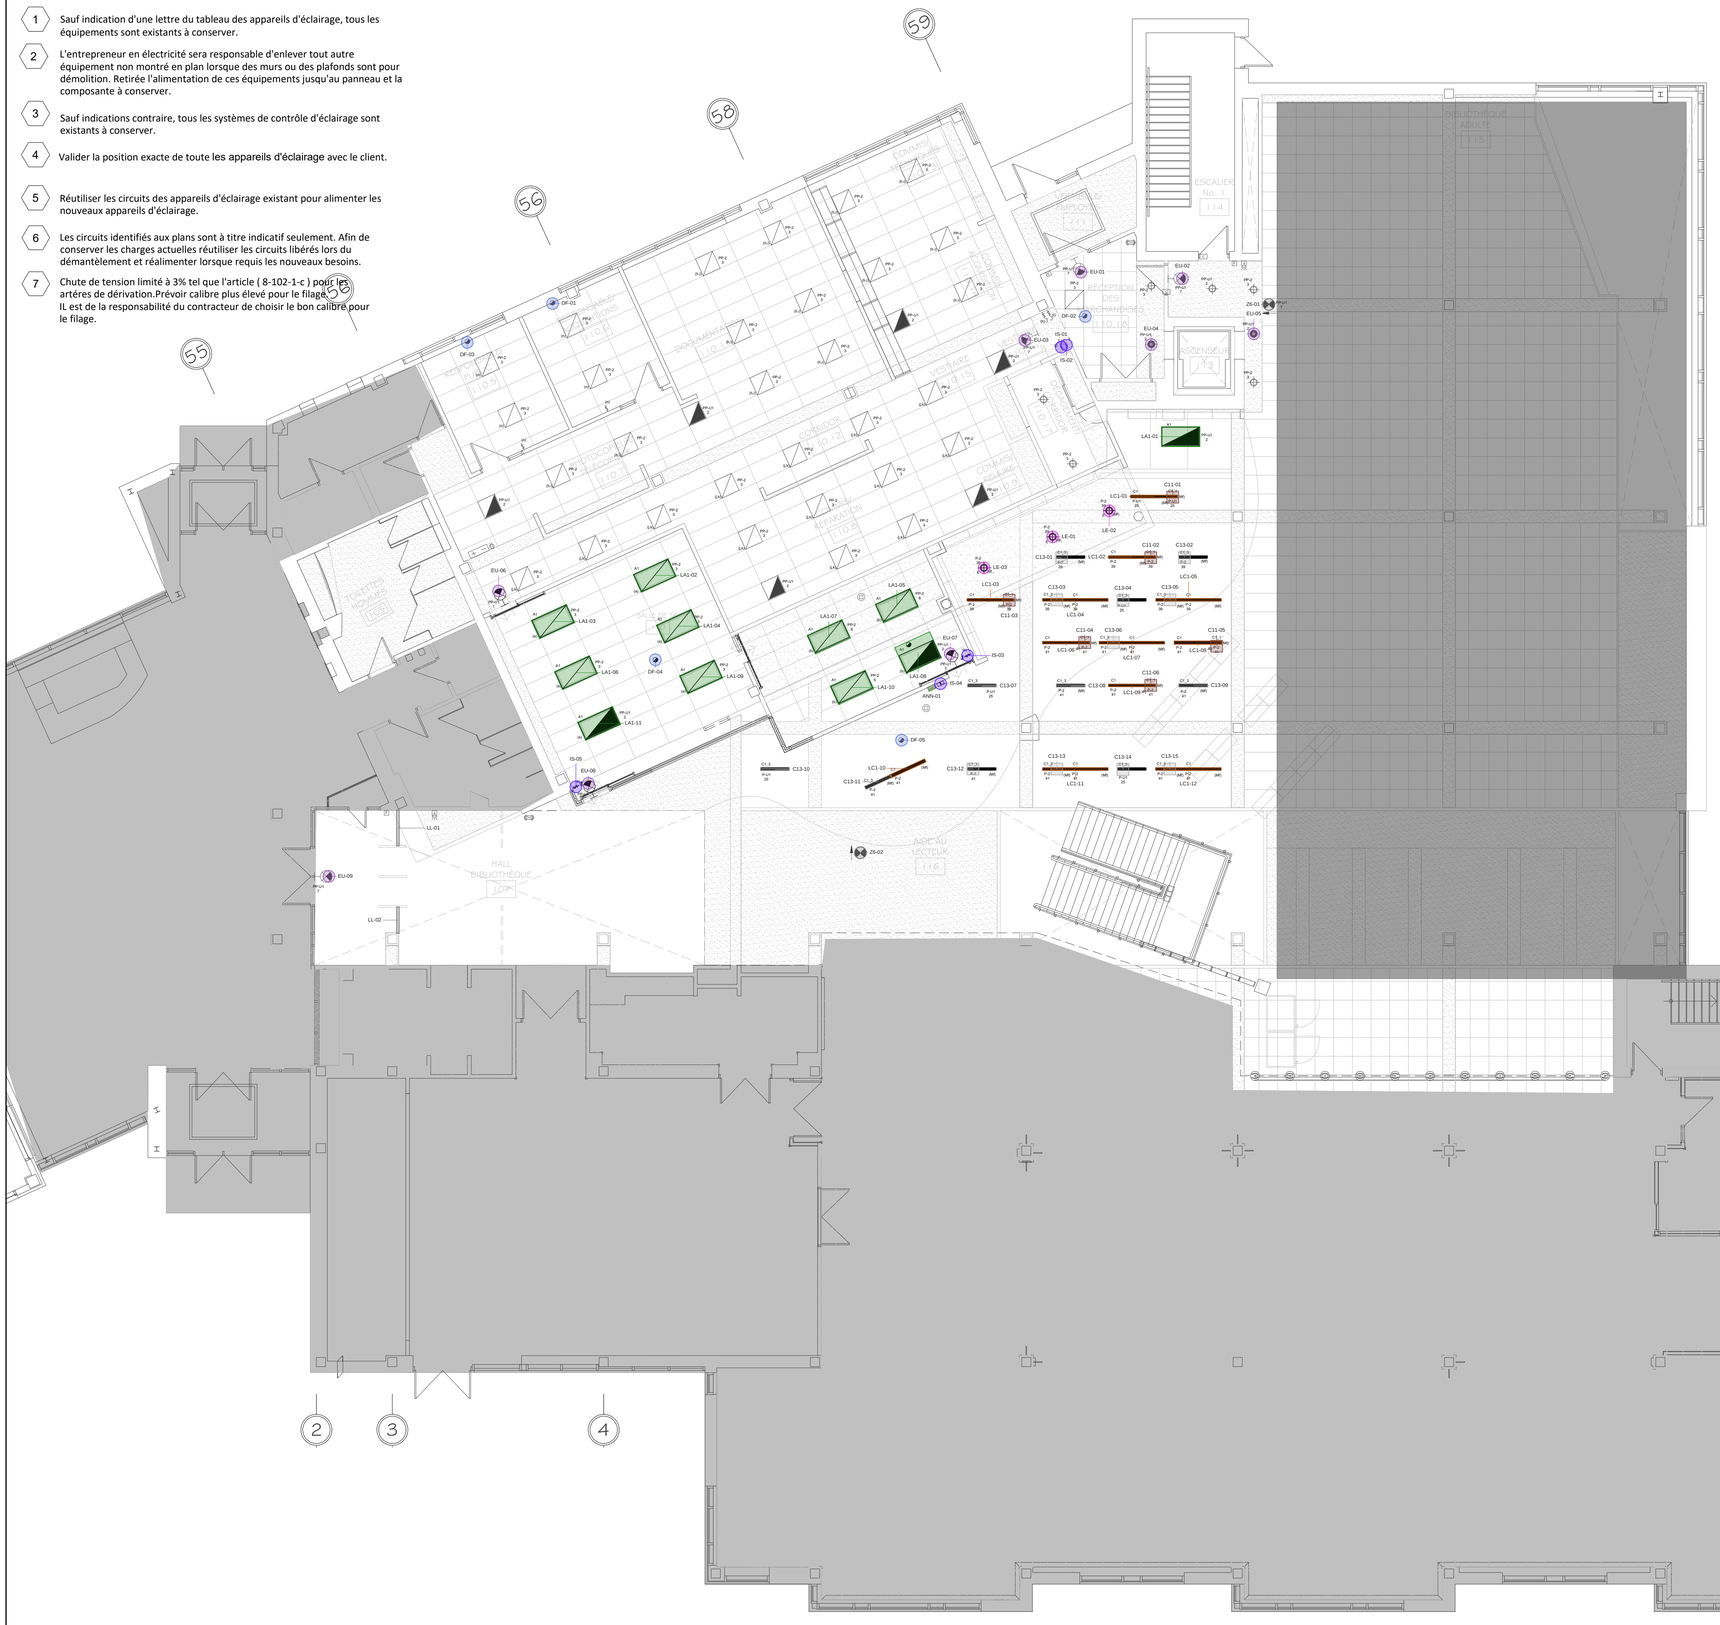

BORDEREAU MATERIEL - E203


71 reperes sur cette feuille - prescriptions recopiees du devis et du releve verifie.

Les modeles non renseignes restent a preciser. Les circuits divergents exigent une clarification.

ID	Qte	Famille	Modele / type	Prescription du devis	Source / reserve
ANN	1	PANNEAU ANNONCIATEUR	MODELE NON PRECISE	PANNEAU ANNONCIATEUR	E-001 légende ; bloc S328
C11	6	APPAREIL D'ECLAIRAGE TYPE C1_1	(MF) P-U1 P-U1 (MF) 25 25; (MF) P-2 P-2 (MF) 39 39; (MF) P-2 P-2 (MF) 41 41 P-2 41; (MF) (MF) P-2 41; (MF) P-2 P-2 (MF) 41 41 C1_1	Luminaire type C1_1 (tableau E-008)	E203 étiquettes
C13	15	APPAREIL D'ECLAIRAGE TYPE C1_3	(MF) P-2 39 (MF); (MF) P-2 39; P-U1 25 (MF) P-2 39; P-U1 25; P-2 (MF) 41; (MF) P-2 41; P-2 (MF) 41 P-2 41; P-U1 25 (MF) P-2 41 C1_3	Luminaire type C1_3 (tableau E-008)	E203 étiquettes
DF	3	DETECTEUR DE FUMEE	MODELE NON PRECISE	DÉTECTEUR DE FUMÉE	E-001 légende ; bloc S146
DF	2	DETECTEUR DE FUMEE	(A) MODELE NON PRECISE	DÉTECTEUR DE FUMÉE	E-001 légende ; bloc S146
EU	9	APPAREIL D'ECLAIRAGE ENCASTRE SUR CIRCUIT D'URGENCE PP-U1 (QUART NOIR)	MODELE NON PRECISE	APPAREIL D'ÉCLAIRAGE ENCASTRÉ SUR CIRCUIT D'URGENCE PP-U1 (quart noir)	E-001 légende ; instances manuelles
IS	5	INTERRUPTEUR SIMPLE	(J) (K); (K) (J); (B) PP-U1; 7; (A) PP-U1 7 MODELE NON PRECISE	INTERRUPTEUR SIMPLE	E-001 légende ; bloc S098
LA1	11	APPAREIL D'ECLAIRAGE TYPE A1	PP-U1 2; PP-2 3 (A); PP-2 (A) 3; DE PP-2 3 (A); PP-2 (B) 6; PP-U1 PP-U1 (B) 2 7; PP-U1 (A) 2 A1	Luminaire type A1 (tableau E-008)	E203 étiquettes
LC1	12	APPAREIL D'ECLAIRAGE TYPE C1	(MF) P-U1 P-U1 (MF) 25 25; (MF) P-2 P-2 (MF) 39 39; (MF) P-2 P-2 (MF) 41 41 P-2 41; (MF) P-2 P-2 (MF) 41 41 (MF); (MF) P-2 P-2 (MF) 41 41; (MF) P-2 41 (MF) C1	Luminaire type C1 (tableau E-008)	E203 étiquettes
LE	3	APPAREIL D'ECLAIRAGE TYPE E	39 (MF) P-2 E	Luminaire type E (tableau E-008)	E203 étiquettes
LL	2	APPAREIL D'ECLAIRAGE LINEAIRE (BARRE C1 / C1_1 / C1_3 - TYPE LU SUR L'ETIQUETTE)	F MODELE NON PRECISE	APPAREIL D'ÉCLAIRAGE LINÉAIRE (barre C1 / C1_1 / C1_3 - type lu sur l'étiquette)	E-001 légende ; bloc S044
Z6	2	ENSEIGNE DE SORTIE DE TYPE PICTOGRAMME Z6 (STANPRO RMSOWH-UDC - TABLEAU E-008)	MODELE NON PRECISE	ENSEIGNE DE SORTIE DE TYPE PICTOGRAMME Z6 (Stanpro RMSOWH-UDC - tableau E-008)	E-001 légende ; instances manuelles

NOTE GÉNÉRALE:

1. Sauf indication d'une lettre du tableau des appareils d'éclairage, tous les équipements sont existants à conserver.
2. L'entrepreneur en électricité sera responsable d'enlever tout autre équipement non montré en plan lorsque des murs ou des plafonds sont pour démolition. Retirée l'alimentation de ces équipements jusqu'au panneau et la composante à conserver.
3. Sauf indications contraire, tous les systèmes de contrôle d'éclairage sont existants à conserver.
4. Valider la position exacte de toute les appareils d'éclairage avec le client.
5. Réutiliser les circuits des appareils d'éclairage existant pour alimenter les nouveaux appareils d'éclairage.
6. Les circuits identifiés aux plans sont à titre indicatif seulement. Afin de conserver les charges actuelles réutiliser les circuits libérés lors du démantèlement et réalimenter lorsque requis les nouveaux besoins.
7. Chute de tension limité à 3% tel que l'article (8-102-1-c) pour les artères de dérivation.Prévoir calibre plus élevé pour le filage. IL est de la responsabilité du contracteur de choisir le bon calibre pour le filage.

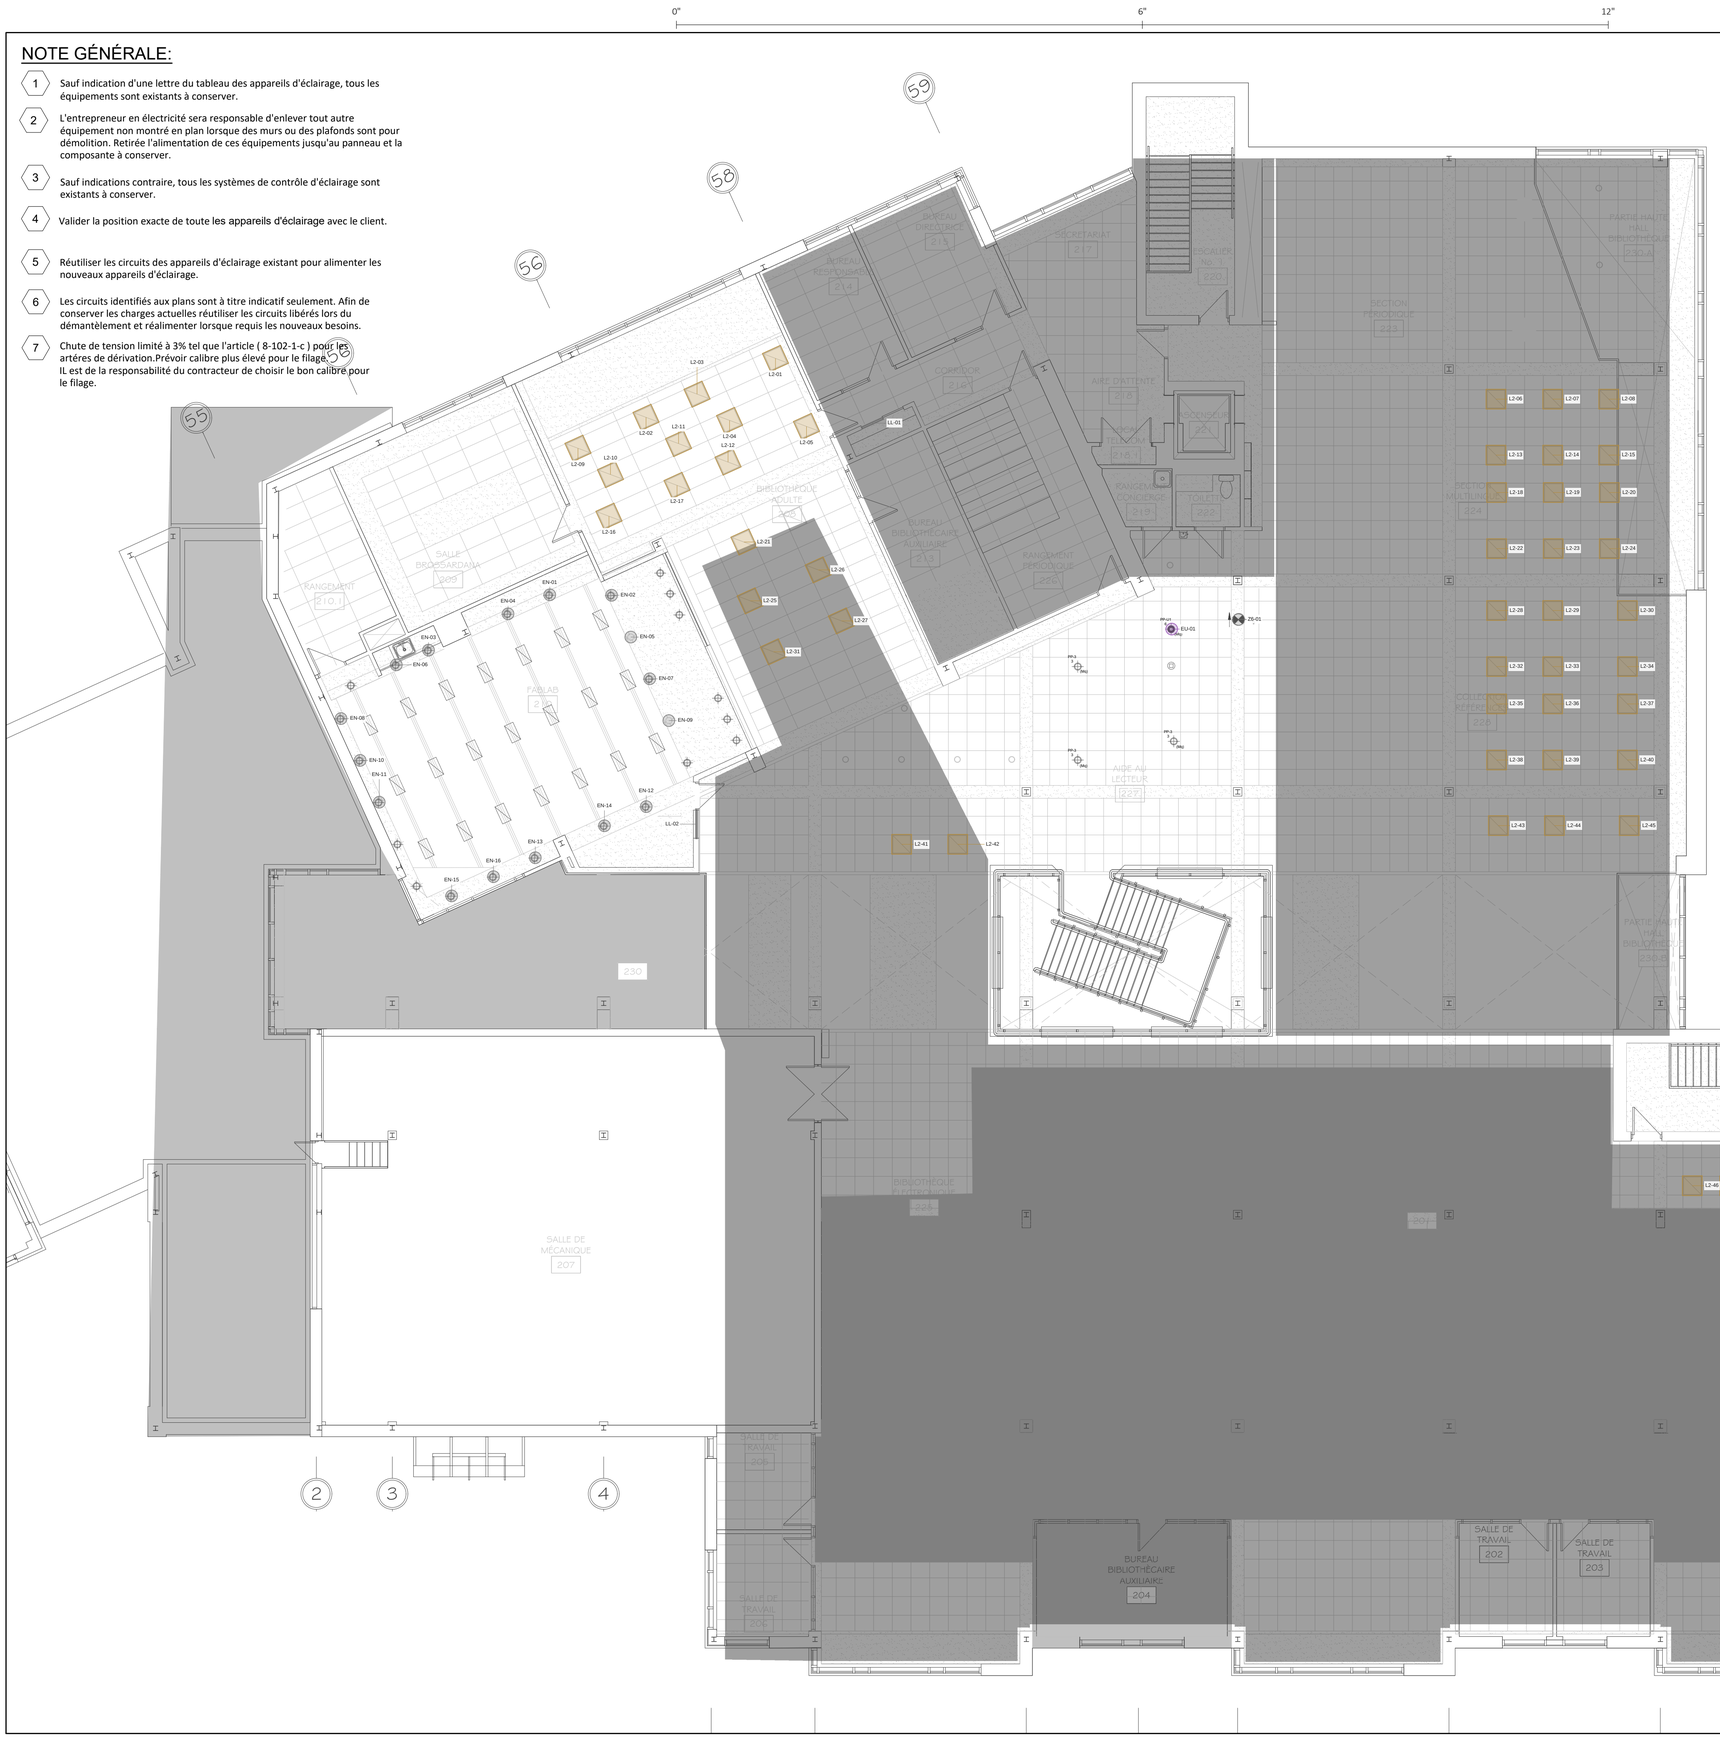

RELEVE E204 - MATERIEL

69 reperes / 5 familles / calques activables

0 non identifies - 0 identifications a revalider (*)

	EN	APPAREIL D'ECLAIRAGE ENCASTRE	16
	EU	APPAREIL D'ECLAIRAGE ENCASTRE SUR CIRCUIT D'URGENCE PP-U1 (QUART N...	1
	L2	APPAREIL D'ECLAIRAGE 2'X2' LED	49
	LL	APPAREIL D'ECLAIRAGE LINEAIRE (BARRE C1 / C1_1 / C1_3 - TYPE LU SUR L'ETIQU...	2
	Z6	ENSEIGNE DE SORTIE DE TYPE PICTOGRAMME Z6 (STANPRO RMSOWH-UDC - TABLEAU E-0...	1

PL : rectangles aux dimensions graphiques du plan.
W et circuits affiches uniquement si verifies.
* : identification heritee a revalider ; NI : materiel non identifie.
Les quantites concernent cette feuille.
Modeles, prescriptions et sources : bordereau page 2.

experts conseils

| HF Experts-Conseils - Mécanique et électricité du bâtiment |
| 7375A rue Beaubien Est, Anjou, QC, H1M 3R5 |
| (514).655.9694 |
| hfec-inc.com |

No.	DATE:	ÉMISSION:
01	2026-09-16	ÉMIS POUR APPEL D'OFFRE
A	2026-08-28	ÉMIS POUR COORDINATION PRÉLIM.

SCEAU:

INGÉNIEURS Hanni Haddad 5026451 QUÉBEC
2026-09-16

ARCHITECTE:

CLIENT:

Brossard

PROJET:

TECHNOLOGIE RFID

BIBLIOTHÈQUE GEORGETTE-LEPAGE - TRAVAUX D'AMÉNAGEMENT DU REZ-DE-CHAUSSÉE ET DE L'ÉTAGE

NO APPEL D'OFFRES : SP-GTER-26-0080

TITRE DU PLAN

ÉCLAIRAGE ET ALARME INCENDIE NOUVEAU 2E ÉTAGE

No DE DOSSIER	26-29		
DESSINÉ PAR:	P. ELISEEV		
PRÉPARÉ PAR:	P. ELISEEV		
VÉRIFIÉ PAR:	R. HADDAD, Ing.		
ÉCHELLE:	1:100	FORMAT	841X594
DATE:	JUILLET 2026		

PLAN E-204

BORDEREAU MATERIEL - E204

69 reperes sur cette feuille - prescriptions recopiees du devis et du releve verifie.

Les modeles non renseignes restent a preciser. Les circuits divergents exigent une clarification.

ID	Qte	Famille	Modele / type	Prescription du devis	Source / reserve
EN	16	APPAREIL D'ECLAIRAGE ENCASTRE	MODELE NON PRECISE	APPAREIL D'ÉCLAIRAGE ENCASTRÉ	E-001 légende ; bloc S014
EU	1	APPAREIL D'ECLAIRAGE ENCASTRE SUR CIRCUIT D'URGENCE PP-U1 (QUART NOIR)	MODELE NON PRECISE	APPAREIL D'ÉCLAIRAGE ENCASTRÉ SUR CIRCUIT D'URGENCE PP-U1 (quart noir)	E-001 légende ; instances manuelles
L2	49	APPAREIL D'ECLAIRAGE 2'X2' LED	MODELE NON PRECISE	APPAREIL D'ÉCLAIRAGE 2'x2' LED	E-001 légende ; bloc S024
LL	2	APPAREIL D'ECLAIRAGE LINEAIRE (BARRE C1 / C1_1 / C1_3 - TYPE LU SUR L'ETIQUETTE)	MODELE NON PRECISE	APPAREIL D'ÉCLAIRAGE LINÉAIRE (barre C1 / C1_1 / C1_3 - type lu sur l'étiquette)	E-001 légende ; bloc S044
Z6	1	ENSEIGNE DE SORTIE DE TYPE PICTOGRAMME Z6 (STANPRO RMSOWH-UDC - TABLEAU E-008)	MODELE NON PRECISE	ENSEIGNE DE SORTIE DE TYPE PICTOGRAMME Z6 (Stanpro RMSOWH-UDC - tableau E-008)	E-001 légende ; instances manuelles