

Rapport de métré (par plans) — PREUVE01

Généré le 2026-09-30 par le pipeline `releve/` (relevé automatique Claude + scripts déterministes). Chaque marque est une occurrence relevée sur le plan (étiquette texte vectorielle ou lecture visuelle) ; les quantités sont des comptes d'objets, sans métrage de câble.

Résumé

Feuille	Marques	Libellés
E103	6	6
Total	6	6

Tous les plans

Libellé	Famille	Quantité
DP1 nLight	commande	1
DP2 nLight	commande	1
PP1 nLight	commande	1
SO3 nLight	commande	1
SO4 nLight	commande	1
SW1 nLight	commande	1

E103

Libellé	Ce plan	Tous les plans
DP1 nLight	1	1
DP2 nLight	1	1
PP1 nLight	1	1
SO3 nLight	1	1
SO4 nLight	1	1
SW1 nLight	1	1

Nomenclature (libellé → source de la lecture)

Libellé	Famille	Description	Source
DP1 nLight	commande	Dispositif de controle nLight DP1 (carre etiquette sur le plan)	E103 symboles carres etiquetes + detail riser
DP2 nLight	commande	Dispositif de controle nLight DP2 (carre etiquette sur le plan)	E103 symboles carres etiquetes + detail riser
PP1 nLight	commande	Dispositif de controle nLight PP1 (carre etiquette sur le plan)	E103 symboles carres etiquetes + detail riser
SO3 nLight	commande	Detecteur/capteur nLight SO3 (carre etiquette sur le plan)	E103 symboles carres etiquetes + detail riser
SO4 nLight	commande	Detecteur/capteur nLight SO4 (carre etiquette sur le plan)	E103 symboles carres etiquetes + detail riser
SW1 nLight	commande	Interrupteur nLight SW1 (carre etiquette sur le plan)	E103 symboles carres etiquetes + detail riser


Réserves

Réserves — PREUVE01/E103 (test de mécanisme, pas un relevé de production)


Échantillon volontairement restreint à 6 repères (DP1, DP2, PP1, SO3, SO4, SW1), choisis parce que leur étiquette et leur symbole carré étaient directement vérifiables sur les tuiles générées par ce run de `prepare.py`. Le reste de la feuille E103 (dizaines d'autres symboles, risers, câblage CAT5e, notes) n'a PAS été relevé ici — hors périmètre de cette preuve de mécanisme.

R-001 E103 · Portée (INSTALLER/CONSERVER/EXISTANT) non confirmée visuellement pour les 6 repères : la feuille est un détail de contrôle d'éclairage « POUR SOUMISSION » qui suggère du neuf, mais aucune mention explicite « existant » ou « nouveau » n'a été vérifiée au zoom pour chaque symbole. Portée posée à « A PRECISER » sur les 6 lignes, sans deviner. R-002 E103 · SW6 (7e famille visible dans les risers, ex. « SW6 - ENTREPOT ») vu dans l'aperçu général mais NON relevé ici (hors échantillon) — ne pas déduire son absence du dossier. R-003 E103 · Identification des modèles (NPP16 D EFP 347, NPP PCD EFP, NPP20 PL BP, WSXA MWO PDT D WH, WSXA MWO PDT WH, NPODMA WH) lue directement sur le texte vectoriel adjacent à chaque symbole (détail de riser), pas dans une cédule de panneau séparée — à recouper avec la cédule si elle existe ailleurs dans le jeu de plans complet (non fourni pour cette preuve, une seule page).


1 nLight - CAISSE TYPE 0 Design 2

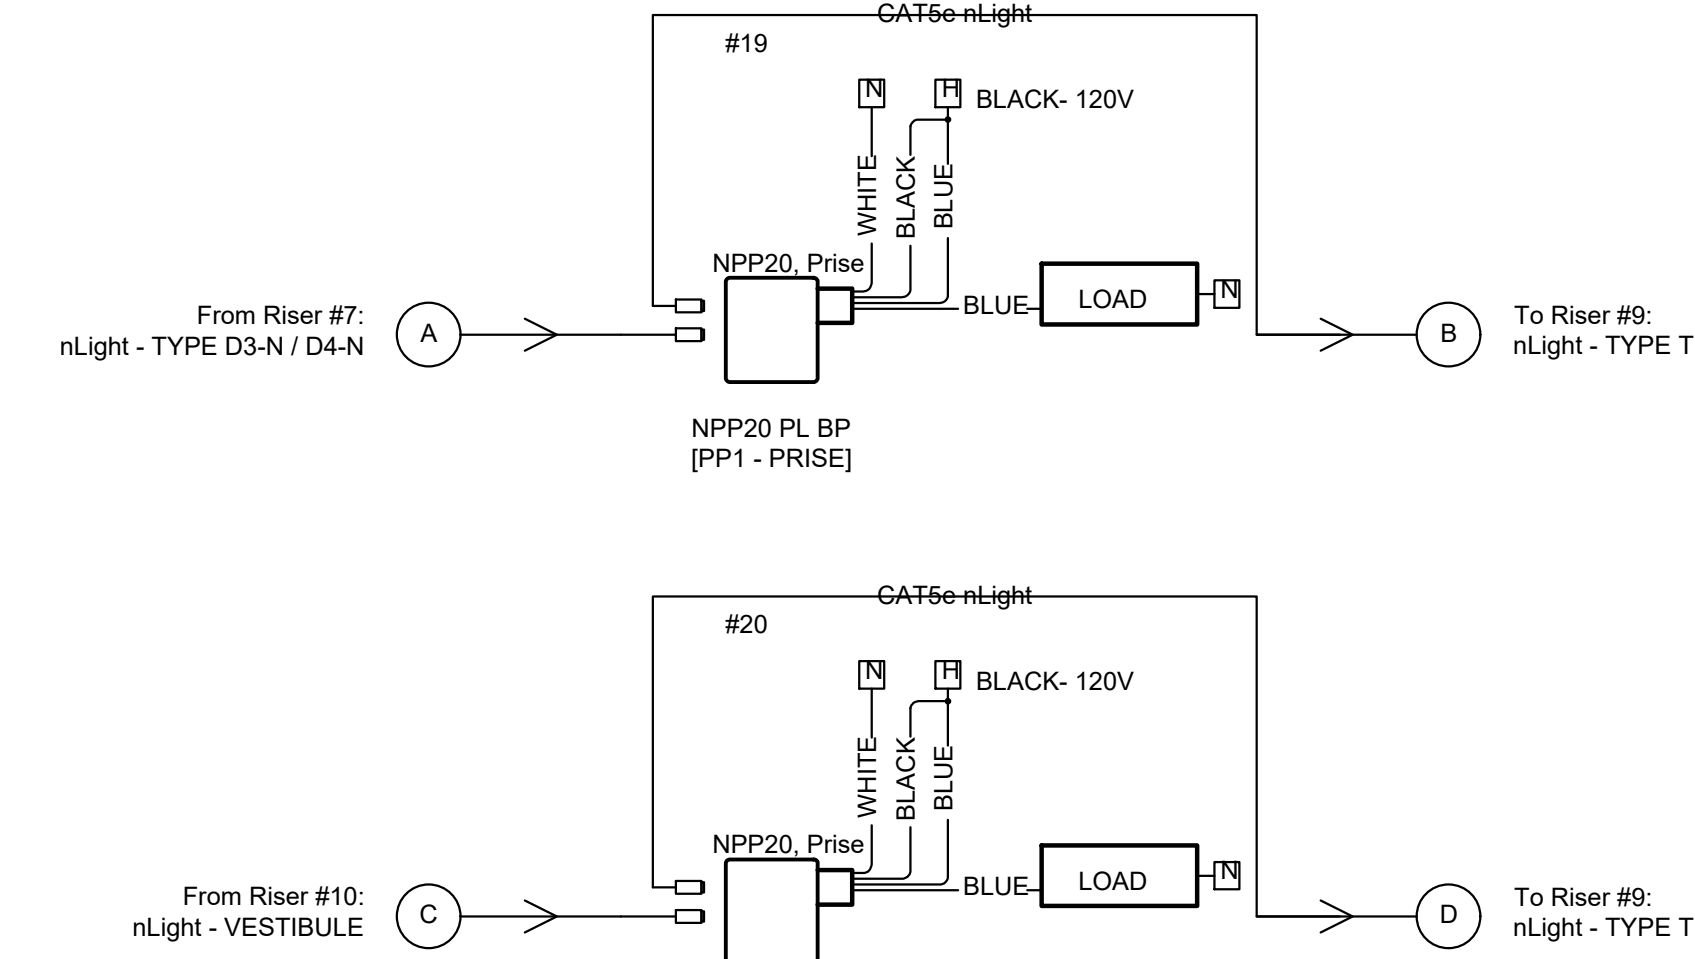


2 nLight - CAISSE TYPE D3-N / D4-N Design 2

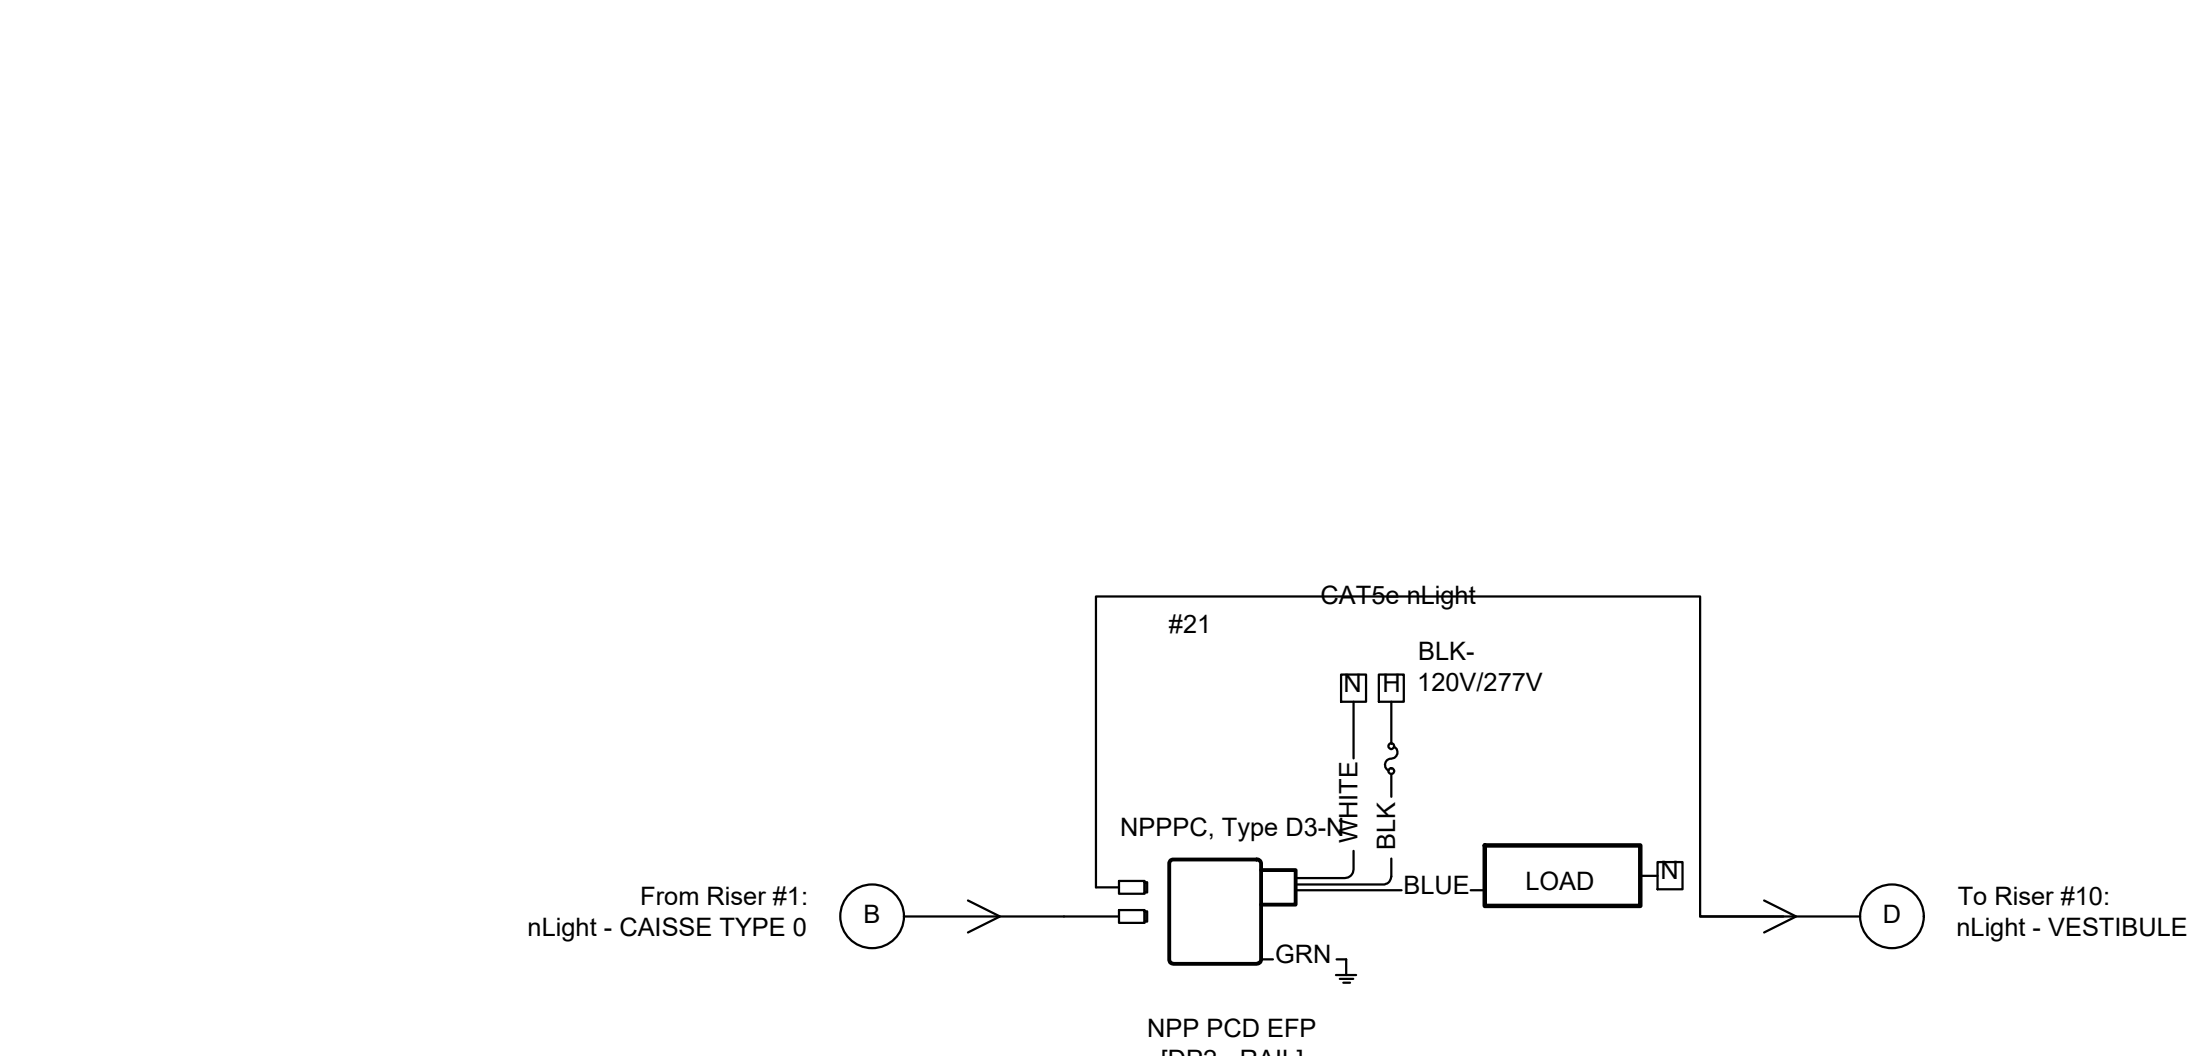

3 nLight - ENTREPOT Design 2

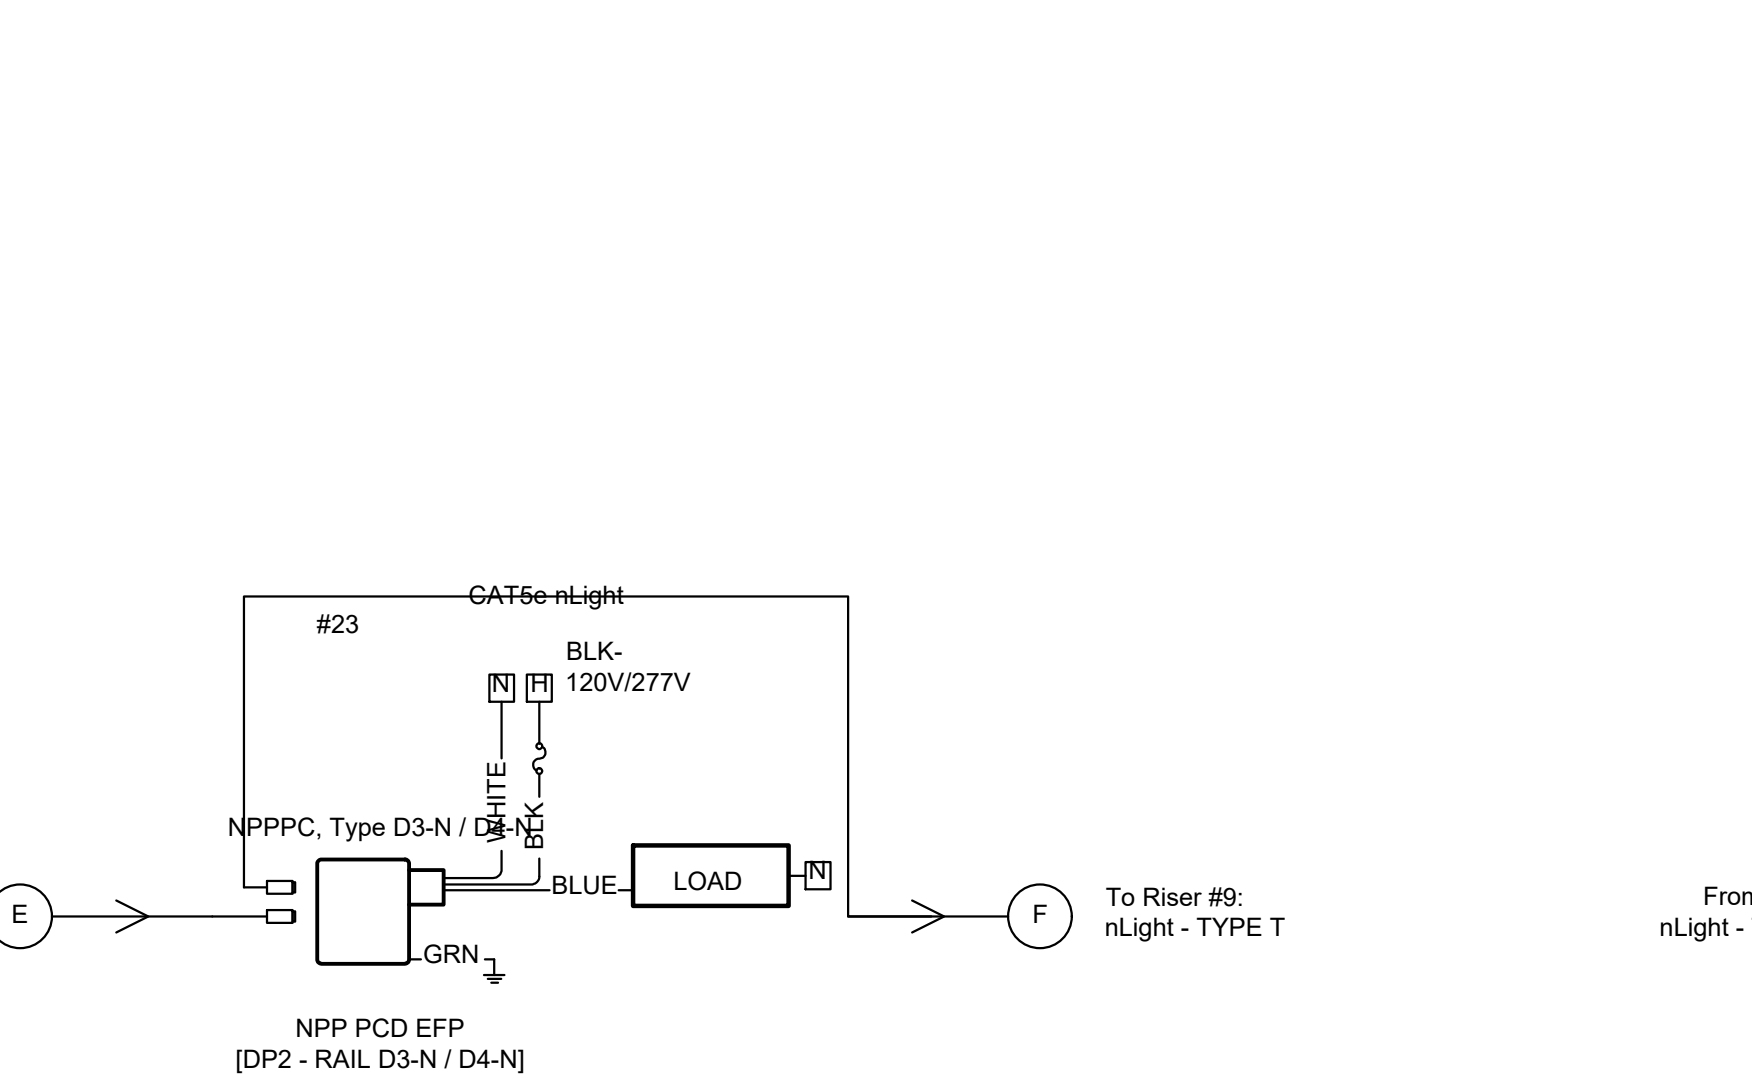


4 nLight - PRISE Design 2

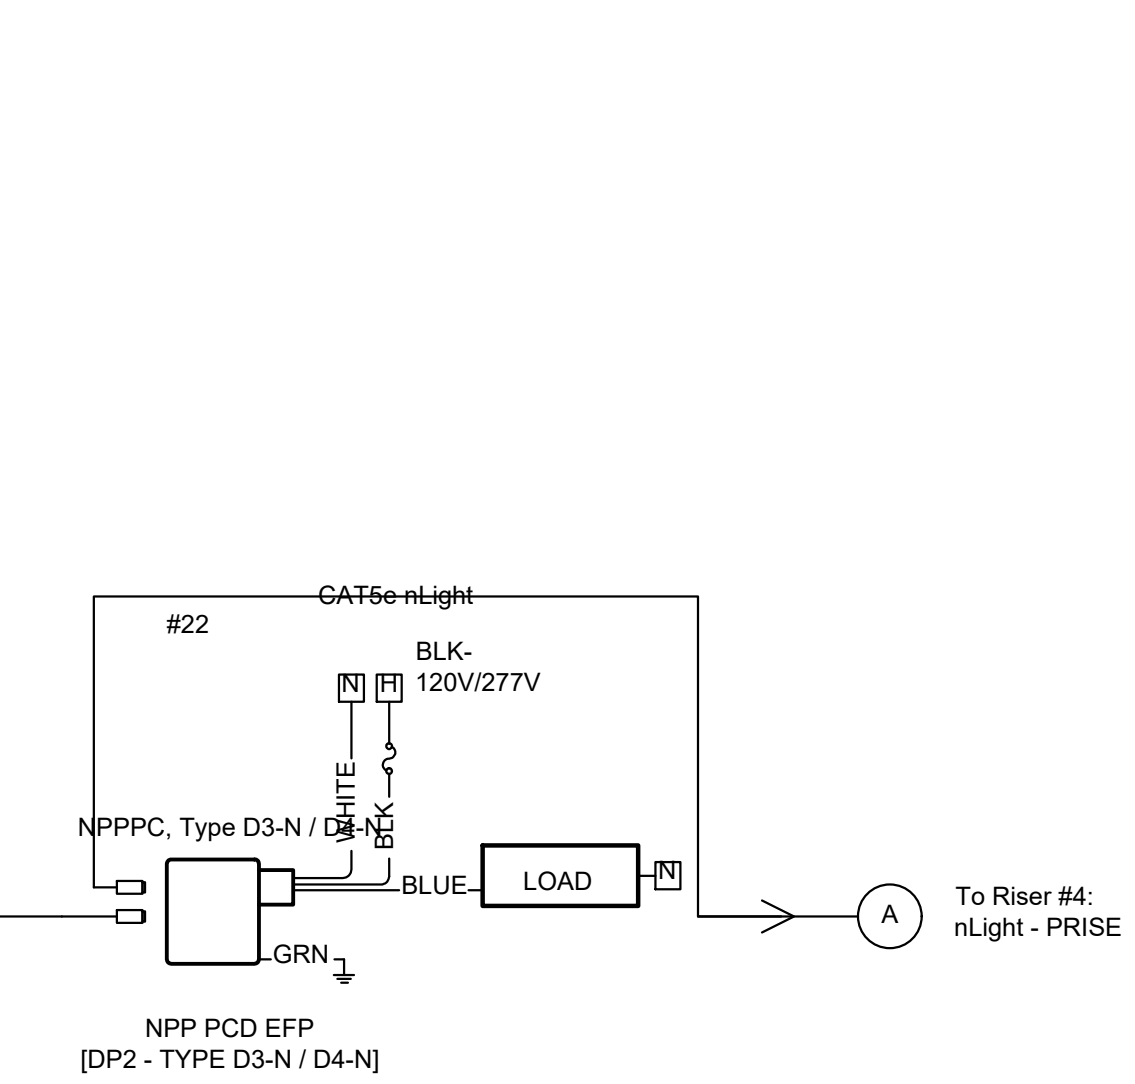


5 nLight - RAIL Design 2




6 nLight - RAIL D3-N / D4-N Design 2

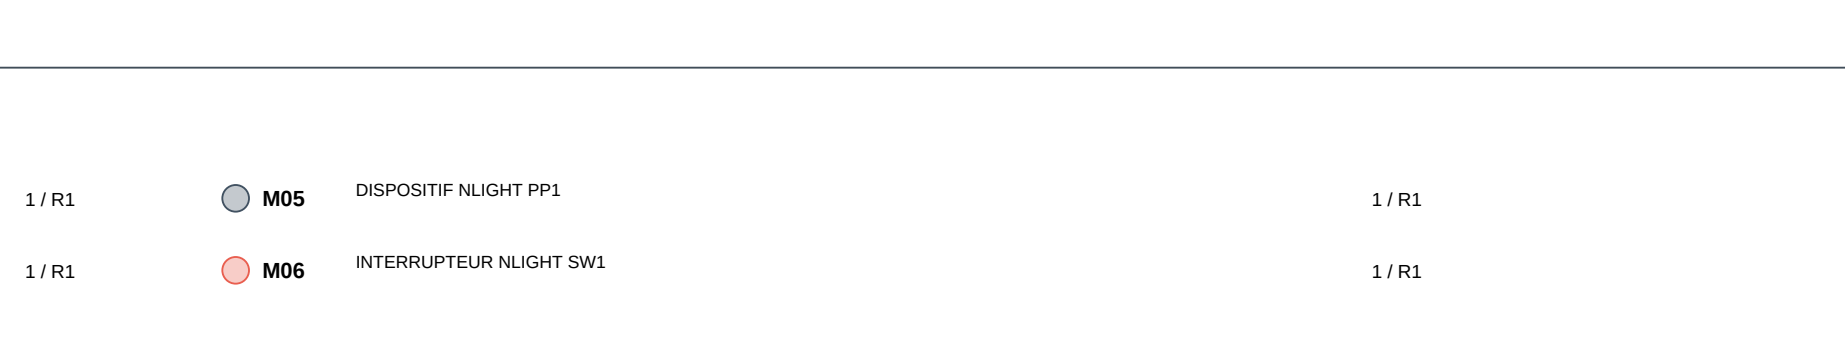


7 nLight - TYPE D3-N / D4-N Design 2

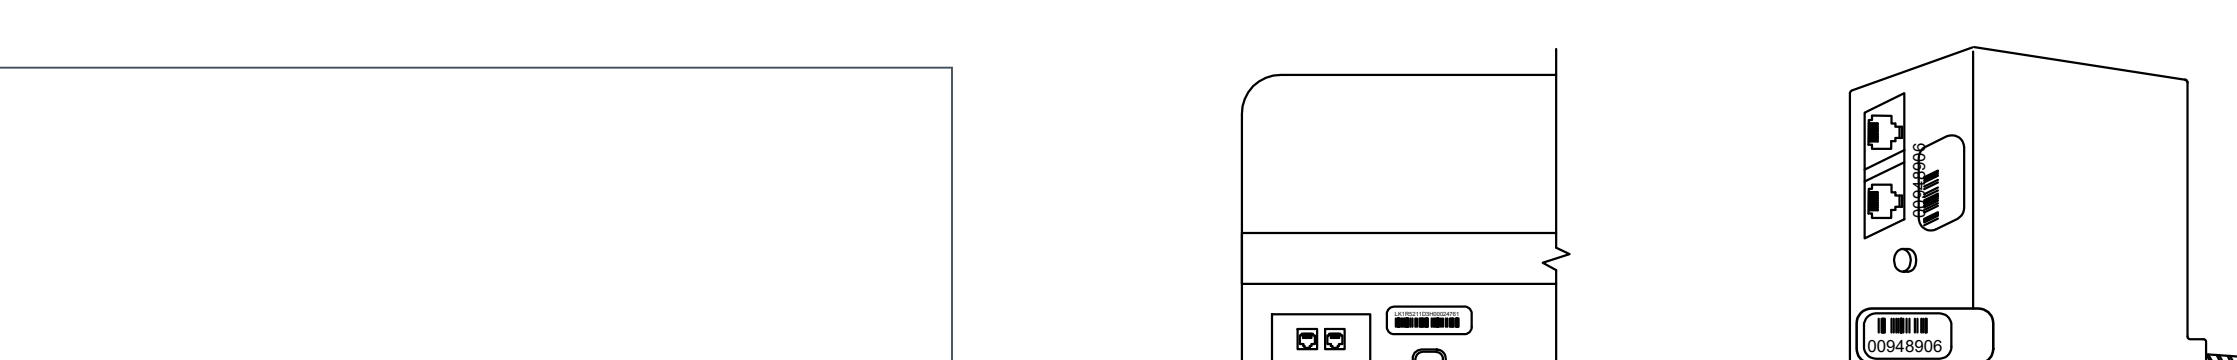




8 nLight - TYPE S20 Design 2

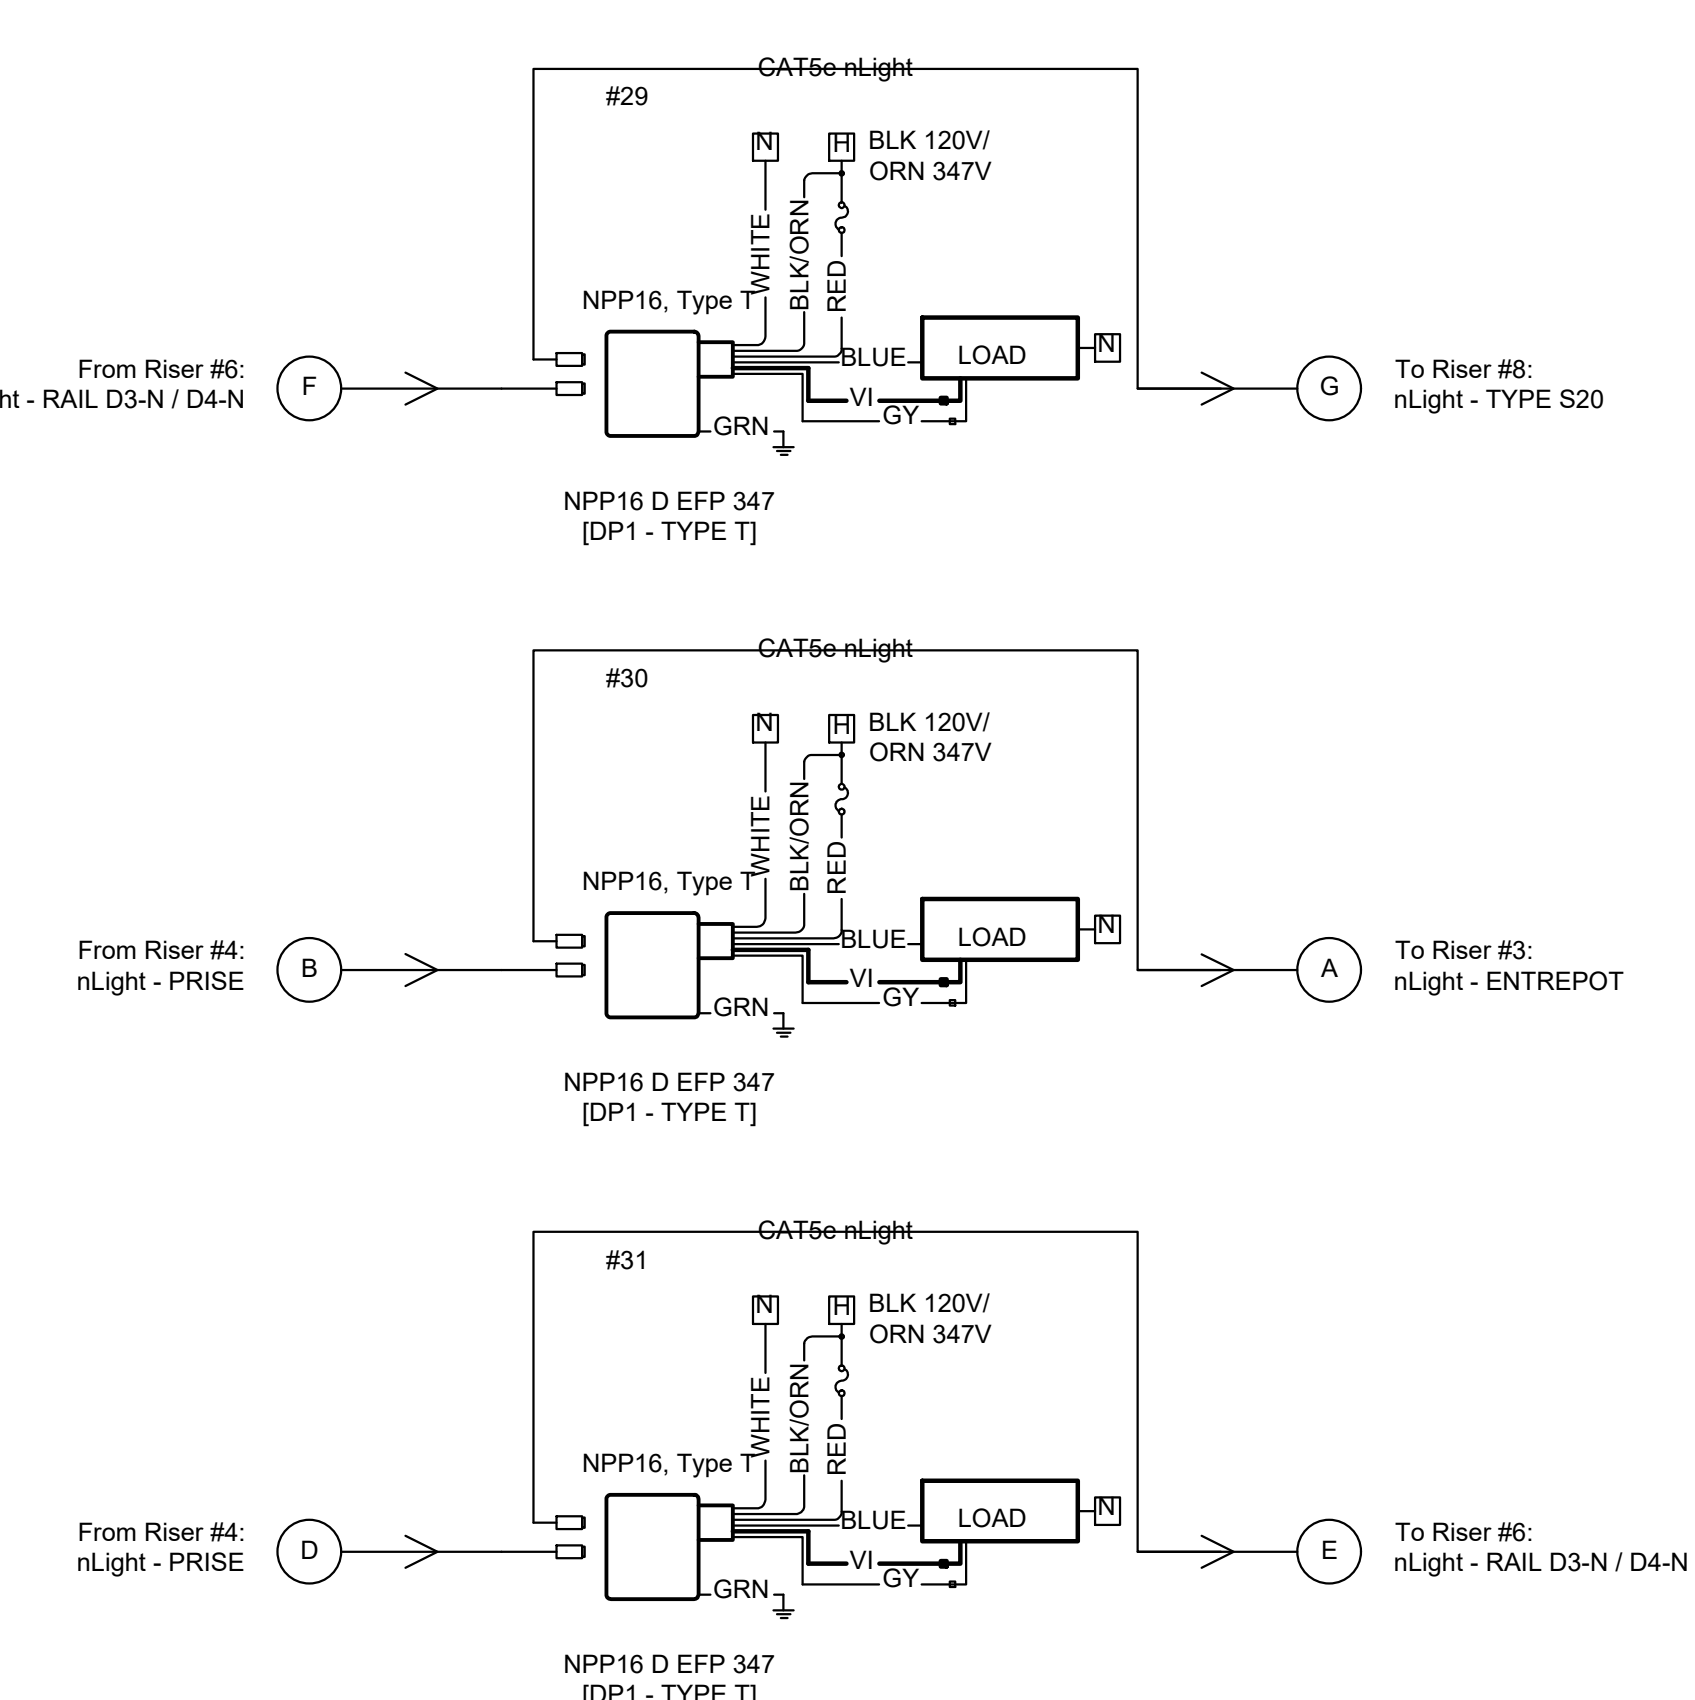

9 nLight - TYPE T Design 2

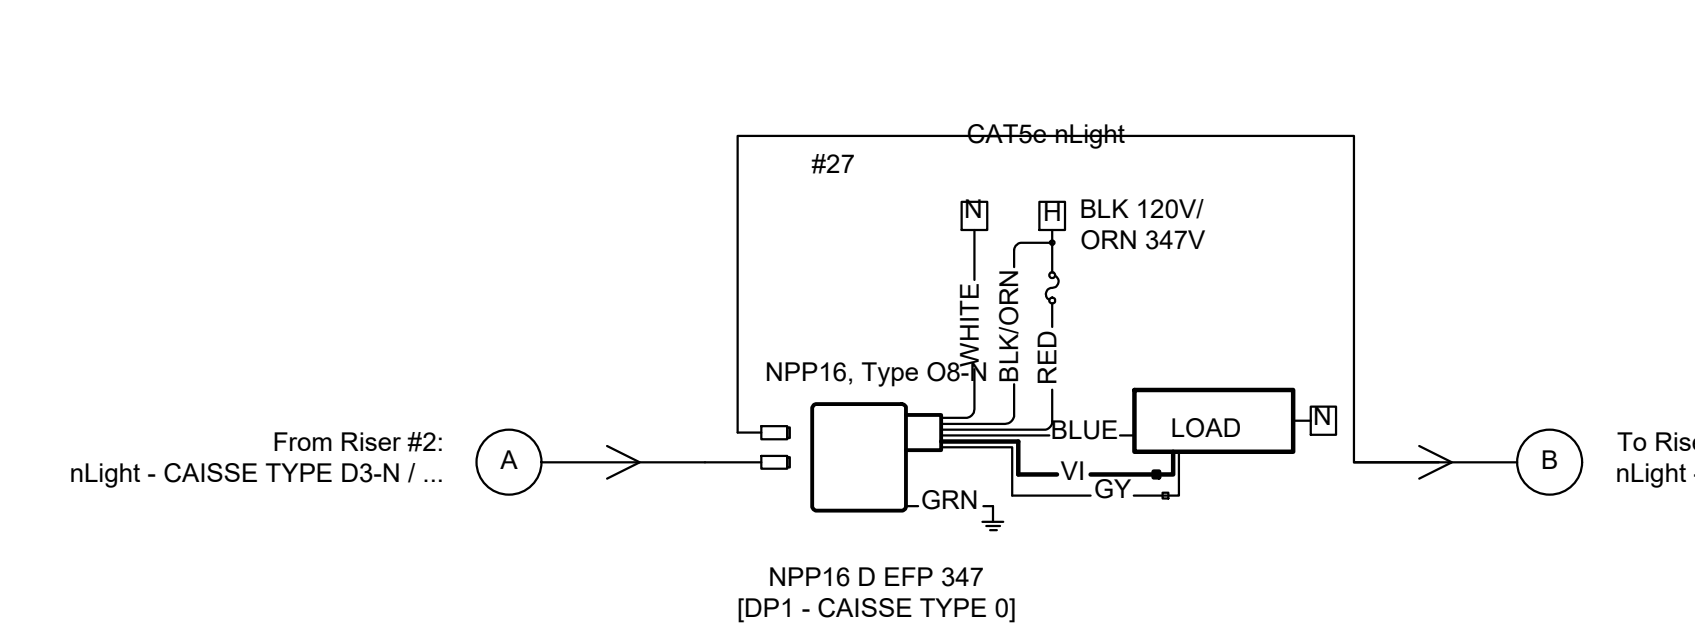

10 nLight - VESTIBULE Design 2

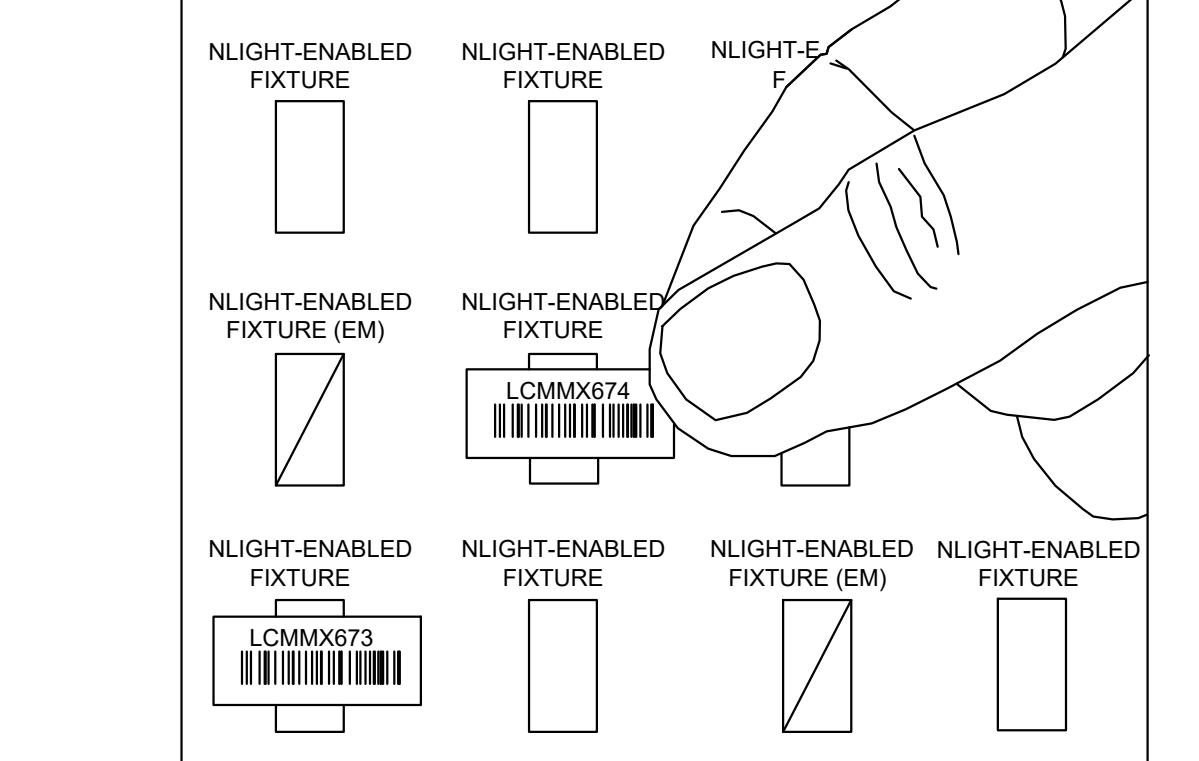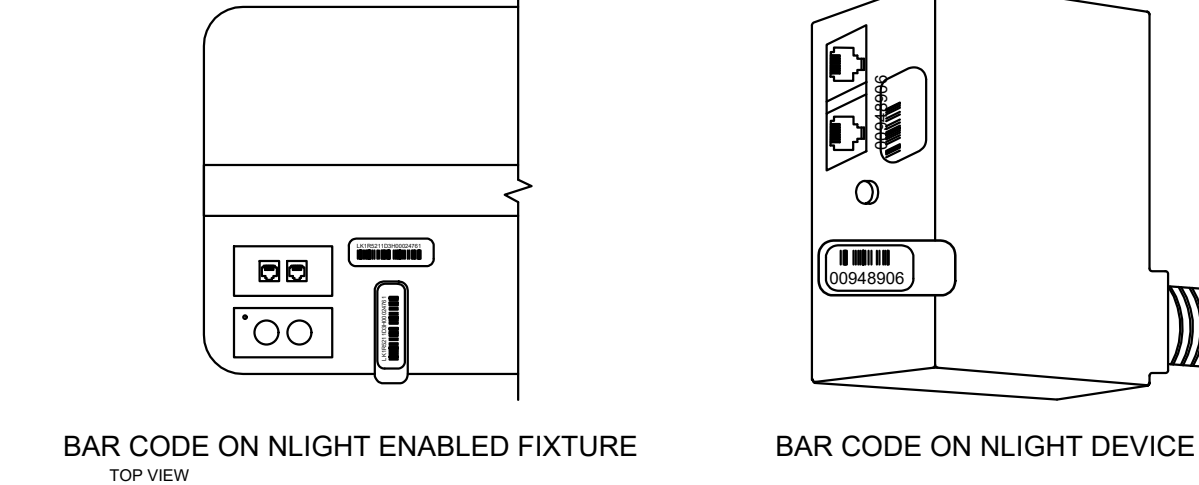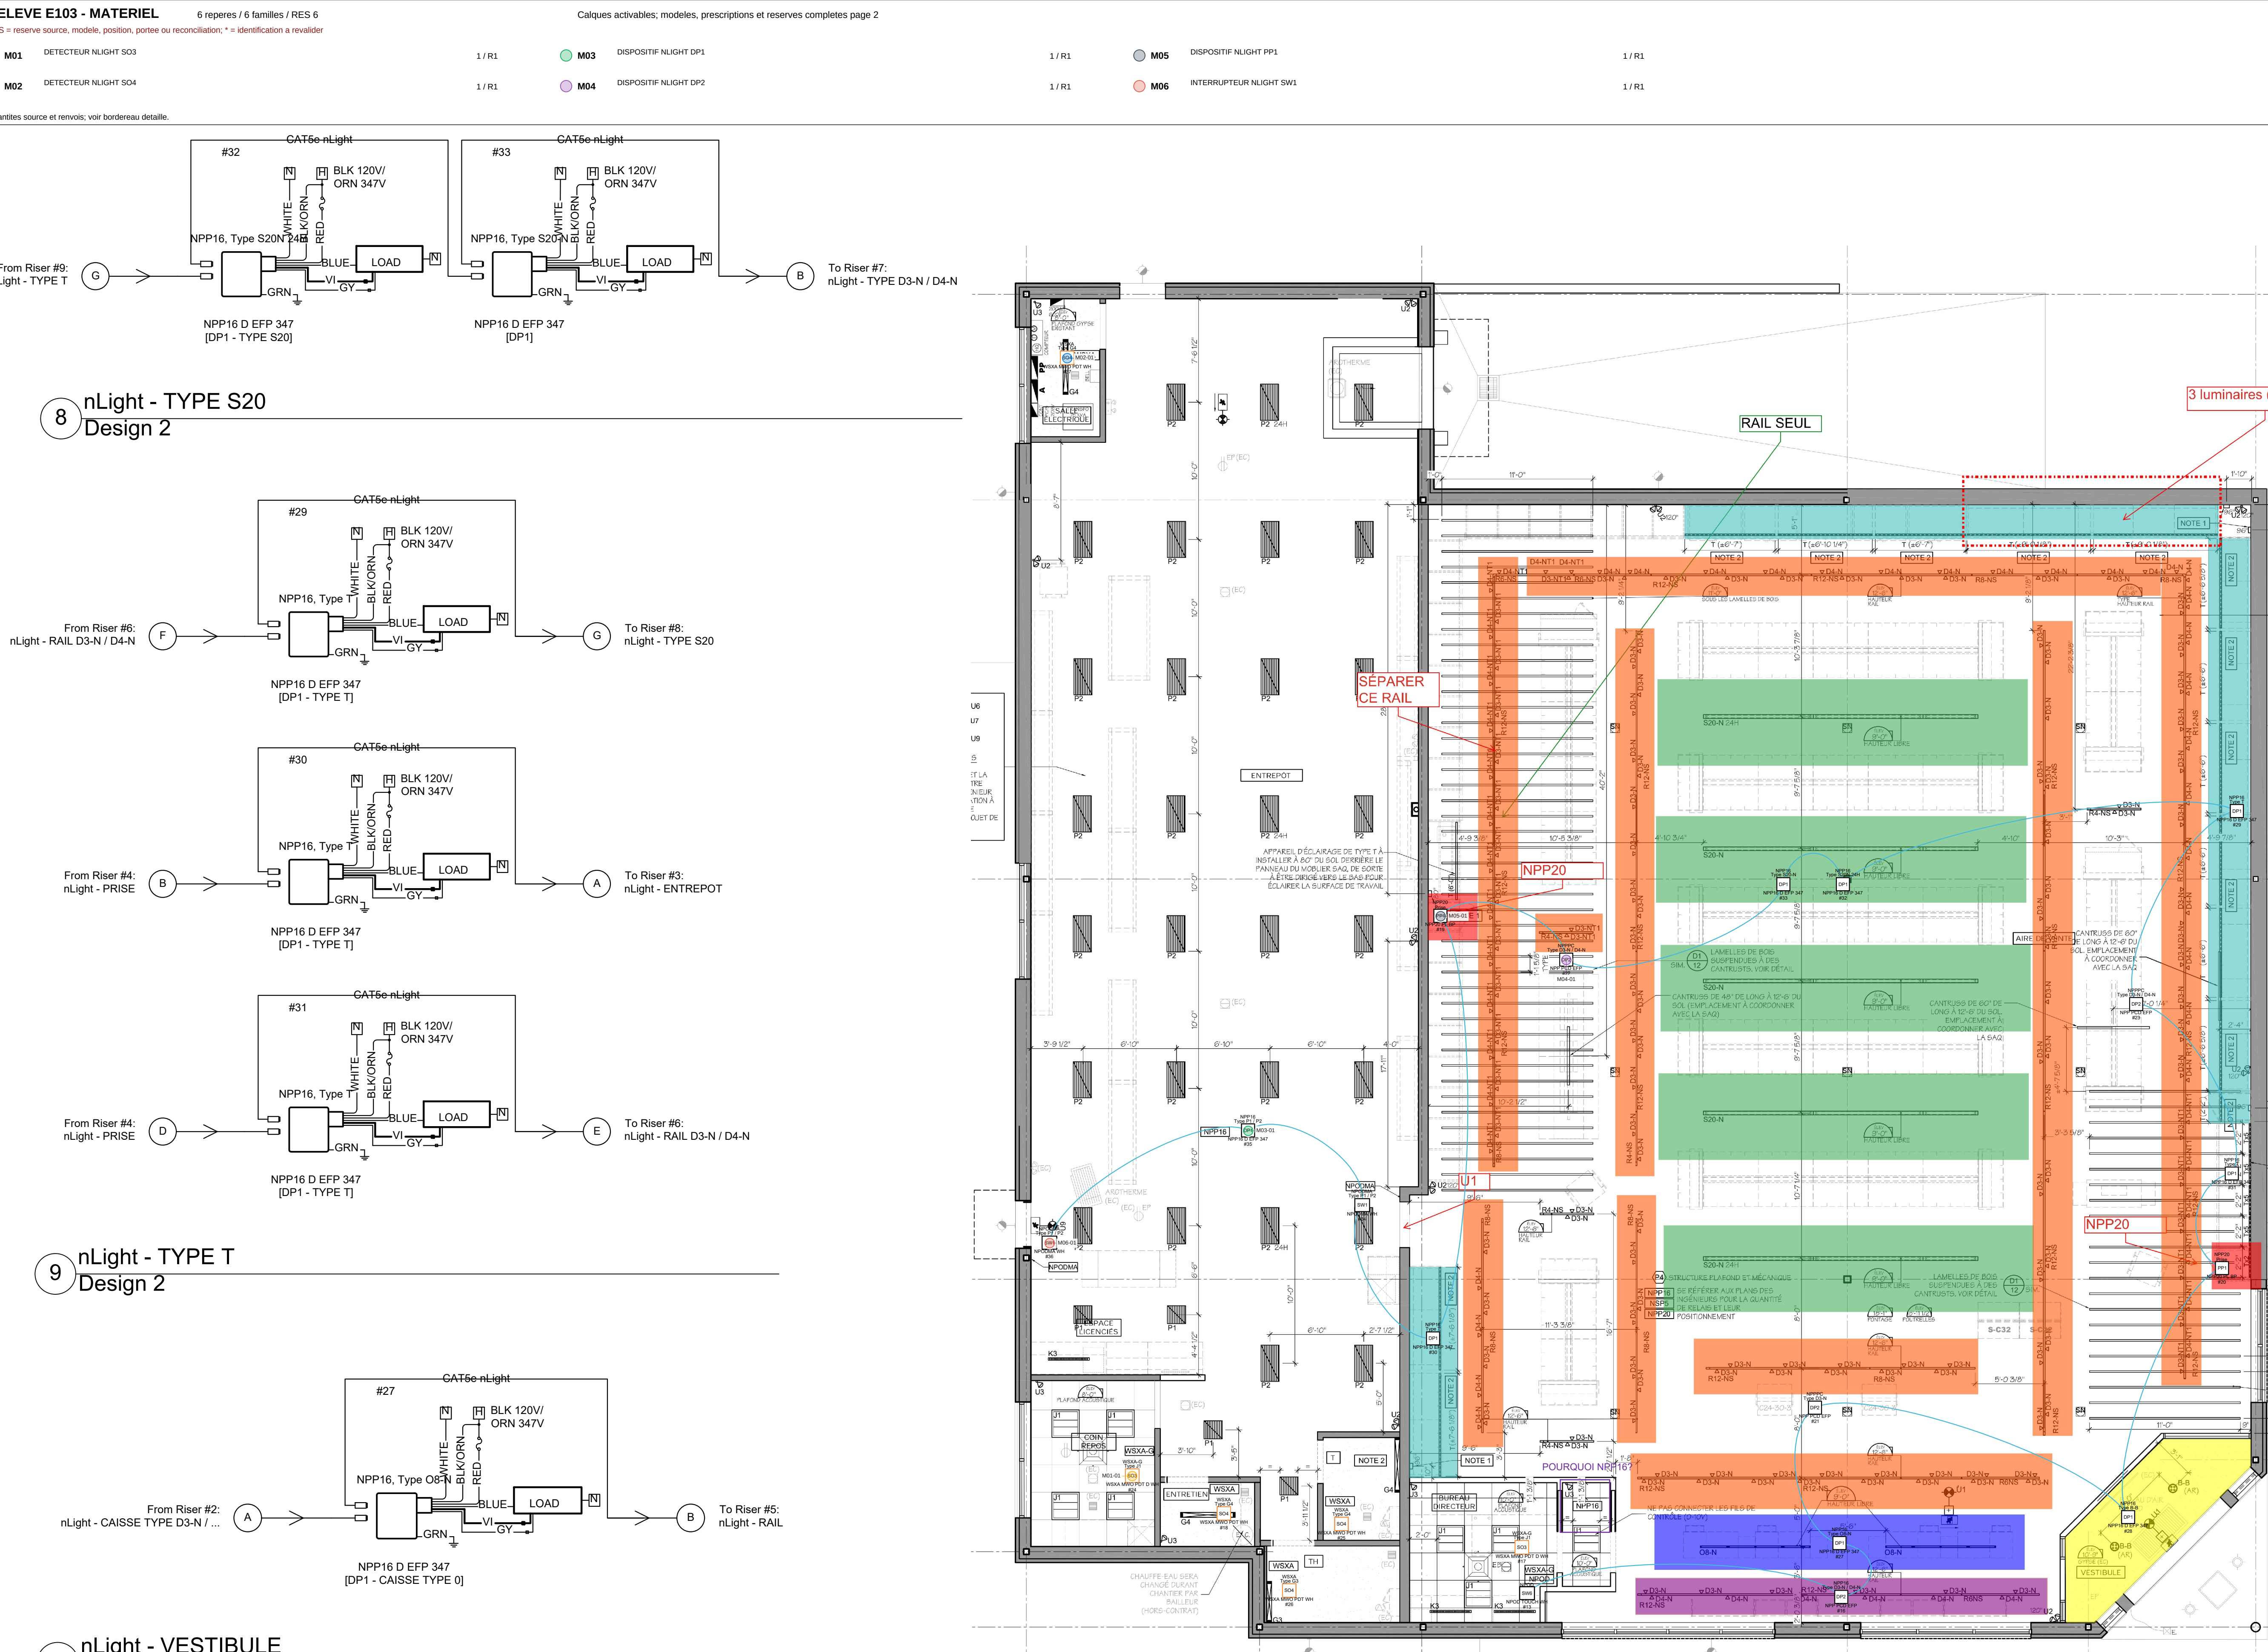

NLIGHT BARCODE INSTRUCTIONS


N.T.S.

Function	PAIR	PN OUT	Wire Color
(T1) 1	5	WHITE w BLUE	BLUE
(R1) 4	4	WHITE w BLUE	BLUE
Tx + (T2)	2	1	WHITE w ORANGE
Rx - (R3)	3	3	WHITE w GREEN
(T4) 8	7	WHITE w BROWN	BROWN
(R4) 8	8	WHITE w BROWN	BROWN

TERMINATION & TESTING OF CAT5 CABLES MUST BE DONE BY A QUALIFIED NETWORK INSTALLER

- Cable termination requirements:
- Strip off outer jacket - approximately 1-1/2" (37.6 mm)
 - Terminate approximately 1/2" (12.2 mm) from end of conductors on type 110 punch down block or connector per schedule (568B) - maximum untwist of conductors to terminations is 1/2" (12.2 mm) - trim excess leads.

SEE SYSTEM SPECIFIC NOTES ON SHEET LC0.1 FOR MAXIMUM CABLE LENGTHS.

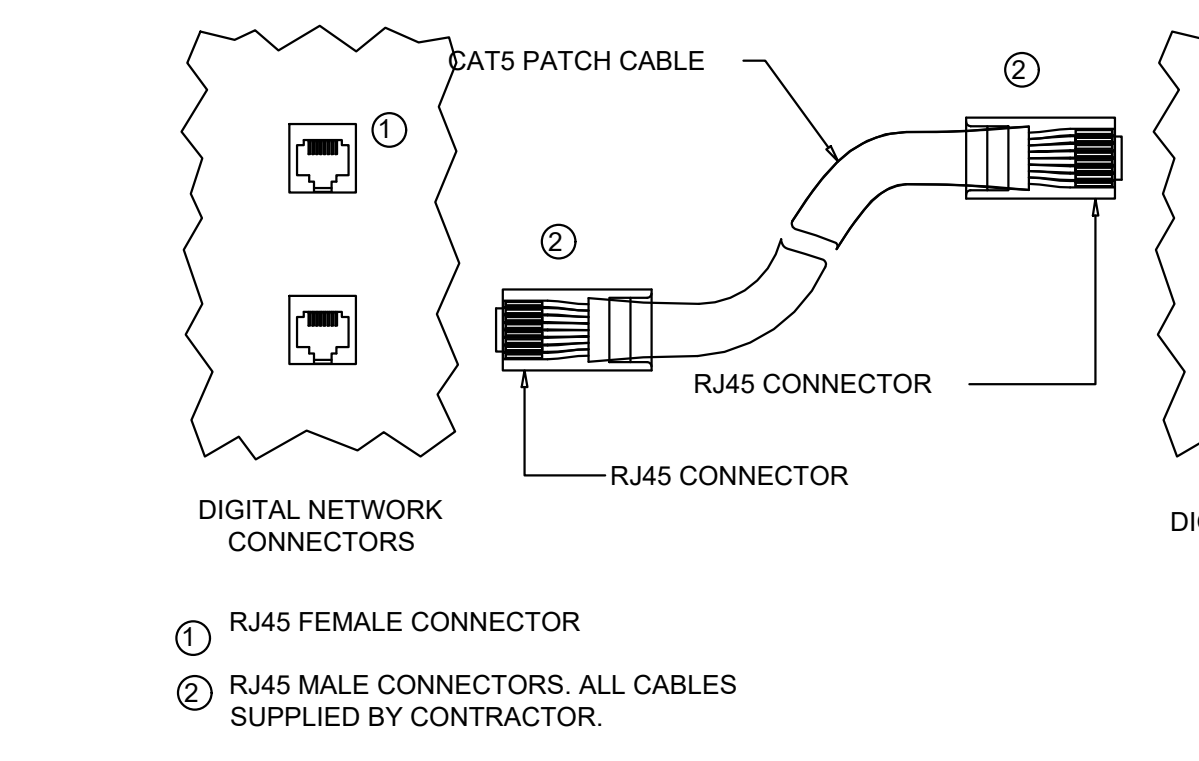

1. RJ45 FEMALE CONNECTOR
2. RJ45 MALE CONNECTORS, ALL CABLES SUPPLIED BY CONTRACTOR.

CAT5E/6 CABLE TERMINATION

N.T.S.

NOTES:
EVERY nLIGHT ENABLED DEVICE (INCLUDING nLIGHT ENABLED FIXTURES) IS FURNISHED WITH (1) PERMANENTLY ADHERED ID TAG AND (1) MATCHING PARTIALLY ADHERED ID TAG TO BE PLACED ON THE RISER DIAGRAM OR BARCODE TEMPLATE SHEET PROVIDED AS PART OF AN nLIGHT SUBMITTAL DURING INSTALLATION AND PRIOR TO FACTORY STARTUP. CONTRACTOR SHALL PLACE EACH ID TAG BELOW EACH CORRESPONDING DEVICE SHOWN ON RISER DIAGRAM TO INDICATE FACTORY STARTUP. FAILURE TO COMPLY MAY RESULT IN STARTUP DELAYS AND ADDITIONAL COSTS AT THE CONTRACTOR'S EXPENSE. DO NOT PLACE DEVICE ID STICKERS ON FLOOR PLAN UNLESS REQUIRED TO EXECUTE nLIGHT PLAN SERVICES. REFERENCE nLIGHT PLAN SERVICE NOTES ON THIS SHEET FOR SPECIFIC REQUIREMENTS.
THE SMALL BARCODE LABELS INCLUDED WITH ALL nLIGHT DEVICES AND nLIGHT ENABLED FIXTURES MUST BE PLACED ON A PRINTED PLAN SHEET BY THE INSTALLER PRIOR TO ONSITE SYSTEM STARTUP.
THE BARCODE INDICATES THE UNIQUE ID OF EACH nLIGHT DEVICE. THIS ID IS USED DURING SYSTEM STARTUP TO PROGRAM DEVICES WITH THE CORRECT GROUPINGS AND SETTINGS. WITHOUT THIS, SYSTEM STARTUP WILL REQUIRE ADDITIONAL DAYS ON THE JOB TO LOCATE DEVICE IDS.
BARCODE INSTRUCTIONS:
1. * PRINT A PLAN SHEET OF THE INSTALLATION AREA TO A MINIMUM D SIZE (24" X 36"). THE PLAN MAY BE A RISER SHEET OR BARCODE TEMPLATE (EITHER ARE PREFERRED). FLECTED CEILING PLAN, LIGHTING PLAN, AND ELECTRICAL PLAN. SO LONG AS ALL DEVICES CAN BE LOCATED BY THE FIELD SUPPORT ENGINEER.
2. PLACE THE SMALL BARCODE LABEL (0.875" LONG) FROM EACH LUMINAIRE AND DEVICE ON THE FLOORPLAN. THE LARGE BARCODE LABEL (1.25" LONG) CAN BE USED ON THE OUTSIDE OF ANY HOUSING OR JUNCTION BOX THAT OBSCURES THE ID NUMBER SHOWN ON THE DEVICE ITSELF.
3. SAVE THE PLAN AT THE JOB SITE, AND HAND OVER TO ACUTY FIELD SUPPORT ENGINEER OR OTHER PERSONNEL RESPONSIBLE FOR ONSITE SYSTEM STARTUP. IT IS ALSO ACCEPTABLE TO PROVIDE THE BARCODE PLAN AS SCANNED PDF FILES. EMAILED TO: CONTROLS.STARTUP@ACUTYBRANDS.COM, WITH PROJECT NAME AND PROJECT ADDRESS IN SUBJECT LINE AND A COPY OF THE ONSITE STARTUP REQUEST FORM.
4. DRAW ON PLAN ANY LOCATION CHANGES FOR A FIXTURE OR DEVICES, IF DIFFERENT THAN SHOWN ON PLAN.

NE PAS UTILISER POUR CONSTRUCTION

NE PAS UTILISER POUR CONSTRUCTION

NE PAS UTILISER POUR CONSTRUCTION

NE PAS UTILISER POUR CONSTRUCTION

NE PAS UTILISER POUR CONSTRUCTION

NE PAS UTILISER POUR CONSTRUCTION

NE PAS UTILISER POUR CONSTRUCTION

NE PAS UTILISER POUR CONSTRUCTION

NE PAS UTILISER POUR CONSTRUCTION

NE PAS UTILISER POUR CONSTRUCTION

NE PAS UTILISER POUR CONSTRUCTION

NE PAS UTILISER POUR CONSTRUCTION

NE PAS UTILISER POUR CONSTRUCTION

NE PAS UTILISER POUR CONSTRUCTION

NE PAS UTILISER POUR CONSTRUCTION

NE PAS UTILISER POUR CONSTRUCTION

NE PAS UTILISER POUR CONSTRUCTION

NE PAS UTILISER POUR CONSTRUCTION

NE PAS UTILISER POUR CONSTRUCTION

NE PAS UTILISER POUR CONSTRUCTION

NE PAS UTILISER POUR CONSTRUCTION

NE PAS UTILISER POUR CONSTRUCTION

NE PAS UTILISER POUR CONSTRUCTION

NE PAS UTILISER POUR CONSTRUCTION

NE PAS UTILISER POUR CONSTRUCTION

NE PAS UTILISER POUR CONSTRUCTION

NE PAS UTILISER POUR CONSTRUCTION

NE PAS UTILISER POUR CONSTRUCTION

NE PAS UTILISER POUR CONSTRUCTION

NE PAS UTILISER POUR CONSTRUCTION

NE PAS UTILISER POUR CONSTRUCTION

NE PAS UTILISER POUR CONSTRUCTION

NE PAS UTILISER POUR CONSTRUCTION

NE PAS UTILISER POUR CONSTRUCTION

NE PAS UTILISER POUR CONSTRUCTION

NE PAS UTILISER POUR CONSTRUCTION

NE PAS UTILISER POUR CONSTRUCTION

NE PAS UTILISER POUR CONSTRUCTION

NE PAS UTILISER POUR CONSTRUCTION

NE PAS UTILISER POUR CONSTRUCTION

NE PAS UTILISER POUR CONSTRUCTION

NE PAS UTILISER POUR CONSTRUCTION

NE PAS UTILISER POUR CONSTRUCTION

NE PAS UTILISER POUR CONSTRUCTION

NE PAS UTILISER POUR CONSTRUCTION

NE PAS UTILISER POUR CONSTRUCTION

NE PAS UTILISER POUR CONSTRUCTION

NE PAS UTILISER POUR CONSTRUCTION

NE PAS UTILISER POUR CONSTRUCTION

NE PAS UTILISER POUR CONSTRUCTION

NE PAS UTILISER POUR CONSTRUCTION

NE PAS UTILISER POUR CONSTRUCTION

NE PAS UTILISER POUR CONSTRUCTION

NE PAS UTILISER POUR CONSTRUCTION

NE PAS UTILISER POUR CONSTRUCTION

Aménagement et design
Réseau des succursales

700, RUE TELIER, MONTRÉAL, QUÉBEC H3W 1W6

ARTESANA

NOTES

NE PAS UTILISER POUR CONSTRUCTION

TITRE DU PROJET

SAQ

SAQ VARENNES
VARENNES, QC, J3X 1P7

TITRE DU DESSIN

DÉTAILS
CONTRÔLE D'ÉCLAIRAGE

CONTRÔLE

ÉLECTRIQUE

CONTRÔLE

ÉLECTRIQUE

BORDEREAU MATERIEL - E103

Quantités representees avec multiplicateurs; portees et composants de chaque ensemble conserves.
Les renvois et composants de panneaux ne constituent pas des ensembles supplementaires a additionner.

Repere / source	Materiel	Designation	Qty	Portee	Modele	Prescription / reserve	Parent
M01-01 E103-006	DETECTEUR NLIGHT SO3	SO3	1	A PRECISER	WSXA MWO PDT D WH	Detecteur/capteur nLight SO3 (carre etiquette sur le plan)	
M02-01 E103-001	DETECTEUR NLIGHT SO4	SO4	1	A PRECISER	WSXA MWO PDT WH	Detecteur/capteur nLight SO4 (carre etiquette sur le plan)	
M03-01 E103-004	DISPOSITIF NLIGHT DP1	DP1	1	A PRECISER	NPP16 D EFP 347	Dispositif de controle nLight DP1 (carre etiquette sur le plan)	
M04-01 E103-003	DISPOSITIF NLIGHT DP2	DP2	1	A PRECISER	NPP PCD EFP	Dispositif de controle nLight DP2 (carre etiquette sur le plan)	
M05-01 E103-002	DISPOSITIF NLIGHT PP1	PP1	1	A PRECISER	NPP20 PL BP	Dispositif de controle nLight PP1 (carre etiquette sur le plan)	
M06-01 E103-005	INTERRUPTEUR NLIGHT SW1	SW1	1	A PRECISER	NPODMA WH	Interrupteur nLight SW1 (carre etiquette sur le plan)	

RESERVES ET COMPLEMENTS
"prepaire.py". Le reste de la feuille E103 (dizaines d'autres symboles, risers, câblage CAT5e, notes) n'a
R-001 E103 - Portée (INSTALLER/CONSERVER/EXISTANT) non confirmée visuellement pour les 6 repères - la
R-002 E103 - SW6 (7e famille visible dans les risers, ex. "SW6 - ENTREPOT") vu dans l'aperçu général mais
R-003 E103 - Identification des modèles (NPP16 D EFP 347, NPP PCD EFP, NPP20 PL BP, WSXA MWO PDT D WH,
Echantillon volontairement restreint à 6 repères (DP1, DP2, PP1, SO3, SO4, SW1), chassis parce que leur
étiquette et leur symbole carré étaient directement vérifiables sur les lules générées par ce run de
PAS été relevé ici - hors périmètre de cette preuve de mécanisme.
feuille est un détail de contrôle d'éclairage "POUR SOUMISSION" qui suggère du neuf, mais aucune mention
explicite "existant" ou "nouveau" n'a été vérifiée au zoom pour chaque symbole. Portée posée à
"A PRECISER" sur les 6 lignes, sans deviner.
NON relevé ici (hors échantillon) - ne pas déduire son absence du dossier.
WSXA MWO PDT WH, NPODMA WH) lue directement sur le texte vectoriel adjacent à chaque symbole (détail de
riser), pas dans une cellule de panneau séparée - à recouper avec la cellule si elle existe ailleurs dans le
jeu de plans complet (non fourni pour cette preuve, une seule page).