

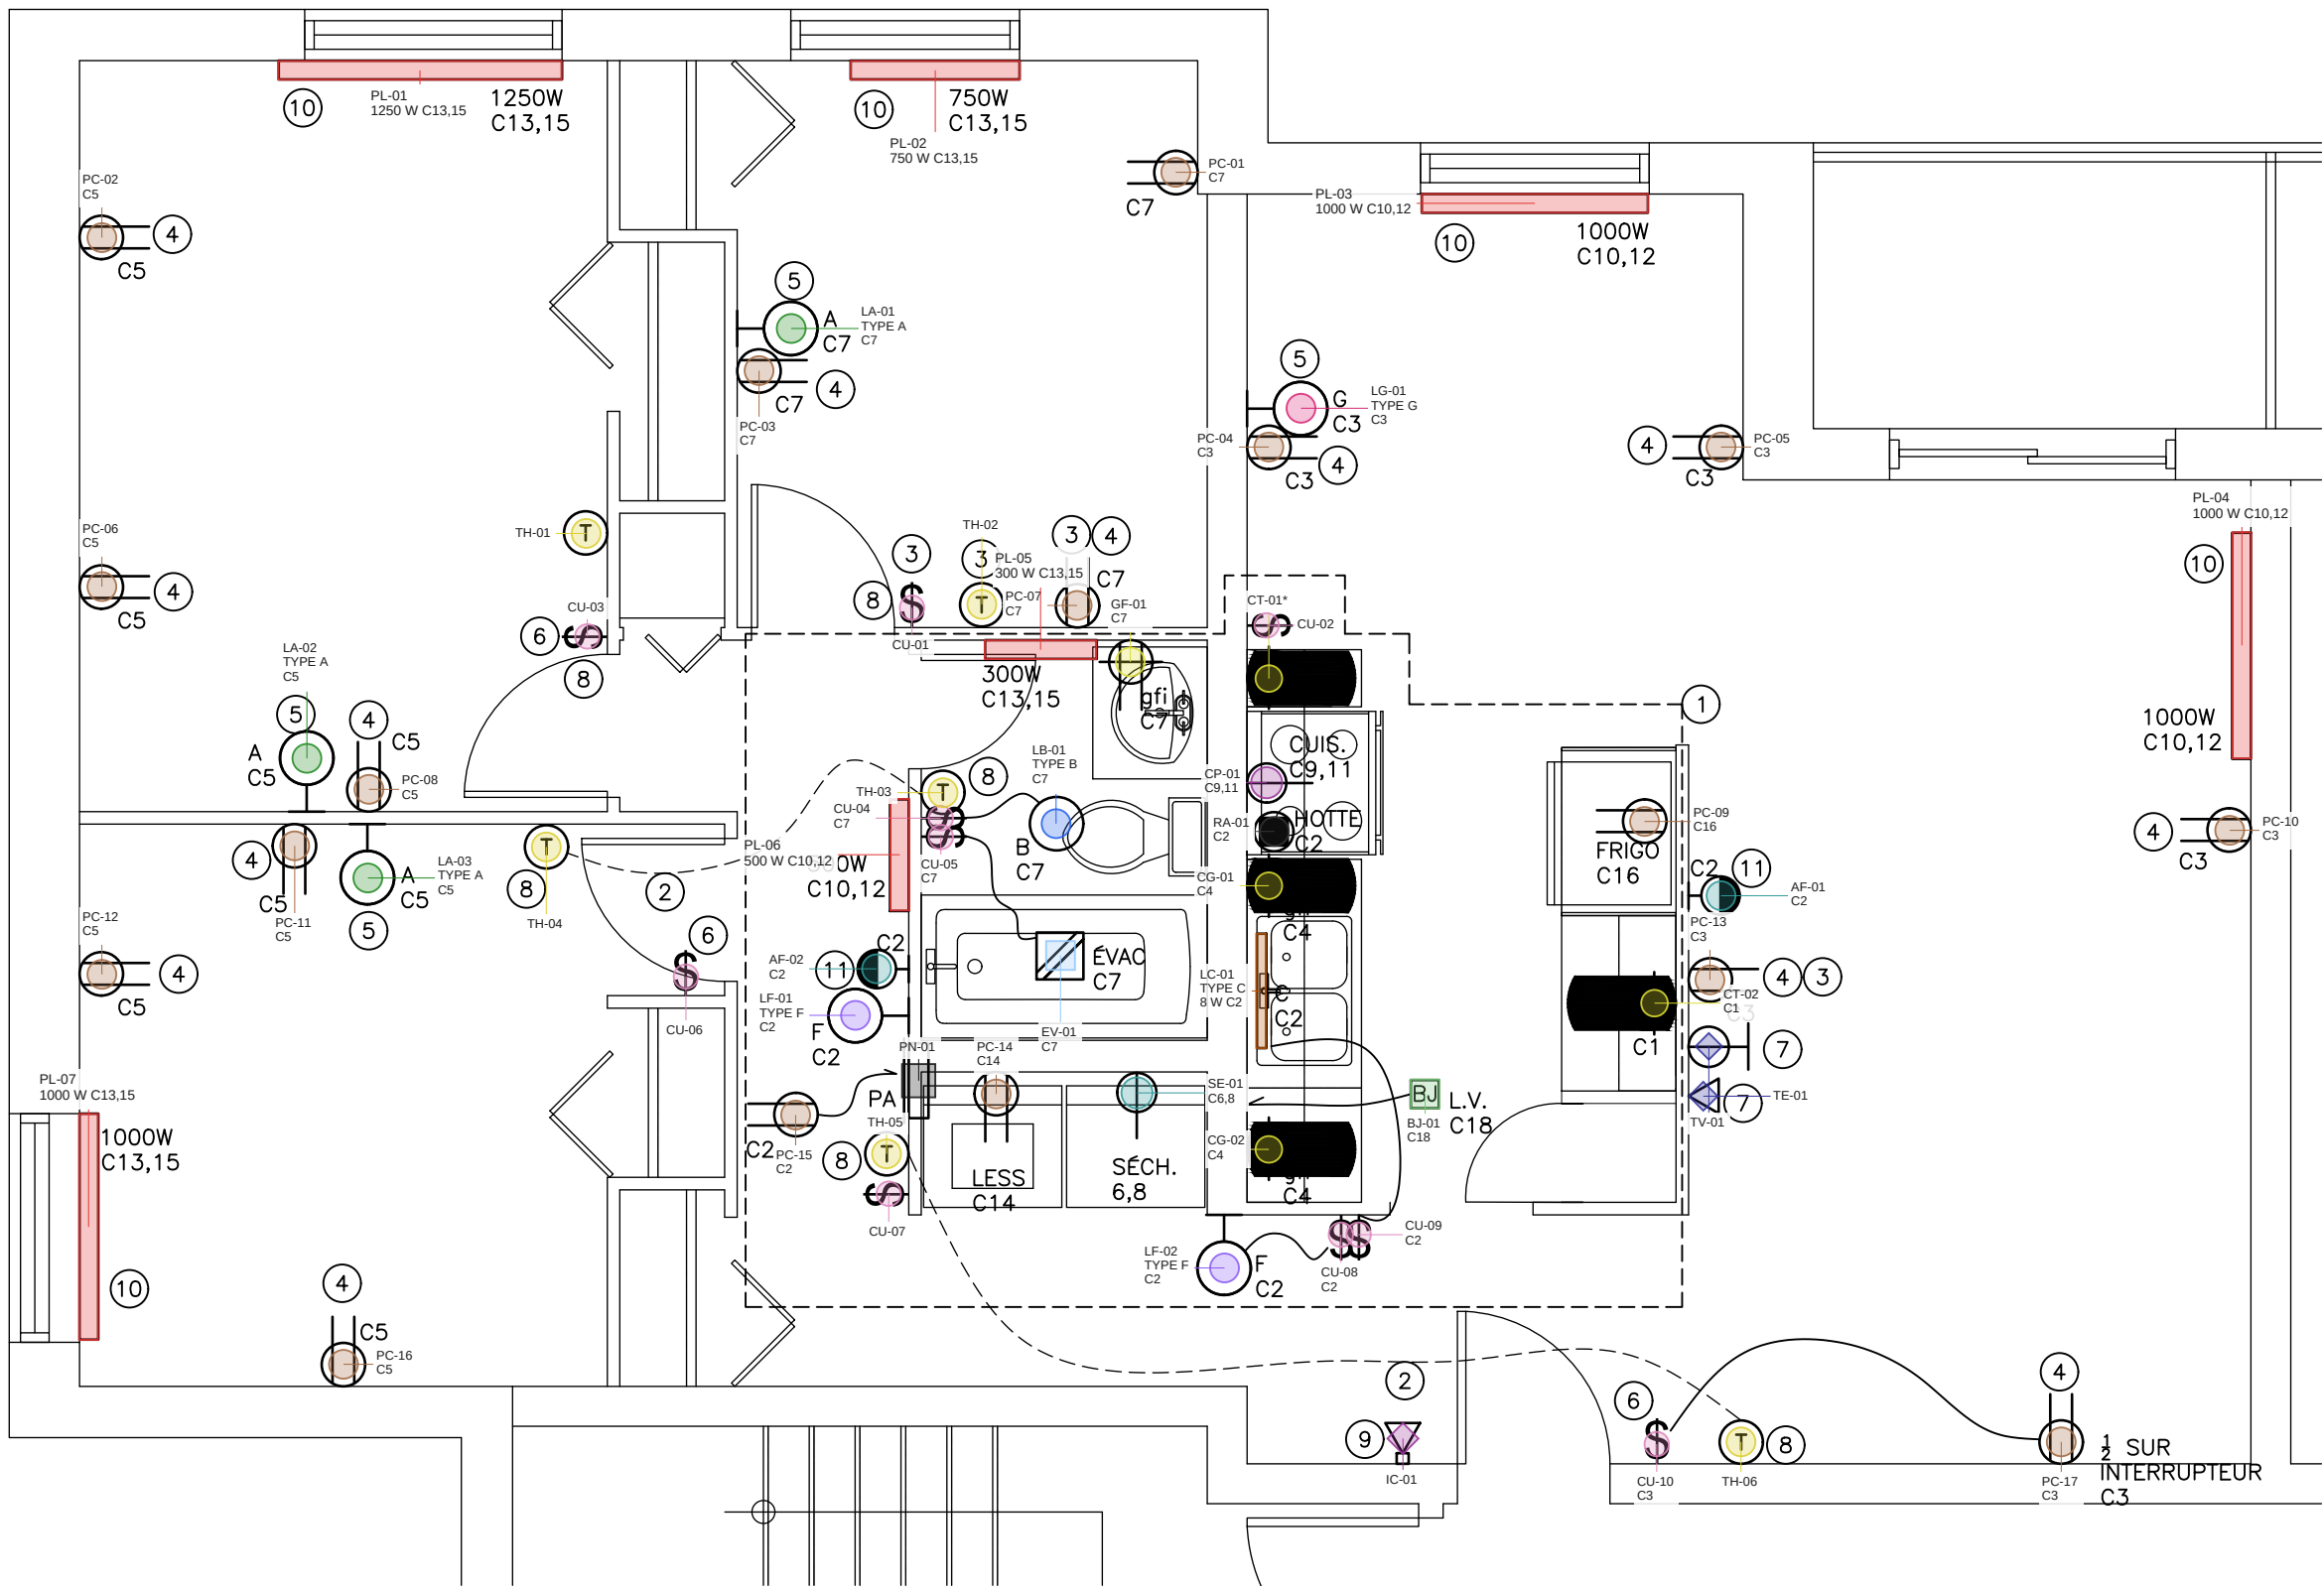


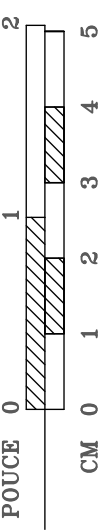

LOGEMENT TYPE A (RDC ET 2E ÉTAGE)

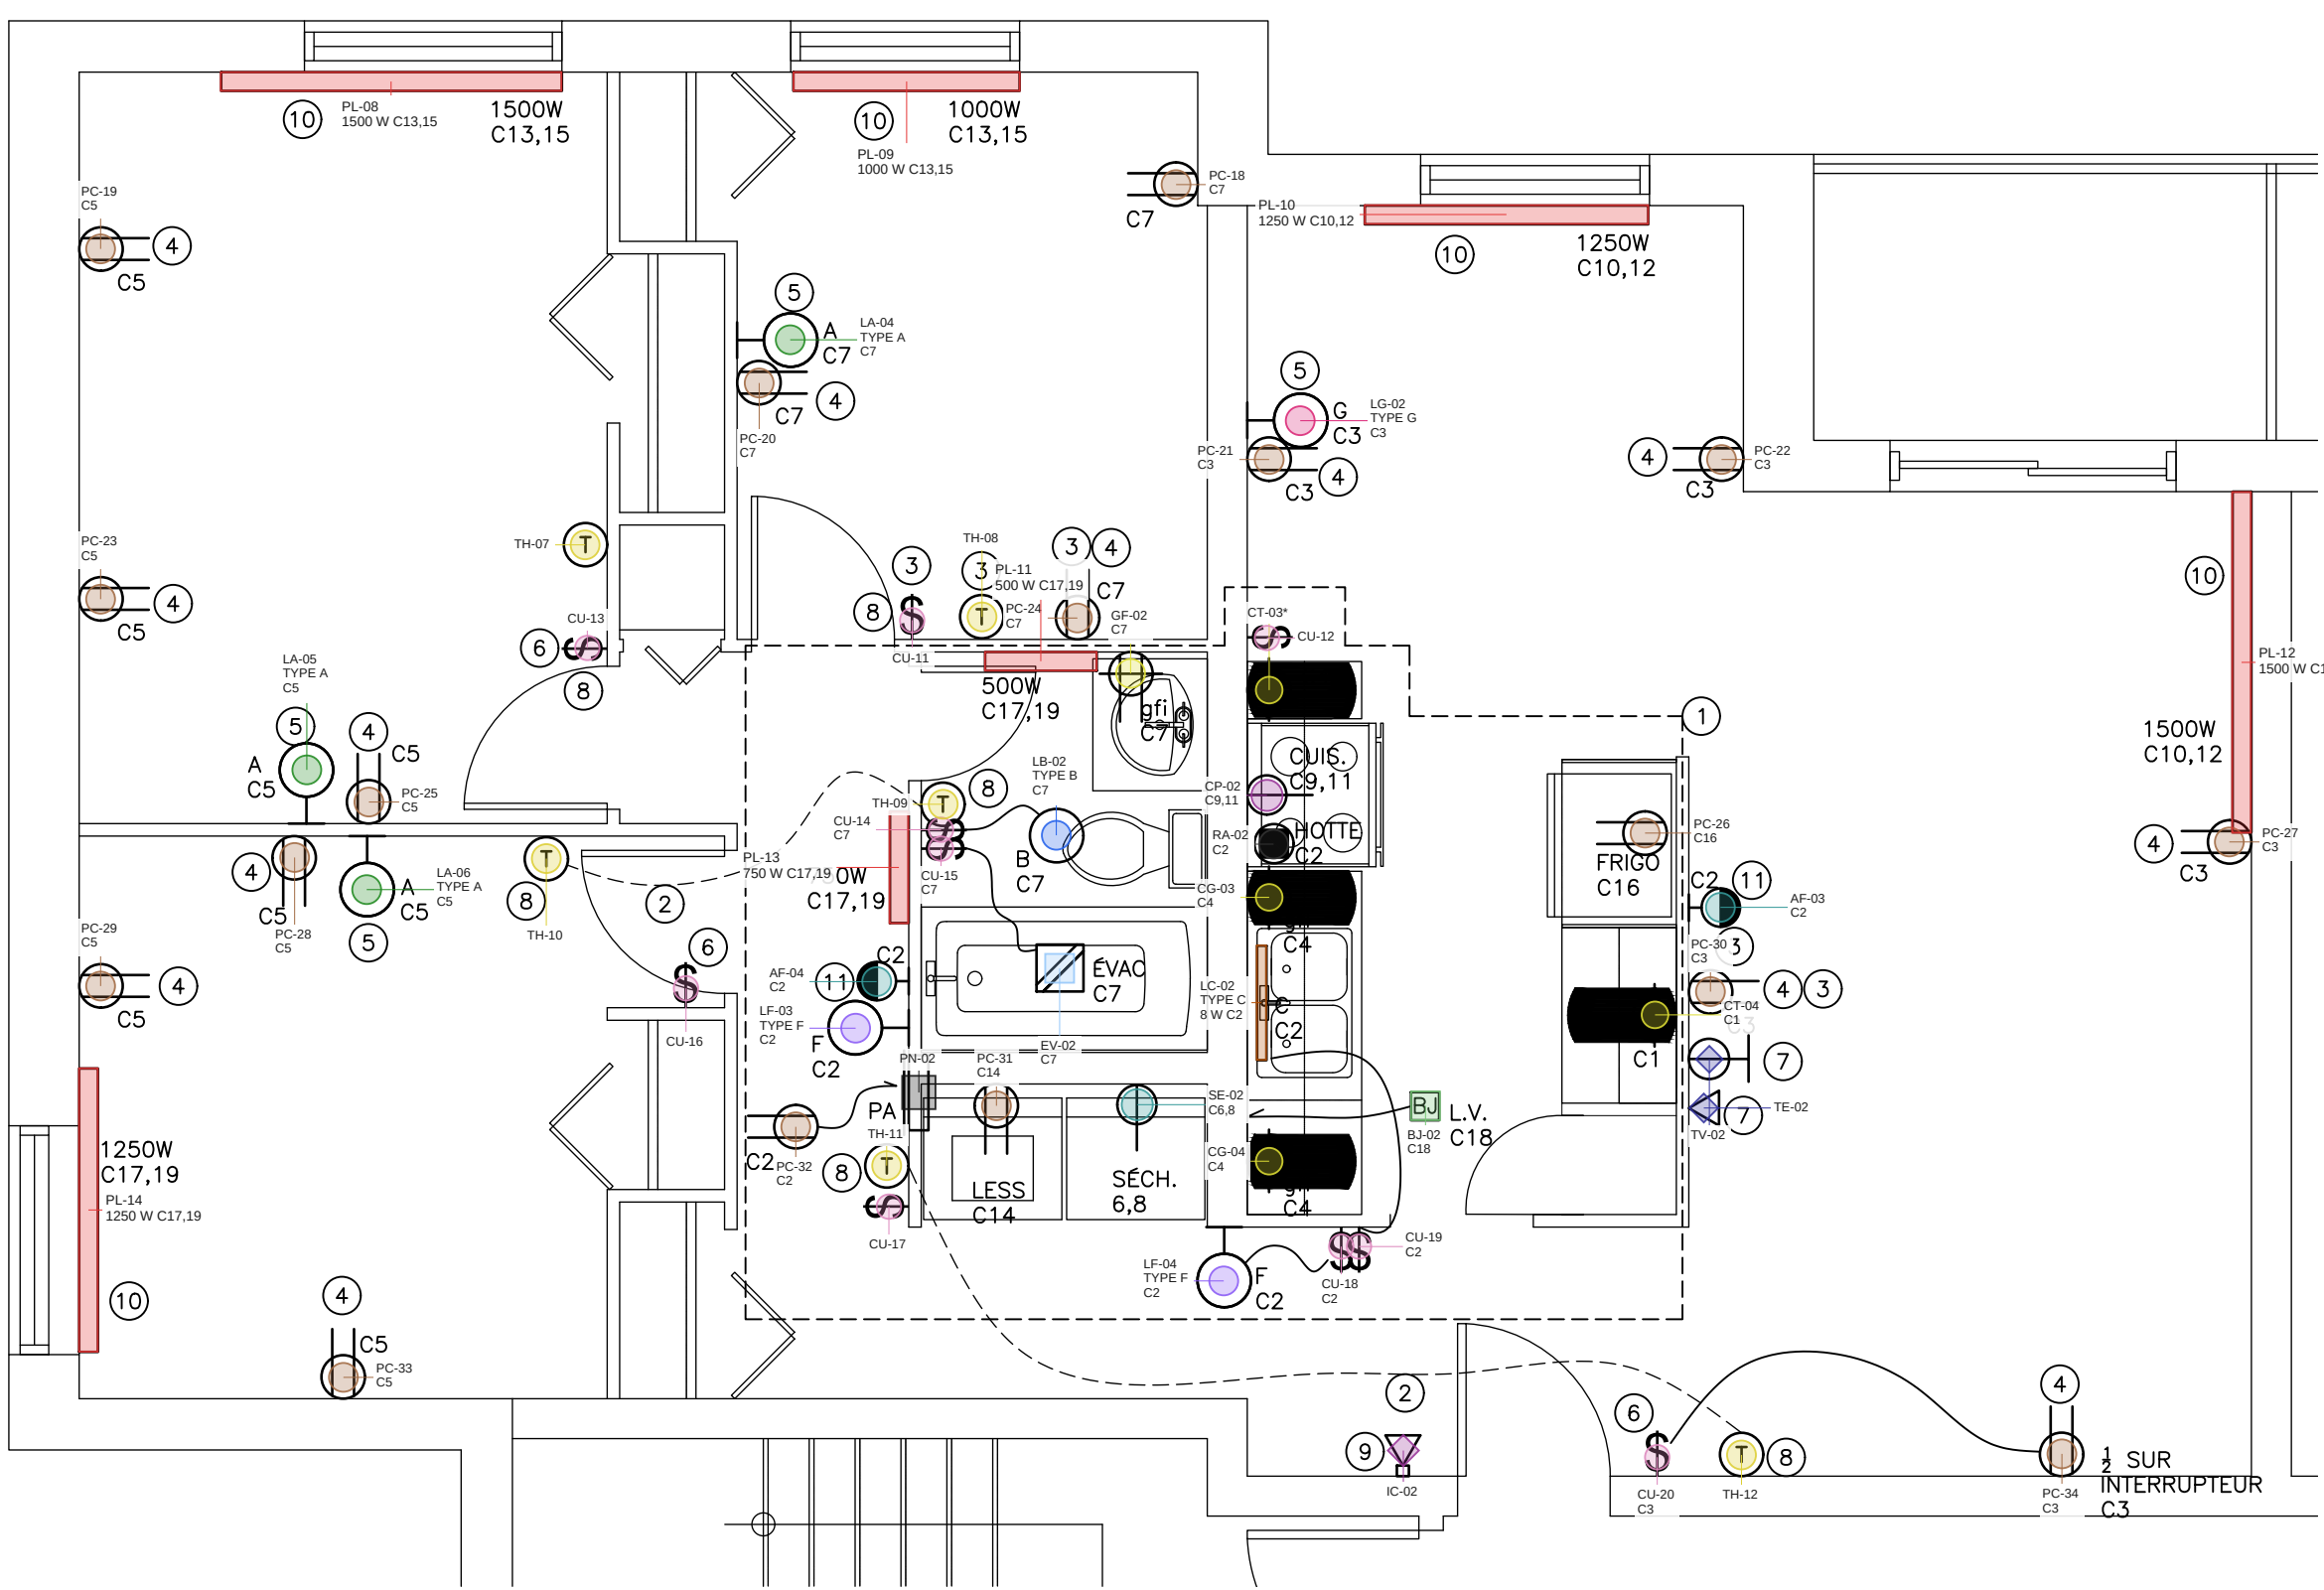

LOGEMENT TYPE B (3E ÉTAGE)

RELEVÉ E08 - MATERIEL

128 repères / 22 familles / calques activables
0 non identifiés - 2 identifications à revalider (*)
5 divergences plan/cadule A RESOUDRE

- AF AVERTISSEUR DE FUMÉE MURAL 120V 4
- BJ BOITE DE JONCTION POUR RACCORD (FUTURE) D'UN LAVE-VAISSELLE 2
- CG PRISE DE COURANT AU DESSUS D'UN COMPTOIR - D'OFF 4
- CP PRISE DE COURANT POUR CUISINIÈRE 50A-120/240V 2
- CT PRISE DE COURANT AU DESSUS D'UN COMPTOIR 4
- CU COMMUTATEUR UNIPOLAIRE 15A-125V 20
- EV EVACUATEUR DE TOILETTE. VOIR VENTILATION. 2
- GF PRISE DE COURANT AVEC DISJONCTEUR DIFFÉRENTIEL DE FUITE À LA TERRE 2
- IC INTERCOMME (CONTRÔLE DE PORTE) 2
- LA LUMINAIRE AU MUR TYPE A 6
- LB LUMINAIRE AU PLAFOND TYPE B 2
- LC LUMINAIRE LINEAIRE TYPE C 2
- LF LUMINAIRE AU MUR TYPE F 4
- LG LUMINAIRE AU MUR TYPE G 2
- PC PRISE DE COURANT DOUBLE 15A-125V 34
- PL PLINTHE DE CHAUFFAGE [R-001] 14
- PN PANNEAU DE LOGEMENT [R-001] 2
- RA RACCORD DIRECT D'UN APPAREIL SPÉCIAL 2
- SE PRISE DE COURANT SIMPLE 30A-120/240V 2
- TE SORTIE TÉLÉPHONIQUE 2
- TH THERMOSTAT [R-001] 12
- TV SORTIE POUR CABLE-DISTRIBUTION (TV) 2

PL : rectangles aux dimensions graphiques du plan.
W et circuits affichés uniquement si vérifiés.
* : identification hénée à revalider ; NI : matériel non identifié.
Les quantités concernent cette feuille de logements types.
R-001 : désignation conservée au registre des réserves.
Modèles, prescriptions et sources : bordereau page 2.

PORTÉE DES TRAVAUX – 155 MERCIER

LES TRAVAUX ÉLECTRIQUES COMPRENNENT ENTRE AUTRES, MAIS SANS S'Y LIMITER :

- LE REMPLACEMENT DE TOUS LES COMPOSANTS ET ÉQUIPEMENTS DE LA DISTRIBUTION PRINCIPALE (INCLUANT LES MÂTS DE LIVRAISON) TELS QU'INDIQUÉS SUR LES UNIFILAIRES.
- LES MESURES DE MAINTIEN DE SERVICES ÉLECTRIQUE DURANT LES TRAVAUX REMPLACEMENT DE LA DISTRIBUTION PRINCIPALE, TEL QU'INDIQUÉ SUR L'UNIFILAIRE ET DÉCRITS AU DEVIS.
- LE REMPLACEMENT DE TOUS LES PANNEAUX DE DISTRIBUTION DES LOGEMENTS.
- LE REMPLACEMENT DES PANNEAUX DE DISTRIBUTION DE SERVICE.
- LE REMPLACEMENT DE TOUS LES APPAREILS DE CHAUFFAGE, INCLUANT LES THERMOSTATS DE PIÈCE AFFÉRENTS, DE TOUS LES LOGEMENTS, DES CORRIDORS DES ESCALIERS, DES DÉPÔTS ET DES ESPACES COMMUNS.
- LE REMPLACEMENT DE TOUTES LES PRISES DE SERVICE INDIQUÉES : NEMA 5-15P, NEMA 5-20P, NEMA 14-30P (SÈCHEUSE) ET NEMA 14-50P (CUISINIÈRE).
- LE REMPLACEMENT DE TOUS LES INTERRUPTEURS DE COURANT POUR LE CONTRÔLE D'ÉCLAIRAGE TELS D'INDIQUÉS.
- POUR CHAQUE LOGEMENT, LA FOURNITURE ET L'INSTALLATION D'UNE NOUVELLE PRISE DE SERVICE DÉDIÉE POUR UNE UNITÉ DE CLIMATISATION-DE-FENÊTRE-À-CONFIRMER.
- LE REMPLACEMENT DE LA DISTRIBUTION ÉLECTRIQUE AU NIVEAU DE LA CUISINE ET DE LA SALLE DE BAIN DE CHACUN DES LOGEMENTS, VOIR LIMITES DES TRAVAUX SUR LES VUES DES LOGEMENTS TYPES.
- LE REMPLACEMENT DE TOUTES LES PRISES DE SERVICE EXTERIEURES INDIQUÉES ET ATTACHÉES AU BÂTIMENT.

NOTES GÉNÉRALES

- LA POSITION DES SERVICES EXISTANTS SUR LES PLANS EST APPROXIMATIVE ET DOIT ÊTRE VÉRIFIÉE ET CONFIRMÉE SUR LE SITE.
- LA POSITION DES NOUVEAUX SERVICES INDIQUÉE SUR LES PLANS EST APPROXIMATIVE ET DOIT ÊTRE CONFIRMÉE AVEC LES PLANS D'AMÉNAGEMENT EN ARCHITECTURE.
- ASSURER LA CONTINUITÉ DES ALIMENTATIONS ÉLECTRIQUES DES SERVICES NON TOUCHÉS PAR LES TRAVAUX DE REMPLACEMENT DE CIRCUITS DANS LES LOGEMENTS. À CET EFFET, PRÉVOIR, POUR FIN DE SOUMISSION, ET CE, POUR CHAQUE LOGEMENT, DEUX CONTINUITÉS DE SERVICE INCLUANT UNE LONGUEUR TOTALE DE CÂBLES DE 10 MÈTRES (30 PIEDS) ET DEUX BOITIERS ÉLECTRIQUES MURAUX ENCASTRES (2X4) AVEC COUVERCLE AVEUGLE.
- LA TOTALITÉ DES CIRCUITS D'ALIMENTATION EXISTANTS À CONSERVER SONT FAITS AVEC DU CÂBLE AVEC CONDUCTEUR D'ALUMINIUM. PRÉVOIR DES DISPOSITIFS (PRISE DE SERVICE, INTERRUPTEUR, ETC.) ET DES MÉTHODES DE RACCORDEMENT ET D'INSTALLATION, APPROPRIÉES ET COMPATIBLES AVEC DES CONDUCTEURS D'ALUMINIUM.
- L'ENTREPRENEUR EST RESPONSABLE DE NE PAS CASSER LES EXTRÉMITÉS DES CONDUCTEURS D'ALUMINIUM EXISTANT. L'ENTREPRENEUR S'ENGAGE À REMPLACER, À SES FRAIS (INCLUANT LES TRAVAUX GÉNÉRAUX) TOUTS LES CÂBLES AVEC CONDUCTEURS D'ALUMINIUM RENDUS TROP COURTS PAR SA MANIPULATION.
- LA POSITION DES SERVICES EST DONNÉE À TITRE INDICATIF SEULEMENT. LA POSITION EXACTE DE CES SERVICES DOIT ÊTRE DÉTERMINÉE SUR LE CHANTIER.
- L'IDENTIFICATION DES CIRCUITS D'ALIMENTATION EST DONNÉE À TITRE INDICATIF SEULEMENT. ELLE DOIT ÊTRE VÉRIFIÉE ET VALIDÉE AU CHANTIER.
- L'ENTREPRENEUR DOIT RESPECTER L'IDENTIFICATION ET LA POSITION DES CIRCUITS D'ALIMENTATION INDIQUÉE SUR CE PLAN, LORS DES BRANCHEMENTS DE CIRCUITS DANS LES NOUVEAUX PANNEAUX DE DISTRIBUTION.

NOTES EN PLAN

- PRÉVOIR LE REMPLACEMENT DES CÂBLES D'ALIMENTATION, DES BOITIERS ET SERVICES (APPAREILS D'ÉCLAIRAGE, INTERRUPTEUR, PRISE DE SERVICE, PLINTHE DE CHAUFFAGE) POUR TOUS LES SERVICES INDIQUÉS À L'INTÉRIEUR DE CETTE LIMITE.
- CÂBLE D'ALIMENTATION EXISTANT À CONSERVER ET À RÉALIMENTER À PARTIR DU NOUVEAU CÂBLE D'ALIMENTATION DANS LE NOUVEAU SERVICE INDIQUÉ.
- PRÉVOIR REMPLACER LE CÂBLE D'ALIMENTATION POUR CES SERVICES EXISTANTS.
- PRISE DE SERVICE EXISTANTE À REMPLACER.
- APPAREILS D'ÉCLAIRAGE EXISTANT À REMPLACER.
- INTERRUPTEUR EXISTANT À REMPLACER.
- PLAQUE DE SERVICE EXISTANTE À REMPLACER (TÉLÉPHONIE OU CABLE DISTRIBUTION).
- THERMOSTAT DE PIÈCE ÉLECTRONIQUE EXISTANT À CONSERVER.
- INTERCOM (CONTRÔLE DE PORTE) EXISTANT À CONSERVER.
- PLINTHE DE CHAUFFAGE ÉLECTRIQUE EXISTANTE À REMPLACER.
- NOUVEL AVERTISSEUR D'INCENDIE AUTONOME (VOIR DÉTECTION ET SIGNALISATION INCENDIE).

PERCEMENT DE DALLE STRUCTURALE

JUSTIFICATION : LES DALLES DE PLAFOND ET PLANCHER SONT DES DALLES DE CIMENT VIDÉES AVEC DES CÂBLES EN PRÉ-TENSION. IL EST PRIMORDIAL DE NE PAS TOUCHER LES CÂBLES EN PRÉ-TENSION LORS DES PERCEMENTS. CECI N'EST PAS APPLICABLE À LA DALLE SUR SOL AU SOUS-SOL.

PROCÉDURE : PRÉVOIR UN "SCAN" LOCAL DE LA DALLE VISÉE PAR LES TRAVAUX. IDENTIFIER À L'AIDE D'UN MARQUEUR LA POSITION DES CÂBLES EN PRÉ-TENSION ET DES SECTIONS VIDÉES DE DALLE. EFFECTUER TOUT PERCEMENT À UNE DISTANCE MINIMUM DE 50MM DE TOUS CÂBLES EN PRÉ-TENSION.

NE PAS UTILISER POUR CONSTRUCTION

CONSULTANT:



168 De la Clairière
St-Adolphe-d'Howard
Québec, J0T2B0
Canada
Tel: 514-300-0626

SCEAU:

CLIENT:

OFFICE D'HABITATIONS
HAUT RICHELIEU
145, RUE LATOUR, BUREAU 100
ST-JEAN-SUR-RICHELIEU, QC

ÉMISSION

No.	DATE	PAR	DESCRIPTION
3	2026-08-31	AR	POUR APPEL D'OFFRES

RÉVISION

No.	DATE	PAR	DESCRIPTION
1	2026-06-16	AR	COMPLÉT

PROJET:



RÉFÉCTION DES CUISINES ET
SALLES DE BAIN ET
ET DIVERS TRAVAUX

DESSIN:


LOT B - 155 MERCIER
LOGEMENTS TYPES
SERVICES ET ÉCLAIRAGE
ÉLECTRICITÉ

No. DOSSIER CLIENT:
HR26-14


DESSINATEUR:	CONCEPTEUR:
AR	AR
ÉCHELLE: 1:40	DATE: 24-03-15
No. DOSSIER ARI: OMR2402RCB	FICHER: ME.dwg
FEUILLE: E08	ÉMISSION: 3
	RÉVISION: C

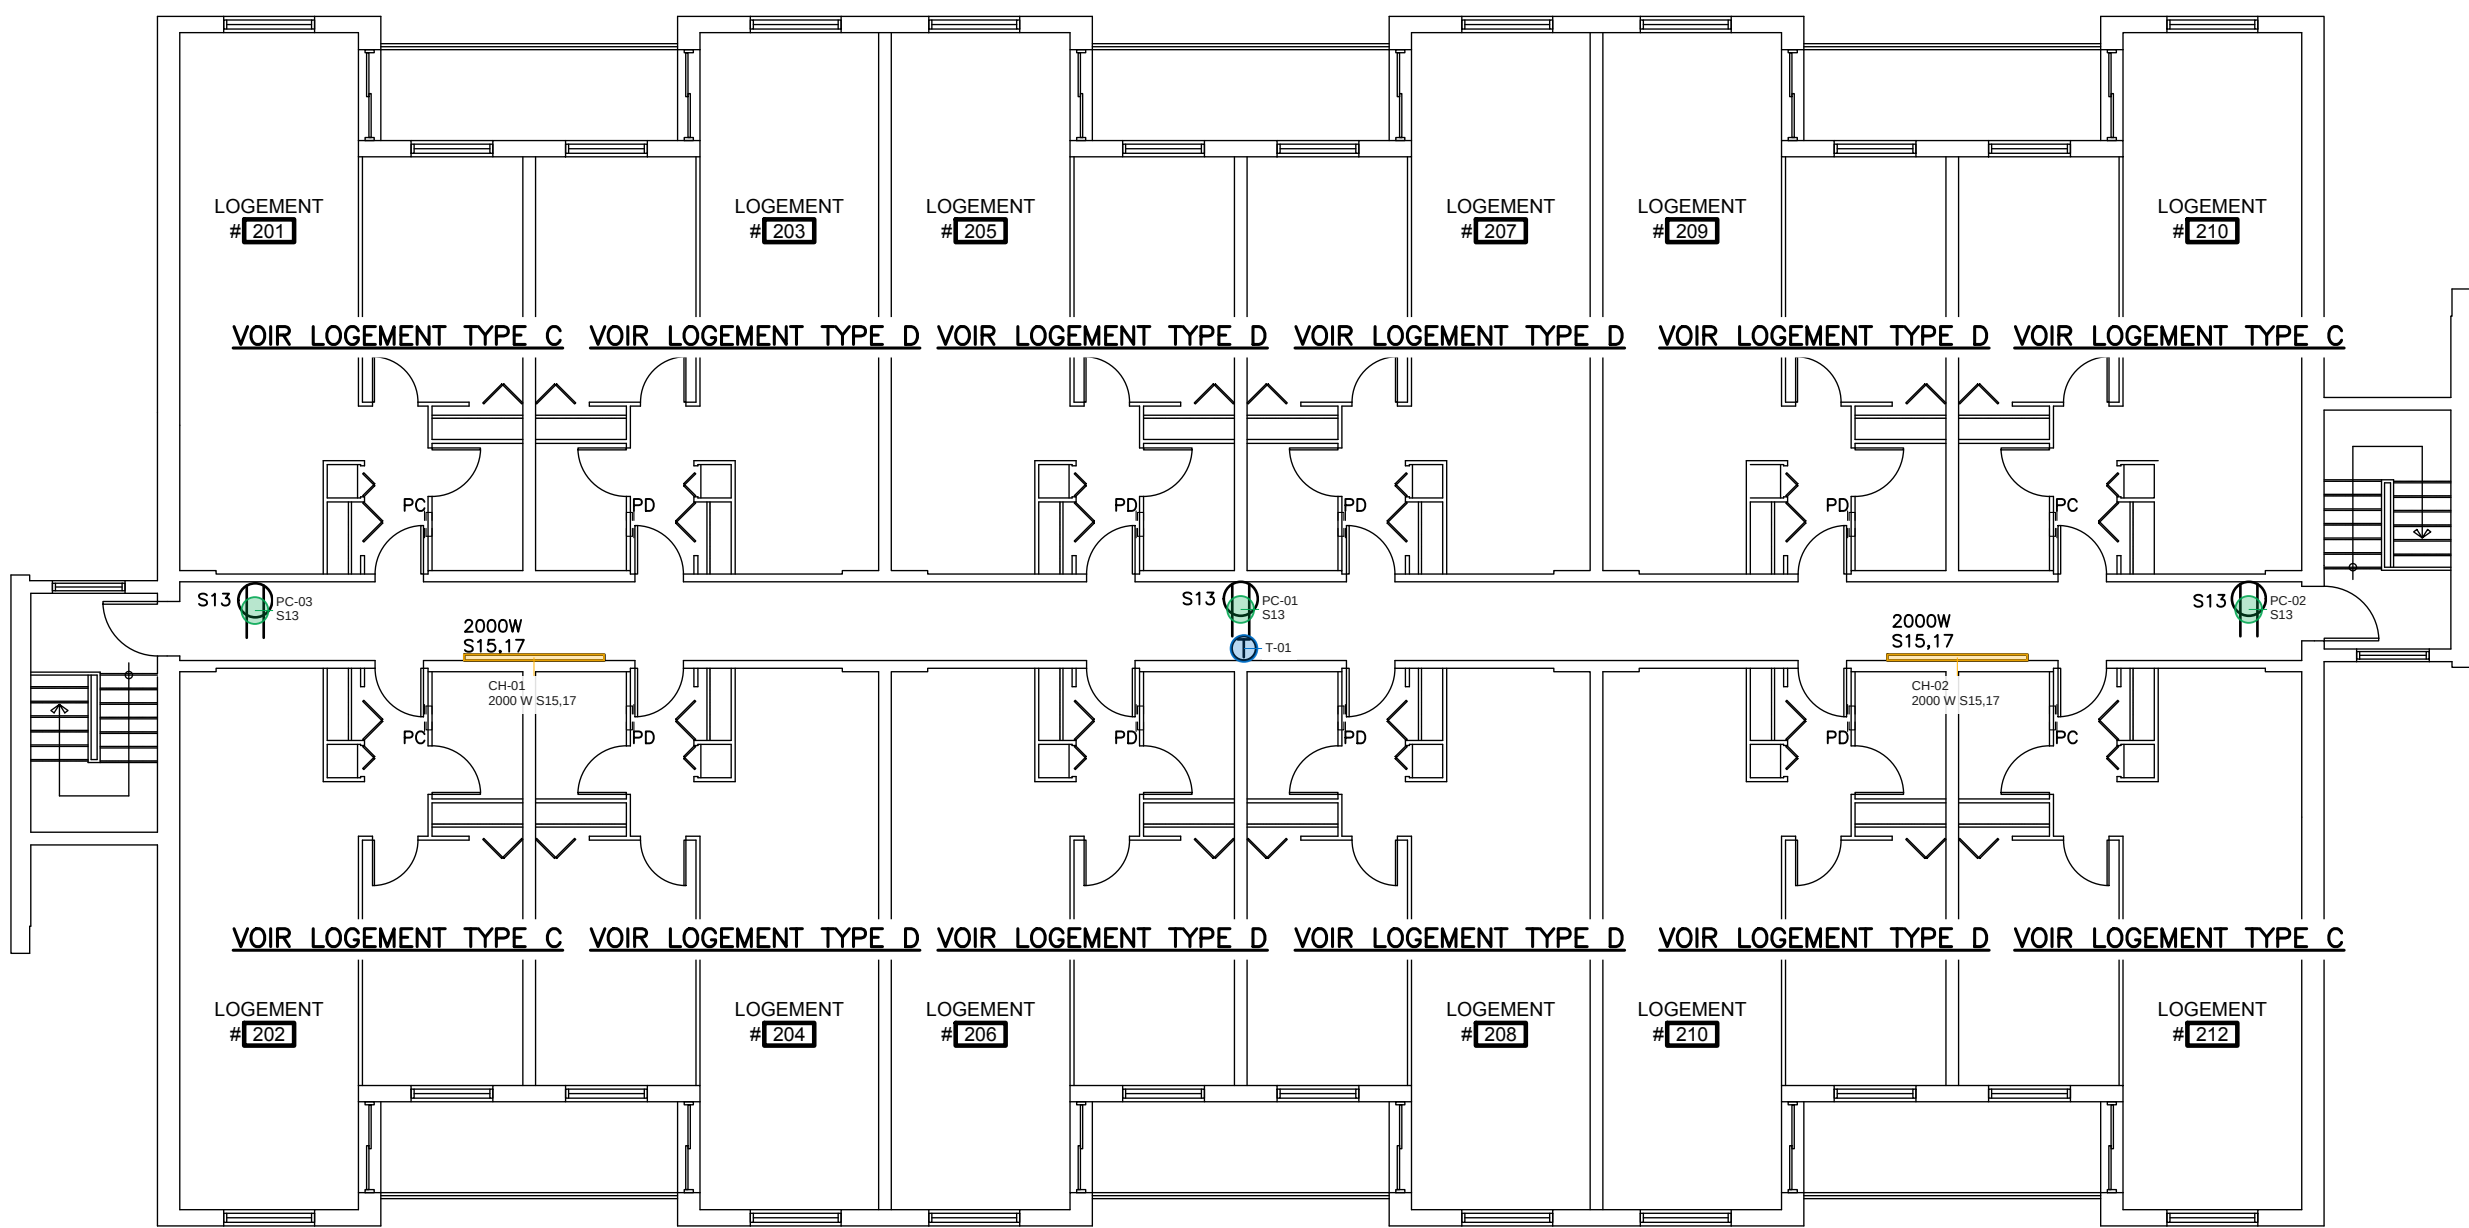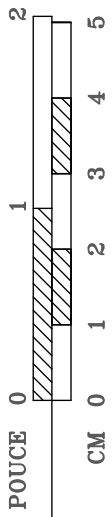

ÉTAGE

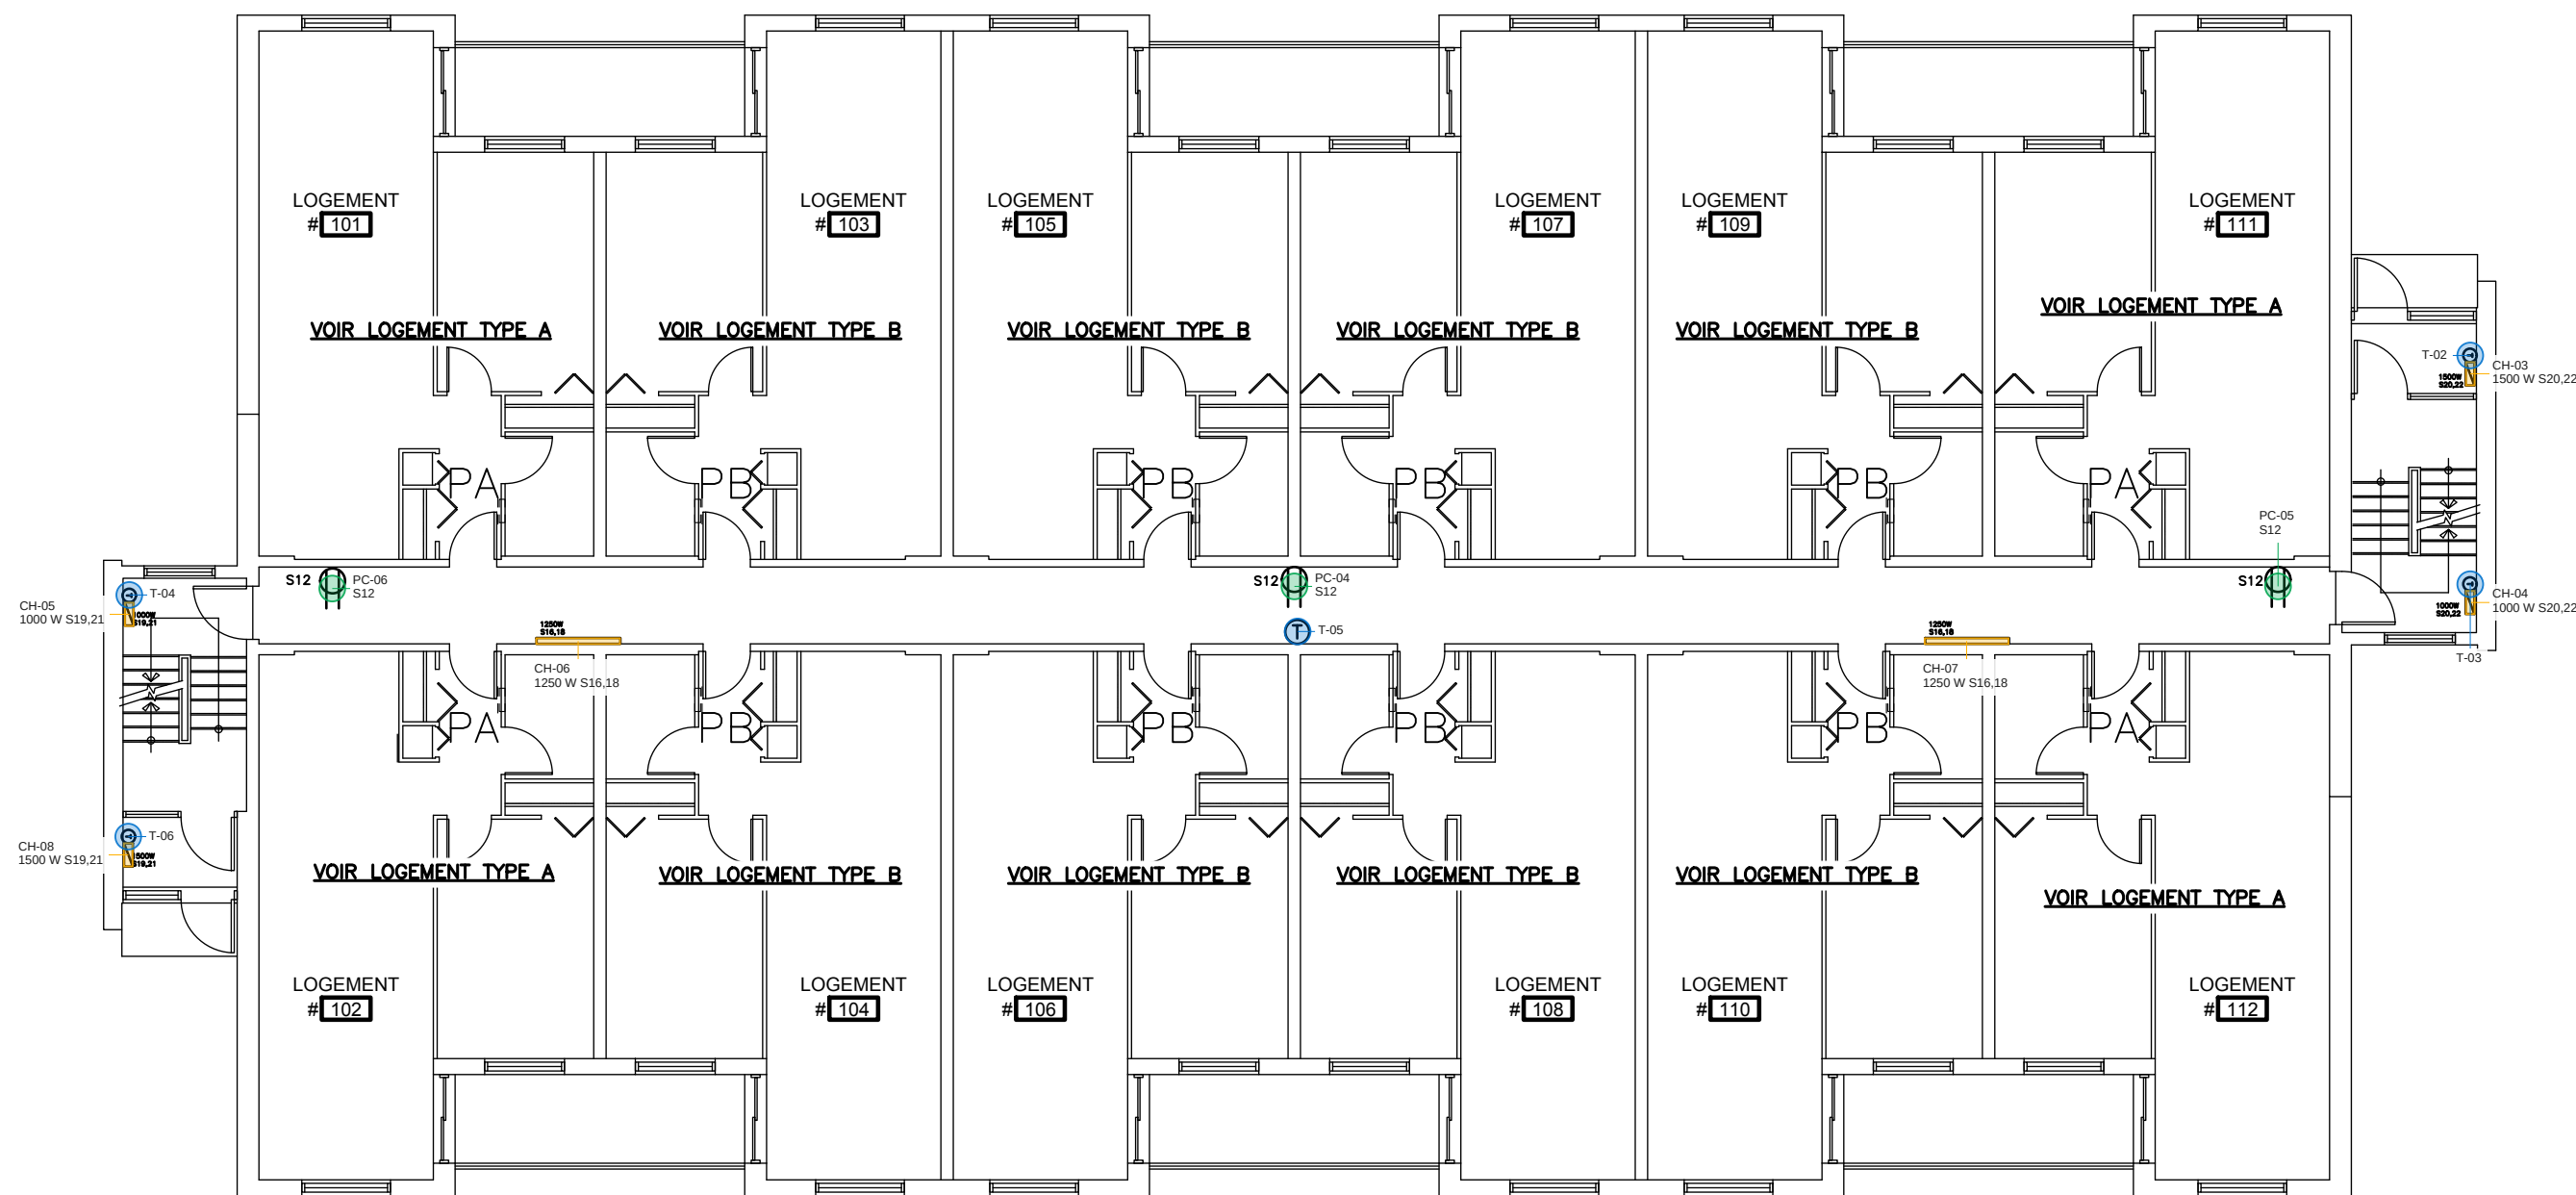

RDC

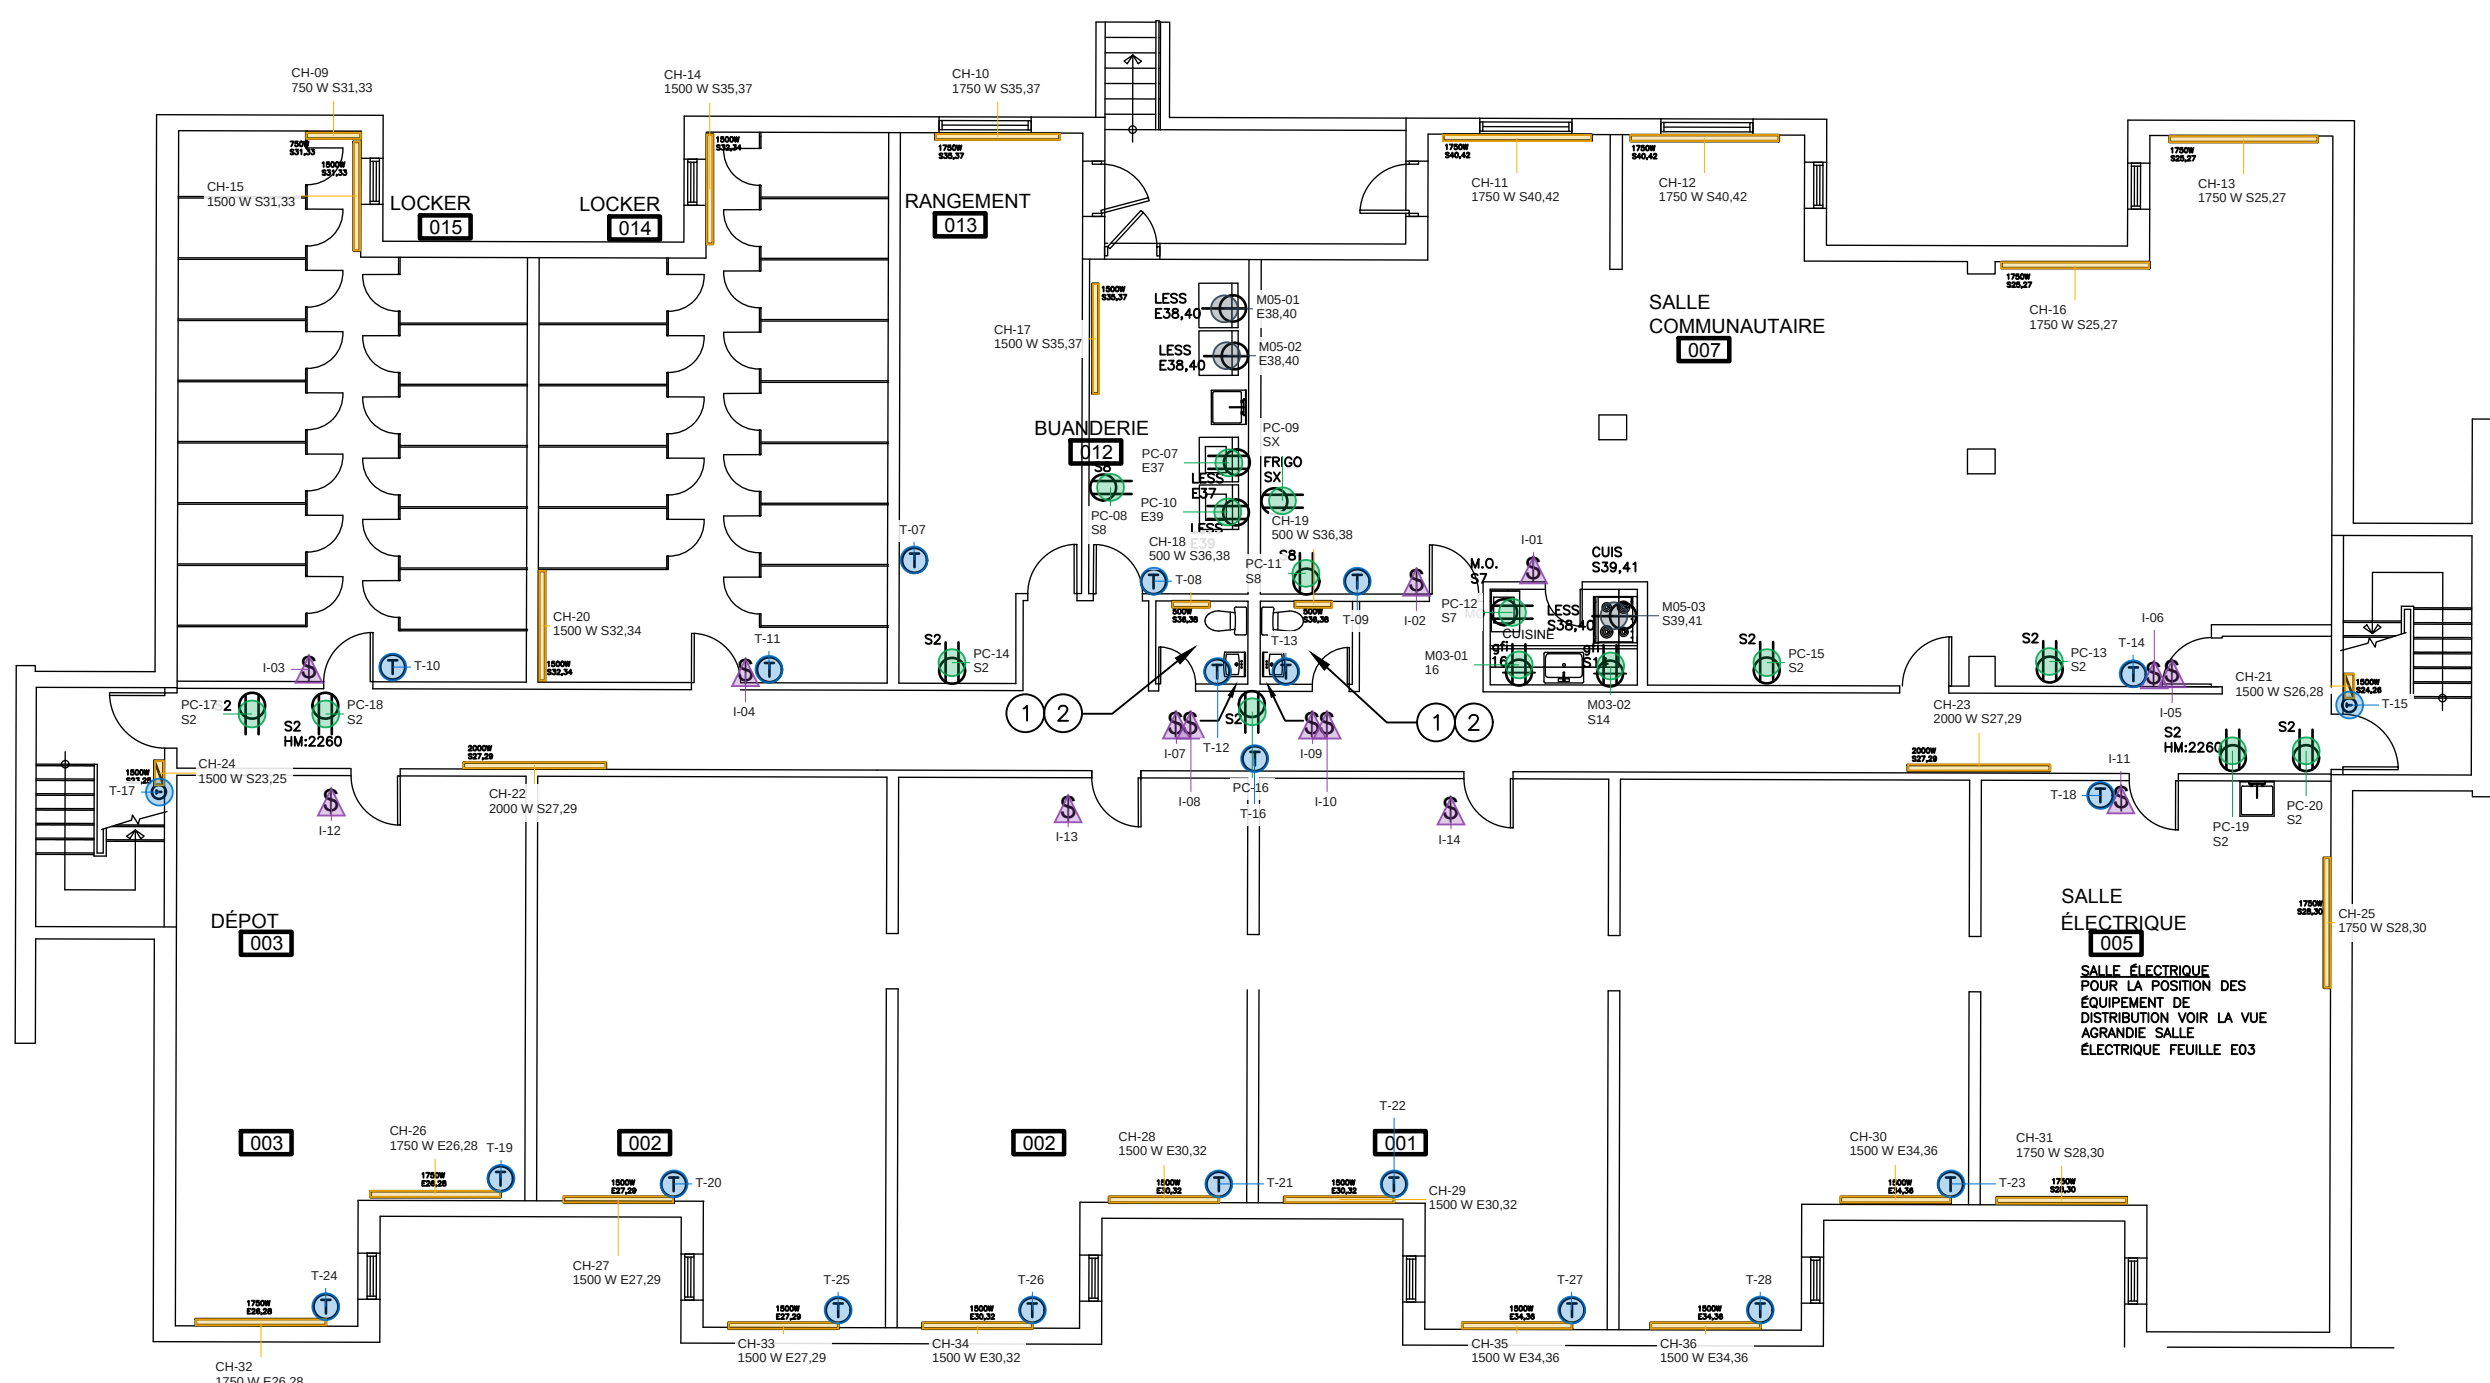

SOUS-SOL

RELEVÉ E09 - MATERIEL

103 repères / 6 familles / RES 103
Calques activables, prescriptions complètes page 2.
RES = reserve source, modele, position ou portee; * = identification a revalider

CH	APPAREIL DE CHAUFFAGE ÉLECTRIQUE EXISTANT	36 / R36	M05	PRISE SPÉCIALE EXISTANTE	3 / R3
I	COMMUTATEUR UNIPOLAIRE EXISTANT	14 / R14	PC	PRISE DE COURANT DOUBLE EXISTANTE	20 / R20
M03	PRISE DOFT EXISTANTE	2 / R2	T	THERMOSTAT EXISTANT	28 / R28

Repères source; quantités et réserves au bordereau.

PERCEMENT DE DALLE STRUCTURALE

JUSTIFICATION : LES DALLES DE PLAFOND ET PLANCHER SONT DES DALLES DE CIMENT VIDÉES AVEC DES CÂBLES EN PRÉ-TENSION. IL EST PRIMORDIAL DE NE PAS TOUCHER LES CÂBLES EN PRÉ-TENSION LORS DES PERCEMENTS. CEI N'EST PAS APPLICABLE À LA DALLE SUR SOL AU SOUS-SOL.

APPLICATION : POUR TOUTS LES PERCEMENTS ET ANCRAGES DEVANT ÊTRE EFFECTUÉS DANS UNE DALLE STRUCTURALE DE PLANCHER ET/OU PLAFOND, EXCLUANT LA DALLE SUR SOL.

PROCÉDURE : PRÉVOIR UN "SCAN" LOCAL DE LA DALLE VISÉE PAR LES TRAVAUX. IDENTIFIER À L'AIDE D'UN MARQUEUR LA POSITION DES CÂBLES EN PRÉ-TENSION ET DES SECTIONS VIDÉES DE DALLE. EFFECTUER TOUT PERCEMENT À UNE DISTANCE MINIMUM DE 50MM DE TOUTS CÂBLES EN PRÉ-TENSION.

NOTES EN PLAN

- ÉVACUEUR DANS CE LOCAL À DÉSINSTALLER ET RÉINSTALLER SUITE AUX TRAVAUX DE RÉAMÉNAGEMENT DU LOCAL. PRÉVOIR LE REMPLACEMENT DU CÂBLE D'ALIMENTATION À PARTIR DE L'INTERRUPTEUR.
- APPAREILS D'ÉCLAIRAGE (INCLUANT BÔÎTIER DE RACCORDEMENT) DANS CE LOCAL À DÉSINSTALLER ET RÉINSTALLER SUITE AUX TRAVAUX DE RÉAMÉNAGEMENT DU LOCAL. PRÉVOIR LE REMPLACEMENT DU CÂBLE D'ALIMENTATION À PARTIR DE L'INTERRUPTEUR.
- AUCUN TRAVAIL ÉLECTRIQUE REQUIS DANS CE LOCAL (LOCAL NOUVELLEMENT AMÉNAGÉ).

NOTES GÉNÉRALES

- LA POSITION DES SERVICES EXISTANTS SUR LES PLANS EST APPROXIMATIVE ET DOIT ÊTRE VÉRIFIÉE ET CONFIRMÉE SUR LE SITE.
- LA POSITION DES NOUVEAUX SERVICES INDICUÉE SUR LES PLANS EST APPROXIMATIVE ET DOIT ÊTRE CONFIRMÉE AVEC LES PLANS D'AMÉNAGEMENT EN ARCHITECTURE.
- LA TOTALITÉ DES CIRCUITS D'ALIMENTATION EXISTANTS À CONSERVER SONT FAITS AVEC DU CÂBLE AVEC CONDUCTEUR D'ALUMINIUM. PRÉVOIR DES DISPOSITIFS (PRISE DE SERVICE, INTERRUPTEUR, ETC.) ET DES MÉTHODES DE RACCORDEMENT ET D'INSTALLATION, APPROPRIÉS ET COMPATIBLES AVEC DES CONDUCTEURS D'ALUMINIUM.
- L'ENTREPRENEUR EST RESPONSABLE DE NE PAS CASSER LES EXTRÉMITÉS DES CONDUCTEURS D'ALUMINIUM EXISTANT. L'ENTREPRENEUR SERA TENU DE REMPLACER, À SES FRAIS, (INCLUANT LES TRAVAUX GÉNÉRAUX) TOUTS LES CÂBLES AVEC CONDUCTEURS D'ALUMINIUM RENDUS TROP COURTS PAR SA MANIPULATION.
- LA POSITION DES SERVICES EST DONNÉE À TITRE INDICATIF SEULEMENT. LA POSITION EXACTE DE CES SERVICES DOIT ÊTRE DÉTERMINÉE SUR LE CHANTIER.
- L'IDENTIFICATION DES CIRCUITS D'ALIMENTATION EST DONNÉE À TITRE INDICATIF SEULEMENT. ELLE DOIT ÊTRE VÉRIFIÉE ET VALIDÉE AU CHANTIER.
- POUR LE REMPLACEMENT DES PLINTE DES ÉQUIPEMENTS DE CHAUFFAGE (PLINTE, AÉROTHERME, CONVECTEUR, ETC.), VÉRIFIER SUR LE SITE ET CONFIRMER LA PUISSANCE DE CHAUFFE, LES CARACTÉRISTIQUES D'ALIMENTATION ET LE TYPE DE CONTRÔLE (THERMOSTAT INTÉGRÉ OU THERMOSTAT DE LIGNE EXISTANT À CONSERVER), ET CE, AVANT DE RELÂCHER LES COMMANDES.
- TOUTS LES APPAREILS DE CHAUFFAGE ÉLECTRIQUE, PRISE DE SERVICE ET INTERRUPTEUR D'ÉCLAIRAGE INDICUÉS SUR LES VUES EN PLAN SONT EXISTANTS À CONSERVER.
- TOUTS LES THERMOSTATS DE PIÈCE INDICUÉS SUR LES VUES EN PLAN SONT EXISTANTS À CONSERVER.

NE PAS UTILISER
POUR CONSTRUCTION

CONSULTANT:



SCEAU:

CLIENT:

OFFICE D'HABITATIONS
HAUT RICHELIEU
145, RUE LATOUR, BUREAU 100
ST-JEAN-SUR-RICHELIEU, QC

ÉMISSION

No.	DATE	PAR	DESCRIPTION
3	2026-08-31	AR	POUR APPEL D'OFFRES

RÉVISION

No.	DATE	PAR	DESCRIPTION
1	2026-06-16	AR	COMPLÉT

PROJET:

RÉFECTION DES CUISINES ET
SALLES DE BAIN ET
ET DIVERS TRAVAUX

DESSIN:

LOT C - 290 MONTCALM
VUES EN PLAN
SERVICES ET ÉCLAIRAGE
ÉLECTRICITÉ

No. DOSSIER CLIENT: HR26-14	CONCEPTEUR: AR
DESSINATEUR:	DATE: 24-03-15
ÉCHELLE: 1:125	FICHER: ME.dwg
No. DOSSIER ARI: OMR2402RCB	RÉVISION C
FEUILLE: E09	ÉMISSION: 3