

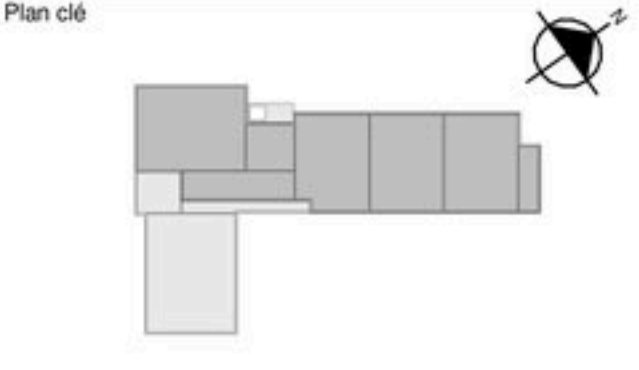


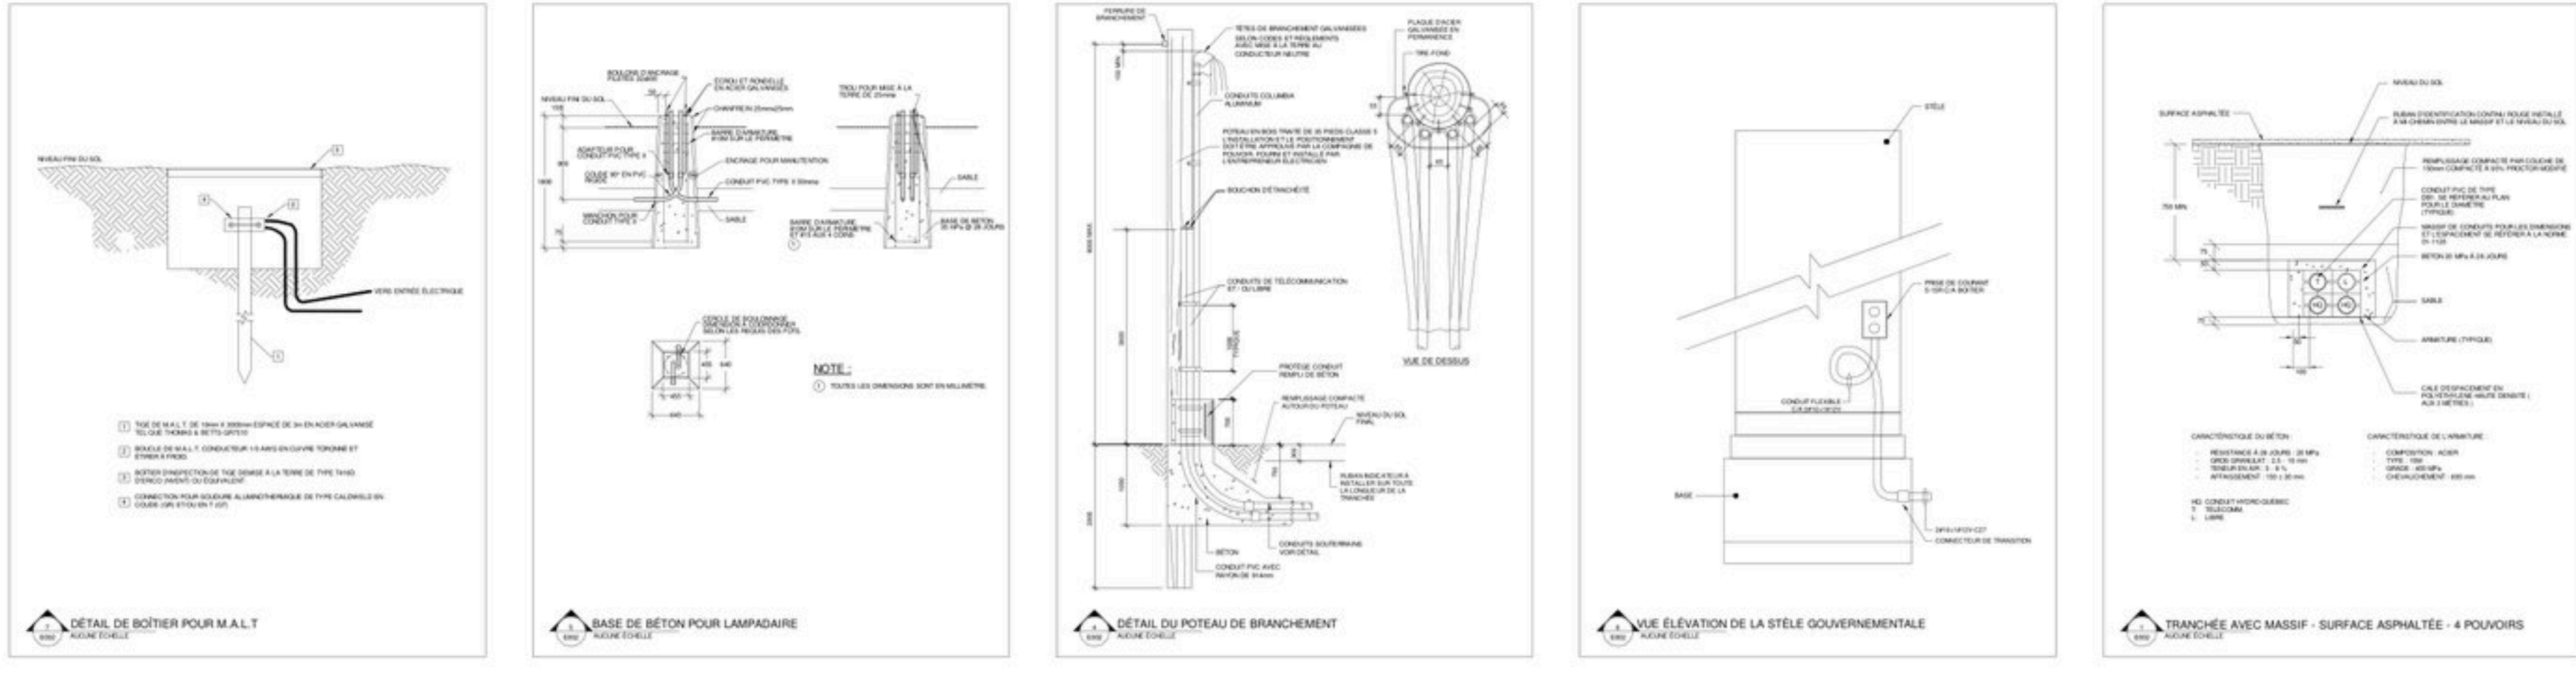

- Notes
- Avant l'exécution des travaux, l'entrepreneur doit vérifier les dimensions et les conditions de chantier et avoir immédiatement l'architecte de toutes les situations non conformes aux plans et devis.
 - Ne jamais prendre de mesures à l'échelle sur les dessins.
 - Ce dessin peut être utilisé pour la construction seulement et seulement s'il a été "ÉMIS POUR CONSTRUCTION".

Légende — E002 (12 marques)

- Luminaire B1 (9)
- Luminaire L1 (2)
- Raccordement équipement divers (1)

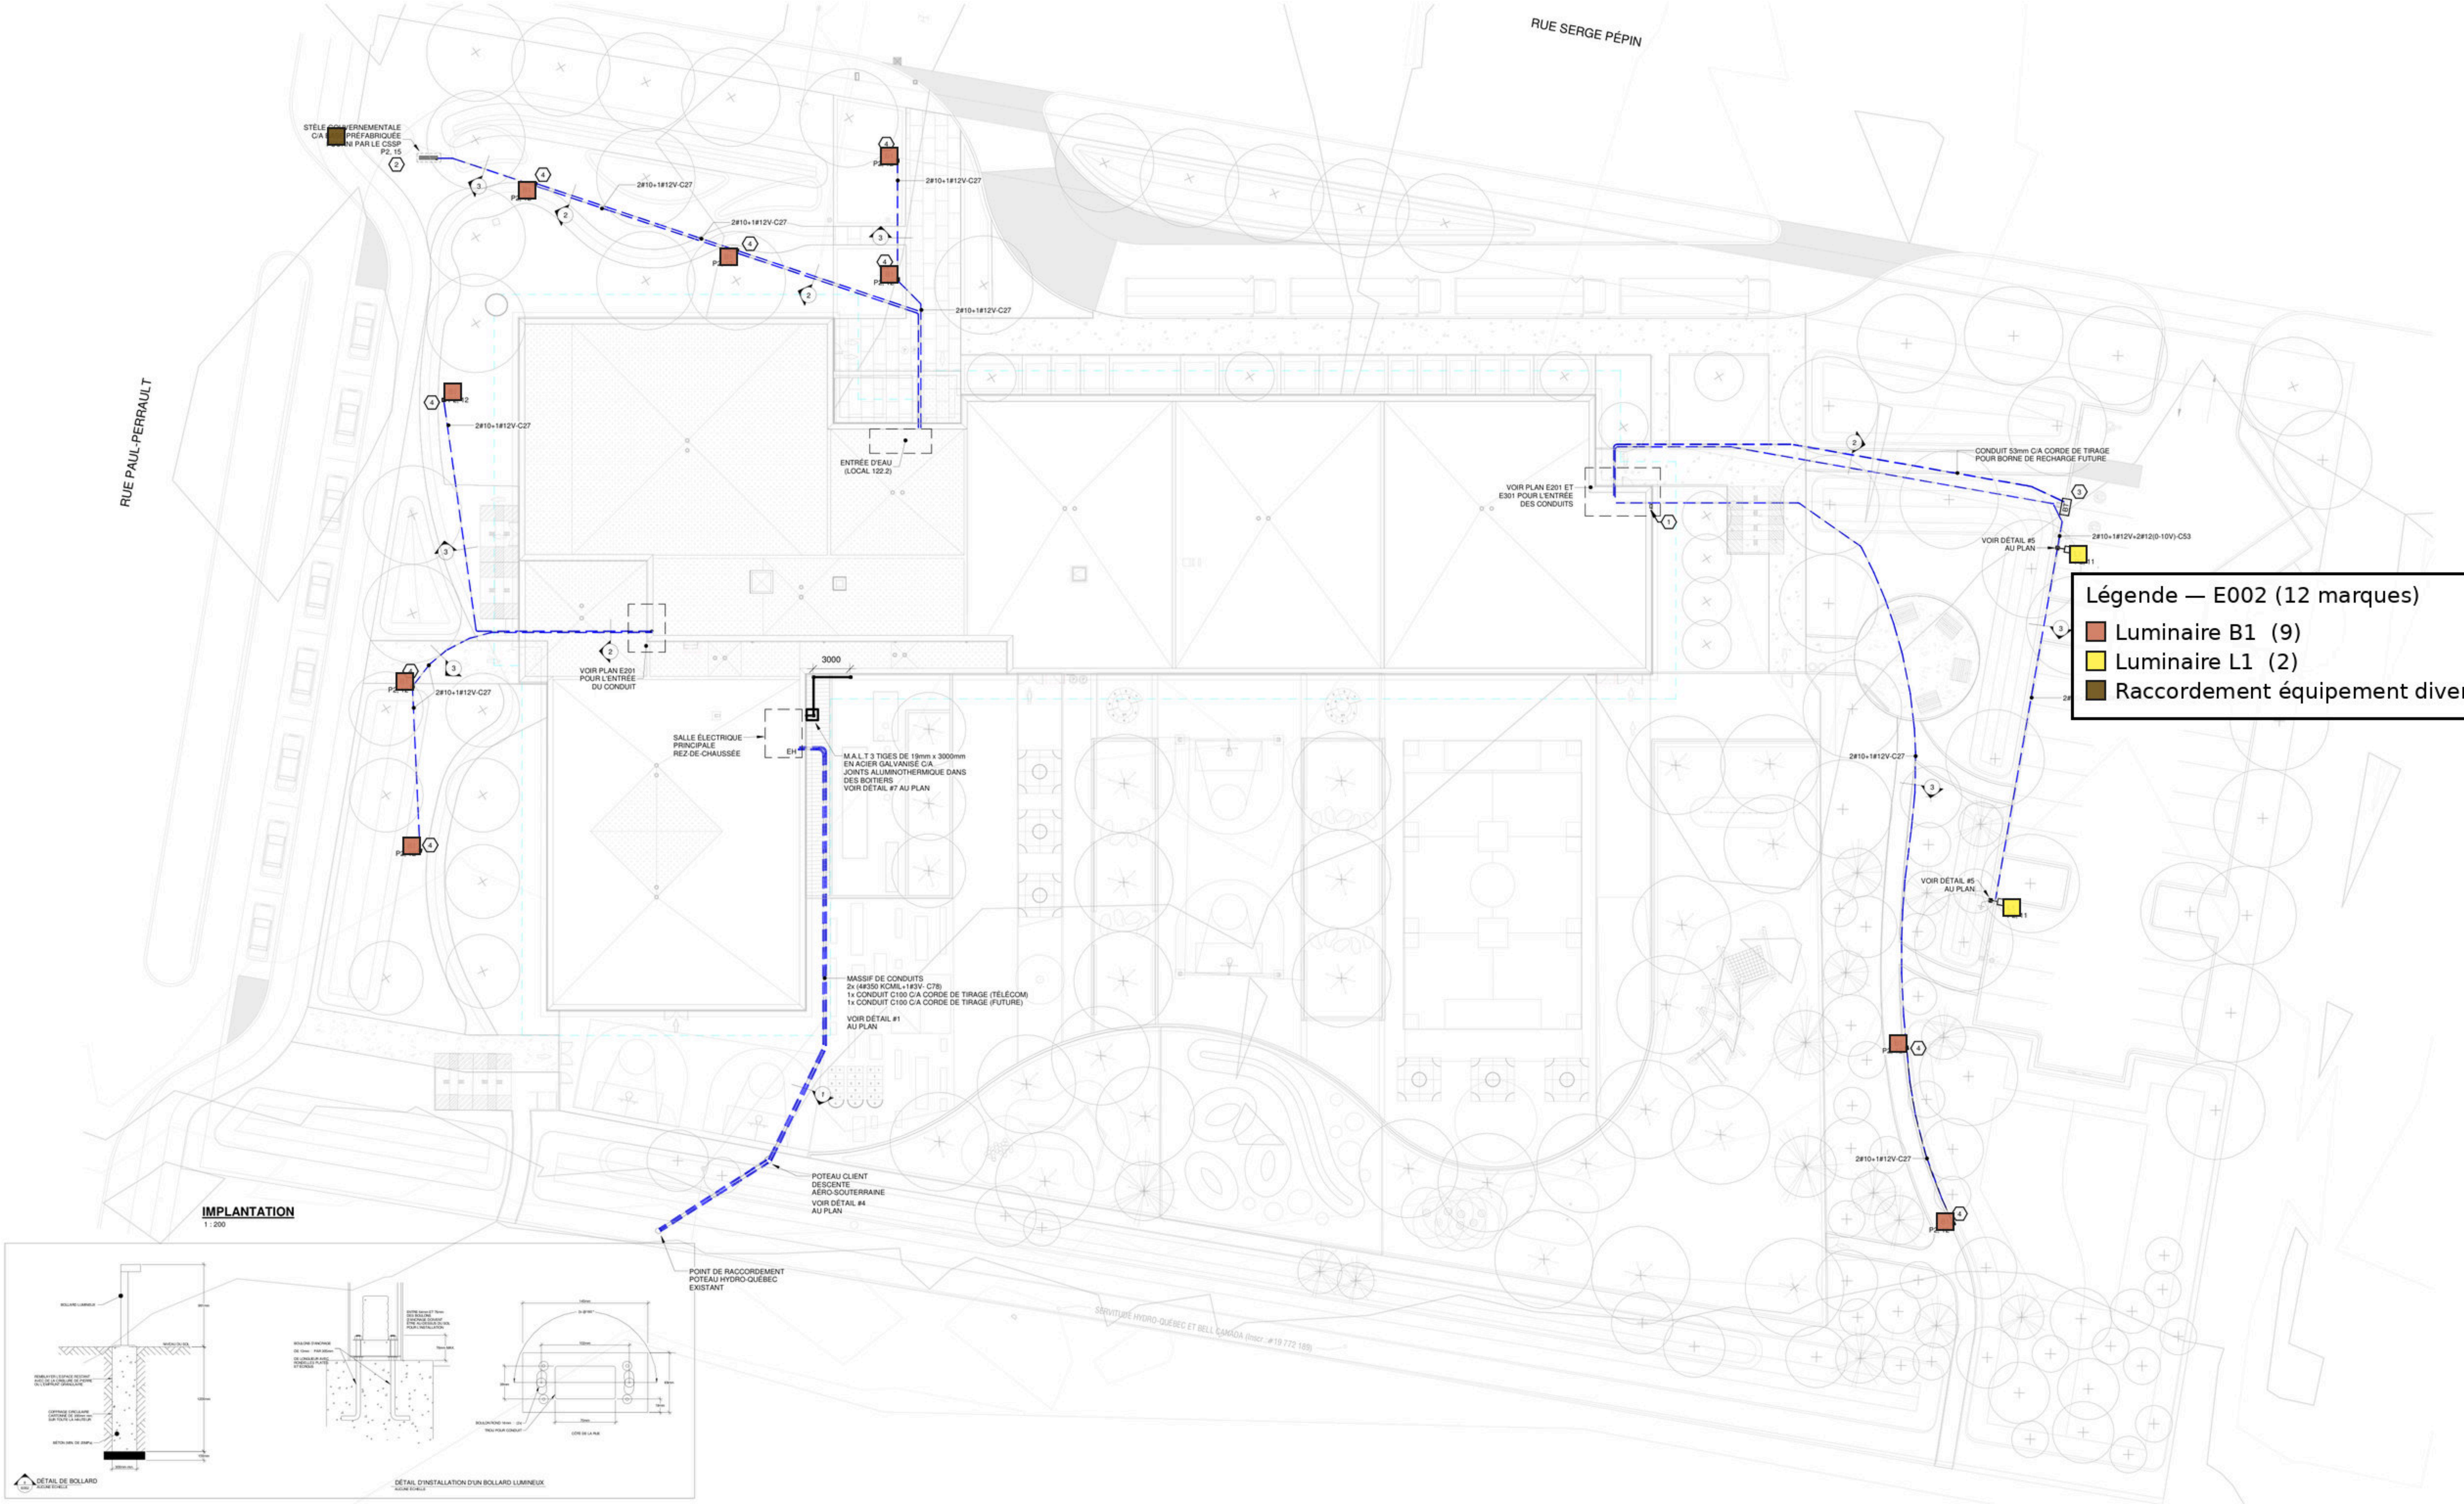

- NOTE(S):**
- 1 FOURNIR ET INSTALLER UN BOUTIER EN PVC ÉTANCHE 300x300x100mm NEMA4 ENCASTRÉ AU MUR C/A PRISE DE COURANT 15A 120V 1PH. CETTE BOTE SERA À ALIMENTER ET PROTÉGER LA PASSERELLE DE COMMUNICATION POUR LA BORNE DE RECHARGE ÉLECTRIQUE (FUTURE). VOIR PLAN E001 POUR L'EMPLACEMENT.
 - 2 FOURNIR ET INSTALLER UNE PRISE DE COURANT 5-15R C/A BOUTIER À L'INTÉRIEUR DE LA STELE. L'AISIR 3M DE FILAGE SUPPLÉMENTAIRE À PARTIR DU SOL. LE DISJONCTEUR QUI ALIMENTE LA STELE DOIT ÊTRE DE TYPE DDFT. COORDONNER AVANT LE DÉBUT DES TRAVAUX.
 - 3 FOURNIR ET INSTALLER UN BOUTIER PVC 300x300x100mm AU SOL ET TERMINER LE CONDUIT À CE DERNIER, POUR BORNE DE RECHARGE FUTURE.
 - 4 FOURNIR ET INSTALLER LA BASE DE BÉTON. COORDONNER LE CERCLE DE BOULONNAGE DE LA BASE DU POTEAU AVEC LA BASE DE BÉTON ET CE AVANT LA COMMANDE. FOURNIR, INSTALLER ET RACCORDER L'APPAREIL D'ÉCLAIRAGE.

0	APPEL D'OFFRES	2026-01-23
Révision	Émis pour	Date



Architecture
PROVENCHER ROY ÉPIGRAPHE
PRA
375, RUE SAINT-JACQUES, BUREAU 700
MONTREAL, QUEBEC, CANADA H2Y1N6
ÉPIGRAPHE
385, RUE RICHELIEU, BUREAU 202
BELOEIL, QUEBEC, CANADA H3A1P9

Experts conseils
Structure



Mécanique - Électricité - Plomberie




TETRA TECH INC.
300, RUE SAINT-JACQUES
BUREAU 210
MONTREAL, QUEBEC, CANADA H2Y1N6
T 439-887-4442
PONTON GUILLLOT
318, CHENEAUX, QUÉBEC, CANADA, H3A 1G3
T 439-513-1022


Dessin
IMPLANTATION

Echelle	Dessiné par	E002_0
Comme indiqué	S.DUBOIS	
Date	Approuvé par	
Date de fin	M.-P. GUILLLOT	
Numéro du projet	Numéro du dessin	Révision
104-14-00	E002	0

2026-02-11 11:35:12

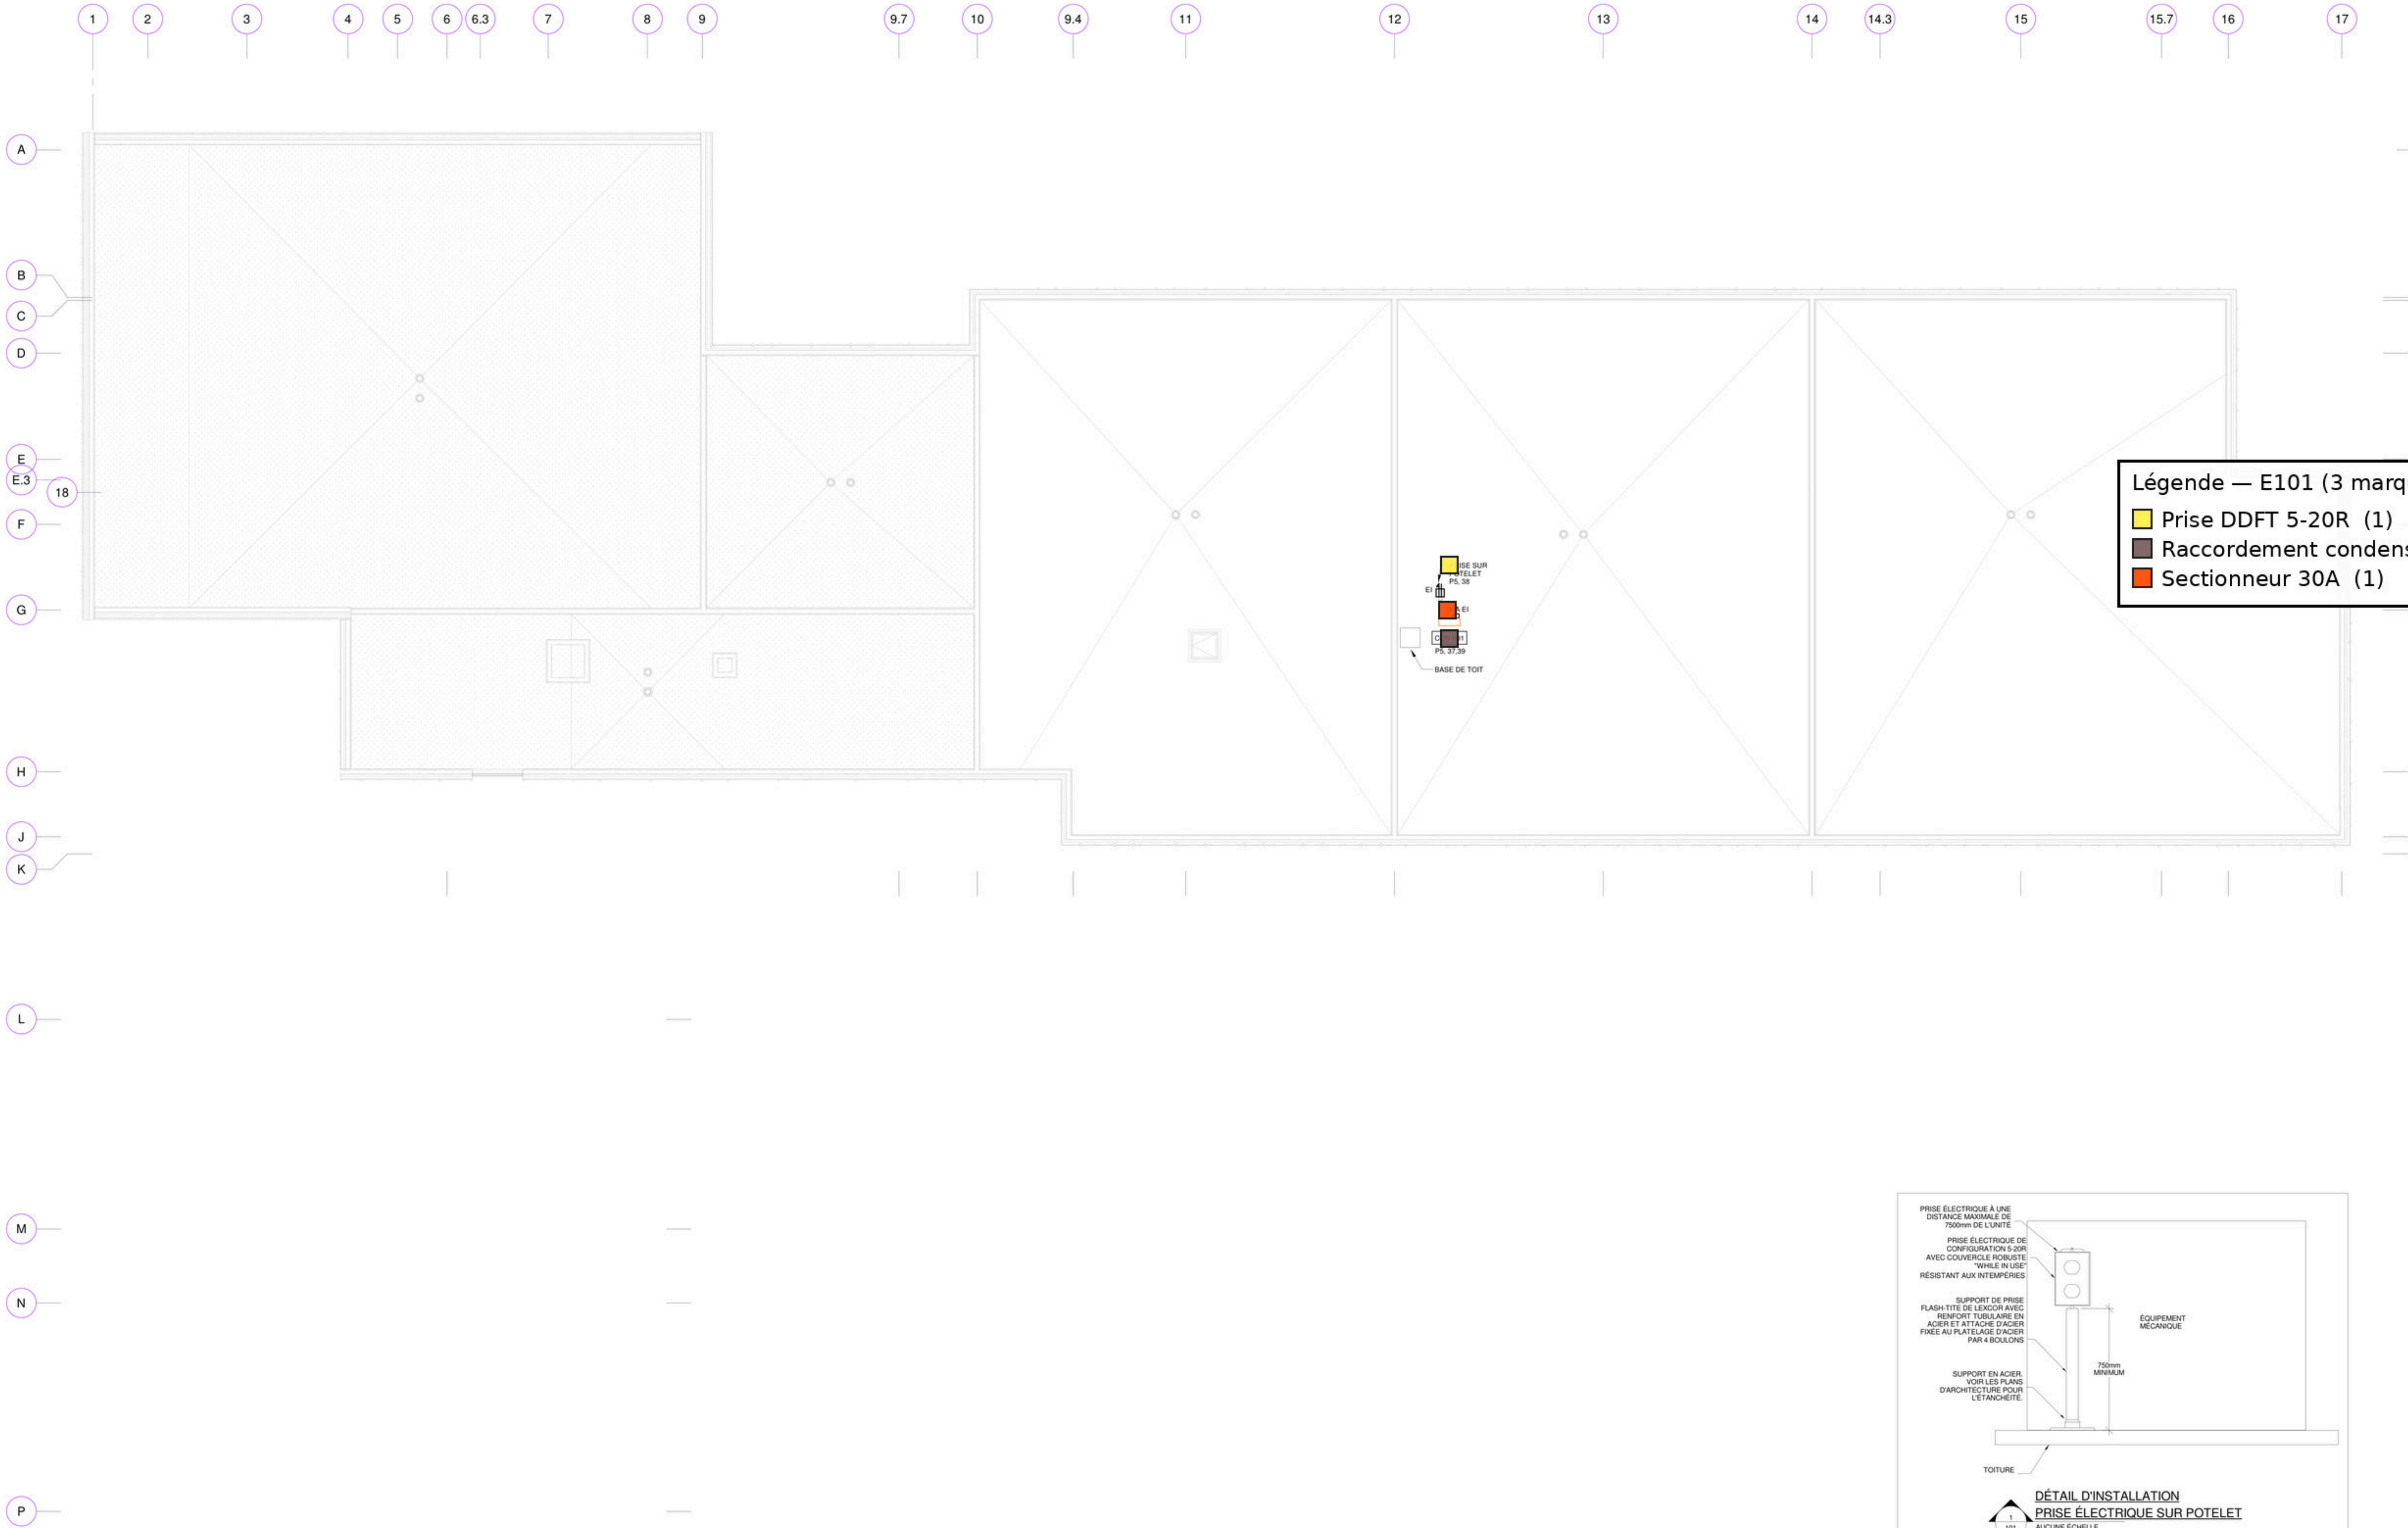

TOITURE
1 : 100

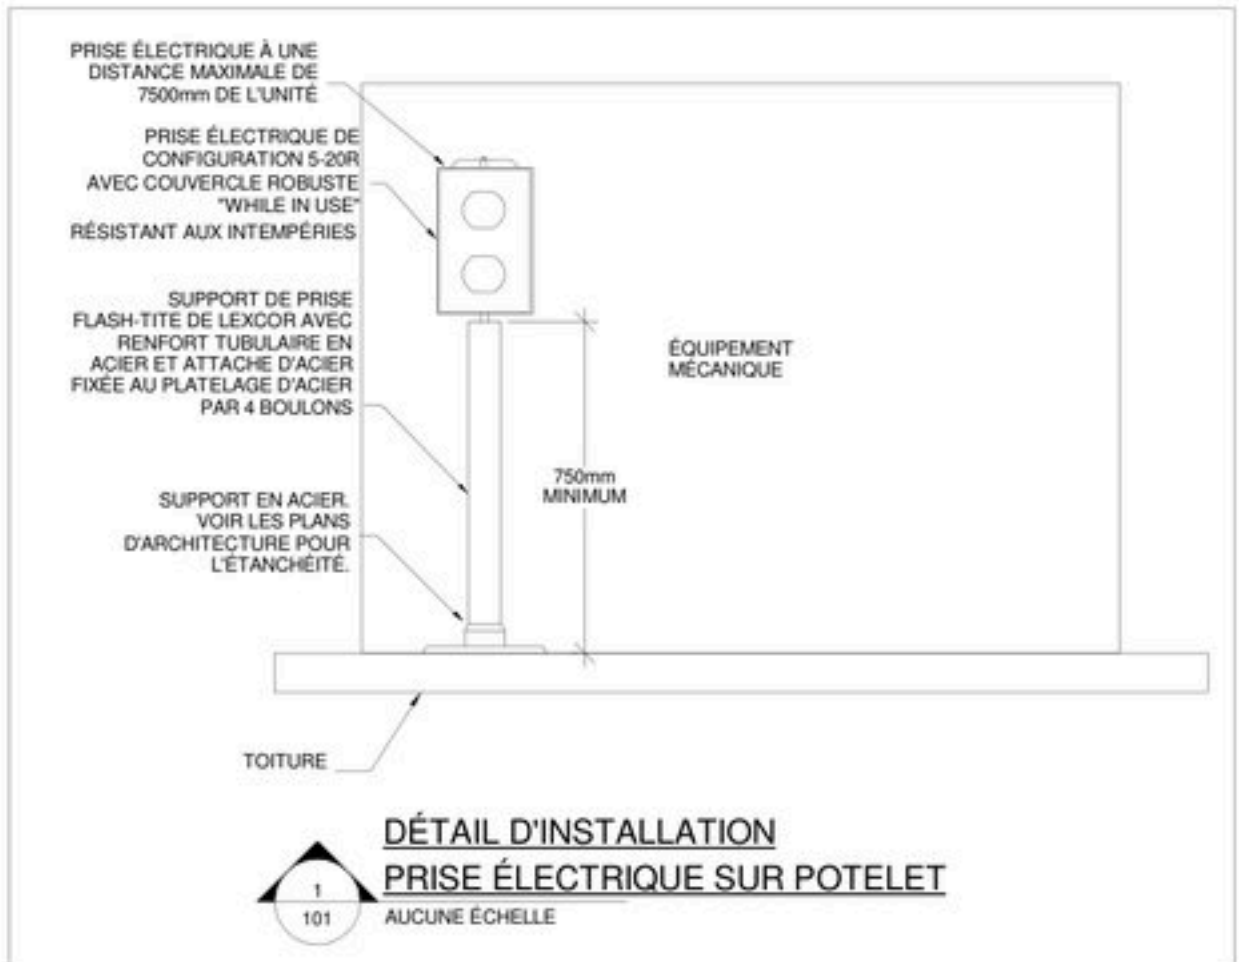


Projet

CONSTRUCTION D'UNE NOUVELLE ÉCOLE PRIMAIRE DE 16 CLASSES À BELOEIL

2800 RUE SERGE-PÉPIN, BELOEIL, QC
CSS DES PATRIOTES

Plan clé

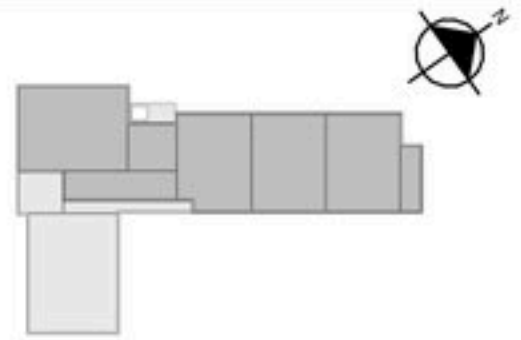

Notes

- Avant l'exécution des travaux, l'entrepreneur doit vérifier les dimensions et les conditions de chantier et avoir immédiatement l'architecte de toutes les situations non conformes aux plans et devis.
- Ne jamais prendre de mesures à l'échelle sur les dessins.
- Ce dessin peut être utilisé pour la construction seulement et seulement s'il a été: "EMIS POUR CONSTRUCTION"

0	APPEL D'OFFRES	2026-01-23
Révision	Émis pour	Date
Scieur		
		
Architecture		
PROVENCHER ROY ÉPIGRAPHE		
P.R.A. 375, RUE SAINT-JACQUES, BUREAU 700 MONTRÉAL, QUÉBEC, CANADA H3T 1Y6		
ÉPARGNE 885, RUE RICHELIEU, BUREAU 202 BELOEIL, QUÉBEC, CANADA H3B 6P6		
Experts conseils		
Structure		
		
GB 1510 RUE DE SÉBASTIEN L'ARROUAILLÉ, QUÉBEC, CANADA J4M 0J7 T 468 670 4225		
Mécanique - Électricité - Plomberie		
		
TETRA TECH Q INC. 2005, RUE JACQUES-CARSON BUREAU 210 L'ARROUAILLÉ, QUÉBEC, CANADA J4M 0J7 T 468 667 4445		
PONTON GUILLOT 2118, CHEMIN D'ARCON L'ARROUAILLÉ, QUÉBEC, CANADA J4M 0J7 T 468 572 1022		
Dessin		
TOITURE		
E101_0		
Echelle	Dessiné par	
Comme indiqué	S.DUBOIS	
Date	Approuvé par	
Date de fin	M.-P. GUILLOT	
Numéro du projet	Numéro du dessin	Révision
104-14-00	E101	0

2026-02-11 11:35:12

2026-02-11 11:35:56



NIVEAU 2 - ÉCLAIRAGE
1 : 100

Projet

CONSTRUCTION D'UNE NOUVELLE ÉCOLE PRIMAIRE DE 16 CLASSES À BELOEIL

2800 RUE SERGE-PÉPIN, BELOEIL, QC
CSS DES PATRIOTES

Plan clé

Notes

- Avant l'exécution des travaux, l'entrepreneur doit vérifier les dimensions et les conditions de chantier et avoir immédiatement l'architecte de toutes les situations non conformes aux plans et devis.
- Ne jamais prendre de mesures à l'échelle sur les dessins
- Ce dessin peut être utilisé pour la construction seulement et seulement s'il a été "EMIS POUR CONSTRUCTION"

0

APPEL D'OFFRES

2026-01-23

Révision

Émis pour

Date

Scieur

Architecture

PROVENCHER ROY
ÉPIGRAPHE

PRO
376, RUE SAINT-JACQUES, BUREAU 700
MONTREAL, QUEBEC, CANADA H2Y1N2
ÉPIGRAPHE
884, RUE RICHELIEU, BUREAU 202
BELOEIL, QUEBEC, CANADA H3B4P5

Experts conseils

Structure

GBI
1510 RUE DE SÉBASTIEN
L'ARROCHEL, QUEBEC, CANADA J4M 0J7
T 468-675-4225

Mécanique - Électricité - Plomberie

TETRA TECH Q INC.
2001, RUE JACQUES-CARON
BUREAU 210
L'ARROCHEL, QUEBEC, CANADA J4M 0J7
T 468-667-4445
PONTON GUILLOT
2118 CHENEAUX-ROUSSEAU
L'ARROCHEL, QUEBEC, CANADA
J4M 0J7
T 468-773-1022

Dessin

ÉCLAIRAGE

NIVEAU 2

E202_0

Echelle

Dessiné par

Date

Approuvé par

Date de fin

Numéro du projet

Numéro du dessin

Révision

1 : 100


S.DUBOIS

M.-P. GUILLOT

104-14-00

E202

0

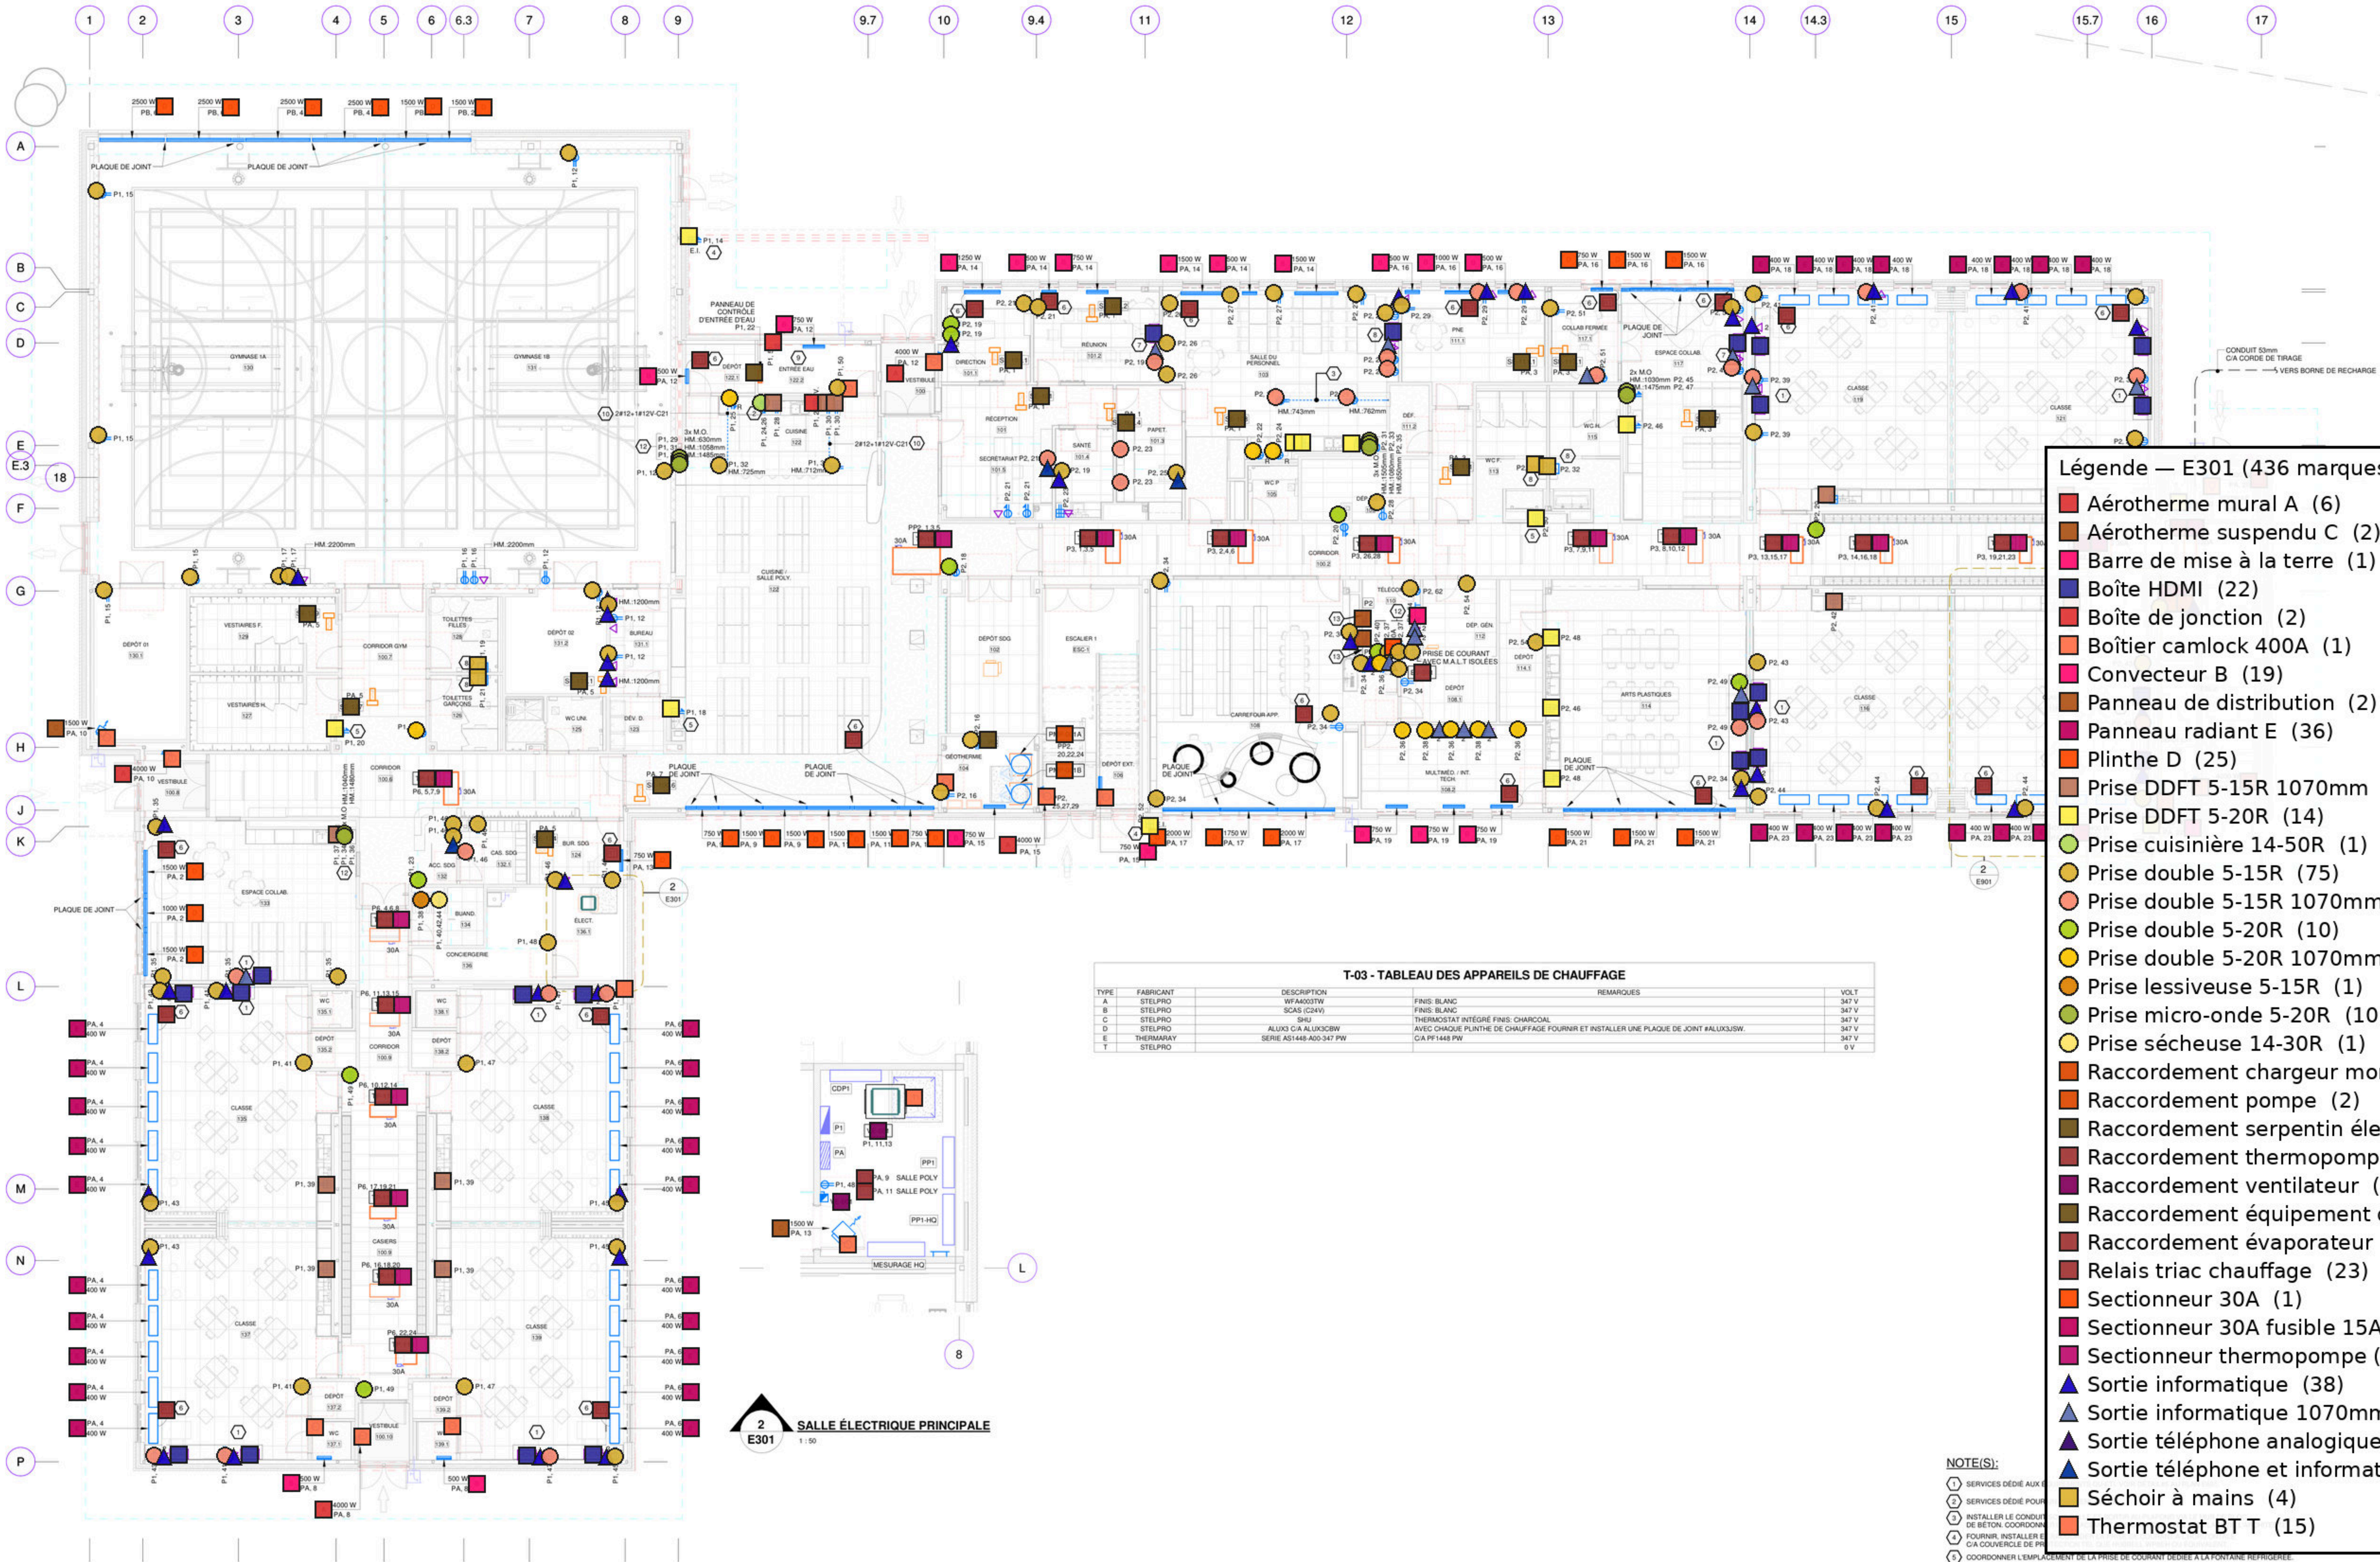

NIVEAU 1 - SERVICES
1:100

T-03 - TABLEAU DES APPAREILS DE CHAUFFAGE				
TYPE	FABRICANT	DESCRIPTION	REMARQUES	VOLT
A	STELPRO	WFA003TW	FNIS BLANC	347 V
B	STELPRO	SCAS (C24V)	FNIS BLANC	347 V
C	STELPRO	SHJ	THERMOSTAT INTÉGRÉ FNIS CHARCOAL	347 V
D	STELPRO	ALUX3 C/A ALUX30BW	AVEC CHAQUE PLINTE DE CHAUFFAGE FOURNI ET INSTALLER UNE PLAQUE DE JOINT #ALUX30W	347 V
E	THERMARAY	SERIE AS1448-ADD-347 PW	C/A P1148 PW	347 V
F	STELPRO			0 V

- NOTE(S):
- SERVICES DÉDIÉ AUX ÉQUIPEMENTS DE LA PRIZE DE COURANT DÉDIÉE À LA FONTAINE RÉFRIGÉRÉE
 - SERVICES DÉDIÉ POUR
 - INSTALLER LE CONDUIT DE BÉTON, COORDONNER L'EMPLACEMENT EXACT AVEC LA DISCIPLINE D'AUTOMATISATION AVANT LE DÉBUT DES TRAVAUX
 - SERVICES DÉDIÉS AUX ÉQUIPEMENTS DU TÉLÉVISEUR INTERACTIF: VOIR DÉTAIL #11
 - FOURNIR, INSTALLER ET RACCORDER UN SÈCHE MAIN TEL QUE COMAC ONE #C-10022004 OU ÉQUIVALENT, COORDONNER AVEC LES PLANS D'ARCHITECTURE POUR LA HAUTEUR DE MONTAGE.
 - BÔTE DE JONCTION DÉDIÉE POUR L'ALIMENTATION ÉLECTRIQUE DES COMPTEURS D'ENTRÉES D'EAU PRIMAIRE ET SECONDAIRE, ASSURER QUE LES VALVES DE CONTRÔLE Y VOIES PRIMAIRE ET SECONDAIRE, TRANSFORMATEUR 120/24V FOURNI, INSTALLER PAR LA DISCIPLINE 22 ET RACCORDER PAR LA DISCIPLINE D'AUTOMATISATION.
 - ACHÉMINER LE CONDUIT SOUS DALLE, COORDONNER L'EMPLACEMENT EXACT AVANT LE DÉBUT DES TRAVAUX.
 - FOURNIR ET INSTALLER UN CONTACTEUR MAGNÉTIQUE 30A, 208V-ØP DANS UN BÔTIER DANS L'ENTREPLAFOND.
 - INSTALLER LES PRISES DE COURANT À PROXIMITÉ DES SERVEURS, LES SITUER LE PLUS HAUT POSSIBLE ET BIEN LES IDENTIFIER.
 - FOURNIR ET INSTALLER UN CONDUIT VIDE DE 53mm C/A CORDE DE TIRAGE ENTRE LE PANNEAU ET L'ENTREPLAFOND POUR FUTURE USAGE.


Légende — E301 (436 marques)

- Aérotherme mural A (6)
- Aérotherme suspendu C (2)
- Barre de mise à la terre (1)
- Boîte HDMI (22)
- Boîte de jonction (2)
- Boîtier camlock 400A (1)
- Convecteur B (19)
- Panneau de distribution (2)
- Panneau radiant E (36)
- Plinthe D (25)
- Prise DDFT 5-15R 1070mm (12)
- Prise DDFT 5-20R (14)
- Prise cuisinière 14-50R (1)
- Prise double 5-15R (75)
- Prise double 5-15R 1070mm (26)
- Prise double 5-20R (10)
- Prise double 5-20R 1070mm (10)
- Prise lessiveuse 5-15R (1)
- Prise micro-onde 5-20R (10)
- Prise sècheuse 14-30R (1)
- Raccordement chargeur monte-personne (2)
- Raccordement pompe (2)
- Raccordement serpentin électrique (14)
- Raccordement thermopompe (18)
- Raccordement ventilateur (2)
- Raccordement équipement divers (2)
- Raccordement évaporateur (1)
- Relais triac chauffage (23)
- Sectionneur 30A (1)
- Sectionneur 30A fusible 15A (add. E-01) (2)
- Sectionneur thermopompe (add. E-02) (18)
- Sortie informatique (38)
- Sortie informatique 1070mm (14)
- Sortie téléphone analogique (1)
- Sortie téléphone et informatique (3)
- Séchoir à mains (4)
- Thermostat BT T (15)

Projet
CONSTRUCTION D'UNE
NOUVELLE ÉCOLE
PRIMAIRE DE 16
CLASSES À BELOEIL

2800 RUE SERGE-PÉPIN, BELOEIL, QC
CSS DES PATRIOTES

Plan clé

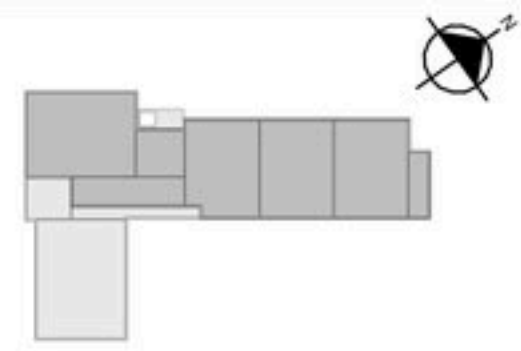

Notes

- Avant l'exécution des travaux, l'entrepreneur doit vérifier les dimensions et les conditions de chantier et avoir immédiatement l'architecte de toutes les situations non conformes aux plans et devis.
- Ne jamais prendre de mesures à l'échelle sur les dessins.
- Ce dessin peut être utilisé pour la construction seulement et seulement s'il a été: "EMIS POUR CONSTRUCTION"

APP. D'OFFRES 2026-01-23
Date



ROCHER ROY
GRAPHIE

gbi

Tetra Tech
Pascal Guilloit


SERVICES

NIVEAU 1

Echelle	Dessiné par	E301_0
Comme indiqué	S. DUBOIS	
Date	Approuvé par	
Date de fin	M.-P. GUILLOT	
Numéro du projet	Numéro du dessin	Révision
104-14-00	E301	0

Notes

- Avant l'exécution des travaux, l'entrepreneur doit vérifier les dimensions et les conditions de chantier et avoir immédiatement l'architecte de toutes les situations non conformes aux plans et devis.
- Ne jamais prendre de mesures à l'échelle sur les dessins.
- Ce dessin peut être utilisé pour la construction seulement et seulement s'il a été "ÉMIS POUR CONSTRUCTION".

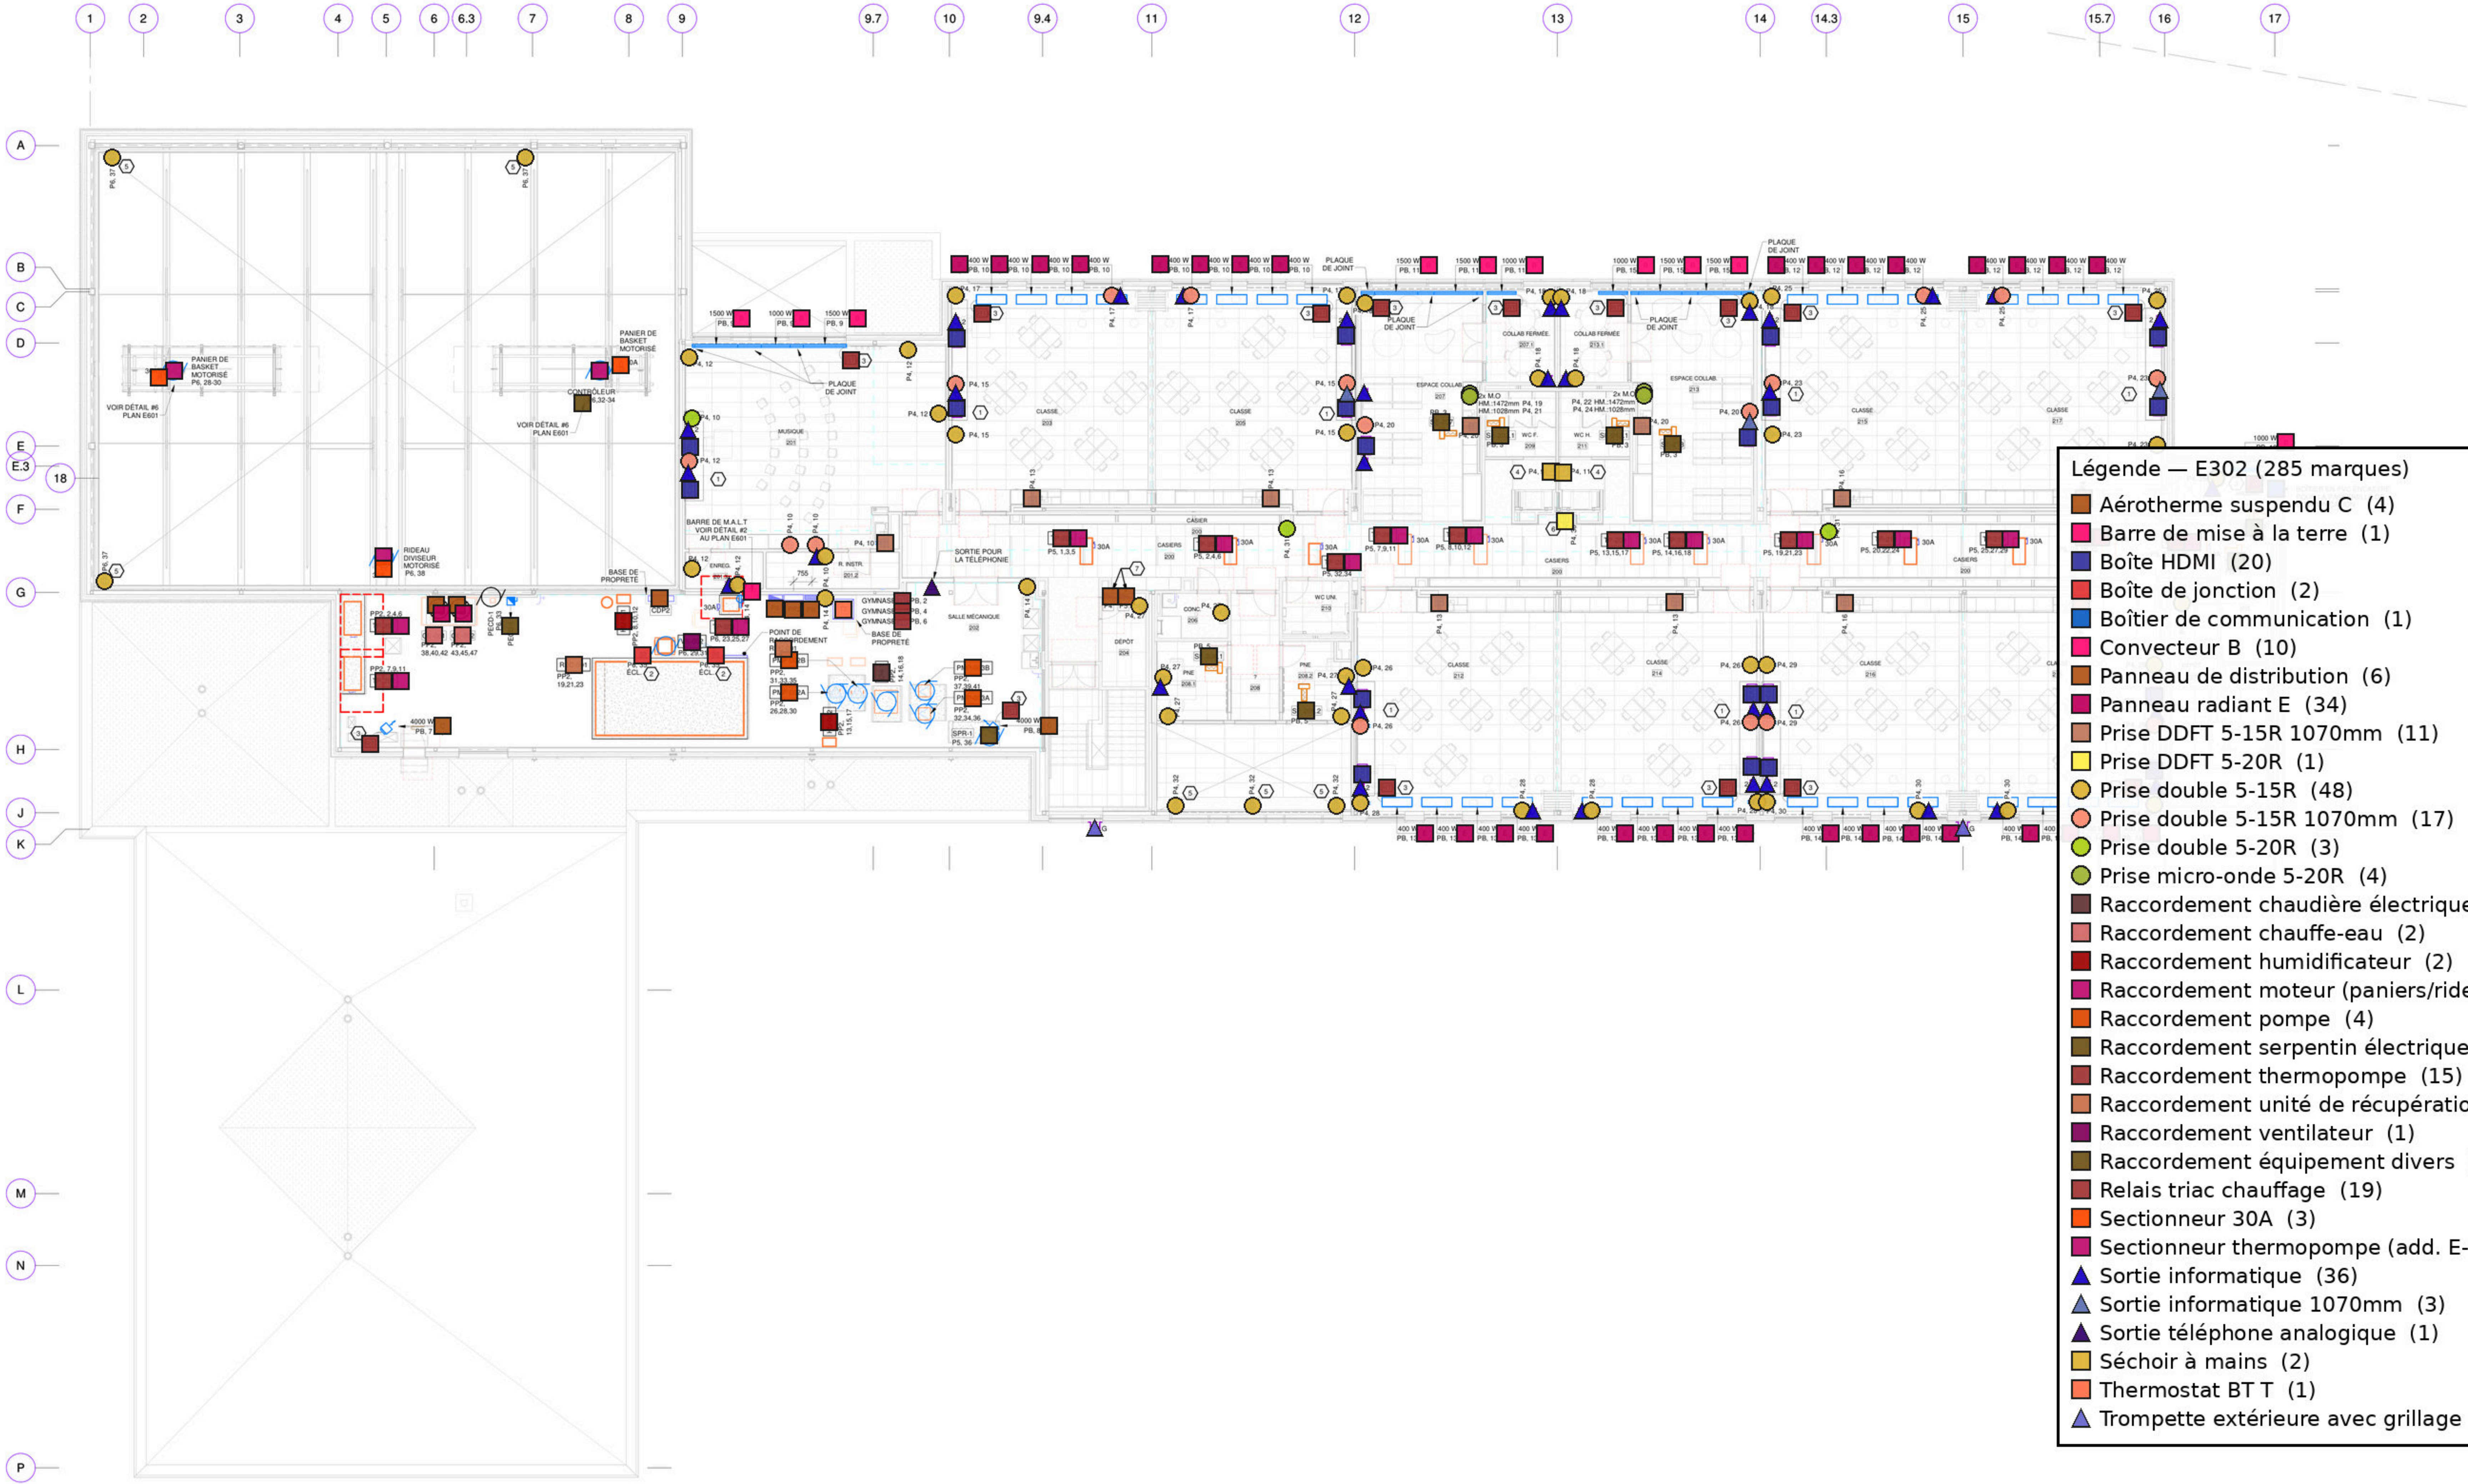

- Légende — E302 (285 marques)**
- Aérotherme suspendu C (4)
 - Barre de mise à la terre (1)
 - Boîte HDMI (20)
 - Boîte de jonction (2)
 - Boîtier de communication (1)
 - Convecteur B (10)
 - Panneau de distribution (6)
 - Panneau radiant E (34)
 - Prise DDFT 5-15R 1070mm (11)
 - Prise DDFT 5-20R (1)
 - Prise double 5-15R (48)
 - Prise double 5-15R 1070mm (17)
 - Prise double 5-20R (3)
 - Prise micro-onde 5-20R (4)
 - Raccordement chaudière électrique (1)
 - Raccordement chauffe-eau (2)
 - Raccordement humidificateur (2)
 - Raccordement moteur (paniers/rideau) (3)
 - Raccordement pompe (4)
 - Raccordement serpentin électrique (8)
 - Raccordement thermopompe (15)
 - Raccordement unité de récupération (2)
 - Raccordement ventilateur (1)
 - Raccordement équipement divers (3)
 - Relais triac chauffage (19)
 - Sectionneur 30A (3)
 - Sectionneur thermopompe (add. E-02) (15)
 - Sortie informatique (36)
 - Sortie informatique 1070mm (3)
 - Sortie téléphone analogique (1)
 - Séchoir à mains (2)
 - Thermostat BT T (1)
 - Trompette extérieure avec grillage (2)

NOTE(S):

- SERVICES DÉDIÉ AU ETI. VOIR DÉTAIL #5 AU PLAN E601.
- L'UNITÉ SERA LIVRÉ EN TROIS MODULES. EFFECTUER LES RACCORDEMENTS 120V POUR L'ÉCLAIRAGE ET PRISE DE COURANT.
- FOURNIR ET INSTALLER UN RELAIS TRIAC TEL QUE STELPRO HRE20C OU ÉQUIVALENT, C/A BOÎTE DE JONCTION DANS L'ENTREPLAFOND ACCESSIBLE LE PLUS PRÈS. RACCORDER CÔTÉ PUISSANCE. VOIR DÉTAIL D'INSTALLATION #11 AU PLAN E601 ET COORDONNER L'EMPLACEMENT EXACT AVEC LA DISCIPLINE D'AUTOMATISATION AVANT LE DÉBUT DES TRAVAUX.
- FOURNIR, INSTALLER ET RACCORDER UN SÈCHE-MAIN TEL QUE COMAC ONE KC-10022004 OU ÉQUIVALENT. COORDONNER AVEC LES PLANS D'ARCHITECTURES POUR LA HAUTEUR DE MONTAGE.
- INSTALLER LA PRISE DE COURANT ENCASTRÉ DANS LE MUR DE BLOC. EMBLEMMENT EXACT À COORDONNER AVEC L'ARCHITECTE.
- COORDONNER L'EMPLACEMENT DE LA PRISE DE COURANT DÉDIÉE À LA FONTAINE RÉFRIGÉRÉE.
- FOURNIR ET INSTALLER UN CONDUIT VIDE DE 50mm C/A CORDE DE TIRAGE ENTRE LE PANNEAU ET L'ENTREPLAFOND POUR FUTURE USAGE.

PEL D'OFFRES 2026-01-23

Date

PROVINCER ROY
PIGRAPHE

gbi

Tetra Tech
Anton Guillot

TETRA TECH Q INC.
2000 RUE JACQUES-CARTE
BUREAU 210
LÉVEL, QUÉBEC, CANADA H1T 2P6
T 418 867-4445


PONTON GUILLLOT
2118 CHEMIN GARDON
SHERBROOKE, QUÉBEC, CANADA
J4H 1G5
T 418 753-1022

Dessin
SERVICES

NIVEAU 2

E302_0

Echelle	Dessiné par
Comme indiqué	S.DUBOIS
Date	Approuvé par
Date de fin	M.-P. GUILLLOT
Numéro du projet	Numéro du dessin
104-14-00	E302
	Révision
	0

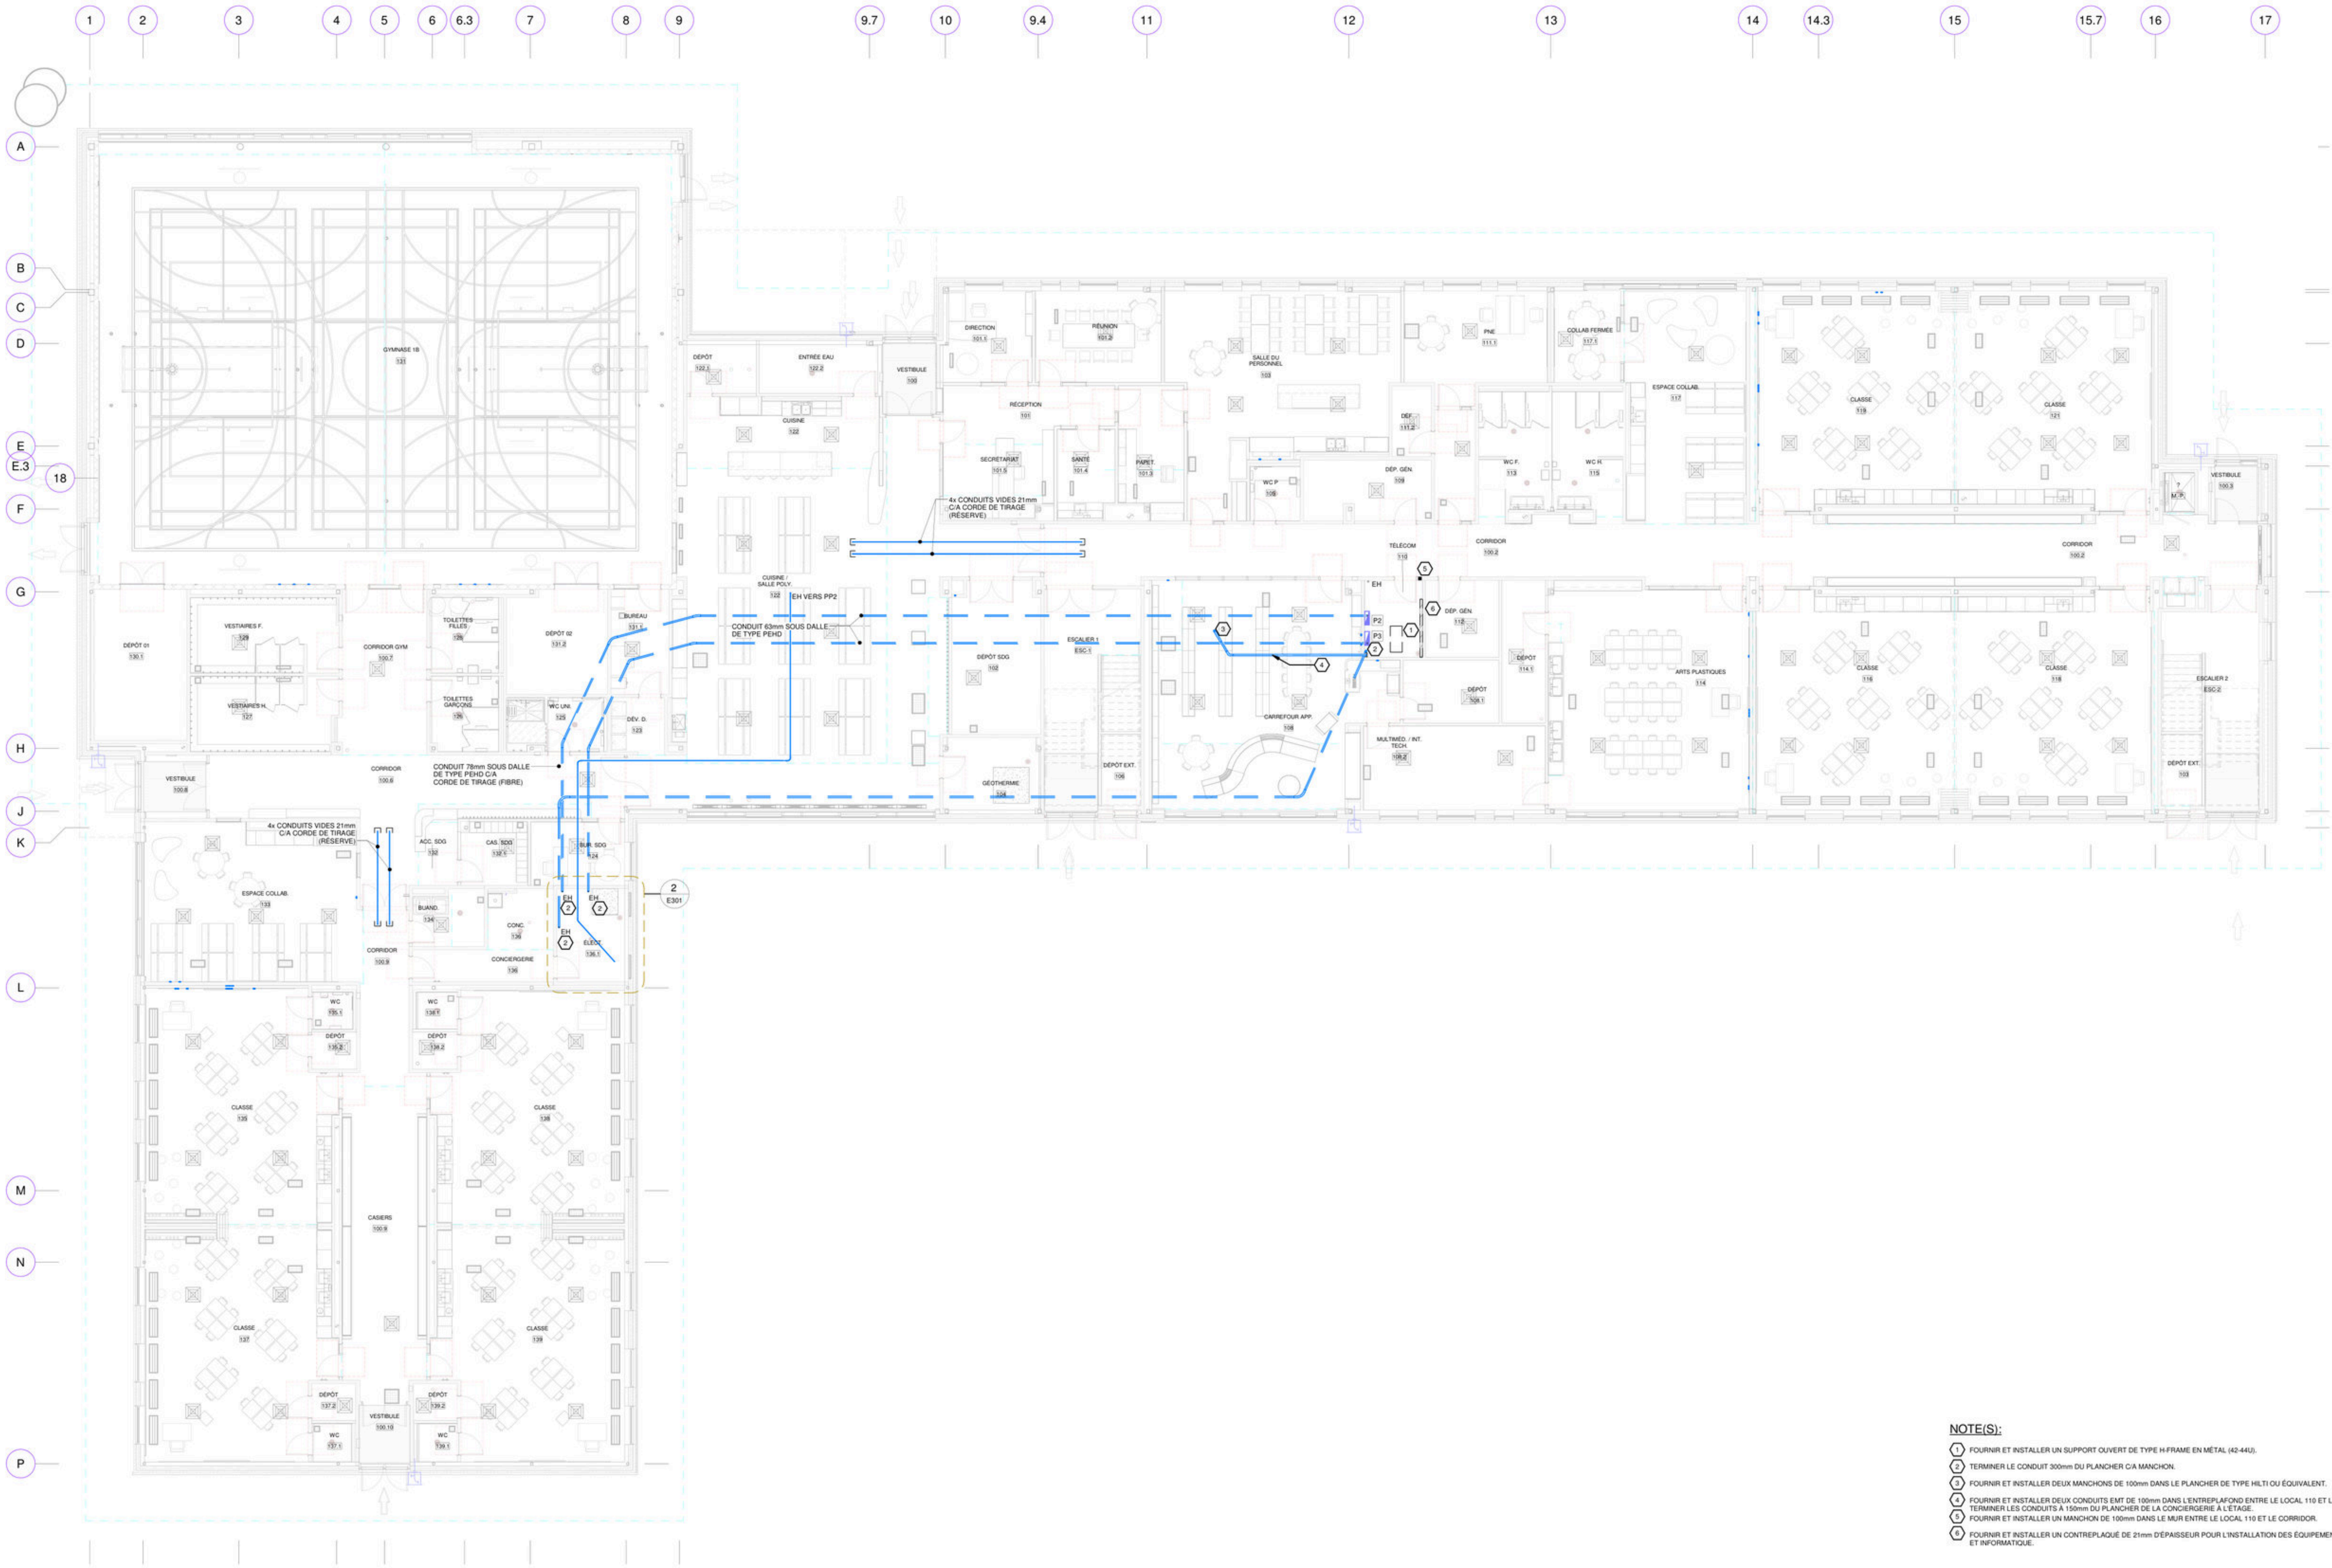


NIVEAU 1 - CHEMINEMENT DES ARTÈRES

1 : 100

- NOTE(S):
- 1 FOURNIR ET INSTALLER UN SUPPORT OUVERT DE TYPE H FRAME EN MÉTAL (42-44U).
 - 2 TERMINER LE CONDUIT 300mm DU PLANCHER GA MANCHON.
 - 3 FOURNIR ET INSTALLER DEUX MANCHONS DE 100mm DANS LE PLANCHER DE TYPE HILTI OU ÉQUIVALENT.
 - 4 FOURNIR ET INSTALLER DEUX CONDUITS SMT DE 100mm DANS L'ENTREPLAFOND ENTRE LE LOCAL 110 ET LE LOCAL 206 À L'ÉTAGE.
 - 5 TERMINER LES CONDUITS À 150mm DU PLANCHER DE LA CONGRÈGÈRE À L'ÉTAGE.
 - 6 FOURNIR ET INSTALLER UN MANCHON DE 100mm DANS LE MUR ENTRE LE LOCAL 110 ET LE CORRIDOR.
 - 7 FOURNIR ET INSTALLER UN CONTREPLAQUE DE 21mm D'ÉPAISSEUR POUR L'INSTALLATION DES ÉQUIPEMENTS D'INTERCOM, INTRUSION ET INFORMATIQUE.

Projet
CONSTRUCTION D'UNE
NOUVELLE ÉCOLE
PRIMAIRE DE 16
CLASSES À BELOEIL

2800 RUE SERGE-PÉPIN, BELOEIL, QC
CSS DES PATRIOTES

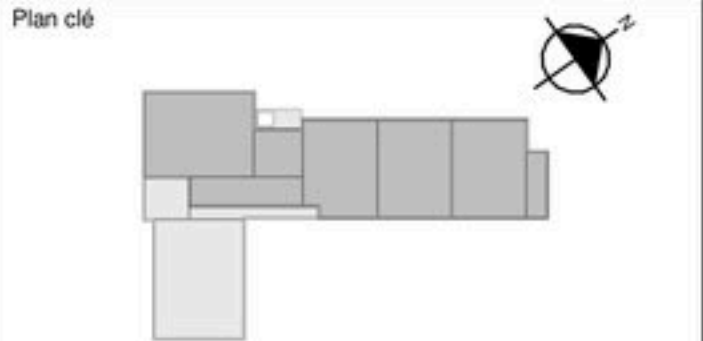

- Notes
- Avant l'exécution des travaux, l'entrepreneur doit vérifier les dimensions et les conditions de chantier et avoir immédiatement l'architecte de toutes les situations non conformes aux plans et devis.
 - Ne jamais prendre de mesures à l'échelle sur les dessins
 - Ce dessin peut être utilisé pour la construction seulement et seulement s'il a été "ÉMIS POUR CONSTRUCTION"

0 APPEL D'OFFRES 2026-01-23

Révision Émis pour Date



Architecture
PROVENCHER ROY
ÉPIGRAPHE

PRO
375, RUE SAINT-JACQUES, BUREAU 700
MONTREAL, QUEBEC, CANADA H2Y1N2

ÉPIGRAPHE
885, RUE RICHELIEU, BUREAU 202
BELOEIL, QUEBEC, CANADA H3A2P5

Experts conseils

Structure

gbi

GBI
1510 RUE DE SÉBASTIEN
L'ARROUAILLÉ, QUEBEC, CANADA J4M 0J7
T 468-675-4225

Mécanique - Électricité - Plomberie

Tetra Tech
Ponton Guillot

TETRA TECH Q INC.
2005, RUE SAINT-JACQUES
BUREAU 210
L'ARROUAILLÉ, QUEBEC, CANADA H2Y 1N2
T 468-667-4445

PONTON GUILLOT
2145, CHENAILLE D'ARROUAILLÉ
L'ARROUAILLÉ, QUEBEC, CANADA
J4M 1G5
T 468-513-1022

Dessin
**CHEMINEMENT DES
ARTÈRES
NIVEAU 1**

E303_0

Echelle Dessiné par

Comme indiqué S.DUBOIS

Date Approuvé par


Date de fin M.-P. GUILLOT

Numéro du projet 104-14-00

Numéro du dessin E303

Révision 0

2025-02-11 11:36:39

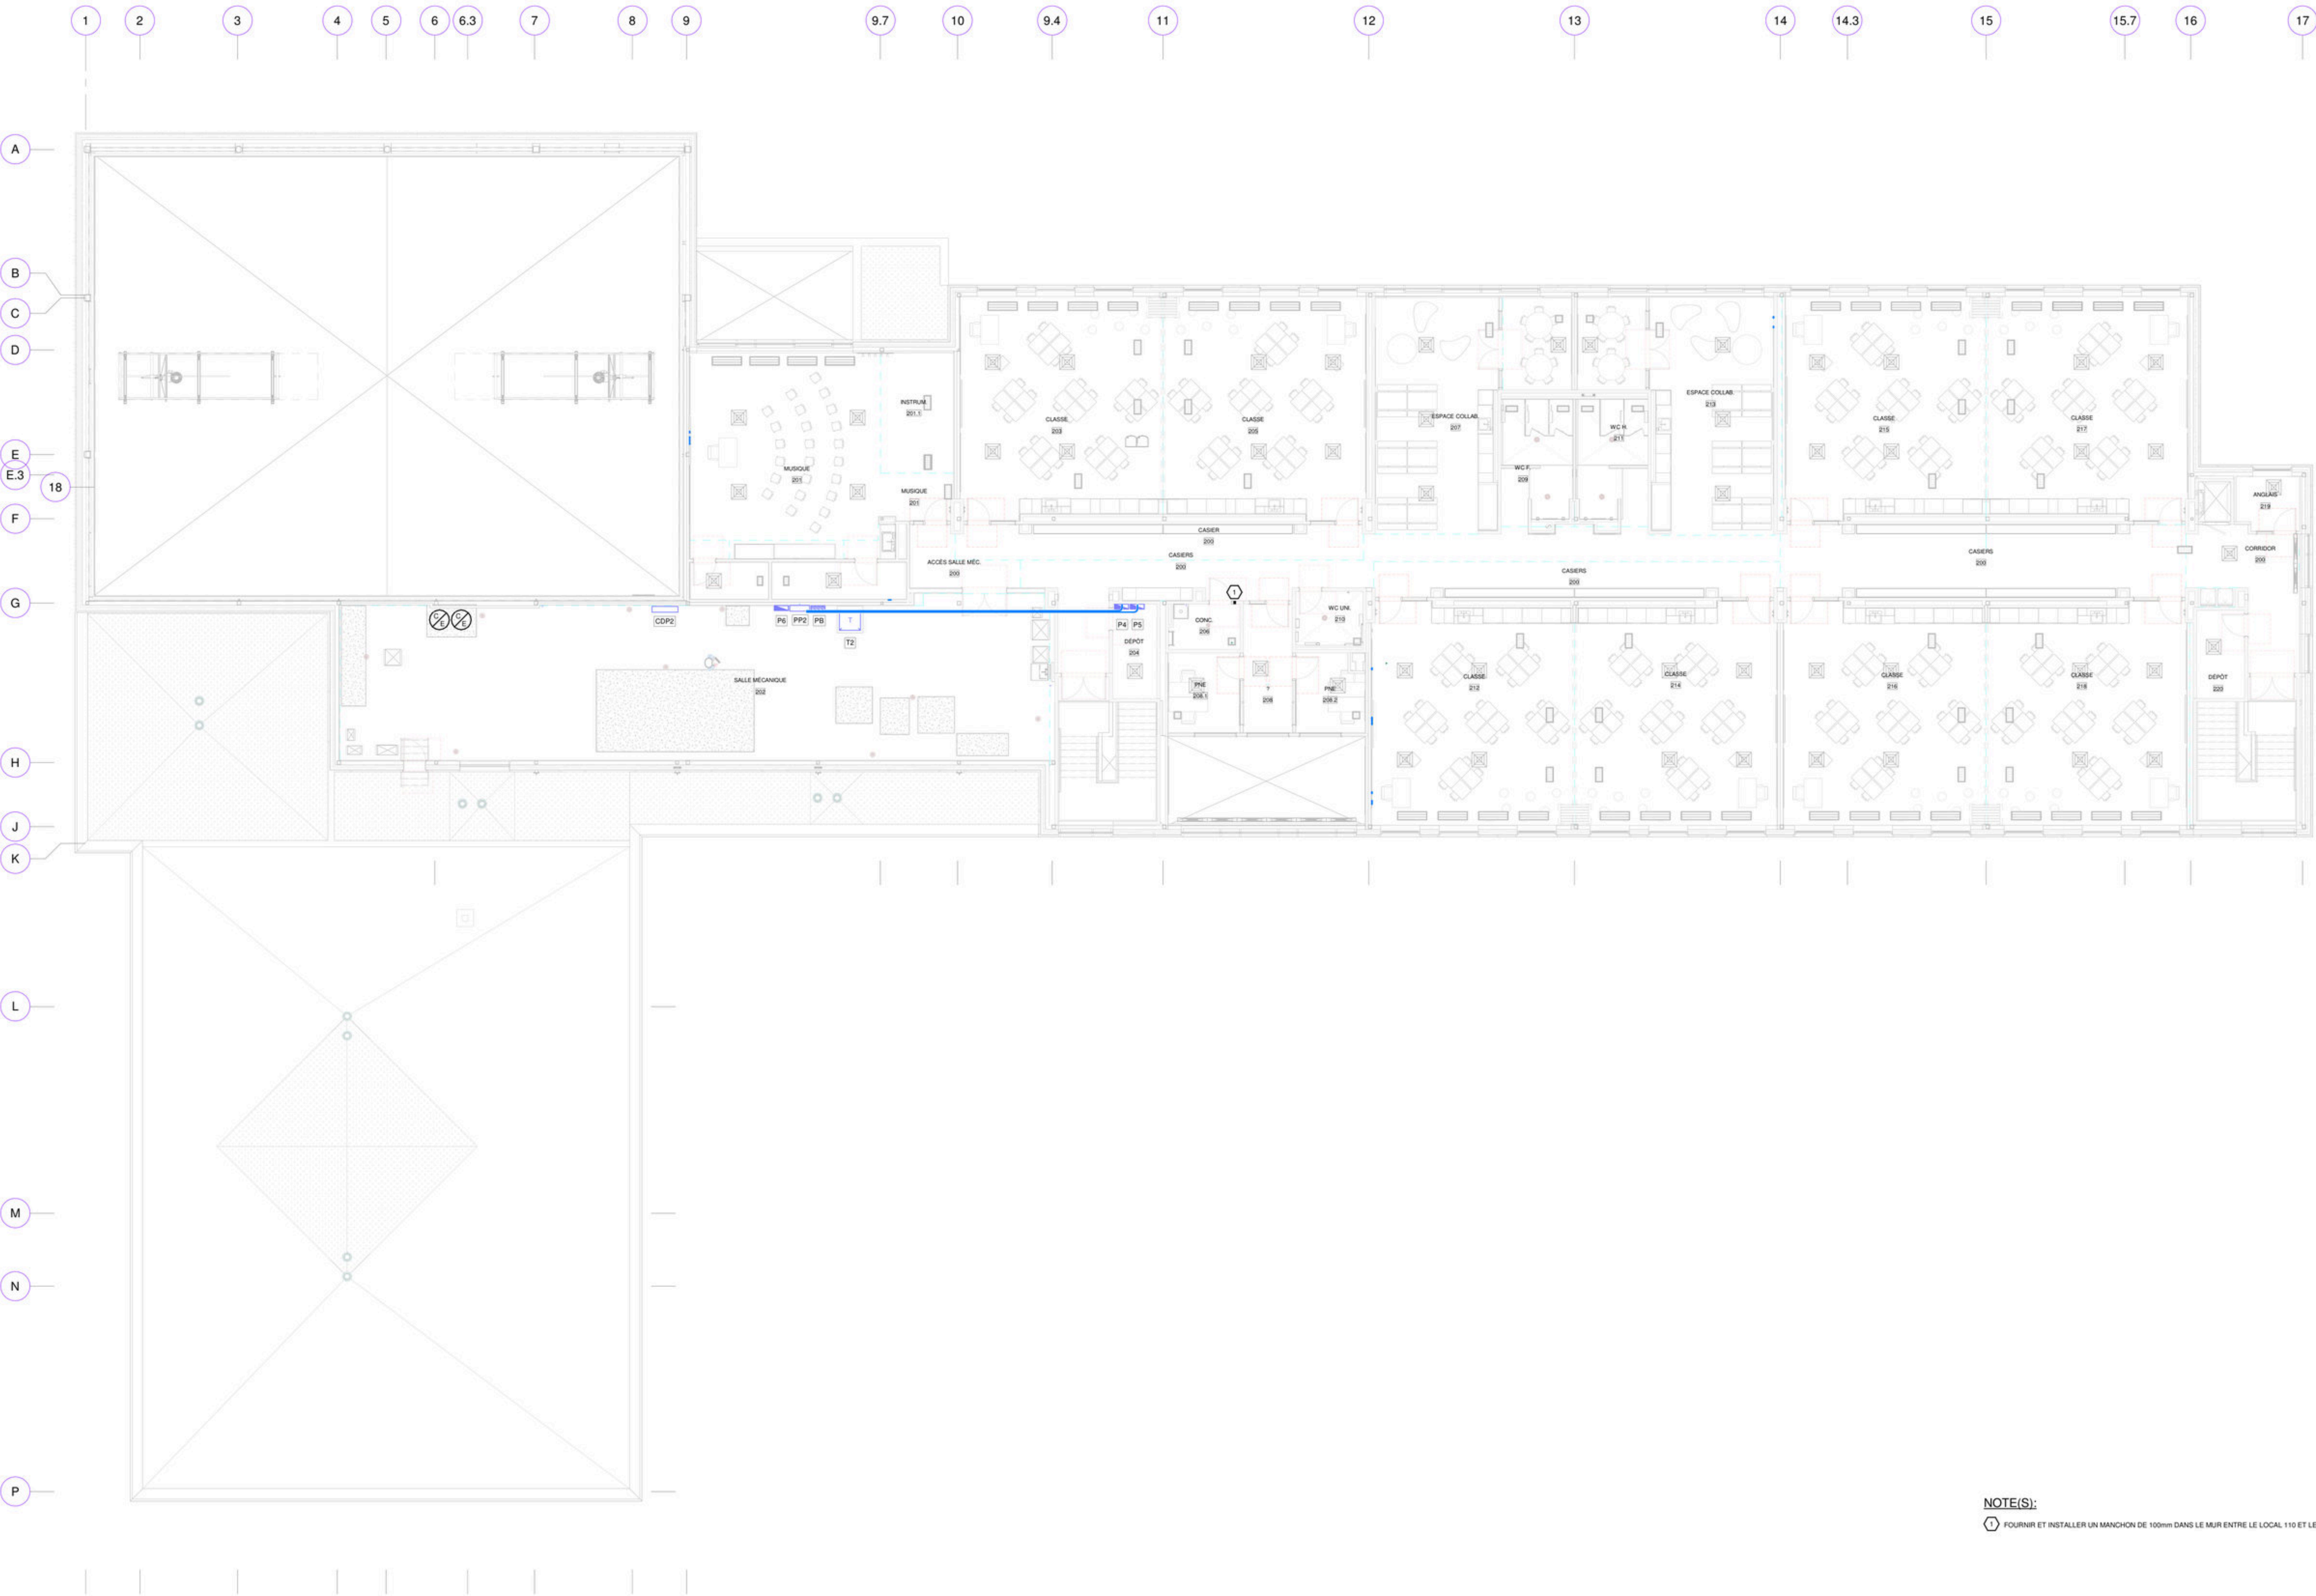

NIVEAU 2 - CHEMINEMENT DES ARTÈRES
1 : 100

NOTE(S):
① FOURNIR ET INSTALLER UN MANCHON DE 100mm DANS LE MUR ENTRE LE LOCAL 110 ET LE CORRIDOR.

Projet

CONSTRUCTION D'UNE NOUVELLE ÉCOLE PRIMAIRE DE 16 CLASSES À BELOEIL

2800 RUE SERGE-PÉPIN, BELOEIL, QC
CSS DES PATRIOTES

Plan clé

Notes

- Avant l'exécution des travaux, l'entrepreneur doit vérifier les dimensions et les conditions de chantier et avoir immédiatement l'architecte de toutes les situations non conformes aux plans et devis.
- Ne jamais prendre de mesures à l'échelle sur les dessins.
- Ce dessin peut être utilisé pour la construction seulement et seulement s'il a été: "EMIS POUR CONSTRUCTION".

0	APPEL D'OFFRES	2026-01-23
Révision	Émis pour	Date
Scrub		

Architecture

PROVENCHER ROY
ÉPIGRAPHE

PRO
275, RUE SAINT-JACQUES, BUREAU 700
MONTREAL, QUEBEC, CANADA H2Y1N2
ÉPIGRAPHE
885, RUE RICHARD, BUREAU 202
BELOEIL, QUEBEC, CANADA H3G1P5

Experts conseils

Structure

GBI
1510 RUE DE SÉBASTIEN
L'ARROCHE, QUEBEC, CANADA J4M 0J7
T 468 675 4225

Mécanique - Électricité - Plomberie

TETRA TECH Q INC.
2005, RUE JACQUES-CARON
BUREAU 210
L'ARROCHE, QUEBEC, CANADA J4M 0J7
T 468 667 4442
PONTON GUILLOT
2105, CHEMIN GARDON
L'ARROCHE, QUEBEC, CANADA
J4M 0J7
T 468 573 1022

Dessin

CHEMINEMENT DES ARTÈRES
NIVEAU 2

E304_0

Echelle	Dessiné par	
Comme indiqué	S.DUBOIS	
Date	Approuvé par	
Date de fin	M.-P. GUILLOT	
Numéro du projet	Numéro du dessin	Révision
104-14-00	E304	0

2025-02-11 11:36:39



NIVEAU 1 - ALARME INCENDIE

1 - 100

ENTRÉES		FONCTIONS AUXILIAIRES						SECTEUR / ZONE
SIGNAL REÇU		SIGNAL TRANSMIS	DÉVERROUILLAGE DES PORTES AVEC VERROUS ÉLECTROMAGNÉTIQUES OU BARRIÈRE MANUELLE	RAPPEL DES ASCENSEURS AU NIVEAU DE SORTIE	FERMETURE DES PORTES COUPE-FEU NORMALEMENT OUVERTES	ARRÊT DES SYSTÈMES DE VENTILATION, HOTTES DE CUISINE, DÉPOSSESSIONNELS, ETC.	AVERTISSEMENT TRANSMIS AU SERVICE D'INCENDIE	
STATION MANUELLE	ACTIVATION D'UN POSTE MANUEL	SIGNAL D'ALARME	OUI, DANS L'ENSEMBLE DU BATIMENT	OUI, POUR L'ENSEMBLE DES ASCENSEURS AU NIVEAU DE SORTIE	OUI, DANS L'ENSEMBLE DU BATIMENT	OUI, DANS L'ENSEMBLE DU BATIMENT	OUI	INDIQUER ZONE
DÉTECTEUR D'INCENDIE (FUMÉE, CHALEUR, ETC.)	DÉTECTEUR DE RAPPEL D'ASCENSEURS	SIGNAL D'ALARME	OUI, DANS L'ENSEMBLE DU BATIMENT	OUI, RAPPEL AUTOMATIQUE DES ASCENSEURS AU NIVEAU DE RAPPEL ALTERNATIF	OUI, DANS L'ENSEMBLE DU BATIMENT	OUI, DANS L'ENSEMBLE DU BATIMENT	OUI	INDIQUER ZONE
	ALLER/REVENIR DANS LE BATIMENT	SIGNAL D'ALARME	OUI, DANS L'ENSEMBLE DU BATIMENT	OUI, RAPPEL AUTOMATIQUE DES ASCENSEURS AU NIVEAU DE RAPPEL	OUI, DANS L'ENSEMBLE DU BATIMENT	OUI, DANS L'ENSEMBLE DU BATIMENT	OUI	INDIQUER ZONE
DÉTECTEURS DU RESEAU DE SECOURS	DÉTECTION DE DÉBIT	SIGNAL D'ALARME	OUI, DANS L'ENSEMBLE DU BATIMENT	OUI, RAPPEL AUTOMATIQUE DES ASCENSEURS AU NIVEAU DE RAPPEL	OUI, DANS L'ENSEMBLE DU BATIMENT	OUI, DANS L'ENSEMBLE DU BATIMENT	OUI	INDIQUER ZONE
	PERTE DE PRESSION OU FERMETURE D'UNE VALVE	SIGNAL SONORE ET TEXTUEL DE SUPERVISION AUX L'ANNONCEUR ET PANNEAUX D'ALARME INCENDIE	NON	NON	NON	NON	OUI	INDIQUER ZONE
MÉTHODE DE CONTOURNEMENT POUR LA MISE HORS TENSION TEMPORAIRE DES CIRCUITS DE SIGNALISATION ET DES RELAIS D'ALARME INCENDIE DES SYSTÈMES DE VENTILATION			SIGNAL SONORE ET TEXTUEL DE SUPERVISION AUX L'ANNONCEUR ET PANNEAUX D'ALARME INCENDIE	NON	NON	NON	NON	INDIQUER CONTOURNEMENT
EN CAS DE DÉTECTEURS CIRCUIT OUVERT, COURT CIRCUIT OU FORTS A LA TERRE			SIGNAL SONORE ET TEXTUEL DE SUPERVISION AUX L'ANNONCEUR ET PANNEAUX D'ALARME INCENDIE	NON	NON	NON	NON	INDIQUER CONTOURNEMENT
OU SYSTÈME D'ALIMENTATION, DES CIRCUITS DE DÉTECTION OU DE SIGNALISATION OU DE TOUT AUTRE COMPOSANTE IMPORTANTE			SIGNAL SONORE ET TEXTUEL DE SUPERVISION AUX L'ANNONCEUR ET PANNEAUX D'ALARME INCENDIE	NON	NON	NON	NON	INDIQUER ZONE

IDENTIFICATION DES REGISTRES
RCFF - REGISTRE COUPE-FEU / FUMÉE
RCFU - REGISTRE COUPE-FUMÉE

Légende — E401_2 (83 marques)

- Détecteur de conduit RCFF/RCFU (5)
- Détecteur de fumée (11)
- Interrupteur de débit ID (2)
- Klaxon (9)
- Klaxon-strobe (8)
- Mini-klaxon M/K (18)
- Module adressable de contrôle RA (7)
- Module de transmission simple MS (2)
- Panneau d'alarme incendie PAI (1)
- Retenue magnétique (8)
- Station manuelle (6)
- Station manuelle c/a garde (2)
- Strobe (4)

NOTE(S):
① FOURNIR ET INSTALLER UN PROTECTEUR EN POLYCARBONATE TEL QUE LEXAN OU ÉQUIVALENT.
② INSTALLER LE RELAIS ADRESSABLE D'ALARME INCENDIE DANS L'ENTREPLAFOND ACCESSIBLE LE PLUS PRÈS POSSIBLE.

Projet

CONSTRUCTION D'UNE NOUVELLE ÉCOLE PRIMAIRE DE 16 CLASSES À BELOEIL

2800 RUE SERGE-PÉPIN, BELOEIL, QC
CSS DES PATRIOTES

Plan clé

Notes

- Avant l'exécution des travaux, l'entrepreneur doit vérifier les dimensions et les conditions de chantier et avoir immédiatement l'architecte de toutes les situations non conformes aux plans et devis.
- Ne jamais prendre de mesures à l'échelle sur les dessins.
- Ce dessin peut être utilisé pour la construction seulement et seulement s'il a été "ÉMIS POUR CONSTRUCTION".

0

APPEL D'OFFRES

2026-01-23

Révision

Émis pour

Date

Scieur

Architecture

PROVENCHER ROY
ÉPIGRAPHE
P.R.A.
374, RUE SAINT-JACQUES, BUREAU 700
MONTREAL, QUEBEC, CANADA H2Y1N1
ÉPIGRAPHE
884, RUE RICHELIEU, BUREAU 202
BELOEIL, QUEBEC, CANADA H3A0P9

Experts conseils

Structure

gbi
1510 RUE DE SÉBASTIEN
L'ARROCHE, QUEBEC, CANADA J4M 0J7
T 468 675 4225

Mécanique - Électricité - Plomberie

TETRA TECH O INC.
2001, RUE SAINT-JACQUES, BUREAU 210
L'ARROCHE, QUEBEC, CANADA J4M 0J7
T 468 675 4445
PONTON GUILLOT
1118, CHENEAUX, QUEBEC, CANADA
J4M 0J7
T 468 113 1022

Dessin

ALARME INCENDIE

NIVEAU 1

E401_0

Echelle

Dessiné par

Comme indiqué

S.DUBOIS

Date

Approuvé par

Date de fin

M.-P. GUILLOT

Numéro du projet

104-14-00

Numéro du dessin

E401

Révision

0

2026-02-11 11:37:15

NIVEAU 2 - ALARME INCENDIE

1 : 100



Légende — E402 (67 marques)

- Détecteur de conduit RCFF/RCFU (20)
- Détecteur de fumée (6)
- Klaxon (4)
- Klaxon-strobe (2)
- Mini-klaxon M/K (11)
- Module adressable de contrôle RA (10)
- Module de transmission double MD (2)
- Retenue magnétique (4)
- Station manuelle (2)
- Strobe (6)

NOTE(S):

1. INSTALLER SELON LA DISPOSITION DES ÉQUIPEMENTS DE LA MÉCANIQUE TOUT EN RESPECTANT LES NORMES. COORDONNER AVANT LE DÉBUT DES TRAVAUX.
2. INSTALLER LE RELAIS ADRESSABLE D'ALARME INCENDIE DANS L'ENTREPLAFOND ACCESSIBLE LE PLUS PRÈS POSSIBLE.
3. INSTALLER LE RELAIS DE PUISSANCE DANS UN BOÎTIER AU PLAFOND. LE RELAIS DE PUISSANCE DOIT ÊTRE INSTALLÉ À CETTE ENDOIT AFIN DE RESPECTER LA DISTANCE DE 18 MÈTRES DES DÉTECTEURS DE FUMÉE.

Projet

CONSTRUCTION D'UNE NOUVELLE ÉCOLE PRIMAIRE DE 16 CLASSES À BELOEIL

2800 RUE SERGE-PÉPIN, BELOEIL, QC
CSS DES PATRIOTES

Plan clé

Notes

- Avant l'exécution des travaux, l'entrepreneur doit vérifier les dimensions et les conditions de chantier et avoir immédiatement l'architecte de toutes les situations non conformes aux plans et devis.
- Ne jamais prendre de mesures à l'échelle sur les dessins.
- Ce dessin peut être utilisé pour la construction seulement et seulement s'il a été "ÉMIS POUR CONSTRUCTION".

0

APPEL D'OFFRES

2026-01-23

Révision

Émis pour

Date

Scieur

Architecture

PROVENCHER ROY
ÉPIGRAPHE
PRO
275, RUE SAINT-JACQUES, BUREAU 700
MONTREAL, QUEBEC, CANADA H2Y1N9
ÉPIGRAPHE
885, RUE RICHELIEU, BUREAU 202
BELOEIL, QUEBEC, CANADA H3B4P9

Experts conseils

Structure

GBI
1510 RUE DE SÉBASTIEN
L'ARROUAILLÉ, QUÉBEC, CANADA J4M 0J7
T 468-675-4225

Mécanique - Électricité - Plomberie

TETRA TECH Q INC.
2005, RUE JACQUES-CARTEUR
BUREAU 210
L'ARROUAILLÉ, QUÉBEC, CANADA J4M 0J7
T 468-667-4442
PONTON GUILLOT
2105, CHENEAUX, QUÉBEC, CANADA
J4M 1G5
T 468-573-1022

Dessin

ALARME INCENDIE
NIVEAU 2

E402_0

Echelle

Dessiné par

Comme indiqué

S.DUBOIS

Date

Approuvé par

Date de fin

M.-P. GUILLOT

Numéro du projet

104-14-00

Numéro du dessin

E402


Révision

0



Notes

- Avant l'exécution des travaux, l'entrepreneur doit vérifier les dimensions et les conditions de chantier et avoir immédiatement l'architecte de toutes les situations non conformes aux plans et devis.
- Ne jamais prendre de mesures à l'échelle sur les dessins.
- Ce dessin peut être utilisé pour la construction seulement et seulement s'il a été "EMIS POUR CONSTRUCTION".

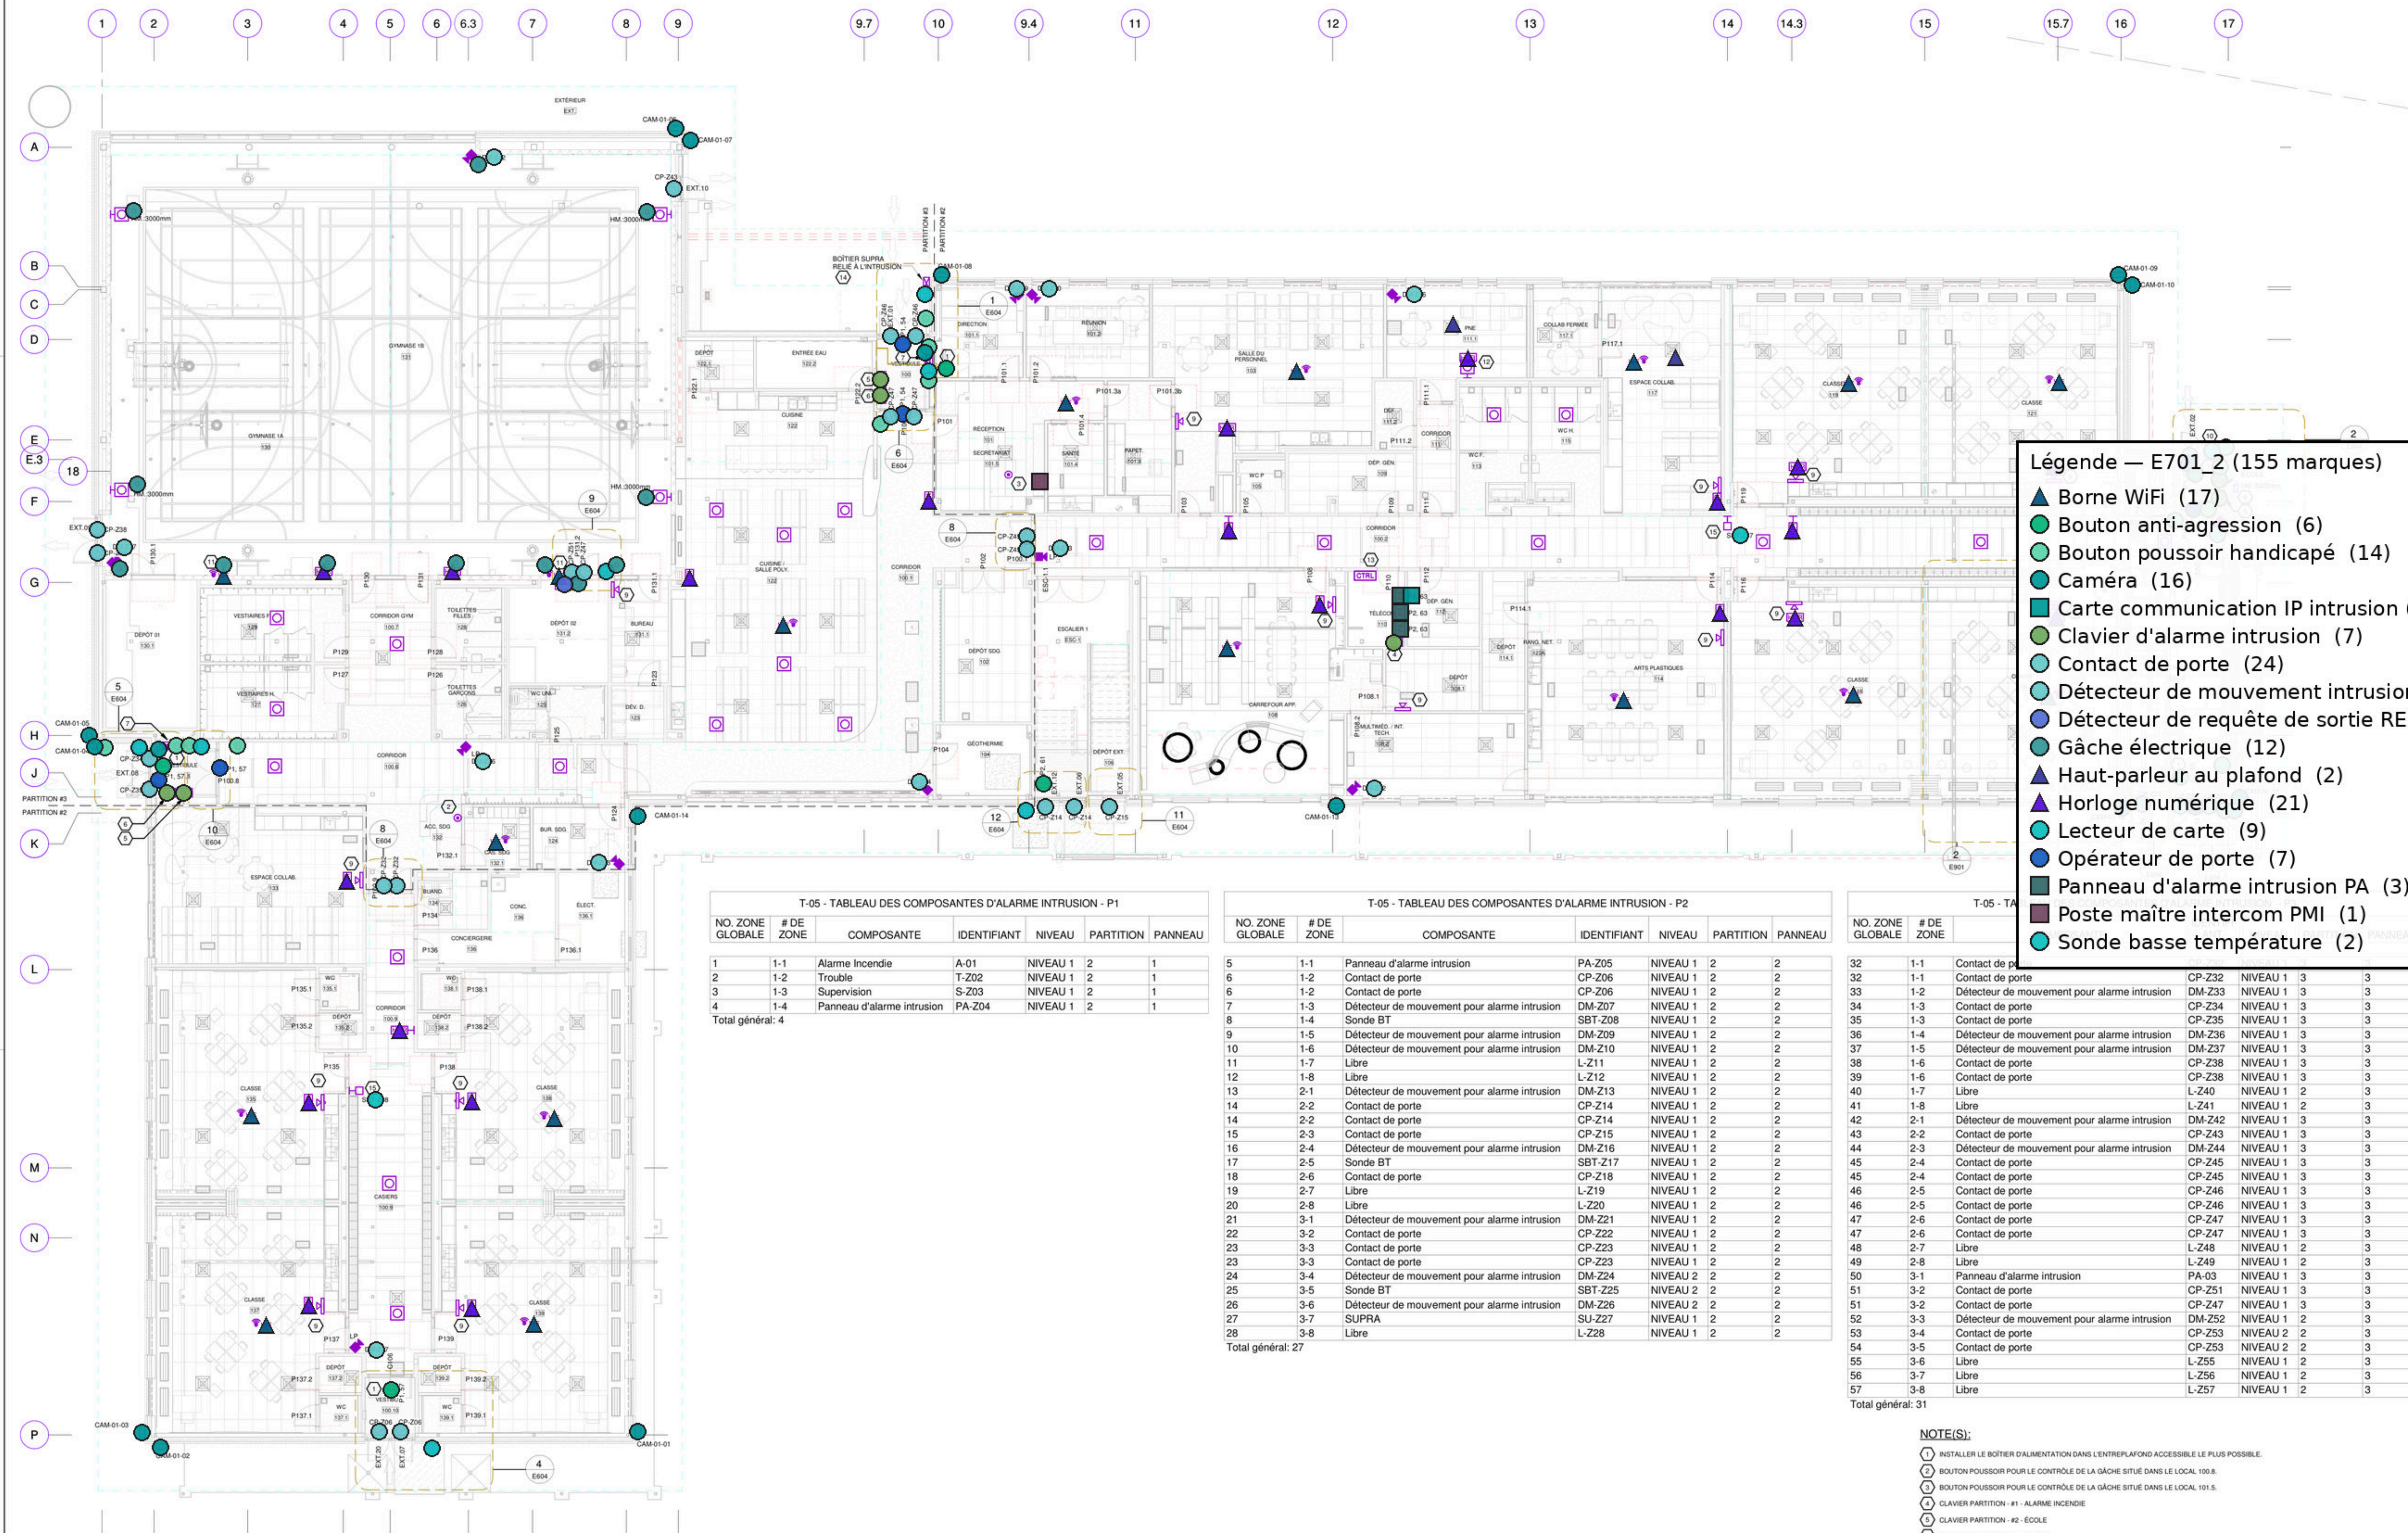

Légende — E701_2 (155 marques)

- ▲ Borne WiFi (17)
- Bouton anti-agression (6)
- Bouton poussoir handicapé (14)
- Caméra (16)
- Carte communication IP intrusion (add. E-01) (1)
- Clavier d'alarme intrusion (7)
- Contact de porte (24)
- Détecteur de mouvement intrusion (12)
- Détecteur de requête de sortie REX (1)
- Gâche électrique (12)
- ▲ Haut-parleur au plafond (2)
- ▲ Horloge numérique (21)
- Lecteur de carte (9)
- Opérateur de porte (7)
- Panneau d'alarme intrusion PA (3)
- Poste maître intercom PMI (1)
- Sonde basse température (2)

T-05 - TABLEAU DES COMPOSANTES D'ALARME INTRUSION - P1

NO. ZONE GLOBALE	# DE ZONE	COMPOSANTE	IDENTIFIANT	NIVEAU	PARTITION	PANNEAU
1	1-1	Alarme Incendie	A-01	NIVEAU 1	2	1
2	1-2	Trouble	T-Z02	NIVEAU 1	2	1
3	1-3	Supervision	S-Z03	NIVEAU 1	2	1
4	1-4	Panneau d'alarme intrusion	PA-Z04	NIVEAU 1	2	1
Total général: 4						

T-05 - TABLEAU DES COMPOSANTES D'ALARME INTRUSION - P2

NO. ZONE GLOBALE	# DE ZONE	COMPOSANTE	IDENTIFIANT	NIVEAU	PARTITION	PANNEAU
5	1-1	Panneau d'alarme intrusion	PA-Z05	NIVEAU 1	2	2
6	1-2	Contact de porte	CP-Z06	NIVEAU 1	2	2
6	1-2	Contact de porte	CP-Z06	NIVEAU 1	2	2
7	1-3	Détecteur de mouvement pour alarme intrusion	DM-Z07	NIVEAU 1	2	2
8	1-4	Sonde BT	SBT-Z08	NIVEAU 1	2	2
9	1-5	Détecteur de mouvement pour alarme intrusion	DM-Z09	NIVEAU 1	2	2
10	1-6	Détecteur de mouvement pour alarme intrusion	DM-Z10	NIVEAU 1	2	2
11	1-7	Libre	L-Z11	NIVEAU 1	2	2
12	1-8	Libre	L-Z12	NIVEAU 1	2	2
13	2-1	Détecteur de mouvement pour alarme intrusion	DM-Z13	NIVEAU 1	2	2
14	2-2	Contact de porte	CP-Z14	NIVEAU 1	2	2
15	2-3	Contact de porte	CP-Z15	NIVEAU 1	2	2
16	2-4	Détecteur de mouvement pour alarme intrusion	DM-Z16	NIVEAU 1	2	2
17	2-5	Sonde BT	SBT-Z17	NIVEAU 1	2	2
18	2-6	Contact de porte	CP-Z18	NIVEAU 1	2	2
19	2-7	Libre	L-Z19	NIVEAU 1	2	2
20	2-8	Libre	L-Z20	NIVEAU 1	2	2
21	3-1	Détecteur de mouvement pour alarme intrusion	DM-Z21	NIVEAU 1	2	2
22	3-2	Contact de porte	CP-Z22	NIVEAU 1	2	2
23	3-3	Contact de porte	CP-Z23	NIVEAU 1	2	2
23	3-3	Contact de porte	CP-Z23	NIVEAU 1	2	2
24	3-4	Détecteur de mouvement pour alarme intrusion	DM-Z24	NIVEAU 2	2	2
25	3-5	Sonde BT	SBT-Z25	NIVEAU 2	2	2
26	3-6	Détecteur de mouvement pour alarme intrusion	DM-Z26	NIVEAU 2	2	2
27	3-7	SUPRA	SU-Z27	NIVEAU 1	2	2
28	3-8	Libre	L-Z28	NIVEAU 1	2	2
Total général: 27						

T-05 - TABLEAU DES COMPOSANTES D'ALARME INTRUSION - P3

NO. ZONE GLOBALE	# DE ZONE	COMPOSANTE	IDENTIFIANT	NIVEAU	PARTITION	PANNEAU
32	1-1	Contact de porte	CP-Z32	NIVEAU 1	3	3
32	1-1	Contact de porte	CP-Z32	NIVEAU 1	3	3
33	1-2	Détecteur de mouvement pour alarme intrusion	DM-Z33	NIVEAU 1	3	3
34	1-3	Contact de porte	CP-Z34	NIVEAU 1	3	3
35	1-3	Contact de porte	CP-Z35	NIVEAU 1	3	3
36	1-4	Détecteur de mouvement pour alarme intrusion	DM-Z36	NIVEAU 1	3	3
37	1-5	Détecteur de mouvement pour alarme intrusion	DM-Z37	NIVEAU 1	3	3
38	1-6	Contact de porte	CP-Z38	NIVEAU 1	3	3
39	1-6	Contact de porte	CP-Z38	NIVEAU 1	3	3
40	1-7	Libre	L-Z40	NIVEAU 1	2	3
41	1-8	Libre	L-Z41	NIVEAU 1	2	3
42	2-1	Détecteur de mouvement pour alarme intrusion	DM-Z42	NIVEAU 1	3	3
43	2-2	Contact de porte	CP-Z43	NIVEAU 1	3	3
44	2-3	Détecteur de mouvement pour alarme intrusion	DM-Z44	NIVEAU 1	3	3
45	2-4	Contact de porte	CP-Z45	NIVEAU 1	3	3
46	2-5	Contact de porte	CP-Z46	NIVEAU 1	3	3
47	2-6	Contact de porte	CP-Z47	NIVEAU 1	3	3
48	2-7	Libre	L-Z48	NIVEAU 1	2	3
49	2-8	Libre	L-Z49	NIVEAU 1	2	3
50	3-1	Panneau d'alarme intrusion	PA-03	NIVEAU 1	3	3
51	3-2	Contact de porte	CP-Z51	NIVEAU 1	3	3
51	3-2	Contact de porte	CP-Z47	NIVEAU 1	3	3
52	3-3	Détecteur de mouvement pour alarme intrusion	DM-Z52	NIVEAU 1	2	3
53	3-4	Contact de porte	CP-Z53	NIVEAU 2	2	3
54	3-5	Contact de porte	CP-Z53	NIVEAU 2	2	3
55	3-6	Libre	L-Z55	NIVEAU 1	2	3
56	3-7	Libre	L-Z56	NIVEAU 1	2	3
57	3-8	Libre	L-Z57	NIVEAU 1	2	3
Total général: 31						

NOTE(S):

- INSTALLER LE BÔÎTER D'ALIMENTATION DANS L'ENTREPLAFOND ACCESSIBLE LE PLUS POSSIBLE.
- BOUTON POUSSOIR POUR LE CONTRÔLE DE LA GÂCHE SITUÉ DANS LE LOCAL 100.8.
- BOUTON POUSSOIR POUR LE CONTRÔLE DE LA GÂCHE SITUÉ DANS LE LOCAL 101.5.
- CLAVIER PARTITION - #1 - ALARME INCENDIE
- CLAVIER PARTITION - #2 - ÉCOLE
- CLAVIER PARTITION - #3 - LOISIRS
- INSTALLER SELON LA HAUTEUR RECOMMANDÉE PAR LE MANUFACTURIER.
- FOURNIR ET INSTALLER UN BÔÎTER EN PVC ÉTANCHE 100x100x100mm NEMA AU MUR C/À PRISE DE COURANT 15A 120V/1PH. CETTE BÔÎTE SERT À ALIMENTER ET PROTÉGER LA PASSERELLE DE COMMUNICATION POUR LA BORNE DE RECHARGE ÉLECTRIQUE (FUTURE).
- COORDONNER LA HAUTEUR DE MONTAGE AVANT LE DÉBUT DES TRAVAUX.
- LECTEUR DE CARTE À INSTALLER À L'INTÉRIEUR SUR LE MENUIS C/À BÔÎTER TEL QUE HAMMOND #1591ASBK
- BORNE WIFI FIXE AU MUR À UNE HAUTEUR D'ENVIRON 3 MÈTRES.
- HAUT-PARLEUR À INSTALLER À 150mm DU PLAFOND TEL QUE TOA #BS-678 OU ÉQUIVALENT.
- INSTALLER LES CONTRÔLEURS SUPERPOSÉS SUR LE MUR.
- FOURNIR, INSTALLER ET RACCORDER LE BÔÎTER TEL QUE SUPRA KEYSAFE #57001267
- FOURNIR, INSTALLER ET RACCORDER UNE SONDE BASSE TEMPÉRATURE AU PANNEAU ALARME INTRUSION. CETTE SONDE DOIT ÊTRE INSTALLÉE À 300mm DU PLAFOND.

NIVEAU 1 - PLF AUXILIAIRE
1 : 100

2026-01-23
Date



Architecture
**PROVENCHER ROY
ÉPIGRAPHE**

PRO
375, RUE SAINT-JACQUES, BUREAU 700
MONTREAL, QUEBEC, CANADA H3T 1V1
ÉPIGRAPHE
300, RUE RICHELIEU, BUREAU 202
BELOEIL, QUEBEC, CANADA J3G 0P9

Experts conseils

Structure
gbi

GBR
1510 RUE DE SÉBASTIEN
L'ARROUAY, QUEBEC, CANADA J9V 0J7
T 468-675-4225

Mécanique - Électricité - Plomberie

**Tetra Tech
Ponton Guillet**

TETRA TECH INC.
300, RUE SAINT-JACQUES
BUREAU 210
L'ARROUAY, QUEBEC, CANADA J9V 0J7
T 468-675-4445



PONTON GUILLOT
310, CHENEAUX
L'ARROUAY, QUEBEC, CANADA
J9V 0J7
T 468-513-1022

Dessin
SERVICES AUXILIAIRES

Echelle
Comme indiqué
Date
Date de fin
Numéro du projet
104-14-00

Dessiné par
S.DUBOIS
Approuvé par
M.-P. GUILLOT
Numéro du dessin
E701

Revision
0

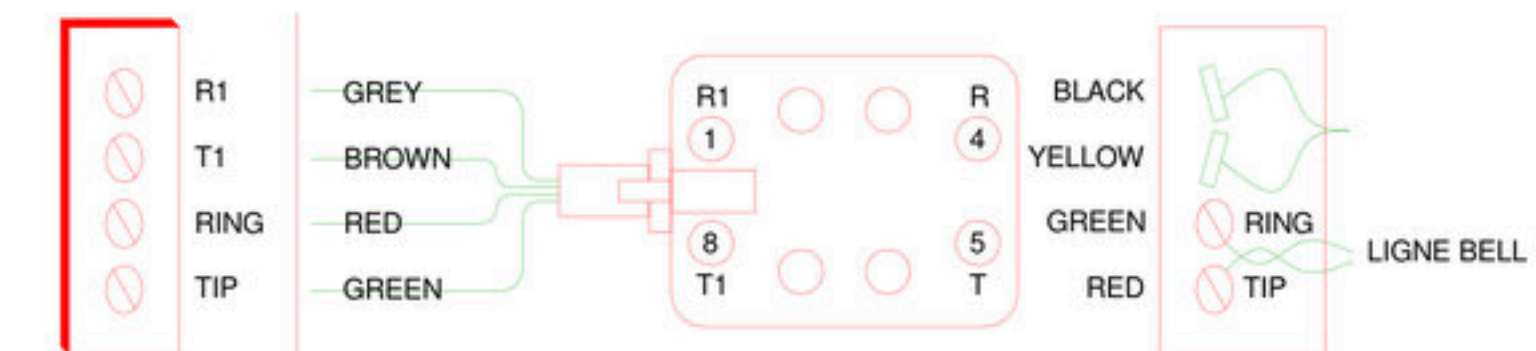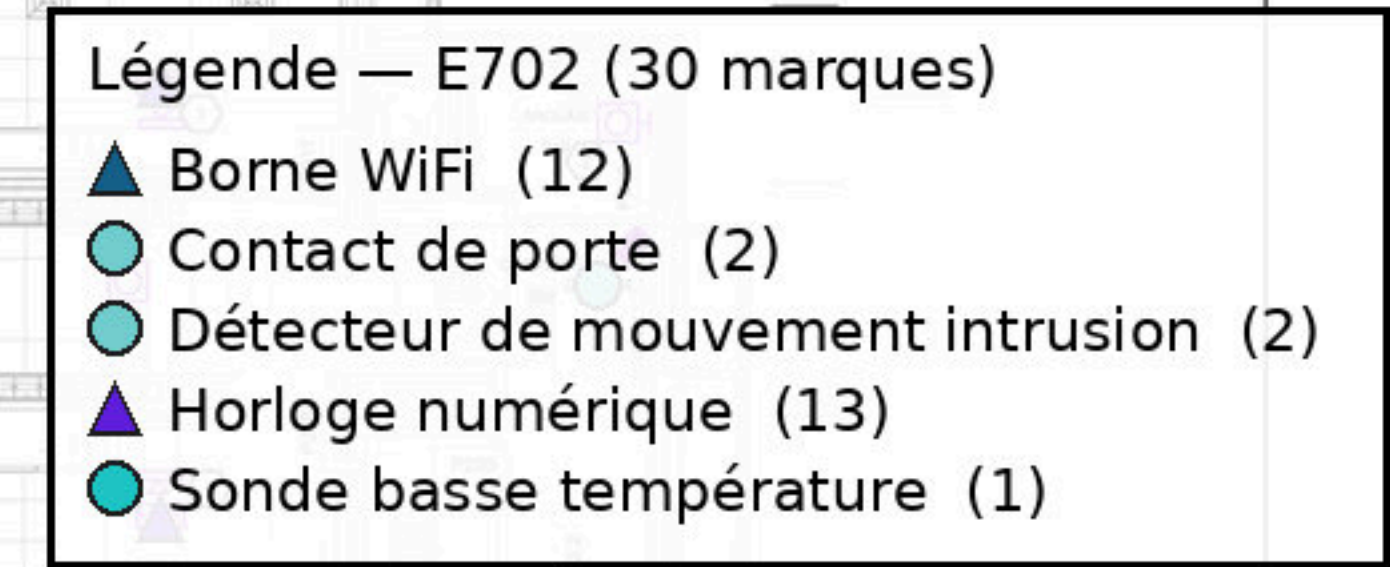

DÉTAIL DE RACCORDEMENT DU MODULE CA38A
1:1

NOTE(S):

1. COORDONNER LA HAUTEUR DE MONTAGE AVANT LE DÉBUT DES TRAVAUX.
2. HAUT-PARLEUR À INSTALLER À 150mm DU PLAFOND TEL QUE TOA #BS-678 OU ÉQUIVALENT.
3. FOURNIR, INSTALLER ET RACCORDER UNE SONDE BASSE TEMPÉRATURE AU PANNEAU ALARME INTRUSION. CETTE SONDE DOIT ÊTRE INSTALLÉE À 300mm DU PLAFOND.