


CE PLAN EST LA PROPRIÉTÉ DES PROFESSIONNELS CI-DESSOUS MENTIONNÉS. IL EST PRÊTÉ À CONDITION QU'IL NE SOIT PAS UTILISÉ À L'ENCONTRE DE LEUR INTÉRÊT NI REPRODUIT EN TOUT OU EN PARTIE ET QU'IL LEUR SOIT REMIS SUR DEMANDE.

AVANT DE PROCÉDER À L'INSTALLATION DES COMPOSANTES ET DES SYSTÈMES ELECTROMECANQUES, L'ENTREPRENEUR DOIT CONSULTER LES DERNIERS PLANS EN ARCHITECTURE. TOUTES LES MESURES DOIVENT ÊTRE PRISES À PARTIR DES DERNIERS PLANS D'ARCHITECTURE.

CE PROJET DOIT SERVIR À LA CONSTRUCTION QUE SI LA MENTION "POUR CONSTRUCTION" FIGURE DANS LA LISTE DES REVISIONS CI-DESSOUS ET QU'IL SOIT DÔMENT SIGNÉ PAR L'INGÉNIEUR.

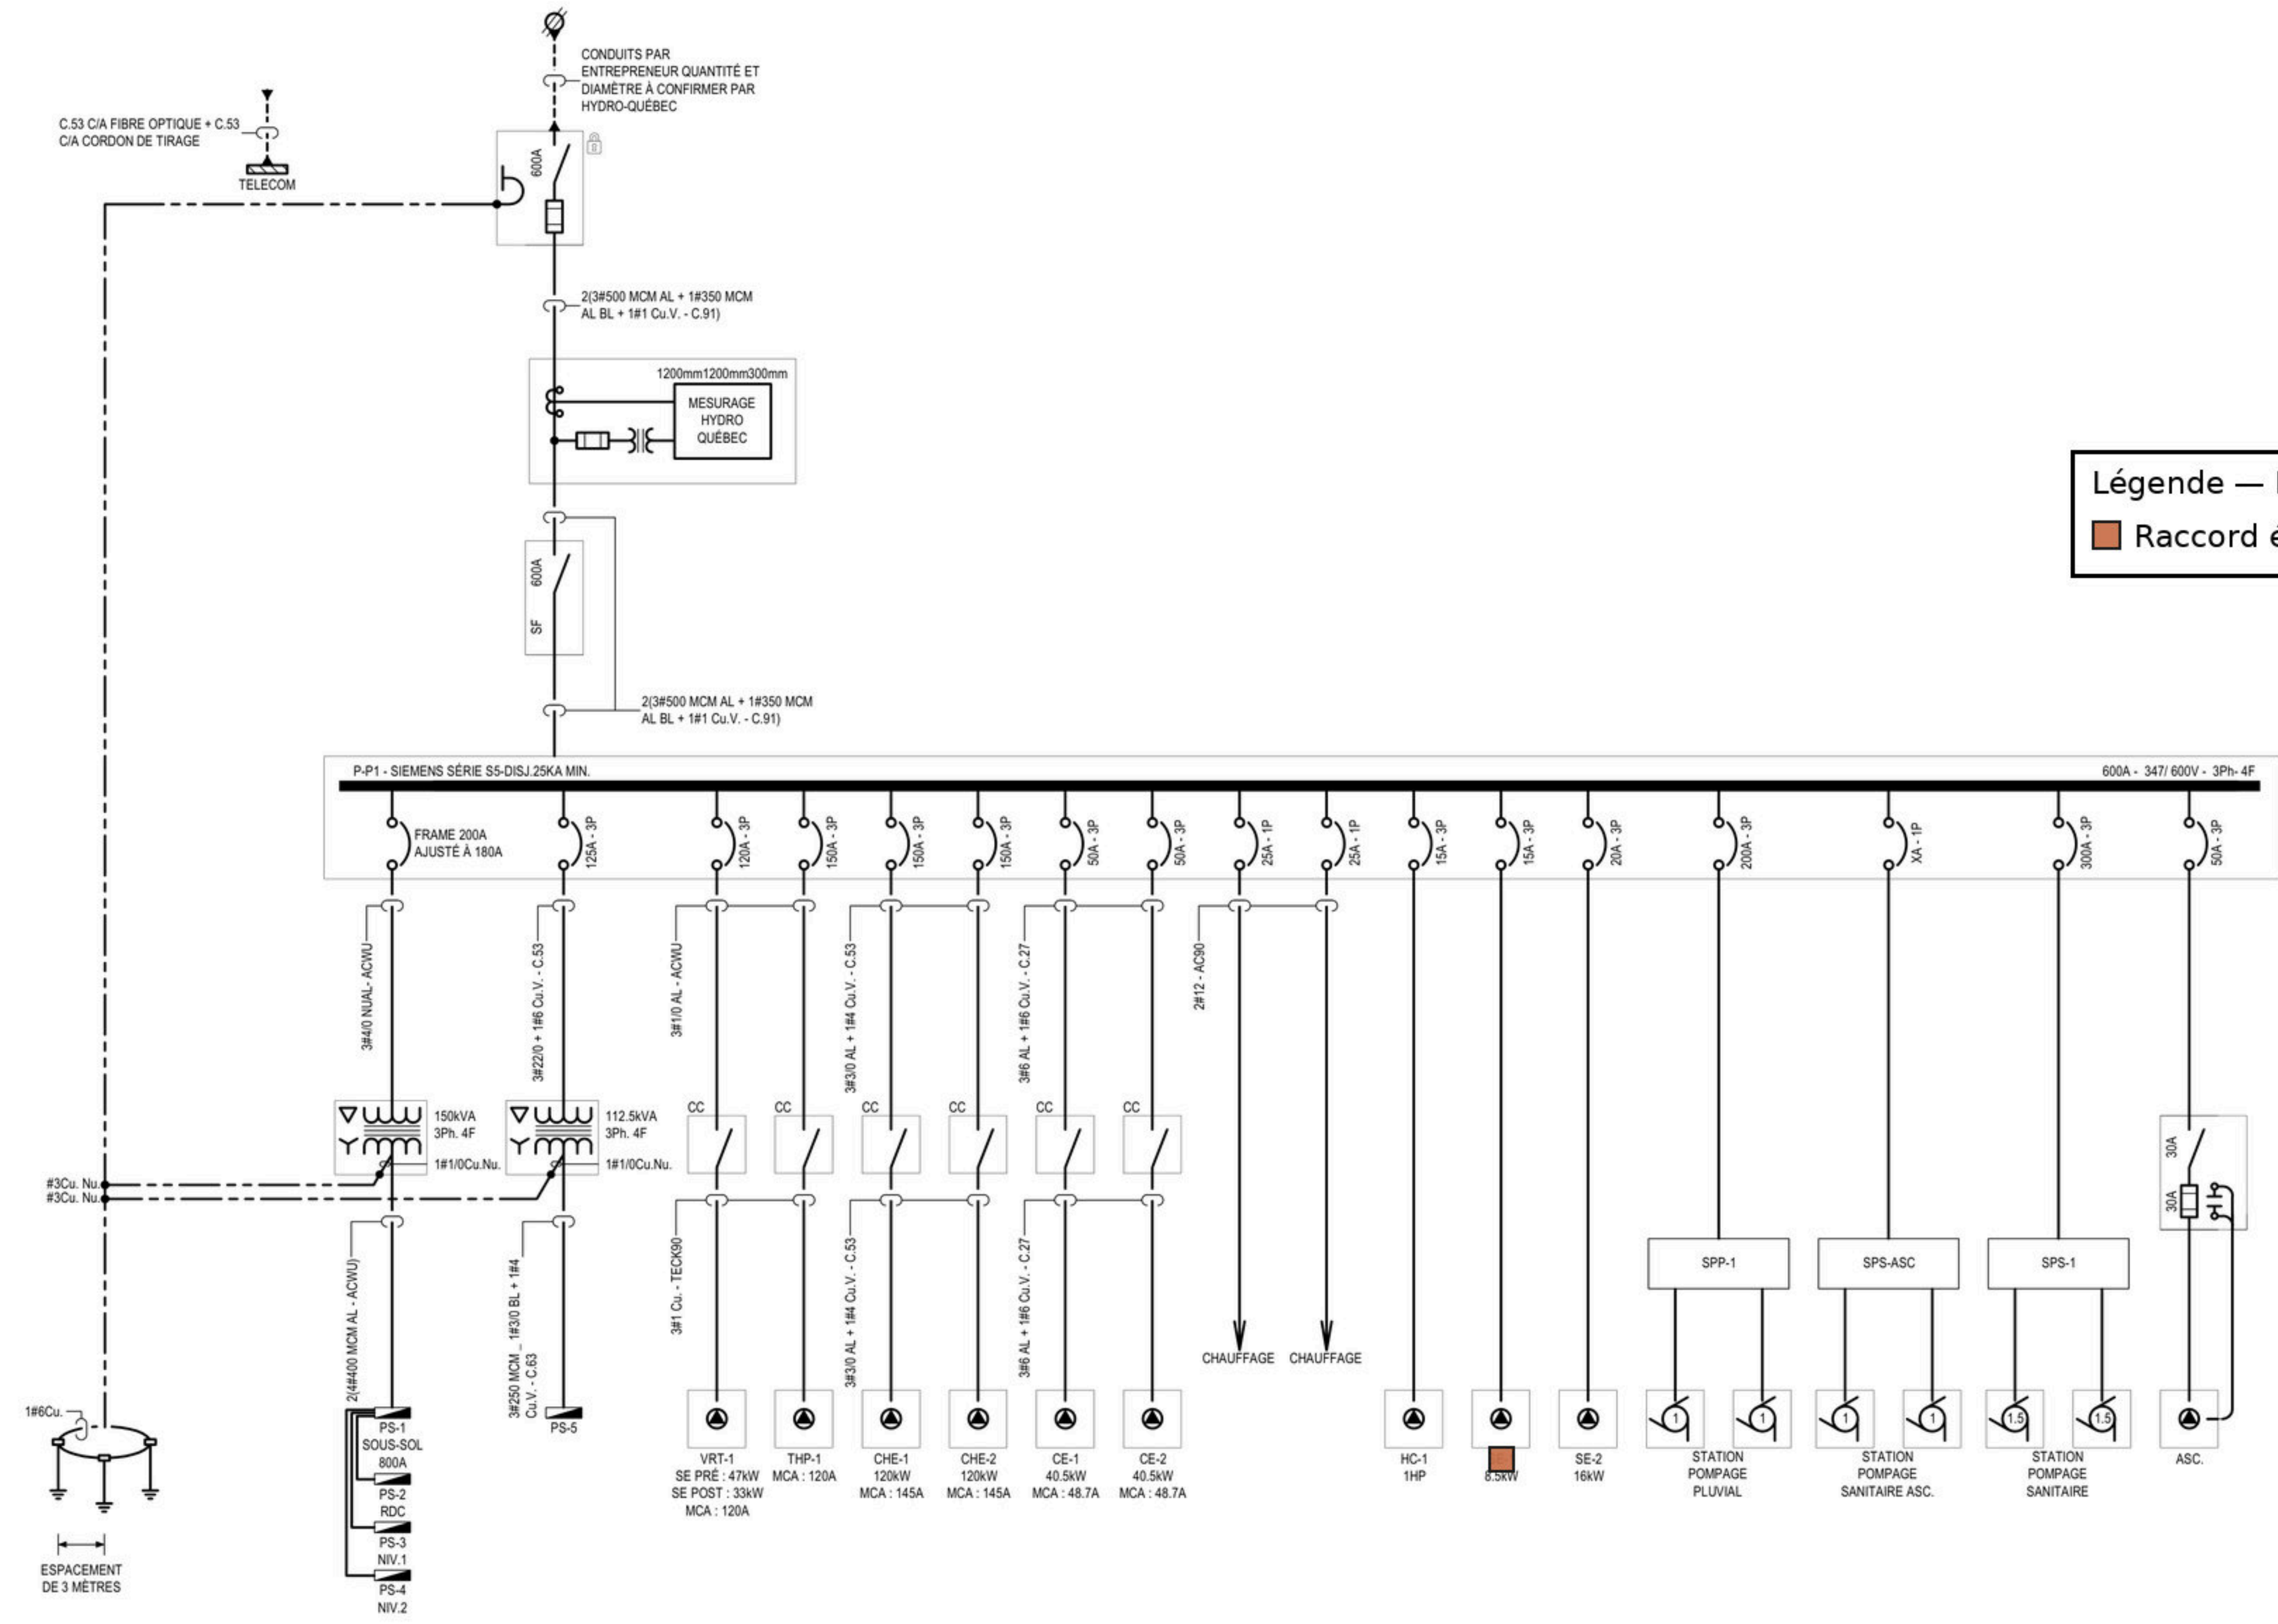

Légende — E200 (1 marques)

Raccord équipement — cédule (1)

ARTELIA

STRUCTURE

POINCARÉ
INGÉNIERIE

ARCHITECTURE

fabg
Architectes

MÉCANIQUE / ÉLECTRIQUE

akonovia

1	SOUSSION	2026-08-17
A	PERMIS	2026-05-08
NO.	Émis pour	Date

TITRE DU PLAN:

SCHÉMA UNIFILAIRE
DISTRIBUTION ÉLECTRIQUE

PRÉPARE PAR:
M. BATISTA, ing.
J. GILBERT, tech.

DESSINÉ PAR:
T. CANDU

DATE:
AVRIL 2026

DOSSIER:
25-0810-QC

DISCIPLINE:
ÉLECTRICITÉ

SCEAU



PLAN:
E200

TITRE DU PLAN:	
SOUS-SOL - ÉCLAIRAGE	
PRÉPARE PAR:	SCEAU
M. BATISTA, ing. J. GILBERT, tech.	
DESSINÉ PAR:	
T. CANDU	
DATE:	
AVRIL 2026	
DOSSIER:	PLAN:
25-0810-QC	E400
DISCIPLINE	
ÉLECTRICITÉ	



CE PLAN EST LA PROPRIÉTÉ DES PROFESSIONNELS CI-DESSOUS MENTIONNÉS. IL EST PRÊTÉ À CONDITION QU'IL NE SOIT PAS UTILISÉ À L'ENCONTRE DE LEUR INTÉRÊT NI REPRODUIT EN TOUT OU EN PARTIE ET QU'IL LEUR SOIT REMIS SUR DEMANDE.

AVANT DE PROCÉDER À L'INSTALLATION DES COMPOSANTES ET DES SYSTÈMES ÉLECTROMÉCANIQUES, L'ENTREPRENEUR DOIT CONSULTER LES DERNIERS PLANS ÉMIS D'ARCHITECTURE. TOUTES LES MESURES DOIVENT ÊTRE PRISES À PARTIR DES DERNIERS PLANS D'ARCHITECTURE.

CE PROJET DOIT SERVIR À LA CONSTRUCTION QUE SI LA MENTION "POUR CONSTRUCTION" FIGURE DANS LA LISTE DES RÉVISIONS CI-DESSOUS ET QU'IL SOIT DÔMENT SIGNÉ PAR L'INGÉNIEUR.



- Légende — E401 (248 marques)
- Accumulateur 18W + enseigne (2)
 - Accumulateur 36W (2)
 - Accumulateur 36W + enseigne (3)
 - Bouton-poussoir B (17)
 - Détecteur inoccupation Do (29)
 - Détecteur occupation Di (14)
 - ◆ Enseigne de sortie (10)
 - Interrupteur (1)
 - Luminaire DR2 (1)
 - Luminaire DR5 (11)
 - Luminaire DR51 (2)
 - Luminaire DR52 (2)
 - Luminaire DS0 (50)
 - Luminaire DS1 (78)
 - Luminaire DS2 (2)
 - Luminaire DW4 (5)
 - Luminaire DW42 (1)
 - Luminaire extérieur — à classer (1)
 - Luminaire mural DMW1 (5)
 - Luminaire ovale — à classer (2)
 - ▲ Phare double (7)
 - ▲ Phare simple PH1 (3)

1	SOUSSION	2026-08-17
A	PERMIS	2026-05-08
NO.	Émis pour	Date

TITRE DU PLAN: REZ DE CHAUSSEE - ÉCLAIRAGE	
PRÉPARÉ PAR: M. BATISTA, ing. J. GILBERT, tech.	SCEAU 
DESSINÉ PAR: T. CANDU	
DATE: AVRIL 2026	PLAN: E401
DOSSIER: 25-0810-QC	
DISCIPLINE: ÉLECTRICITÉ	



- 
STRUCTURE
- 
CHIMIE
- 
CANIQUE / ÉLECTRIQUE
- 

[illegible]

TITRE DU PLAN:	
NIVEAU 1 - ÉCLAIRAGE	
PRÉPARÉ PAR:	SCEAU
M. BATISTA, ing. J. GILBERT, tech.	
DESSINÉ PAR:	
T. CANDU	
DATE:	
AVRIL 2026	
DOSSIER:	
25-0810-QC	
DISCIPLINE:	
ÉLECTRICITÉ	
PLAN:	
E402	

1	SOUSSION	2026-08-17
A	PERMIS	2026-05-08
NO.	Émis pour	Date

TITRE DU PLAN:	
NIVEAU 2 - ÉCLAIRAGE	
PRÉPARÉ PAR:	SCEAU
M. BATISTA, ing.	
J. GILBERT, tech.	
DESSINÉ PAR:	
T. CANDU	
DATE:	PLAN:
AVRIL 2026	E403
DOSSIER:	
25-0810-QC	
DISCIPLINE:	ÉLECTRICITÉ
ÉLECTRICITÉ	

- Légende — E403 (161 marques)
- Accumulateur 36W (1)

Accumulateur 36W + enseigne (4)

Bouton-poussoir B (9)

Cercle barré fléché — à classer (3)

Détecteur inoccupation Do (13)

Détecteur occupation Di (10)

Enseigne de sortie (5)

Interrupteur (2)

Luminaire DR2 (1)

Luminaire DR5 (7)

Luminaire DR51 (2)

Luminaire DR52 (2)

Luminaire DS0 (26)


Luminaire DS1 (63)

Luminaire DS4 (2)

Luminaire mural DMW1 (5)

Phare double (5)

Phare simple PH1 (1)

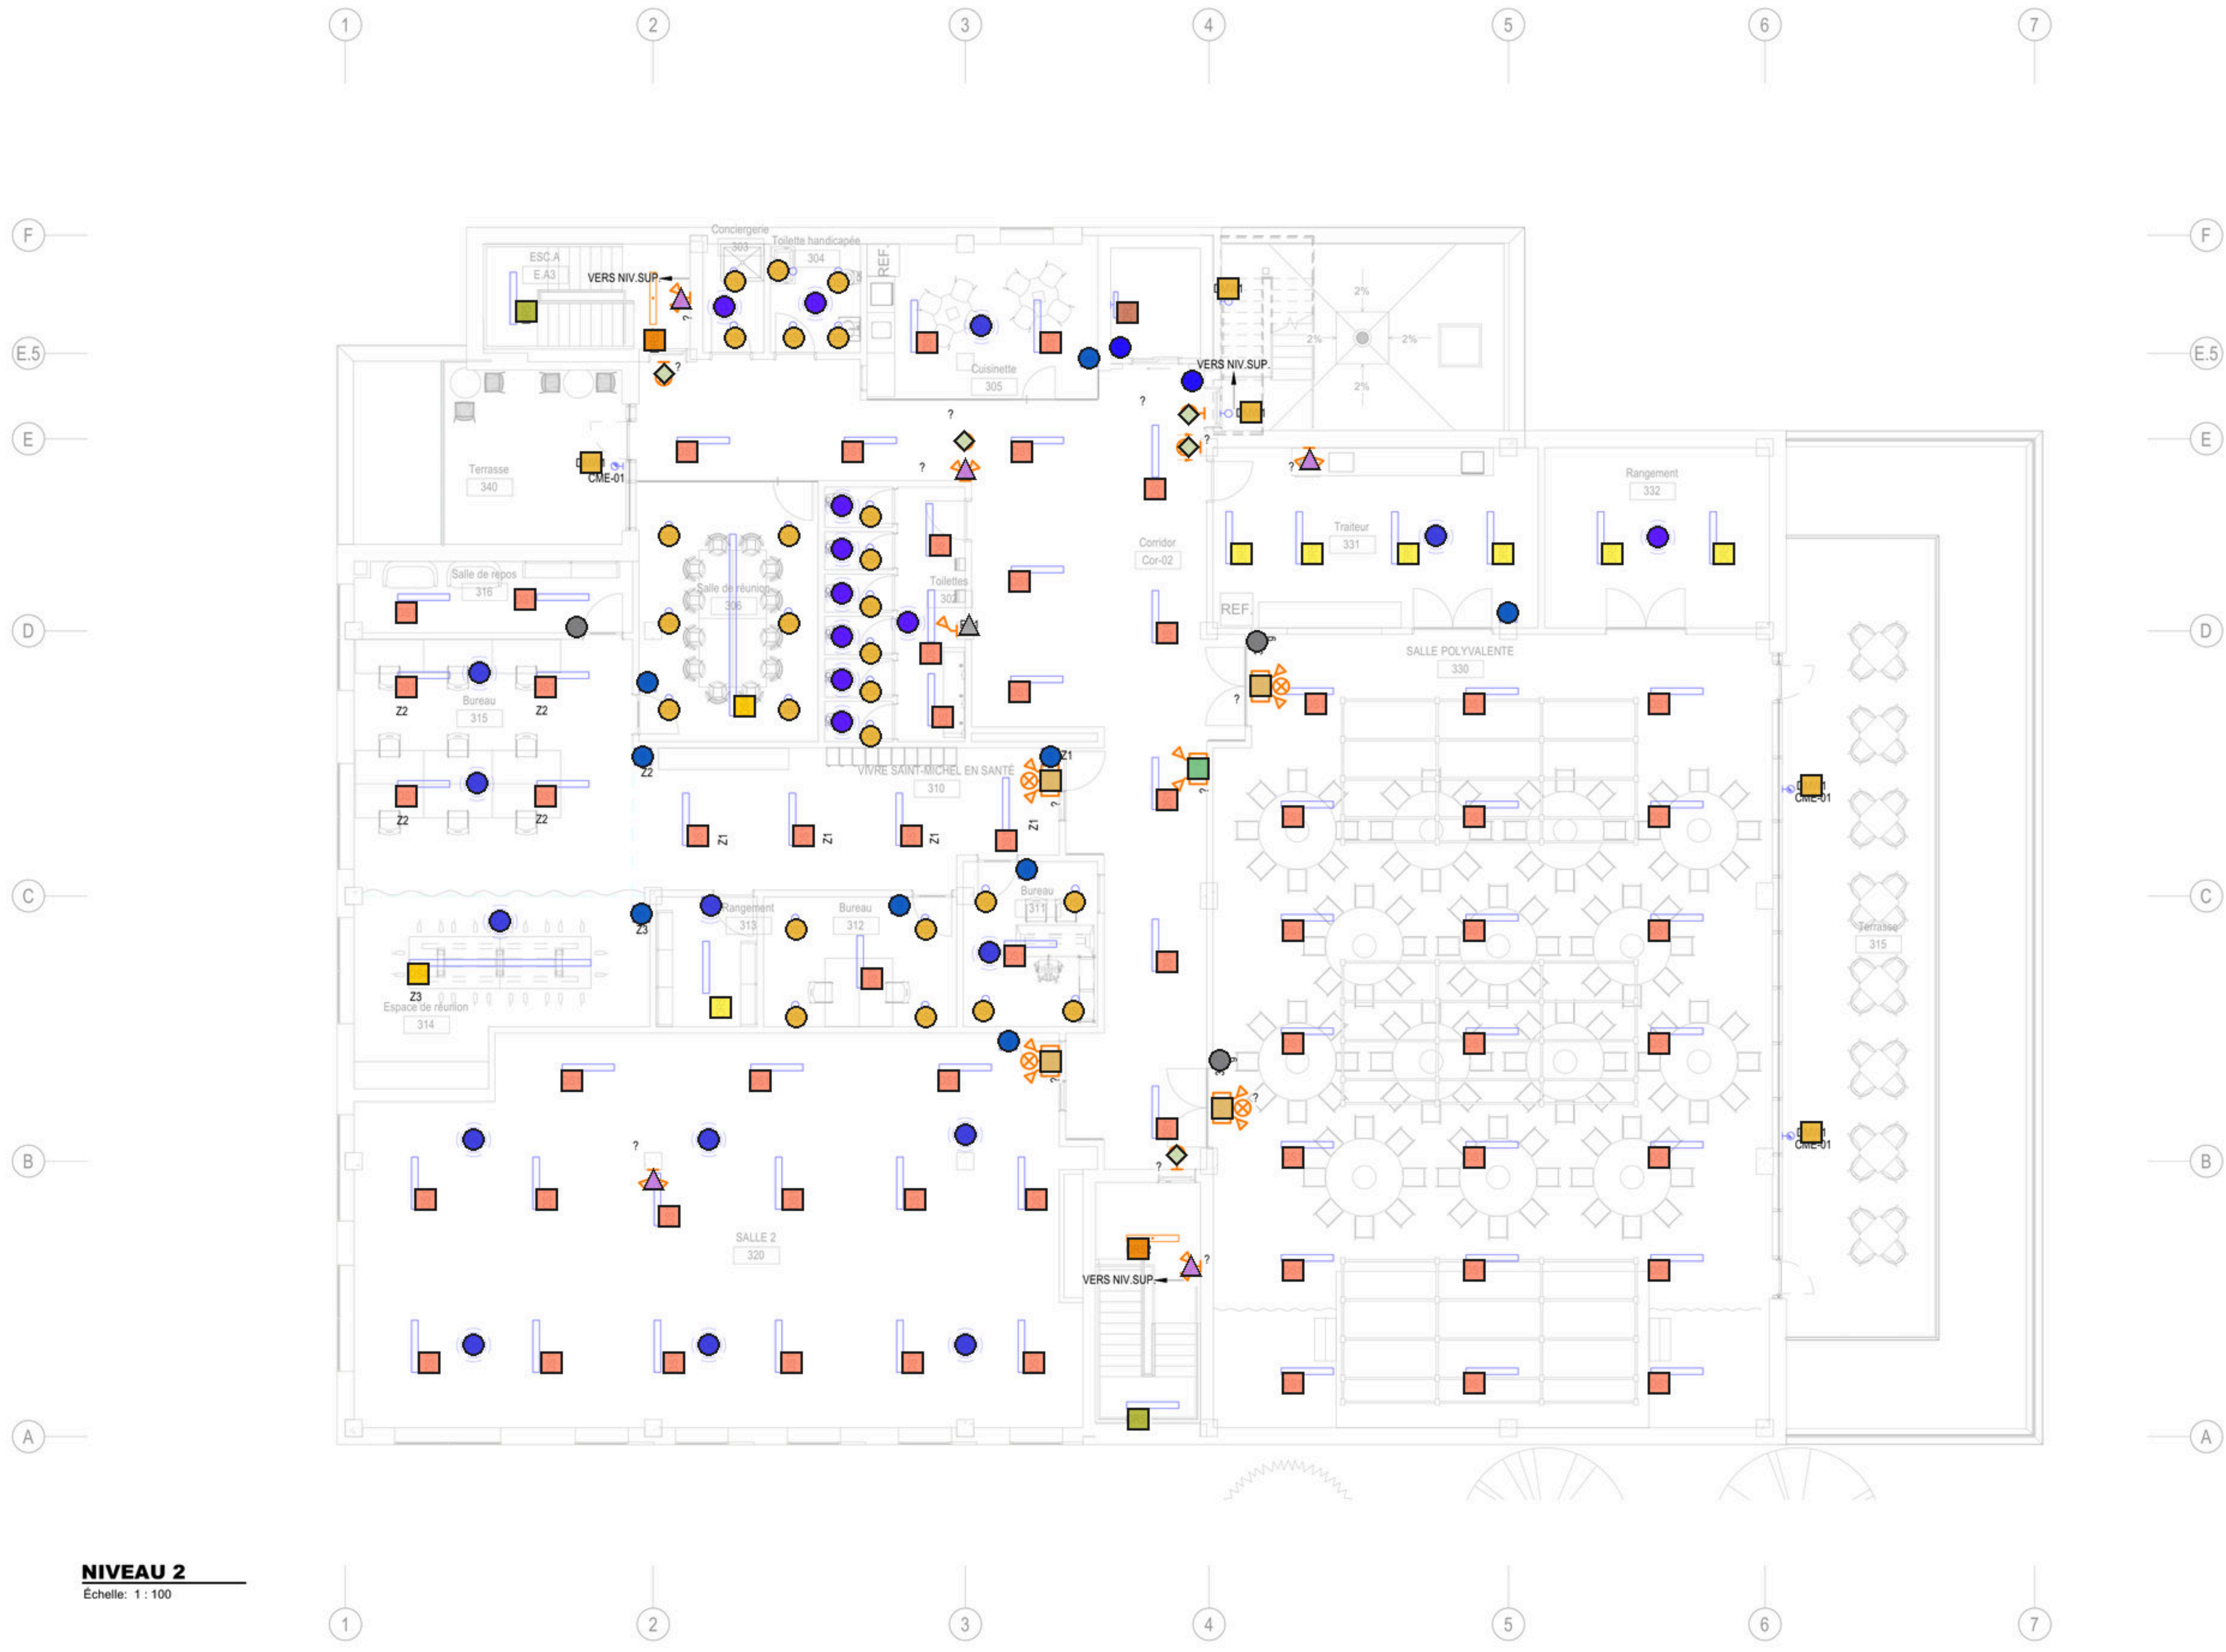

NIVEAU 2


Echelle: 1 : 100

TITRE DU PLAN:		ACCÈS TOITURE - ÉCLAIRAGE	
PRÉPARÉ PAR:		SCEAU	
M. BATISTA, ing. J. GILBERT, tech.			
DESSINÉ PAR:			
T. CANDU			
DATE:		PLAN:	
AVRIL 2026		E404	
DOSSIER:			
25-0810-QC			
DISCIPLINE			
ÉLECTRICITÉ			



TITRE DU PLAN:
**SOUS-SOL - ALARME
INCENDIE - PRISES ET
SERVICES**

PRÉPARE PAR:	SCEAU
M. BATISTA, ing. J. GILBERT, tech.	
DESSINE PAR:	
T. CANDU	
DATE:	
AVRIL 2026	
DOSSIER:	PLAN:
25-0810-QC	E405
DISCIPLINE	
ÉLECTRICITÉ	

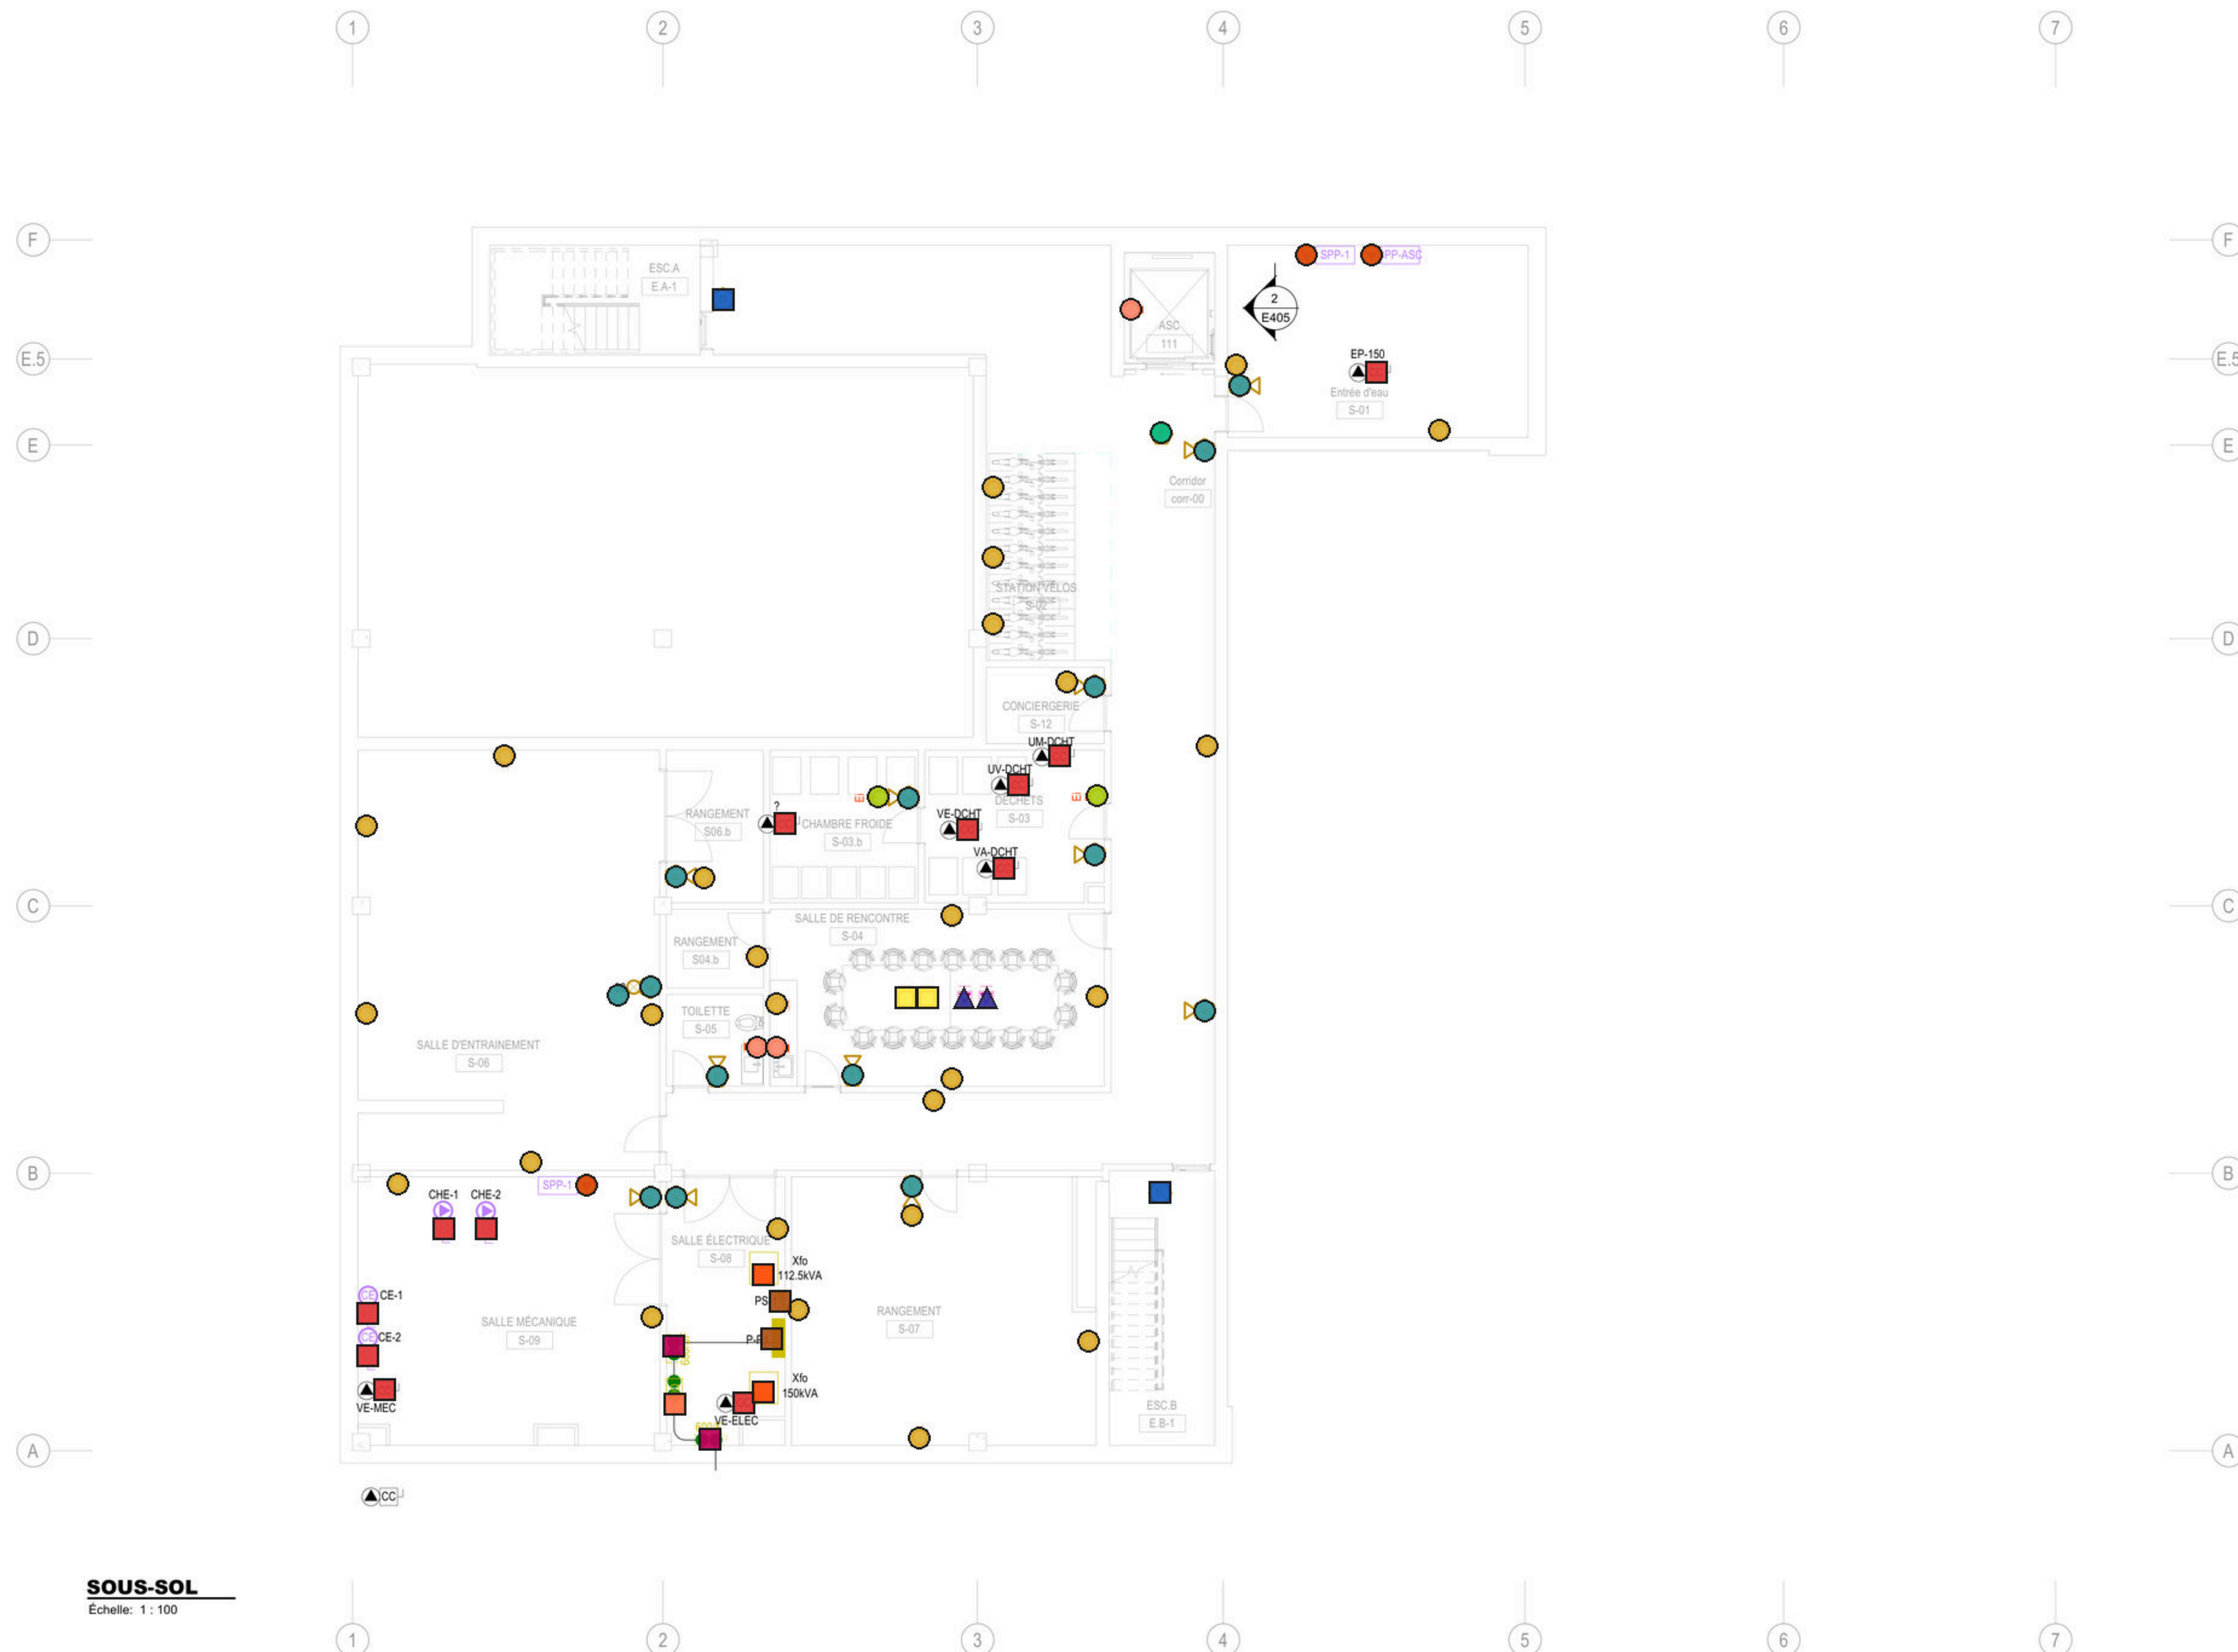


-  Avertisseur visuel (1)
-  Détecteur de fumée (1)
-  Indicateur de débit ID (5)
-  Interrupteur fin de course Ls (6)
-  Klaxon (13)
-  Mesurage Hydro-Québec (1)
-  Module de supervision Sx (6)
-  Panneau (2)
-  Poste manuel (2)
-  Prise DDFT Ei (2)
-  Prise duplex (26)
-  Prise duplex DDFT (3)
-  Prise mobilier (2)
-  Raccord CC équipement (12)
-  Raccord pompe (3)
-  Sectionneur (2)
-  Sortie data mobilier (2)
-  Transformateur (2)

CE PLAN EST LA PROPRIÉTÉ DES PROFESSIONNELS CI-DESSOUS
MENTIONNÉS. IL EST PRÊTÉ À CONDITION QU'IL NE SOIT PAS UTILISÉ À
L'ENCONTRE DE LEUR INTÉRÊT NI REPRODUIT EN TOUT OU EN PARTIE ET
QU'IL LEUR SOIT REMIS SUR DEMANDE.

AVANT DE PROCÉDER À L'INSTALLATION DES COMPOSANTES ET DES
SYSTÈMES ELECTROMECANQUES, L'ENTREPRENEUR DOIT CONSULTER LES
DERNIERS PLANS EMIS D'ARCHITECTURE. TOUTES LES MESURES DOIVENT
ÊTRE PRISES À PARTIR DES DERNIERS PLANS D'ARCHITECTURE.

CE PROJET DOIT SERVIR À LA CONSTRUCTION QUE SI LA MENTION "POUR
CONSTRUCTION" FIGURE DANS LA LISTE DES RÉVISIONS
CI-DESSOUS ET QU'IL SOIT DÔMENT SIGNÉ PAR L'INGÉNIEUR.

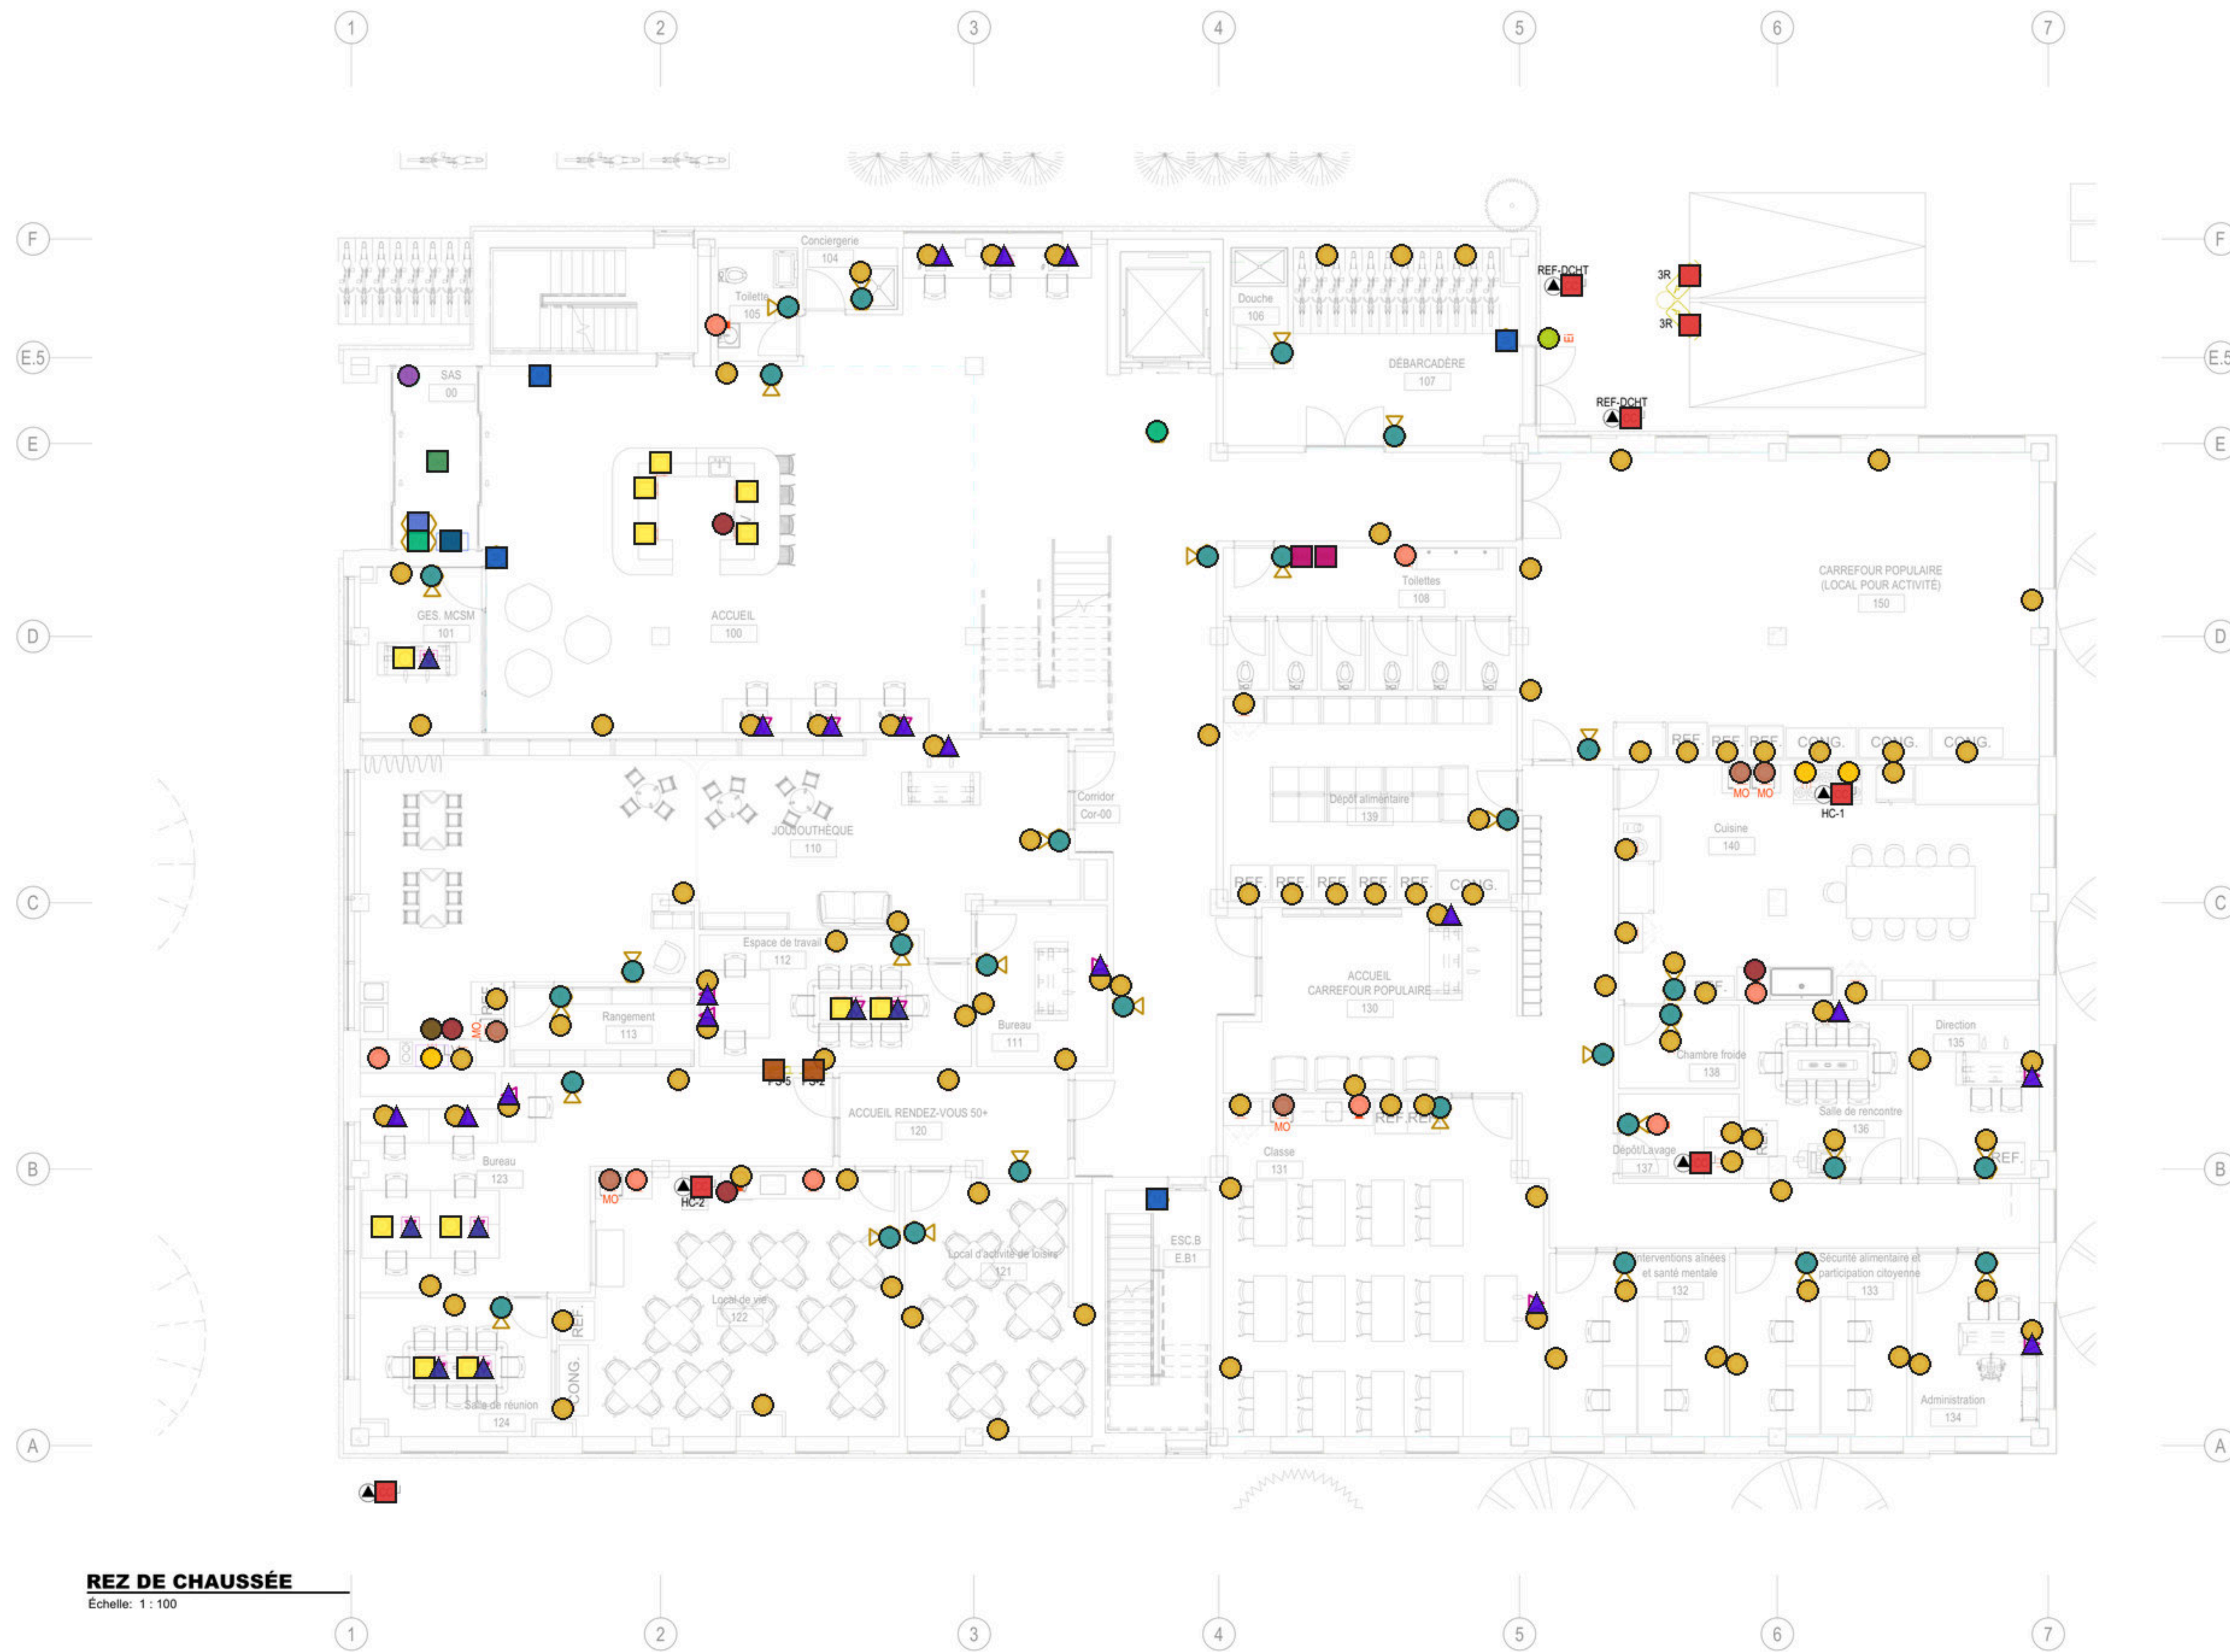

- Légende — E406 (216 marques)
- Détecteur de fumée (1)
 - Klaxon (31)
 - Module transmission TRA (1)
 - Panneau (2)
 - Panneau d'alarme PAI (1)
 - Poste manuel (4)
 - Poste-maître intercom PMI (1)
 - Prise DDFT Ei (1)
 - Prise cuisinière C (3)
 - Prise duplex (104)
 - Prise duplex DDFT (8)
 - Prise micro-onde (5)
 - Prise mobilier (12)
 - Raccord CC équipement (8)
 - Raccord hotte Ht (1)
 - Raccord lave-vaisselle (4)
 - Raccord sèche-main (2)
 - ▲ Sortie data (18)
 - ▲ Sortie data mobilier (7)
 - Symbole vert pointillé — à classer (1)
 - TS — à classer (1)



1	SOUSSION	2026-08-17
A	PERMIS	2026-05-08
NO.	Émis pour	Date


TITRE DU PLAN:
**REZ DE CHAUSSÉE - ALARME
INCENDIE - PRISES ET
SERVICES**

PRÉPARE PAR: M. BATISTA, ing. J. GILBERT, tech.	SCEAU
DESSINÉ PAR: T. CANDU	INGÉNIEUR Méthy Batista Soto Québec
DATE: AVRIL 2026	PLAN: E406
DOSSIER: 25-0810-QC	
DISCIPLINE: ÉLECTRICITÉ	

CE PLAN EST LA PROPRIÉTÉ DES PROFESSIONNELS CI-DESSOUS MENTIONNÉS. IL EST PRÊTÉ À CONDITION QU'IL NE SOIT PAS UTILISÉ À L'ENCONTRE DE LEUR INTÉRÊT NI REPRODUIT EN TOUT OU EN PARTIE ET QU'IL LEUR SOIT REMIS SUR DEMANDE.

AVANT DE PROCÉDER À L'INSTALLATION DES COMPOSANTES ET DES SYSTÈMES ELECTROMECANQUES, L'ENTREPRENEUR DOIT CONSULTER LES DERNIERS PLANS EMIS D'ARCHITECTURE. TOUTES LES MESURES DOIVENT ÊTRE PRISES À PARTIR DES DERNIERS PLANS D'ARCHITECTURE.

CE PROJET DOIT SERVIR À LA CONSTRUCTION QUE SI LA MENTION "POUR CONSTRUCTION" FIGURE DANS LA LISTE DES RÉVISIONS CI-DESSOUS ET QU'IL SOIT DÔMENT SIGNÉ PAR L'INGÉNIEUR.

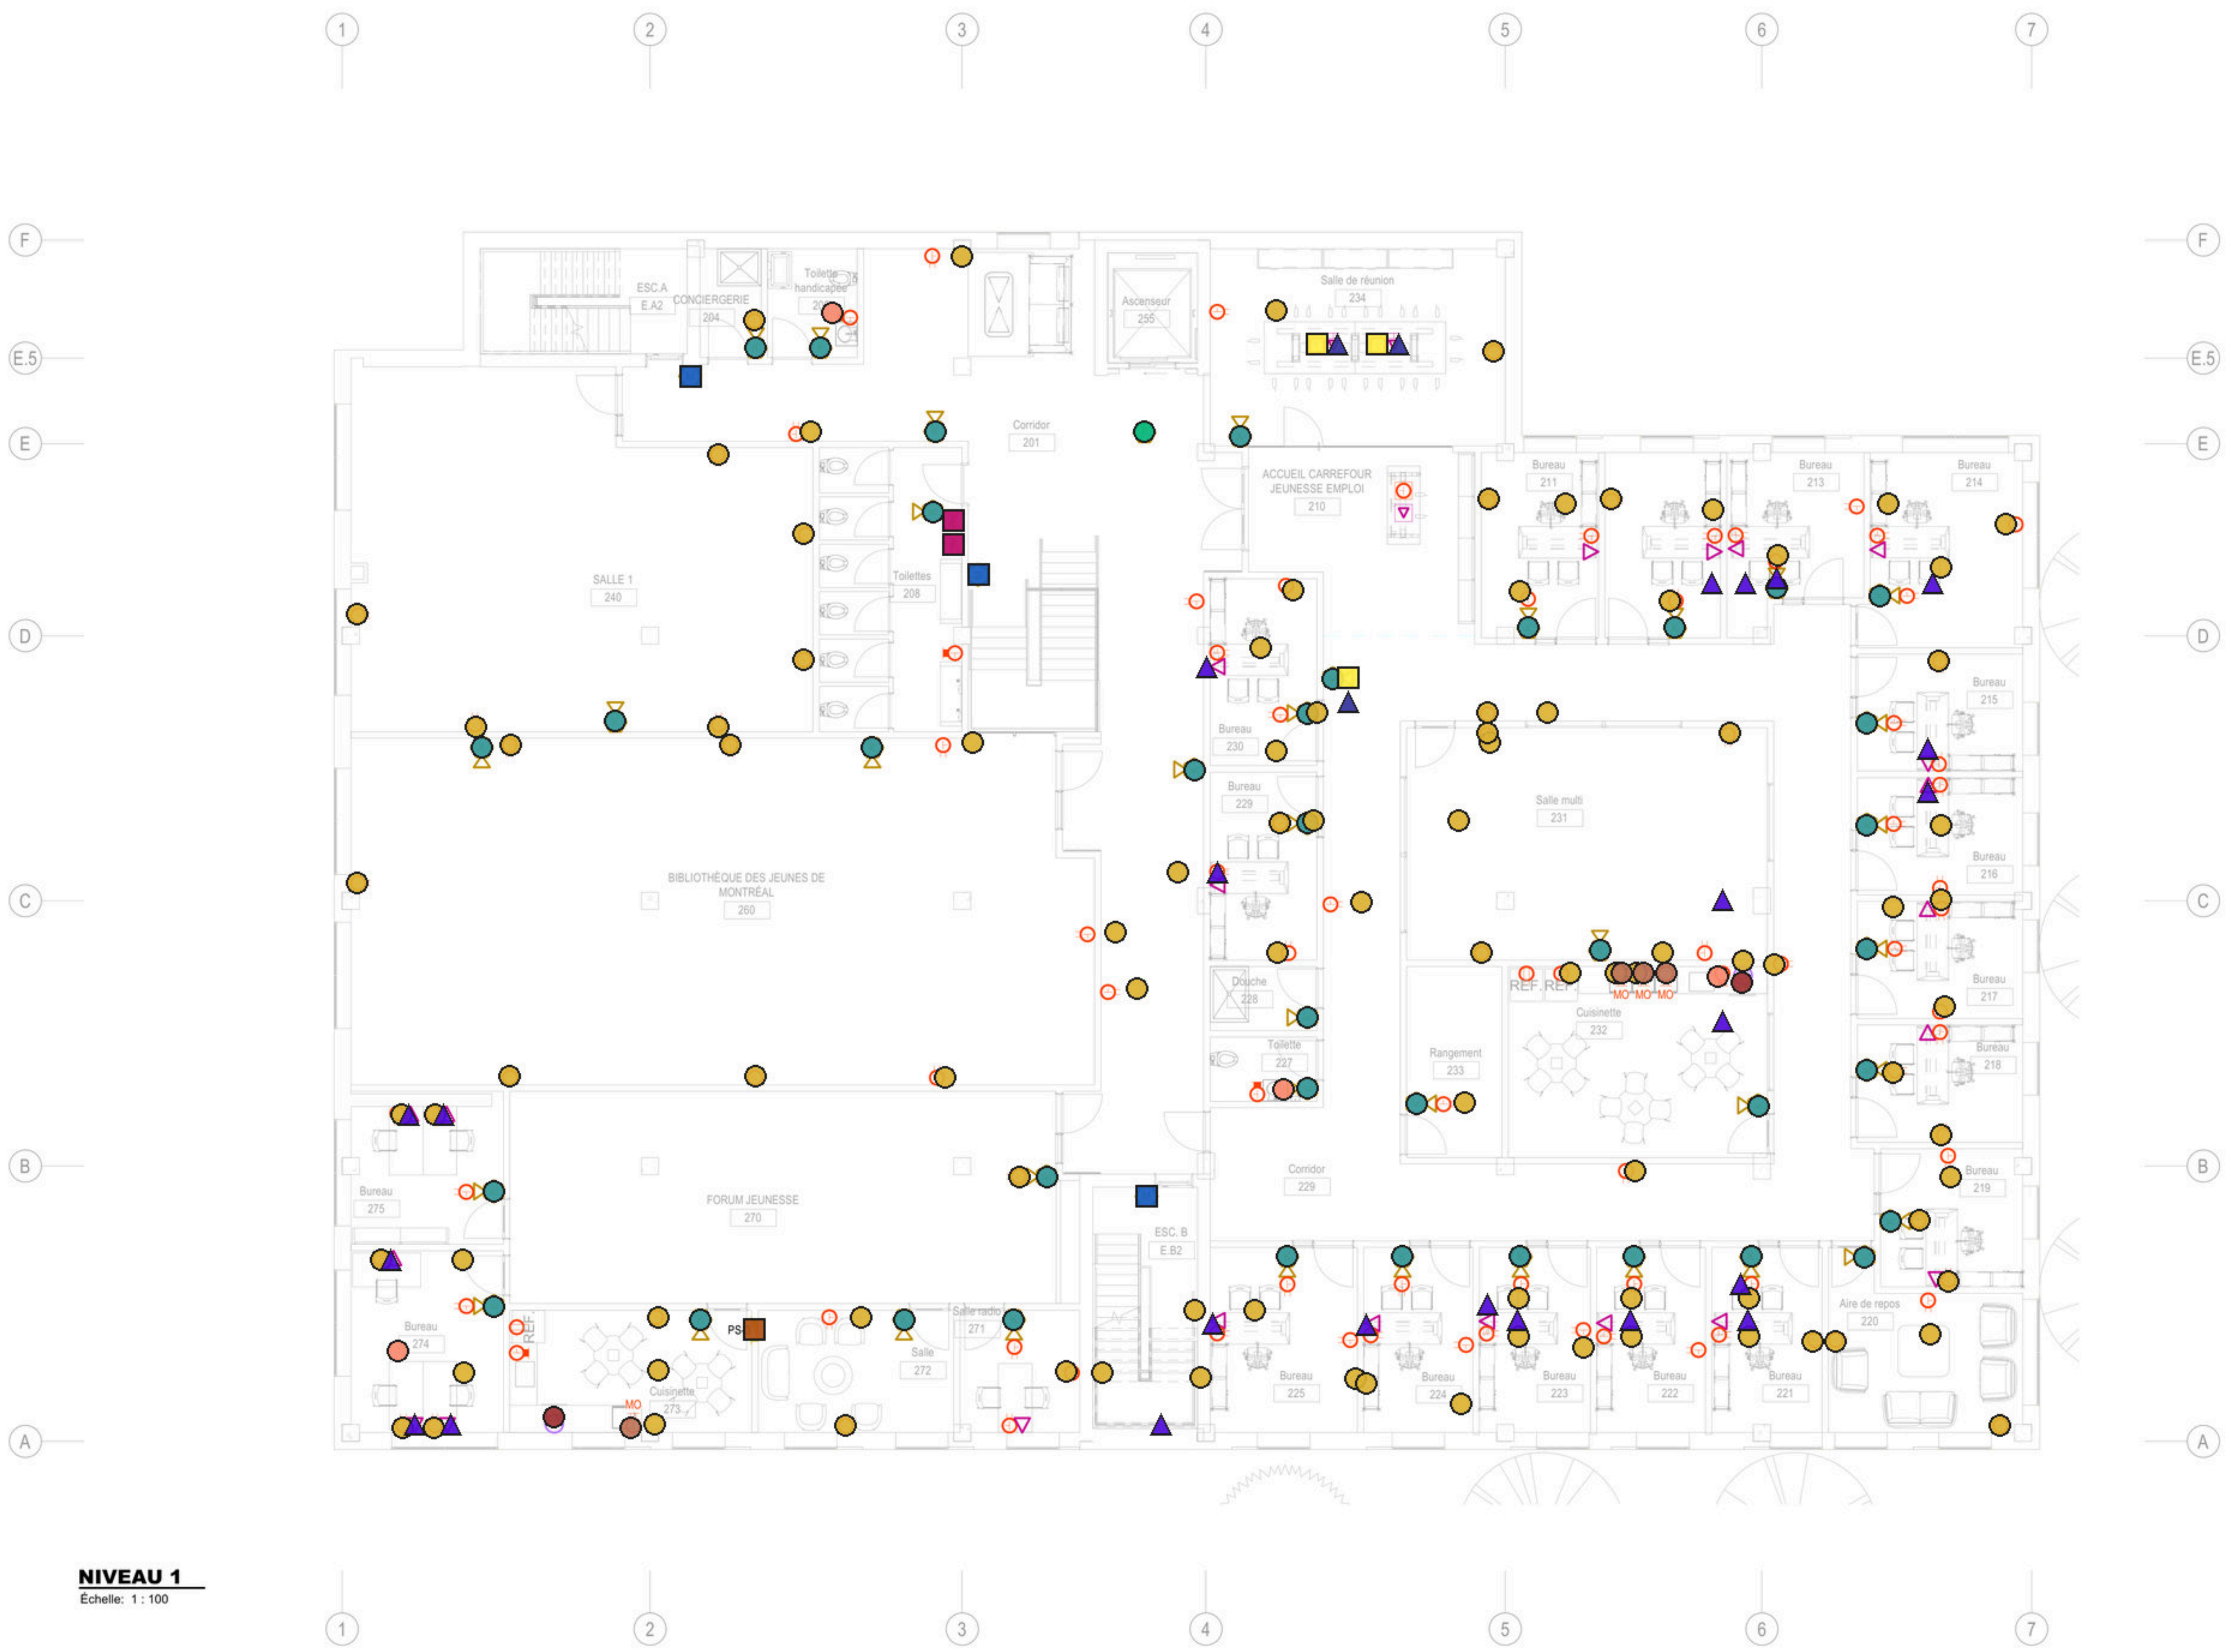

- Légende — E407 (180 marques)
- Détecteur de fumée (1)
- Klaxon (38)
- Panneau (1)
- Poste manuel (3)
- Prise duplex (96)
- Prise duplex DDFT (4)
- Prise micro-onde (4)
- Prise mobilier (3)
- Raccord lave-vaisselle (2)
- Raccord sèche-main (2)
- Sortie data (23)
- Sortie data mobilier (3)

CIVIL



STRUCTURE



ARCHITECTURE



MÉCANIQUE / ELECTRIQUE



1	SOUSSION	2026-08-17
A	PERMIS	2026-05-08
NO.	Émis pour	Date

TITRE DU PLAN:

NIVEAU 1 - ALARME

INCENDIE - PRISES ET

SERVICES

PRÉPARÉ PAR:

M. BATISTA, ing.

J. GILBERT, tech.

DESSINÉ PAR:

T. CANDU

DATE:

AVRIL 2026

DOSSIER:

25-0810-QC

DISCIPLINE

ÉLECTRICITÉ

SCEAU



PLAN:


E407

NIVEAU 1
Echelle: 1 : 100



- [illegible]

TITRE DU PLAN:	
NIVEAU 2 - ALARME INCENDIE - PRISES ET SERVICES	
PRÉPARÉ PAR:	SCEAU
M. BATISTA, ing. J. GILBERT, tech.	
DESSINÉ PAR:	
T. CANDU	
DATE:	
AVRIL 2026	
DOSSIER:	PLAN:
25-0810-QC	E408
DISCIPLINE:	
ÉLECTRICITÉ	

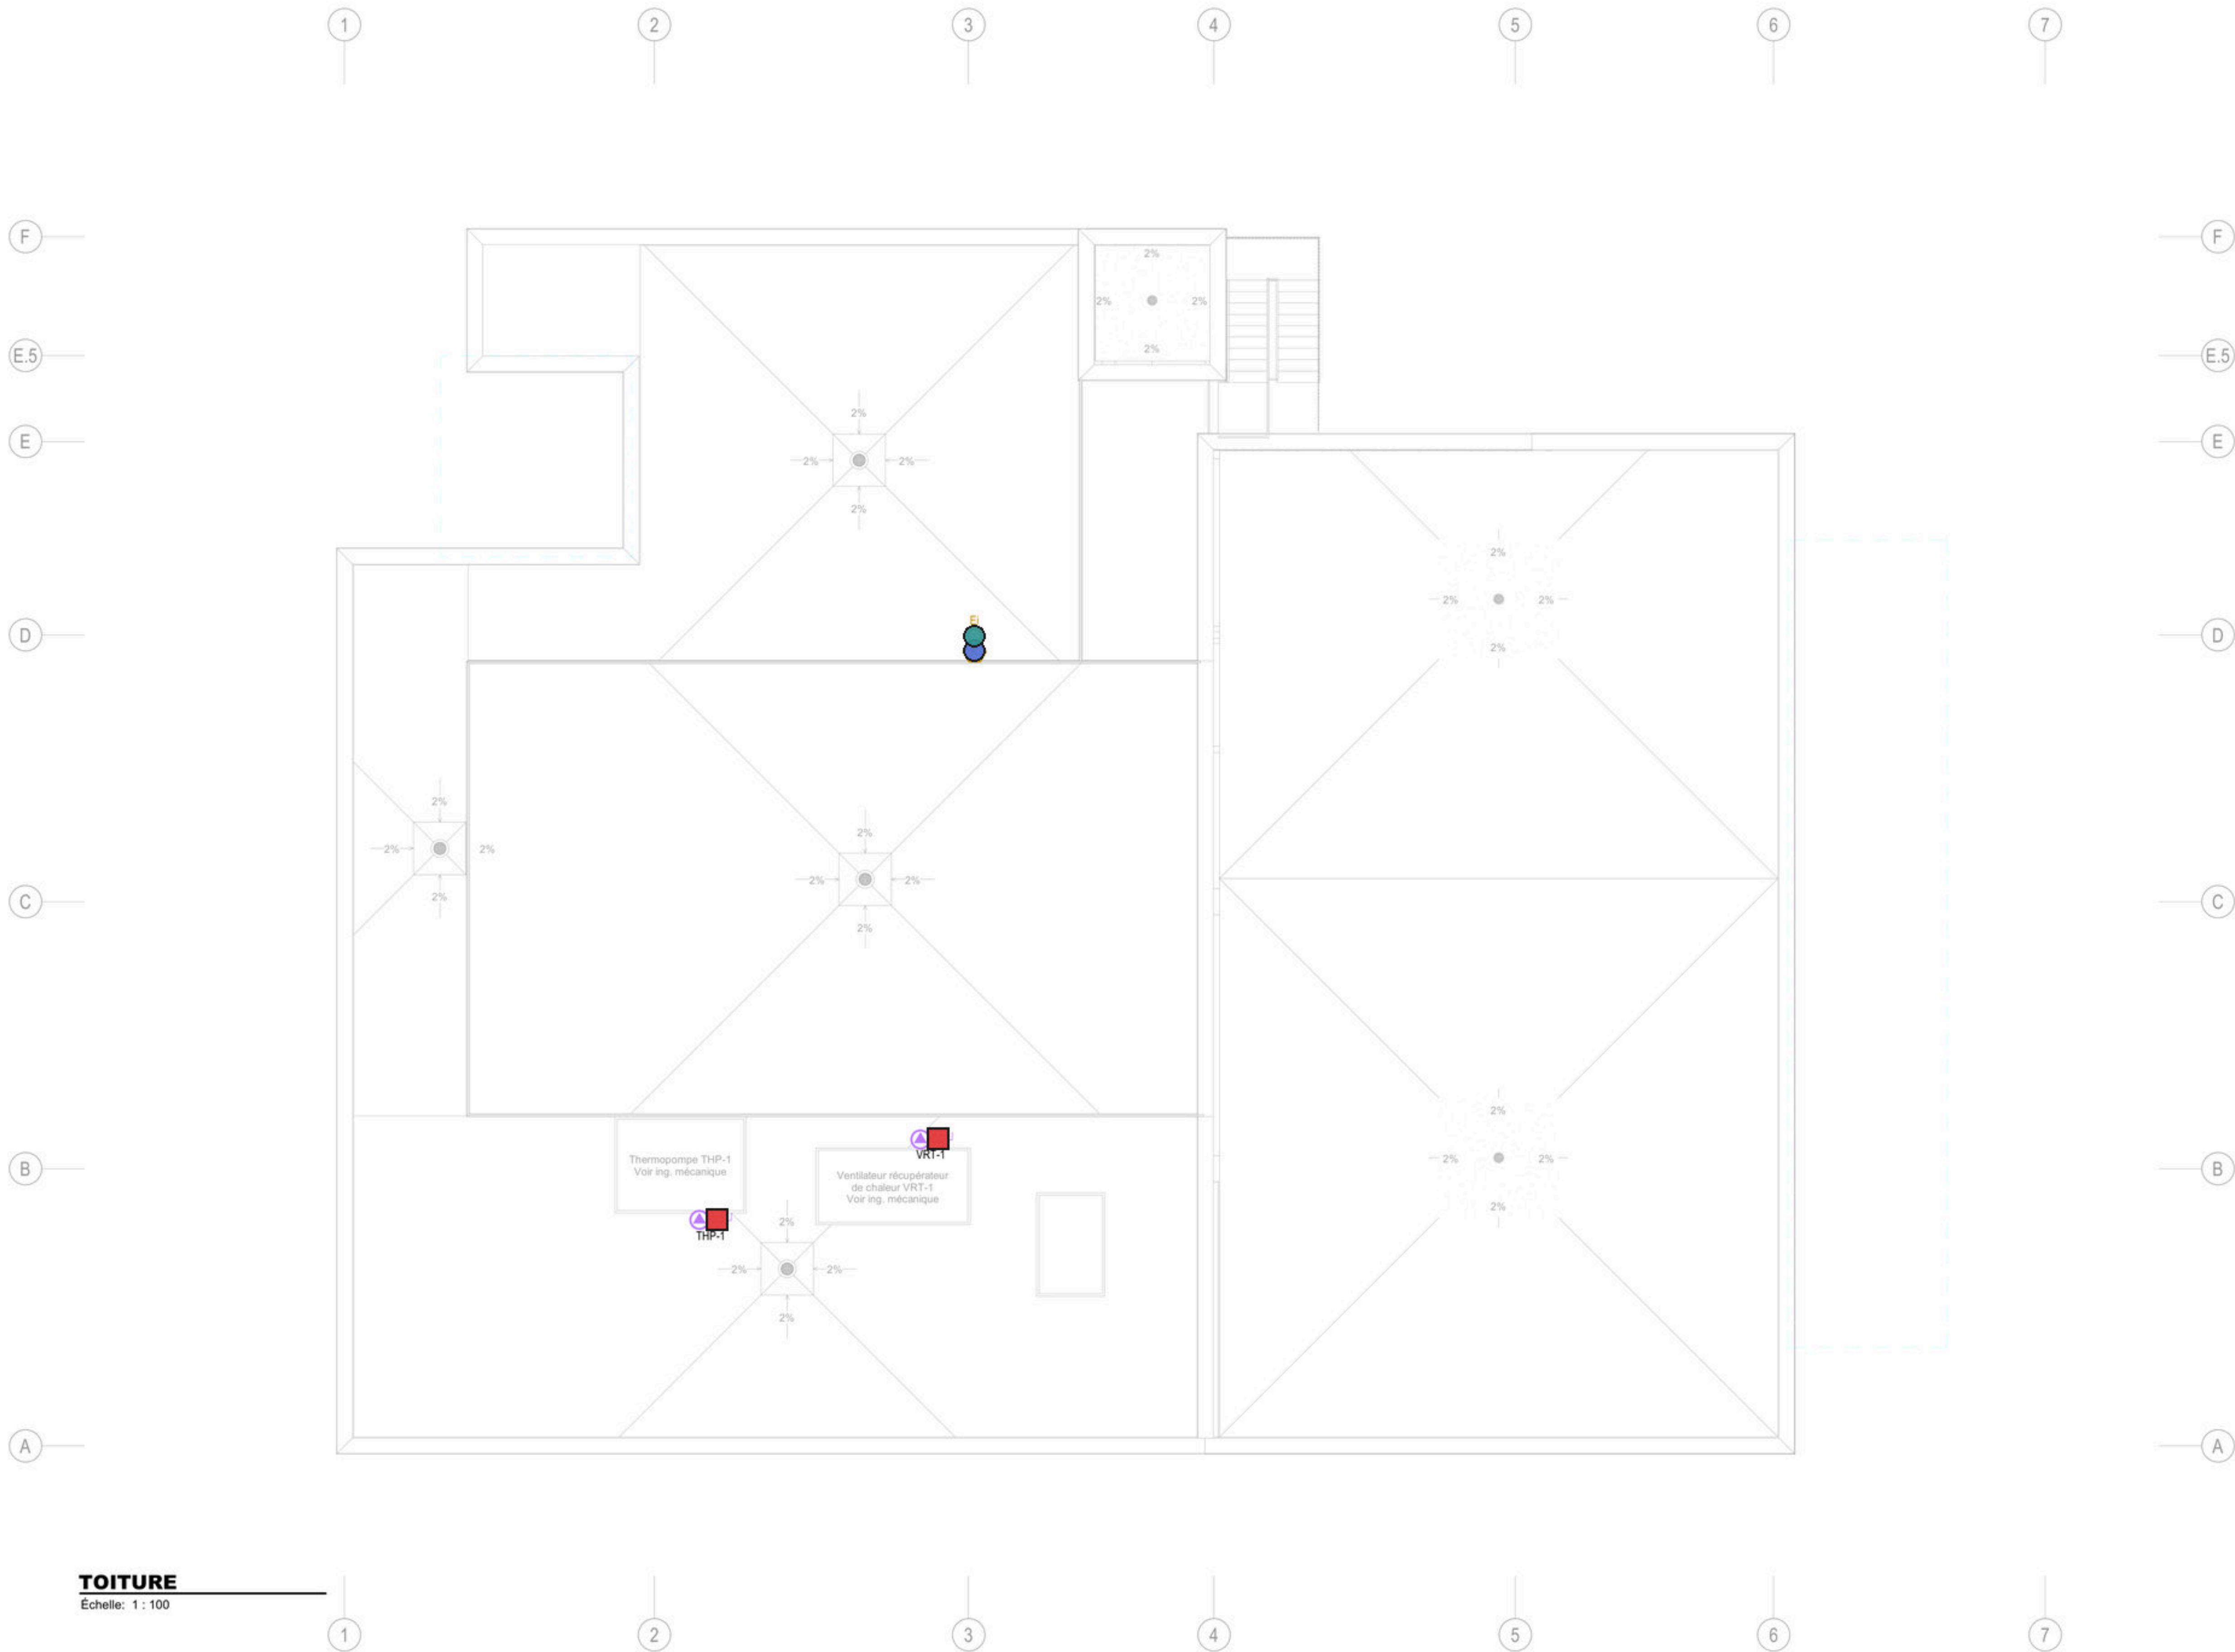

TOITURE
Echelle: 1 : 100

Légende — E409 (4 marques)

- Avertisseur visuel (1)
- Klaxon Ei (1)
- Raccord CC équipement (2)



**Saint-Michel
Quartier
de l'innovation
sociale**

**Maison Communautaire
Saint-Michel**
8615, Boulevard Saint-Michel
MONTRÉAL (QUÉBEC)

CE PLAN EST LA PROPRIÉTÉ DES PROFESSIONNELS CI-DESSOUS MENTIONNÉS. IL EST PRÊT À CONDITION QU'IL NE SOIT PAS UTILISÉ À L'ENCONTRE DE LEUR INTÉRÊT NI REPRODUIT EN TOUT OU EN PARTIE ET QU'IL LEUR SOIT REMIS SUR DEMANDE.

AVANT DE PROCÉDER À L'INSTALLATION DES COMPOSANTES ET DES SYSTÈMES ÉLECTROMÉCANIQUES, L'ENTREPRENEUR DOIT CONSULTER LES DERNIERS PLANS ÉMIS D'ARCHITECTURE. TOUTES LES MESURES DOIVENT ÊTRE PRISES À PARTIR DES DERNIERS PLANS D'ARCHITECTURE.

CE PROJET DOIT SERVIR À LA CONSTRUCTION QUE SI LA MENTION "POUR CONSTRUCTION" FIGURE DANS LA LISTE DES RÉVISIONS CI-DESSOUS ET QU'IL SOIT DÔMENT SIGNÉ PAR L'INGÉNIEUR.

CIVIL


STRUCTURE


ARCHITECTURE


MÉCANIQUE / ÉLECTRIQUE


1	SOUSSION	2026-08-17
A	PERMIS	2026-05-08
NO.	Émis pour	Date

TITRE DU PLAN:
**ACCÈS TOITURE - ALARME
INCENDIE - PRISES ET
SERVICES**

PRÉPARE PAR:
M. BATISTA, ing.
J. GILBERT, tech.

DESSINÉ PAR:
T. CANDU

DATE:
AVRIL 2026

DOSSIER:
25-0810-QC

DISCIPLINE:
ÉLECTRICITÉ

SCEAU

Merly Batista Soto
INGÉNIEUR
QUÉBEC

PLAN:
E409

PANNEAU : PS-1													
TENSION : 120/208V, 3Ø, 4F						BARRE OMNIBUS : 600A							
LOCALISATION : S-08 SALLE ELECTRIQUE						DISJ. MAITRE : NA							
OPTION :						MONTAGE : SURFACE							
BOITER :						ENTREE CABLE :							
FABRICANT : SQUARE D # NQ484L6CMH68-NC68V1													
ABV	DESCRIPTION	DISJ.	#	A	B	C	#	DISJ.	DESCRIPTION	ABV			
E	ASCENSEUR 111	15 A	1	34 / 92			2	15 A	D-1	Q			
Q	EP-150 (S-03, S-01)	15 A	3		86 / 114		4	15 A	S-03/03b	E			
E	MINUTERIE (ECL-EXT)	15 A	5			35 / 114	6	15 A	ESCALIER A	Q			
EV	S-03/03b/04/05/06/07	15 A	7	144 / 166			8	15 A	VE-MEC (S-09)	Q			
Q	VE-ELEC (S-08)	15 A	9		166 / 218		10	15 A	VAL-DOHT (S-01)	Q			
E	ESCALIER B	15 A	11			152 / 174	12	15 A	ELECTRIQUE	Q			
E	CORRIDOR-00	15 A	13	228 / 260			14	15 A	ESCALIER B	EV			
EV	ESCALIER A	15 A	15		242 / 360		16	20 A	S-01	P			
P	S-03/03b	20 A	17			240 / 276	18	15 A	CORRIDOR-00	EV			
P	S-02	20 A	19	360 / 750			20	15 A	UV-DOHT (S-01)	Q			
E	S-01/04/04b/05/06/06b/07/08/12	15 A	21		618 / 720		22	20 A	S-06	P			
Q	VC (SS)	15 A	23			408 / 960	24	20 A	110 / 111	P			
P	S-04	20 A	25	840 / 840			26	20 A	S-07/08/09	P			
P	S-05	20 A	27		120 / 120		28	20 A	COMPTOIR (S-04)	Q			
P	121/122	20 A	29			960 / 2000	30	40 A	SPP-ASC, 2HP	P			
P	CTRASC (S-01)	20 A	31	120 / 19952			32						
			33		0 / 19958		34	125 A	PS-2	QV			
			35			11323 / 19965	36						
QV	PS-4 125 A		37	11207 / 20334			38						
			39		11267 / 20450		40	200 A	PS-3	QV			
P	S-12	20 A	41			120 / 20476	42						
P	ASCENSEUR	20 A	43	120 / 1400			44						
			45		0 / 1400		46	20 A	REF-DOHT (EXT)	Q			
P	COMPTOR (S-04)	20 A	47			120 / 1400	48						
			49				50						
			51				52						
			53				54						
			55				56						
			57				58						
			59				60						
			61				62						
			63				64						
			65				66						
			67				68						
			69				70						
			71				72						
CHARGES RACCORDEES PAR PHASE: 56847 55839 58723													
ABRÉVIATIONS (ABV)				A : DISJONCTEUR ANTI-ARC C : CHAUFFAGE D : DISJONCTEUR D.D.F.T. E : ECLAIRAGE				P : PRISE DE COURANT R : ROUGE (A) Q : EQUIPEMENT V : VERROUILLAGE MECANIQUE				TOTAL DES CHARGES RACCORDEES 171468 WATTS	

PANNEAU : PS-4														
TENSION : 120/208V, 3Ø, 4F					BARRE OMNIBUS : 125A									
LOCALISATION :					DISJ. MAÎTRE :									
OPTION :					MONTAGE :					ENCASTRE				
BOÎTIER :					ENTRÉE CÂBLE :									
FABRICANT : SQUARE D # NQ484L6CMH68-NC68V1														
ABV	DESCRIPTION	DISJ.	#	A	B	C	#	DISJ.	DESCRIPTION	ABV				
Q	EVIER ÉLECTRIQUE (302, 304)	15 A	1	100 / 198			2	15 A	302/310/320/330/331	EV				
P	302	20 A	3		120 / 240		4	20 A	331	P				
EV	CORRIDOR 3 NIV.	15 A	5			144 / 240	6	20 A	EXT (315)	P				
E	CORRIDOR 3 NIV.	15 A	7	387 / 600			8	15 A	COLONETTE (310)	P				
P	331/332	20 A	9		480 / 620		10	15 A	REFRIGERATEUR (305)	P				
E	302-309/311/312/313	15 A	11			540 / 720	12	15 A	311/320	P				
P	320	20 A	13	1720 / 1110			14	15 A	VC (NIVEAU 2)	P				
P	310	20 A	15		840 / 1000		16	20 A	MO (305)	P				
P	310/312/313	20 A	17			840 / 946	18	15 A	330/331/332/EXT	E				
P	310/312/313	15 A	19	1181 / 500			20	15 A	SÈCHE-MAIN (302)	Q				
P	MO (331)	20 A	21		1000 / 500		22	15 A	SÈCHE-MAIN (302)	E				
P	306	20 A	23			960 / 970	24	15 A	314/315/316/320	E				
Q	SÈCHE-MAIN (302)	15 A	25	500 / 240			26	20 A	EXT TOIT	P				
P	REFRIGERATEUR (331)	15 A	27		500 / 120		28	15 A	LV (331)	P				
P	REFRIGERATEUR (331)	15 A	29			120 / 120	30	20 A	ASCENSEUR	P				
P	304	20 A	31	120 / 5667			32							
P	340	20 A	33		120 / 5667		34	60 A	LV	Q				
			35			0 / 5667	36							
			37				38							
			39				40							
			41				42							
			43				44							
			45				46							
			47				48							
			49				50							
			51				52							
			53				54							
			55				56							
			57				58							
			59				60							
			61				62							
			63				64							
			65				66							
			67				68							
			69				70							
			71				72							
CHARGES RACCORDEES PAR PHASE:					11323	11207	11267							
ABRÉVIATIONS (ABV)					P : PRISE DE COURANT R : ROUGE (A) Q : EQUIPEMENT V : VERROUILLAGE MÉCANIQUE					TOTAL DES CHARGES RACCORDEES 33796 WATTS				

PANNEAU : PS-2

TENSION : 120/208V, 3Ø, 4F	BARRE OMNIBUS : 125A
LOCALISATION : 123 (BUREAU)	DISJ. MAÎTRE : N/A
OPTION : PORTE DANS PORTE	MONTAGE : ENCASTRE
BOÎTIER : NEMA 2	ENTRÉE CÂBLE : N/A
FABRICANT : SQUARE D # NQ484L6CMH68-NC68V1	

ABV	DESCRIPTION	DISJ.	#	A	B	C	#	DISJ.	DESCRIPTION	ABV
Q	ÉLECTRIQUE (105)	15 A	1	50 / 100			2	15 A	VE-SECH	Q
Q	ÉVIER ÉLECTRIQUE (108)	15 A	3		50 / 120		4	20 A	108	P
E	100	15 A	5			100 / 120	6	20 A	122 (CONGÉLO)	P
P	105, 104	20 A	7	240 / 410			8	15 A	101/CORRIDOR RDC	E
EV	SAS/100 CORRIDOR	15 A	9		254 / 458		10	15 A	101/107/108/110/120/122/130/140...	EV
P	100	20 A	11			360 / 500	12	15 A	LAVEUSE (137)	P
E	110/111/112/113	15 A	13	584 / 720			14	20 A	150	P
P	100	20 A	15		600 / 832		16	15 A	120/122/121/123/124	E
P	136/135 CORRIDOR	20 A	17		720 / 835		18	15 A	104/108/137/138/140/150	E
Q	112(113)	20 A	19	960 / 1000			20	15 A	MO (110)	P
Q	VC (RDC)	15 A	21		1334 / 120		22	15 A	COMPTOIR (122)	P
Q	130/131/132	15 A	23			960 / 1060	24	15 A	130-136/139	E
Q	VC (RDC)	15 A	25	1078 / 500			26			
P	150	20 A	27		240 / 500		28	15 A	SECHE-MAIN (108)	Q
Q	HOTTE CUISINE (117)	40 A	29			3000 / 500	30			
P	137	15 A	31	120 / 500			32	15 A	SECHE-MAIN (108)	Q
Q	ÉCHEUSE	30 A	33		2000 / 360		34	20 A	107	P
Q			35			2000 / 120	36	20 A	EXTÉRIEUR	P
Q	LV (100)	50 A	37	4000 / 240			38	20 A	110 (COMPTOIR)	P
P			39		4000 / 840		40	20 A	123	P
P	COMPTOIR (122)	15 A	41			240 / 360	42	20 A	124	P
P	100	20 A	43	360 / 840			44	15 A	100/101	P
			45		0 / 4000		46	50 A	LV (122)	Q
Q	132/133/134	20 A	47			840 / 4000	48			
P	LV (110)	50 A	49	4000 / 250			50			
Q			51		4000 / 250		52	15 A	HC-2 (RDC)	Q
Q	LV (150)	50 A	53			4000 / 250	54			
			55	4000 / 0			56			
			57				58			
			59				60			
			61				62			
			63				64			
			65				66			
			67				68			
			69				70			
			71				72			

CHARGES RACCORDEES PAR PHASE				19952	19958	19965
ABSEVATIONS				P : PRISE DE COURANT		
(ABV)				R : ROUGE (IN)		
				C : CHAUFFAGE		
				O : EQUIPEMENT		
				V : VERROUILLAGE MECANIQUE		
				D : DISJONCTEUR D.D.F.T.		
				E : ECLARAGE		
				TOTAL DES CHARGES RACCORDEES		
				59875		
				WATTS		