

RC-PDNO-600(600)													
Local:			Tension: 247500V			Type barres:			Disjoncteur Maître: N/A				
Alimenté:			Phases: 3			Barres: 600 A							
Niveau:			Fils: 4										
Courant Rupture: 22kA													
Note	Description	Disj.	Poles	C C T	A	B	C	C C T	Poles	Disj.	Description	Note	
	ECLAIRAGE STATIONNEMENT	15 A	1	1	164 VA	8000 VA		2	1	15 A	CHAUFFAGE 101 / 102		
	CHAUFFAGE 103 / 104 + ENTREE	15 A	1	3		3000 VA	3750 VA	4	1	15 A	SE-01 / SE-02		
	CHAUFFAGE 105 / 106 / 109 / 110 / ENTREE GARAGE	15 A	1	5			3000 VA	15000 VA	6	1	60 A	CHAUFFAGE GARAGE 20000N	
	CHAUFFAGE VESTIAIRE	15 A	1	7	4000 VA	10000 VA		8	1	40 A		SE-07	
	CHAUFFAGE SALLE MECANIQUE	15 A	1	9		4000 VA	7750 VA	10	1	30 A	SE-03 / SE-04		
				11				9687 VA	12				
				13	20861 VA	9687 VA			14				
	RC-TRNO-600	50 A	3	15		28008 VA	9687 VA		16				
				17			20888 VA	12000 VA	18				
				19	12000 VA	12000 VA			20				
				21		12000 VA	15000 VA		22				CE-01
	CE-02	60 A	3	23			12000 VA	12000 VA	24				
				25	8333 VA	12000 VA			26				
				27		8333 VA	12000 VA		28				CE-03
	SE-05	50 A	3	29				8333 VA	10000 VA	30			
				31		10000 VA			32				
				33			10000 VA		34				SE-06
				36					36				
				37					38				
				39					40				
				41					42				
Total Charge:					195625 VA	195508 VA		196188 VA					
Total Courant :					564 A	563 A		565 A					
Total du panneau													
Charge totale raccordée: 157521 VA													
Courant total raccordé: 565 A													
Notes:													

RC-PSNO-200(200)													
Local: SALLE ELECTRIQUE 109				Tension: 12000V				Type barres:					
Alimenté: RC-TRNO-600				Phases: 3				Barres: 400 A					
Niveau: NIVEAU 1				Fils: 4				Disjoncteur Maître:					
Courant Rupture: 19kA													
Note	Description	Disj.	Poles	C T	A	B	C	C T	Poles	Disj.	Description	Note	
	ECLAIRAGE 109 / 110	15 A	1	1	105 VA	187 VA		2	1	15 A	ECLAIRAGE 101 / 102 / 103		
	ECLAIRAGE SALLE MECANIQUE	15 A	1	3		132 VA	204 VA	4	1	15 A	ECLAIRAGE GARAGE		
	ECLAIRAGE SALLE MECANIQUE	15 A	1	5			132 VA	175 VA	6	1	15 A	ECLAIRAGE EXTÉRIEUR	
	ECLAIRAGE ENTRÉE ET TOILETTES	15 A	1	7	251 VA	478 VA		8	1	15 A	ECLAIRAGE PATINOIRE		
	ECLAIRAGE GARAGE	15 A	1	9		307 VA	500 VA	10	1	15 A	PRISE FONTAINE REFRIGÉRÉE		
	ECLAIRAGE PATINOIRE	15 A	1	11			478 VA	540 VA	12	1	15 A	PRISSES BUREAU 101	
	ECLAIRAGE PATINOIRE	15 A	1	13	666 VA	696 VA		14	1	15 A	VA-01		
	ECLAIRAGE PATINOIRE	15 A	1	15		666 VA	714 VA	16	1	15 A	ECLAIRAGE PATINOIRE		
	PROJECTEURS	15 A	1	17			660 VA	714 VA	18	1	15 A	ECLAIRAGE PATINOIRE	
	PRISE PORTE DE GARAGE	15 A	1	19	1000 VA	180 VA		20	1	15 A	PRISE ENTRÉE D'EAU 110		
	ECLAIRAGE VESTIAIRE	15 A	1	21		809 VA	1170 VA	22	1	15 A	DEV-01		
	VE-03 / VE-04	15 A	1	23			1872 VA	180 VA	24	1	15 A	PRISSES T1	
	ECH-01	15 A	2	25	500 VA	900 VA		26		15 A		VC-01	
	PRISE ENTRETIEN GARAGE	20 A	1	29		500 VA	500 VA	30					
	VE-01	15 A	2	31	812 VA	2099 VA		32		20 A		COND-01	
	PRISSES VESTIAIRE	15 A	1	33		812 VA	636 VA	34					
	PRISE AGRICULTURE DE PATIN	15 A	1	35			980 VA	936 VA	36	2	15 A	VE-02	
	PRISE SALLE ELECTRIQUE 109	15 A	1	37	180 VA	360 VA		38	1	15 A	PRISSES T1		
	PRISE SALLE ELECTRIQUE 109	15 A	1	39		180 VA	180 VA	40	1	15 A	PRISE CONCIERGE		
	PRISSES GARAGE 108	15 A	1	41		360 VA	540 VA	42	1	15 A	PRISSES SALLE MECANIQUE 111		
	PRISSES ENTRETIEN VESTIAIRE	20 A	1	43	360 VA	540 VA		44	1	15 A	PRISSES ENTRETIEN 102		
	PRISSES T1	15 A	1	45	360 VA	360 VA		46	1	15 A	PRISSES GARAGE 108		
	SÈCHE-MAINS 106	15 A	1	47			600 VA	82 VA	48	1	15 A	ECLAIRAGE DE SECOURS	
	SÈCHE-MAINS 104	15 A	1	49	600 VA	900 VA		50	1	15 A	PRISSES T1		
	PRISSES EXTÉRIEURE	1	51		540 VA	900 VA		52	1	15 A	SÈCHE-MAINS 105		
			53				10371 VA	0 VA	54	1	15 A	RÉGULATION	
	BÔÎTER CAMLOCK	200 A	3	55	10371 VA	0 VA		56	1	15 A	RÉGULATION		
				57		10371 VA	636 VA	58		15 A		VA-02	
				59				60					
	PANNEAU ALARMES INCENDIE	15 A	1	61	500 VA	108 VA		62	1	15 A	ECLAIRAGE MARGOISE		
				63				64					
				65				66					
				67				68					
				69				70					
				71				72					
Total Charge:					25961 VA	26008 VA		26688 VA					
Total Courant :					216 A	217 A		222 A					
Total du panneau													
Charge totale raccordée: 78857 VA													
Courant total raccordé: 216 A													
Notes:													
1 - DISJONCTEUR DE COULEUR ROUGE ET CADENASSABLE													

ÉCLAIRAGE

1502

1501

1500

LUMINAIRE DE TYPE "N", CONTRÔLÉ PAR L'INTERRUPTEUR "N", ALIMENTÉ PAR LE CIRCUIT "1" DU PANNEAU "2"

LUMINAIRE AU MUR DE TYPE "N"

LAMPADAIRE SIMPLE DE TYPE "N"

LUMINAIRE DE TYPE "N", CONTRÔLÉ PAR L'INTERRUPTEUR "N", ALIMENTÉ PAR LE CIRCUIT "1" DU PANNEAU "2"

CONTRÔLE D'ÉCLAIRAGE DE LIGNE

1503

1504

1505

INTERRUPTEUR UNIPOLAIRE "N" INDIQUE LES APPARELS COMMANDÉS PAR CET INTERRUPTEUR

GRADATEUR MANUEL

DÉTECTEUR DE PRÉSENCE 300' POUR LE CONTRÔLE DE L'ÉCLAIRAGE

INTERRUPTEUR BASSE TENSION

GRADATEUR BASSE TENSION

CONTRÔLE D'ÉCLAIRAGE BASSE TENSION

1506

ARMOIRE DE RELAIS BASSE TENSION

INDICATEURS D'ISSUE

1507

1508

1509

1510

1511

1512

INDICATEUR D'ISSUE SIMPLE FACE SANS FLÈCHE DE DIRECTION, AU PLAFOND

INDICATEUR D'ISSUE SIMPLE FACE SANS FLÈCHE DE DIRECTION, AU MUR

ACCUMULATEUR D'ÉCLAIRAGE DE SECOURS AVEC TÊTE D'ÉCLAIRAGE DOUBLE TYPE "AUX"

TÊTE D'ÉCLAIRAGE SIMPLE TYPE "A", AU MUR ALIMENTÉE PAR L'ACCUMULATEUR UBX

TÊTE D'ÉCLAIRAGE DOUBLE TYPE "A", AU MUR ALIMENTÉE PAR L'ACCUMULATEUR UBX

PRISES DE COURANT

1513

1514

19

TABLEAUX DES LUMINAIRES										
IDENTIFICATION	MARQUE	MODELE	TYPE DE MONTAGE	LAMPE	TEMPERATURE COULEURS	LUMENS	DONNÉES ÉLECTRIQUE		REMARQUES	
R1	COOPER LIGHTING	24C25CT3-LV-LV-LV-300K	ENCASTRE	DEL	3000 K	3777 lm	24 VA	120 V		
D1	COOPER LIGHTING	GH-L-SAB-300-LU-14W	LAMPADAIRE	T-3	0 K	0 lm	82 VA	347 V		
L1	AXIS	BRLE-300-30-30-30-30-30	ENCASTRE	DEL	3000 K	3000 lm	78 VA	120 V		
L3	AXIS	BRLE-300-30-30-30-30-30	ENCASTRE	DEL	3000 K	3000 lm	78 VA	120 V		
L3A	COOPER LIGHTING	42N4-L-LV-LV-LV-LV-LV-300K	ENCASTRE	DEL	3000 K	3000 lm	78 VA	120 V		
L4	COOPER LIGHTING	4V73-L-DS-8-2-LV-LV-LV-LV-LV-300K	SURFACE	DEL	4000 K	4000 lm	51 VA	120 V		
L4A	COOPER LIGHTING	4V73-L-DS-8-2-LV-LV-LV-LV-LV-300K	SURFACE	DEL	4000 K	4000 lm	51 VA	120 V		
M1	COOPER LIGHTING	4V73-L-DS-8-2-LV-LV-LV-LV-LV-300K	SURFACE	DEL	4000 K	4000 lm	51 VA	120 V		
P1	COOPER LIGHTING	4V73-L-DS-8-2-LV-LV-LV-LV-LV-300K	SURFACE	DEL	4000 K	4000 lm	51 VA	120 V		
R1	COOPER LIGHTING	4V73-L-DS-8-2-LV-LV-LV-LV-LV-300K	SURFACE	DEL	4000 K	4000 lm	51 VA	120 V		
R3	COOPER LIGHTING	4V73-L-DS-8-2-LV-LV-LV-LV-LV-300K	SURFACE	DEL	4000 K	4000 lm	51 VA	120 V		

CARACTÉRISTIQUES DES APPAREILS DE CHAUFFAGE

NOTES:

IDENTIFICATION	DESCRIPTION	MARQUE	MODELE	ENCASTRE	CONTRÔLE	DONNÉES ÉLECTRIQUE		REMARQUES
						TENSION	PUISSANCE (W)	
A15	AÉROTHERME MURAL	STELPRO	WFA150324W	Oui	RELAS	347 V	1500 W	
B5	PLINTHE	STELPRO	B1030W	Non	RELAS	347 V	300 W	
B10	PLINTHE	STELPRO	B1030W	Non	RELAS	347 V	1000 W	
B12	PLINTHE	STELPRO	B1030W	Non	RELAS	347 V	1500 W	
B15	PLINTHE	STELPRO	B1030W	Non	RELAS	347 V	1500 W	
B25	PLINTHE	STELPRO	B2030W	Non	RELAS	347 V	2000 W	
T4	AÉROTHERME PLAFOND	STELPRO	SHU451COCHAR	Non	Oui	347 V	4000 W	
T15	AÉROTHERME PLAFOND	STELPRO	SHU151COCHAR	Non	Oui	347 V	15000 W	
RT	RELAS TRIAC	STELPRO	RE253T	Non	Oui	347 V	1	

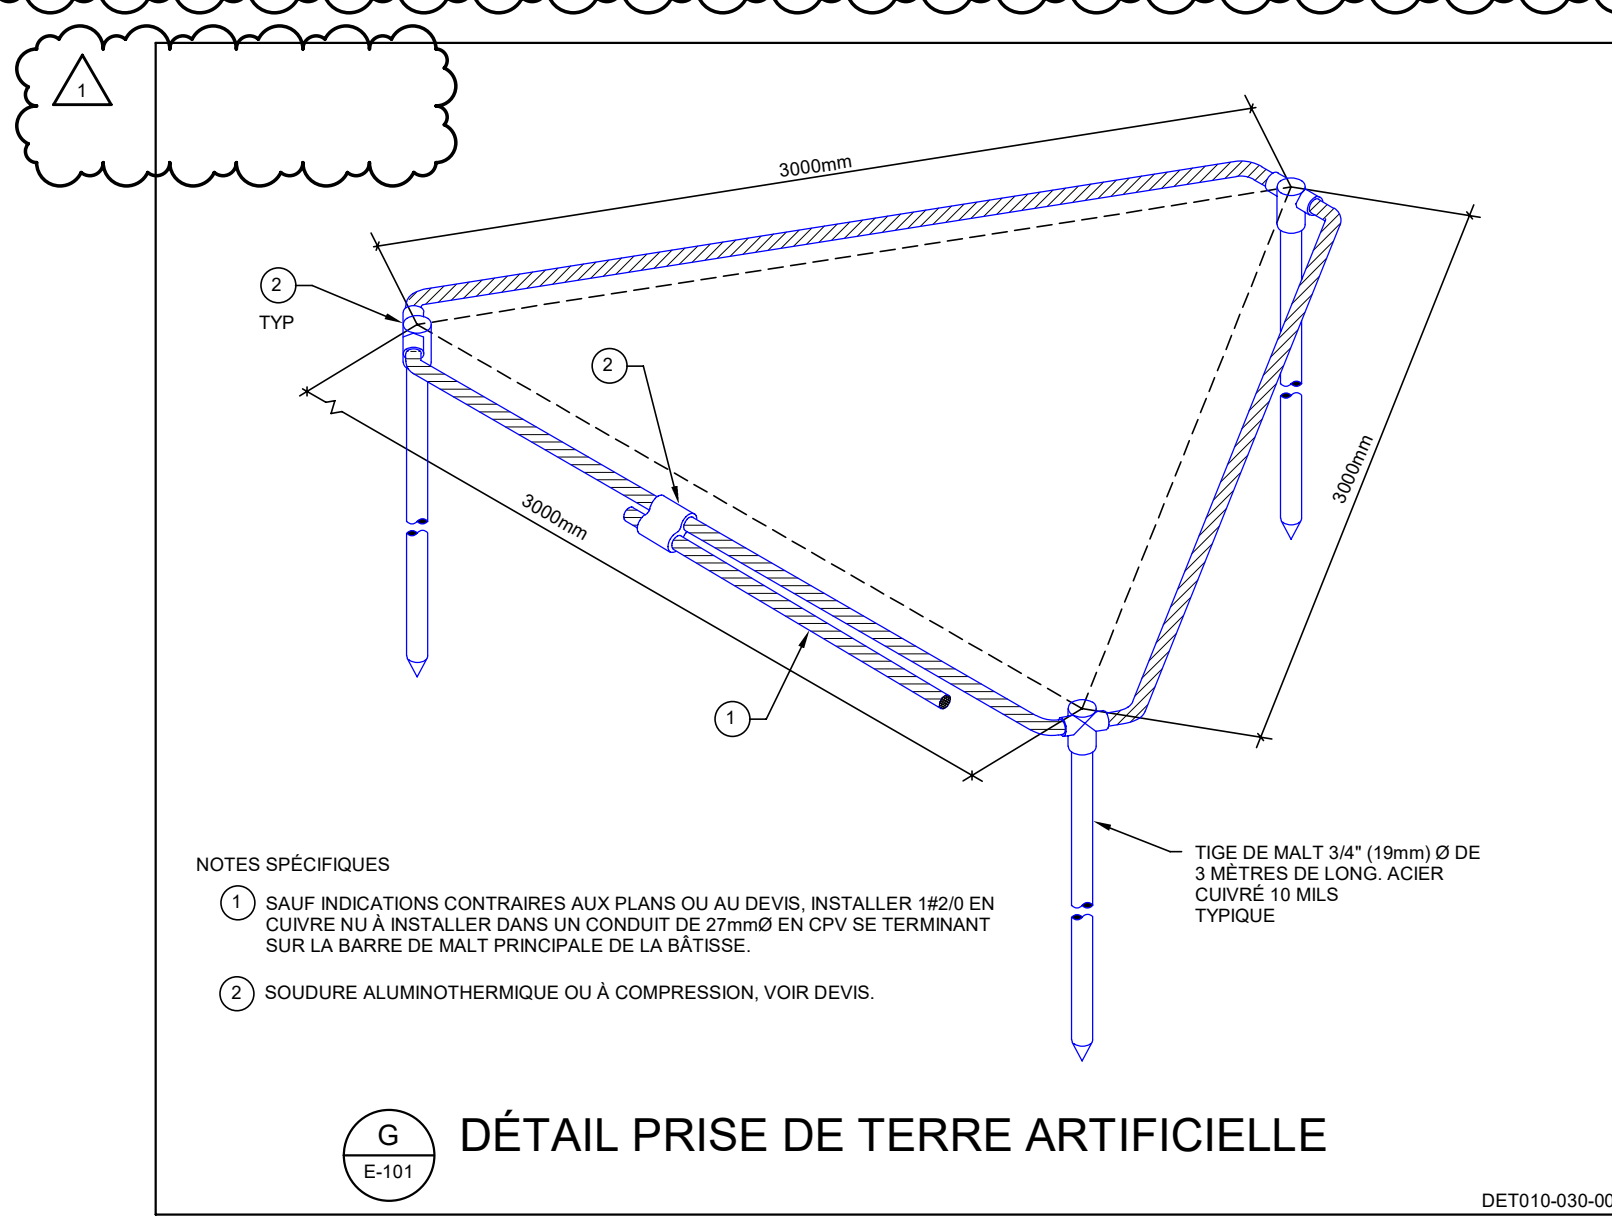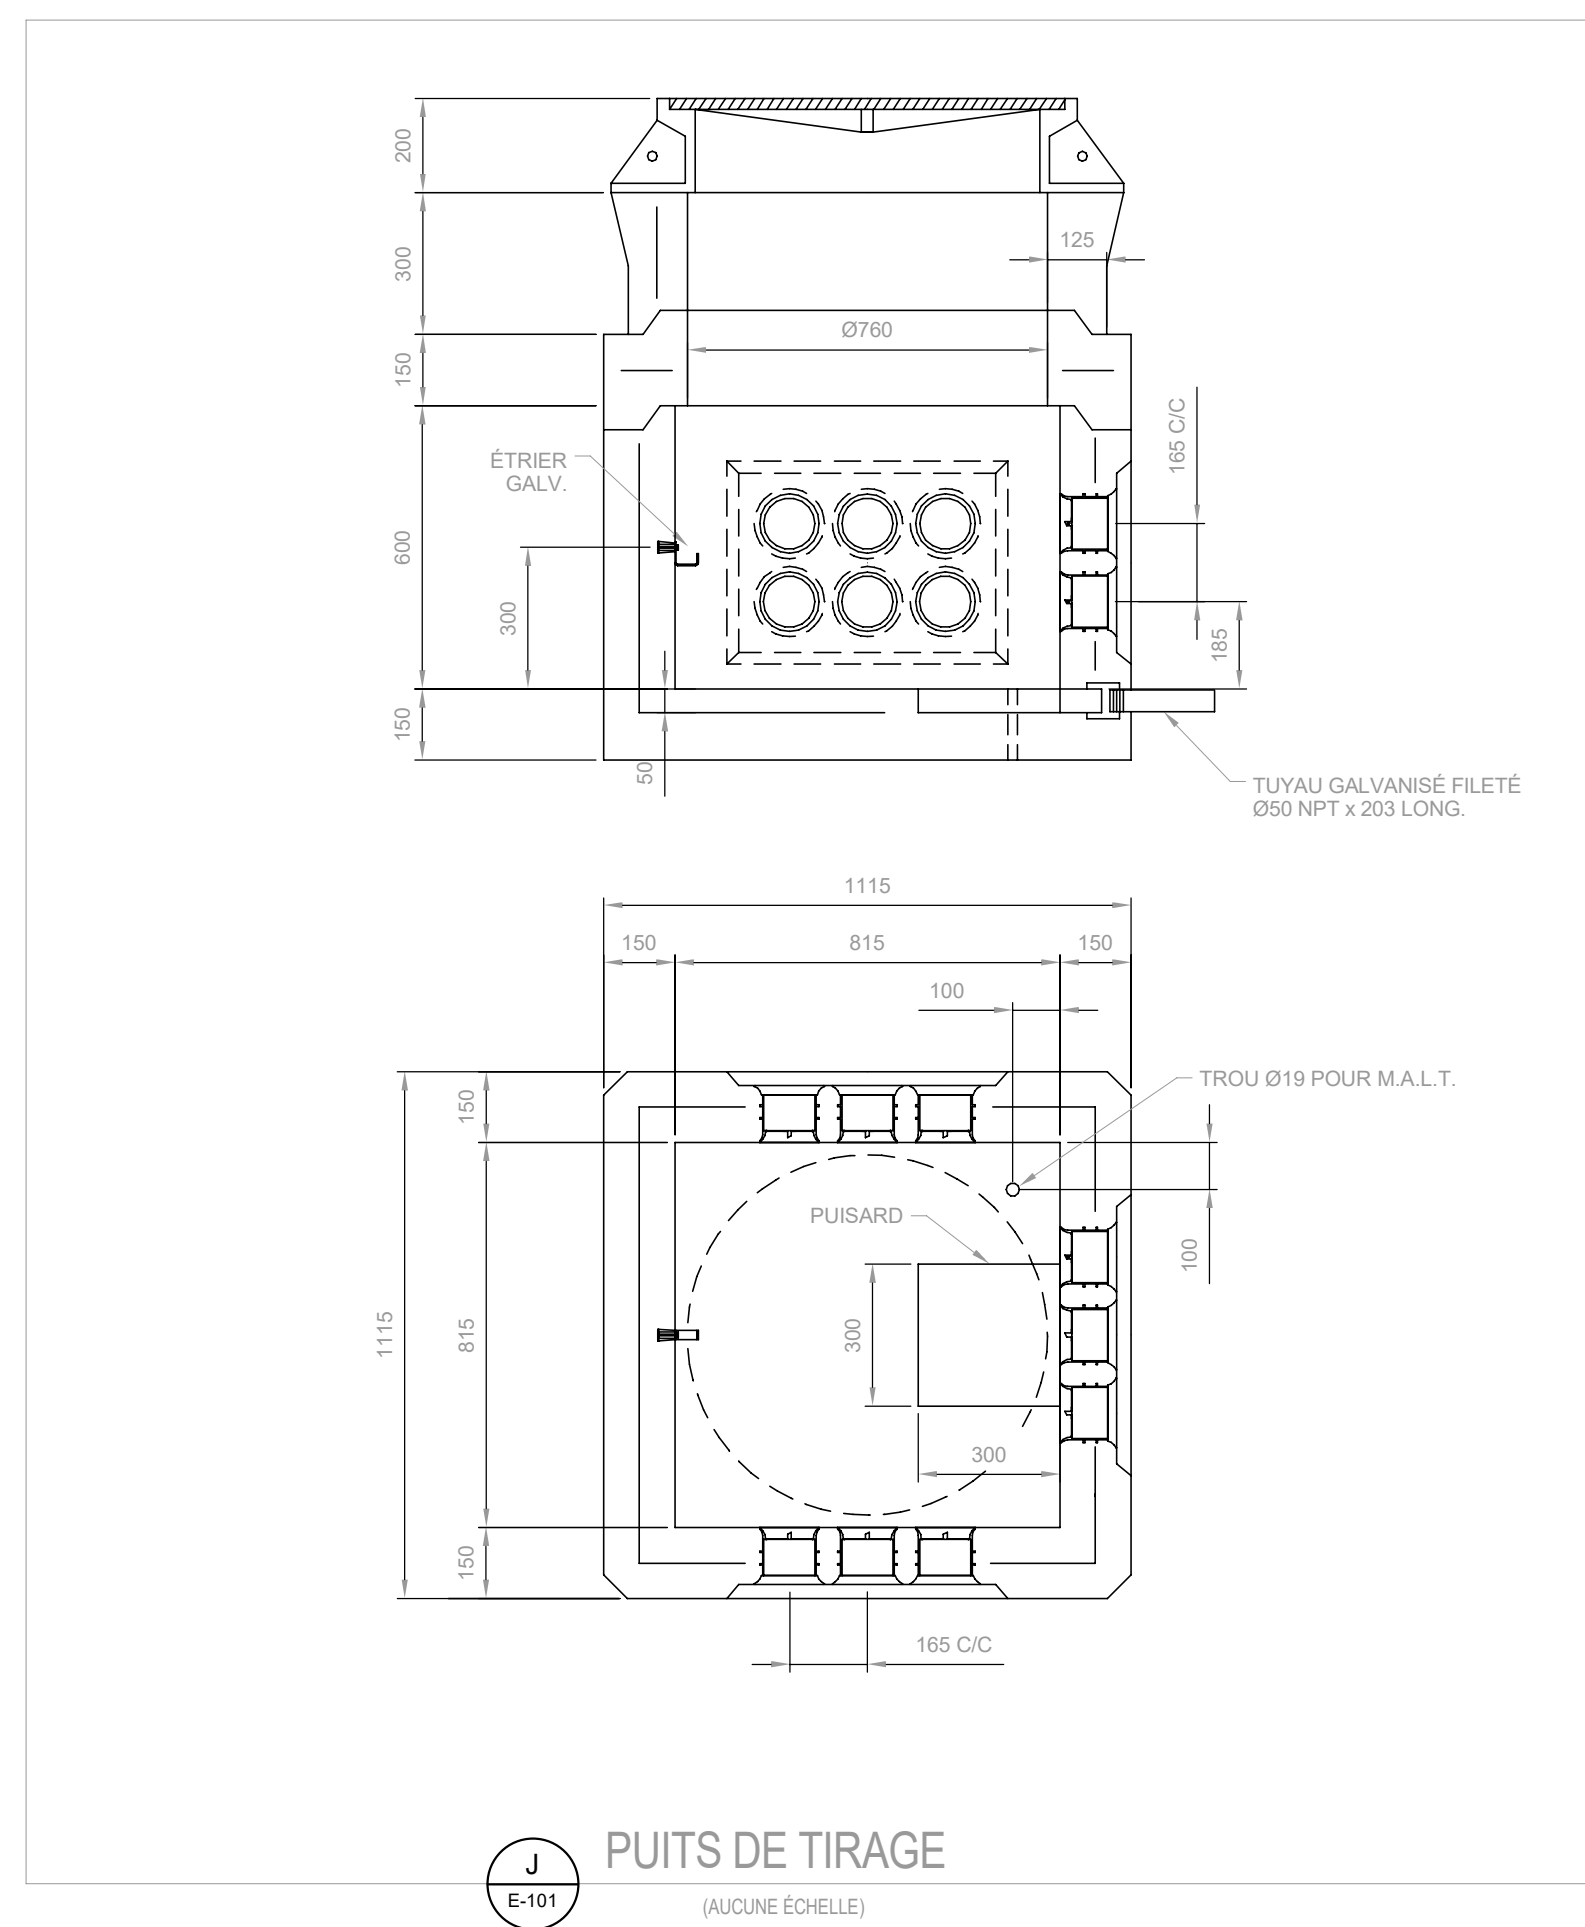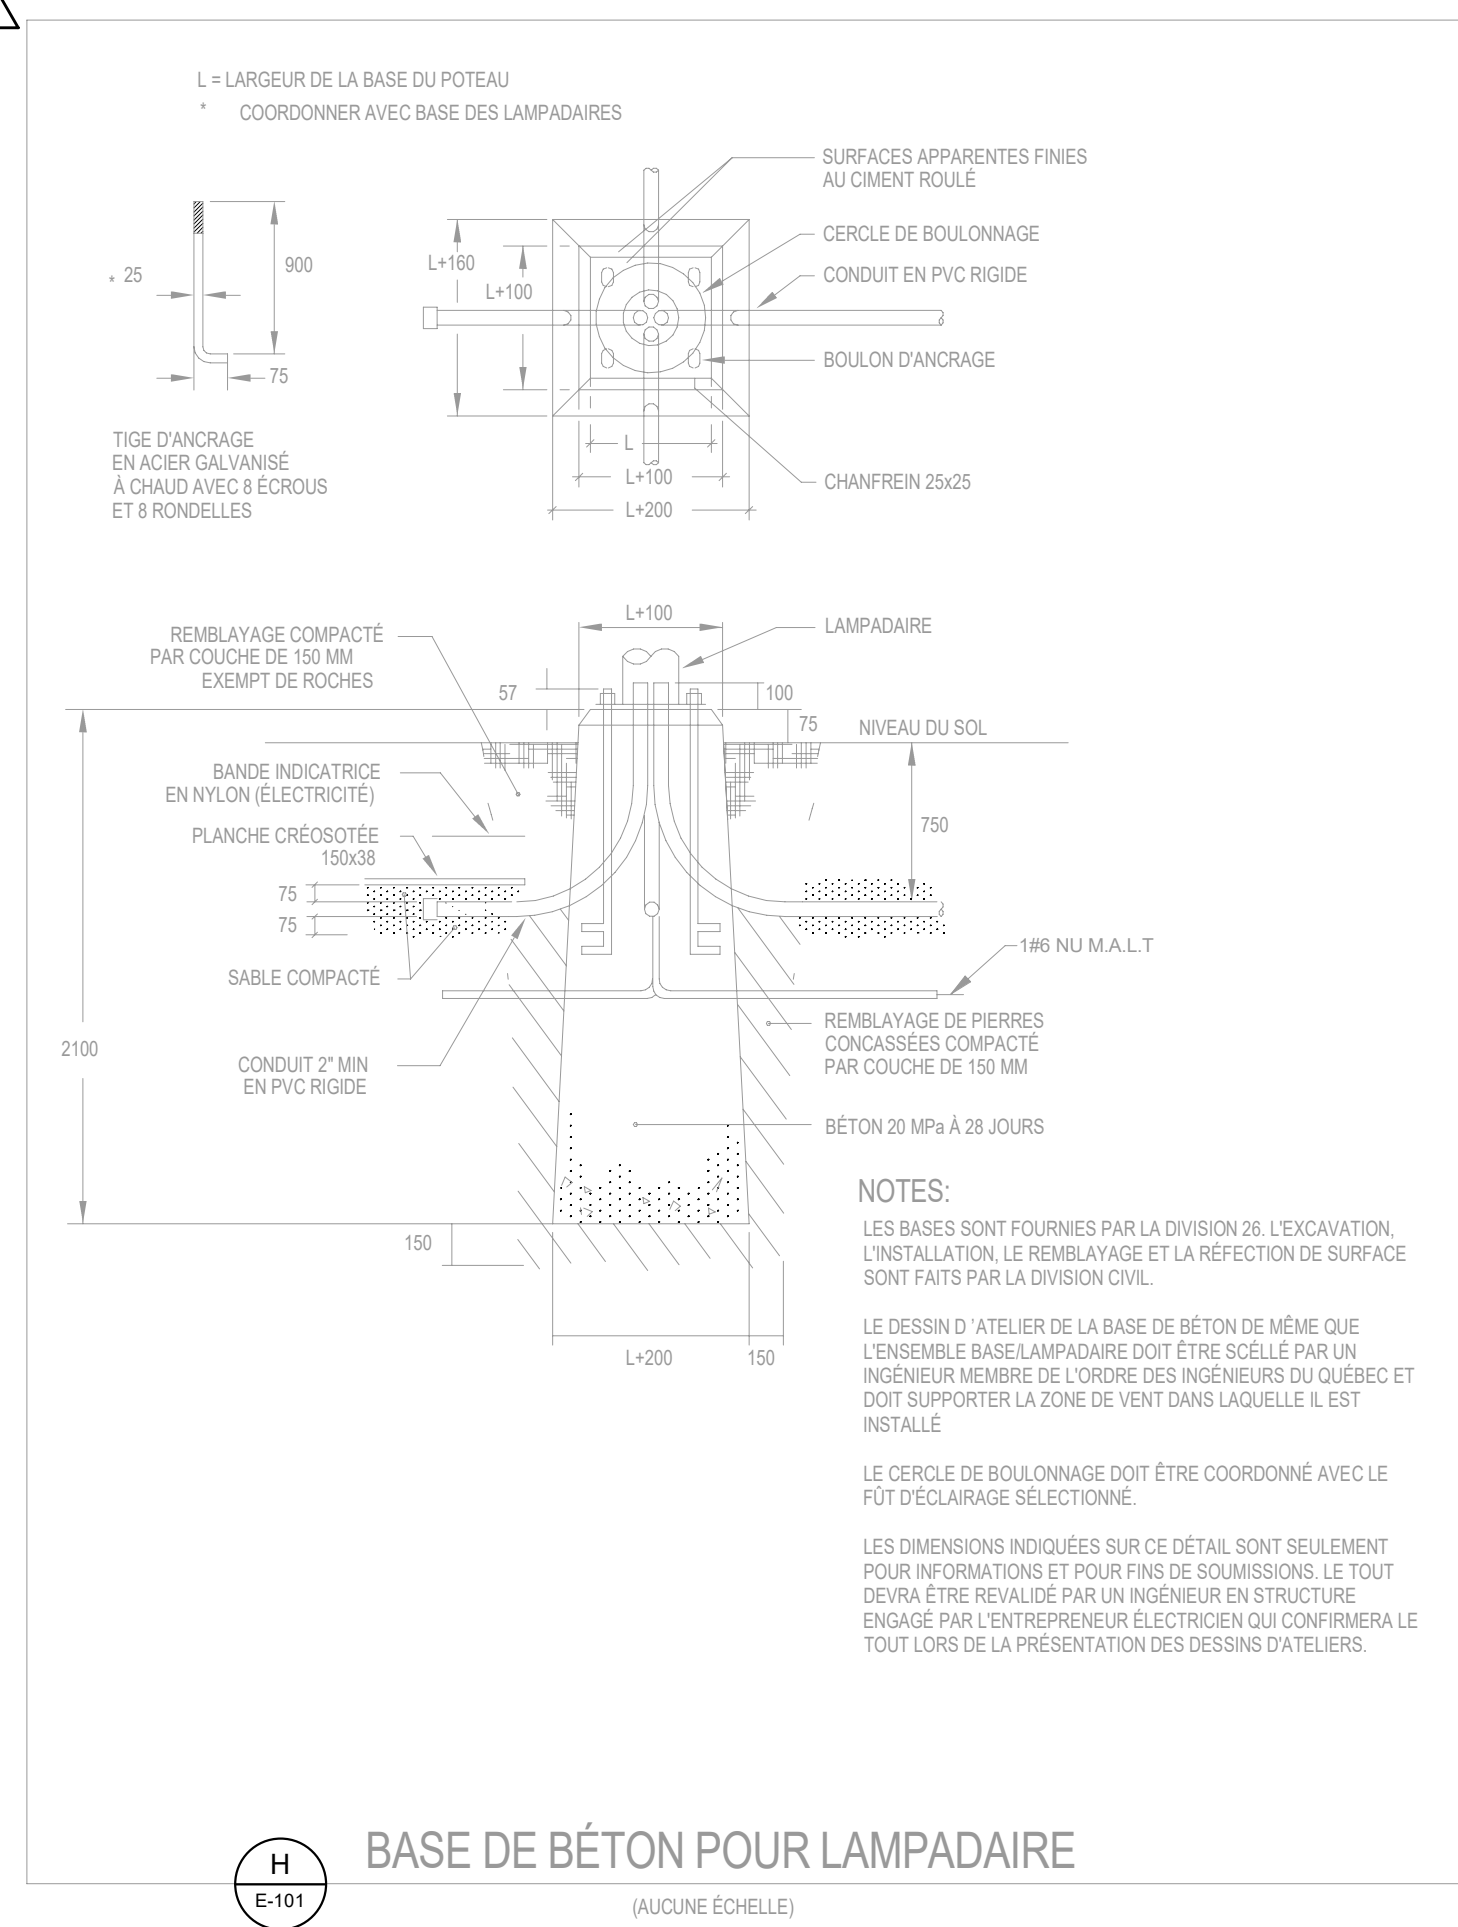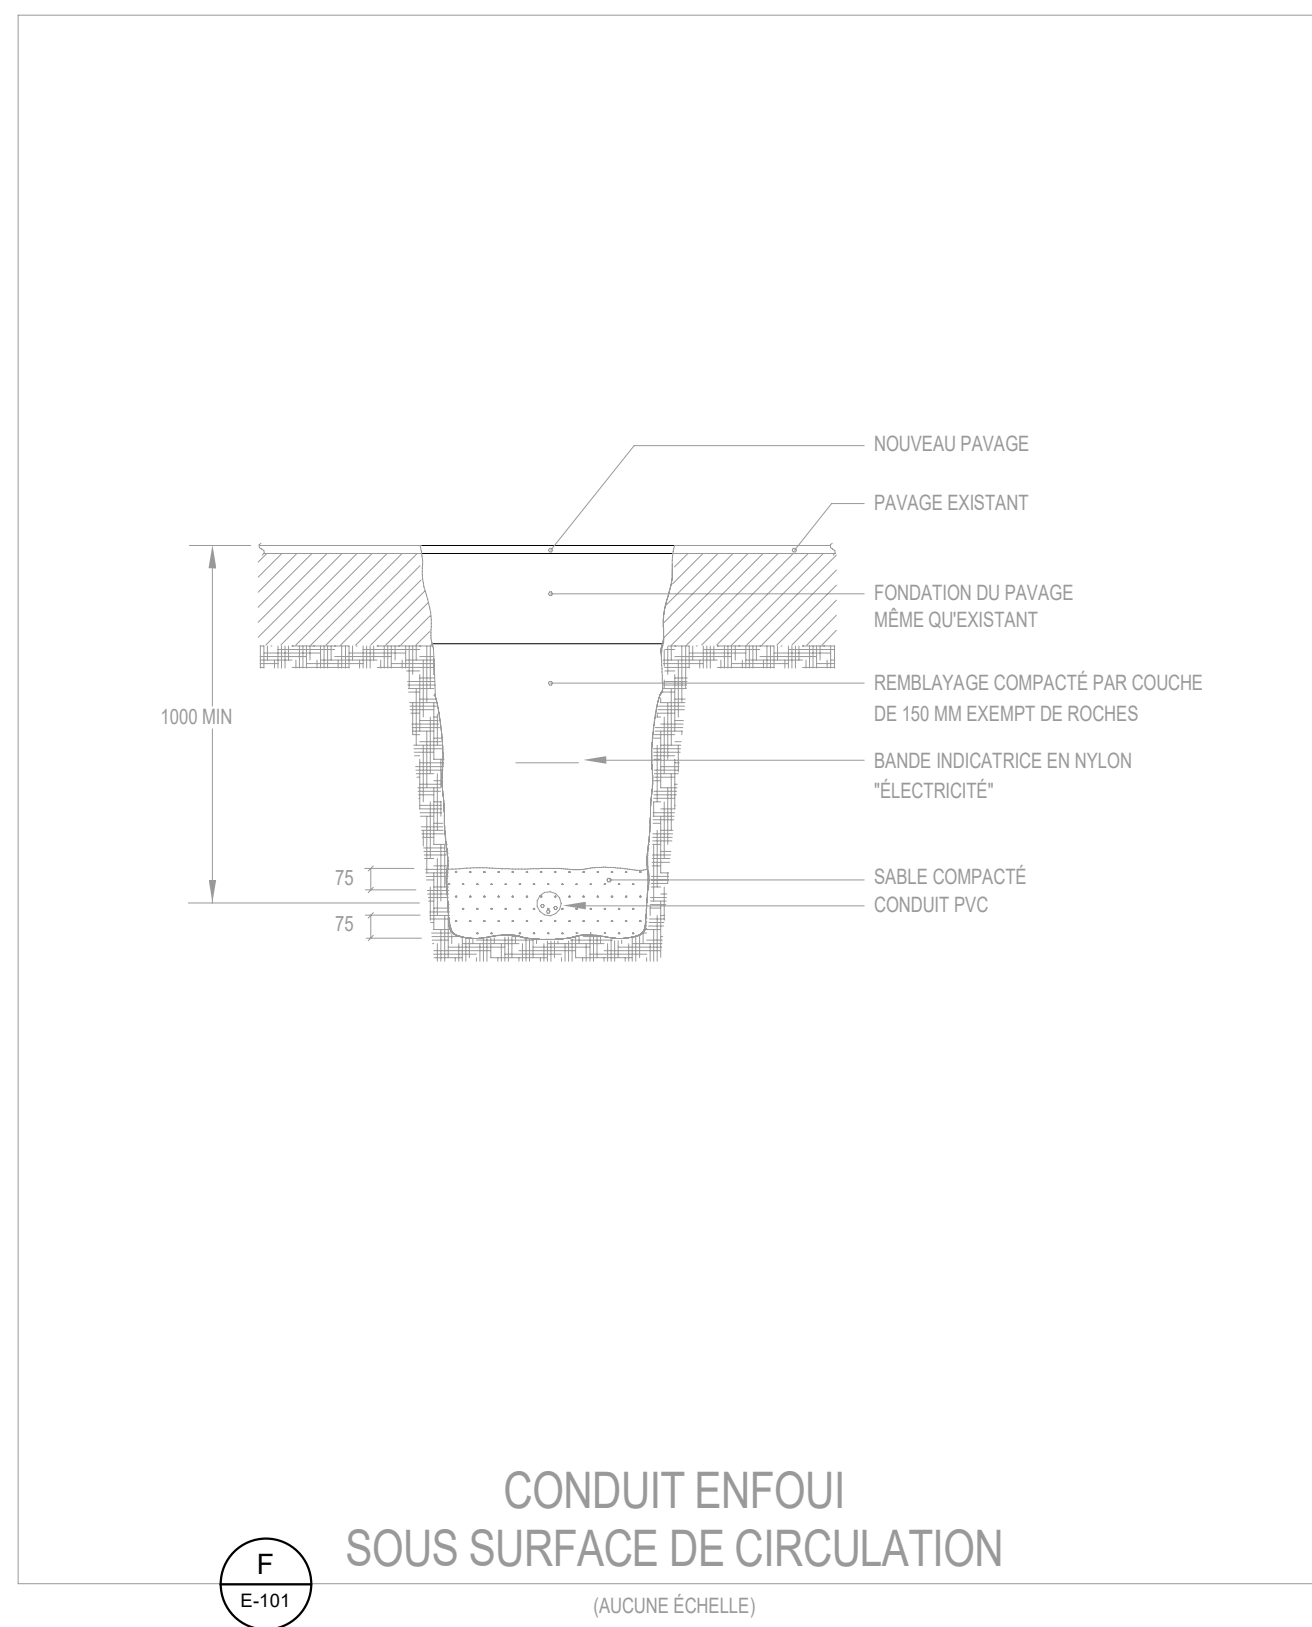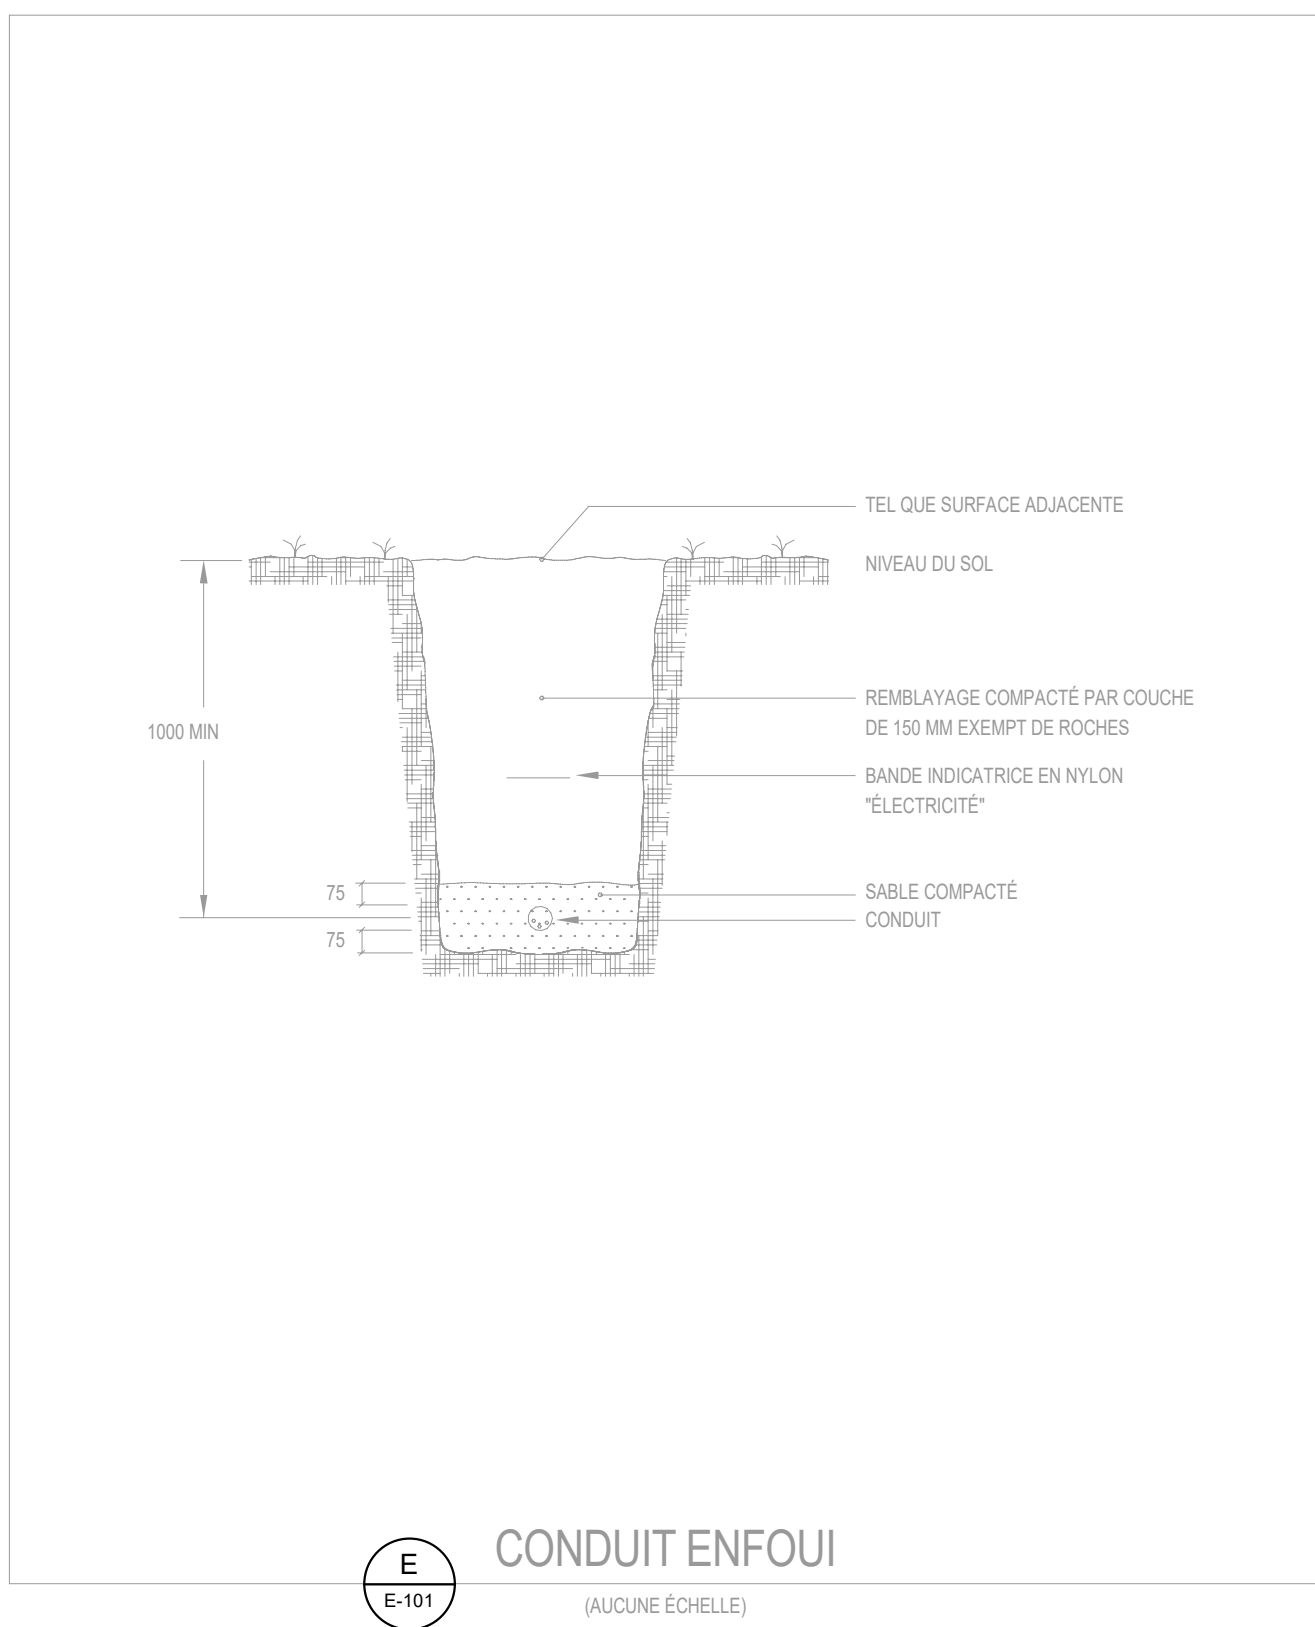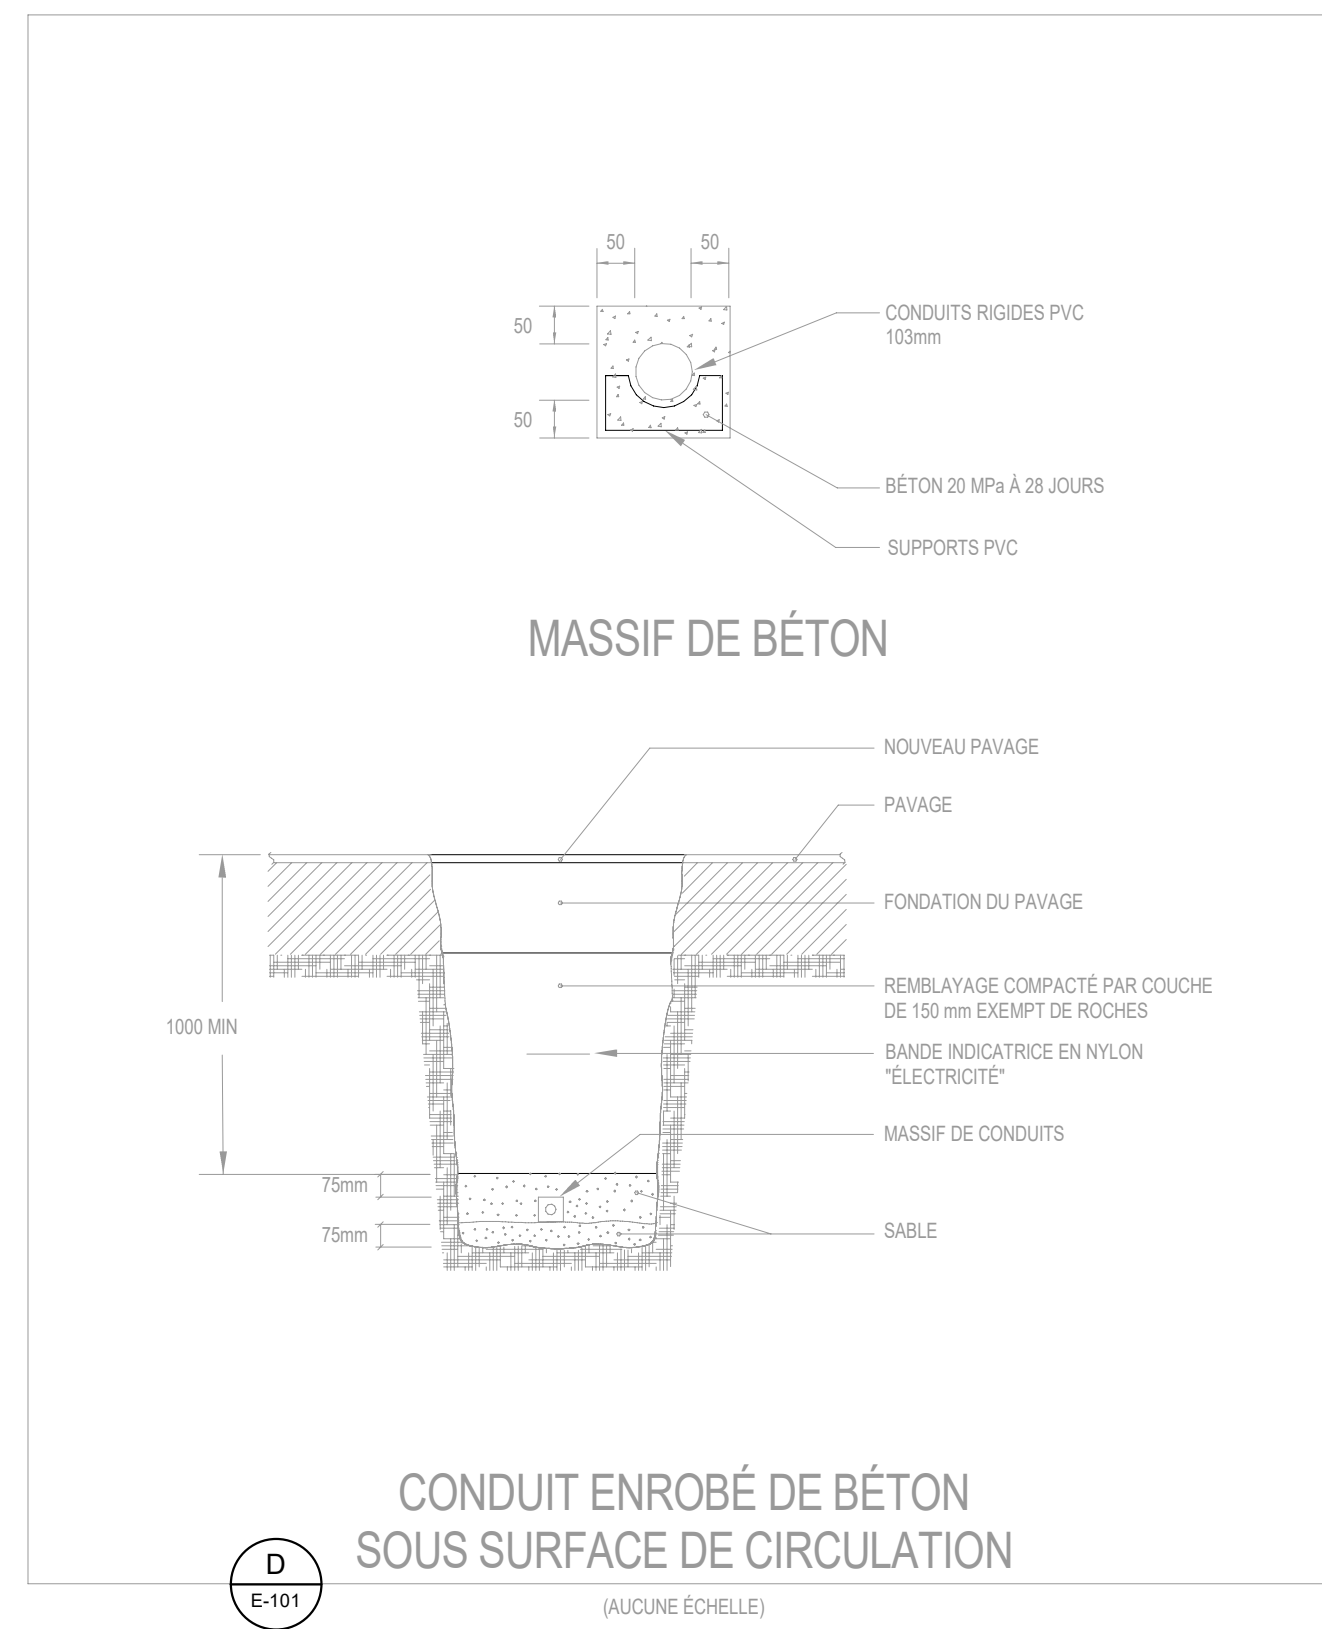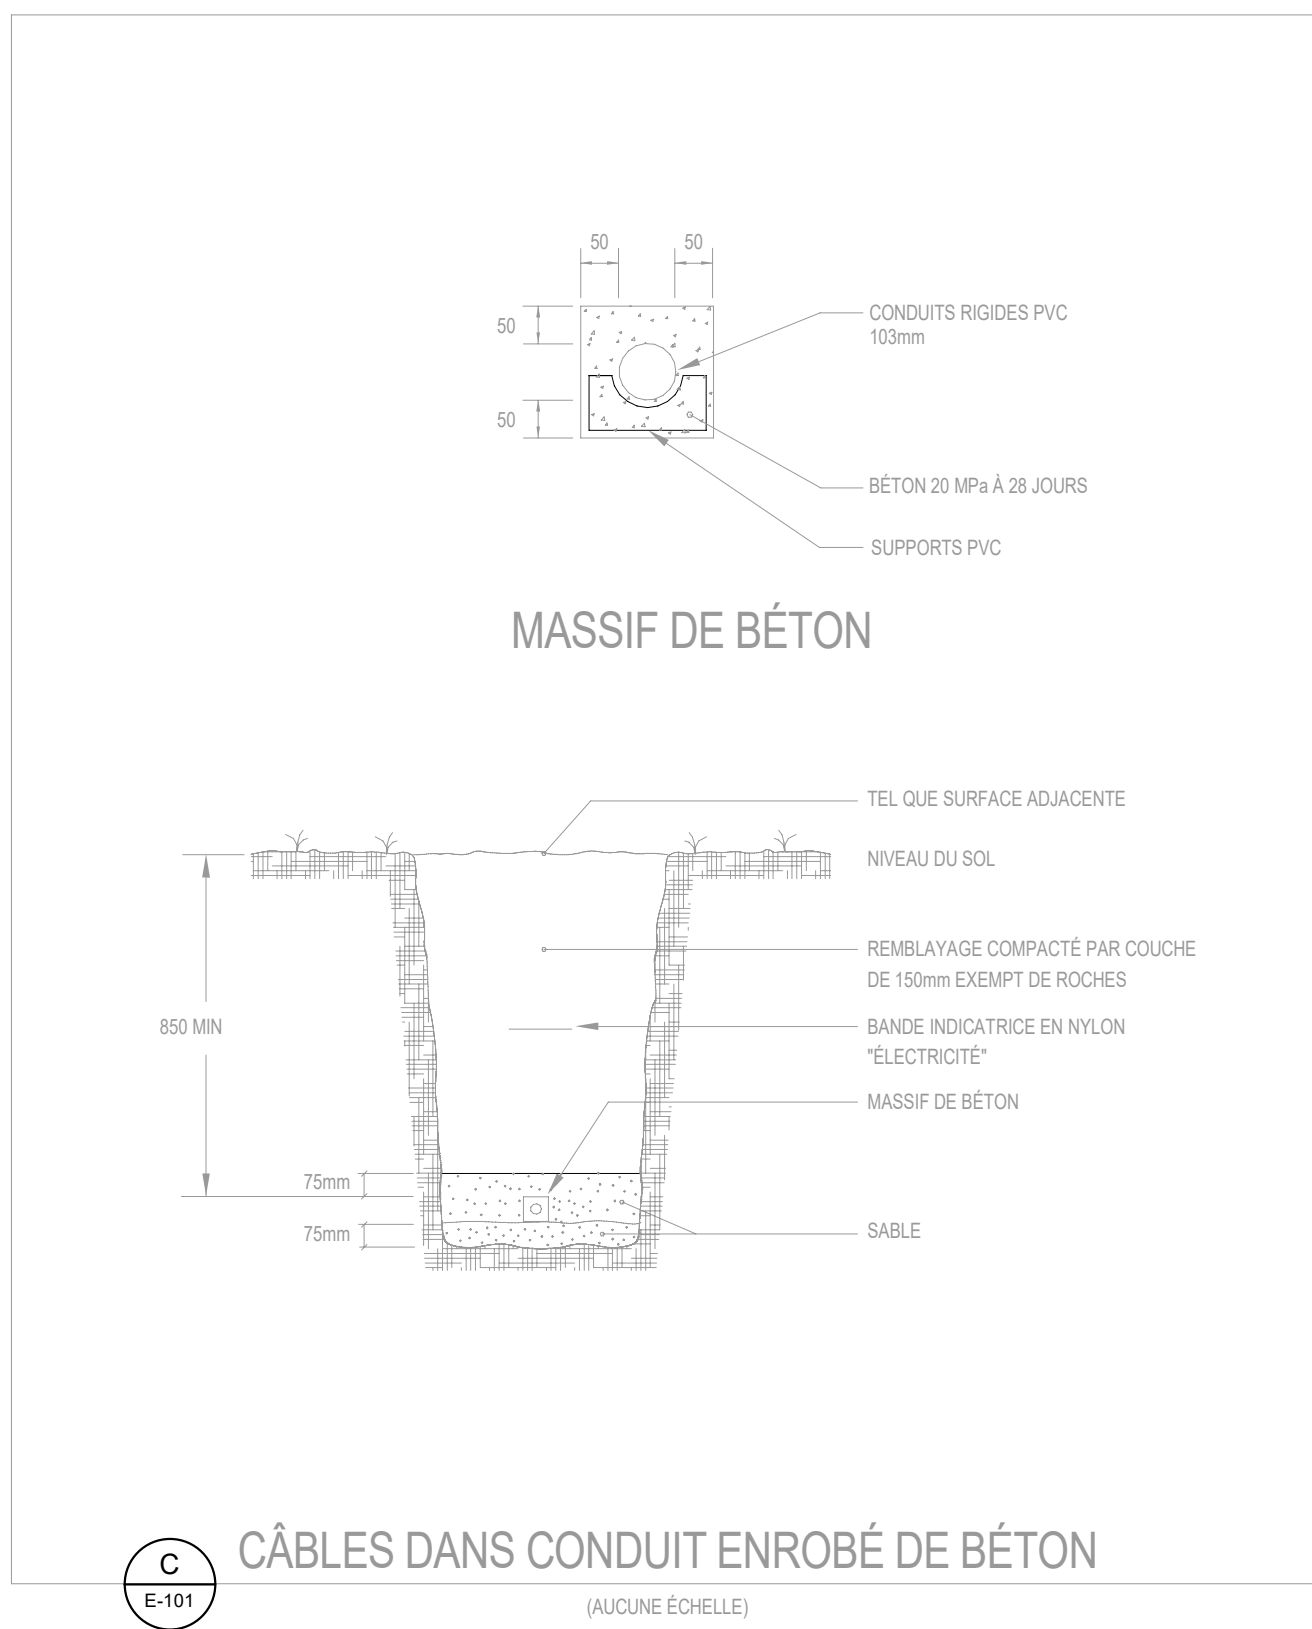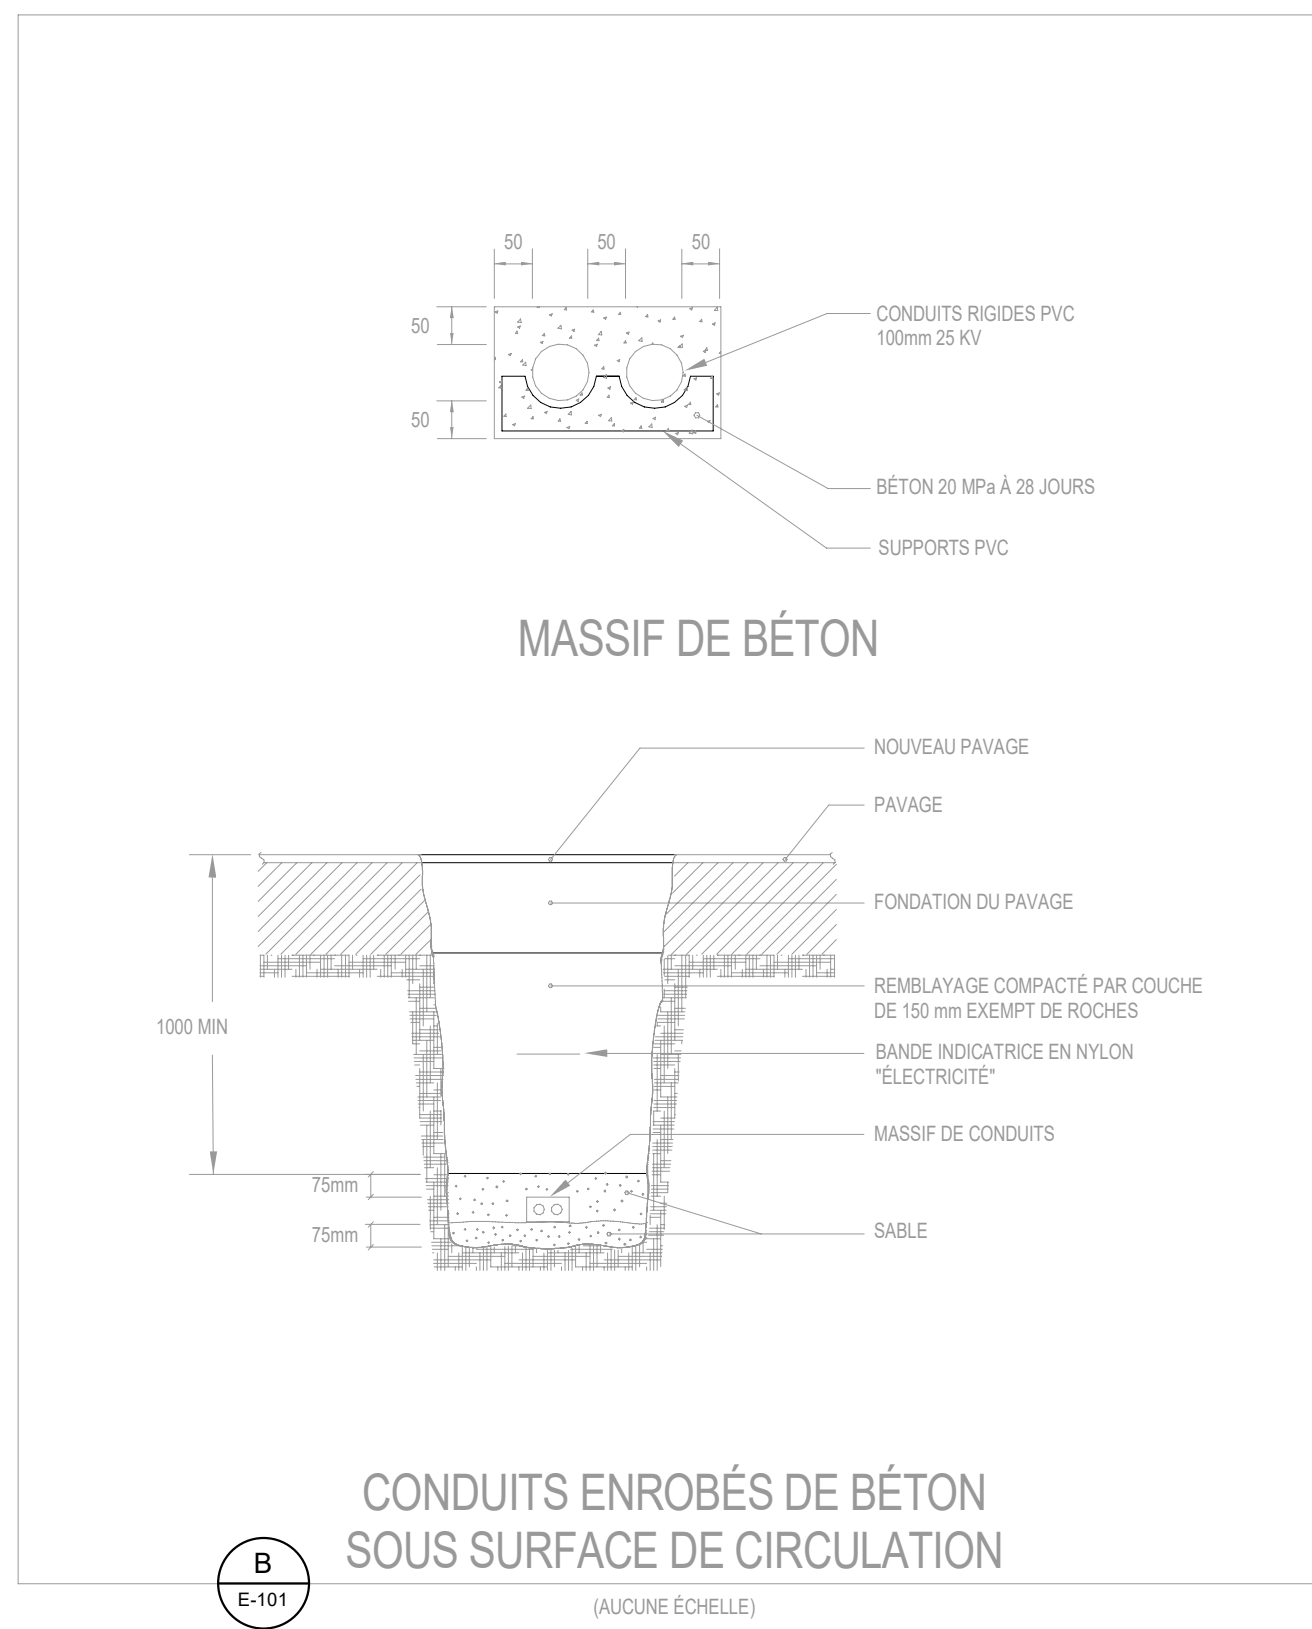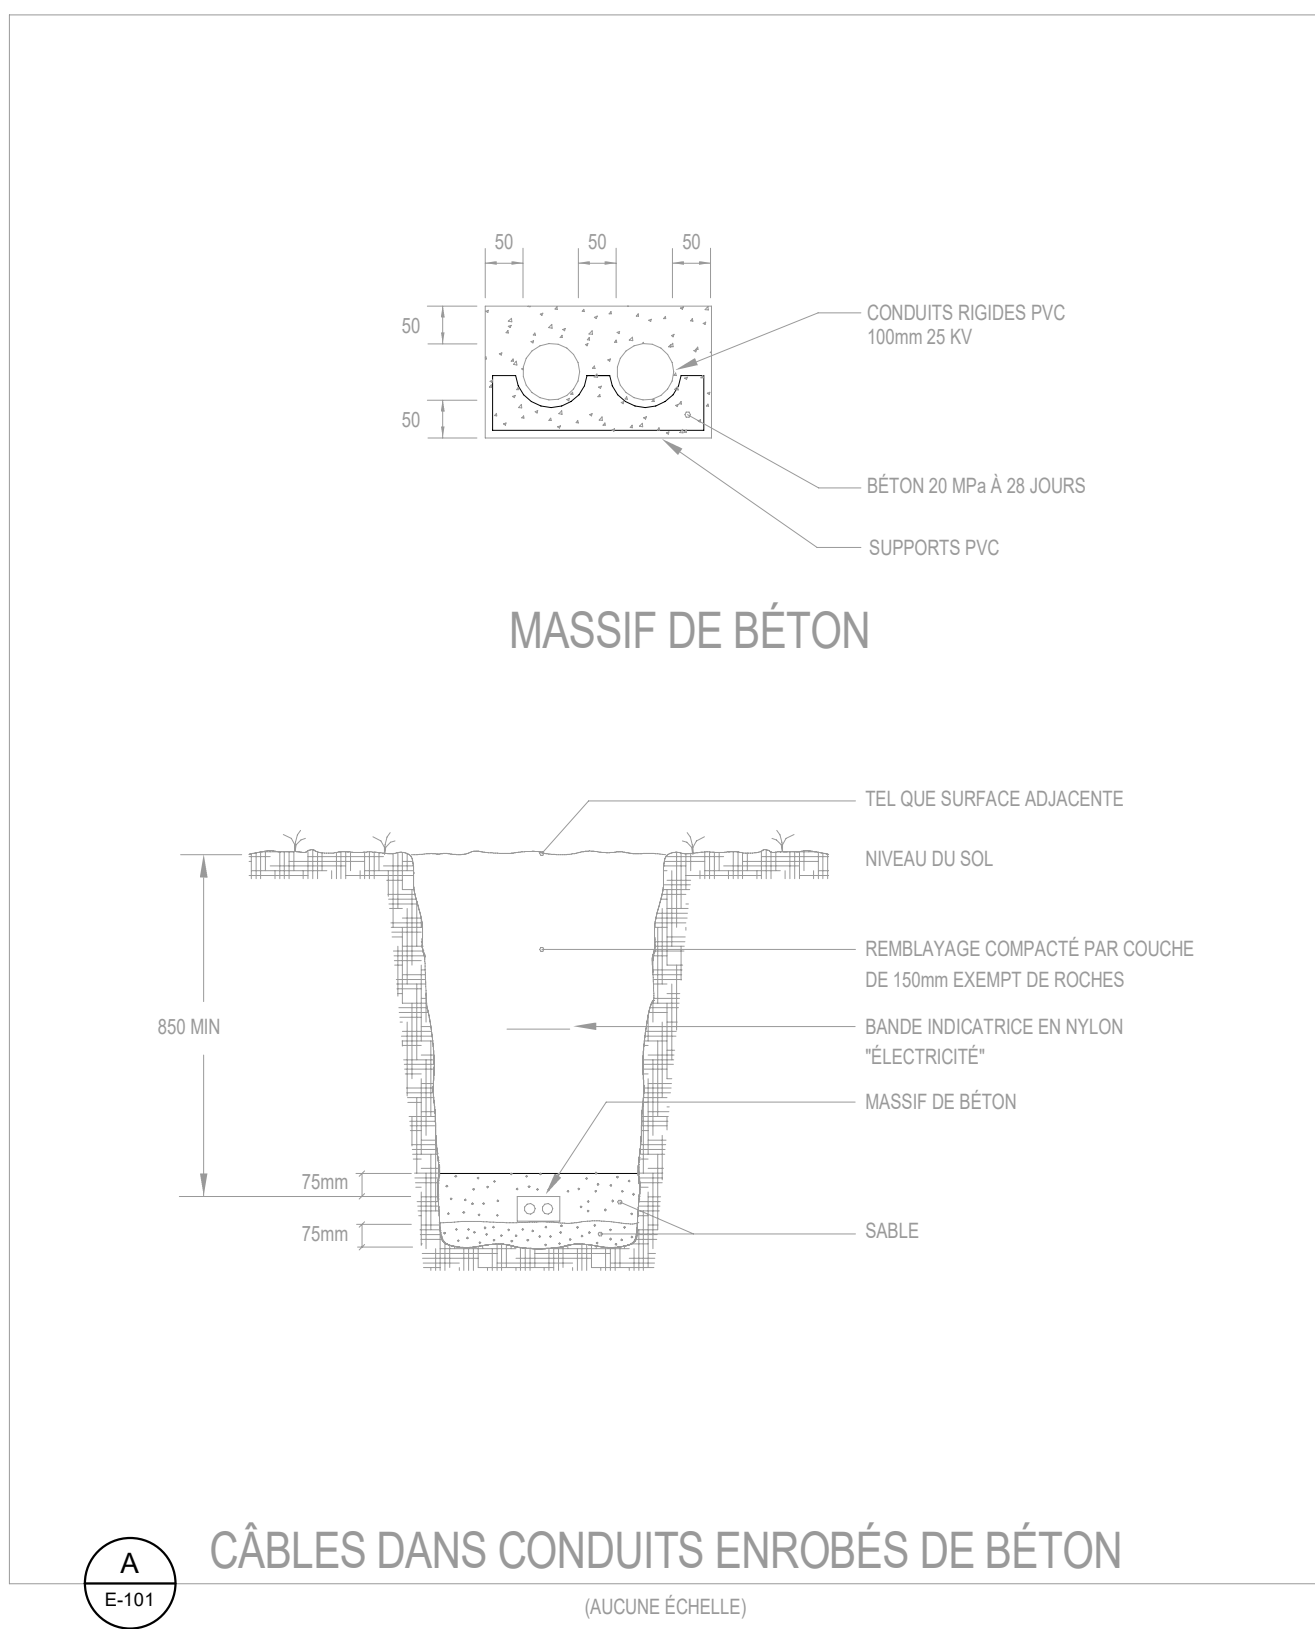

No.	Revisions	Date
1	POUR ADDENDA ELE-001	2026-03-02
0	POUR SOUMISSIONS	2026-02-06


CES DOCUMENTS NE DOIVENT PAS ÊTRE UTILISÉS À DES FINS DE CONSTRUCTION.

ÉLECTRICITÉ

Titre: Électricité
Echelle: NAE

ÉLECTRICITÉ GÉNÉRALE DÉTAILS ET TABLEAUX

Conçu par: D. DUSSAULT	Page
Dessiné par: M. GUAY	E-101
Vérifié par: D. DUSSAULT	DE
Dossier BPA: 25-13561	11
Dossier BBC: 25-1811	

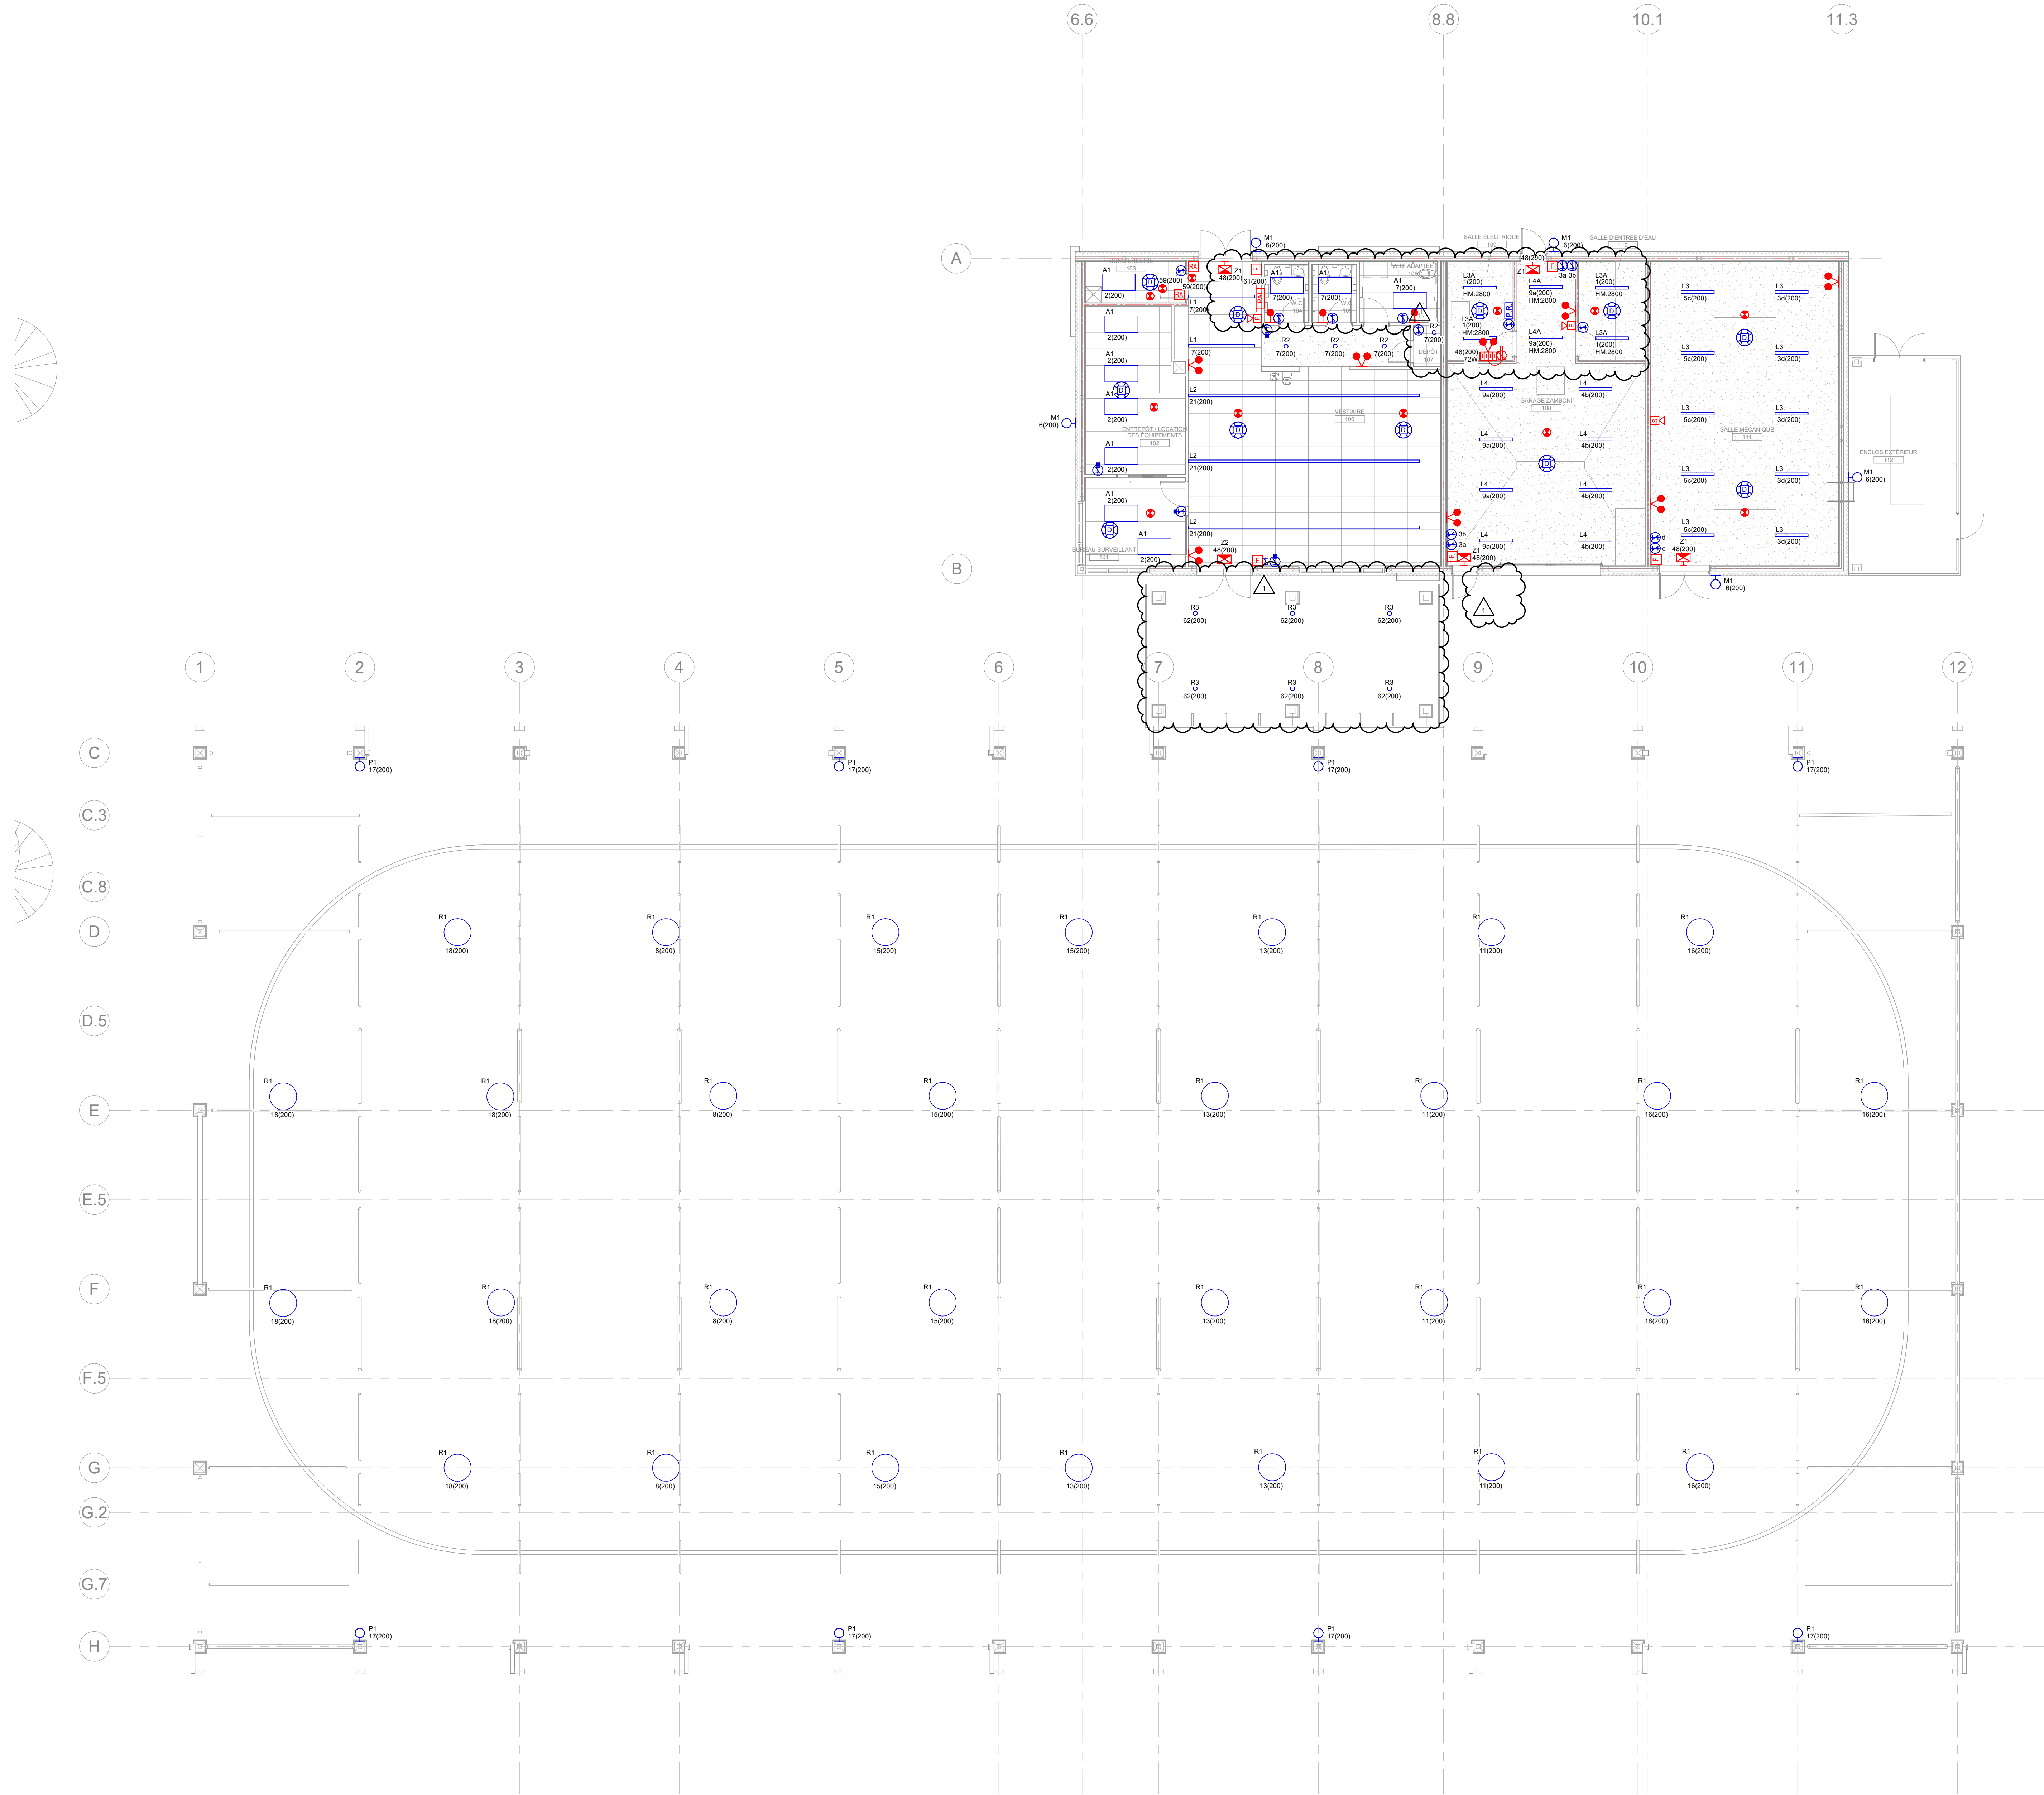

LÉGENDE DES COULEURS ÉLECTRICITÉ

LES PLANS DU PROJET DOIVENT ÊTRE CONSULTÉS EN COULEUR AUX FINS DE COMPRÉHENSION.

- RESEAU NORMAL
- SÉCURITÉ DES PERSONNES
- ALARME INCENDIE
- EXISTANT

Cliant:

VILLE DE SALABERRY-DE-VALLEYFIELD
61, RUE SAINTÉ-CECILE, SALABERRY-DE-VALLEYFIELD (QUÉBEC), J6T 1L8

CONSTRUCTION D'INFRASTRUCTURES SPORTIVES AU PARC LIONEL-GROULX
118, RUE MATHIAS, SALABERRY-DE-VALLEYFIELD (QUÉBEC), J6T 3J6

CHALET, PATINOIRE ET STATIONNEMENT

POUR ADDENDA ELE-001

Architectes:

BBC
architectes

1535, chemin Sainte-Foy, suite 120
Québec (Québec) G1S 2P1
418 684-5185
architectes@bbcarchitectes.ca

Ingénieurs mécanique / électrique:

BPA

Ingénieurs structure:

wsp

1105, BOULEVARD LEBOURNIEUF
QUÉBEC (QUÉBEC) CANADA G2N 0B8
TEL. 418 821-0241 / TÉLEX. 418 821-1071 / WWW.WSP.COM

Plan clé:

Scieur:

INGÉNIEUR
Stéphanie Rondeau
5063789
QUÉBEC

2026-03-01

No.	Revisions	Date
1	POUR ADDENDA ELE-001	2026-03-02
0	POUR SOUMISSIONS	2026-02-06

CES DOCUMENTS NE DOIVENT PAS ÊTRE UTILISÉS À DES FINS DE CONSTRUCTION.


ÉLECTRICITÉ

Titre: ÉLECTRICITÉ ÉCLAIRAGE ET ALARME INCENDIE NIVEAU 1

Échelle: 1 : 100

Conçu par: D. DUSSAULT
Dessiné par: M. GUAY
Vérifié par: D. DUSSAULT
Dossier BPA: 25-13561
Dossier BBC: 25-1811

Page **E-201** DE 11

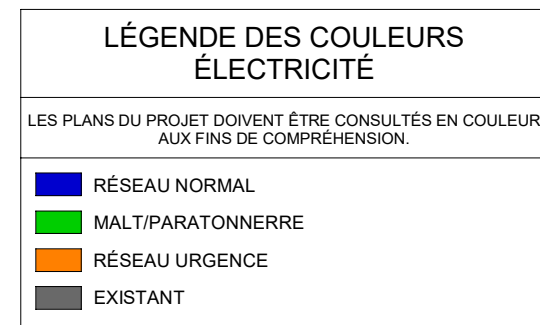

VILLE DE SALABERRY-DE-VALLEYFIELD

CONSTRUCTION D'INFRASTRUCTURES SPORTIVES AU PARC LIONEL-GROULX

118, RUE MATHIAS, SALABERRY-DE-VALLEYFIELD (QUÉBEC), J6T 3L6

1
 2
[illegible]

Architects

BBC
architectes
1535, chemin Sainte-Foy, suite
Québec (Québec) G1S 2P1
418 694-9185
architectes@bbcarchitectes.ca


Ingénieurs mécanique / électricité



Ingénieurs structure:



Plan clé:

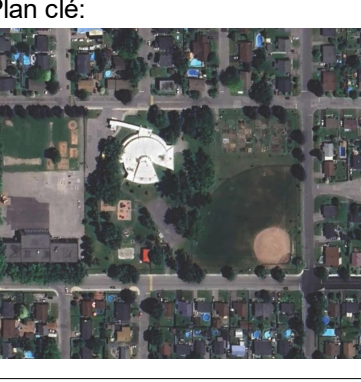

Sceau:

[illegible]

CES DOCUMENTS NE DOIVENT PAS
ÊTRE UTILISÉS À DES FINS DE
CONSTRUCTION.

ÉLECTRICITÉ

ÉLECTRICITÉ
SERVICES
NIVEAU 1

Conçu par: D. DUSSAULT	Page E-30
Dessiné par: M. GUAY	
Vérifié par: D. DUSSAULT	
Dossier BPA: 25-13561	
Dossier BBC: 25-1811	

-30

DE

—