
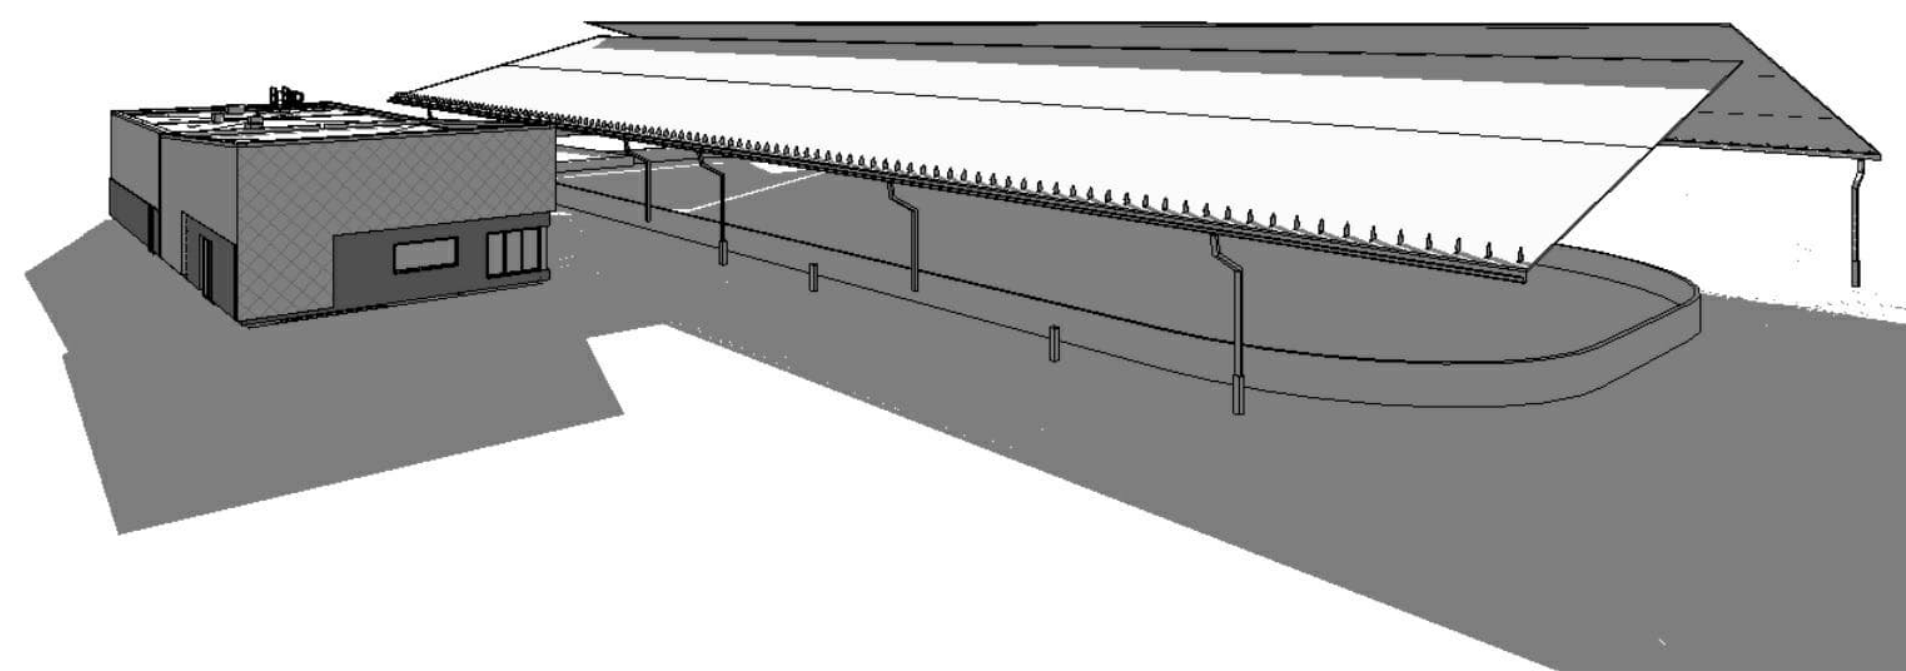


LISTE DES PLANS				
NO PLAN	DISCIPLINE	SOUS-DISCIPLINE	NOM PLAN	REVISION ACTUELLE
E-001	ELECTRICITE	GÉNÉRALE	PAGE FRONTISPICE	POUR SOUMISSIONS
E-002	ELECTRICITE	GÉNÉRALE	LEGENDE, FICHE DE PANNEAU ET SCHEMA UNIFILAIRE	POUR SOUMISSIONS
E-003	ELECTRICITE	GÉNÉRALE	DE DALLS ET TEGELAGE	POUR SOUMISSIONS
E-102	ELECTRICITE	GÉNÉRALE	PLAN IMPLANTATION	POUR SOUMISSIONS
E-101	ELECTRICITE	ÉCLAIRAGE ET ALARME INCENDIE	NIVEAU 1	POUR SOUMISSIONS
E-301	ELECTRICITE	SÉVICES	NIVEAU 1	POUR SOUMISSIONS

CONSTRUCTION D'INFRASTRUCTURES SPORTIVES AU PARC LIONEL-GROULX

CHALET, PATINOIRE ET STATIONNEMENT
VILLE DE SALABERRY-DE-VALLEYFIELD

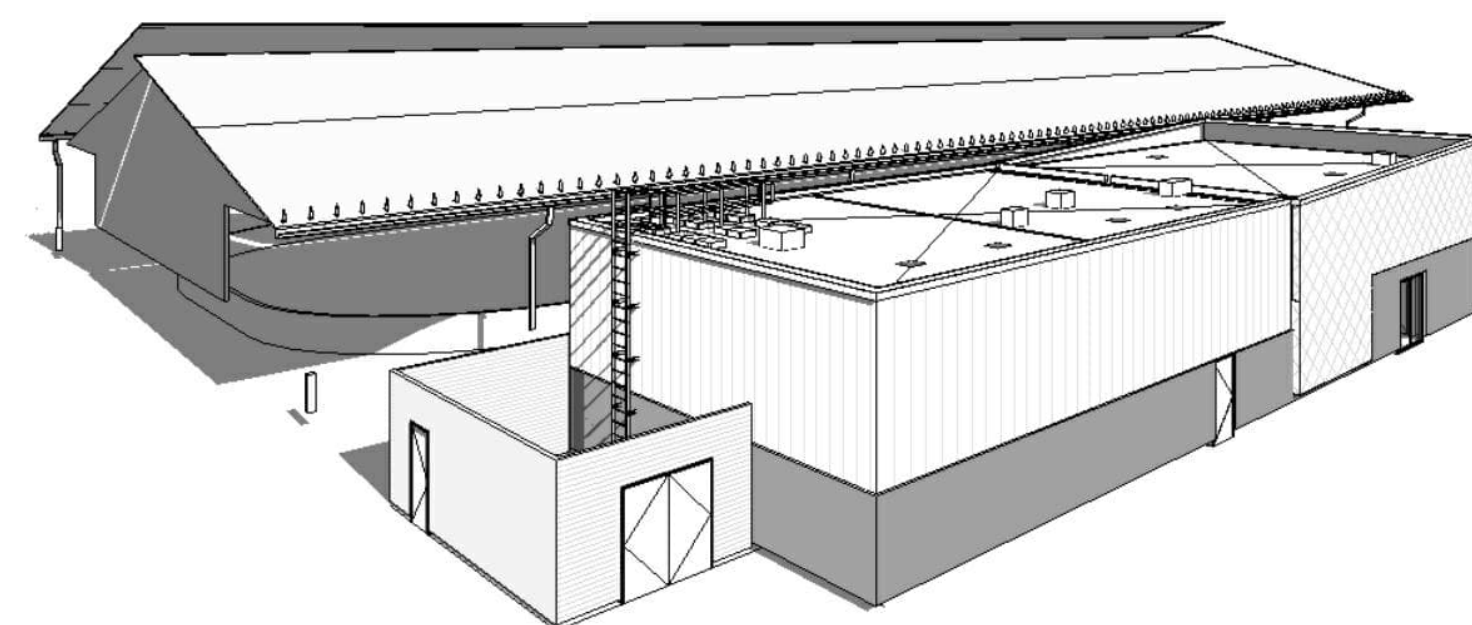

CES REPRÉSENTATIONS GRAPHIQUES SONT À TITRE INDICATIF ET PEUVENT VARIER DES PLANS. ELLES NE DOIVENT PAS SERVIR À L'ESTIMATION OU À LA RÉALISATION DU PROJET.

NOTE IMPORTANTE : CE DOCUMENT CONTIENT DES ÉLÉMENTS GRAPHIQUES QUI UTILISENT DIFFÉRENTES COULEURS POUR REPRÉSENTER DES ASPECTS SPÉCIFIQUES. LES COULEURS ONT ÉTÉ CHOISIES POUR DES RAISONS DE CLARTÉ ET DE COMPRÉHENSION. VEUILLEZ VOUS RÉFÉRER À LA LÉGENDE ET AUX ANNOTATIONS ASSOCIÉES POUR UNE INTERPRÉTATION CORRECTE DES COULEURS UTILISÉES. NOTEZ QUE CES COULEURS SONT REPRÉSENTÉES SUR LA VERSION NUMÉRIQUE DU DOCUMENT ET QU'UNE VERSION IMPRIMÉE PEUT DIFFÉRER.

POUR SOUMISSIONS

2026-02-06

ent:



61, RUE SAINTE-CÉCILE, SALABERRY-DE-VALLEYFIELD (QUEBEC), J6T 1L8

CONSTRUCTION D'INFRASTRUCTURES
SPORTIVES AU PARC LIONEL-GROULX

.....

CHALEI, PATINOIRE ET STATIONNEMENT


Architects:




Ingenieurs mécanique / électricité:




6700, boulevard Pierre-Bertrand, suite 300
 Québec (Québec) G2J 1R4
 418 614-9300

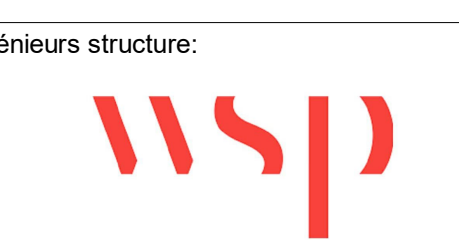

en clé:

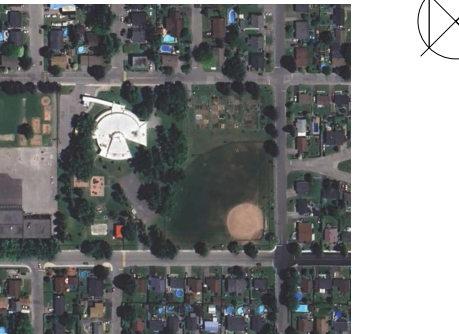

8U

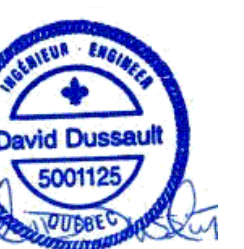

2026-02-09

[illegible]

CES DOCUMENTS NE DOIVENT PAS
ÊTRE UTILISÉS À DES FINS DE
CONSTRUCTION.




ELECTRICITÉ

3:


ELECTRICITÉ
GÉNÉRALE
PAGE FRONTISPICE

çu par: D. DUSSAULT	Page
siné par: M. GUAY	E-001
fié par: D. DUSSAULT	DE
sier BPA: 25-13561	15
sier BBC: 25-1811	


ÉCLAIRAGE

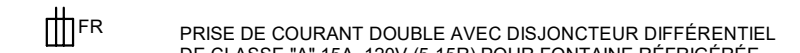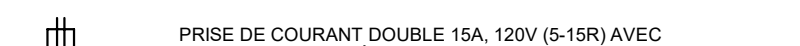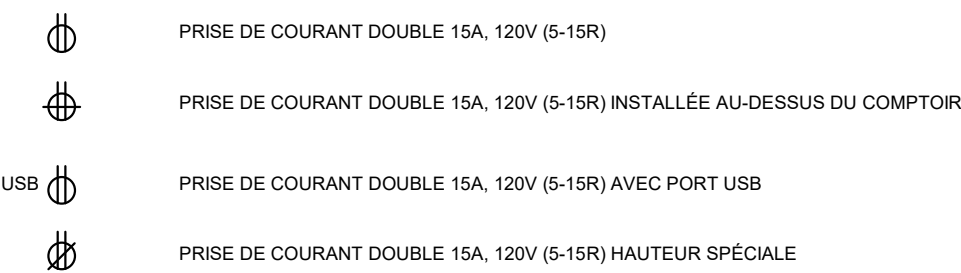


CHAUFFAGE

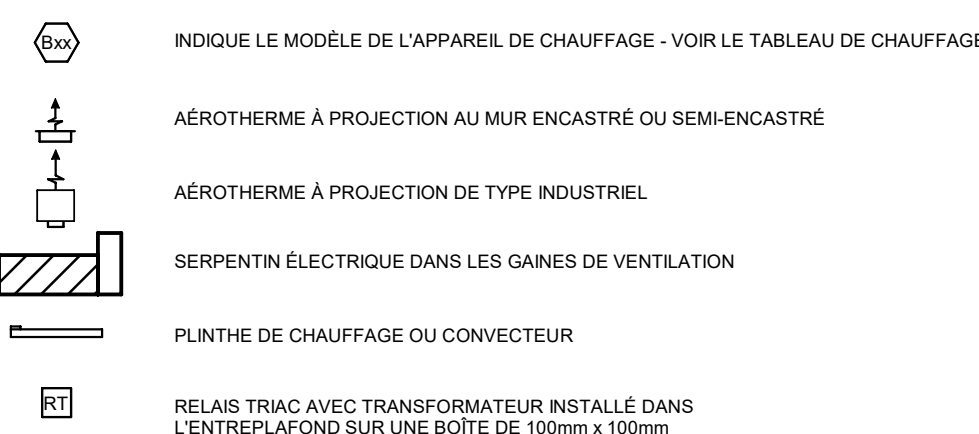


DISTRIBUTION ÉLECTRIQUE

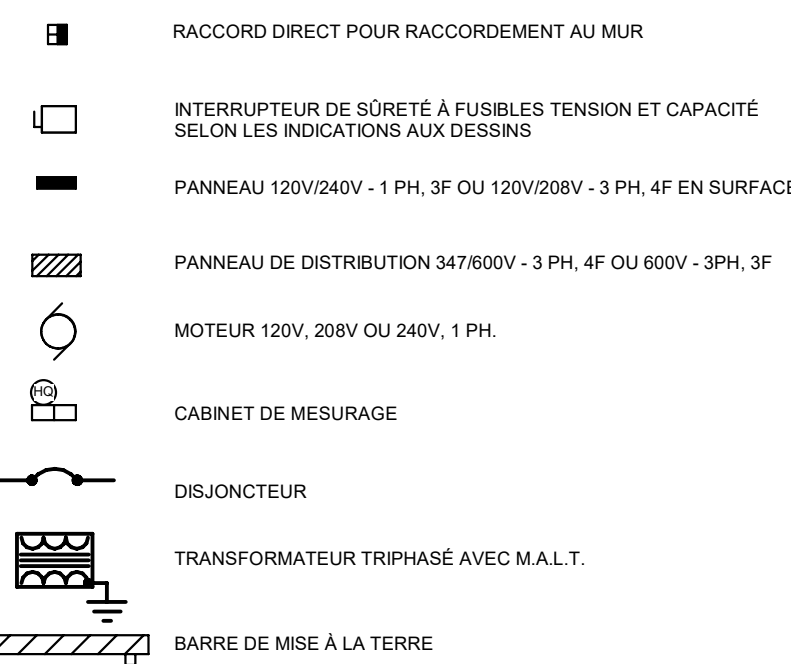


ALARME INCENDIE

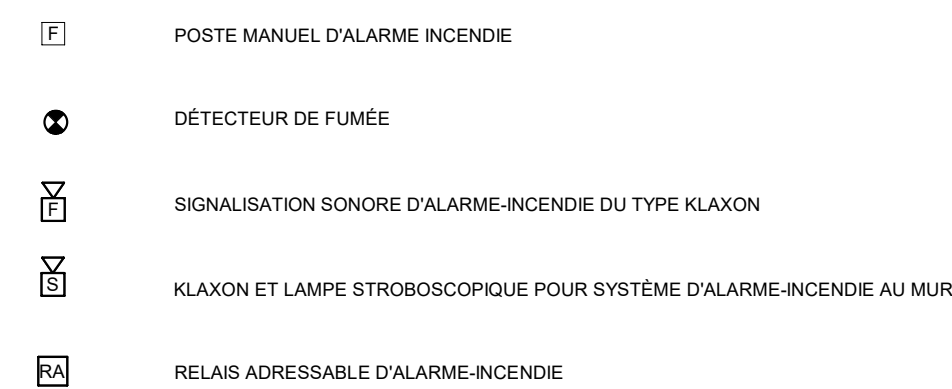

APPAREILS DIVERS

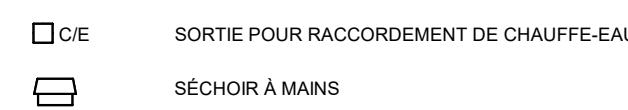

NOMENCLATURE

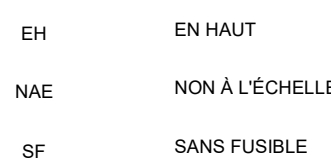

RC-PSNO-200(200)

Local: SALLE ELECTRIQUE 109

Tension: 120/208V

Type barres:

Alimenté: RC-TFNO-500

Phases: 3

Barres: 40' A

Niveau: NIVEAU 1


Fils: 4

Déjoncteur Maître:

Courant Rupture: 10kA

Note	Description	Djsj.	Poles	C C T	A	B	C	C C T	Poles	Djsj.	Description	Note	
	ECLAIRAGE 109 / 110	15A	1	1	125 VA	187 VA		2	1	15A	ECLAIRAGE 101 / 102 / 103		
	ECLAIRAGE SALLE MECANIQUE	15A	1	3		110 VA	504 VA	4	1	15A	ECLAIRAGE GARAGE		
	ECLAIRAGE SALLE MECANIQUE	15A	1	5				122 VA	258 VA	6	1	15A	ECLAIRAGE EXTÉRIEUR
	ECLAIRAGE ENTRÉE ET TOILETTES	15A	1	7	245 VA	476 VA		8	1	15A	ECLAIRAGE PATINOIRE		
	ECLAIRAGE GARAGE	15A	1	9		307 VA	600 VA	10	1	15A	PRISE FONTAINE RÉFRIGÉRÉE		
	ECLAIRAGE PATINOIRE	15A	1	11				476 VA	560 VA	12	1	15A	PRISES BUREAU 101
	ECLAIRAGE PATINOIRE	15A	1	13	686 VA	686 VA		14	1	15A	VA-01		
	ECLAIRAGE PATINOIRE	15A	1	15		686 VA	714 VA	16	1	15A	ECLAIRAGE PATINOIRE		
	PROJECTEURS	15A	1	17			660 VA	714 VA	18	1	15A	ECLAIRAGE PATINOIRE	
	PRISE PORTE DE GARAGE	15A	1	19	1000 VA	160 VA		20	1	15A	PRISE ENTREE D'EAU 110		
	ECLAIRAGE VESTIAIRE	15A	1	21		806 VA	1176 VA	22	1	15A	DEV01		
	VE-03 / VE-04	15A	1	23			1360 VA	180 VA	24	1	15A	PRISES TI	
	ECH01	15A	2	25	500 VA	500 VA		26					
				27		500 VA	500 VA	28					
	PRISE ENTRETIEN GARAGE	20A	1	29			160 VA	2099 VA	30				
	VE-01	15A	2	31	812 VA	2099 VA		32			20 A	COND-01	
				33		812 VA	606 VA	34					
	PRISES VESTIAIRE	15A	1	35			560 VA	606 VA	36	2	15A	VE-02	
	PRISE AQUISAGE DE PATIN	15A	1	37	100 VA	360 VA		38					
	PRISE SALLE ELECTRIQUE 109	15A	1	39		180 VA	180 VA	40	1	15A	PRISE CONCIERGERIE		
	PRISES GARAGE 108	15A	1	41			360 VA	540 VA	42	1	15A	PRISES SALLE MECANIQUE 111	
	PRISES ENTRETIEN VESTIAIRE	20A	1	43	360 VA	540 VA		44	1	15A	PRISES ETHIOPET 102		
	PRISES TI	15A	1	45		360 VA	360 VA	46	1	15A	PRISES GARAGE 106		
	SÈCHE-MAINS 106	15A	1	47			900 VA	82 VA	48	1	15A	ECLAIRAGE DE SECOURS	
	SÈCHE-MAINS 104	15A	1	49	600 VA	300 VA		50	1	15A	RFCR-01		
	PRISES EXTÉRIEURE	15A	1	51		540 VA	600 VA	52	1	15A	SÈCHE-MAINS 105		
				53				1037 VA	0 VA	54	1	15A	RÉGULATION
	BOTIER CAMLOCK	15A	3	55	1627 VA	0 VA		56	1	15A	RÉGULATION		
				57		1627 VA	606 VA	58					
	RCFM	15A	1	59			200 VA	606 VA	60	2	15A	VA-02	
				61				62					
				63				64					
				65				66					
				67				68					
				69				70					
				71				72					
Total Charge:						25346 VA	26008 VA	26278 VA					
Total Courant :						211 A	218 A	220 A					
								Total du panneau					
								Charge totale raccorder: 7761 VA					
								Courant total raccorder: 216 A					

Notes:







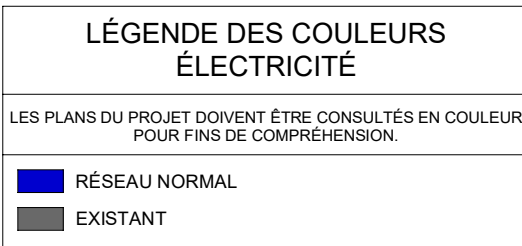


TABLEAUX DES LUMINAIRES									
IDENTIFICATION	MARQUE	MODELE	TYPE DE MONTAGE	LAMPE	TEMPERATURE COULEURS	LUMENS	DONNÉES ÉLECTRIQUE		REMARQUES
							PUISSANCE	TENSION	
R1	COOPER LIGHTING	2KCECT3-LVW-LW-300K	ENCASTRE	DEL	3000 K	3737 lm	24 VA	120 V	
D1	COOPER LIGHTING	GH-L-SAR-320-LU-14W	ENCASTRE	T-3	0 K	0 lm	82 VA	247 V	
L1	AXIS	BBULED-500-40-35-F-L-8	ENCASTRE	DEL	3000 K	3000 lm	78 VA	120 V	
L2	AXIS	BBULED-500-40-35-F-L-28	ENCASTRE	DEL	3000 K	33000 lm	289 VA	120 V	
L3	COOPER LIGHTING	48W-4-TSL-UV-LVW-L-BA-CD	SURFACE	DEL	4000 K	3976 lm	38 VA	120 V	
L4	COOPER LIGHTING	4V73-L-DS-6-G-UNV-LBAP-CD-L-U	SURFACE	DEL	4000 K	2000 lm	51 VA	120 V	
M1	COOPER LIGHTING	DWG-SAVA-850-LU-14W	AU MUR	DEL	3000 K	2627 lm	34 VA	120 V	
P1	REL	CZM-LVW-RGBW-8W-81	SUR COLONNE	DEL	0 K	2000 lm	80 VA	120 V	
R1	COOPER LIGHTING	UHES-1218-M-L-850-L	SUSPENDU	DEL	4000 K	18867 lm	119 VA	120 V	
R2	COOPER LIGHTING	RAIL-8P-502W-1E1W40M	ENCASTRE	DEL	3000 K	800 lm	6 VA	120 V	

CARACTÉRISTIQUES DES APPAREILS DE CHAUFFAGE

NOTES:

IDENTIFICATION	DESCRIPTION	MARQUE	MODELE	ENCASTRE	CONTRÔLE		TENSION	DONNÉES ÉLECTRIQUE		REMARQUES
					TYPE	INTÉGRÉ		PHASE	PUISSANCE (W)	
A15	AÉROTHERME MURAL	STELPRO	WFA15032GW	Oui	RELAS	Oui	347 V	1	1500 W	
B5	PLINTHE	STELPRO	B5030W	Non	RELAS	Non	347 V	1	500 W	
B10	PLINTHE	STELPRO	B10030W	Non	RELAS	Non	347 V	1	1000 W	
B12	PLINTHE	STELPRO	B12030W	Non	RELAS	Non	347 V	1	1200 W	
B15	PLINTHE	STELPRO	B15030W	Non	RELAS	Non	347 V	1	1500 W	
B25	PLINTHE	STELPRO	B25030W	Non	RELAS	Non	347 V	1	2500 W	
T4	AÉROTHERME PLAFOND	STELPRO	SHU451COCHAR	Non	Oui	Oui	347 V	1	4000 W	
T15	AÉROTHERME PLAFOND	STELPRO	SHU151COCHAR	Non	Oui	Oui	347 V	1	15000 W	
RT	RELAS TMC	STELPRO	RE20T	Non			347 V	1		

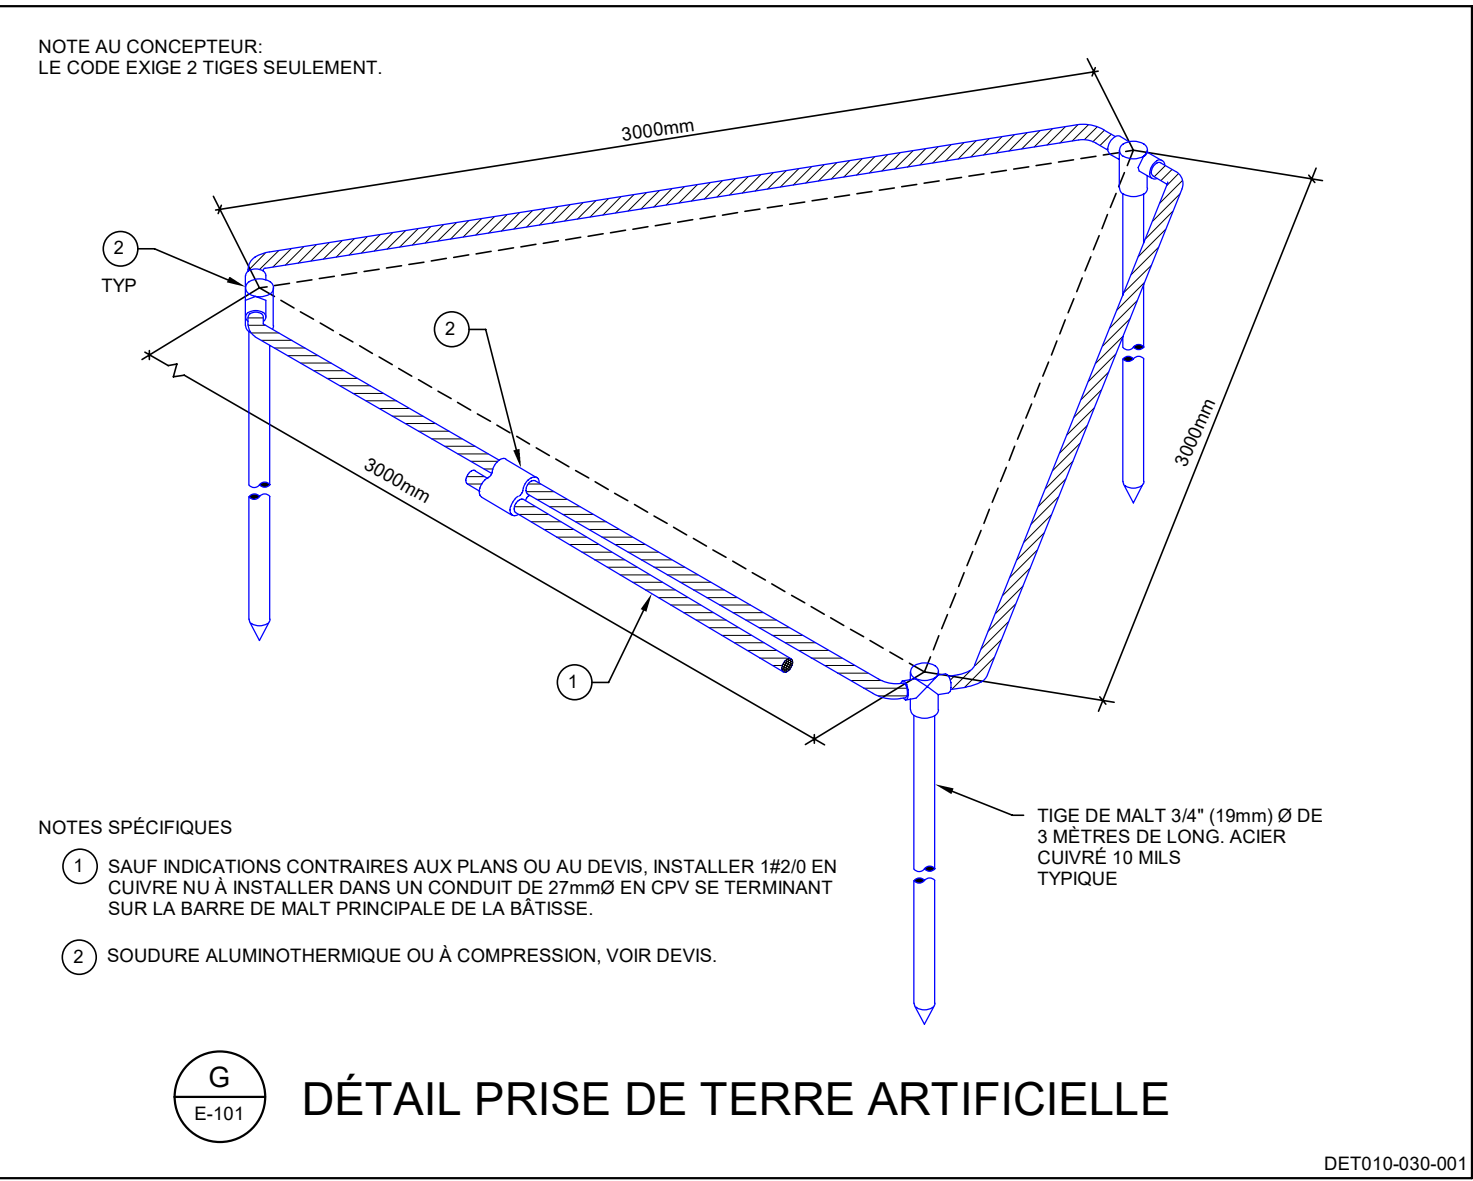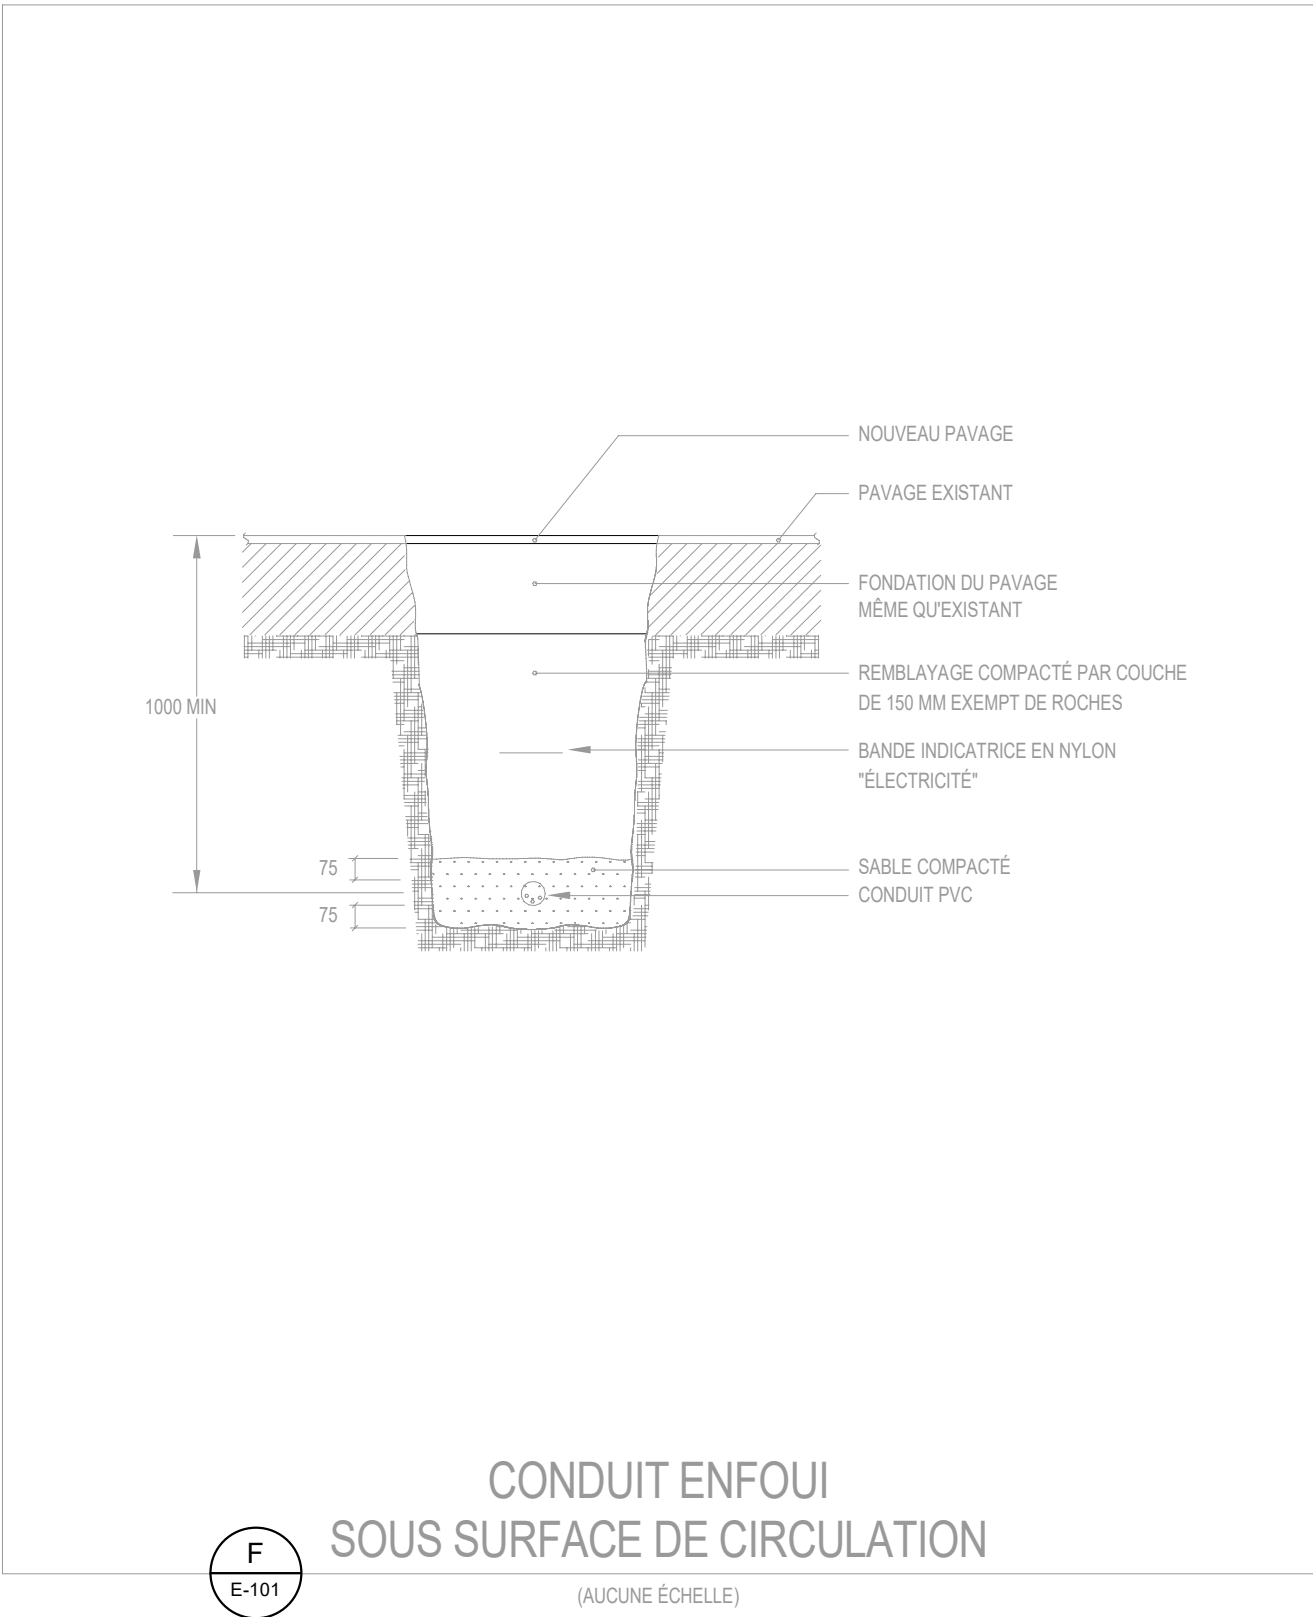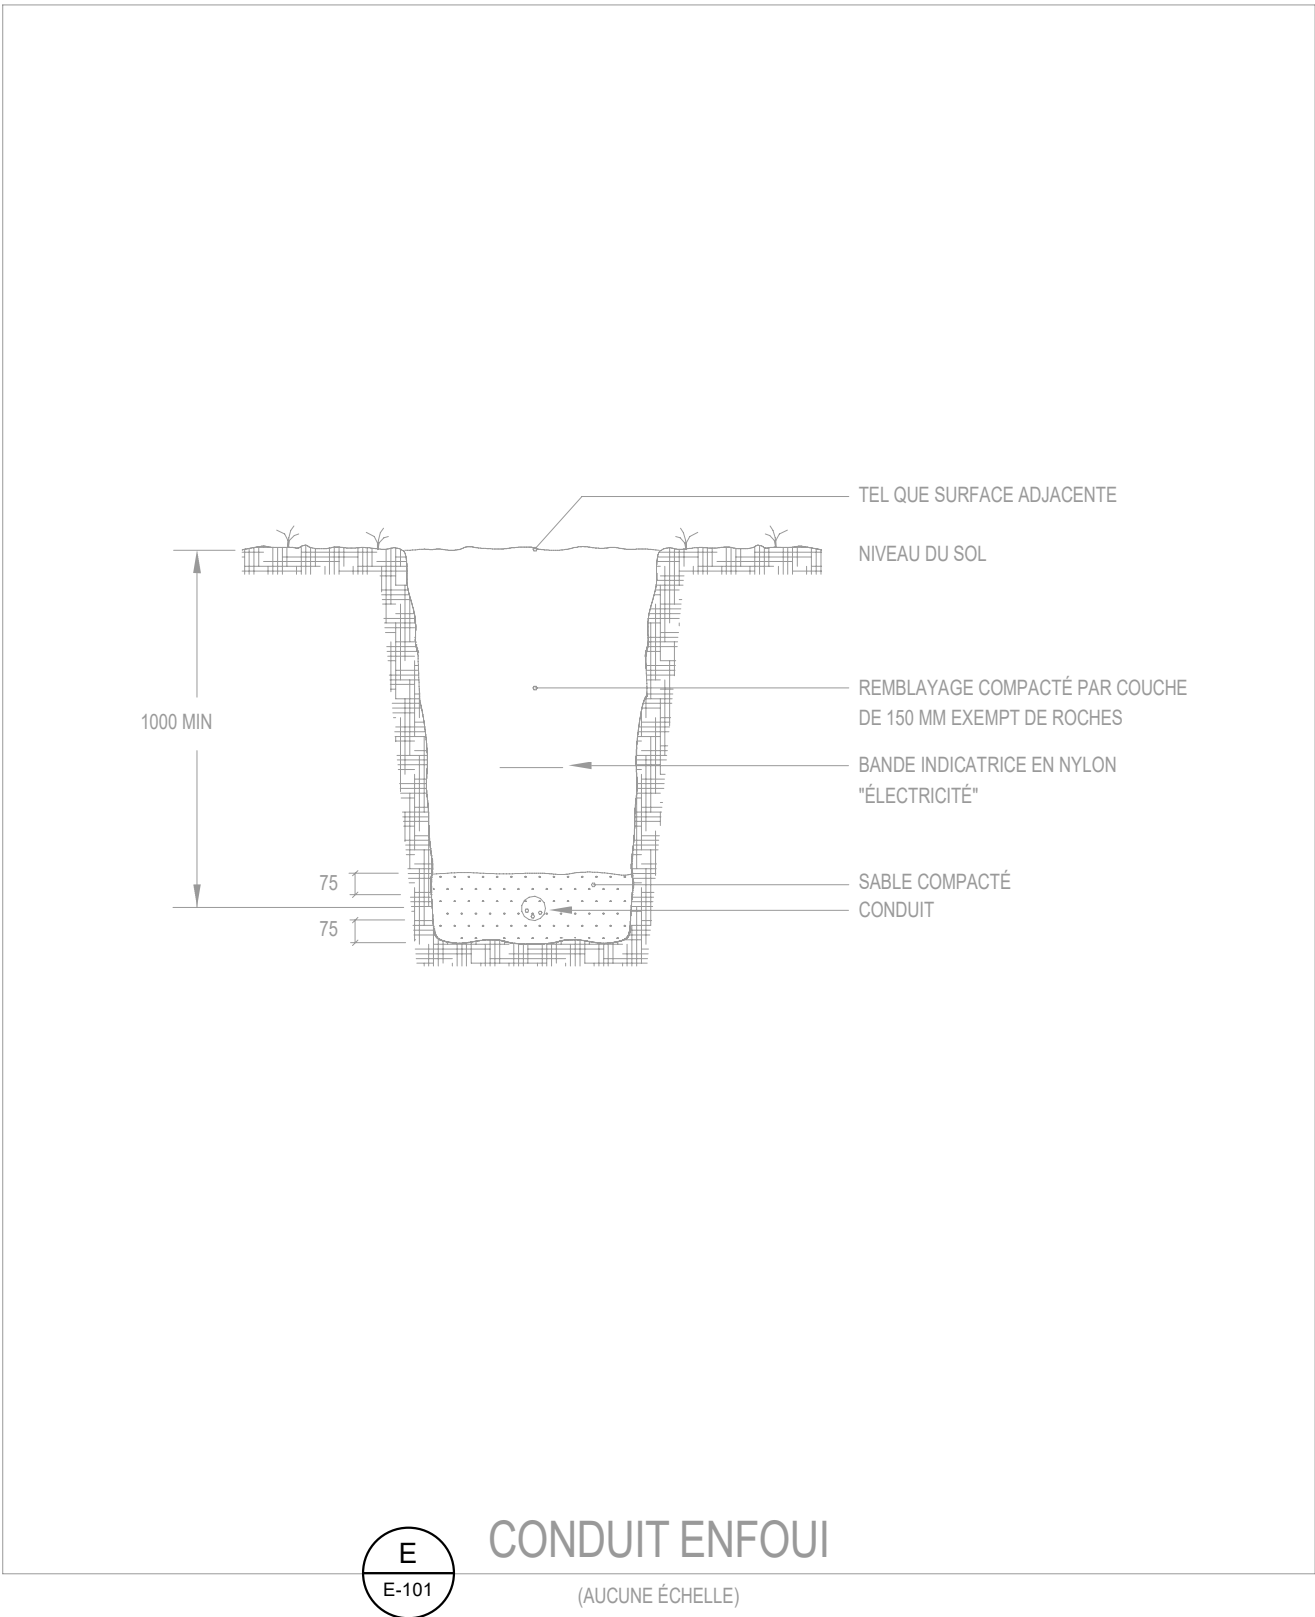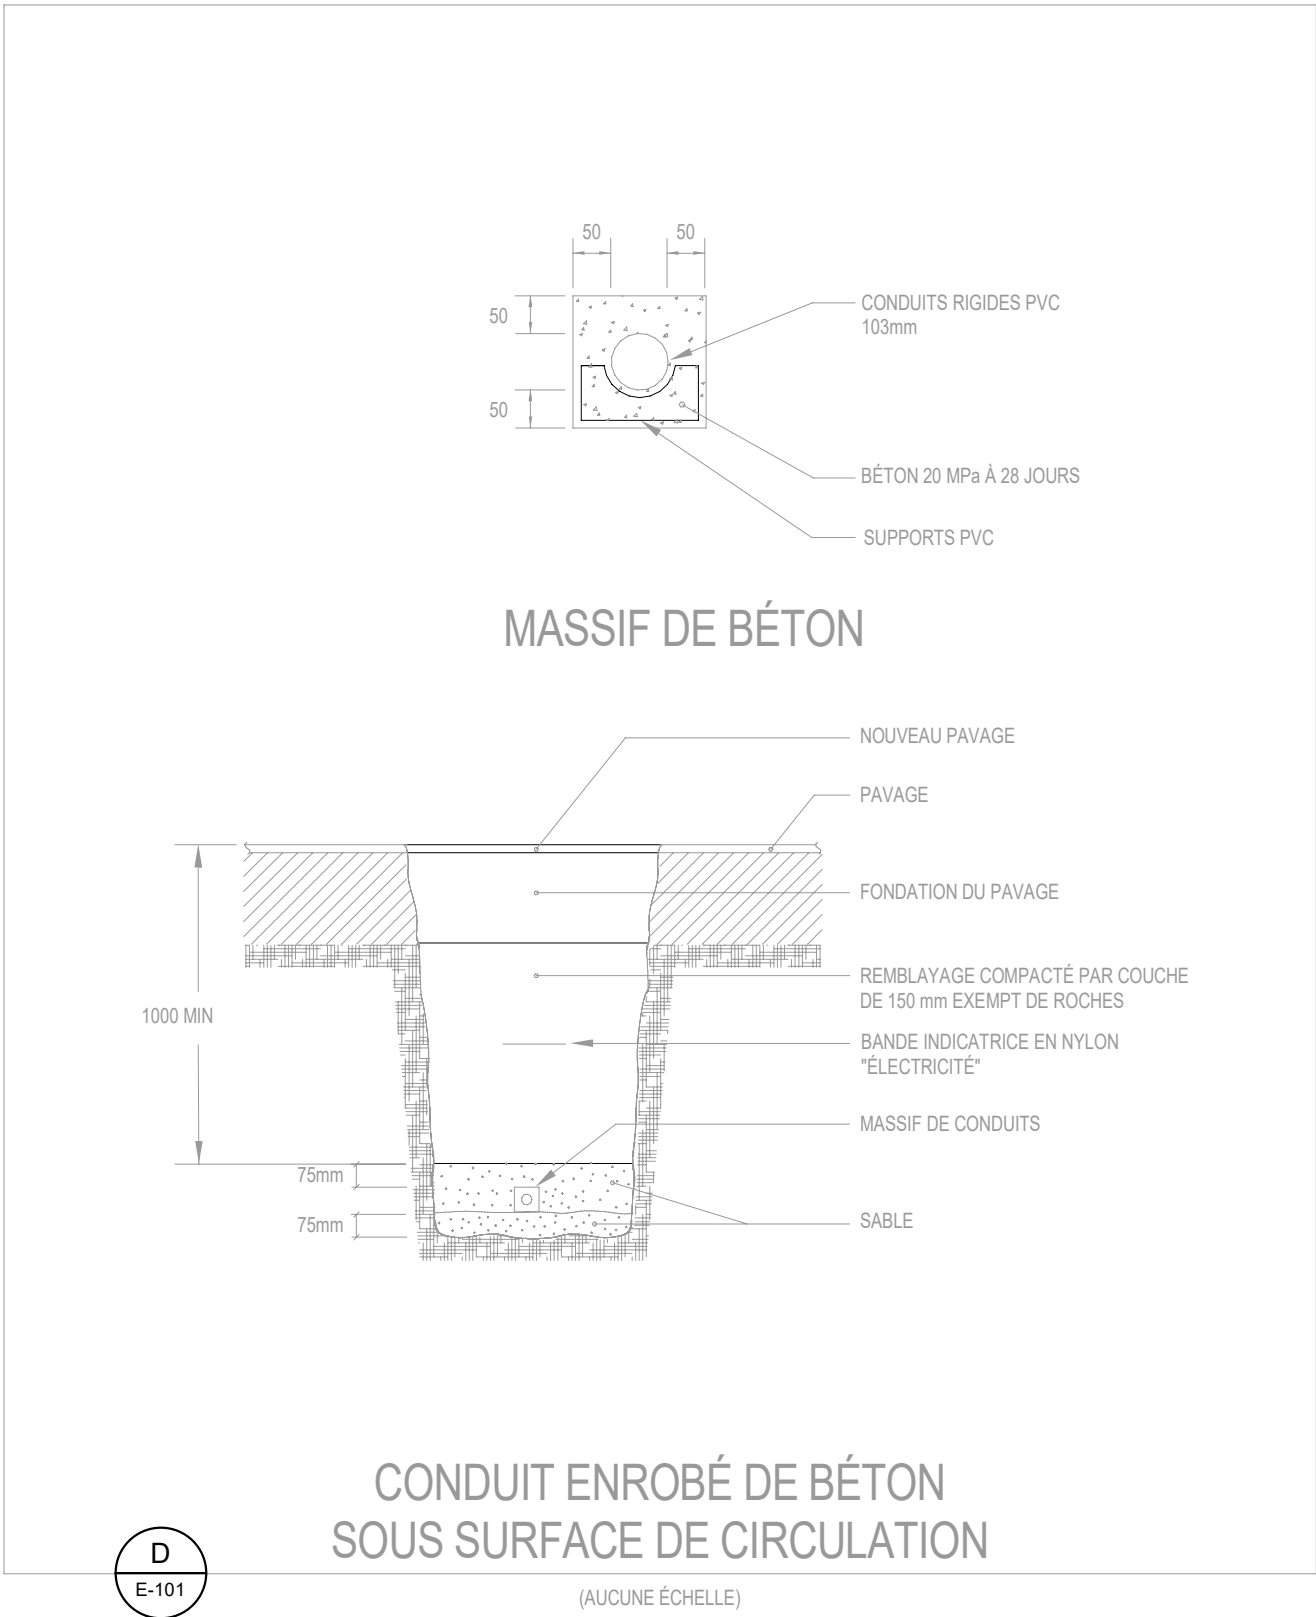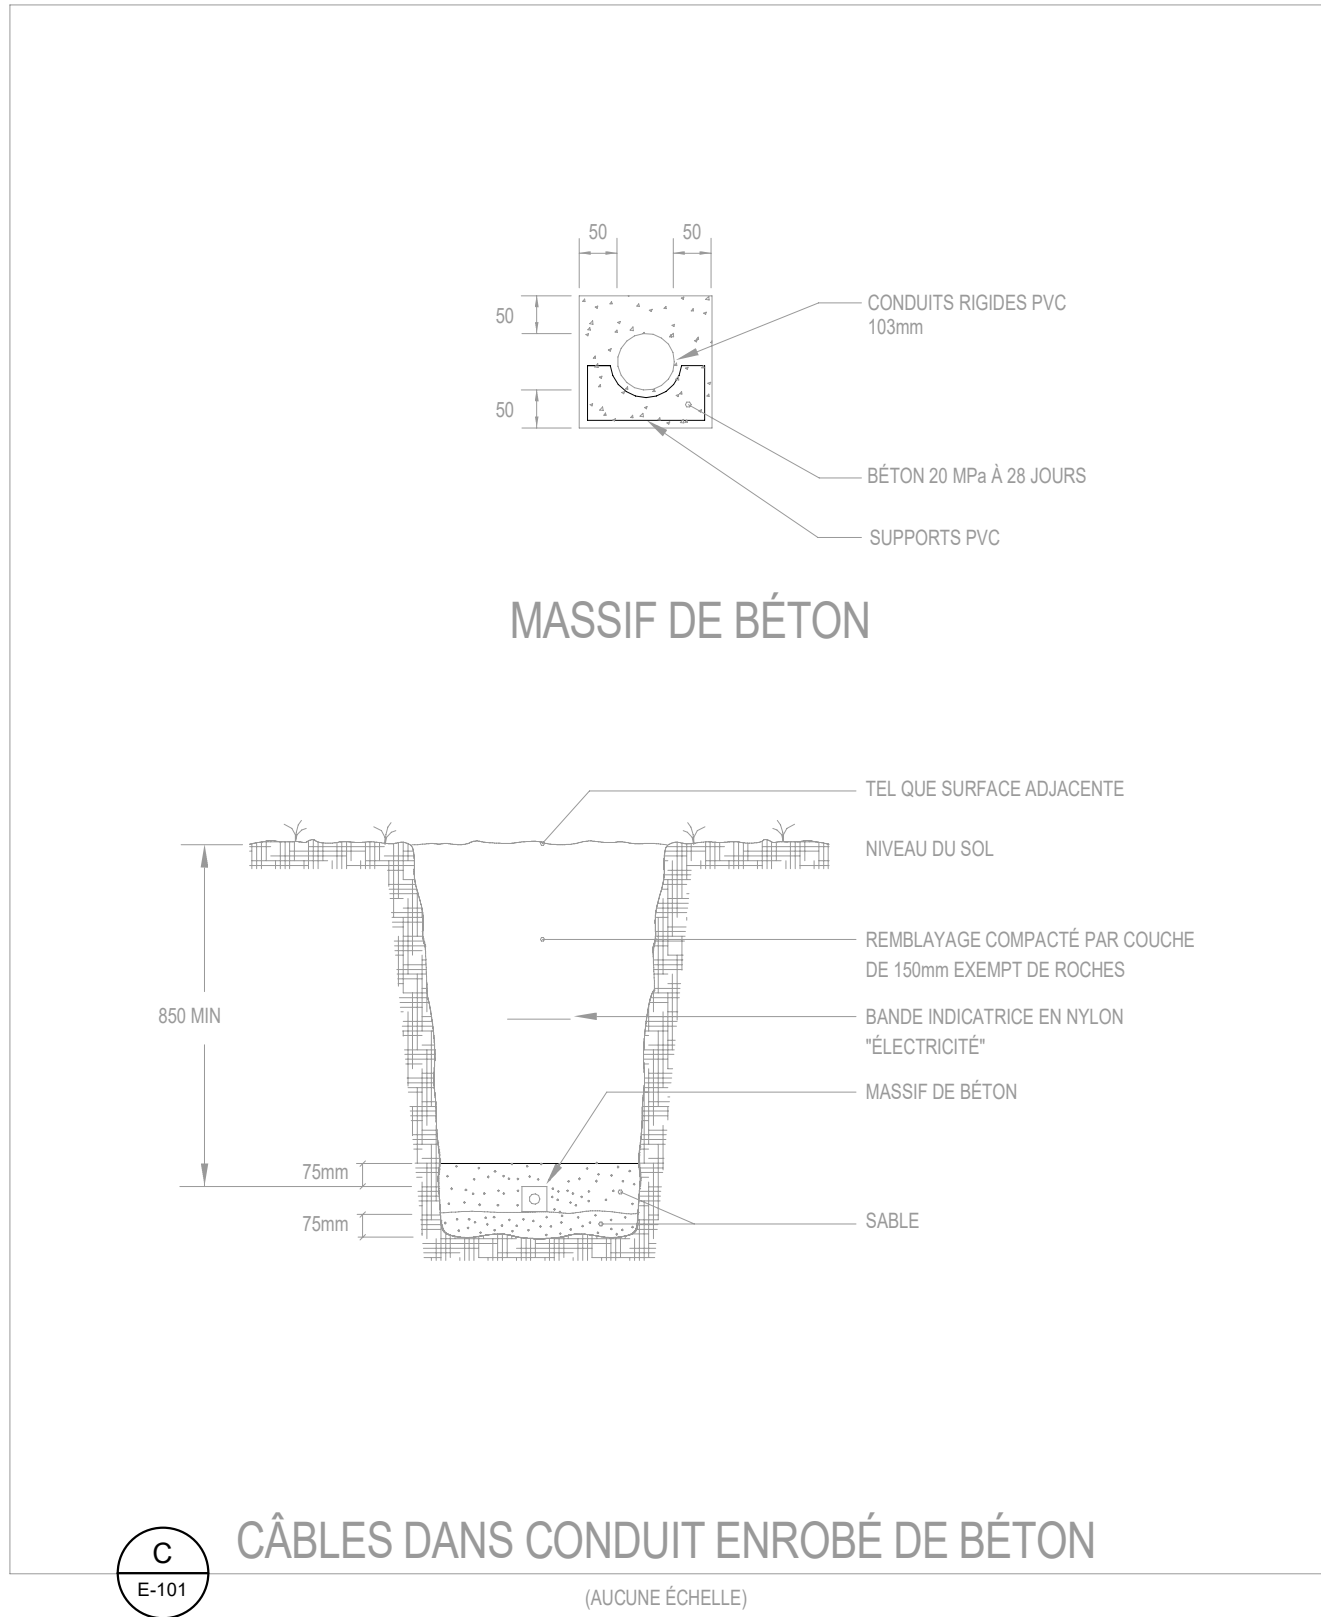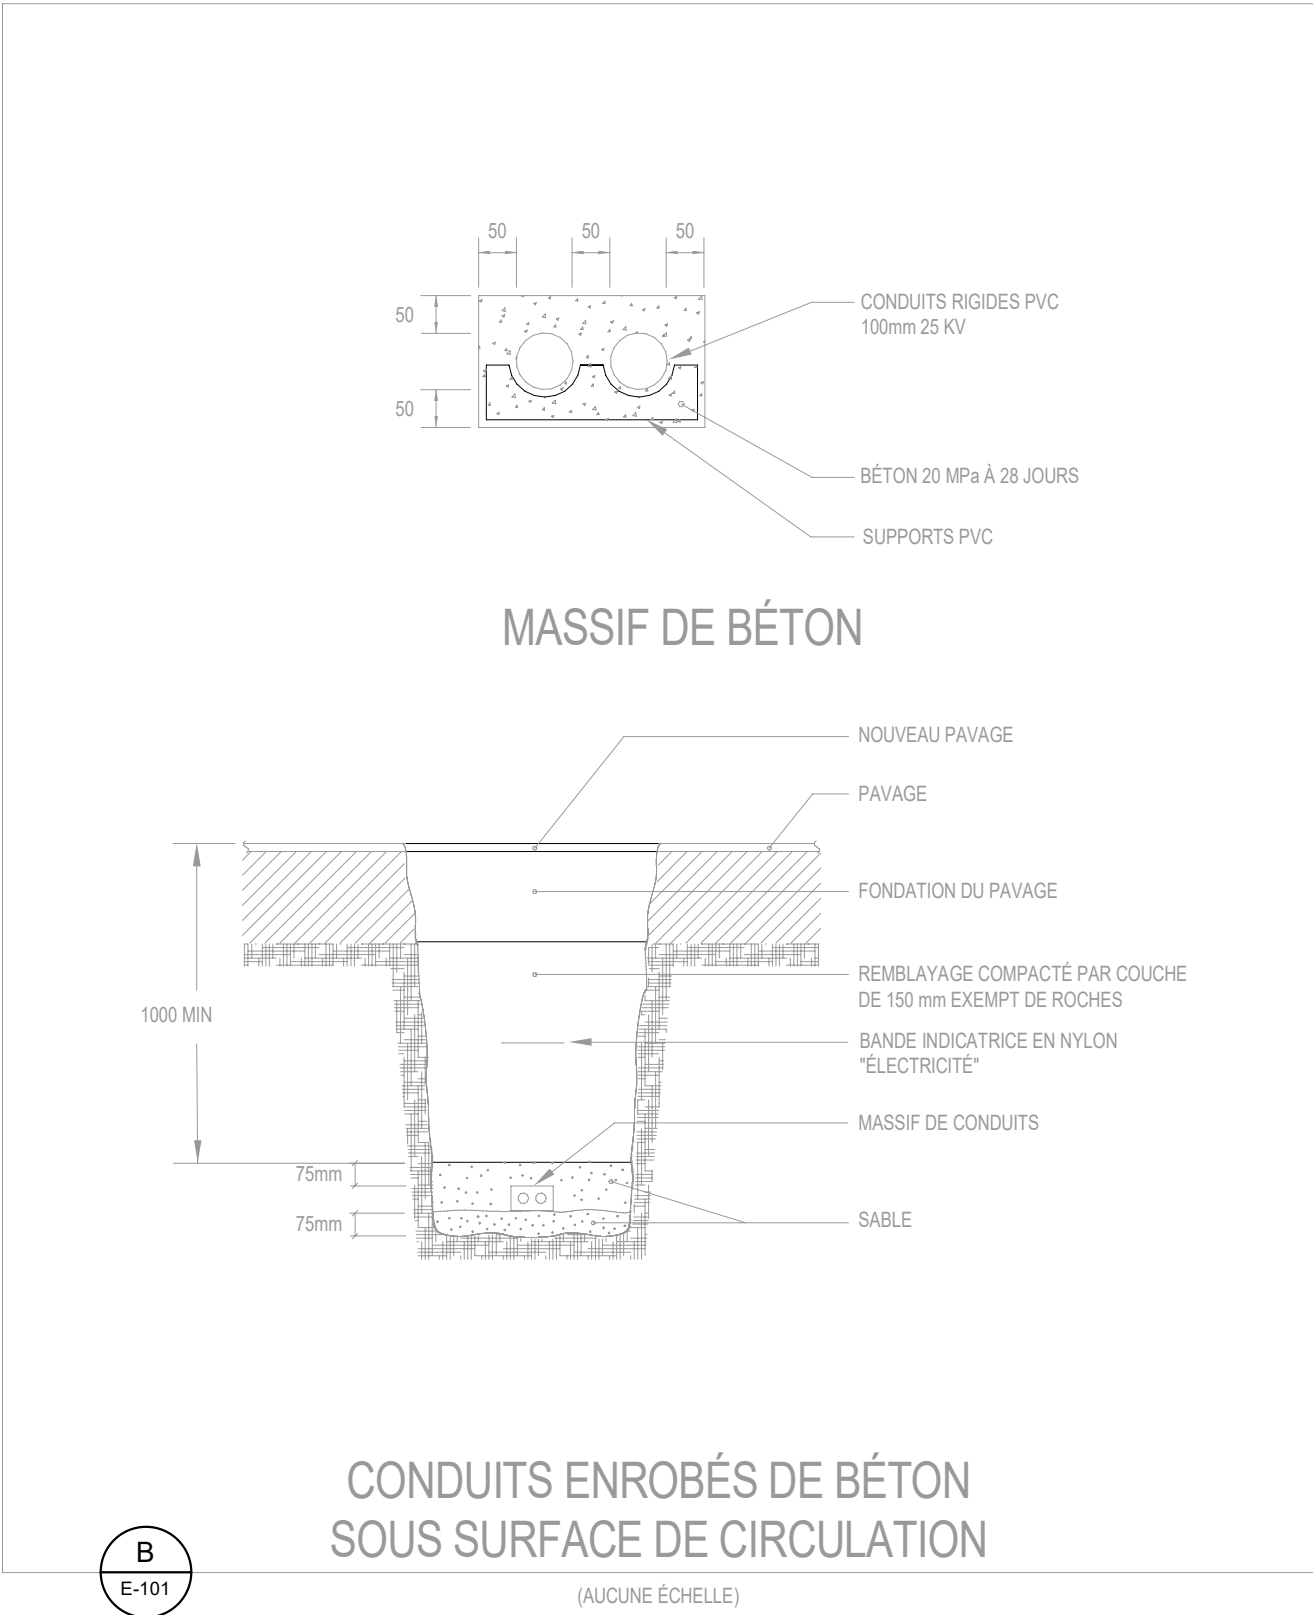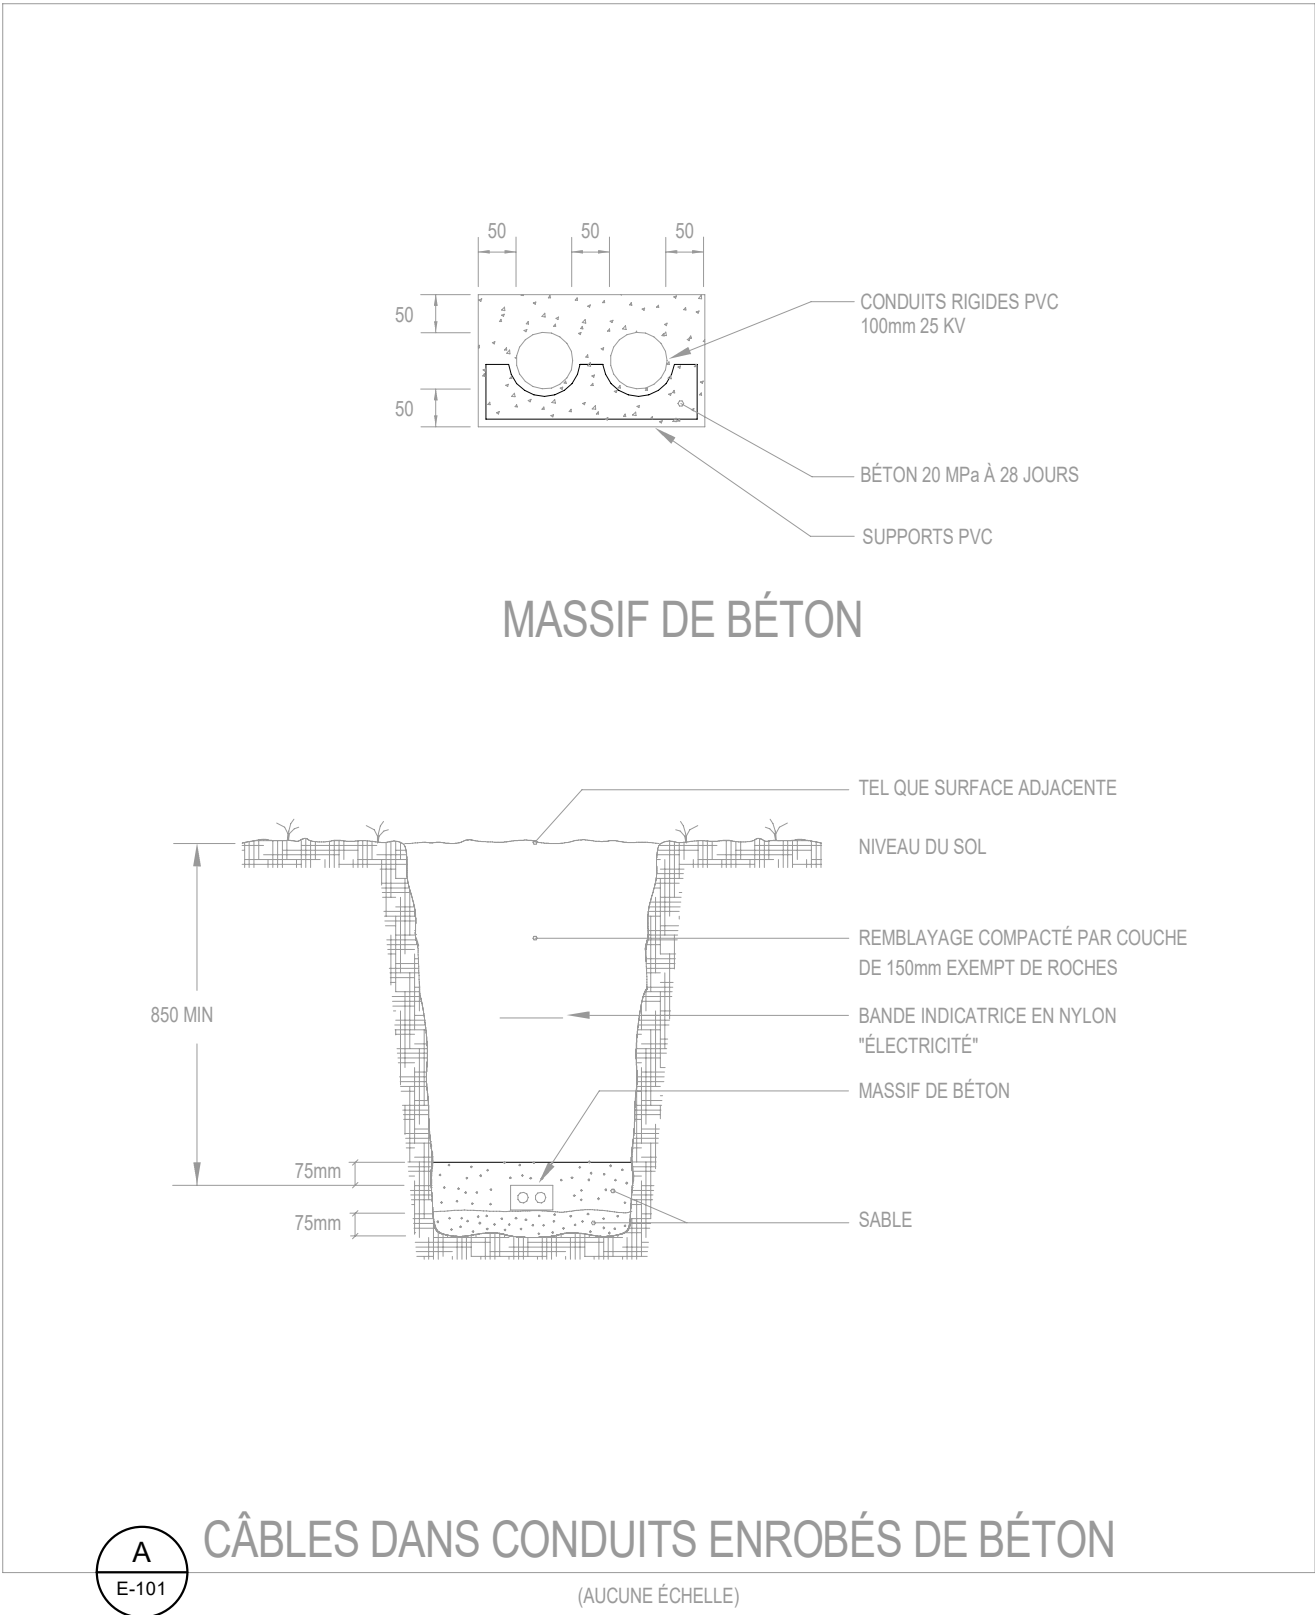

Cliet:



VILLE DE SALABERRY-DE-VALLEYFIELD
61, RUE SAINTÉ-CECILE, SALABERRY-DE-VALLEYFIELD (QUÉBEC), J6T 1L8

CONSTRUCTION D'INFRASTRUCTURES
SPORTIVES AU PARC LIONEL-GROULX

118, RUE MATHIAS, SALABERRY-DE-VALLEYFIELD (QUÉBEC), J6T 3J6

CHALET, PATINOIRE ET STATIONNEMENT

POUR SOUMISSIONS

Architectes:




Ingénieurs mécanique / électrique:



Ingénieurs structure:




Pian clé:

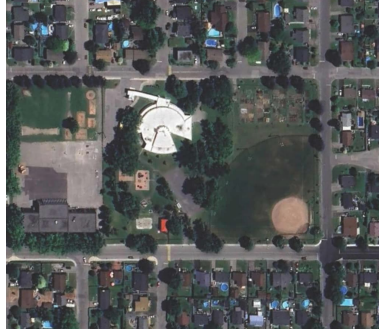

Scieur:



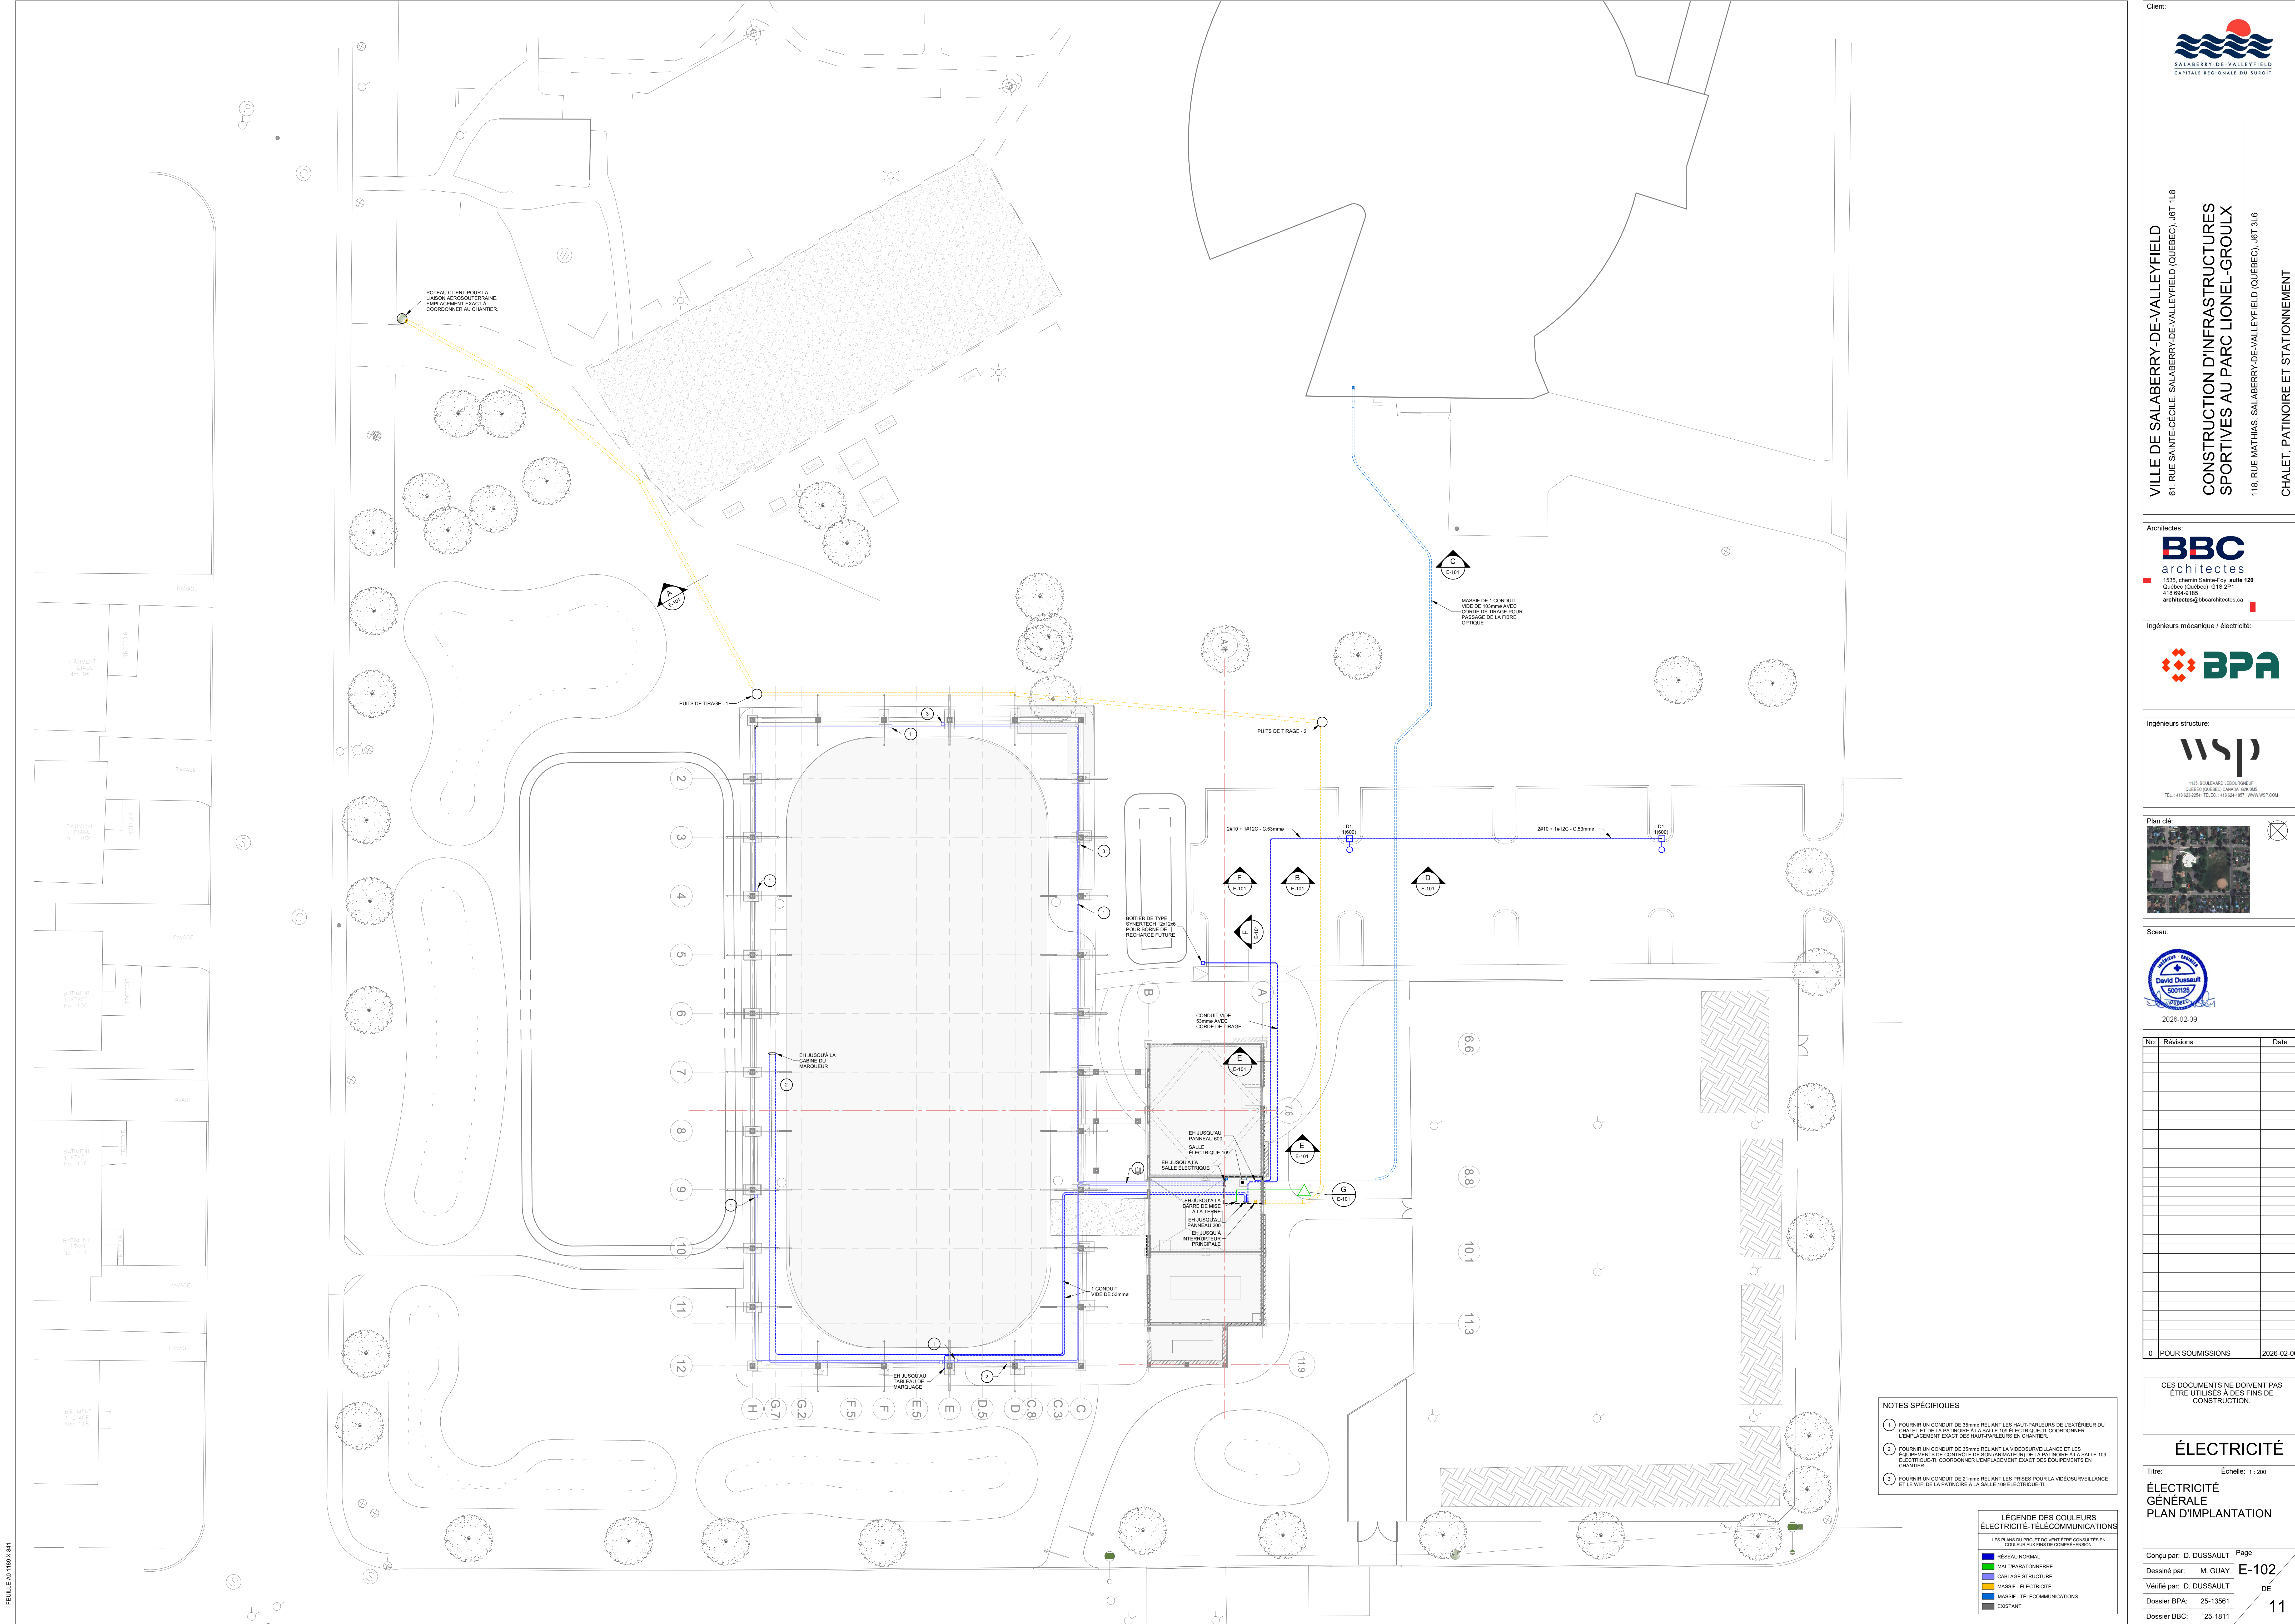

FEMME A2 1180 X 841

VILLE DE SALABERRY-DE-VALLEYFIELD
81, RUE SAINTÉ-CECILE, SALABERRY-DE-VALLEYFIELD (QUÉBEC), J8T 1L8

CONSTRUCTION D'INFRASTRUCTURES
SPORTIVES AU PARC LIONEL-GROULX

118, RUE MATHIAS, SALABERRY-DE-VALLEYFIELD (QUÉBEC), J8T 3J6

CHALET, PATINOIRE ET STATIONNEMENT

POUR SOUMISSIONS

Architectes:
BBC
architectes
1535, chemin Sainte-Foy, suite 120
Québec (Québec) G1S 2P1
418 684-5185
architectes@bbcarchitectes.ca

Ingénieurs mécanique / électricité:
BPA

Ingénieurs structure:
wsp
1105, BOULEVARD LEBLANC
QUÉBEC (QUÉBEC) CANADA G1M 3B8
TEL. 418 683-0344 / 1-877-448-8844 / WWW.WSP.COM

Plan site:

Sceau:
David Dussault
2005
2026-02-09

No.	Revisions	Date
0	POUR SOUMISSIONS	2026-02-06

CES DOCUMENTS NE DOIVENT PAS
ÊTRE UTILISÉS À DES FINS DE
CONSTRUCTION.


ÉLECTRICITÉ

Titre: Échelle: 1 : 200

ÉLECTRICITÉ
GÉNÉRALE
PLAN D'IMPLANTATION

Conçu par: D. DUSSAULT
Dessiné par: M. GUAY
Vérifié par: D. DUSSAULT
Dossier BPA: 25-13561
Dossier BBC: 25-1811

Page
E-102
DE
11

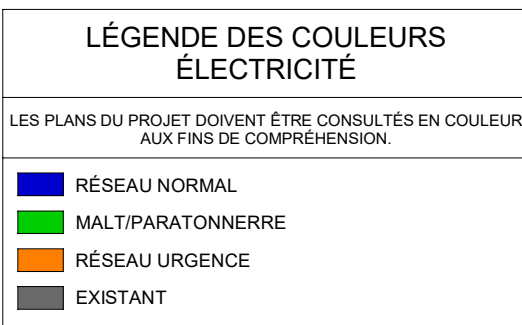

IDENTIFICATION NORMALISÉE DES SORTIES DE COMMUNICATIONS

SÉCURITÉ

IDENTIFICATION NORMALISÉE DES SORTIES DE COMMUNICATIONS

AFFECTATION DES LIENS DE COMMUNICATIONS

LIEN HORIZONTAL DU RÉSEAU DE DONNÉES LOCAL, FIBRE OPTIQUE, 1 Paire

LIEN HORIZONTAL DU RÉSEAU DE DONNÉES LOCAL, CUIVRE, 4 Paires

LIEN HORIZONTAL DU RÉSEAU TÉLÉPHONIQUE ANALOGIQUE, CUIVRE, 4 Paires

LIEN AFFECTÉ AU SYSTÈME AUDIOVISUEL

SORTIE DE COMMUNICATION AFFECTÉE AU POINT D'ACCÈS SANS-FIL

IDENTIFICATION NORMALISÉE
DES ÉQUIPEMENTS

TYPE D'ÉQUIPEMENT

IDENTIFICATION NORMALISÉE DES CAMÉRAS

GÉNÉRAL

NOMENCLATURE

IDENTIFICATION NORMALISÉE DES CAMÉRAS

A. CONSERVER

Client



VILLE DE SALABERRY-DE-VALLEYFIELD
61, RUE SANTE-CÉCILE, SALABERRY-DE-VALLEYFIELD (QUEBEC), J6T 1L8

CONSTRUCTION D'INFRASTRUCTURES
SPORTIVES AU PARC LIONEL-GROULX

118, RUE MATHIAS, SALABERRY-DE-VALLEYFIELD (QUÉBEC), J6T 3L6

POUR SOUMISSIONS

Architectes:




Ingénieurs mécanique / électricité



Ingénieurs structure



Plan clé:

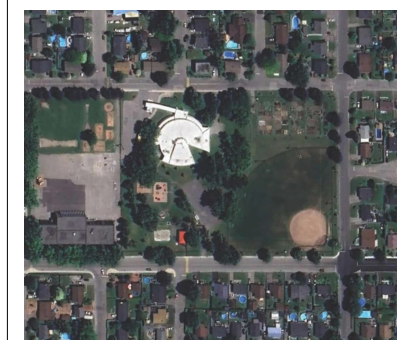

Sceau

[illegible]

CES DOCUMENTS NE DOIVENT PAS
ÊTRE UTILISÉS À DES FINS DE
CONSTRUCTION.

TÉLÉCOMMUNICATION

Titre: Échelle

TÉLÉCOMMUNICA
CABLAGE STRUC
LÉGENDE

Conçu par:	M. BAAR	Page T-001 DE 11
Dessiné par:	R. ST-LOUIS	
Vérifié par:	R. SIDANI	
Dossier BPA:	25-13561	
Dossier BBC:	25-1811	

- INSTALLER TOUS LES CÂBLES DANS LES CONDUITS.
- UTILISER LE TABLEAU POUR CALCULER LE DIAMÈTRE DE CHAQUE CONDUIT
- LES CONDUITS SONT FOURNIS ET INSTALLÉS PAR L'ENTREPRENEUR EN ÉLECTRICITÉ.

DIAMÈTRE INTERNE DU CONDUIT EN mm	NOMBRE DE PORTES ASSOCIÉES
21	1
35	3
41	4
53	7
63	11

10 DIMENSION DES CONDUITS POUR LE SYSTÈME DE CONTRÔLE D'ACCÈS

- INSTALLER TOUS LES CÂBLES DANS LES CONDUITS.
- UTILISER LE TABLEAU POUR CALCULER LE DIAMÈTRE DE CHAQUE CONDUIT.
- LES CONDUITS SONT FOURNIS ET INSTALLÉS PAR L'ENTREPRENEUR EN ÉLECTRICITÉ.

DIAMÈTRE INTERNE DU CONDUIT EN mm	NOMBRE DE PORTES ASSOCIÉES
21	7
27	12
35	21
41	29
53	49

11 DIMENSION DES CONDUITS POUR LE SYSTÈME DÉTECTION D'INTRUSION





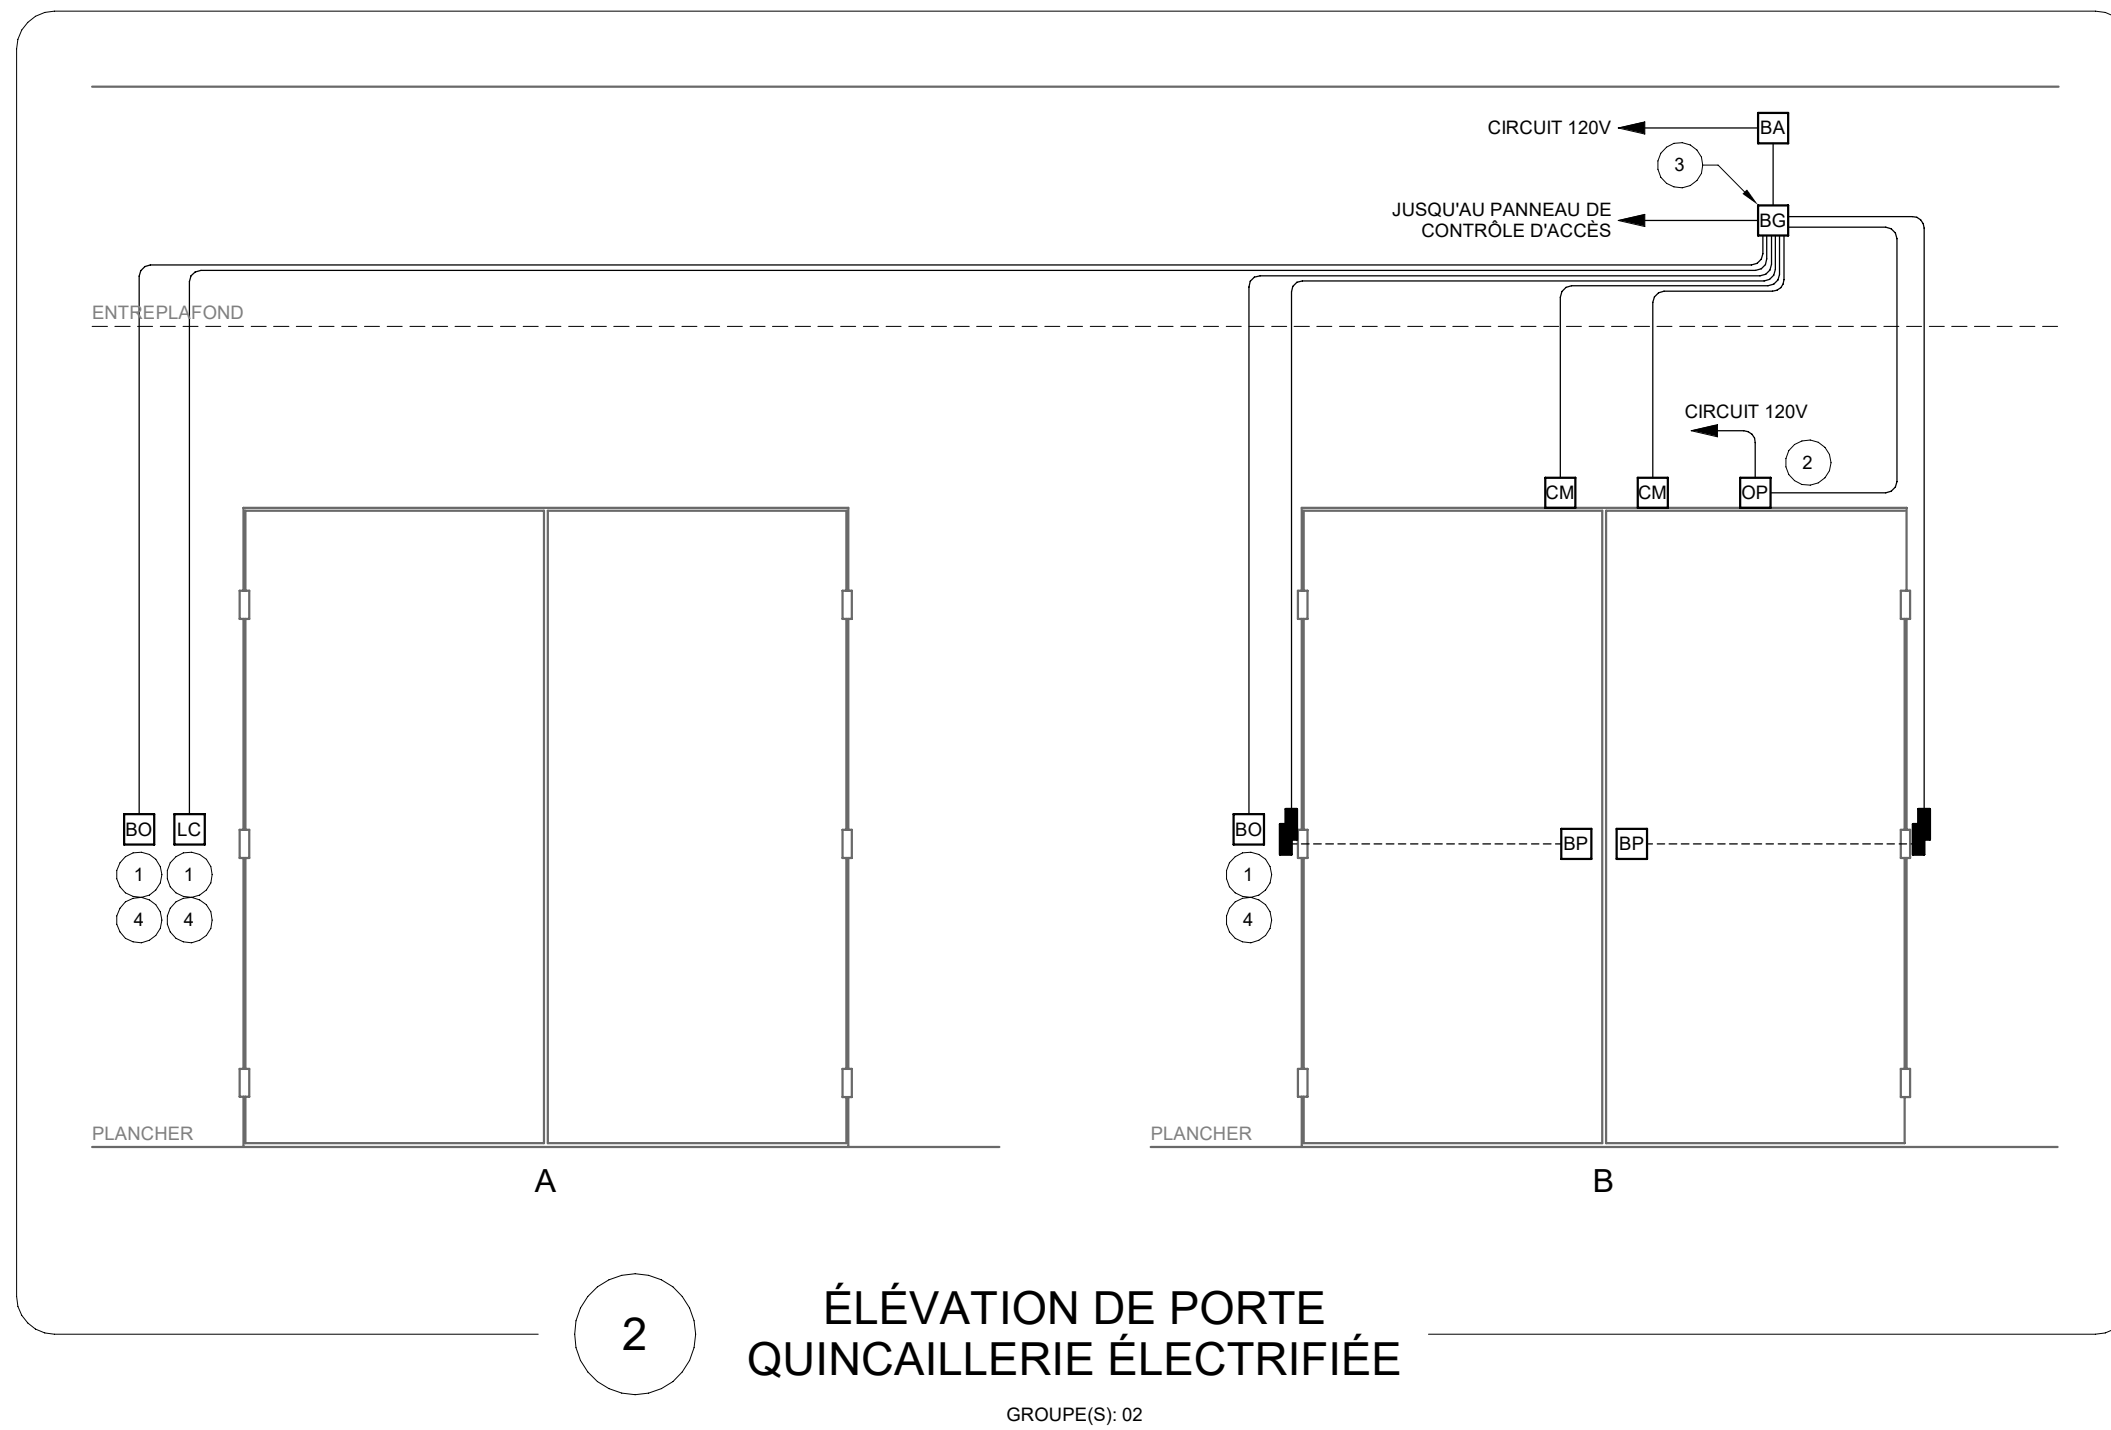


TABLEAU DES PORTES			
GRUPE DE PORTE	LISTE DES PORTES ASSOCIÉES		
01	P-EXT-01		
02	P-EXT-02		
03	P-EXT-03	P-EXT-06	
05	P-EXT-05		
06	P-101		
08	P-103	P-109	P-110
10	P-106		
11	P-107		

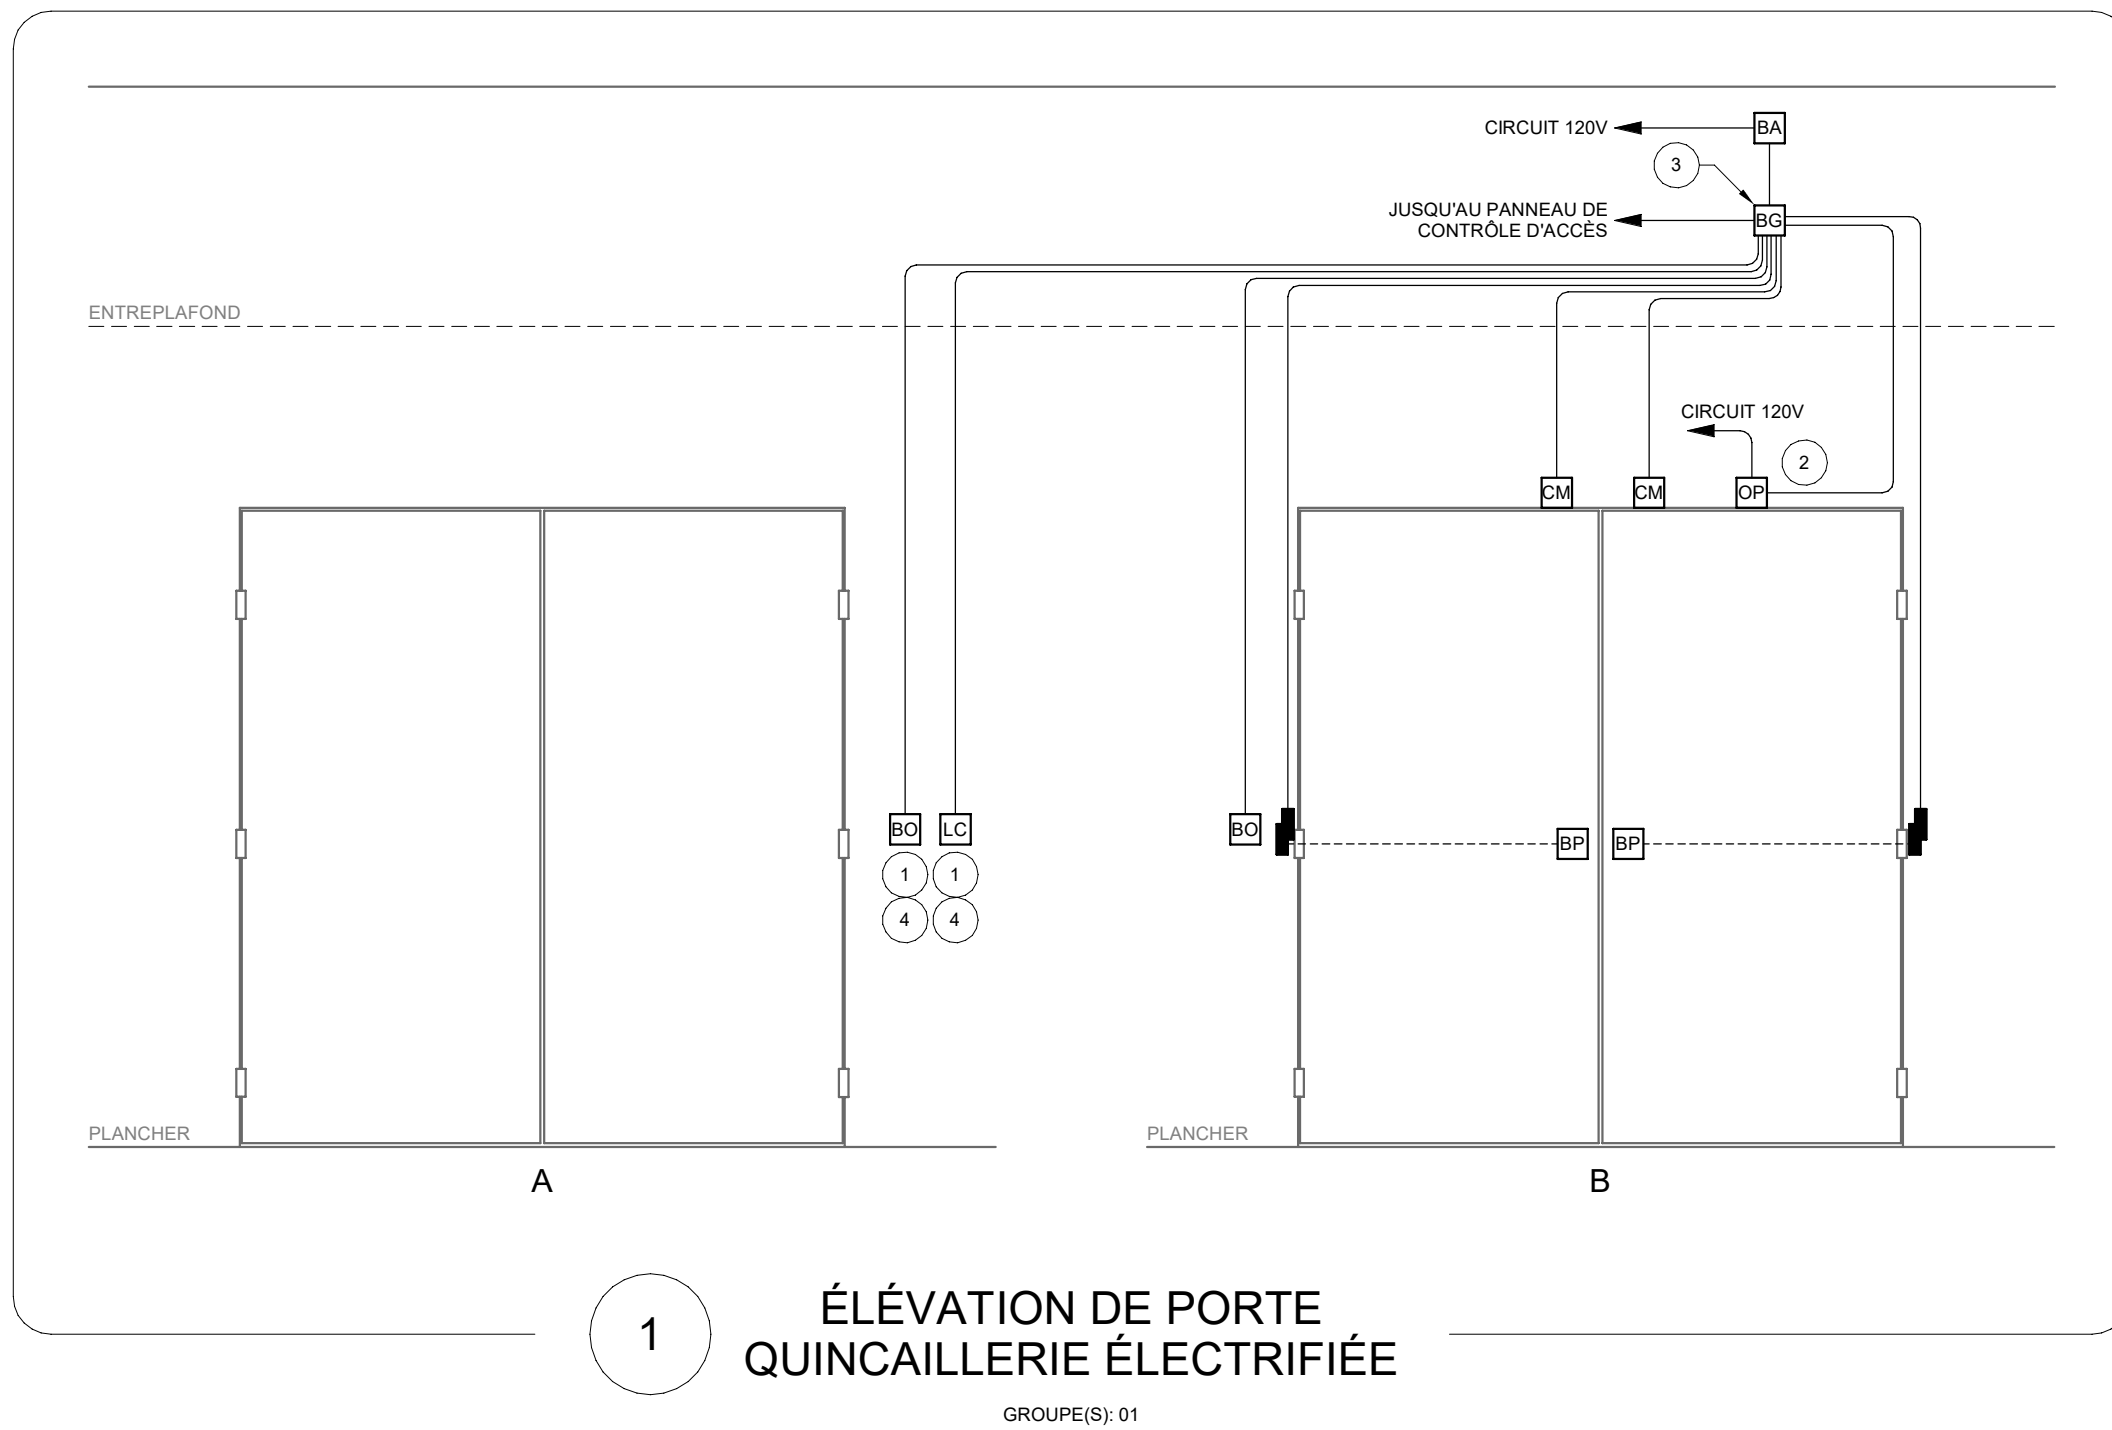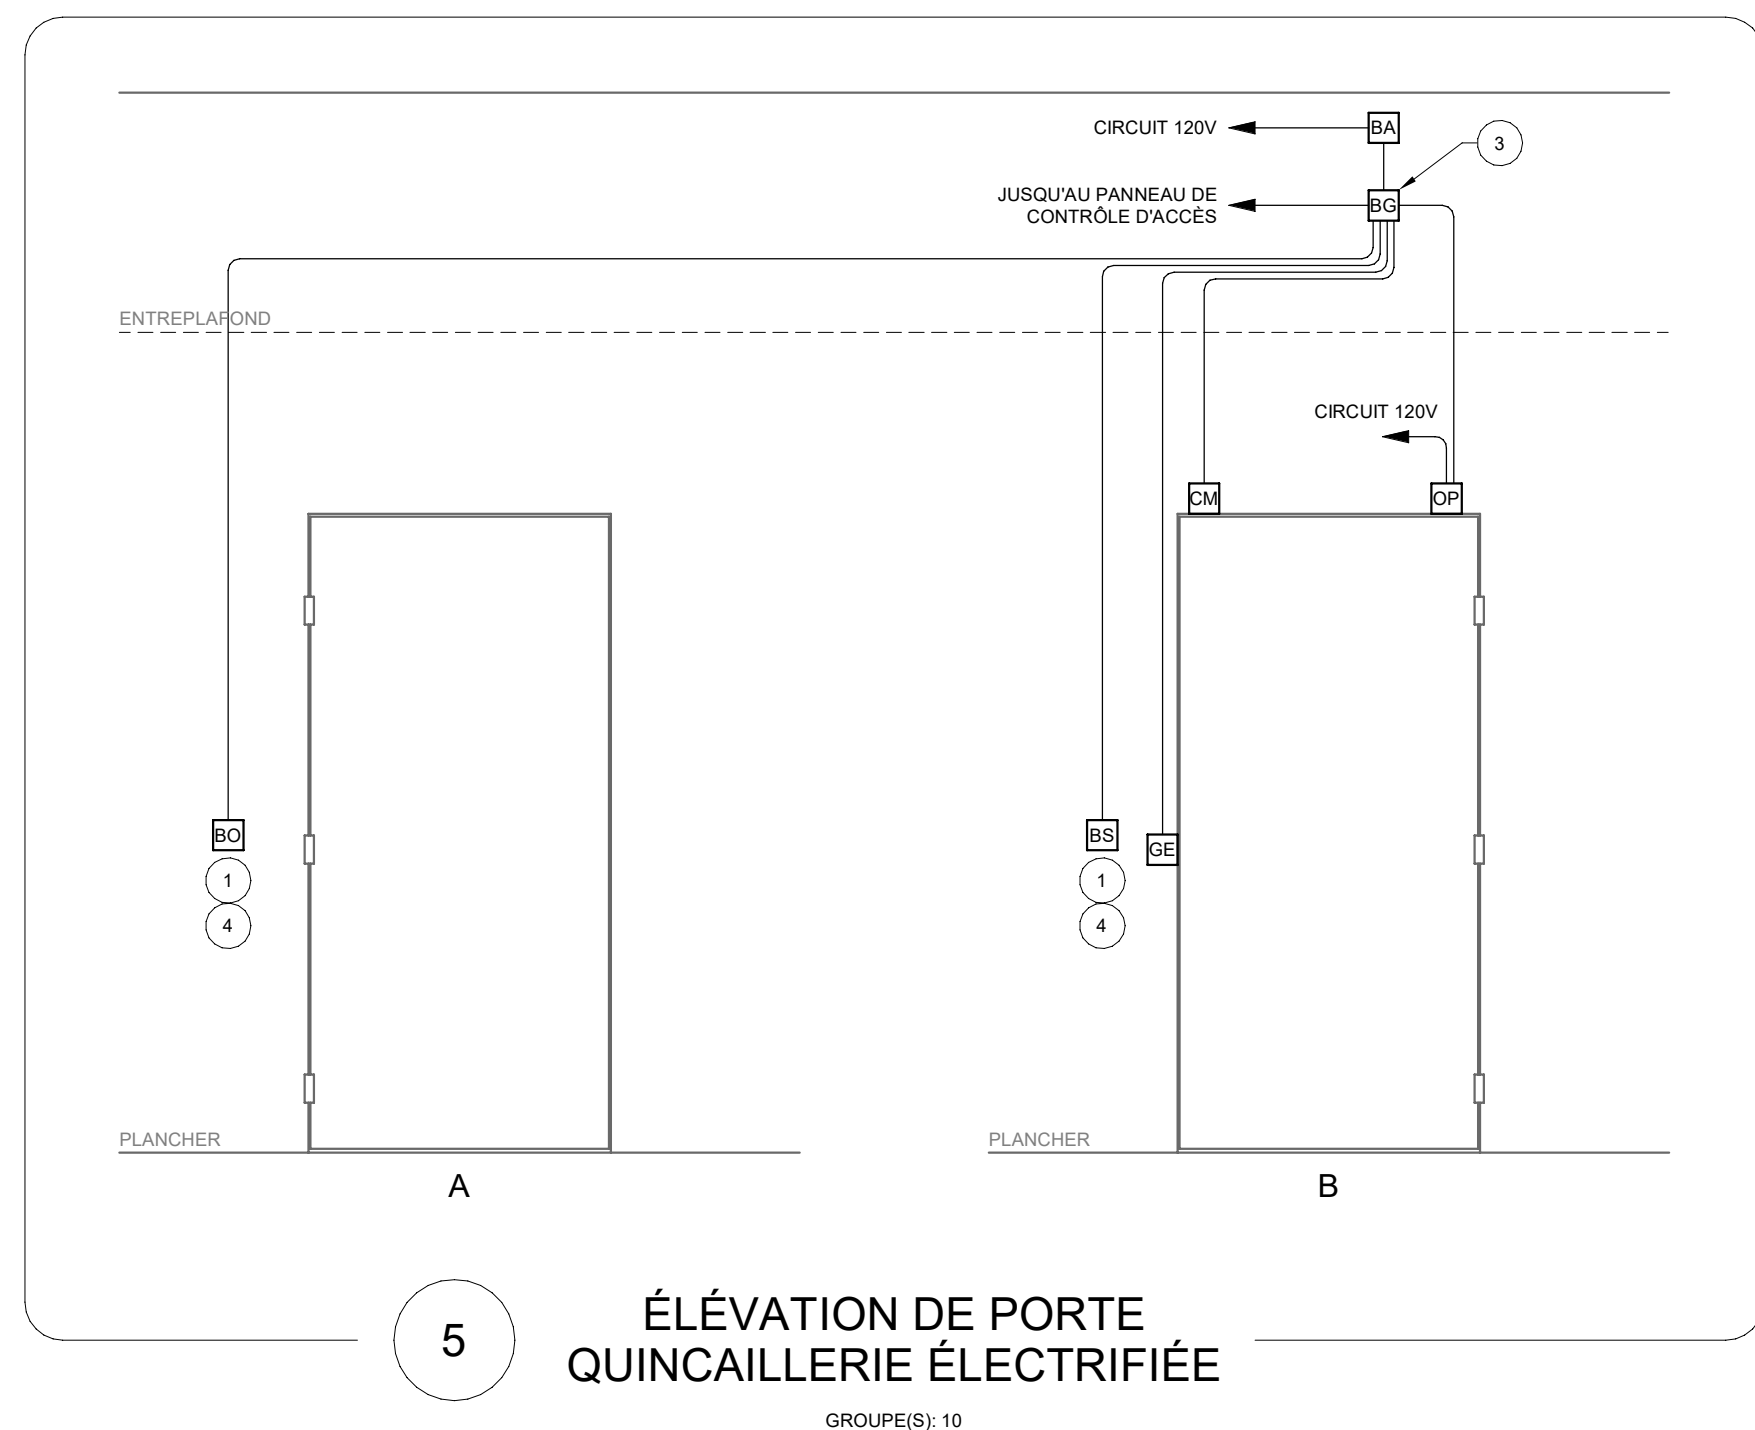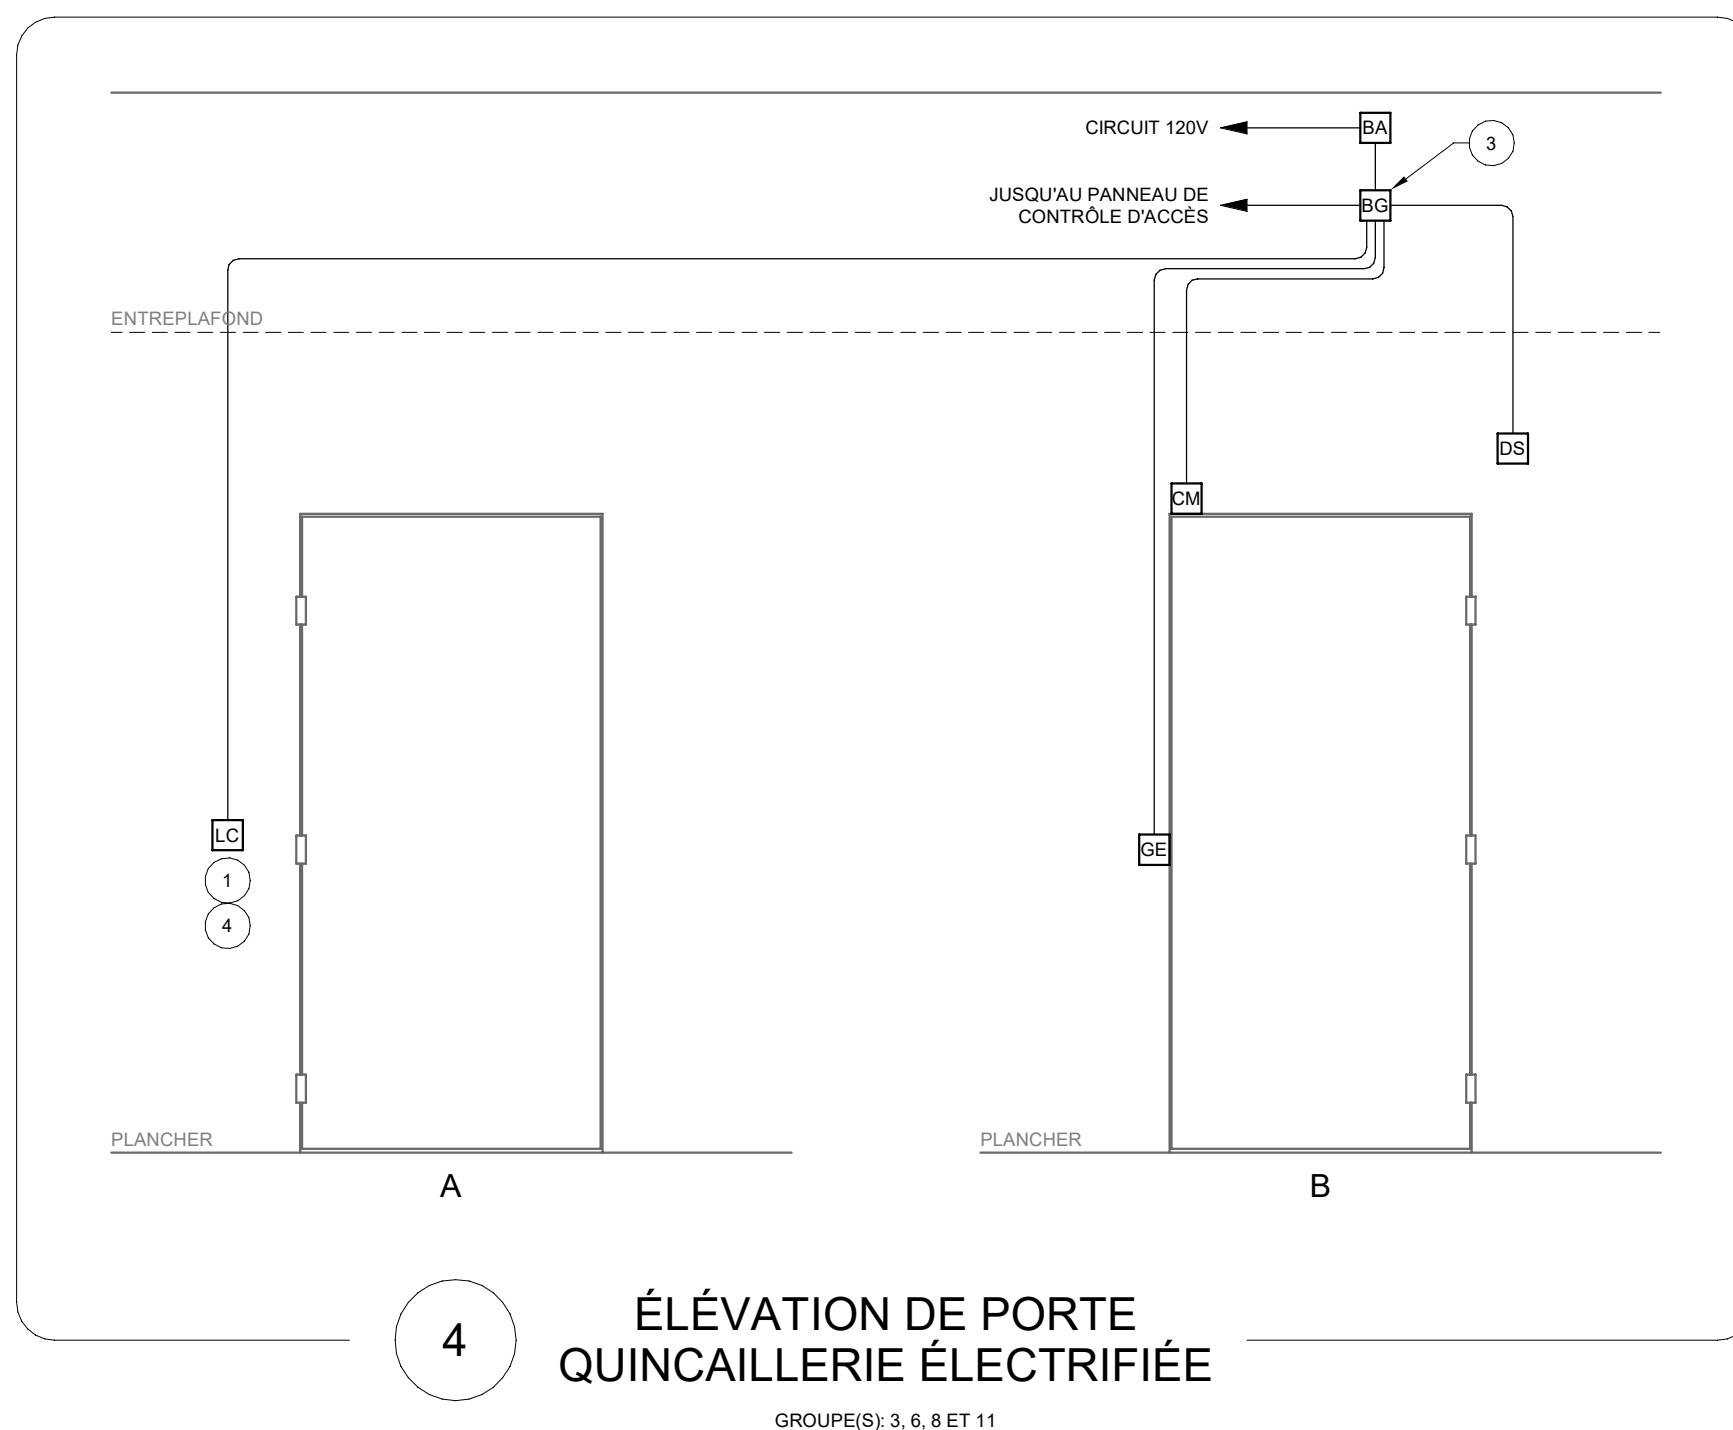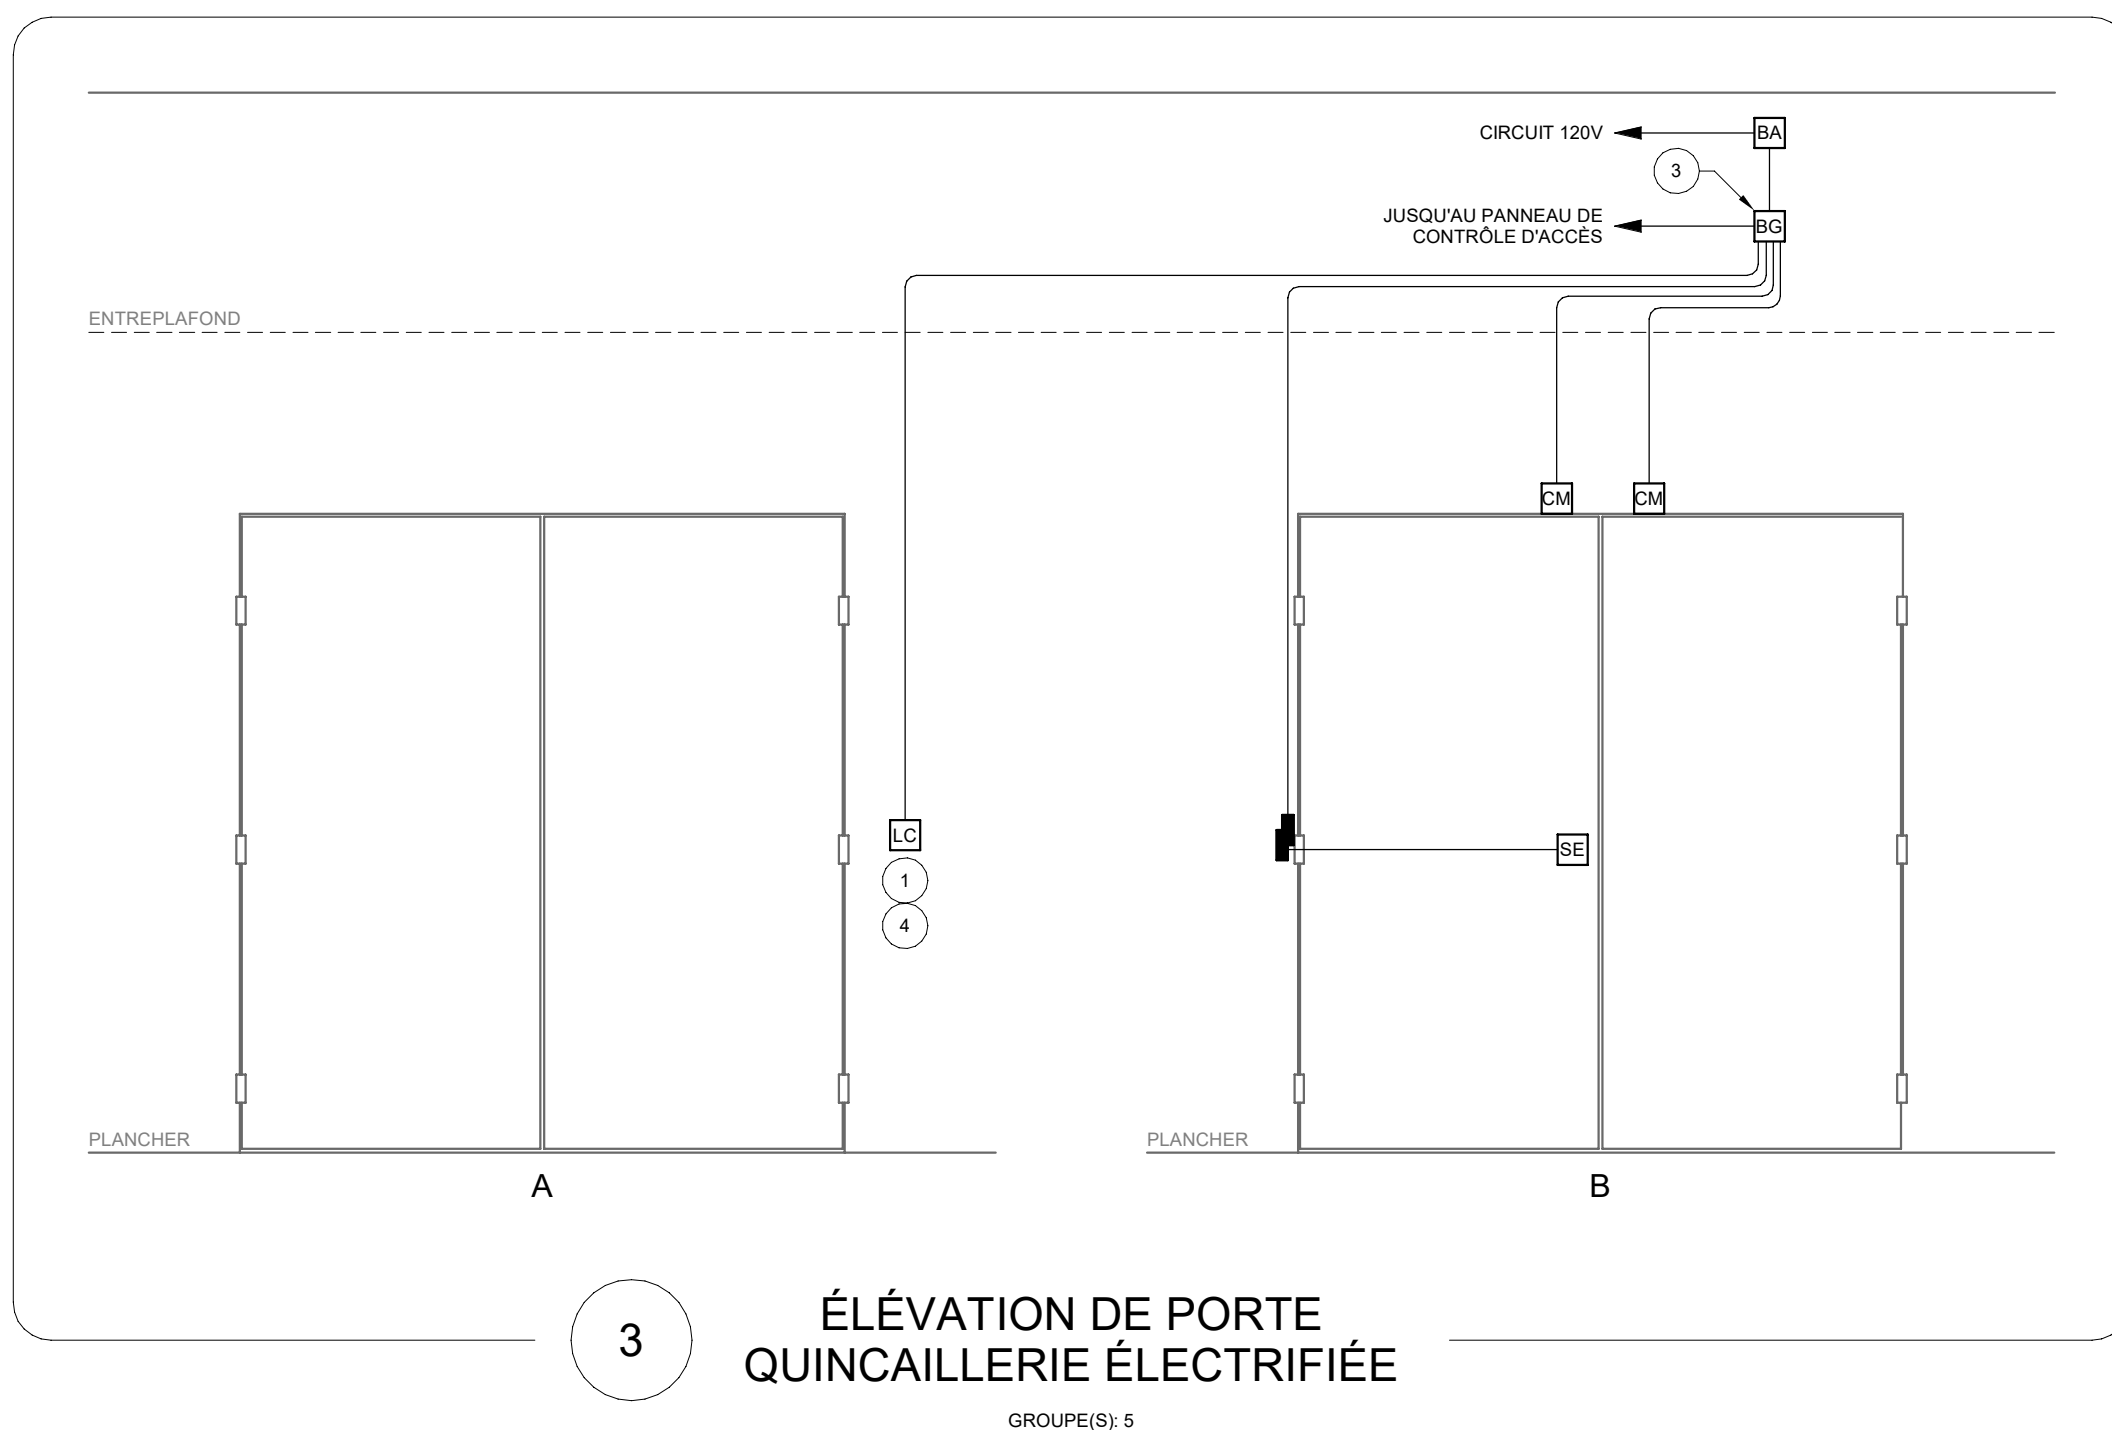

A. À MOINS D'INDICATIONS CONTRAIRES, TOUS LES CONDUITS SONT DE 21mm DE DIAMÈTRE.

B. TOUTES LES DIMENSIONS SONT EN MILLIMÈTRES.

- 1 FOURNIR ET INSTALLER UNE BOÎTE DE SORTIE. UTILISER UNE PLAQUE DE MONTAGE ADAPTÉE LORSQU'UN ÉQUIPEMENT EST INSTALLÉ SUR UNE BOÎTE DE SORTIE ET QUE CELUI-CI NE PARVIENT PAS À COUVRIR LA TOTALITÉ DE L'ORIFICE.
- 2 DISTANCE MAXIMALE DE 100mm entre L'EXTREMITÉ DU CONDUIT ET LA QUINCAILLERIE. ALÉSER ET MUNIR DE DOULES ("BUSHINGS/GROMMETS") LES EXTREMITÉS DES CONDUITS.
- 3 BOÎTE DE TIRAGE 200x200x100mm INSTALLÉE AU-DESSUS DE LA PORTE.
- 4 COORDONNER L'EMPLACEMENT DE L'ÉQUIPEMENT AVEC LE CLIENT.



SALABERRY-DE-VALLEYFIELD
CAPITALE RÉGIONALE DU SUD-OUEST

VILLE DE SALABERRY-DE-VALLEYFIELD
61, RUE SAINTE-CÉCILE, SALABERRY-DE-VALLEYFIELD (QUEBEC), J6T 1L8

CONSTRUCTION D'INFRASTRUCTURES SPORTIVES AU PARC LIONEL-GROULX

118, RUE MATHIAS, SALABERRY-DE-VALLEYFIELD (QUÉBEC), J6T 3L6

CHALET, PATINO
POUR SOUMISSIONS

BBC
architectes
1535, chemin Sainte-Foy, suite 100
Québec (Québec) G1S 2P1
418 694-9185
architectes@bbcarchitectes.ca



wsp
1135, BOULEVARD LEBOURGNEUF
QUÉBEC (QUÉBEC) CANADA G2K 0B5
TÉL. : 418 624-2254 | TÉLÉC. : 418 624-1937 | WWW.WSP.COM

An aerial photograph of a suburban neighborhood. A large, white, two-story house with a prominent chimney is the central focus. It is surrounded by green lawns and mature trees. To the left of the house is a smaller, dark-roofed building, possibly a garage or shed. The surrounding area consists of other residential lots with houses and trees, separated by streets.

DOCUMENT ORIGINAL, PSE B046
NUMÉRO DE SÉRIE: 0020136


[illegible]

CES DOCUMENTS NE DOIVENT PAS
ÊTRE UTILISÉS À DES FINS DE
CONSTRUCTION.

TÉLÉCOMMUNICATION
CABLAGE STRUCTURÉ
DÉTAILS ET SCHÉMA

Dossier BPA: 25-13561

1

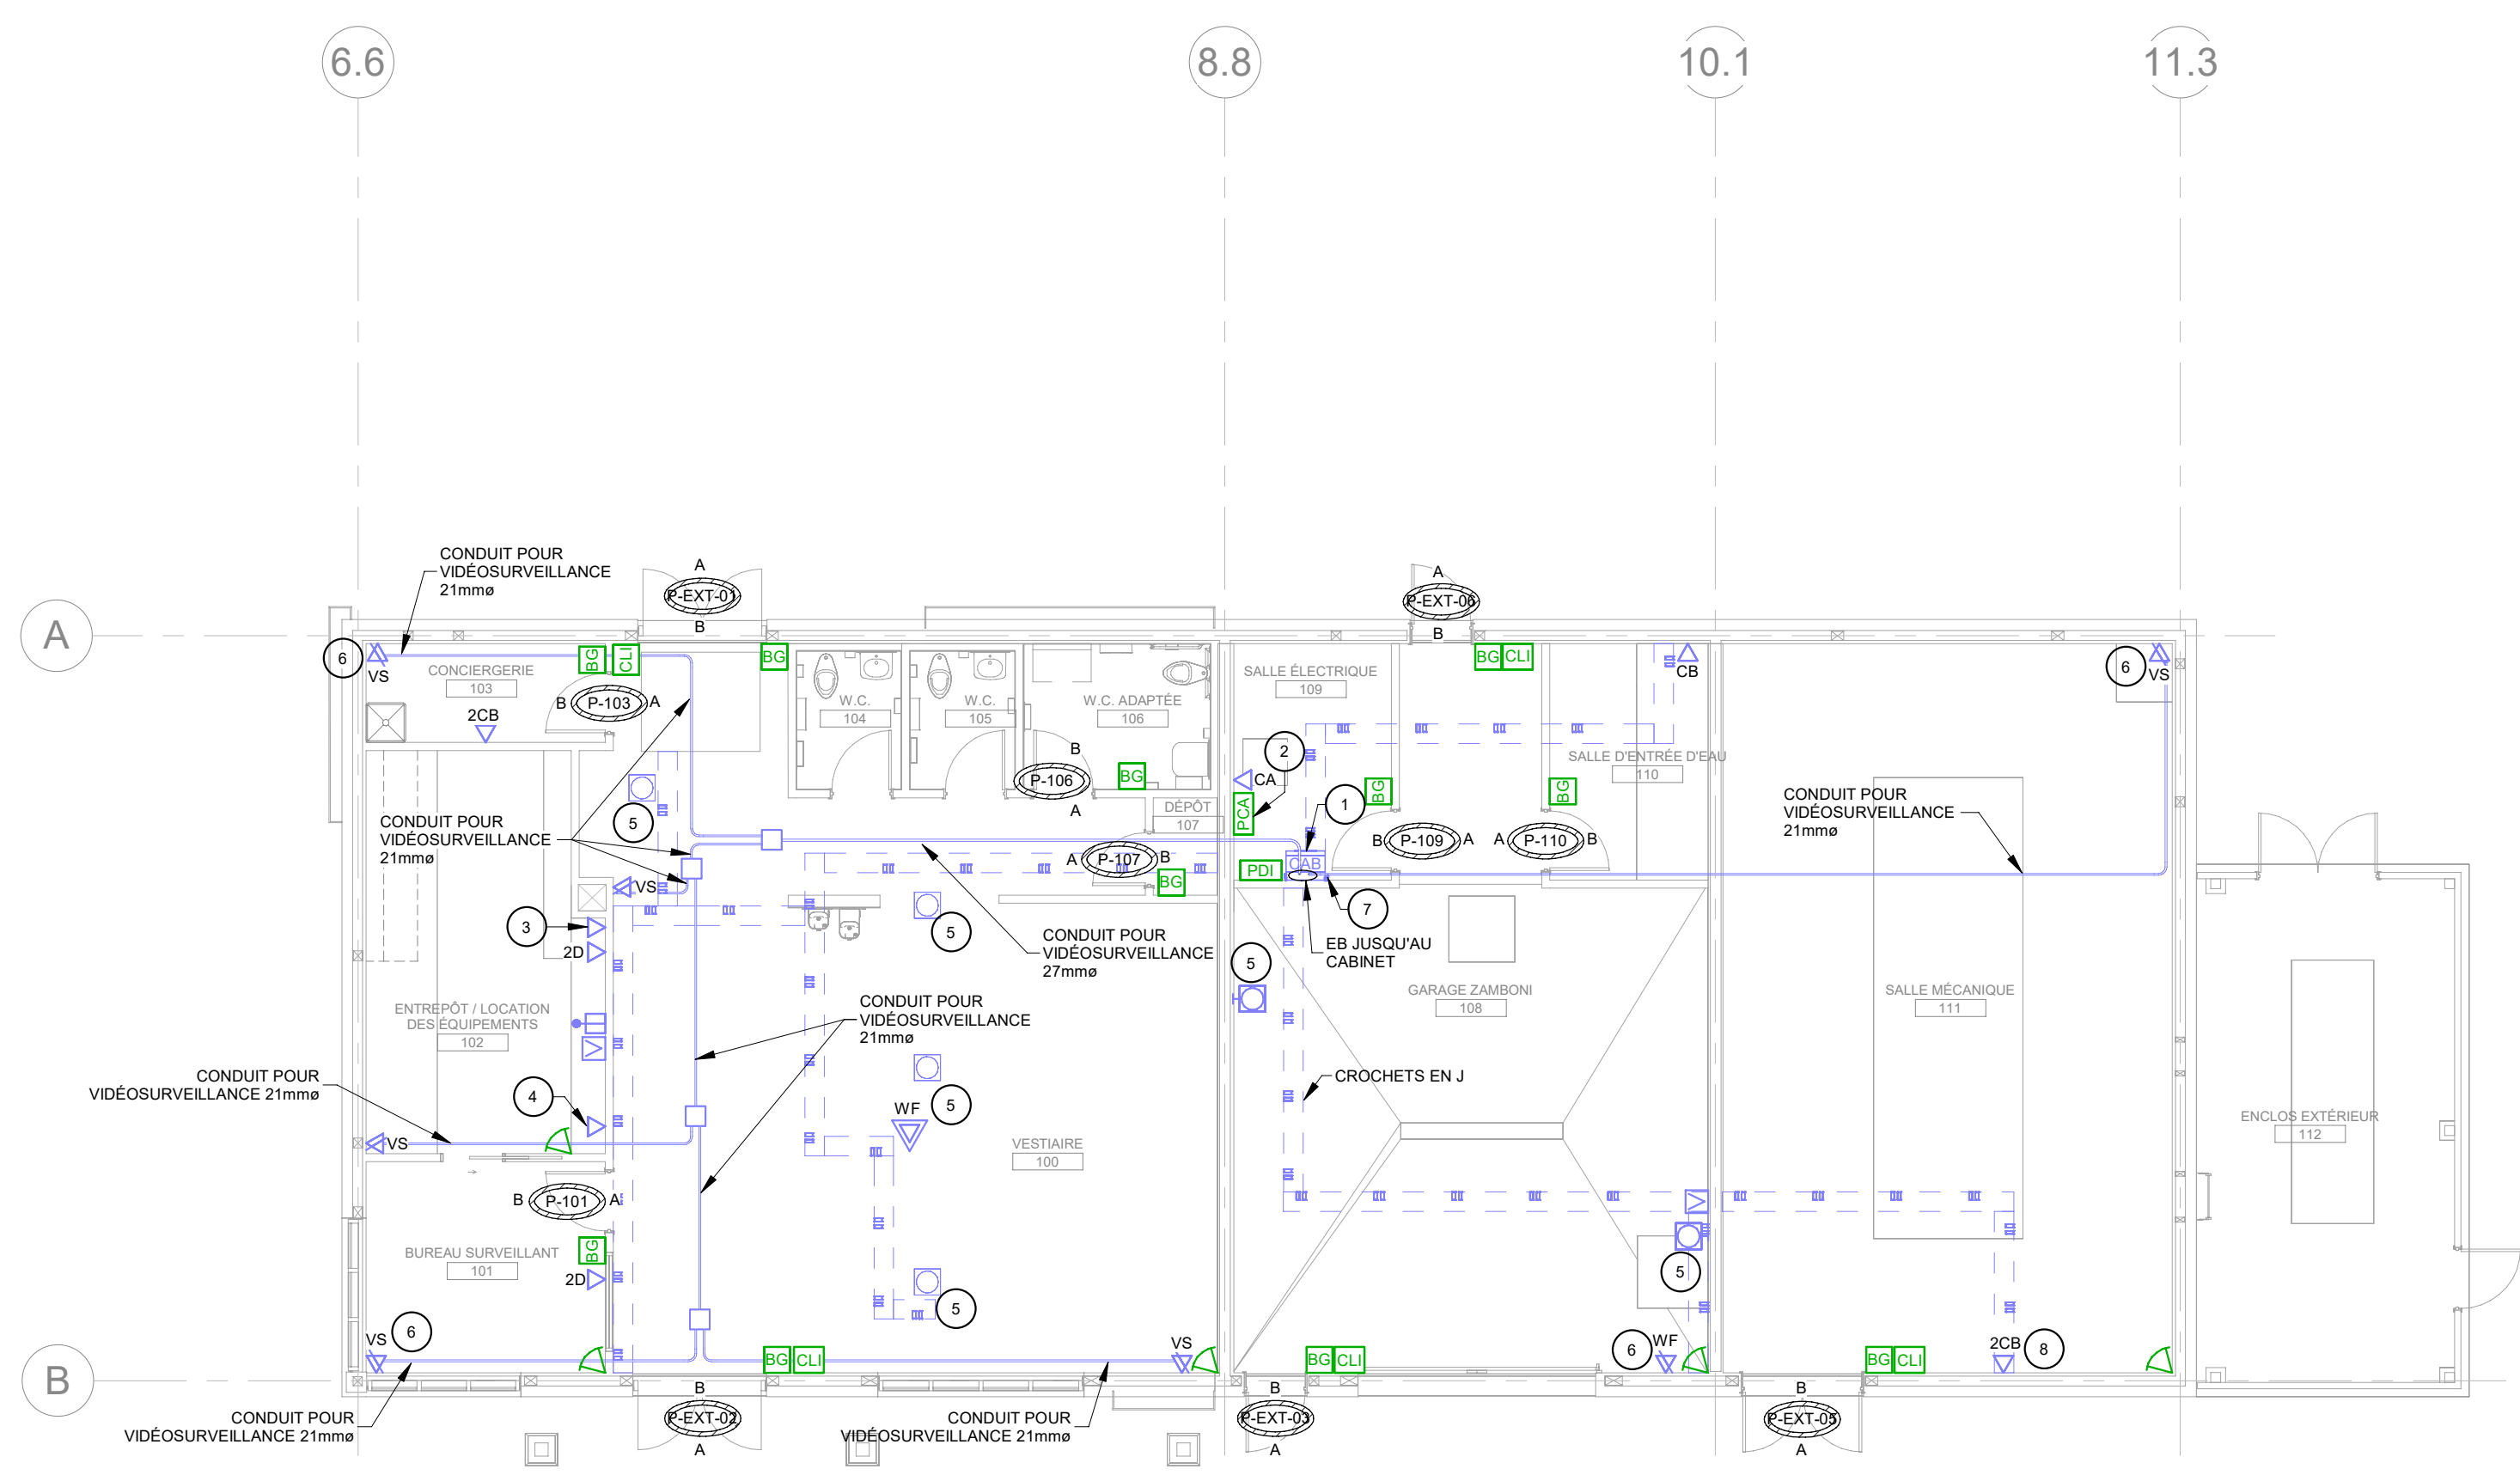

- 1 CABINET MURAL FOURNI ET INSTALLÉ PAR LE CLIENT.
- 2 GARNIR LE CROCHET D'ACCÈS FOURNI ET INSTALLÉ PAR L'ENTREPRENEUR.
FOURNIR LE RÉSEAU DE CONDUIT POUR RACCORDER DU PANNEAU À TOUTES LES
POUR CES COLÈQUES.
- 3 PRISE POUR PLAQUE DE CONTRÔLE DE SON TACTILE.
- 4 PRISE POUR L'ANTENNE BLUETOOTH.
- 5 FOURNIR UN RÉSEAU DE CROCHETS EN JEU/L'ANTENNE PARLEUR DANS LE CHA
ET LA SALLE (VOIE ÉLECTRIQUE, COORDONNER L'EMPLOI D'ACCÈS EXACT DES HAUT-
PARLEURS EN CHAÎNE, HAUT-PARLEURS FOURNIS ET INSTALLÉS PAR LE CLIENT.
- 6 PRÉVOIR UN PERÇEMENT POUR LE RACCORDEMENT PAR LE CLIENT DES CAMÉRA
SONS WIRELESS EXTÉRIEURS.
- 7 BARRE OMBILICulaire SECONDAIRE DE MISE À LA TERRE POUR LES ÉQUIPEMENTS
DE COMMUNICATION, FOURNI ET INSTALLÉ PAR L'ENTREPRENEUR EN ÉLECTRICIEN
INSTALLER LA BARRE ENDOUSSOUS DU CABINET MURAL.
- 8 FOURNIR LE PANNEAU DE MONTAGE ET L'INSTALLER PAR L'ENTREPRENEUR. COORDONNER
L'EMPLOI D'ACCÈS DU PANNEAU AVEC L'ENTREPRENEUR DE RÉFRIGÉRATION.

CHALET, PATINC
POUR SOUMISSIONS

Conçu par:	M. BAAR	Page T-201 DE 1
Dessiné par:	R. ST-LOUIS	
Vérifié par:	R. SIDANI	
Dossier BPA:	25-13561	
Dossier BBC:	25-1811	

LES PLANS DU PROJET DOIVENT ÊTRE CONSULTÉS EN COULEUR
AUX FINS DE COMPRÉHENSION.

	CÂBLAGE STRUCTURE
	CONTRÔLE D'ACCÈS ET VIDÉOSURVEILLANCE
	EXISTANT