

16.0 ENTRÉE ÉLECTRIQUE, DISTRIBUTION ET GÉNÉRAL (SUITE ...)

Note 16.0.0
AUCUN FIL APPARENT NE SERA TOLÉRÉ POUR L'ALIMENTATION ET LE RACCORDEMENT DES OUVRAGES PORTES AUTOMATIQUES, AU BESOIN L'ÉLECTRICIEN DEVRA PASSER LES FILS PAR LES MENEaux DU VESTIBULE.

Note 16.0.10
FOURNIR ET INSTALLER UN RÉSEAU DE CONDUITS DE PVC TEL QUE DÉFINI À LA LÉGENDE ÉLECTRIQUE, LORSQUE LES RETOURS DE VENTILATION SONT DE TYPE PLENUM LES CONDUITS DOIVENT ÊTRE DE CATÉGORIE 5.

NOTE 16.0.11
L'ENTREPRENEUR DEVRA RETIRER LES CÂBLES DES PRISES DATA, DES CAMÉRAS, DES PRISES ET DES ÉQUIPEMENTS CONDAMNÉS OU DÉMONTÉS JUSQU'À LA SOURCE.

NOTE 16.0.12
LORSQUE PLUSIEURS PRISES ÉLECTRIQUES, INFORMATIQUES ET/OU TÉLÉPHONIQUES SONT IDENTIFIÉES AU PLAN UNE À CÔTÉ DE L'AUTRE AVEC UNE COTE CENTRE, CELLES CI DEVRONT ÊTRE INSTALLÉES LE PLUS PRÈS POSSIBLE L'UNE DE L'AUTRE EN RESPECTANT LES HAUTEURS SPÉCIFIÉES.

NOTE 16.0.13
AUCUNE DIMENSION NE PEUT ÊTRE MESURÉE DIRECTEMENT AU PLAN POUR POSITIONNER LES PRISES ÉLECTRIQUES, INFORMATIQUES ET TÉLÉPHONIQUES. SE RÉFÉRER AUX COTES PRÉSENTES AU PLAN OU CONFIRMER SI REQUIS LE POSITIONNEMENT AVEC LE RESPONSABLE DE PROJET DE LA SAQ.

NOTE 16.0.14
EN CAS DE PRISE DE POSSESSION DU LOCAL, LA SAQ ENVERA DE L'ÉLECTRICIEN ÉCARTANT DES TRAVAUX AU CHANTIER, UNE ATTESTATION CONFIRMANT QUE SEULE LA SONDMANION ÉLECTRIQUE DU SAQ LONGUE PAR LA SAQ EST LAUE PAR LE COMPTÉUR ÉLECTRIQUE DÉDÉ EXCLUSIVEMENT À L'USAGE DE CETTE DÉRIVÉE. EN CAS DE DOUTE, LA SAQ POURRAIT DEMANDER UNE VALÉDATION EN ÉMISANT UN "BRIEF-CORRE".

16.5 ÉCLAIRAGE

Note 16.5.1
LES APPAREILS D'ÉCLAIRAGE ET LE CONTRÔLE DE CEUX CI DOIVENT ÊTRE TEL QUE SPÉCIFIÉ AU TABLEAU SUR LA PAGE « LÉGENDE PLAFOND RÉFLECTIF ET ÉCLAIRAGE » AUCUNE ÉQUIVALENCE ACCEPTÉE.

TOUTEFOIS, DANS UNE OPTIQUE DE RÉDUCTION DE CÔÛTS, LES RELAIS AVEC UN FAIBLE AMPÉRAGE (EX. 5AMP) PEUVENT ÊTRE INSTALLÉS DANS L'AIRE DE VENTE AVEC UNE INSTALLATION DE TYPE «CHICAGO PLENUM» (DANS LE CAS D'UN PLAFOND À STRUCTURE APPARENTE), LES BOÎTIERS « CHICAGO PLENUM » DEVRONT ÊTRE PEINTS DE LA MÊME COULEUR QUE LE PLAFOND AFIN Q'ILS SOIENT DISIMULÉS.

POUR LE CÂBLAGE DATA REQUIS DE TYPE FTS OU F76, IL N'EST PAS OBLIGATOIRE DE PASSER DANS DES CONDUITS EMT. TOUTEFOIS, DANS LE CAS D'UN PLAFOND À STRUCTURE APPARENTE, LA COULEUR DU CÂBLAGE DEVRA ÊTRE AGENCÉ AVEC LA COULEUR DE PEAUURE DE LA STRCUTURE (À COORDONNER AVEC LE RESPONSABLE DE PROJET SAQ).

Note 16.5.2
LES NIVEAUX D'ÉCLAIREMENT MAINTENUS UNIFORMES ET MESURÉS À PLUS DE 12" D'UN LUIR, DOIVENT PERMETTRE L'AJUSTEMENT PAR UN CONTRÔLEUR GRAPHIQUE (VOIR TABLEAU DES LUMINAIRES) AUX VALEURS SUIVANTES, SUR TOUTE L'AIRE CONCERNÉE

- 200-250 LUX MESURÉ AU PLANCHER DANS LES AIRES DE CIRCULATION ET SERVICES, TELS QUE : CORRIDORS, VESTIBULES, VESTIAIRES, TOILETTES, ET AUTRES LOCAUX DE MÊME NATURE.
- 300 LUX MESURÉ À 30" DU PLANCHER DANS LES AIRES GÉNÉRALES SUIVANTES: DÉPÔTS, SALLES DE REPOS, LOCAUX TECHNIQUES ET AUTRES LOCAUX DE MÊME NATURE.
- 400-450 LUX MESURÉ À 30" DU PLANCHER DANS LES BUREAUX.
- 500 LUX MESURÉ À 30" DU PLANCHER DANS LA PARTIE AIRE DE RÉCEPTION DES MARCHANDISES ET ENTREPÔSAGE.
- 700 LUX MESURÉ À 30" DANS L'AIRE DE VENTE (VOIR PLAN).

Note 16.5.3
SÉQUENCES D'OPÉRATIONS DU SYSTÈME

VOIR LÉGENDE D'ÉCLAIRAGE

SÉQUENCE D'OPÉRATIONS D'OUVETURE/FERMETURE

À L'ACTIVATION DE LA SÉQUENCE D'OUVETURE, TOUS LES LUMINAIRES DU SYSTÈME DOIVENT S'ALLUMER À UN NIVEAU QUI SERA DÉTERMINÉ LORS DE LA MISE EN SERVICE.

À L'ACTIVATION DE LA SÉQUENCE DE FERMETURE, TOUS LES LUMINAIRES DOIVENT S'ÉTEINDRE À L'EXCEPTION DES LUMINAIRES 24H QUI SERONT À 100% PEU IMPORTÉ LE NIVEAU DE GRADATION PRÉCÉDEMMENT APPLIQUÉ.

NOTES RELATIVES À L'INTERFACE GRAPHIQUE

L'INTERFACE GRAPHIQUE, À LA SUITE DE LA PROGRAMMATION, DOIT ARBORER LE LOGO DE LA SAQ LORSQU'EN MODE VIELLE. LES NOMS DES ZONES DE CONTRÔLE D'ÉCLAIRAGE DEVRONT RÉFLECTER LES ESPACES DANS CHAQUE SUCCESSIONALE ET DEVRONT ÊTRE DÉTERMINÉS AU PRÉALABLE, AVANT LA CONSTRUCTION (EX. ESPACE CELLIER, VESTIBULE).

16.6 RACCORDEMENT ÉLECTRIQUE DIVERS

Note 16.6.1
L'ENTREPRENEUR DEVRA RACCORDER TOUS LES ÉQUIPEMENTS OU APPAREILS INSTALLÉS PAR L'ENTREPRENEUR OU LA SAQ (EX. LAVE-VERRES, HUMIDIFICATEURS, SOUS-COMPTÉURS, OUVRAGES PORTES AUTOMATIQUES, ÉCLAIRAGE À L'INTÉRIEUR DES MEUBLES, ENSEIGNES LUMINEUSES INTÉRIEURES ET EXTERIEURES, ETC., ...).

Note 16.6.2
L'ENTREPRENEUR GÉNÉRAL SERA RESPONSABLE DE FOURNIR UNE COPIE DU PLAN DE PLAFOND PROPOSÉ AU SOUSMISSIONNAIRE.

Note 16.6.3
L'INSTALLATION DU SYSTÈME DE COMMUNICATION DOIT ÊTRE EFFECTUÉE PAR UN TECHNICIEN ACCRÉDITÉ PAR LA COMPAGNIE AYANT FOURNI LE SYSTÈME, SELON L'ÉCHÉANCIER PROPOSÉ PAR L'ENTREPRENEUR GÉNÉRAL.

Note 16.6.4
SI DES CLOCHES POUR L'ALARME-INCENDIE SONT REQUISES, ELLES DEVRONT ÊTRE INSTALLÉES À PLUS DE 10"0" DU SOL.

16.7 CONTRÔLE DE L'ÉCLAIRAGE

Note 16.7.1
LA SAQ POUVRRAIS QUE LES RELAIS POUR LE CONTRÔLE DE L'ÉCLAIRAGE SOIENT SITUÉS DANS L'ENTRÉE/PÔT PRÈS DES PANNEAUX ÉLECTRIQUES, IL EST TOUT DE MÊME RECOMMANDÉ AFIN DE RÉDUIRE LES CÔÛTS QUE LES RELAIS AVEC UN FAIBLE AMPÉRAGE (EX. 5AMP) SOIENT INSTALÉS DANS L'AIRE DE VENTE ET AVEC UNE INSTALLATION DE TYPE «CHICAGO PLENUM» DANS LE CAS D'UN PLAFOND À STRUCTURE APPARENTE À PRENDRE DE LA MÊME COULEUR QUE LE PLAFOND, DE PLUS, IL N'EST PAS OBLIGATOIRE POUR LE CÂBLAGE DATA REQUIS DE TYPE FTS OU F76 DE PASSER DANS DES CONDUITS EMT. À NOTER, LA COULEUR DU CÂBLAGE DATA DEVRA ÊTRE CHOISI EN CONSÉQUENCE (CÂBLAGE NOIR DANS LE CAS D'UN PLAFOND AVEC STRUCTURE APPARENTE ET À COORDONNER AVEC LE RESPONSABLE DE PROJET SAQ POUR UN PLAFOND AVEC STRUCTURE APPARENTE AYANT UN AUTRE TYPE DE FINITION).

Note 16.7.2
FOURNIR ET INSTALLER DEUX PHOTO-CELLULES : UNE POUR TOUS LES APPAREILS D'ÉCLAIRAGE EXTERIEURS ET LA SECONDE POUR LES ENSEIGNES, L'ÉCLAIRAGE EXTERIEUR DOIT ÊTRE COMMANDE PAR UNE CELLULE PHOTOÉLECTRIQUE AVEC RELAIS AU PANNEAU. UNE MINUTERIE DEVRA ÊTRE INSTALLÉE PRÈS DES PANNEAUX ÉLECTRIQUES, POUR LA FERMETURE DES ENSEIGNES À PROGRAMMER POUR 23H00 À CHAQUE JOUR.

16.8 SERVICE TÉLÉPHONIQUE, INFORMATIQUE ET SÉCURITÉ SAQ

Note 16.8.1
FOURNIR ET INSTALLER DANS LES ESPACES FERMÉS (CLOISONS ET RETOMBÉES DE GYPSES) ET PLAFOND OUVERT AVEC STRUCTURE APPARENTE, UN RÉSEAU COMPLET DE CONDUITS "EMT" ET PVC DE 1"0" POUR SERVICES DE COMMUNICATION INFORMATIQUE ET 1"0" 0" POUR TÉLÉPHONE. NE PAS INSTALLER DE CONDUITS AU DESSUS DE PLAFOND SUSPENDU (RÉCUPÉRER LE CÂBLAGE ENSEMBLE DE FAÇON ORDONNÉE).

DANS LE CAS D'UN PLAFOND À STRUCTURE APPARENTE SEULEMENT, FOURNIR ET INSTALLER UN RÉSEAU COMPLET DE DEUX CONDUITS DISTINCTS POUR LE CÂBLAGE DES CAMÉRAS ET DU SYSTÈME D'ALARME, ILS DEVRONT ÊTRE UTILISÉS UNIQUEMENT POUR LES ÉQUIPEMENTS DE SÉCURITÉ DE LA SAQ. LE FORAMT, LA QUANTITÉ ET LE PARCOURS DES CONDUITS "EMT" ET PVC SERONT PRÉCISÉS AU PLAN DE CONDUITS FOURNI PAR LA SAQ. TOUS LES CONDUITS ET BOÎTES DE JONCTION DOIVONT ÊTRE PEINTS TEL QUE LA STRUCTURE APPARENTE, DES FICELLES DE TIRAGE SERONT REQUISES POUR CHAQUE CONDUIT. ÉVITER AUTANT QUE POSSIBLE LES VIRAGES À 90° ET INSTALLER DES BOÎTES DE TIRAGE À CES ENDOITS.

Note 16.8.2
TOUTES LES SORTIES DE COMMUNICATION-INFORMATIQUE, SONT CONSTITUÉES D'UNE BOÎTE CONVENABLEMENT INSTALLÉE ET MUNIE D'UNE PLAQUE (BLANCHE) PRÊTE À RÉCEVOIR JUSQU'À QUATRE INTERFACES. LA PLAQUE DE SORTIE POUR LA TÉLÉPHONE SERA FOURNIE PAR LA COMPAGNIE DE TÉLÉPHONE MANDATÉE PAR LA SAQ.

Note 16.8.3
TOUS LES CONDUITS N'AURONT AUCUN CHANGEMENT DE DIRECTION DE PLUS DE 45°, DE FAÇON À ASSURER LE PASSAGE DES CÂBLES. À CETTE FIN, L'ENTREPRENEUR LAISSERA UN FIL DE TIRAGE EN NYLON, DANS LA COURSE DES CONDUITS, ELLE SERA ATTACHÉE AUX DEUX (2) EXTRÉMITÉS. PRÉVOIR UNE BOÎTE DE JONCTION, SI LA DISTANCE EXCÈDE 90 PIEDS.

Note 16.8.4
LE PROPRIÉTAIRE DEVRA FOURNIR UNE PRISE DE COURANT 120 VAC POUR LE BRANCHÉMENT DU SYSTÈME-TÉLÉPHONIQUE.

Note 16.8.5
LORSQU'IL Y A UNE STATION "INSITE TERMINAL" À L'EXTERIEUR DU LOCAL DE LA SAQ, LE PROPRIÉTAIRE DOIT FOURNIR UN CONDUIT RIGIDE EMT DE 9/8" - DU BIX DE LA STATION "INSITE TERMINAL" DU PROPRIÉTAIRE JUSQU'À LA ZONE DES PANNEAUX ÉLECTRIQUES DANS LE LOCAL DE LA SAQ - UNE FICELLE DE TIRAGE ET L'IDENTIFICATION DES BOÎTES DE TIRAGE SONT REQUISES. LE PROPRIÉTAIRE DOIT APPORTER LES FACILITES DANS LE BÂTIMENT DE LA SAQ - FUTURE POSITION DU BIX DE LA SAQ À ÊTRE DÉTERMINÉE PAR LE FOURNISSEUR DE TÉLÉPHONE À TITRE INFORMATIF. LE FOURNISSEUR DE SERVICES DE TÉLÉPHONE DE LA SAQ EST VIDEO TIRON ET IL UTILISE DES FILS DE TYPE 60AIAA-ROND.

16.9 ÉCLAIRAGE D'URGENCE

Note 16.9.1
FOURNIR ET INSTALLER UN SYSTÈME COMPLET D'ÉCLAIRAGE D'URGENCE FONCTIONNANT À 12 VOLTS C.C., POUVANT FONCTIONNER POUR UNE PÉRIODE DE TRENTE (30) MINUTES, CE SYSTÈME PERMETTRA L'ALIMENTATION DES LUMINAIRES D'URGENCE ET DE TOUS LES APPAREILS IDENTIFIÉS "SORTIE". LA CAPACITÉ SERA CALCULÉE EN FONCTION DES APPAREILS RACCORDEÉS ET DES DISTANCES ENTRE LES DIFFÉRENTES COMPOSANTES. DANS LE CAS DES SUCCESSIONALES DE LA BANNIÈRE DÉPÔTS, LES APPAREILS AU DESSUS DES ALLÉES DEVRONT ÊTRE PLACÉS DE FAÇON À NE PAS ÊTRE HEURTÉS PAR DES CHARIOTS ÉLÉVATEURS.

Note 16.9.2
L'ACCUMULATEUR DOIT ÊTRE DU TYPE AU PLOMB LONGUE DURÉE. LE CHARGEUR AUTOMATIQUE DOIT ÊTRE À 120 VOLTS C.A., D'UNE CAPACITÉ SUFFISANTE POUR RECHARGER COMPLETEMENT L'ACCUMULATEUR EN DEÇA DE VINGT-QUATRE (24) HEURES.

Note 16.9.3
L'UNITÉ DOIT ÊTRE COMPLÈTE AVEC TOUTES LES COMPOSANTES STANDARD TEL QUE : ACCUMULATEUR, CHARGEUR, RELAIS DE COMBINATION, CIRCUIT MINIME, FUSIBLE, DE PROTECTION DES CIRCUITS DE SORTIE, FUSIBLE DE PROTECTION DU CHARGEUR, TRANSFORMATEUR, LAMPE-TÉMOIN DE C.A., LAMPE-TÉMOIN DE BON FONCTIONNEMENT, BOUTON POUSSOIR D'ESSAI, CORDON C.A., ANS D'UN SUPPORT DE MONTAGE (MPA) LE TOUT TEL QUE L'APPAREIL "EMERGO-LITE" MODÈLE 2561-433 OU ÉQUIVALENT "LUMICELL".

Note 16.9.4
LES LUMINAIRES D'URGENCE EN SALLIE DOIVENT ÊTRE CONÇUS POUR FONCTIONNER À 24 VOLTS C.C.. LES LUMINAIRES DOIVENT ÊTRE DE TYPE EFS ET/OU EFS0, COMPLETS AVEC PLAQUES DE MONTAGE ET LAMPE DE 9 WATTS.

Note 16.9.5
LES CONDUCTEURS D'ALIMENTATION DES LUMINAIRES ET AUTRES APPAREILS D'URGENCE DOIVENT ÊTRE DE CUIRE ET DE CALIBRE APPROPRIÉ POUR QUE LA CHUTE DE TENSION NE DÉPASSE PAS 5 % DU VOLTAGE NOMINAL, LE TOUT SUIVANT LES RECOMMANDATIONS DU MANUFACTURIER. CES CONDUCTEURS DOIVENT ÊTRE INSTALLÉS DANS DES CONDUITS DE TYPE E.M.T.

Note 16.9.6
AUCUN ACCUMULATEUR NE SERA TOLÉRÉ DANS L'AIRE DE VENTE. UTILISER UNIQUEMENT DES TÊTES D'ÉCLAIRAGE AU PLAFOND.

16.10 SYSTÈME DE CHAUFFAGE

Note 16-10-1
non

Note 16.10.2
LES RELAIS DOIVENT ÊTRE DE TYPE SILENCIEUX À ACTION THERMIQUE, ILS DOIVENT ÊTRE INTÉGRÉS À L'APPAREIL ET MUNIS DE TRANSFORMATEURS INTÉGRÉS LORSQUE REQUIS.

Note 16-10-4
FOURNIR ET INSTALLER DES RIDEAUX D'AIR CHAUD ET/OU AÉROTHERMIQUES-VOIR PLANS POUR SPÉCIFICATIONS ET EMPACEMENTS.

16.11 SYSTÈME DE COMMUNICATION ET DE SONORISATION

Note 16.11.1
PLAGE 218 FT 4 EN CUIVRE, INSTALLÉ DANS DES CONDUITS "EMT". IL EST EXIGÉ QUE LES CÂBLES SOIENT MARQUÉS FTS SI ILS PASSENT DANS L'ENTRÉE/AFOND, SAUF SI CES CÂBLES SONT DANS UNE CANALISATION.

Note 16.11.2
L'ENTREPRENEUR GÉNÉRAL SERA RESPONSABLE DE FOURNIR UNE COPIE DU PLAN DE PLAFOND PROPOSÉ AU SOUSMISSIONNAIRE.

Note 16.11.3
LA SAQ PROPOSE DEUX COMPAGNIES RÉPONDANT AUX NORMES SPÉCIFIÉES: L'INSTALLATION DU SYSTÈME DE COMMUNICATION DOIT ÊTRE EFFECTUÉE PAR UN TECHNICIEN ACCRÉDITÉ PAR LA COMPAGNIE AYANT FOURNI LE SYSTÈME, SELON L'ÉCHÉANCIER PROPOSÉ PAR L'ENTREPRENEUR GÉNÉRAL.

Note 16.11.4
AMPIFICATEUR 6W.

- HAUT-PARLEURS ENCASTRÉS OU SUSPENDUS (VOIR QUANTITÉS ET POSITIONNEMENTS AU PLAN DE PLAFOND)
- CONTRÔLES DE VOLUME SÉQUENTIELS AVEC PLAQUES EN ACIER INOXYDABLE.

Note 16.11.6
L'INSTALLATION COMPLÈTE DEVRA ÊTRE INCLUSE AU CONTRAT, AINSI QUE LA FORMATION REQUISE POUR LES APPAREILS FOURNIS.

- LE SOUSMISSIONNAIRE DEVRA FOURNIR LES FICHES TECHNIQUES DE TOUS LES ÉQUIPEMENTS EN PLACE.
- SOUS TOUTES RÉSERVES, LES DEMANDES D'ÉQUIVALENTS DEVRONT ÊTRE SOUMISES AU RESPONSABLE DE PROJET DE LA SAQ AVEC LES SPÉCIFICATIONS EN ÉQUIVALENCE. LE CHARGE DE PROJET DE LA SAQ SE RÉSERVE LE DROIT DE REFUSER TOUTES SOUMISSIONS INCOMPLÈTES.

NOTES ÉCLAIRAGE ET CONTRÔLES

1. L'ENTREPRENEUR ÉLECTRICIEN DEVRA MANDATER LE FOURNISSEUR D'APPAREIL D'ÉCLAIRAGE POUR LA MISE EN MARCHÉ ET LA PROGRAMMATION DES SYSTÈMES DE CONTRÔLE D'ÉCLAIRAGE, LE TECHNICIEN DE CONTRÔLE DES APPAREILS D'ÉCLAIRAGE SERA SOUS LA RESPONSABILITÉ DE L'ENTREPRENEUR ÉLECTRICIEN.

2. L'ENTREPRENEUR ÉLECTRICIEN DEVRA INCLURE DANS SA SOUMISSION LES FRAIS DU FOURNISSEUR D'APPAREIL D'ÉCLAIRAGE POUR LA MISE EN MARCHÉ DU SYSTÈME DE CONTRÔLE (PROGRAMMATION ET MISE EN MARCHÉ) ET LA COORDINATION ENTRE EUX (ENTREPRENEUR ÉLECTRICIEN ET SON SOUS-TRAITANT EN CONTRÔLE D'ÉCLAIRAGE).

NOTES GÉNÉRALES

VOIR LES PLANS D'ARCHITECTURE POUR LES COULEURS ET LES HAUTEURS DE MONTAGE, COORDONNER LE TOUT AVEC L'ENTREPRENEUR GÉNÉRAL.

LA LISTE DES ÉQUIPEMENTS ET LA CÉDULE D'ÉCLAIRAGE SONT DONNÉS À TITRE INDICATIF, SE RÉFÉRER AUX DESSINS DE DESIGN.

COORDONNER L'EMPLACEMENT FINAL DES PRISES ET DES SORTIES AVEC LE CLIENT.

TOUS LES LUMINAIRES DEVRONT ÊTRE APPROUVÉS CSA ET/OU UL ET PARTOUT OÙ C'EST POSSIBLE, ILS AURONT DES BALLASTS ÉLECTRONIQUES.

L'APPELLATION "24H" SIGNIFIE QUE L'APPAREIL DEVRA DEMEURER ALLUMÉ 24 HEURES (ÉCLAIRAGE DE SÉCURITÉ).

VALIDER, LES HAUTEURS D'INSTALLATION AVEC LE RESPONSABLE DE PROJET.

L'ENTREPRENEUR OU LE SOUS-TRAITANT DOIT TRANSMETTRE UNE COPIE DU PLAN DE PLAFOND AU FOURNISSEUR CHOISI.



CLIENT



Aménagement et design
Réseau des succursales

780, RUE TELLEUR, MONTRÉAL, QUÉBEC H3T 1Y6

PROFESSEUR



artesa

NOTES

TITRE DU PROJET

SAQ

SAQ VARENNES
VARENNES, QC, J3X 1P7

TITRE DU DESSIN

DEVIS
SAQ

DESCRIPTION

ÉLECTRIQUE

CONÇU PAR
H. HATTAB, CPI

DATE: JAAA-MM-JJ
2026-07-13

ÉCRIT PAR
F. BELAND, tech.

ÉCHELLE
AUCUNE

VERIFIÉ PAR
J. BACHKONGI, ING.

NO. DE PROJET
26-0094-02

APProuvé PAR
J. BACHKONGI, ing.

PLAN NO.
E002

LÉGENDE ÉLECTRIQUE

NOTE: HAUTEUR D'INSTALLATION DES SERVICES ÉLECTRIQUES, INFORMATIQUES ET TÉLÉPHONIQUES À 12" DU PLANCHER, SAUF INDICATION CONTRAIRE AU PLAN (HAUTEUR D'INSTALLATION INDIQUÉE EN POUCE À CÔTÉ DU SYMBOLE).

- CONDUITS RIGIDES SOUS LA DALLE DE BÉTON - UN (1) CONDUIT DE 1 1/2" Ø CONTINU POUR L'ÉLECTRICITÉ DES COMPTOIRS-CASSIÈRES ET UN (1) CONDUIT DE 1" Ø POUR LE SYSTÈME TÉLÉPHONIQUE ET INFORMATIQUE POUR CHAQUE COMPTOIR-CASSIÈRE.
- PRISE DE COURANT DUPLEX 15A-120 VOLTS SUR CIRCUIT INDÉPENDANT, FIXÉE AU BOUT D'UN "BX" LIBRE DE 24", SAUF INDICATION CONTRAIRE.
- PRISE DE COURANT DUPLEX 15A-120 VOLTS AU BOUT D'UN "BX" LIBRE DE 24", SAUF INDICATION CONTRAIRE.
- PRISE DE COURANT DUPLEX 15A 120V SUR CIRCUIT INDÉPENDANT, LORSQUE LA PRISE EST IDENTIFIÉE "LB", PRÉVOIR UN LOCK-BREAKER.
- PRISE DE COURANT DUPLEX 20A 120V SUR CIRCUIT INDÉPENDANT (POUR LES RÉFRIGÉRATEURS FERMÉS).
- PRISE DE COURANT (DOPT - DÉTECTION DE FUITE À LA MASSE) DUPLEX 15A 120V SUR CIRCUIT INDÉPENDANT (LA HAUTEUR D'INSTALLATION EST INDIQUÉE À CÔTÉ DE LA PRISE).
- PRISE DE COURANT DUPLEX 15A 120V POSITIONNÉE EN HAUTEUR DANS L'ALIGNEMENT DU MENEAU DE LA FENÊTRE POUR L'ALIMENTATION DES TOILES MOTORISÉES. COORDONNER LE POSITIONNEMENT AVEC LE FABRICANT DES TOILES ET LE CHARGÉ DE PROJET DE LA SAQ.
- PRISE DE COURANT DUPLEX 15A 120V

- PRISE DE COURANT SIMPLE 30 A VERROUILLABLE, 120 VOLTS DE GRADÉ INDUSTRIEL, TYPE LS-30R TEL QUE MODÈLE 2010 DE LEVITON (FIL NO 12 VERT REQUIS) (POUR CABINET INFORMATIQUE) NOTE: LE DISJONCTEUR SERA IDENTIFIÉ DE LA FAÇON SUIVANTE: RUBAN GOMME DE TYPE "TOUCH" AVEC LA MENTION "UPS SEULEMENT".
- BOÎTE DE SORTIE ÉLECTRIQUE À AFFLEUREMENT (MÊME NIVEAU QUE LE PLANCHER FINI) AVEC DUPLEX 15A / 120V SUR CIRCUIT INDÉPENDANT POUR INSTALLATION DANS UNE DALLE DE BÉTON AVEC REVÊTEMENT DE CARREAUX DE VINYLE TEL QUE LEGRAND 880 SÉRIE, MODÈLE À ÊTRE SPÉCIFIÉ PAR L'INGÉNIEUR EN ÉLECTRICITÉ. LE DISJONCTEUR DE PROTECTION 885TCAL (FINI ALUMINIUM) OU ÉQUIVALENT APPROUVÉ.
- OPÉRATEUR POUR TOILES MOTORISÉES, VOIR NOTES GÉNÉRALES.

- BOÎTE DE JONCTION DE DIMENSIONS INDIQUÉES.
- BOÎTE DE SORTIE 2 X 3 DÉDIÉE AU SYSTÈME D'ALARME. MUNIR CETTE BOÎTE D'UN CONDUIT JUSQU'À PROXIMITÉ DU BIX ET D'UNE FICELLE DE TIRAGE.

- BOÎTE DE SORTIE 2 X 3 ENCASTRÉE POUR CÂBLAGE INFORMATIQUE-TÉLÉPHONIQUE (BUREAUX).

- BOÎTE DE SORTIE 2 X 3 ENCASTRÉE À 54" DU PLANCHER, SAUF INDICATION CONTRAIRE AU PLAN. MUNIR CETTE BOÎTE D'UN CONDUIT JUSQU'À L'ENTREPLAFOND ET D'UNE FICELLE DE TIRAGE. L'ASSER UN DÉGAGEMENT DE 12" AU PÉRIMÈTRE DE CETTE BOÎTE POUR L'INSTALLATION DU TÉLÉPHONE.)

- SORTIE DU CONDUIT DE 1" Ø DANS LA DALLE POUR TÉLÉPHONE ET INFORMATIQUE. LE CONDUIT DEVAIT DÉPASSER DE LA DALLE DE 1" MIN. À 2" MAX.

- BOÎTE DE SORTIE (HAUTEUR INDIQUÉE AU PLAN), POUR RACCORDEMENT DES HAUT-PARLEURS DU SYSTÈME DE SONORISATION, CONDUIT 1" Ø JUSQU'À L'ENTREPLAFOND ACCESSIBLE.

- BOUTON POUSSOIR POUR OUVERTURE DES PORTES AUTOMATIQUES, CONDUIT 5/8" Ø JUSQU'À L'ENTREPLAFOND ACCESSIBLE C/A #181VT. COORDONNER LES BESOINS EN CONDUIT ET ALIMENTATION AVEC LE DISTRIBUTEUR DE BOUTONS ET LES PLANS D'ARCHITECTURE.

- THERMOSTAT PROGRAMMABLE, TEL QUE HONEYWELL VISONPRO 8000, MODÈLE TH8320U1016 HAUTEUR D'INSTALLATION: 60". FOURNI, INSTALLER ET RACCORDER PAR ENTREPRENEUR EN CVAC.

- THERMOSTAT PROGRAMMABLE, TEL QUE HONEYWELL VISONPRO 8000, MODÈLE TH8320U1016 HAUTEUR D'INSTALLATION: 60". FOURNI, INSTALLER ET RACCORDER PAR ENTREPRENEUR EN ÉLECTRICIEN.

- THERMOSTAT NON PROGRAMMABLE, TEL QUE MODÈLE STE403NP DE STELPRO OU ÉQUIVALENT APPROUVÉ. HAUTEUR D'INSTALLATION: 48". FOURNI, INSTALLER ET RACCORDER PAR ENTREPRENEUR ÉLECTRICIEN.

- SONDE DE TEMPÉRATURE TEL QUE HONEYWELL, MODÈLE C 7189U, POSITIONNEMENT À COORDONNER AVEC SAQ, FOURNI, INSTALLER ET RACCORDER PAR ENTREPRENEUR EN CVAC.

- MINUTERIE, CIE HONEYWELL (AISE TECHNOLOGIES), MODÈLE T1073-3W, LOCALISÉE PRÈS DES PANNEAUX ÉLECTRIQUES. HAUTEUR D'INSTALLATION À 60" CC. POSITIONNEMENT À COORDONNER AVEC SAQ, (POUR DES ENSEIGNES EXTÉRIEURES).

- CONTRÔLE DE VOLUME INDÉPENDANT, ±5 CONTRÔLES DE VOLUME SÉQUENTIELS 1 WATTS POUR L'ENTRÉE, LES BUREAUX ET L'AIRE DE REPOS.

- AMPLIFICATEUR TEL QUE TOA BG 2060, 60W AVEC SORTIE 70V, INCLUANT L'ENTRÉE POUR LA MUSIQUE, APPEL GÉNÉRAL, AUXILIAIRE, MODULE DE MUSIQUE EN ATTENTE ET SORTIE POUR LES HAUT-PARLEURS.

- MINUTERIE POUR SYSTÈME D'ÉVACUATION MUR D'UN CONTACTEUR 24V, FOURNI ET INSTALLÉ PAR L'ENTREPRENEUR EN CVCA ET RACCORDER PAR L'ENTREPRENEUR ÉLECTRICIEN.

- SONNETTE, CLOCHE GRISE DE 6" DE DIAMÈTRE, EDWARDS # 345-6NS, INSTALLER DANS L'ENTRÉE À 9'0" MIN. DU PLANCHER.

- CARILLON, MODÈLE EDWARDS # C210-W, UN DANS L'ENTRÉE À 11'4" DU PLANCHER ET UN DANS L'AIRE DE VENTE, POUR SONNETTE COM. LICENCES SI REQUIS.

- UN BOUTON POUSSOIR POUR SONNETTE À L'ÉPREUVE DES INTÉRIÈRES ET INSTALLÉ SUR LE CORDE À 60" DE HAUTEUR, TEL QUE LE MODÈLE # 1786 C DE EDWARDS.

- AÉROTHÈRME ÉLECTRIQUE ENCASTRÉ DE 44W OU 84W (VOIR SPÉCIFICATION AU PLAN) AVEC CONTACTEUR MAGNÉTIQUE ET THERMOSTAT MURAL AVEC COUVERCLE ANTI-VANDALE. TOUTS LES ARTICLES NÉCESSAIRES POUR L'ENCASTRICMENT AU MUR, SELON LES INDICATIONS SUR LE PLAN, MODÈLE SÉRIE 040 DE OUELLET, (5 REQUIS).

- PLINTHE ÉLECTRIQUE SÉRIE OFM DE OUELLET COULEUR BLANC OU ÉQUIVALENT APPROUVÉ, RELIÉ AU THERMOSTAT MURAL.

- POUR L'AIRE DE VENTE, PLINTHE DE CHAUFFAGE TYPE ARCHITECTURAL, AVEC GRILLE LINÉAIRE, TEL QUE SÉRIE 008 DE OUELLET OU ÉQUIVALENT, COULEUR: ARGENT, POSÉES AU MUR OU SUR PIÉDESTAL.

- SÈCHE MAIN EL NINO DE LA CIE STELPRO, FINI BLANC (INSTALLÉ À 48" DU PLANCHER).

LÉGENDE ÉLECTRICITÉ

* VOIR NOTE 10.11, DES NOTES GÉNÉRALES, FEUILLE 1.2, DES PLANS D'ARCHITECTURE.

HAUT-PARLEURS SUSPENDUS POUR PLAFOND, A. STRUCTURE, APPARENTE, AIRE DE VENTE, MODÈLE TOA Q-PE-304BK, COULEUR NOIR OU BLANC. (VALIDER LA COULEUR AVEC LE CHARGÉ DE PROJET SAQ). ENTREPÔT: TOA-PE-304, COULEUR BLANC. INSTALLER LE DÉSSUS À LA MÊME HAUTEUR QUE LES RAILS D'ÉCLAIRAGE, VOIR QUANTITÉ AU PLAN.

HAUT-PARLEURS ENCASTRÉS POUR PLAFOND DE TUILES ACOUSTIQUES OU GYPSE, MODÈLE BOSE FREE SPACE DS-16F, 70 VOLTS ET TOA-F-0322C, 70 VOLTS, VOIR QUANTITÉ AU PLAN.

RIDEAU D'AIR EN SURFACE (ENTRÉE) EXISTANT CONSERVÉ.

RIDEAU D'AIR ENCASTRÉ (VESTIBULE) EXISTANT CONSERVÉ.

AÉROTHÈRME EXISTANT CONSERVÉ.

BOÎTE DE JONCTION 4" x 4" - INSTALLER DANS L'ENTREPLAFOND POUR LE RACCORDEMENT DE L'ENSEIGNE LUMINEUSE. IDENTIFIER SUR LA BOÎTE DE JONCTION QUELLE SERVIRA UNIQUEMENT AU RACCORDEMENT DE L'ENSEIGNE LUMINEUSE. CETTE BOÎTE SERA SITUÉE PRÈS DE LA TRAPPE D'ACCÈS (S/L Y A LIÉU) ET RACCORDER SUR CIRCUIT INDÉPENDANT. L'ÉLECTRICIEN DEVA RACCORDER L'ENSEIGNE LORSQUE CELLE-CI SERA INSTALLÉE. LE RACCORDEMENT FINAL D'UNE OU DES ENSEIGNES INSTALLÉES) PAR D'AUTRES EST LA RESPONSABILITÉ DU PRÉSENT ENTREPRENEUR.

PRISE DE COURANT DUPLEX 15A 120V - INSTALLER AU BOUT D'UN "BX" LIBRE DE 12" Ø - SITUER DANS L'ENTREPLAFOND OU AU DESSUS DES GAINES DE CLIMATISATION. CES PRISES DOIVONT ÊTRE RELIÉES À UN CIRCUIT INDÉPENDANT, MUNI D'UN MÉCANISME DE VERROUILLAGE "LOCK BREAKER". IDENTIFIER AU PANNEAU ÉLECTRIQUE ÉCLAIRAGE DE SECOURS.

TRANSFO. TRANSFORMATEUR EXISTANT CONSERVÉ.

BOÎTE DE SORTIE ÉLECTRIQUE À AFFLEUREMENT (MÊME NIVEAU QUE LE PLANCHER FINI) AVEC DUPLEX 15A / 120V SUR CIRCUIT INDÉPENDANT POUR INSTALLATION DANS UNE DALLE DE BÉTON AVEC REVÊTEMENT DE CARREAUX DE VINYLE TEL QUE LEGRAND 880 SÉRIE, MODÈLE À ÊTRE SPÉCIFIÉ PAR L'INGÉNIEUR EN ÉLECTRICITÉ. LE DISJONCTEUR DE PROTECTION 885TCAL (FINI ALUMINIUM) OU ÉQUIVALENT APPROUVÉ.

OPÉRATEUR POUR TOILES MOTORISÉES, VOIR NOTES GÉNÉRALES.

BOÎTE DE JONCTION DE DIMENSIONS INDIQUÉES.

BOÎTE DE SORTIE 2 X 3 DÉDIÉE AU SYSTÈME D'ALARME. MUNIR CETTE BOÎTE D'UN CONDUIT JUSQU'À PROXIMITÉ DU BIX ET D'UNE FICELLE DE TIRAGE.

BOÎTE DE SORTIE 2 X 3 ENCASTRÉE POUR CÂBLAGE INFORMATIQUE-TÉLÉPHONIQUE (BUREAUX).

BOÎTE DE SORTIE 2 X 3 ENCASTRÉE À 54" DU PLANCHER, SAUF INDICATION CONTRAIRE AU PLAN. MUNIR CETTE BOÎTE D'UN CONDUIT JUSQU'À L'ENTREPLAFOND ET D'UNE FICELLE DE TIRAGE. L'ASSER UN DÉGAGEMENT DE 12" AU PÉRIMÈTRE DE CETTE BOÎTE POUR L'INSTALLATION DU TÉLÉPHONE.)

SORTIE DU CONDUIT DE 1" Ø DANS LA DALLE POUR TÉLÉPHONE ET INFORMATIQUE. LE CONDUIT DEVAIT DÉPASSER DE LA DALLE DE 1" MIN. À 2" MAX.

BOÎTE DE SORTIE (HAUTEUR INDIQUÉE AU PLAN), POUR RACCORDEMENT DES HAUT-PARLEURS DU SYSTÈME DE SONORISATION, CONDUIT 1" Ø JUSQU'À L'ENTREPLAFOND ACCESSIBLE.

BOUTON POUSSOIR POUR OUVERTURE DES PORTES AUTOMATIQUES, CONDUIT 5/8" Ø JUSQU'À L'ENTREPLAFOND ACCESSIBLE C/A #181VT. COORDONNER LES BESOINS EN CONDUIT ET ALIMENTATION AVEC LE DISTRIBUTEUR DE BOUTONS ET LES PLANS D'ARCHITECTURE.

THERMOSTAT PROGRAMMABLE, TEL QUE HONEYWELL VISONPRO 8000, MODÈLE TH8320U1016 HAUTEUR D'INSTALLATION: 60". FOURNI, INSTALLER ET RACCORDER PAR ENTREPRENEUR EN CVAC.

THERMOSTAT PROGRAMMABLE, TEL QUE HONEYWELL VISONPRO 8000, MODÈLE TH8320U1016 HAUTEUR D'INSTALLATION: 60". FOURNI, INSTALLER ET RACCORDER PAR ENTREPRENEUR EN ÉLECTRICIEN.

THERMOSTAT NON PROGRAMMABLE, TEL QUE MODÈLE STE403NP DE STELPRO OU ÉQUIVALENT APPROUVÉ. HAUTEUR D'INSTALLATION: 48". FOURNI, INSTALLER ET RACCORDER PAR ENTREPRENEUR ÉLECTRICIEN.

SONDE DE TEMPÉRATURE TEL QUE HONEYWELL, MODÈLE C 7189U, POSITIONNEMENT À COORDONNER AVEC SAQ, FOURNI, INSTALLER ET RACCORDER PAR ENTREPRENEUR EN CVAC.

MINUTERIE, CIE HONEYWELL (AISE TECHNOLOGIES), MODÈLE T1073-3W, LOCALISÉE PRÈS DES PANNEAUX ÉLECTRIQUES. HAUTEUR D'INSTALLATION À 60" CC. POSITIONNEMENT À COORDONNER AVEC SAQ, (POUR DES ENSEIGNES EXTÉRIEURES).

CONTRÔLE DE VOLUME INDÉPENDANT, ±5 CONTRÔLES DE VOLUME SÉQUENTIELS 1 WATTS POUR L'ENTRÉE, LES BUREAUX ET L'AIRE DE REPOS.

AMPLIFICATEUR TEL QUE TOA BG 2060, 60W AVEC SORTIE 70V, INCLUANT L'ENTRÉE POUR LA MUSIQUE, APPEL GÉNÉRAL, AUXILIAIRE, MODULE DE MUSIQUE EN ATTENTE ET SORTIE POUR LES HAUT-PARLEURS.

MINUTERIE POUR SYSTÈME D'ÉVACUATION MUR D'UN CONTACTEUR 24V, FOURNI ET INSTALLÉ PAR L'ENTREPRENEUR EN CVCA ET RACCORDER PAR L'ENTREPRENEUR ÉLECTRICIEN.

SONNETTE, CLOCHE GRISE DE 6" DE DIAMÈTRE, EDWARDS # 345-6NS, INSTALLER DANS L'ENTRÉE À 9'0" MIN. DU PLANCHER.

CARILLON, MODÈLE EDWARDS # C210-W, UN DANS L'ENTRÉE À 11'4" DU PLANCHER ET UN DANS L'AIRE DE VENTE, POUR SONNETTE COM. LICENCES SI REQUIS.

UN BOUTON POUSSOIR POUR SONNETTE À L'ÉPREUVE DES INTÉRIÈRES ET INSTALLÉ SUR LE CORDE À 60" DE HAUTEUR, TEL QUE LE MODÈLE # 1786 C DE EDWARDS.

AÉROTHÈRME ÉLECTRIQUE ENCASTRÉ DE 44W OU 84W (VOIR SPÉCIFICATION AU PLAN) AVEC CONTACTEUR MAGNÉTIQUE ET THERMOSTAT MURAL AVEC COUVERCLE ANTI-VANDALE. TOUTS LES ARTICLES NÉCESSAIRES POUR L'ENCASTRICMENT AU MUR, SELON LES INDICATIONS SUR LE PLAN, MODÈLE SÉRIE 040 DE OUELLET, (5 REQUIS).

PLINTHE ÉLECTRIQUE SÉRIE OFM DE OUELLET COULEUR BLANC OU ÉQUIVALENT APPROUVÉ, RELIÉ AU THERMOSTAT MURAL.

POUR L'AIRE DE VENTE, PLINTHE DE CHAUFFAGE TYPE ARCHITECTURAL, AVEC GRILLE LINÉAIRE, TEL QUE SÉRIE 008 DE OUELLET OU ÉQUIVALENT, COULEUR: ARGENT, POSÉES AU MUR OU SUR PIÉDESTAL.

SÈCHE MAIN EL NINO DE LA CIE STELPRO, FINI BLANC (INSTALLÉ À 48" DU PLANCHER).

TABLEAU DISTRIBUTION ÉLECTRIQUE

SYMBOLE	DESCRIPTION	MONTAGE	REMARQUES
OU	PANNEAU DE DISTRIBUTION	SURFACE OU ENCASTRÉ	C/A PORTE AVEC SERRURE MONTÉE SUR CHARNIÈRES
	TRANSFORMATEUR	AU SOL OU FIXER AU MUR	-
	INTERRUPTEUR DE SÉCURITÉ	SURFACE	CAPACITÉ DE X AMPÈRES
	INTERRUPTEUR DE SÉCURITÉ SANS FUSIBLES	SURFACE	CAPACITÉ DE 30 AMPÈRES, SANS FUSIBLES
	INTERRUPTEUR DE SÉCURITÉ AVEC FUSIBLES	SURFACE	CAPACITÉ DE 30 AMPÈRES, AVEC FUSIBLES DE 20 AMPÈRES
	BOÎTE DE JONCTION OU DE TIRAGE	SURFACE OU ENCASTRÉ	-
	EMBASE	SURFACE	-
	DÉMARREUR MAGNÉTIQUE À 120V	SURFACE	-
	DÉMARREUR MAGNÉTIQUE À 208V	SURFACE	-
	DÉMARREUR MAGNÉTIQUE À 600V	SURFACE	-
	CONTACTEUR MAGNÉTIQUE À 120V	SURFACE	-
	CONTACTEUR MAGNÉTIQUE À 208V	SURFACE	-
	CONTACTEUR MAGNÉTIQUE À 600V	SURFACE	-
	RACCORD DIRECT	SURFACE	-
	TRANSFO. TRANSFORMATEUR BASSE TENSION POUR ROBINETS ET/OU DISTRIBUTEUR DE SAVON	-	FOURNI PAR D'AUTRE À INSTALLER DANS UNE BOÎTE DE JONCTION; RACCORDER LE 120V UNIQUEMENT, À RACCORDER AU CIRCUIT DE PRISES LE PLUS PRÈS SELON LES RECOMMANDATIONS DU MANUFACTURIER.
	OUVRE-PORTE AUTOMATIQUE	ENCASTRÉ	L'OUVRE-PORTE AUTOMATIQUE EST FOURNI ET INSTALLÉ PAR L'ENTREPRENEUR GÉNÉRAL.
	BORNE DE RECHARGE DE VÉHICULE ÉLECTRIQUE	-	MODÈLE À VALIDER AVEC LE CLIENT

TABLEAU DES APPAREILS DE CHAUFFAGE, VENTILATION ET CLIMATISATION (CVC)

SYMBOLE	DESCRIPTION	MANUFACT.	MODÈLE	TENSION	REMARQUES
	RELAIS BASSE TENSION (24V)	STELPRO OUELLET	SÉRIE RE308 SÉRIE RC840	-	RELAIS BASSE TENSION (24V) MODULANT (FOURNI ET INSTALLÉ PAR ÉLECTRICIEN)
	THERMOSTAT À ACTION INVERSE	EXISTANT	-	-	FOURNI ET INSTALLÉ PAR L'ENTREPRENEUR EN MÉCANIQUE ET RACCORDER PAR L'ENTREPRENEUR ÉLECTRICIEN AVEC SECTIONNEUR.
	CHAUFFE-EAU	-	-	-	FOURNI ET INSTALLÉ PAR L'ENTREPRENEUR EN MÉCANIQUE ET RACCORDER PAR L'ENTREPRENEUR ÉLECTRICIEN AVEC SECTIONNEUR.
	SERPENTIN DE CHAUFFAGE ÉLECTRIQUE	-	-	-	FOURNI ET INSTALLÉ PAR L'ENTREPRENEUR EN MÉCANIQUE ET RACCORDER PAR L'ENTREPRENEUR ÉLECTRICIEN AVEC SECTIONNEUR.
	BOUTON À VOLUME D'AIR VARIABLE	-	-	-	FOURNI ET INSTALLÉ PAR L'ENTREPRENEUR EN MÉCANIQUE ET RACCORDER PAR L'ENTREPRENEUR ÉLECTRICIEN.
	MOTEUR MONOPHASE	-	-	-	FOURNI ET INSTALLÉ PAR L'ENTREPRENEUR EN MÉCANIQUE ET RACCORDER PAR L'ENTREPRENEUR ÉLECTRICIEN.
	MOTEUR TRIPHASE	-	-	-	FOURNI ET INSTALLÉ PAR L'ENTREPRENEUR EN MÉCANIQUE ET RACCORDER PAR L'ENTREPRENEUR ÉLECTRICIEN.
	PLINTHE DE CHAUFFAGE ÉLECTRIQUE DE TYPE STANDARD	OUELLET	SÉRIE OFM	-	-
	DÉMARREUR MANUEL À 120V c/a PROTECTION THERMIQUE ET LAMPE TÉMOIN	-	-	-	-

TABLEAUX DIAGRAMME DE DISTRIBUTION

SYMBOLE	DESCRIPTION	REMARQUES
	PANNEAU ÉLECTRIQUE	XXX: NOM DU PANNEAU ICC: COURANT DE COURT-CIRCUIT
	SECTIONNEUR	XXXX: TENSION XXXX: AMPÉRAGE FXXXX: FUSIBLE
	SECTIONNEUR	XXXX: TENSION XXXX: AMPÉRAGE FXXXX: FUSIBLE
	TRANSFORMATEUR	-
	BOÎTE DE MESURAGE HYDRO-QUÉBEC	-
	EMBASE DE MESURAGE HYDRO-QUÉBEC	-
	MINUTERIE	-
	CONTACTEUR	-
	DISJONCTEUR MAÎTRE	-
	BARRE DE MISE À LA TERRE	-
	MISE À LA TERRE	-
	NU - MISE À LA TERRE	-
	ESPACE TÉLÉCOMMUNICATIONS	-

INDICATEUR DE SORTIE "SORTIE"

SYMBOLE	DESCRIPTION
	INDICATEUR DE SORTIE AU MUR
	INDICATEUR DE SORTIE AU PLAFOND
	BATTERIE 2 PHARES LED C/A INDICATEUR DE SORTIE

Grille d'analyse de code	CCQ 2015 - Partie 3		
Protection contre l'incendie	Séparation des usages principaux	n/a	3.1
	☒ Construction combustible	3.1.4.1, matériaux combustibles autorisés, indice propagation flamme surface exposée d'un isolant en mousse plastique doit être d'au plus 500	3.1.4
	Dispositif d'obturation	☒ SCF 45 min ou 60 min = D.O. 45 min ☐ SCF 90 min = D.O. 60 min ☐ SCF 120 min = D.O. 90 min ☐ SCF 3 hrs = D.O. 120 min ☐ SCF 4 hrs = D.O. 3 hrs	3.1.8.4
Matériaux de revêtement intérieur	Indice de propagation de la flamme	Max 150	3.1.13.2
Sécurité incendie des bâtiments	Classification du bâtiment et DRF pour l'ensemble du bâtiment	Le plus restrictif s'applique	3.2
	3.2.2.68 Bâtiment du groupe E, au plus 2 étages, aire maximale 1250m²	Type de const. autorisé	3.2.2.20-90
		Planchers	Comb. 45 min
		Toits	n/a
		Mezzanine	n/a
		Structure	égal à la construction qu'ils supportent
Sécurité dans les aires de plancher	Séparation des suites	n/a	3.3
	Porte de sorties	3.3.1.5 1) d) Usage E - non glacé > D.P. 15 m = 2 portes de sortie espace client	3.3.1.1, 3.3.1.5
	Distance entre les portes de sortie (si 2 portes)	1/3 de la grande diagonale (plus courte distance de la fumée)	3.3.1.6 & 3.4.2.5
	Corridors communs (largeur)	Usage : E 30 m	3.3.1.9
	Sens d'ouvertures des portes	Dans le sens d'évacuation sauf pièce < 60 personnes ou F1: Requis intérieur de la suite	3.3.1.11
	Largeur de portes	Capacité d'un accès à l'issue 128 pers X 6,1 mm = 841,8mm	3.3.1.13
	Portes et Panneaux transparents	Meneaux, marquage ou autres éléments requis pour la visibilité des portes, panneaux latéraux translucides et de panneaux entièrement vitrés (contraste visuel, 50mm minimum de hauteur, pleine largeur du panneau vitré, situés entre 1350mm et 1500mm au-dessus du plancher)	3.3.1.10
	Locaux de conciergerie et produits d'entretien	☐ Glacé: SCF 0 HR ☒ Non glacé: SCF 1 HR	3.3.1.21
Grille d'analyse de code	CCQ 2015 - Partie 3		
Exigence relative aux issues	Nombre minimal d'issues	Non glacé > 60 pers, E > 150 m² > D.P. 15 m	3.4
	Distance minimale entre deux issues (parcours le plus court de la fumée)	Aire de plancher sans corridor commun	3.4.2.1, 3.4.2.3
	Distance de parcours maximale vers au moins une issue si l'aire de plancher en comporte plus qu'une	1/2 de la grande diagonale sans être inférieur à 9m	3.4.2.5
Dimensions des issues	Largeur et hauteur des issues	Corridor 1,1m ou 6,1 mm / personne 841,8 mm 1100 mm min. requis	3.4.3, 3.4.3.2
	Hauteur libre des issues	Hauteur libre des baies de portes ferme porte ou autre dispositif peut réduite à 2030 mm 1980 mm	3.4.3.4
Signalisation d'issues requise	Quel	☐ Oui ☒ Non	3.4.5.1
Caractéristiques des issues	Portes d'issues ouvrant dans le sens de l'issue: Requis	Dispositifs de fermeture des portes (ferme-porte): Requis	3.4.6.12
	Dispositifs d'ouverture des portes (barre panique): Non requis	Sécurité incendie des banques et établissements commerciaux	3.4.6.13 & 3.1.8.14
	Serrure permise sur porte principale puisque 2e issue		3.4.6.16, 3.4.6.17
Exigences de salubrité	Les équipements sanitaires non modifiés desservant une partie de bâtiment transformée doit être conforme à 3.7.2 si le nombre de personnes augmente de plus de 25 personnes		3.7
	Nombre de WC existants non transformés	1 WC hommes - 1 WC femmes	3.7.2.2
	Nombre de lavabo: 1 dans chaque WC		3.7.2.3
Accessibilité	Domaine d'application	Entrée sans obstacle exigée (50%) Existant non modifié	3.8
	Aires où un parcours sans obstacle est exigé	Requis dans toute la suite	3.8.2.2, 3.8.2.3
	Mécanisme d'ouverture électrique	Non requis mais existant conservé	3.8.2.7
	Équipement sanitaire	2 WC universels fournis	3.8.2.8
	Signalisation	☒ Entrée sans obstacle ☒ Salles de toilettes sans obstacles	3.8.2.10
Normes de conception	Largeur minimale des accès	920 mm	3.8.3.2
	Aire de manœuvre entre des portes d'un vestibule WC accessible aux handicapés dans tous les étages	1200 mm	3.8.3.6
	Largeur libre des portes	800 mm	3.8.2.11, 3.8.3.19 et 3.8.3.20
	Comptoir de plus de 2 m doit avoir une section sans obstacle d'au moinsbas de 760 mm (30") large	Non requis	
	À 965 mm (34") du sol et avec dégagement des pieds de 685 mm (27") de haut		
	Fontaine pour handicapé	Non requis	

LÉGENDE - DESSINS

- LES ÉQUIPEMENTS EN LIGNES CONTINUES ET DE COULEUR PÂLES MONTRENT LES OUVRAGES EXISTANTS.
- LES ÉQUIPEMENTS EN TRAITS POINTILLÉS ET DE COULEUR FONCÉES MONTRENT LES OUVRAGES À ENLEVER.
- LES ÉQUIPEMENTS EN LIGNES CONTINUES FONCÉES MONTRENT LES OUVRAGES PROPOSÉS.



CLIENT

Aménagement et design Réseau des succurs

$R(X)-B$
 $R(X)-BS$
 $R(X)-N$
 $R(X)-NS$



 $S(X)$

LISTE DES GRADATEURS /									
INTERRUPTEUR SUR L'INTERFACE GRAPHIQUE NP0D TOUCH									
ZONE	TYPES	#0 RELAIS	TYPE0 GRADATION	GRADATEUR	RELAIS	INTERRUPTEUR	SCÈNE 1 OUVERTURE	SCÈNE 2 FERMETURE	SCÈNE 3 100%
ILÔTS	S20	#33	0-10V	X	NP 16 (DP1)	NP0D (SW6)	50%	0%	100%
ILÔTS 24H	S24H	#32	0-10V	X	NP 16 (DP2)	NP0D (SW6)	50%	100%	100%
RAIN / CELLIER	D3-N / D4-N	#22	ELV/PHASE	X	NP 16 (DP1)	NP0D (SW6)	90%	0%	100%
ENSEIGNE CELLIER	ENSEIGNE CELLIER	#27	N/A	X	NP20 PL (PP1)	NP0D (SW6)	ON	OFF	ON
AU-DESSUS CAISSES LINÉAIRES	08-N	#19	N/A	X	NP 16 (DP1)	NP0D (SW6)	70%	0%	100%
AU-DESSUS CAISSES RAILS	D3-N / D4-N	#16	ELV/PHASE	X	NP 16 (DP2)	NP0D (SW6)	90%	0%	100%
MURALES		#31, #29, #30	0-10V	X	NP 16 (DP1)	NP0D (SW6)	ON	OFF	ON
VESTIBULE	B-B	#26	0-10V	X	NP 16 (DP1)	NP0D (SW6)	90%	0%	100%
ARMOIRES VITRÉES	PRISES DUPLEX	#20	N/A	X	NP20 PL (PP1)	NP0D (SW6)	ON	OFF	ON
ENTRÉPÔT	P1 et P2	#35	0-10V	X	NP 16 (DP1)	NP0DMA (SW3)	100%	0%	100%
ENTRÉPÔT 24H	P1 ET P2	N/A	N/A		NON CONTRÔLÉ, RACCORDÉ DIRECTEMENT AU PANNEAU				
BUREAU	J1 et K3	#17	0-10V	X	WSXA (S03)	WSXA (S03)			
CUISINE	J4	#24	0-10V	X	WSXA (S03)	WSXA (S03)			
ENTRETIEN	G4	#18	N/A		WSXA (S04)	WSXA (S04)			
SALLE DE BAIN	G4	#25, #26	N/A		WSXA (S04)	WSXA (S04)			

TABLEAU D'ÉCLAIRAGE ET CONTRÔLES PROVENANT DES PLANS D'ARCHITECTURE
TABLEAU EST À TITRE INFORMATIF SEULEMENT, POUR LES REQUIS EN ÉLECTRICITÉ
COORDONNER LES TRAVAUX AVEC L'ENTREPRENEUR GÉNÉRAL ET LES PLANS
D'ARCHITECTURE

--	--	

1 nLight - CAISSE TYPE 0
Design 2

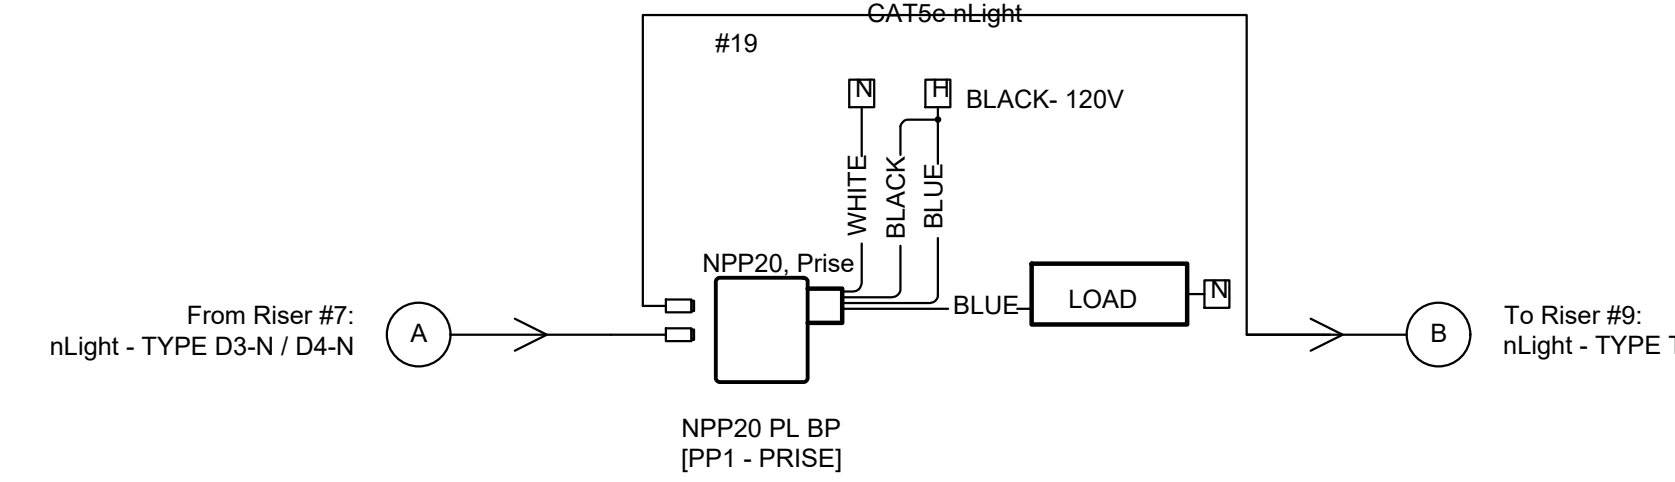


2 nLight - CAISSE TYPE D3-N / D4-N
Design 2



3 nLight - ENTREPOT
Design 2



4 nLight - PRISE
Design 2

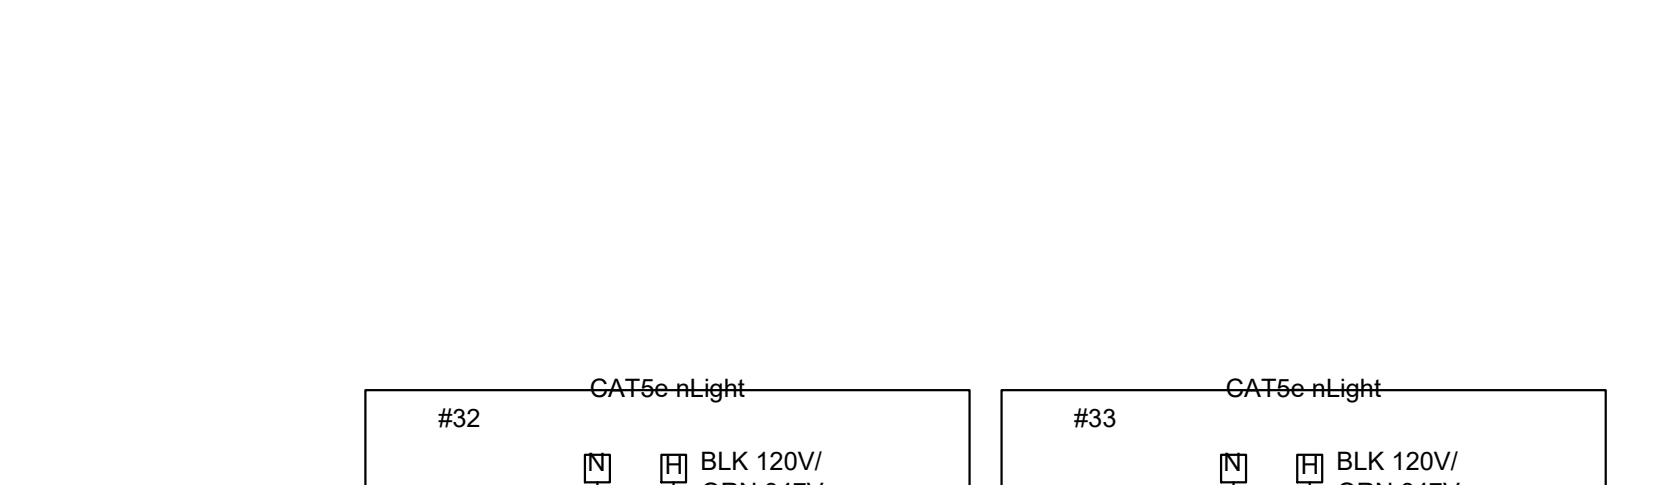


5 nLight - RAIL
Design 2




6 nLight - RAIL D3-N / D4-N
Design 2




7 nLight - TYPE D3-N / D4-N
Design 2

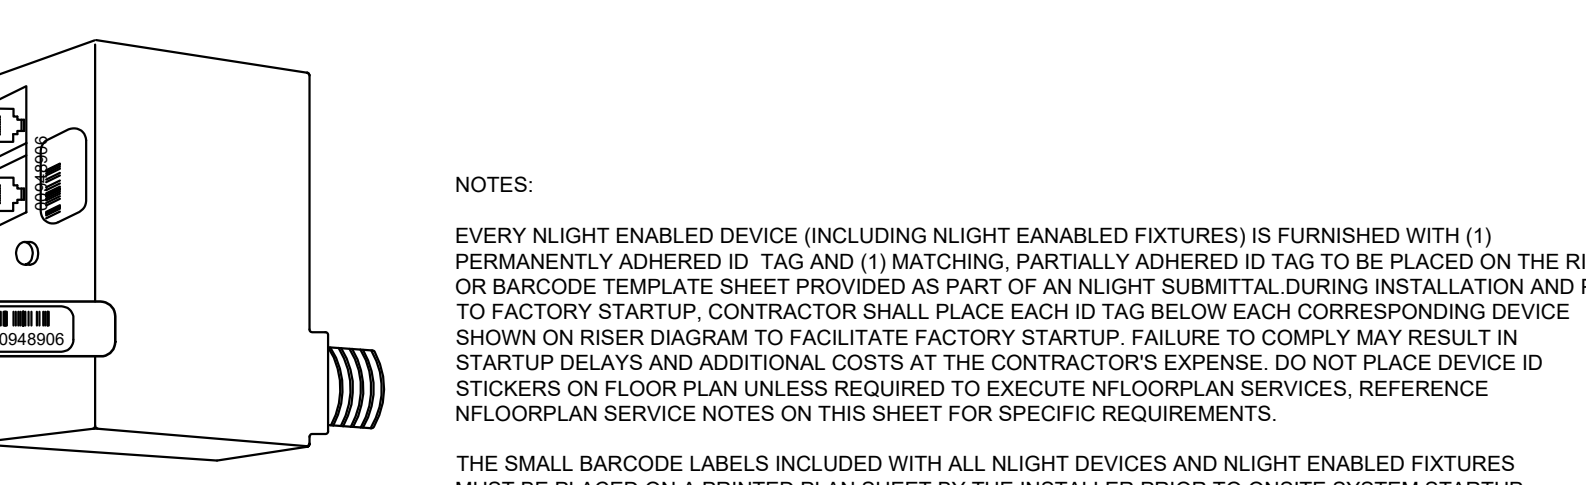



8 nLight - TYPE S20
Design 2

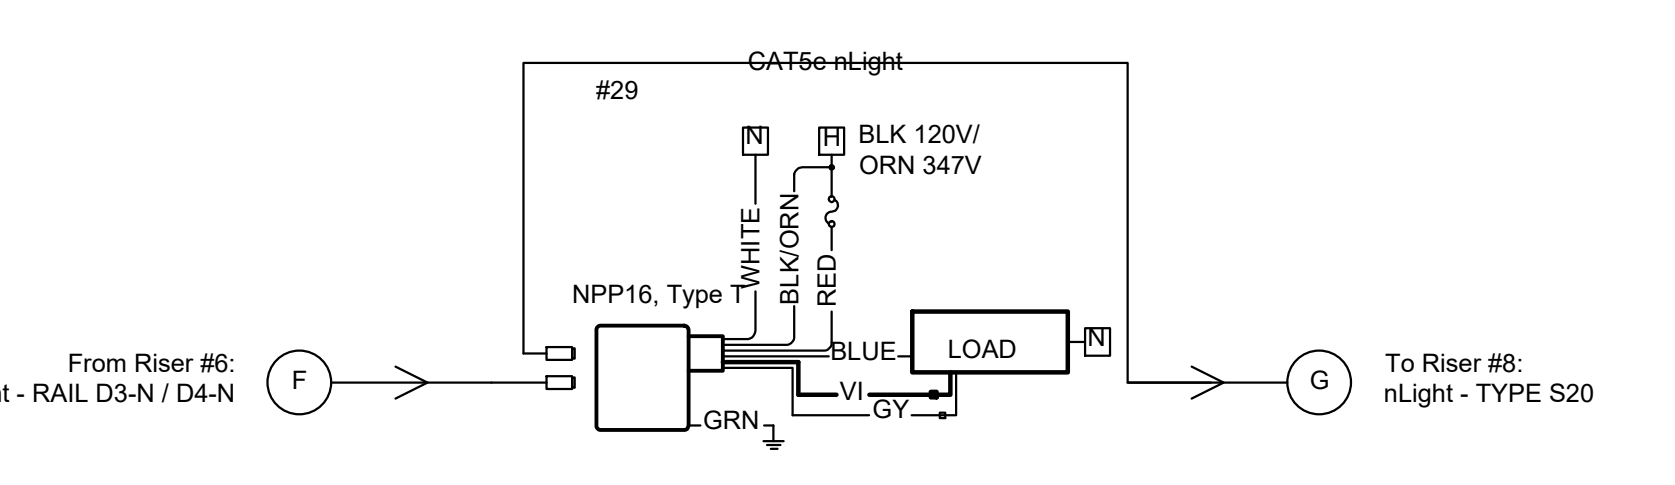


9 nLight - TYPE T
Design 2

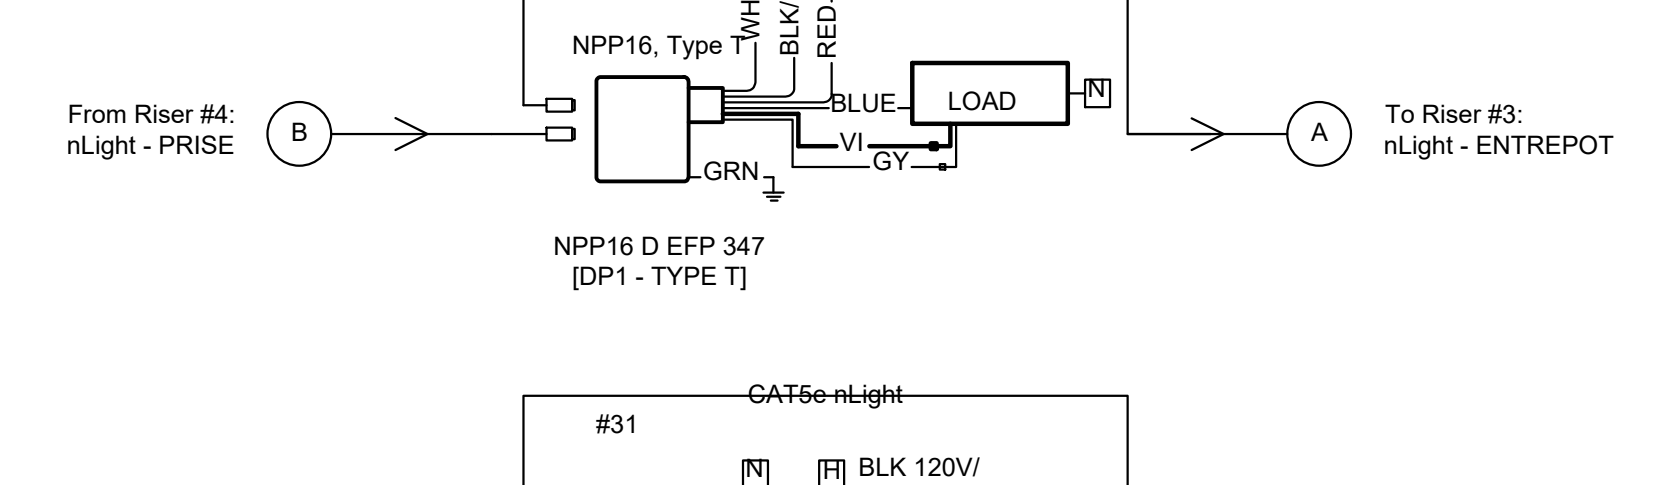

10 nLight - VESTIBULE
Design 2

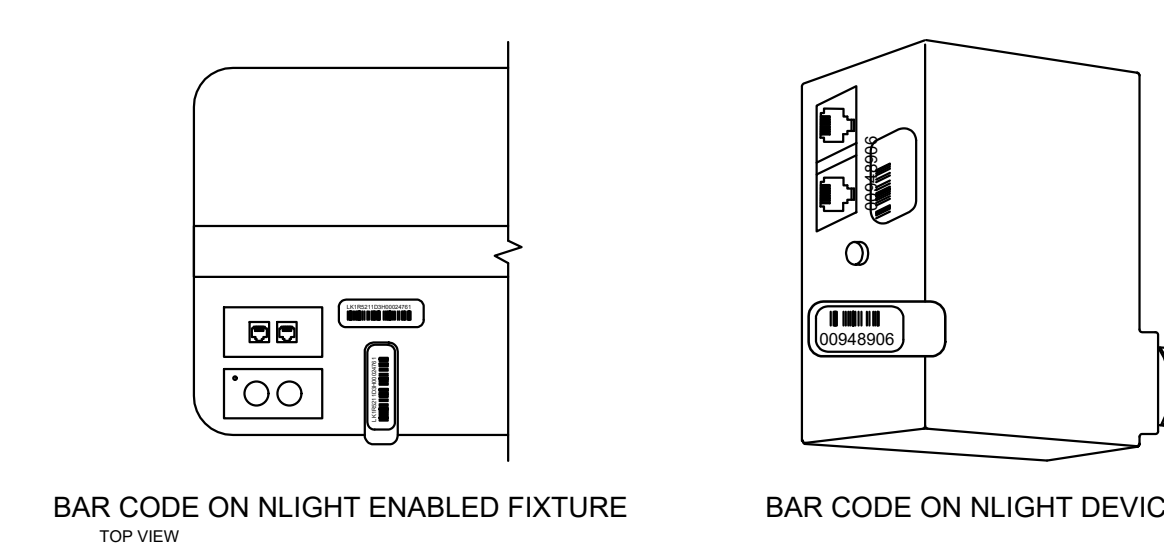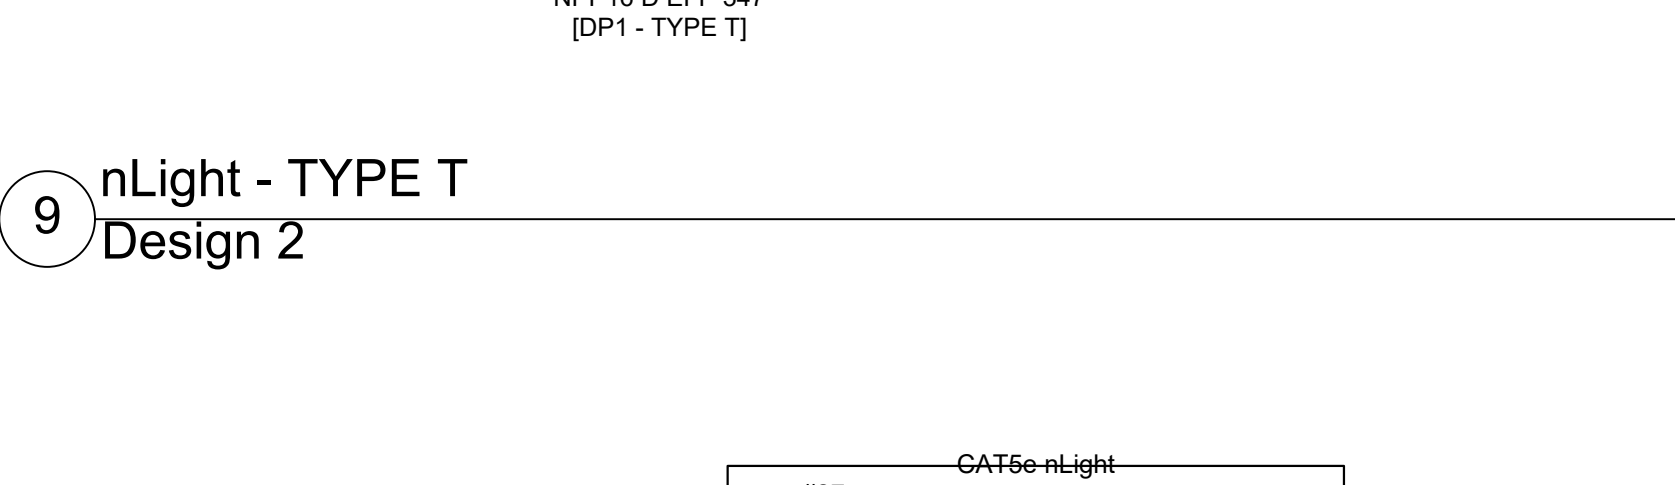

NOTES:
EVERY nLIGHT ENABLED DEVICE (INCLUDING nLIGHT ENABLED FIXTURES) IS FURNISHED WITH (1) PERMANENTLY ADHERED ID TAG AND (1) MATCHING, PARTIALLY ADHERED ID TAG TO BE PLACED ON THE RISER DIAGRAM OR BARCODE TEMPLATE SHEET PROVIDED AS PART OF AN nLIGHT SUBMITTAL DURING INSTALLATION AND PRIOR TO FACTORY STARTUP. CONTRACTOR SHALL PLACE EACH ID TAG BELOW EACH CORRESPONDING DEVICE SHOWN ON RISER DIAGRAM TO FACILITATE FACTORY STARTUP. FAILURE TO COMPLY MAY RESULT IN STARTUP DELAYS AND ADDITIONAL COSTS AT THE CONTRACTOR'S EXPENSE. DO NOT PLACE DEVICE ID STICKERS ON FLOOR PLAN UNLESS REQUIRED TO EXECUTE nLIGHT PLAN SERVICES. REFERENCE nLIGHT PLAN SERVICE NOTES ON THIS SHEET FOR SPECIFIC REQUIREMENTS.
THE SMALL BARCODE LABELS INCLUDED WITH ALL nLIGHT DEVICES AND nLIGHT ENABLED FIXTURES MUST BE PLACED ON A PRINTED PLAN SHEET BY THE INSTALLER PRIOR TO ONSITE SYSTEM STARTUP.
THE BARCODE INDICATES THE UNIQUE ID OF EACH nLIGHT DEVICE. THIS ID IS USED DURING SYSTEM STARTUP TO PROGRAM DEVICES WITH THE CORRECT GROUPINGS AND SETTINGS. WITHOUT THIS, SYSTEM STARTUP WILL REQUIRE ADDITIONAL DAYS ON THE JOB TO LOCATE DEVICE IDS.
BARCODE INSTRUCTIONS:
1. * PRINT A PLAN SHEET OF THE INSTALLATION AREA TO A MINIMUM D SIZE (24" X 36"). THE PLAN MAY BE A RISER SHEET OR BARCODE TEMPLATE (EITHER ARE PREFERRED). FLECTED CEILING PLAN, LIGHTING PLAN, AND ELECTRICAL PLAN, SO LONG AS ALL DEVICES CAN BE LOCATED BY THE FIELD SUPPORT ENGINEER.
2. PLACE THE SMALL BARCODE LABEL (0.875" LONG) FROM EACH LUMINAIRE AND DEVICE ON THE FLOORPLAN. THE LARGE BARCODE LABEL (1.25" LONG) CAN BE USED ON THE OUTSIDE OF ANY HOUSING OR JUNCTION BOX THAT OBSCURES THE ID NUMBER SHOWN ON THE DEVICE ITSELF.
3. SAVE THE PLAN AT THE JOB SITE, AND HAND OVER TO ACUTY FIELD SUPPORT ENGINEER OR OTHER PERSONNEL RESPONSIBLE FOR ONSITE SYSTEM STARTUP. IT IS ALSO ACCEPTABLE TO PROVIDE THE BARCODE PLAN AS SCANNED PDF FILES, EMAILED TO: CONTROLS.STARTUP@ACUTYBRANDS.COM, WITH PROJECT NAME AND PROJECT ADDRESS IN SUBJECT LINE AND A COPY OF THE ONSITE STARTUP REQUEST FORM.
4. DRAW ON PLAN ANY LOCATION CHANGES FOR A FIXTURE OR DEVICES, IF DIFFERENT THAN SHOWN ON PLAN.

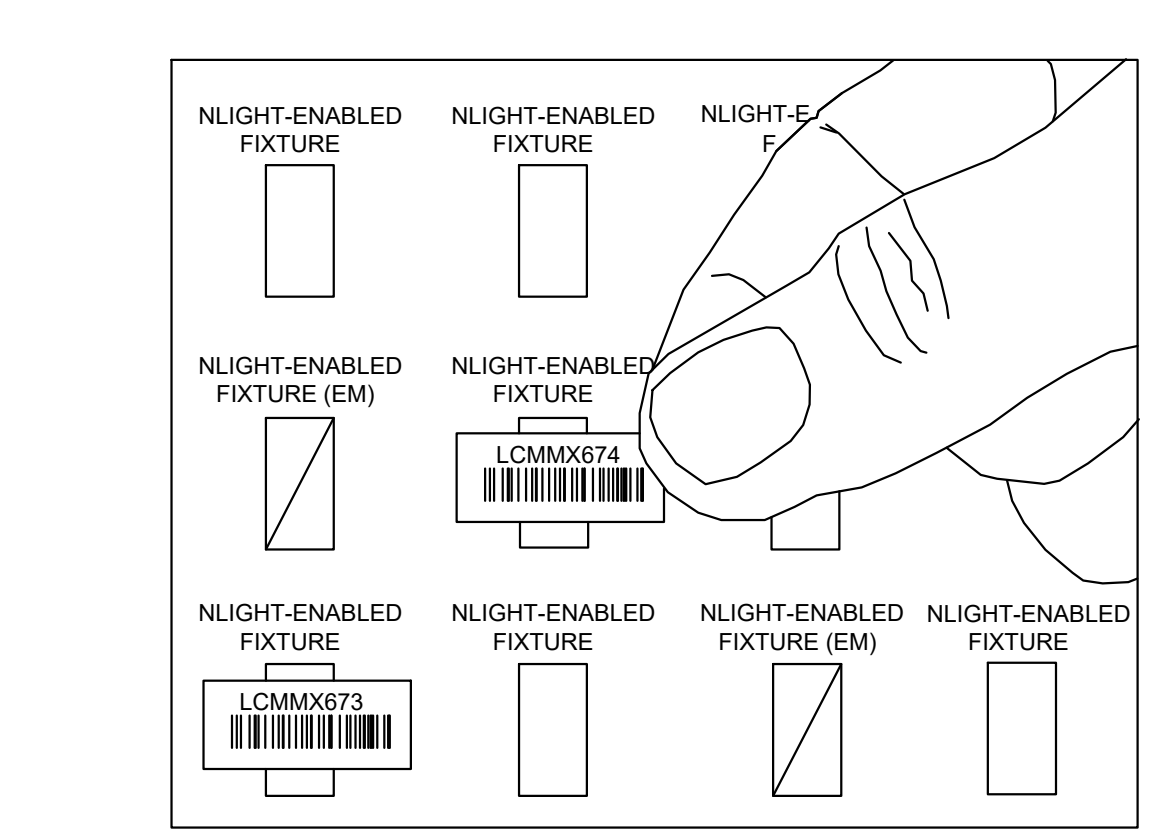

NLIGHT BARCODE INSTRUCTIONS




N.T.S.

Function	PAIR	PN OUT	Wire Color
(T1)	1	5	WHITE w BLUE
(R1)	4	4	BLUE
Tx + (T2)	2	1	WHITE w ORANGE
Rx - (R3)	3	3	WHITE w GREEN
(T4)	8	7	WHITE w BROWN
(R4)	8	8	BROWN

TERMINATION & TESTING OF CAT5 CABLES MUST BE DONE BY A QUALIFIED NETWORK INSTALLER

Cable termination requirements:
1. Strip off outer jacket - approximately 1-1/2" (37.6 mm)
2. Terminate approximately 1/2" (12.2 mm) from end of conductors on type 110 punch down block or connector per schedule (568B) - maximum untwist of conductors to terminations is 1/2" (12.2 mm) - trim excess leads.

SEE SYSTEM SPECIFIC NOTES ON SHEET LC0.1 FOR MAXIMUM CABLE LENGTHS.

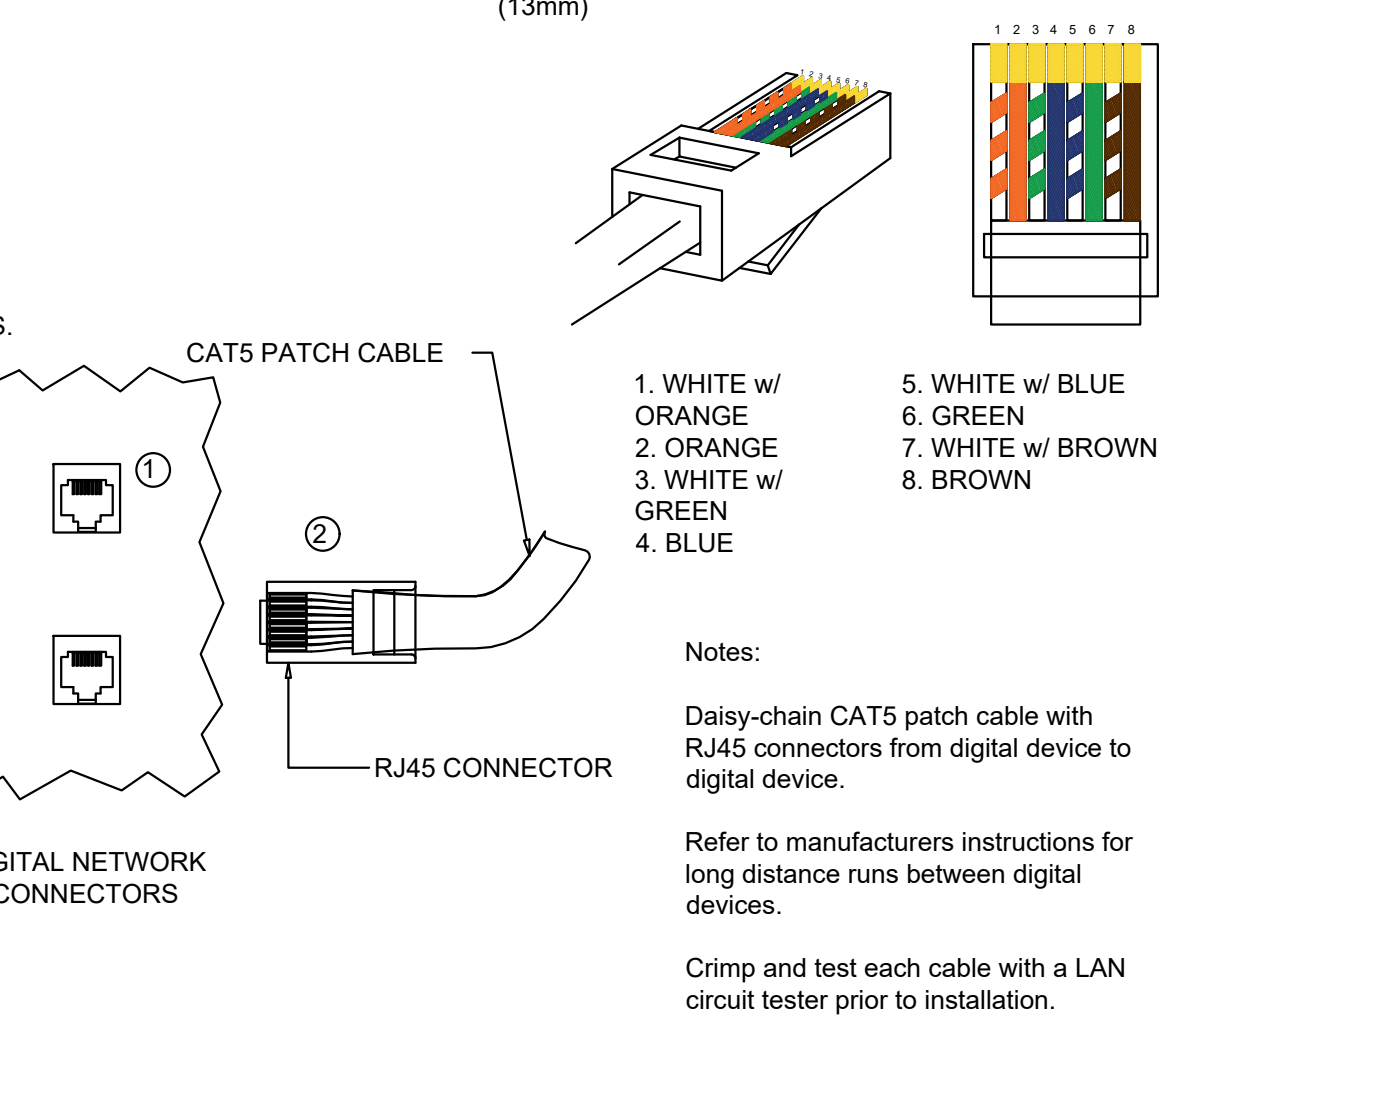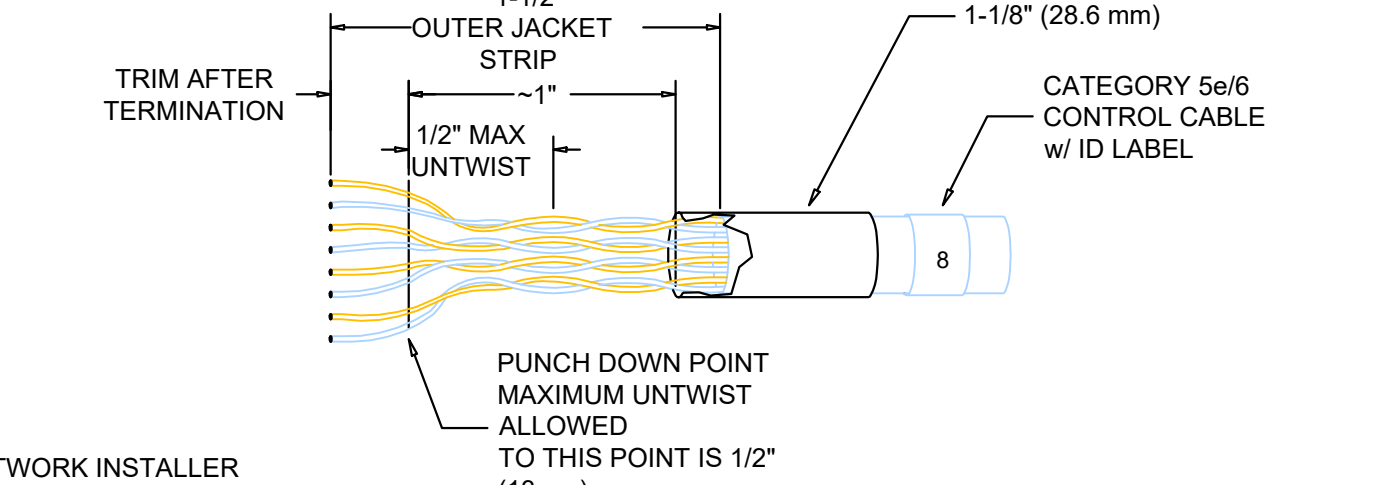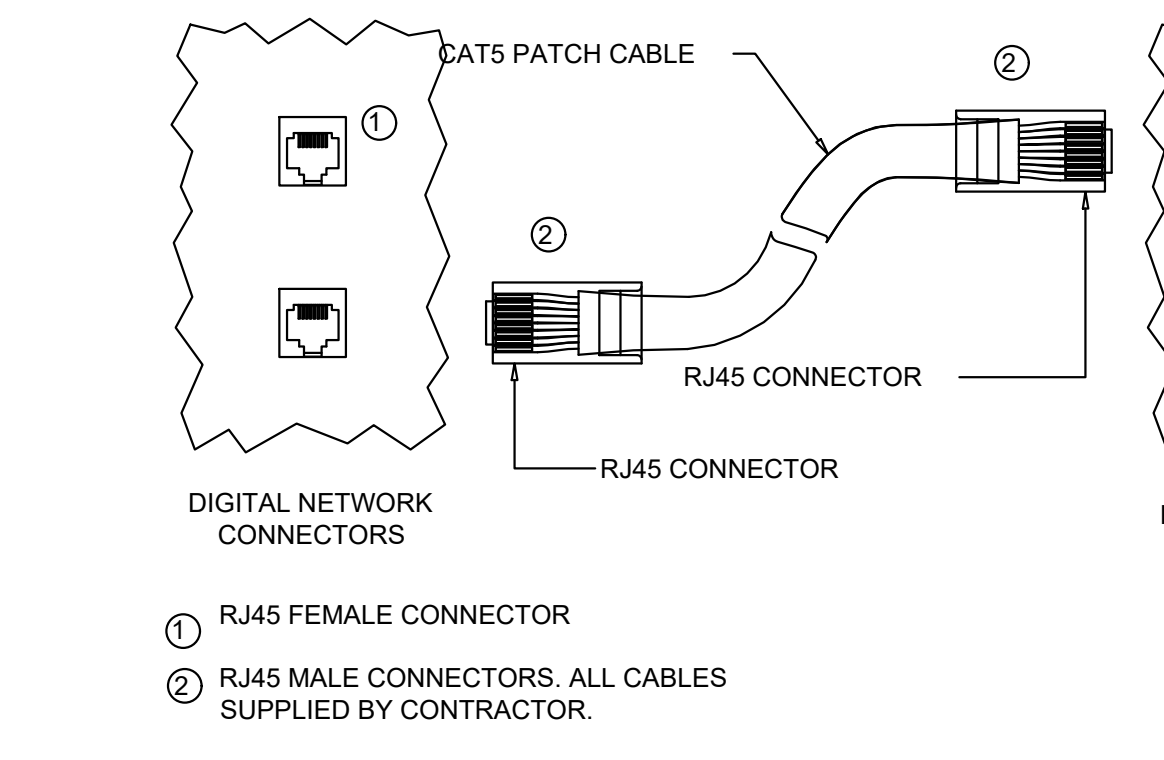


Notes:
Daisy-chain CAT5 patch cable with RJ45 connectors from digital device to digital device.
Refer to manufacturers instructions for long distance runs between digital devices.
Crimp and test each cable with a LAN circuit tester prior to installation.

CAT5E/6 CABLE TERMINATION

N.T.S.

NE PAS UTILISER POUR CONSTRUCTION


D	2026-08-26	POUR SOUMISSIONS	J.B.
NO	DATE	REVISION	PAR

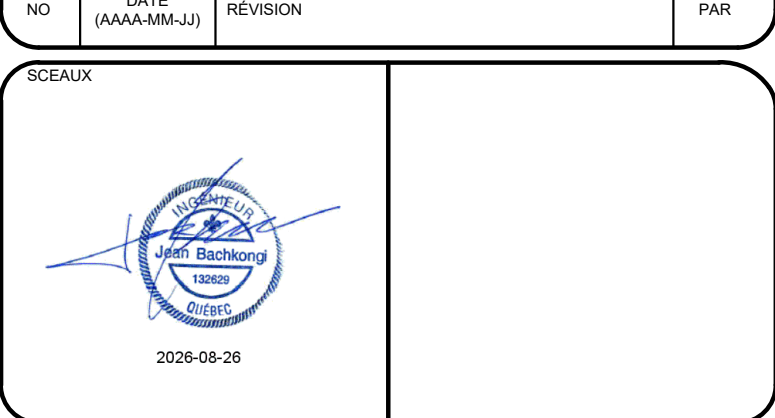

TITRE DU PROJET
SAQ
SAQ VARENNES
VARENNES, QC, J3X 1P7

TITRE DU DESIGN
DÉTAILS
CONTRÔLE D'ÉCLAIRAGE

CONCEPTEUR	ÉLECTRIQUE
CONÇU PAR H. HATTAB, CPI	DATE (AAAA-MM-JJ) 2026-07-13
ÉCRIT PAR F. BELAND, tech.	ÉCHÉLLE AUCUNE
VÉRIFIÉ PAR J. BACHKONGI, ING.	NO DE PROJET 26-0094-02
APPROUVÉ PAR J. BACHKONGI, Ing.	PLAN NO E103

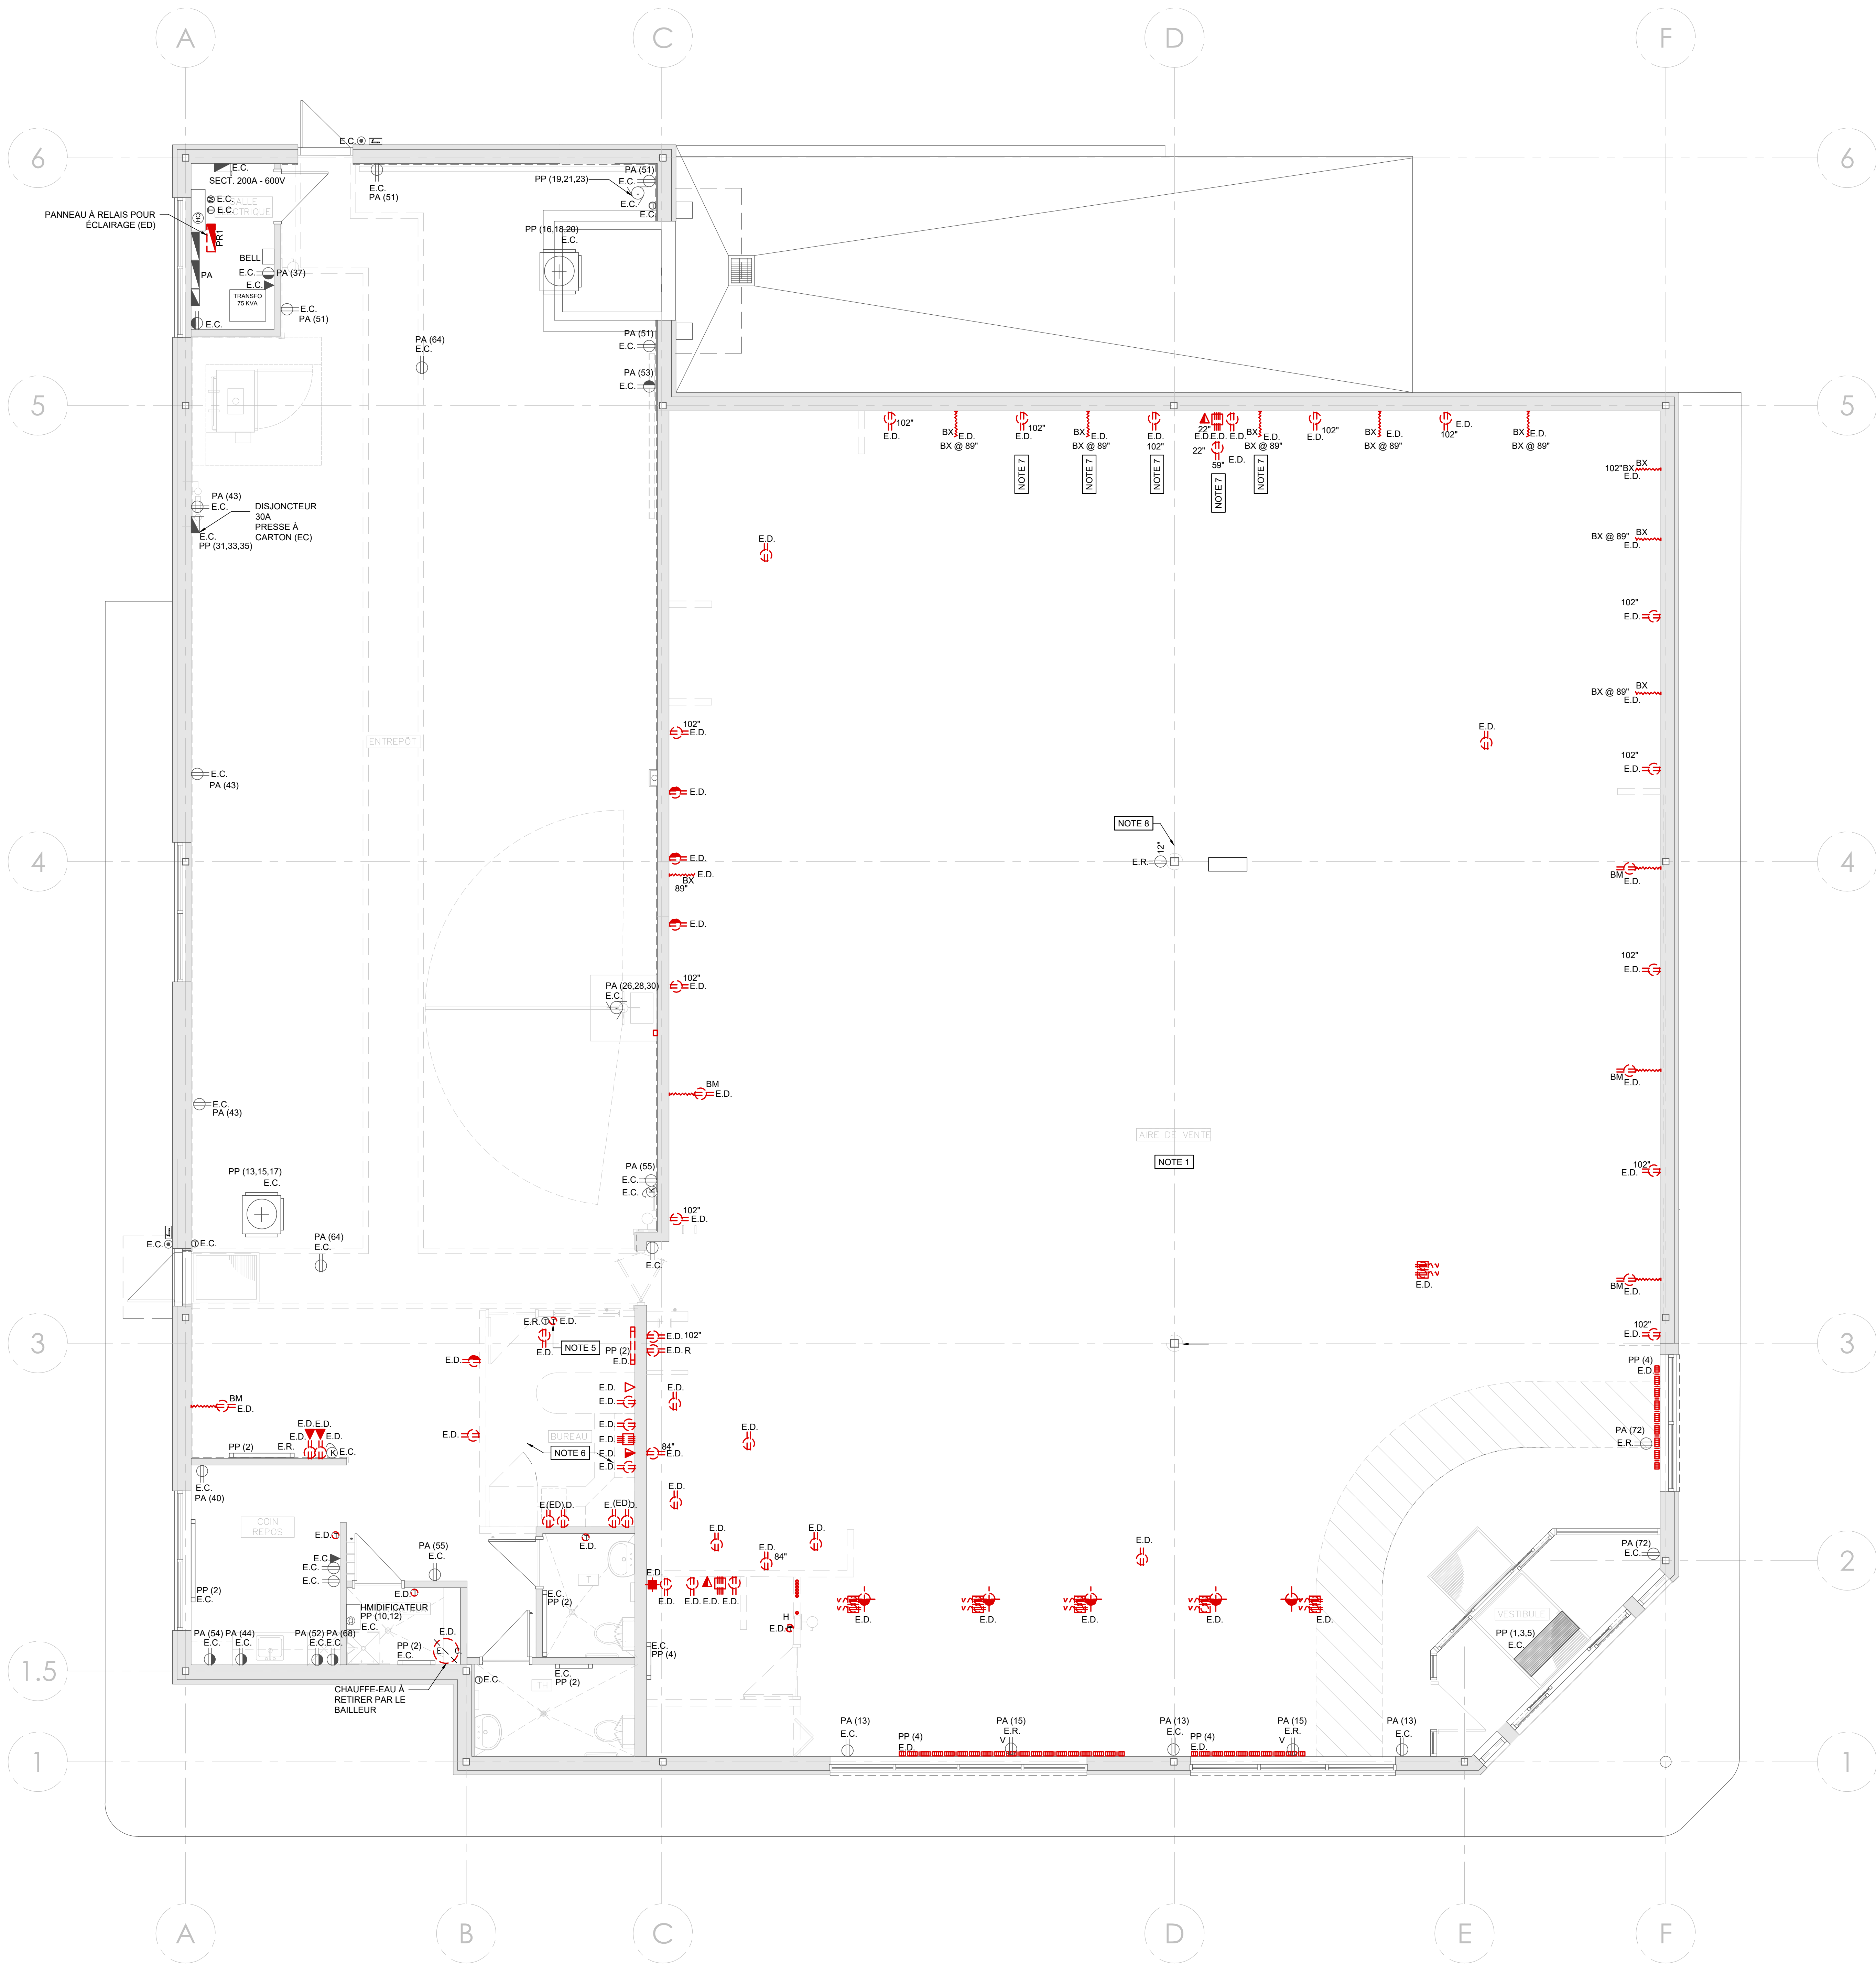

NOTES - DÉMOLITION

IL EST DE LA RESPONSABILITÉ DE L'ENTREPRENEUR D'ÉVALUER LES COÛTS DE DÉMOLITION DURANT LA VISITE DES LIEUX AVANT LA SOUMISSION.

SAUF INDICATION CONTRAIRE ET SI LE CLIENT NE DESIRE PAS LES CONSERVER, TOUS LES ÉQUIPEMENTS INDiquÉS SUR LES PLANS DE DÉMOLITION SONT EXISTANTS À ENLEVER ET À DISPOSER HORS DU SITE.

REMETTRE AU PROPRIÉTAIRE TOUS LES ÉQUIPEMENTS QU'IL DESIRE CONSERVER ET LES ENTREPOSER À UN ENDROIT DÉSIGNÉ PAR CELUI-CI. CE QUE LE PROPRIÉTAIRE NE DESIRE PAS CONSERVER, L'ENTREPRENEUR DEVRA EN DISPOSER À SES FRAIS HORS DU SITE. COORDONNER AU CHANTIER AVEC LE PROPRIÉTAIRE LE CHEMINEMENT DES MATÉRIAUX ENLEVÉS ET LES NOUVEAUX ÉQUIPEMENTS À INSTALLER.

L'ENTREPRENEUR ÉLECTRICIEN DOIT FAIRE UN TRAÇAGE DES CIRCUITS ET IDENTIFIER LES CIRCUITS DES APPAREILS TOUCHÉS DURANT LES TRAVAUX DANS TOUS LES PANNEAUX ET SOUS-PANNEAUX. TOUS LES CÂBLES ET FILAGE ÉLECTRIQUE ET TÉLÉCOM DÉSAFFECTÉS DOIVENT ÊTRE ENLEVÉS ET DISPOSÉS.

ENLEVER TOUS LES CONDUCTEURS, CONDUITS ET CÂBLES EXISTANTS JUSQU'À LA SOURCE OU JUSQU'À LA DERNIÈRE BOÎTE DE JONCTION TOUJOURS EN FONCTION. BOUCHER LES OUVERTURES FAITES DANS LES BOÎTES ET BOÎTIERS AVEC LES ACCESSOIRES REQUIS.

ALIMENTER ET RACCORDER TOUS LES APPAREILS D'ÉCLAIRAGE EXISTANTS, PRISES OU AUTRES ÉQUIPEMENTS TOUJOURS REQUIS (INCLUANT CEUX HORS DE LA ZONE DES TRAVAUX) ET DONT L'ALIMENTATION ÉLECTRIQUE A ÉTÉ DÉBRANCHÉE DURANT LES TRAVAUX DE DÉMOLITION.

DÉBRANCHER LES ÉQUIPEMENTS MÉCANIQUES POUR LEUR DÉMANTÈLEMENT PAR D'AUTRES (COORDONNER AVEC L'ENTREPRENEUR EN MÉCANIQUE).

LES ÉQUIPEMENTS EXISTANTS DANS LA ZONE DES TRAVAUX SONT INDiquÉS À TITRE INFORMATIF ET POUR DES FINS DE SOUMISSIONS. À MOINS INDICATION CONTRAIRE, TOUS LES ÉQUIPEMENTS RACCORDÉS ÉLECTRIQUEMENT SONT EXISTANTS À ENLEVER INCLUANT LES ÉQUIPEMENTS NON MONTRES AU PLANS.

TOUS LES CÂBLES DE TÉLÉCOMMUNICATION EXISTANTS DANS LA ZONE DES TRAVAUX (INCLUANT LES SYSTÈMES INTERCOMS, TÉLÉPHONIQUES, ETC.) SONT À ENLEVER JUSQU'À LA SOURCE.

FOURNIR, INSTALLER ET RACCORDER UN ÉCLAIRAGE TEMPORAIRE DANS LA ZONE DES TRAVAUX.

NOTES GÉNÉRALES - DÉMOLITION

1. PRÉPARER TOUTES LES SURFACES POUR RECEVOIR LES NOUVEAUX FINIS. ENLEVER VIS ET AUTRES DÉBRIS ET RAGRÉER LES SURFACES AU BESOIN.
2. LES TRAVAUX DE DÉMOLITION ET CONTRÔLE DES POUSSIÈRES DÉCRITS AUX PLANS D'ARCHITECTURE NE SONT PAS LIMITATIFS. VOIR LES DOCUMENTS DES AUTRES DISCIPLINES.
3. L'ENTREPRENEUR DOIT SUIVRE LES RECOMMANDATIONS D'UN INGÉNIEUR EN STRUCTURE POUR TOUS LES PERCEMENTS OU LE RAGRAGE DES OUVERTURES DANS LA DALLE DE BÉTON EXISTANTE. L'ENTREPRENEUR DOIT S'ASSURER DE NEFFECTUER AUCUN NOUVEAU PERCEMENT DANS UN ÉLÉMENT STRUCTURAL POUVANT COMPROMETTRE L'INTÉGRITÉ STRUCTURALE ET DE NE PAS PERCER AUCUN CONDUIT. INCLURE TOUS LES SCANS DE LA DALLE REQUIS PAR UN PROFESSIONNEL.
4. L'ENTREPRENEUR DEVRA VEILLER À NE PAS ENDOMMAGER LA STRUCTURE CONSERVÉE ET L'AMÉNAGEMENT EXTÉRIEUR CONSERVÉ AU PÉRIMÈTRE DU BÂTIMENT.
5. LES TRAVAUX DE DÉMOLITION DEVONT SE FAIRE EN CONFORMITÉ AUX CONDITIONS DES DOCUMENTS DU CONSULTANT EN HYGIÈNE.
6. LE TERME "DÉMOLIR" UTILISÉ DANS CES DOCUMENTS N'IMPLIQUE PAS NÉCESSAIREMENT UNE DESTRUCTION, MAIS IMPLIQUE PLUTÔT, SANS S'Y LIMITER, DÉMANTÉLER, DÉMONTÉ, DÉGARNIR, ENLEVER, DÉCONSTRUIRE OU RETIRER, ET REQUIÈRE POSSIBLEMENT DES PRÉCAUTIONS NÉCESSAIRES POUR ACCUEILLIR LES NOUVEAUX ÉLÉMENTS OU ASSEMBLAGES. PRENDRE NOTE QUE LES COMPOSANTES DÉMOLIES CONTIENNENT OU PEUVENT CONTENIR DE L'AMIANTE. POUR LA DISPOSITION DES MATÉRIAUX CONTAMINÉS, SE RÉFÉRER AUX DOCUMENTS D'HYGIÈNE DU MAÎTRE DE L'OUVRAGE POUR PRENDRE LES MESURES NÉCESSAIRES.
7. PRENDRE NOTE QUE LES COMPOSANTES DÉMOLIES CONTIENNENT OU PEUVENT CONTENIR DES MATÉRIAUX NOCIFS POUR LA SANTÉ ET L'ENVIRONNEMENT. SE RÉFÉRER AUX DOCUMENTS D'HYGIÈNE POUR PRENDRE LES MESURES NÉCESSAIRES.
8. LORSQUE REQUIS POUR LA NATURE DES TRAVAUX INDiquÉS AU PLAN, INCLURE LES ÉTAIMENTS TEMPORAIRES POUR SUPPORTER LES MATÉRIAUX EXISTANTS À CONSERVER EN PLACE.
9. TOUT ENTREPOSAGE ET PROTECTION DES ÉLÉMENTS RÉCUPÉRABLES LORS DE LA DÉMOLITION SONT À LA CHARGE DE L'ENTREPRENEUR.

NOTES SPÉCIFIQUES - DÉMOLITION

NOTE 1	SAUF INDICATIONS CONTRAIRES, TOUS LES SERVICES ÉLECTRIQUES ET INFORMATIQUES EXISTANTS DE L'AIRE DE VENTE SONT À RETIRER ET CONDAMNER.
NOTE 2	NA
NOTE 3	NA
NOTE 4	NA
NOTE 5	THERMOSTAT RELIÉ À LA SONDE DE TEMPÉRATURE DE L'AIRE DE VENTE À RETIRER ET EN FOURNIR UN NOUVEAU SITUÉ DANS LE BUREAU DE L'AIRE DE VENTE
NOTE 6	NA
NOTE 7	EMPLACEMENT EXISTANT À CONSERVER, ALIMENTATION ÉLECTRIQUE À MODIFIER
NOTE 8	SONDE EXISTANTE À RÉ-INSTALLER SUR LA COLONNE (VOIR PLAN MÉCANIQUE)
NOTE 9	NA
NOTE 10	NA
NOTE 11	NA



CLIENT


Aménagement et design
Réseau des succursales
780, RUE TELLIER, MONTRÉAL, QUÉBEC H3Y 1W6


ARCHITECTE

artesa
ARCHITECTURE

NOTES

NE PAS UTILISER
POUR CONSTRUCTION

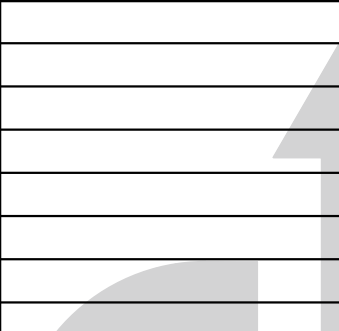					
D	2026-08-26	POUR SOUMISSIONS			J.B.
NO	DATE (AAAA-MM-JJ)	REVISION	PAGE		

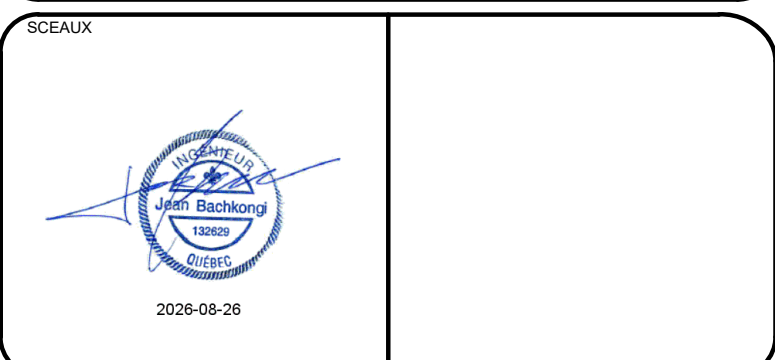

SAQ
SAQ VARENNES
VARENNES, QC, J3X 1P7

ÉLECTRICITÉ
PRISES & SERVICES
REZ-DE-CHAUSSÉE
DÉMOLITION

ÉLECTRIQUE	
CONQUÉ H. HATTAB, CPI	DATE: 2026-07-13
ÉCRITURE: F. BÉLAND, tech.	ÉCHELLE: INDiquÉE
VERIFIÉ: J. BACHKONGI, ING.	NO DE PROJET: 26-0094-02
APPROUVÉ: J. BACHKONGI, Ing.	PLAN NO: E200D



NOTES SPÉCIFIQUES

GÉNÉRALITÉS :

LES NOTES GÉNÉRALES SONT COMPLÉMENTAIRES À CE PLAN.

TOUS LES CONDUITS RIGIDES "EMT" OU PVC DESTINÉS À L'ALIMENTATION DE SERVICES INFORMATIQUES DONT IL EST QUESTION DANS LES NOTES CI-BASSES DOIVENT :

- ÊTRE MUNIS DE FICELLE DE TIRAGE BIEN IDENTIFIÉES AUX DEUX EXTRÉMITÉS.
- ÊTRE MUNIS DE BAGUES DE TERMINAISON AUX DEUX EXTRÉMITÉS.
- SE PROLONGER DANS L'ENTRE-PLAFOND JUSQU'À UN ENDOIT FACILEMENT ACCESSIBLE (IE : AU-DESSUS D'UNE TUILE ACOUSTIQUE).

LE RÉSEAU DE CONDUITS CI-HAUT DÉCRIT EST RÉALISÉ PAR L'ENTREPRENEUR ÉLECTRICIEN MAIS LE CÂBLAGE INFORMATIQUE ET SÉCURITÉ EST RÉALISÉ PAR UN SOUS-TRAITANT MANDATÉ PAR LA SAQ.

TOUS LES CONDUITS RIGIDES "EMT" OU PVC DESTINÉS À ALIMENTATION DES SERVICES ÉLECTRIQUES DONT IL EST QUESTION DANS LES NOTES CI-BASSES DOIVENT :

- SE TERMINER, DANS L'ENTRE-PLAFOND, PAR UNE BOÎTE DE JONCTION SITUÉE À UN ENDOIT FACILEMENT ACCESSIBLE (IE : AU-DESSUS D'UNE TUILE ACOUSTIQUE).

SEULEMENT SI LA STRUCTURE DU PLAFOND RESTE APPARENTE, L'ENTREPRENEUR ÉLECTRICIEN DOIT INSTALLER UN RÉSEAU COMPLET DE CONDUITS RIGIDES "EMT" POUR LE CÂBLAGE ÉLECTRIQUE, INFORMATIQUE, TÉLÉPHONIQUE ET SÉCURITÉ, À PARTIR DES SOURCES D'ALIMENTATION JUSQU'ÀUX ENDOITS INDQUÉS AU PLAN OU DE TELS SERVICES SONT REQUIS (BUREAUX, COMPTOIR-CAISSES, ETC); MUNIS LES CONDUITS DE BOÎTES ET DE FICELLES DE TIRAGE.

SI UN RÉSEAU COMPLET DE CONDUITS RIGIDES N'EST PAS PRÉVU POUR LA DISTRIBUTION ÉLECTRIQUE, AU MINIMUM, L'ÉLECTRICIEN INSTALLERA DES BOÎTES DE JONCTION DANS L'ENTRE-PLAFOND AU DESSUS DES PANNEAUX DE DISTRIBUTION AVEC UN RÉSEAU DE CONDUITS RIGIDES ENTRE LES DEUX. LES RACCORDS DU CÂBLAGE "BX" DE TOUS LES CIRCUITS S'EFFECTUERONT DANS CES BOÎTES DE JONCTION.

NOTES SPÉCIFIQUES :

[NOTE 1] : CONDUIT RIGIDE EN PVC 1 1/2" Ø (SAUF INDICATION CONTRAIRE AU PLAN). SOUS LA DALLE, CE CONDUIT MONTE DANS UN MUR À PROXIMITÉ JUSQU'À UNE BOÎTE DE JONCTION DANS L'ENTRE-PLAFOND. LORSQUE LE PLAFOND EST OUVERT, PROLONGER LE CONDUIT JUSQUE DANS L'ENTREPÔT. À L'AUTRE EXTRÉMITÉ, IL EST RELIÉ À UNE BOÎTE DE JONCTION FIXÉE À PLAT SUR LA DALLE POUR LE RACCORDEMENT DES SERVICES ÉLECTRIQUES REQUIS AUX COMPTOIRS CAISSES, OU ENCORE, IL SE DIRIGE VERS DES PRISES ÉLECTRIQUES AU SOL.


[NOTE 2] : CONDUIT RIGIDE EN PVC 1" Ø, SOUS LA DALLE, CE CONDUIT MONTE DANS UN MUR À PROXIMITÉ JUSQUE DANS L'ENTRE-PLAFOND. LORSQUE LE PLAFOND EST OUVERT, PROLONGER LE CONDUIT JUSQUE DANS L'ENTREPÔT. À L'AUTRE EXTRÉMITÉ, LE CONDUIT SORTIRA DE 1" AU-DESSUS DE LA DALLE, (POUR CÂBLAGE INFORMATIQUE, TÉLÉPHONE ET DATA PAR AUTRES).

[NOTE 3] : CONDUIT RIGIDE DE 3/4" Ø RACCORDÉ À UNE BOÎTE DE SORTIE MURALE 2 X 3 ET MONTANT DANS L'ENTRE-PLAFOND. LORSQUE PLAFOND OUVERT, PROLONGE LE CONDUIT DU BUREAU JUSQUE DANS L'ENTREPÔT.

[NOTE 4] : 2 CONDUITS RIGIDES DE 2" AVEC BAGUES DE FINITION, DÉBUTANT À 115" DU PLANCHER ET SE TERMINANT DANS L'ENTRE-PLAFOND.

NOTES - PROTECTION IGNIFUGE

FOURNIR ET INSTALLER UNE PROTECTION IGNIFUGE AUTOUR DES BOÎTES DE JONCTION ENCASTRÉES T/O CP 617 DE HILTI OU AUTRE PRODUIT ÉQUIVALENT DANS LES DIVISIONS (MURS, PLANCHERS, PLAFONDS) ISOLÉS ET PROTÉGÉS CONTRE LE FEU (LUMINAIRES, INTERRUPTEURS, PRISES ÉLECTRIQUES, ÉCLAIRAGE D'URGENCE, APPARELS DE CHAUFFAGE, ETC.), VEUILLEZ-VOUS RÉFÉRER AUX PLANS D'ARCHITECTURES.

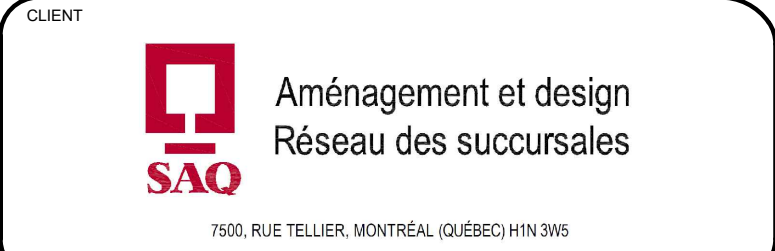

NOTES

NE PAS UTILISER POUR CONSTRUCTION


NO	DATE	REVISION	PAR
0	2026-08-26	POUR SOUMISSIONS	J.B.

TITRE DU PROJET
SAQ
SAQ VARENNES
VARENNES, QC, J3X 1P7



TITRE DU DESSIN
ÉLECTRICITÉ
PRISES & SERVICES
REZ-DE-CHAUSSÉE
CONSTRUCTION


DISCIPLINE
ÉLECTRIQUE


CONQUÉ PAR H. HATTAB, CPI	DATE (AAAA-MM-JJ) 2026-07-13
ÉVALUÉ PAR F. BELAND, tech.	ÉCHELLE INDIQUÉE
VERIFIÉ PAR J. BACHKONGI, ING.	NO DE PROJET 26-0094-02
APProuvé PAR J. BACHKONGI, Ing.	PLAN NO E200

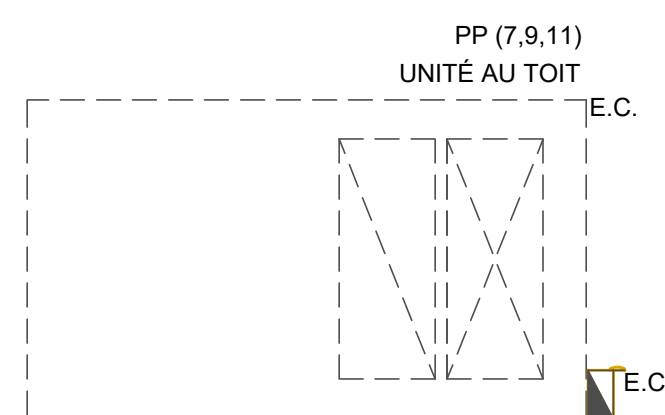

VENTILATEUR VE-02 CONTRÔLÉ
PAR MINUTERIE PROGRAMMABLE
INSTALLÉE DANS LA SALLE
ÉLECTRIQUE (PAR DIVISION 25)
À RACCORDER

 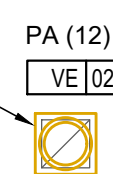

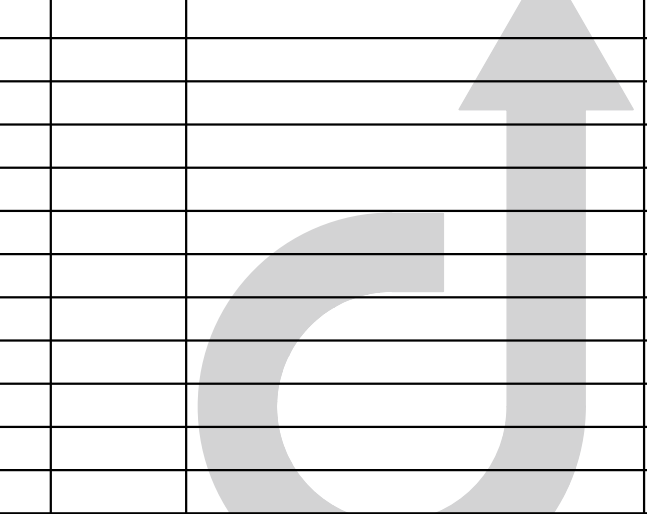			
0	2026-08-26	POUR SOUMISSIONS	J.B.
NO	DATE (AAAA-MM-JJ)	REVISION	PAR

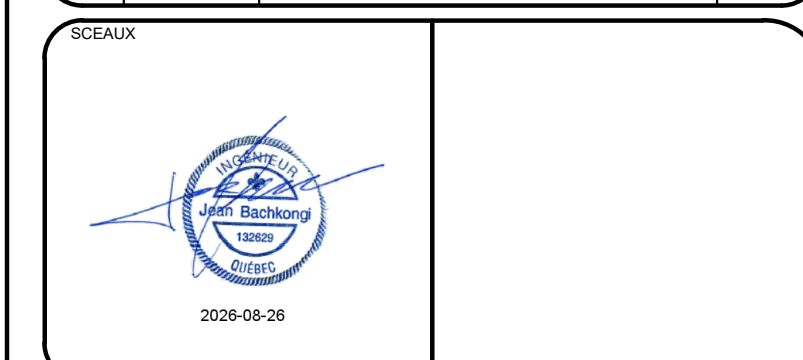

TITRE DU PROJET

SAQ


SAQ VARENNES
VARENNES, QC, J3X 1P7

TITRE DU DESSIN

ÉLECTRICITÉ
PLAN DE TOITURE
EXISTANT /
CONSTRUCTION

1141-508-6325

CSC/CP/PL/NE	
ÉLECTRIQUE	
CONQU PAR H. HATTAB, CPI	DATE (AAAA-MM-JJ) 2026-07-13
DESSIN PAR F. BÉLAND, tech.	ÉCHELLE INDIQUÉE
VERIFIE PAR J. BACHKONGI, ING.	NO DE PROJET 26-0094-02
APPROUVE PAR J. BACHKONGI, ing.	PLAN NO E201

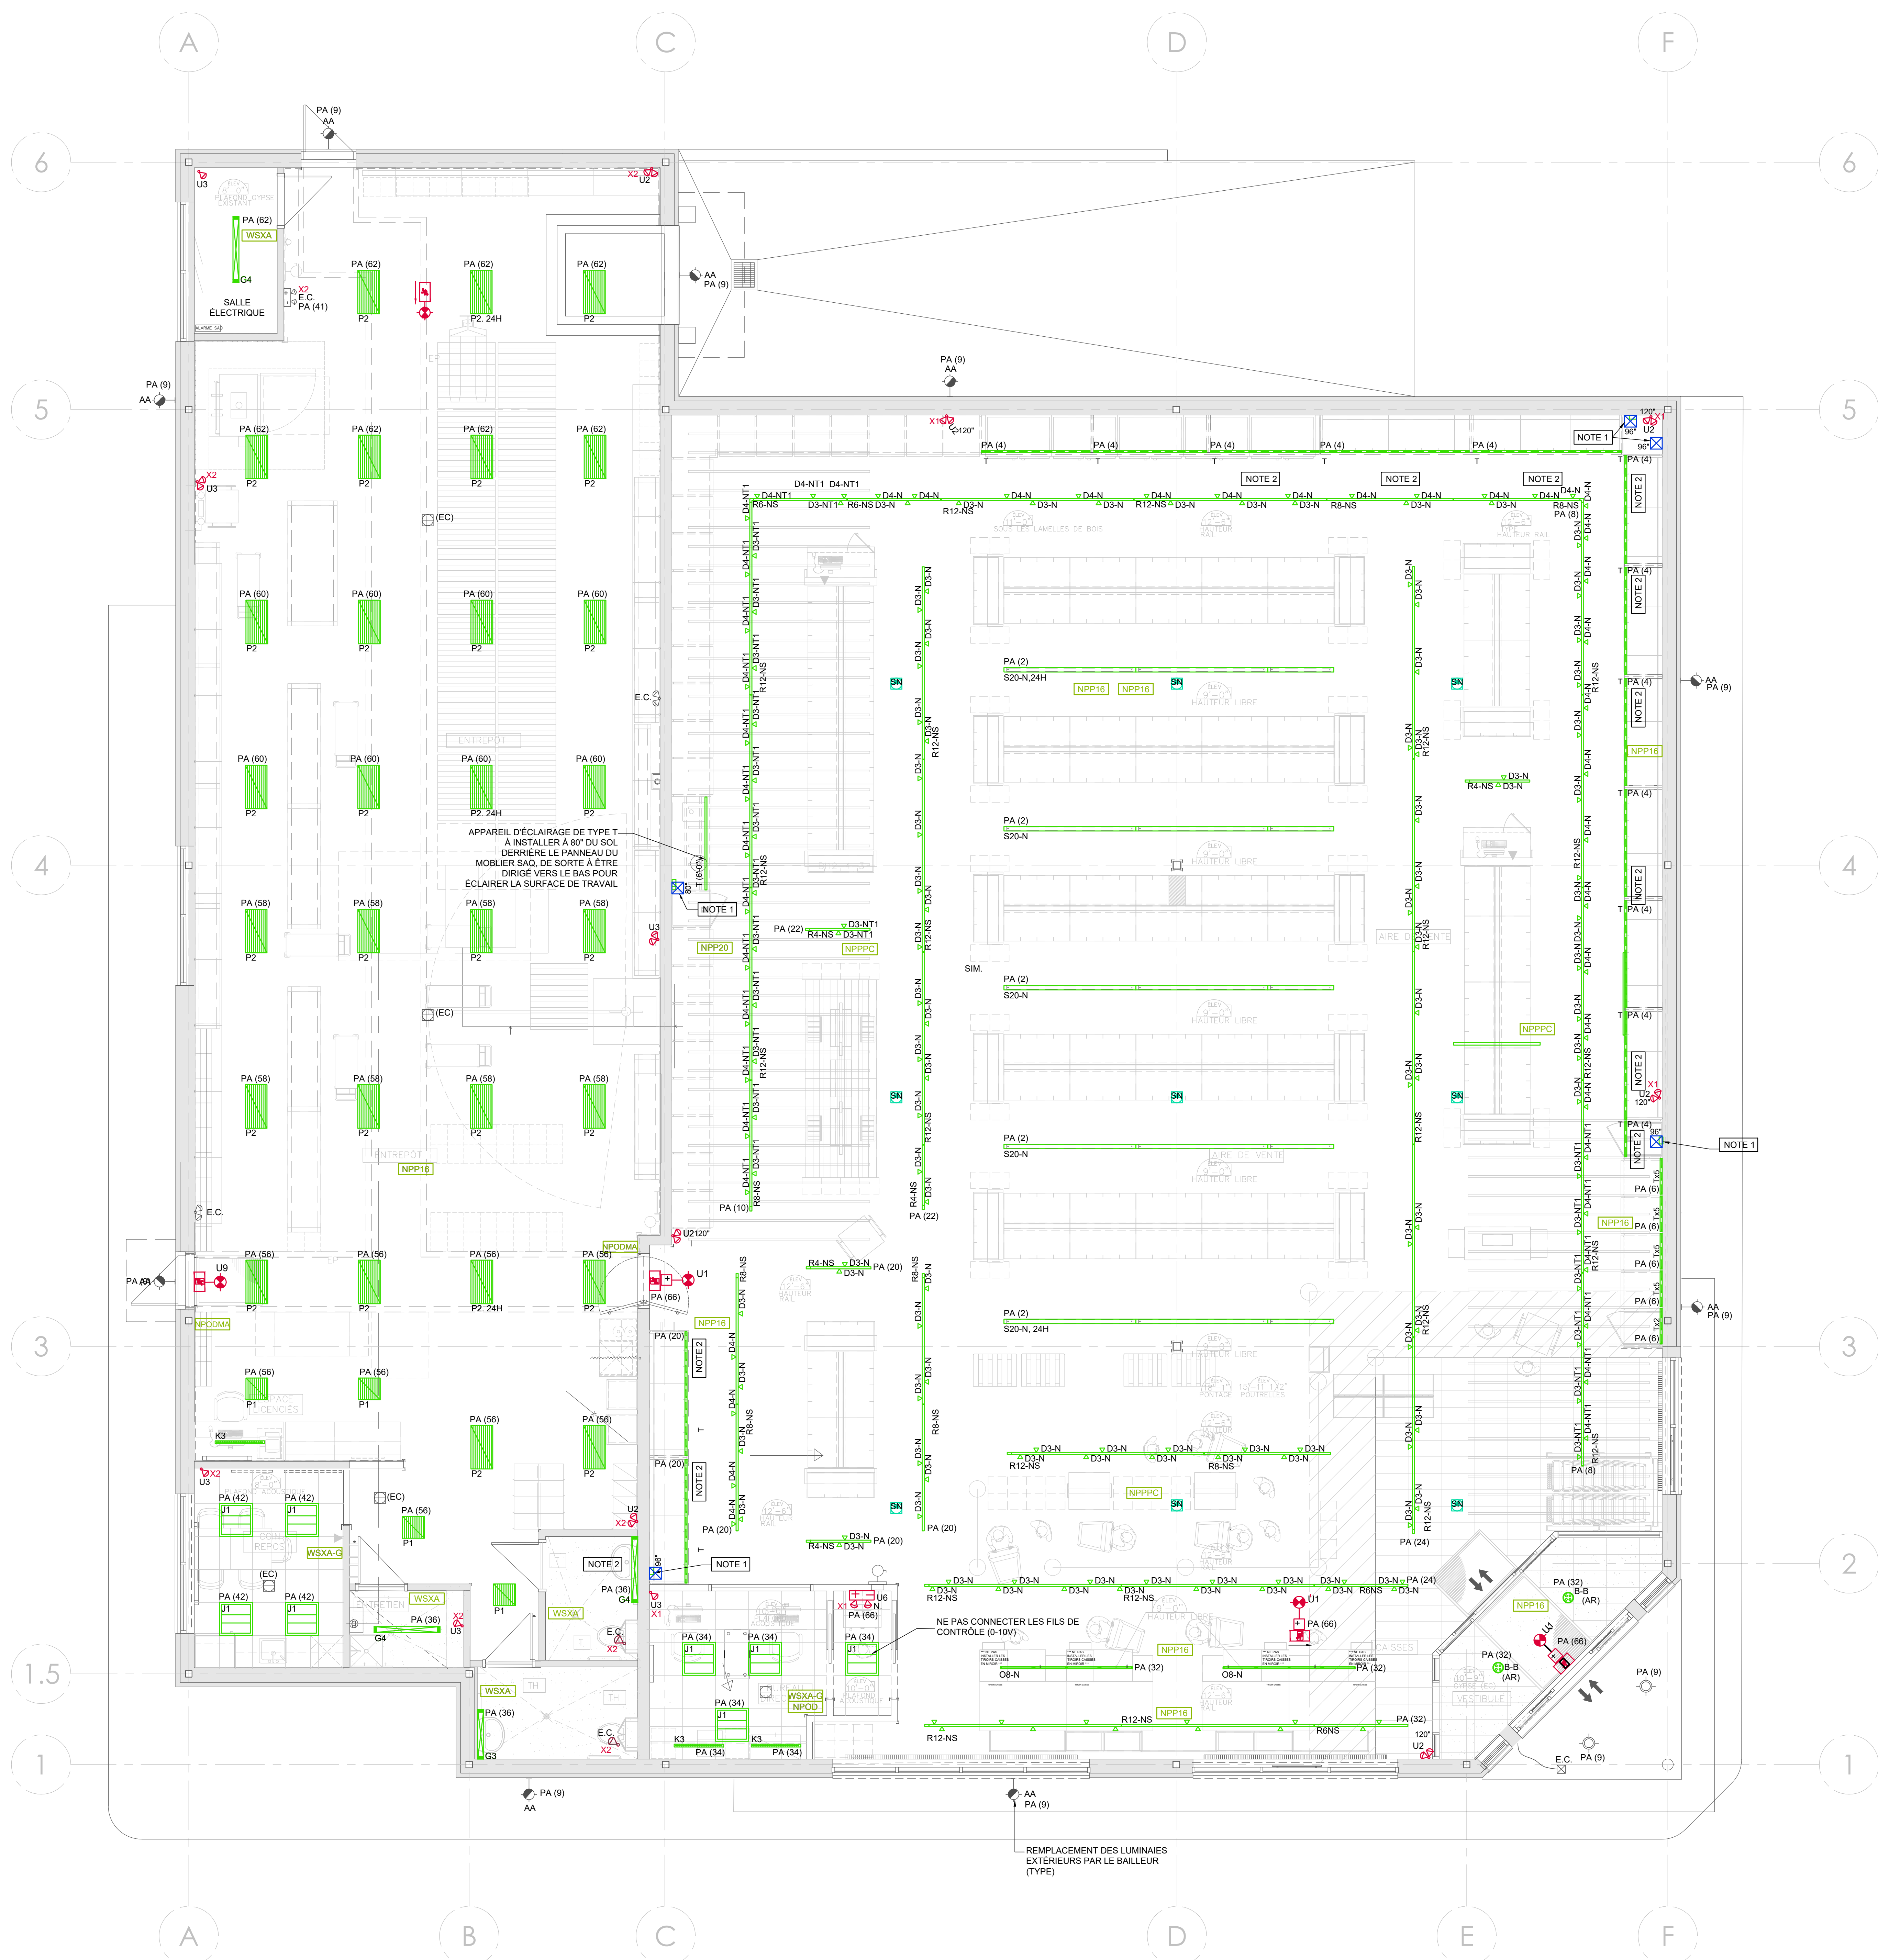

NOTES PLAFOND RÉFLÉCHI

- TOUS LES LUMINAIRES DEVONT ÊTRE APPROUVÉS CSA ET/OU UL ET PARTOUT OÙ C'EST POSSIBLE, ILS AURONT DES BALLASTS ÉLECTRONIQUES.
- REMETTRE AU RESPONSABLE DE PROJET DE LA SAQ UNE DEMONSTRATION PROPOSÉE DES APPAREILS PERMETTANT D'OBTENIR 50 PIEDS-BOUGES À 3 X 3' OU 5 X 3'.
- L'APPELATION "24H" SIGNIFIE QUE L'APPAREIL DEPUIS DISPOSEUR ALLUMÉ 24 HEURES (ÉCLAIRAGE DE SÉCURITÉ).
- VALIDER LES AUTEURS D'INSTALLATION AVEC LE RESPONSABLE DE PROJET.
- L'ENTREPRENEUR QU'IL SOIT TRAITANT DOIT TRANSMETTRE UNE COPIE DU PLAN DE PLAFOND AU FOURNISSEUR CHOISI.
- L'ÉLECTRICIEN DEVAIT AJUSTER LES FAISCEAUX LUMINEUX DES APPAREILS D'ÉCLAIRAGE DIRIGEABLES AVEC LE MOBILIER SAQ SUITE À SON INSTALLATION.
- DANS LE CAS DUN PLAFOND À STRUCTURE APPARENTE, L'ÉLECTRICIEN ET L'ÉBÉNISTE DE L'ENTREPRENEUR DEVONT PRÉVOIR LES CADRONS NÉCESSAIRES POUR LEURS INSTALLATIONS. LES CADRANTS ET TIGES DE FIXATION DEVONT ÊTRE PEINTS TEL QUE LE PLAFOND.

NOTES SPÉCIFIQUES - DÉMOLITION

- | | |
|--------|---|
| NOTE 1 | BOÎTE DE JONCTION ENCASTRÉE DANS LE MUR POUR RACCORDEMENT DES APPAREILS D'ÉCLAIRAGE DE TYPE T. QUANTITÉ À VALIDER AU CHANTIER, ET LOCALISATION À COORDONNER AVEC LA SAQ. PRÉVOIR UNE PLAQUE DE FINITION À PENDRE TOUTE LE MUR. |
| NOTE 2 | L'ÉLECTRICIEN DEVRA INSTALLER LES APPAREILS D'ÉCLAIRAGE DE TYPE "T" AU DOS DE LA STRUCTURE INFÉRIEURE DU SYSTÈME DE SIGNALISATION MALLÉABLE (L'AMÉNAGEMENT DE LA LIGNE À FAISCEAU AU LAUGUE DOIT ÊTRE DÉFINI EN VUE DE LA HAUT. CES DERNIERS DEVONT ÊTRE VISSÉS DANS LA STRUCTURE D'ACIER PAR DERRIÈRE, LES VUS COUPÉS AU RAS DE LA STRUCTURE ET UNE RETOUQUE NOIRE DEVRA ÊTRE FAIT SUR LA VIS. LA DATE EXACTE D'INSTALLATION DEVRA ÊTRE COORDONNÉE AVEC LE RESPONSABLE DE PROJETS DE LA SAQ. |

NOTE GÉNÉRALE

EN PLUS DU FILAGE DE PUISSANCE, FOURNIR, INSTALLER ET RACCORDER LES CÂBLES DE CONTRÔLE D'ÉCLAIRAGE BAS VOLTAGE 0-10V. SE RÉFÉRER AUX INSTRUCTIONS DU FABRICANT POUR UNE INSTALLATION COMPLÈTE ET FONCTIONNELLE. INSTALLER LES CÂBLES SOUS CONDUIT EMT ET CÂBLE AC90 C/A CONDUCTEURS BAS VOLTAGE POUR LE RACCORDEMENT FINAL AUX LUMINAIRES.

FURNIR ET INSTALLER LES CONDUITS EMT REQUIS POUR LE RACCORDEMENT DES CIRCUITS DE CONTRÔLE D'ÉCLAIRAGE.

NOTES - PROTECTION IGNIFUGE

FOURNIR ET INSTALLER UNE PROTECTION IGNIFUGE AUTOUR DES BOÎTES DE JONCTION ENCASTRÉES T/Q CP 617 DE HILTI OU AUTRE PRODUIT ÉQUIVALENT DANS LES DIVISIONS (MURS, PLANCHERS, PLAFONDS) ISOLÉS ET PROTÉGÉS CONTRE LE FEU (LUMINAIRES, INTERRUPTEURS, PRISES ÉLECTRIQUES, ÉCLAIRAGE D'URGENCE, APPAREILS DE CHAUFFAGE, ETC.). VEUILLEZ-VOUS RÉFÉRER AUX PLANS D'ARCHITECTURES.

NOTE GÉNÉRALE

IL A ÉTÉ CONVENU AVEC LE CLIENT QUE LES NIVEAUX D'ÉCLAIRAGE SERONT VALIDÉS ENTRE CE DERNIER ET LE FABRICANT. PAR CONSÉQUENT, DIRECTION 360 NE PEUT ÊTRE TENUE RESPONSABLE DES NIVEAUX D'ÉCLAIREMENT OBTENUS À LA FIN DES TRAVAUX.

