

Les architectes Clermont St-Germain associés
1845 Rue de l'Église
Sainte-Julie, Qc, J3E1E9
t. 450.461.0835
pstgermain@architectescs.com
www.architectescs.com

RELEVÉ A801 - MATERIEL

66 repères / 14 familles / RES 66

RES = réserve source, modèle, position, portée ou réconciliation; * = identification à révalider

- M01 APPLIQUE MURALE - SALLE D'ATTENTE
- M02 DETECTEUR DE FUMÉE D.F.E. (HORS LÉGENDE - R-001)
- M03 ENCASTRE SLIM
- M04 INTERRUPTEUR 3 VOIES HAUTEUR STANDARD


- M05 INTERRUPTEUR HAUTEUR STANDARD
- M06 LUMINAIRE SUSPENDU
- M07 PLAFONNIER DETECTEUR DE MOUVEMENT
- M08 PLINTE ÉLECTRIQUE

Calques activables; modèles, prescriptions et réserves complètes page 2


- M09 PRISE ÉLECTRIQUE CONTRÔLÉ PAR INTERRUPTEUR
- M10 PRISE ÉLECTRIQUE HAUTEUR COMPTOIR
- M11 PRISE ÉLECTRIQUE HAUTEUR STANDARD
- M12 RACCORD DIRECT VRC (HORS LÉGENDE - R-001)

- M13 THERMOSTAT
- M14 VENTILATEUR

Quantités source et renvois; voir bordereau détail.

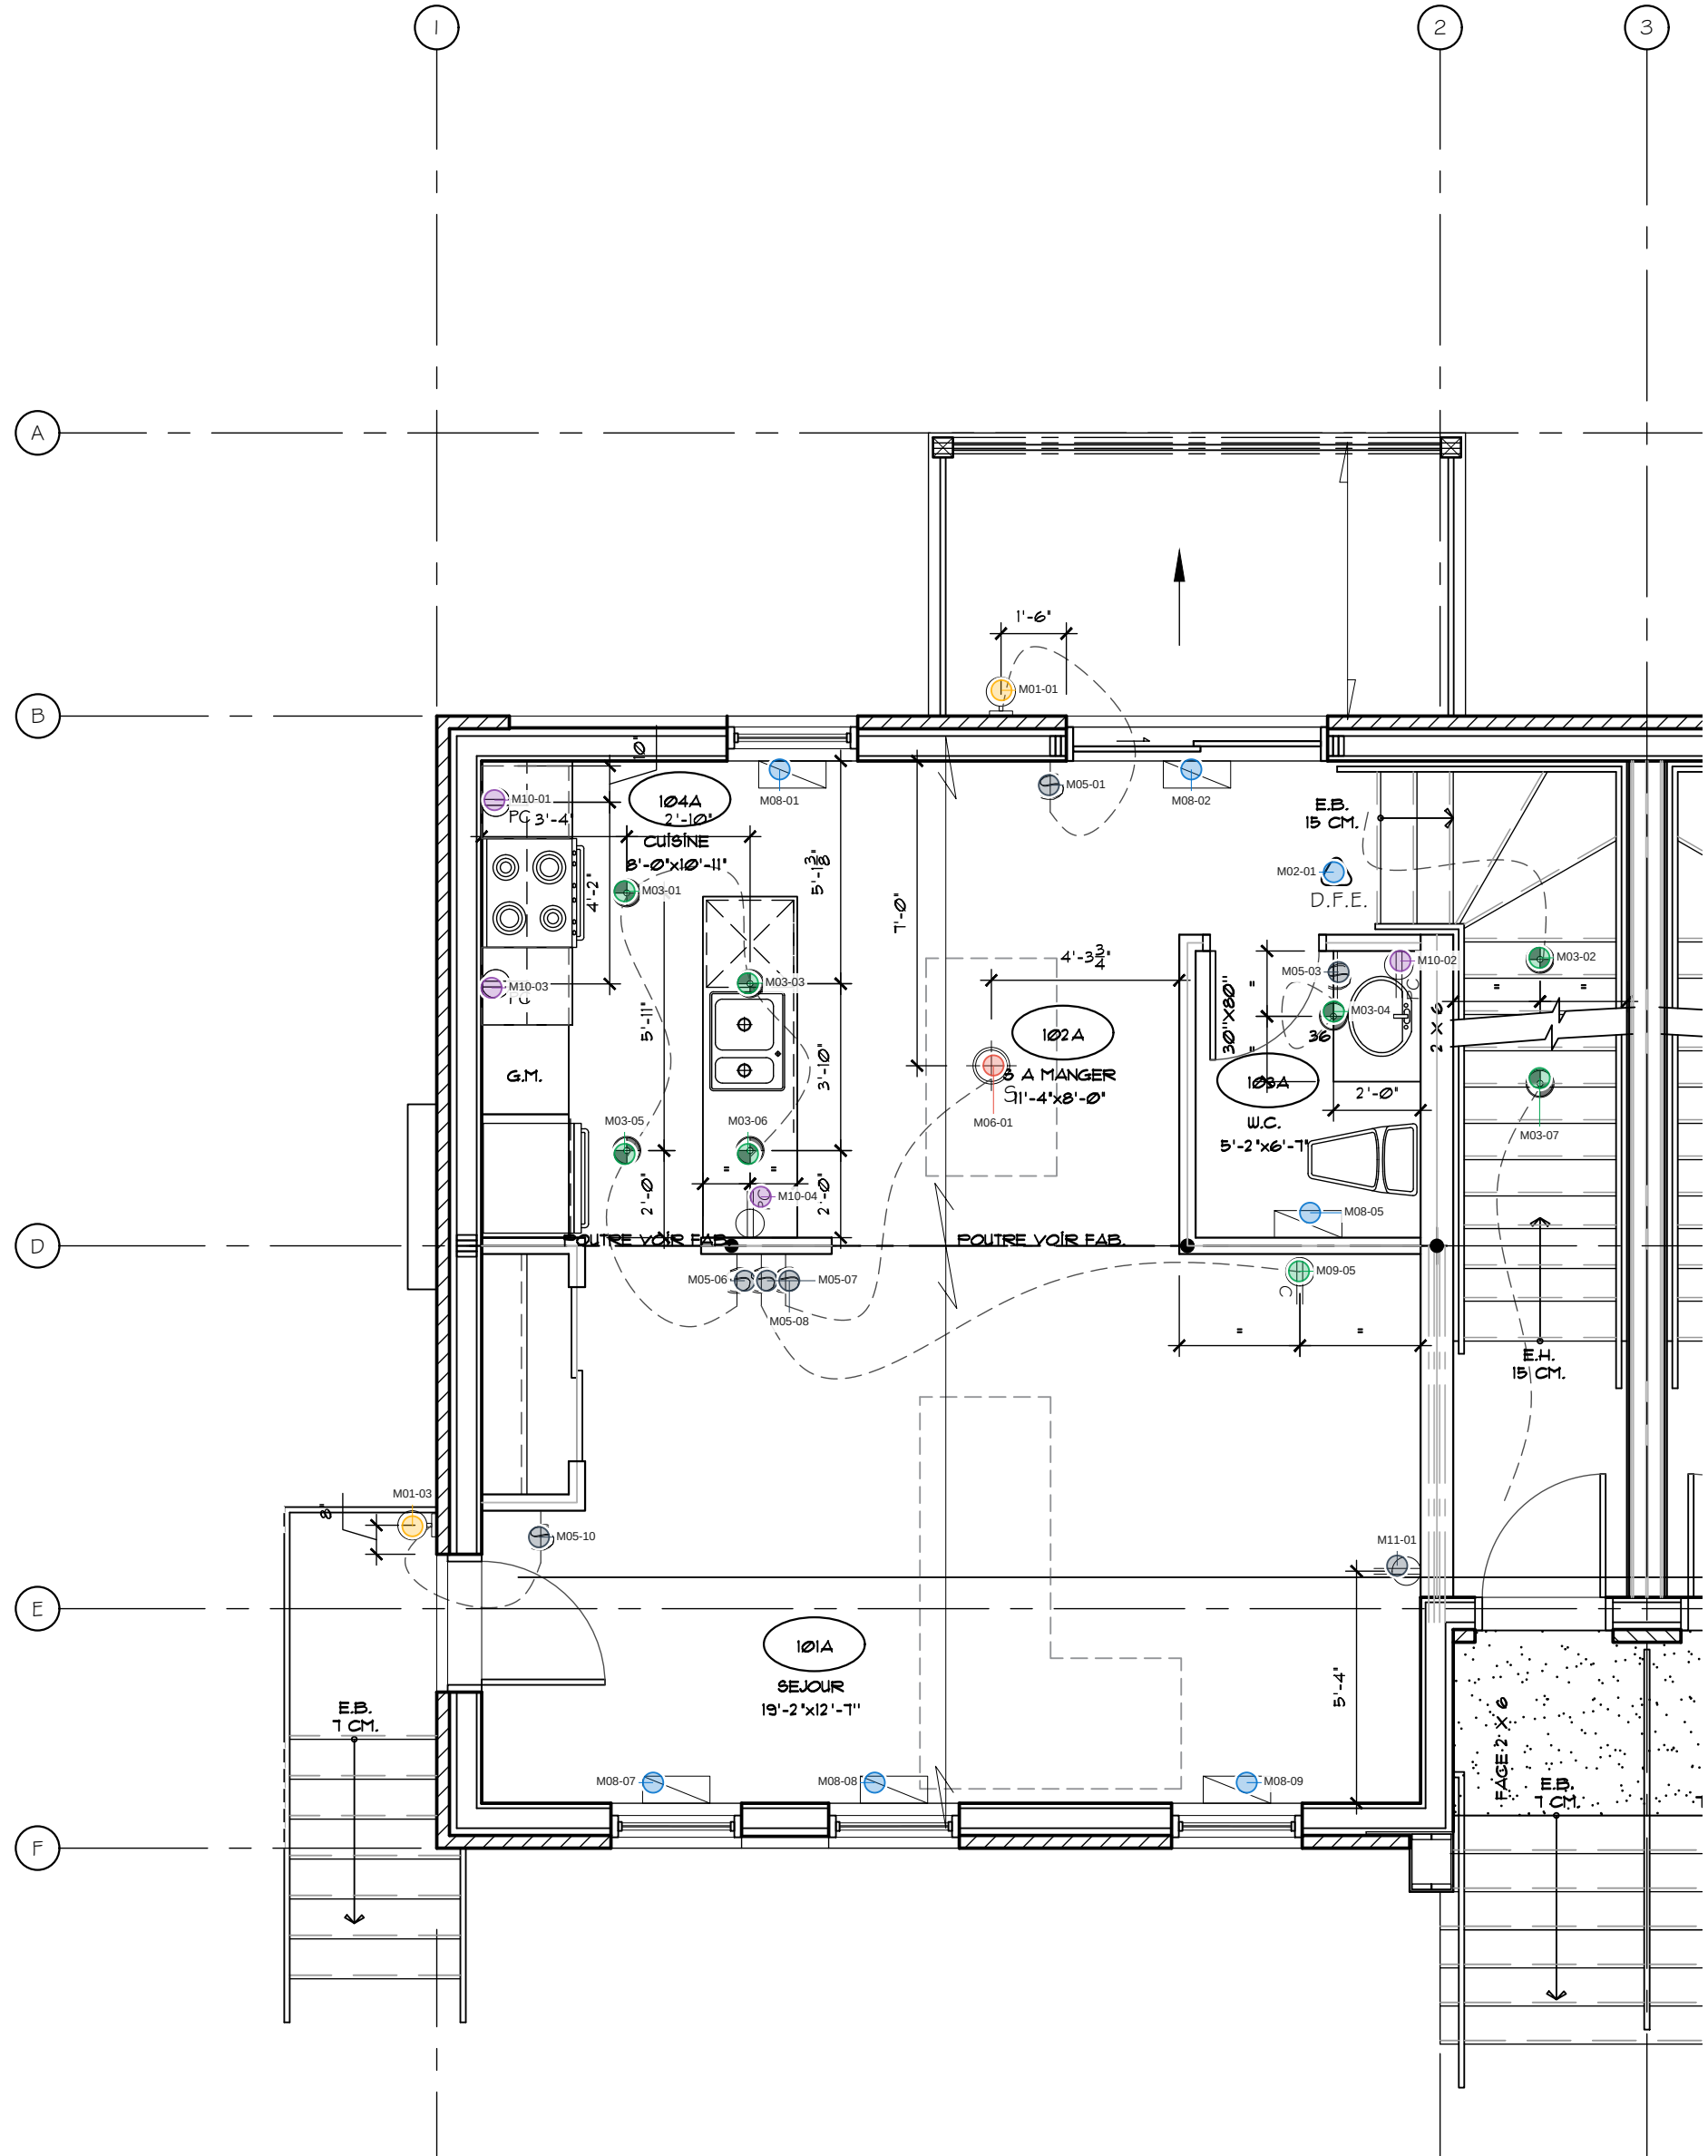

UNITÉ TYPE A - PLAN DU REZ-DE-CHAUSSEE
NOUVELLE CONDITION
Echelle 1/4" = 1'-0"
A-801

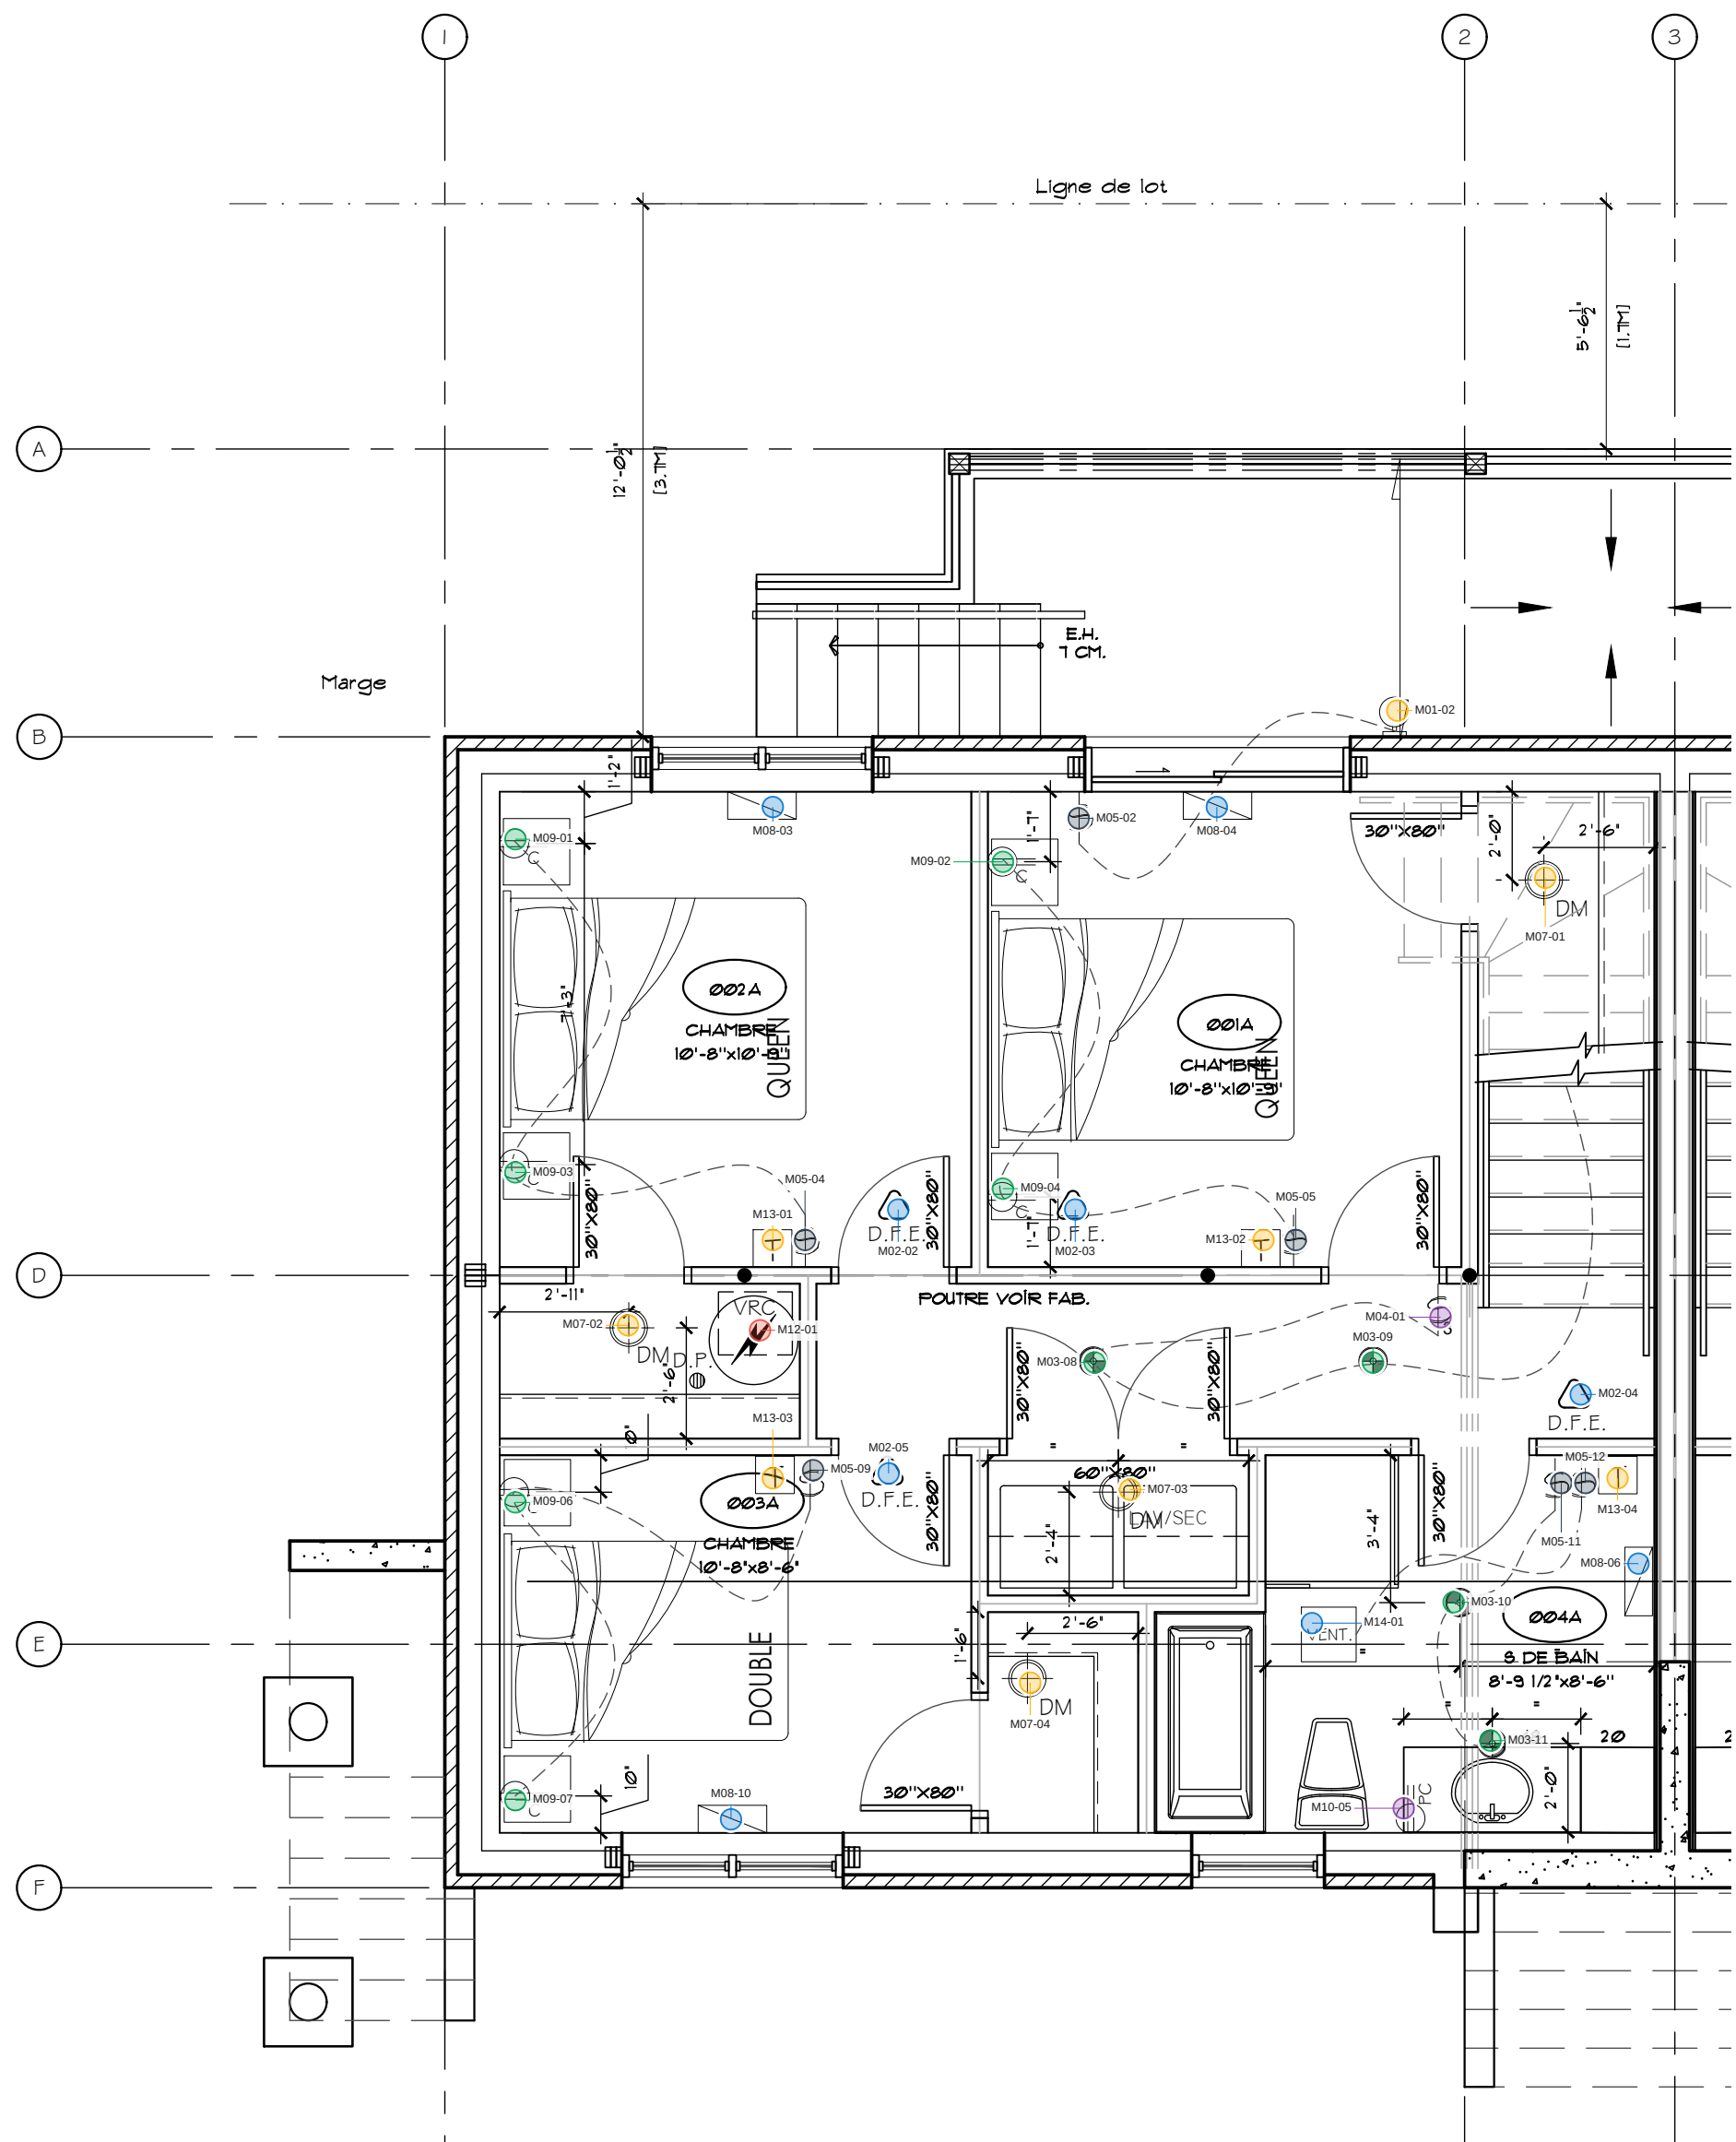

UNITÉ TYPE A - PLAN SOUS-SOL
NOUVELLE CONDITION
Echelle 1/4" = 1'-0"
A-801

LÉGENDE D'ÉCLAIRAGE

- ENCASTRE SLIM
MODÈLE: XX
CODE: XX
DIM: BLANC
FINI: BLANC
- LUMINAIRE SUSPENDU
MODÈLE:
CODE:
FINI:
- PLAFONNIER DETECTEUR DE MOUVEMENT
MODÈLE:
CODE:
FINI: BLANC
- APPLIQUE MURALE - SALLE D'ATTENTE
MODÈLE: JASPER WALL SCONE
CODE: 4192504
FINI: EBONY
DIM: 4" X 24"

LÉGENDE ÉLECTRIQUE

- PRISE ÉLECTRIQUE HAUTEUR STANDARD
- PRISE ÉLECTRIQUE HAUTEUR COMPTOIR
- PRISE ÉLECTRIQUE SUR CABINET
- PRISE ÉLECTRIQUE CONTRÔLÉ PAR INTERRUPTEUR
- THERMOSTAT
- INTERRUPTEUR HAUTEUR STANDARD
- INTERRUPTEUR 3 VOIES HAUTEUR STANDARD
- VENTILATEUR
MODÈLE À VALIDER AVEC ÉLECTRICIEN, VALIDER SON POSITIONNEMENT SUITE À LA COORDINATION AVEC LES PLANS MÉCANIQUES COMPLET
- PANNEAU ÉLECTRIQUE
MODÈLE À VALIDER AVEC ÉLECTRICIEN, VALIDER SON POSITIONNEMENT SUITE À LA COORDINATION AVEC LES PLANS MÉCANIQUES COMPLET
- PLINTE ÉLECTRIQUE
WATT À VALIDER PAR ÉLECTRICIEN, SELON LES NORMES EN VIGUEUR

NOTES :

TOUTES LES MESURES ONT ÉTÉ VÉRIFIÉES SUR PLACE EN PRÉSENCE DU CLIENT. LES LOCAUX DU REZ-DE-CHAUSSEE ET DES ÉTAGES ONT ÉTÉ VALIDÉS.

CES PLANS SONT LA VERSION ABRÉGÉE POUR LA DEMANDE DE PERMIS ET SOUMISSIONS SEULEMENT ET EN CONFORMITÉ AU CNBQ PR-VIGUEUR 2015 MODIFIÉ.

LE NIVEAU 1000' CORRESPOND AU NIVEAU 16,74m DU PLAN D'ARPEUTEUR (GÉOMÉTRIE) DU 23 MARS 2026.

16	EMIS POUR CONSTRUCTION - ESTIMATION FINALE	FSTG 2026/08/26
15	EMIS POUR CONSTRUCTION	FSTG 2026/08/26
14	EMIS COORD/CONSTRUCTION 95% Rev	FSTG 2026/04/30
13	EMIS PERMIS/CONSTRUCTION 95% Rev	FSTG 2026/04/21
12	EMIS PERMIS/CONSTRUCTION 95%	FSTG 2026/04/13
11	EMIS POUR CONSTRUCTION 90%	FSTG 2026/03/30
10	EMIS POUR PERMIS/SOUMISSION REV02	FSTG 2026/03/13
09	EMIS POUR PERMIS/SOUMISSION	FSTG 2026/01/21
08	EMIS POUR PERMIS/SOUMISSION	FSTG 2025/12/11
07	EMIS POUR COMMENTAIRES	FSTG 2025/11/06
06	EMIS POUR COMMENTAIRES	FSTG 2025/10/02
05	EMIS POUR CCU/FI/A	FSTG 2024/10/30
04	EMIS POUR CCU/FI/A	FSTG 2024/10/18
03	EMIS POUR CCU/FI/A	FSTG 2024/10/18
02	EMIS POUR APPROBATION	FSTG 2023/12/14
01	EMIS POUR APPROBATION	FSTG 2023/06/14
No.	REVISION	PAR DATE

PROJET: AGRANDISSEMENT
MULTILOGEMENT-ROY
POUR PERMIS
Sorel, QC

CLIENT: IMMEUBLES DE TRACY INC
40 RUE ELIZABETH
SOREL-TRACY, QC
450-701-1998 COURRIEL: dev@tracyrealestate.com
ARCHITECTE

CONSULTANTS:

STRUCTURE:

MEC/ELEC:

A: No. DU DESSIN
B: No. DE FEUILLE OU LE DESSIN EST DÉTAILLÉ

DESSINE PAR:
P.BTG.
VÉRIFIÉ PAR:
P.BTG.

TITRE:
UNITÉ TYPE A ET TYPE B EN MIROIR

NOUVELLE CONDITION

DOSSIER:
23-2554
DATE:
2024/01
ÉCHELLE:
INDIQUÉE

No.:
A-801

NOTE:
L'ENTREPRENEUR DEVRA PRENDRE ET VÉRIFIER SUR PLACE LES DIMENSIONS AVANT DE COMMENCER TOUT TRAVAIL.

LE MOBILIER INTÉGRÉ ET LE PLAN ÉLECTRIQUE SCHÉMATIQUE SONT PRÉSENTÉS AUX PRÉSENTES À TITRE DE COORDINATION ET D'INFORMATION SEULEMENT. ILS ONT ÉTÉ INCLUS AFIN D'ASSURER LA COMPATIBILITÉ AVEC LES PLANS D'ARCHITECTURE ET DE FACILITER LA LECTURE DES DOCUMENTS. EN CAS DE DISCORDANCE ENTRE LES PRÉSENTS PLANS ET CEUX DU DESIGNER D'INTÉRIEUR, LES PLANS DU DESIGNER D'INTÉRIEUR PRÉVALENT QUANT À LA CONFIGURATION DU MOBILIER INTÉGRÉ, À L'EMPLACEMENT DES PRISES ÉLECTRIQUES ET AUX ÉQUIPEMENTS QUI Y SONT ASSOCIÉS.

BORDEREAU MATERIEL - A801

Quantites representees avec multiplicateurs; portees et composants de chaque ensemble conserves.
Les renvois et composants de panneaux ne constituent pas des ensembles supplementaires a additionner.

Repere / source	Materiel	Designation	Qte	Portee	Modele	Prescription / reserve	Parent
M01-01 A801-002	APPLIQUE MURALE - SALLE D'ATTENTE	LM	1	INSTALLER	UNION LIGHTING JASPER WALL SCONCE CODE: 4192584	FINI: EBONY DIM: 4 X 24	
M01-02 A801-004	APPLIQUE MURALE - SALLE D'ATTENTE	LM	1	INSTALLER	UNION LIGHTING JASPER WALL SCONCE CODE: 4192584	FINI: EBONY DIM: 4 X 24	
M01-03 A801-046	APPLIQUE MURALE - SALLE D'ATTENTE	LM	1	INSTALLER	UNION LIGHTING JASPER WALL SCONCE CODE: 4192584	FINI: EBONY DIM: 4 X 24	
M02-01 A801-014	DETECTEUR DE FUMEE D.F.E. (HORS LEGENDE - R-001)	AF	1	A PRECISER	MODELE NON PRECISE	Detecteur de fumee D.F.E. (hors legende - R-001)	
M02-02 A801-030	DETECTEUR DE FUMEE D.F.E. (HORS LEGENDE - R-001)	AF	1	A PRECISER	MODELE NON PRECISE	Detecteur de fumee D.F.E. (hors legende - R-001)	
M02-03 A801-032	DETECTEUR DE FUMEE D.F.E. (HORS LEGENDE - R-001)	AF	1	A PRECISER	MODELE NON PRECISE	Detecteur de fumee D.F.E. (hors legende - R-001)	
M02-04 A801-045	DETECTEUR DE FUMEE D.F.E. (HORS LEGENDE - R-001)	AF	1	A PRECISER	MODELE NON PRECISE	Detecteur de fumee D.F.E. (hors legende - R-001)	
M02-05 A801-050	DETECTEUR DE FUMEE D.F.E. (HORS LEGENDE - R-001)	AF	1	A PRECISER	MODELE NON PRECISE	Detecteur de fumee D.F.E. (hors legende - R-001)	
M03-01 A801-013	ENCASTRE SLIM	LE	1	INSTALLER	MODELE: XX CODE: XX	FINI: BLANC	
M03-02 A801-016	ENCASTRE SLIM	LE	1	INSTALLER	MODELE: XX CODE: XX	FINI: BLANC	
M03-03 A801-018	ENCASTRE SLIM	LE	1	INSTALLER	MODELE: XX CODE: XX	FINI: BLANC	
M03-04 A801-019	ENCASTRE SLIM	LE	1	INSTALLER	MODELE: XX CODE: XX	FINI: BLANC	
M03-05 A801-021	ENCASTRE SLIM	LE	1	INSTALLER	MODELE: XX CODE: XX	FINI: BLANC	
M03-06 A801-022	ENCASTRE SLIM	LE	1	INSTALLER	MODELE: XX CODE: XX	FINI: BLANC	
M03-07 A801-024	ENCASTRE SLIM	LE	1	INSTALLER	MODELE: XX CODE: XX	FINI: BLANC	
M03-08 A801-041	ENCASTRE SLIM	LE	1	INSTALLER	MODELE: XX CODE: XX	FINI: BLANC	
M03-09 A801-042	ENCASTRE SLIM	LE	1	INSTALLER	MODELE: XX CODE: XX	FINI: BLANC	
M03-10 A801-058	ENCASTRE SLIM	LE	1	INSTALLER	MODELE: XX CODE: XX	FINI: BLANC	
M03-11 A801-060	ENCASTRE SLIM	LE	1	INSTALLER	MODELE: XX CODE: XX	FINI: BLANC	
M04-01 A801-043	INTERRUPTEUR 3 VOIES HAUTEUR STANDARD	C3	1	INSTALLER	MODELE NON PRECISE	Interrupteur 3 voies hauteur standard	

BORDEREAU MATERIEL - A801

Quantites representees avec multiplicateurs; portees et composants de chaque ensemble conserves.
Les renvois et composants de panneaux ne constituent pas des ensembles supplementaires a additionner.

Repere / source	Materiel	Designation	Qte	Portee	Modele	Prescription / reserve	Parent
M05-01 A801-006	INTERRUPTEUR HAUTEUR STANDARD	CU	1	INSTALLER	MODELE NON PRECISE	Interrupteur hauteur standard	
M05-02 A801-010	INTERRUPTEUR HAUTEUR STANDARD	CU	1	INSTALLER	MODELE NON PRECISE	Interrupteur hauteur standard	
M05-03 A801-020	INTERRUPTEUR HAUTEUR STANDARD	CU	1	INSTALLER	MODELE NON PRECISE	Interrupteur hauteur standard	
M05-04 A801-029	INTERRUPTEUR HAUTEUR STANDARD	CU	1	INSTALLER	MODELE NON PRECISE	Interrupteur hauteur standard	
M05-05 A801-034	INTERRUPTEUR HAUTEUR STANDARD	CU	1	INSTALLER	MODELE NON PRECISE	Interrupteur hauteur standard	
M05-06 A801-035	INTERRUPTEUR HAUTEUR STANDARD	CU	1	INSTALLER	MODELE NON PRECISE	Interrupteur hauteur standard	
M05-07 A801-036	INTERRUPTEUR HAUTEUR STANDARD	CU	1	INSTALLER	MODELE NON PRECISE	Interrupteur hauteur standard	
M05-08 A801-037	INTERRUPTEUR HAUTEUR STANDARD	CU	1	INSTALLER	MODELE NON PRECISE	Interrupteur hauteur standard	
M05-09 A801-044	INTERRUPTEUR HAUTEUR STANDARD	CU	1	INSTALLER	MODELE NON PRECISE	Interrupteur hauteur standard	
M05-10 A801-047	INTERRUPTEUR HAUTEUR STANDARD	CU	1	INSTALLER	MODELE NON PRECISE	Interrupteur hauteur standard	
M05-11 A801-052	INTERRUPTEUR HAUTEUR STANDARD	CU	1	INSTALLER	MODELE NON PRECISE	Interrupteur hauteur standard	
M05-12 A801-053	INTERRUPTEUR HAUTEUR STANDARD	CU	1	INSTALLER	MODELE NON PRECISE	Interrupteur hauteur standard	
M06-01 A801-023	LUMINAIRE SUSPENDU	LS	1	INSTALLER	MODELE NON PRECISE	Luminaire suspendu (legende d'eclairage)	
M07-01 A801-012	PLAFONNIER DETECTEUR DE MOUVEMENT	LD	1	INSTALLER	MODELE NON PRECISE	FINIS: BLANC	
M07-02 A801-039	PLAFONNIER DETECTEUR DE MOUVEMENT	LD	1	INSTALLER	MODELE NON PRECISE	FINIS: BLANC	
M07-03 A801-051	PLAFONNIER DETECTEUR DE MOUVEMENT	LD	1	INSTALLER	MODELE NON PRECISE	FINIS: BLANC	
M07-04 A801-059	PLAFONNIER DETECTEUR DE MOUVEMENT	LD	1	INSTALLER	MODELE NON PRECISE	FINIS: BLANC	
M08-01 A801-001	PLINTHE ELECTRIQUE	PL	1	INSTALLER	MODELE NON PRECISE	WATT A VALIDER PAR ELECTRICIEN SELON LES NORMES EN VIGUEURES	
M08-02 A801-003	PLINTHE ELECTRIQUE	PL	1	INSTALLER	MODELE NON PRECISE	WATT A VALIDER PAR ELECTRICIEN SELON LES NORMES EN VIGUEURES	
M08-03 A801-008	PLINTHE ELECTRIQUE	PL	1	INSTALLER	MODELE NON PRECISE	WATT A VALIDER PAR ELECTRICIEN SELON LES NORMES EN VIGUEURES	

BORDEREAU MATERIEL - A801

Quantites representees avec multiplicateurs; portees et composants de chaque ensemble conserves.
Les renvois et composants de panneaux ne constituent pas des ensembles supplementaires a additionner.

Repere / source	Materiel	Designation	Qte	Portee	Modele	Prescription / reserve	Parent
M08-04 A801-011	PLINTHE ELECTRIQUE	PL	1	INSTALLER	MODELE NON PRECISE	WATT A VALIDER PAR ELECTRICIEN SELON LES NORMES EN VIGUEURES	
M08-05 A801-027	PLINTHE ELECTRIQUE	PL	1	INSTALLER	MODELE NON PRECISE	WATT A VALIDER PAR ELECTRICIEN SELON LES NORMES EN VIGUEURES	
M08-06 A801-055	PLINTHE ELECTRIQUE	PL	1	INSTALLER	MODELE NON PRECISE	WATT A VALIDER PAR ELECTRICIEN SELON LES NORMES EN VIGUEURES	
M08-07 A801-061	PLINTHE ELECTRIQUE	PL	1	INSTALLER	MODELE NON PRECISE	WATT A VALIDER PAR ELECTRICIEN SELON LES NORMES EN VIGUEURES	
M08-08 A801-062	PLINTHE ELECTRIQUE	PL	1	INSTALLER	MODELE NON PRECISE	WATT A VALIDER PAR ELECTRICIEN SELON LES NORMES EN VIGUEURES	
M08-09 A801-063	PLINTHE ELECTRIQUE	PL	1	INSTALLER	MODELE NON PRECISE	WATT A VALIDER PAR ELECTRICIEN SELON LES NORMES EN VIGUEURES	
M08-10 A801-065	PLINTHE ELECTRIQUE	PL	1	INSTALLER	MODELE NON PRECISE	WATT A VALIDER PAR ELECTRICIEN SELON LES NORMES EN VIGUEURES	
M09-01 A801-007	PRISE ELECTRIQUE CONTROLE PAR INTERRUPTEUR	CI	1	INSTALLER	MODELE NON PRECISE	Prise electrique controle par interrupteur C	
M09-02 A801-009	PRISE ELECTRIQUE CONTROLE PAR INTERRUPTEUR	CI	1	INSTALLER	MODELE NON PRECISE	Prise electrique controle par interrupteur C	
M09-03 A801-025	PRISE ELECTRIQUE CONTROLE PAR INTERRUPTEUR	CI	1	INSTALLER	MODELE NON PRECISE	Prise electrique controle par interrupteur C	
M09-04 A801-031	PRISE ELECTRIQUE CONTROLE PAR INTERRUPTEUR	CI	1	INSTALLER	MODELE NON PRECISE	Prise electrique controle par interrupteur C	
M09-05 A801-038	PRISE ELECTRIQUE CONTROLE PAR INTERRUPTEUR	CI	1	INSTALLER	MODELE NON PRECISE	Prise electrique controle par interrupteur C	
M09-06 A801-048	PRISE ELECTRIQUE CONTROLE PAR INTERRUPTEUR	CI	1	INSTALLER	MODELE NON PRECISE	Prise electrique controle par interrupteur C	
M09-07 A801-064	PRISE ELECTRIQUE CONTROLE PAR INTERRUPTEUR	CI	1	INSTALLER	MODELE NON PRECISE	Prise electrique controle par interrupteur C	
M10-01 A801-005	PRISE ELECTRIQUE HAUTEUR COMPTOIR	CT	1	INSTALLER	MODELE NON PRECISE	Prise electrique hauteur comptoir PC	
M10-02 A801-015	PRISE ELECTRIQUE HAUTEUR COMPTOIR	CT	1	INSTALLER	MODELE NON PRECISE	Prise electrique hauteur comptoir PC	
M10-03 A801-017	PRISE ELECTRIQUE HAUTEUR COMPTOIR	CT	1	INSTALLER	MODELE NON PRECISE	Prise electrique hauteur comptoir PC	
M10-04 A801-026	PRISE ELECTRIQUE HAUTEUR COMPTOIR	CT	1	INSTALLER	MODELE NON PRECISE	Prise electrique hauteur comptoir PC	
M10-05 A801-066	PRISE ELECTRIQUE HAUTEUR COMPTOIR	CT	1	INSTALLER	MODELE NON PRECISE	Prise electrique hauteur comptoir PC	
M11-01 A801-056	PRISE ELECTRIQUE HAUTEUR STANDARD	PC	1	INSTALLER	MODELE NON PRECISE	Prise electrique hauteur standard	

BORDEREAU MATERIEL - A801

Quantites representees avec multiplicateurs; portees et composants de chaque ensemble conservees.
Les renvois et composants de panneaux ne constituent pas des ensembles supplementaires a additionner.

Repere / source	Materiel	Designation	Qte	Portee	Modele	Prescription / reserve	Parent
M12-01 A801-040	RACCORD DIRECT VRC (HORS LEGENDE - R-001)	RA	1	A PRECISER	MODELE NON PRECISE	Raccord direct VRC (hors legende - R-001)	
M13-01 A801-028	THERMOSTAT	TH	1	INSTALLER	MODELE NON PRECISE	Thermostat T	
M13-02 A801-033	THERMOSTAT	TH	1	INSTALLER	MODELE NON PRECISE	Thermostat T	
M13-03 A801-049	THERMOSTAT	TH	1	INSTALLER	MODELE NON PRECISE	Thermostat T	
M13-04 A801-054	THERMOSTAT	TH	1	INSTALLER	MODELE NON PRECISE	Thermostat T	
M14-01 A801-057	VENTILATEUR	EV	1	INSTALLER	MODELE NON PRECISE	MODELE A VALIDER AVEC ELECTRICIEN; POSITIONNEMENT A VALIDER SUITE A LA COORDINATION MECANIQUE	

RESERVES ET COMPLEMENTS
R-001 - A-801 : symboles D.F.E. (triangle, 5) et VRC (1) présents au plan, absents des légendes électrique et d'éclairage - relevés sous libellé "hors légende", portée A PRECISER ; avertisseur autonome ou détecteur relié au réseau : non tranché par le plan.
R-002 - A-801 RDC W.C. 103A : prise comptoir au lavabo partiellement masquée par le dessin du lavabo - identification à revalider (*).
R-003 - A-801 RDC séjour 101A : prise classée hauteur standard - type à confirmer (*).
R-004 - A-801 RDC sous la poutre (salle à manger / séjour) : prise contrôlée par interrupteur ou standard - glyphe "C" ambigu (*).
R-005 - A-801 : PANNEAU ELECTRIQUE (P.E.) et PRISE ELECTRIQUE SUR CABINET (M) figurent dans la légende électrique mais aucun symbole n'est dessiné sur les deux plans (RDC, sous-sol) - vérifié tuile par tuile ; non relevés.
R-006 - A-801 : plan électrique "schématique, à titre de coordination et d'information seulement" (note *) ; case MEC.ÉLEC. vide (pas d'ingénieur électrique) ; tampon "PLAN PAS POUR CONSTRUCTION".
R-007 - A-801 : quantités = une unité type A ; l'unité type B est en miroir (titre de la feuille) - aucune multiplication par le nombre d'unités sur cette feuille (renvoi au nombre d'unités du projet, 59 logements selon AN25004E, à confirmer).
R-008 - A-801 : aucun circuit ni puissance (W) indiqué au plan ; plinthes "WATT À VALIDER PAR ÉLECTRICIEN" (légende).
R-009 - Sources : aucun devis électrique dans 01_SOURCES ; la directive dc03 porte sur l'entrée électrique (3030/3020), hors A-801 - aucune prescription ajoutée.