

Les architectes Clermont St-Germain associés
1845 Rue de l'Église
Sainte-Julie, Qc, J3E1E9
t. 450.461.0835
pstgermain@architectescs.com
www.architectescs.com

NOTES :
TOUTES LES MESURES ONT ÉTÉ VÉRIFIÉES SUR PLACE EN PRÉSENCE DU CLIENT. LES LOCAUX DU REZ-DE-CHAUSSEE ET DES ÉTAGES ONT ÉTÉ VALIDÉS.

CES PLANS SONT LA VERSION ABREGÉE POUR LA DEMANDE DE PERMIS ET SOUMISSIONS SEULEMENT ET EN CONFORMITÉ AU CNBQ PR-VIGUEUR 2015 MODIFIÉ.
LE NIVEAU 100'0" CORRESPOND AU NIVEAU 16,74m DU PLAN D'ARPEUTEUR (GÉOTERRA) DU 23 MARS 2026.

PLAN PAS POUR CONSTRUCTION

16	EMIS POUR CONSTRUCTION - ESTIMATION FINALE	FSTG 2026/08/26
15	EMIS POUR CONSTRUCTION	FSTG 2026/08/26
14	EMIS COORD/CONSTRUCTION 95% Rev	FSTG 2026/04/30
13	EMIS PERMIS/CONSTRUCTION 95% Rev	FSTG 2026/04/21
12	EMIS PERMIS/CONSTRUCTION 95%	FSTG 2026/04/13
11	EMIS POUR CONSTRUCTION 90%	FSTG 2026/03/30
10	EMIS POUR PERMIS/SOUMISSION REV02	FSTG 2026/03/13
09	EMIS POUR PERMIS/SOUMISSION	FSTG 2026/01/21
08	EMIS POUR PERMIS/SOUMISSION	FSTG 2025/12/11
07	EMIS POUR COMMENTAIRES	FSTG 2025/11/06
06	EMIS POUR COMMENTAIRES	FSTG 2025/10/02
05	EMIS POUR CCU/FIJA	FSTG 2024/10/30
04	EMIS POUR CCU/FIJA	FSTG 2024/10/18
03	EMIS POUR CCU/FIJA	FSTG 2024/10/18
02	EMIS POUR APPROBATION	FSTG 2023/12/14
01	EMIS POUR APPROBATION	FSTG 2023/06/14
No.	REVISION	PAR DATE

PROJET: **AGRANDISSEMENT MULTILOGEMENT-ROY**
POUR PERMIS
Sorel, QC

CLIENT: **IMMEUBLES DE TRACY INC**
40 RUE ELISABETH
SOREL-TRACY, QC
450-781-1886 COURRIEL: dev@tracyrealestate.com
ARCHITECTE


CONSULTANTS:
STRUCTURE:
MEC/ELEC:

A: No. DU DESSIN
B: No. DE FEUILLE OU LE DESSIN EST DÉTAILLÉ
Dessine par: **P.BTG.**
Vérifié par: **P.BTG.**


TITRE:
UNITÉ TYPE A ET TYPE B EN MIROIR
NOUVELLE CONDITION

DOSSIER: **23-2554**
DATE: **2024/01**
ÉCHELLE: **INDIQUÉE**
No.: **A-801**

NOTE:
L'ENTREPRENEUR DEVRA PRENDRE ET VÉRIFIER SUR PLACE LES DIMENSIONS AVANT DE COMMENCER TOUT TRAVAIL.

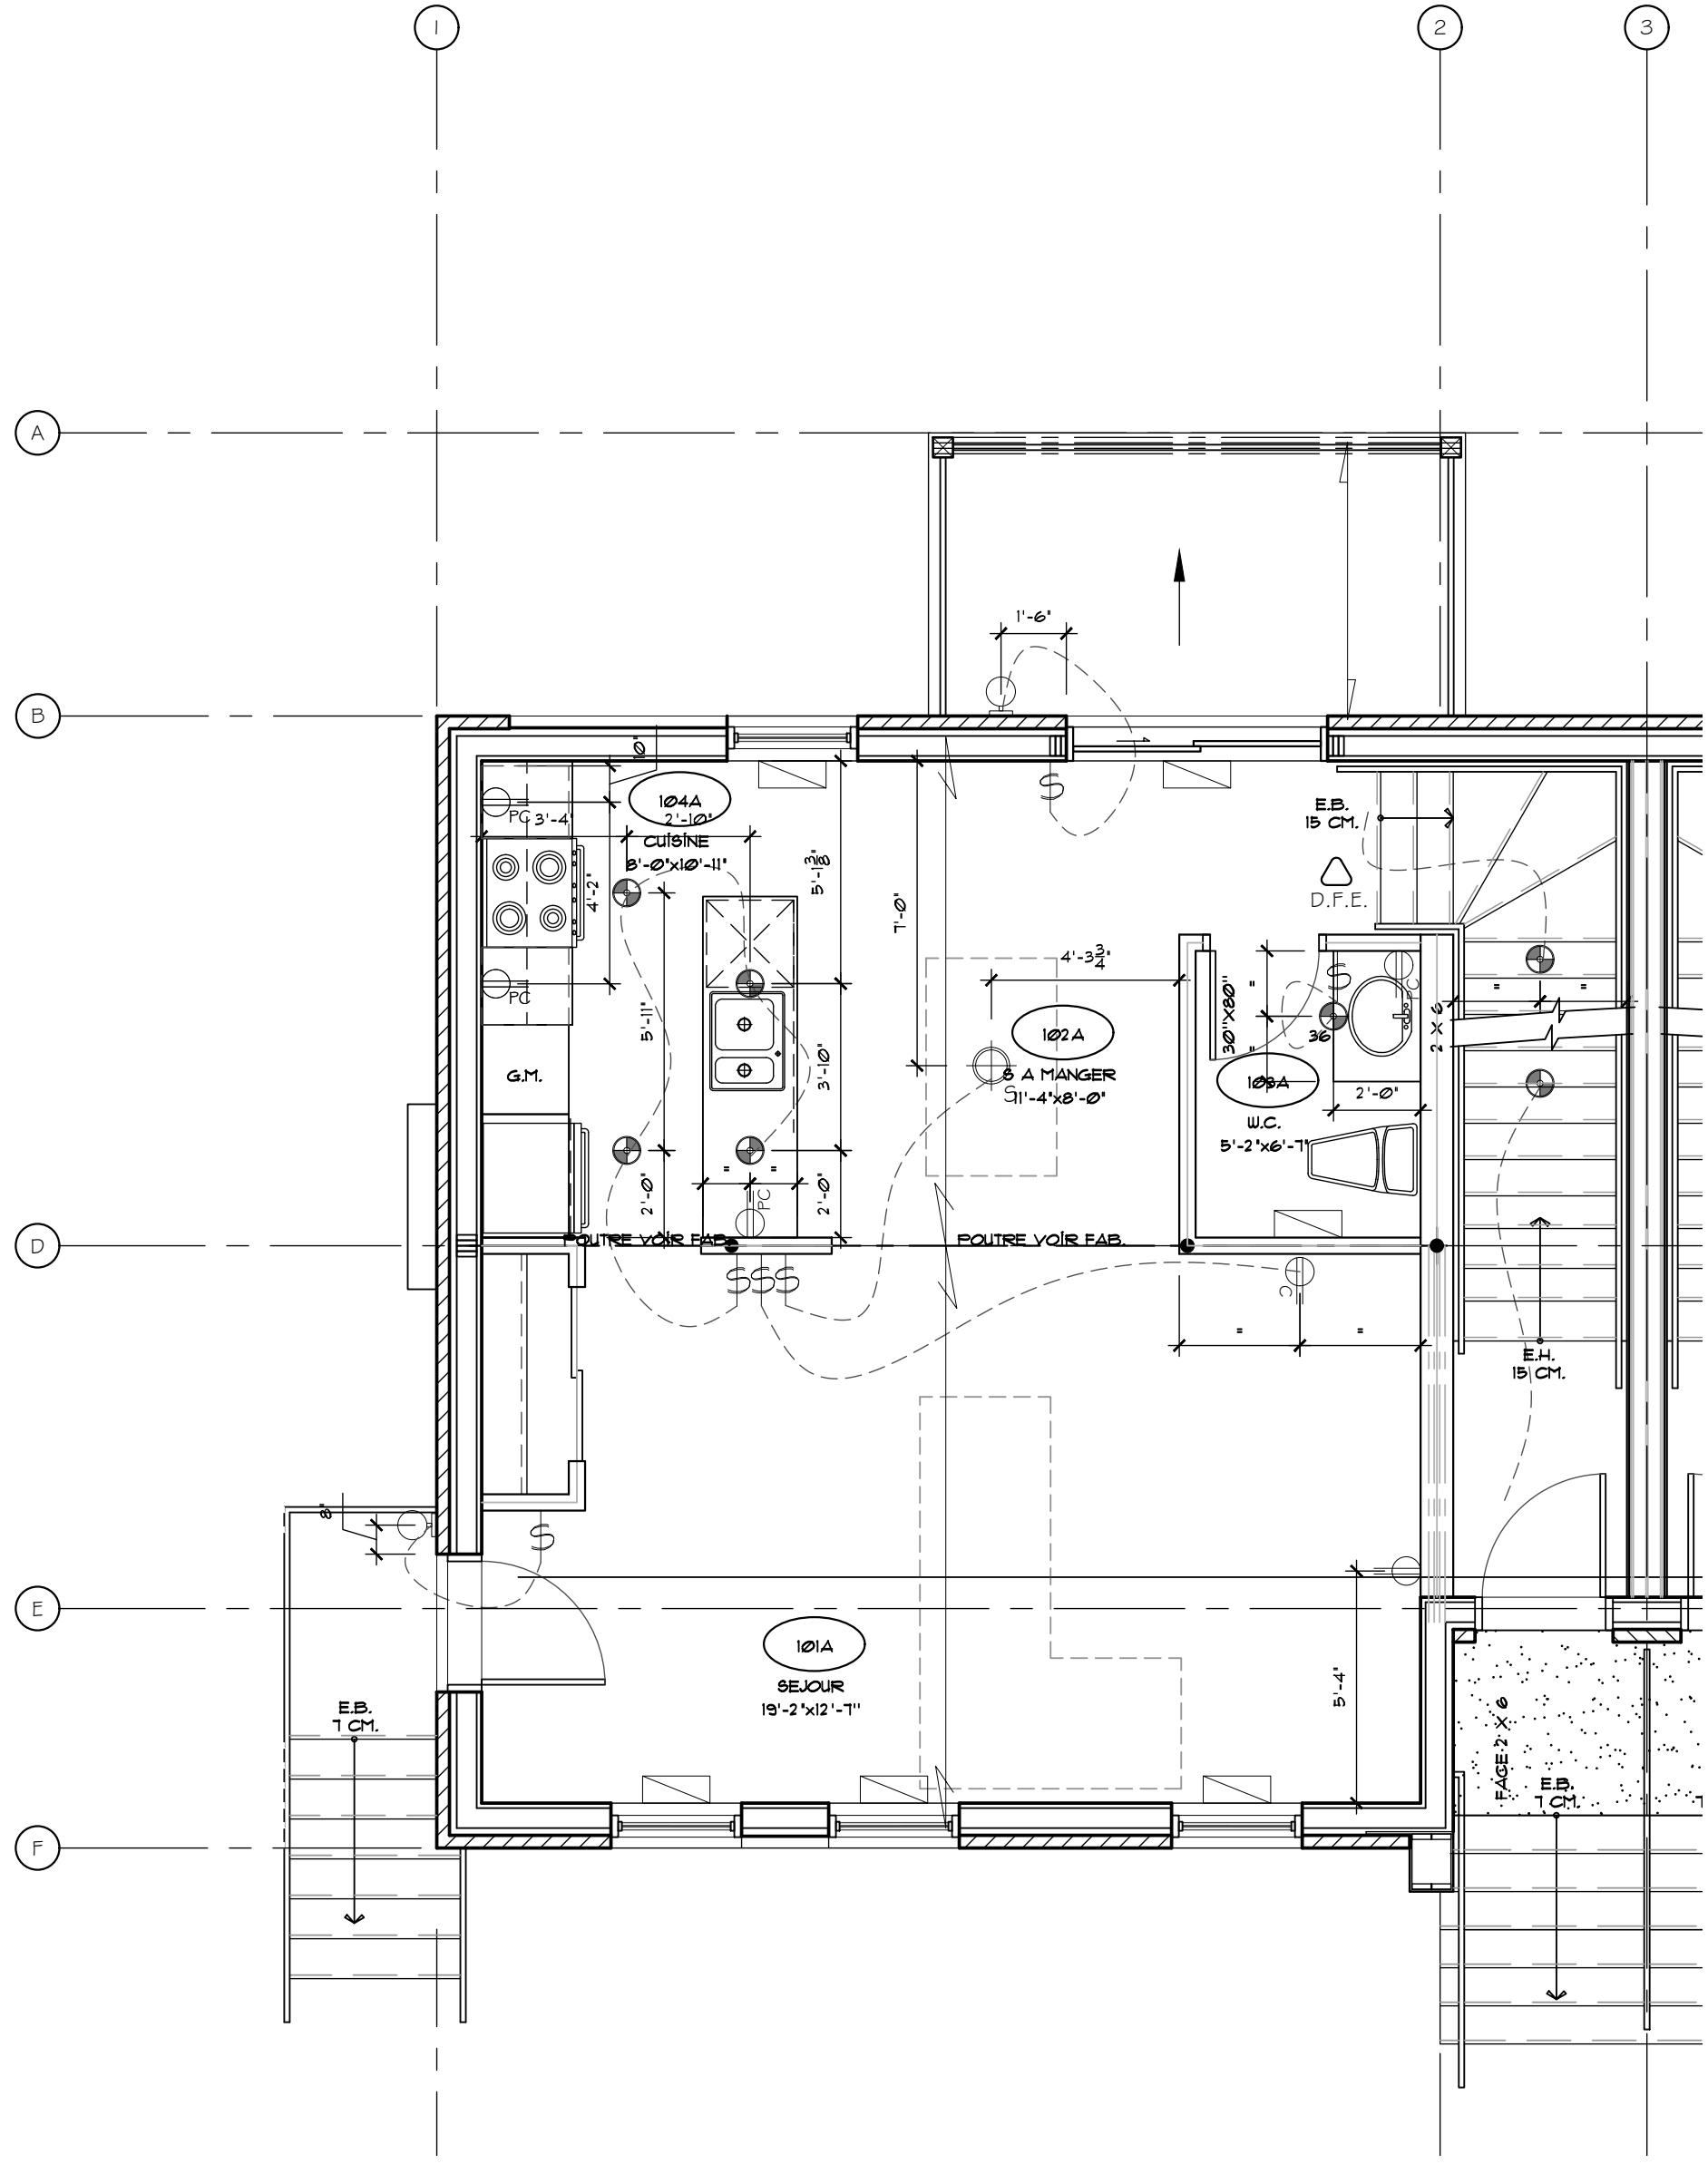

UNITÉ TYPE A - PLAN DU REZ-DE-CHAUSSEE
NOUVELLE CONDITION
ÉCHELLE 1/4"=1'-0" A-801

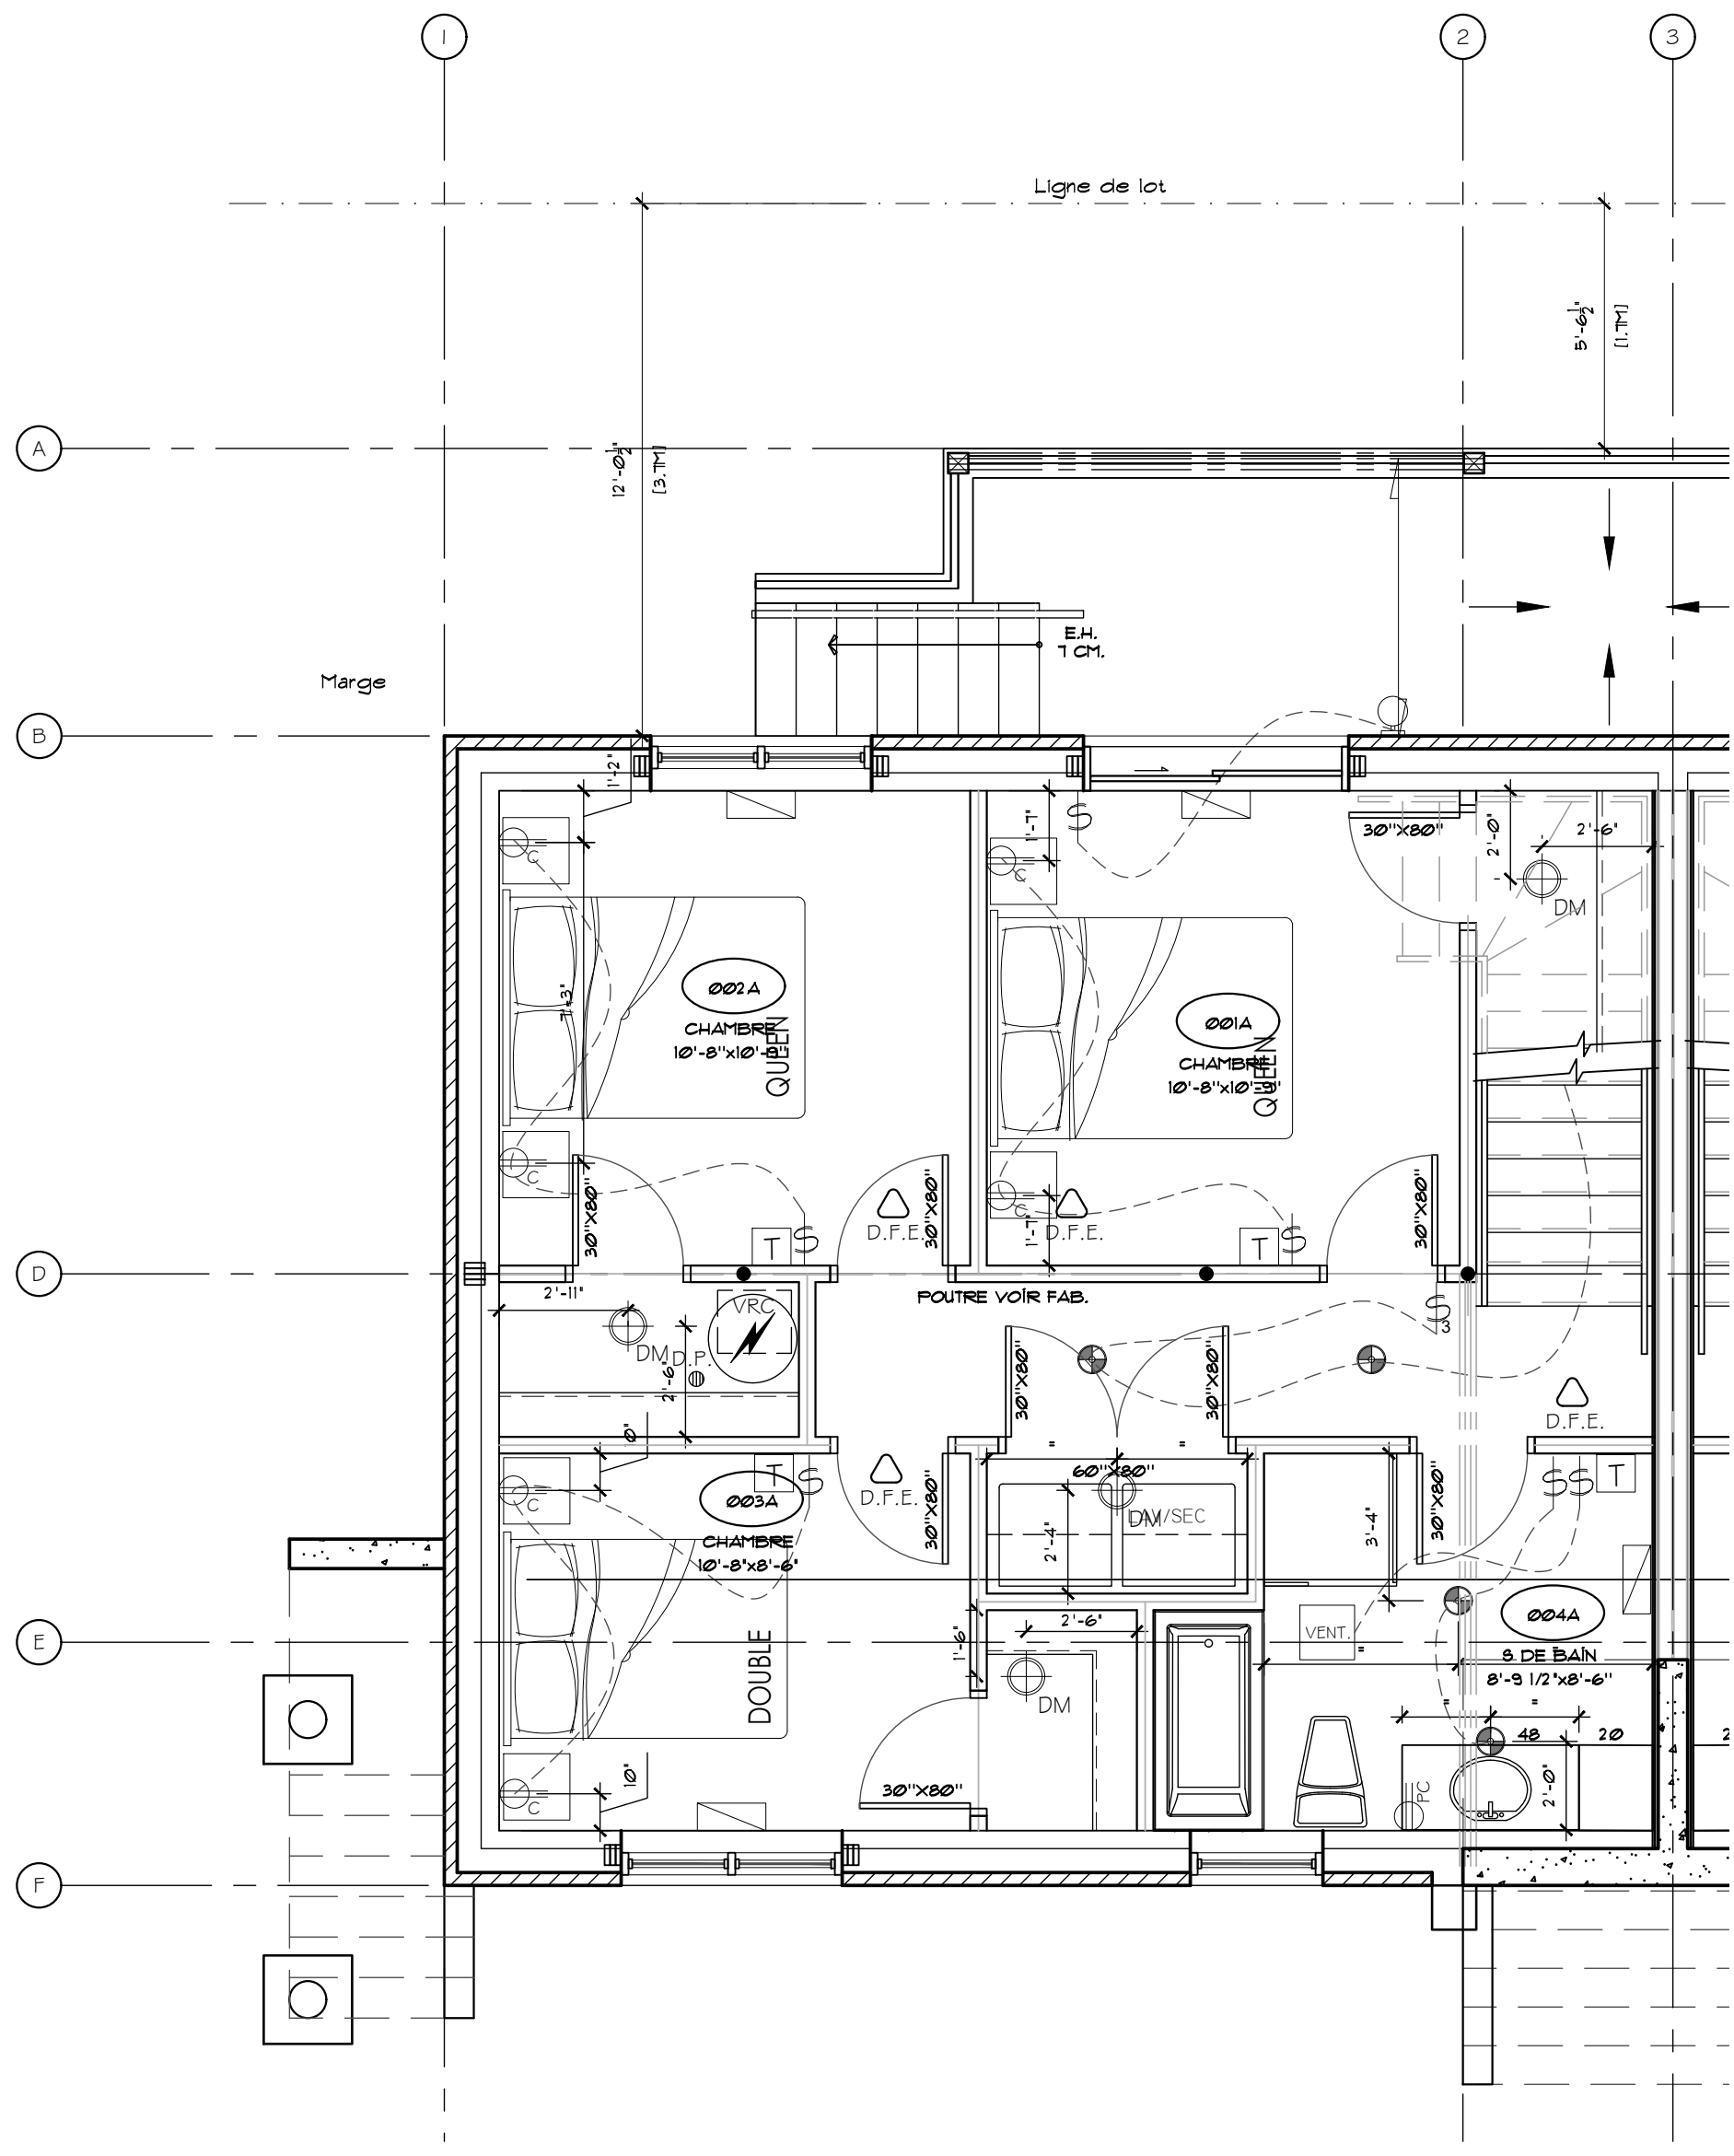

UNITÉ TYPE A - PLAN SOUS-SOL
NOUVELLE CONDITION
ÉCHELLE 1/4"=1'-0" A-801

LE MOBILIER INTÉGRÉ ET LE PLAN ÉLECTRIQUE SCHEMATIQUE SONT PRÉSENTÉS AUX PRÉSENTES À TITRE DE COORDINATION ET D'INFORMATION SEULEMENT. ILS ONT ÉTÉ INCLUS AFIN D'ASSURER LA COMPATIBILITÉ AVEC LES PLANS D'ARCHITECTURE ET DE FACILITER LA LECTURE DES DOCUMENTS. EN CAS DE DISCORDANCE ENTRE LES PRÉSENTS PLANS ET CEUX DU DESIGNER D'INTÉRIEUR, LES PLANS DU DESIGNER D'INTÉRIEUR PRÉVALENT QUANT À LA CONFIGURATION DU MOBILIER INTÉGRÉ, À L'EMPLACEMENT DES PRISES ÉLECTRIQUES ET AUX ÉQUIPEMENTS QUI Y SONT ASSOCIÉS.