

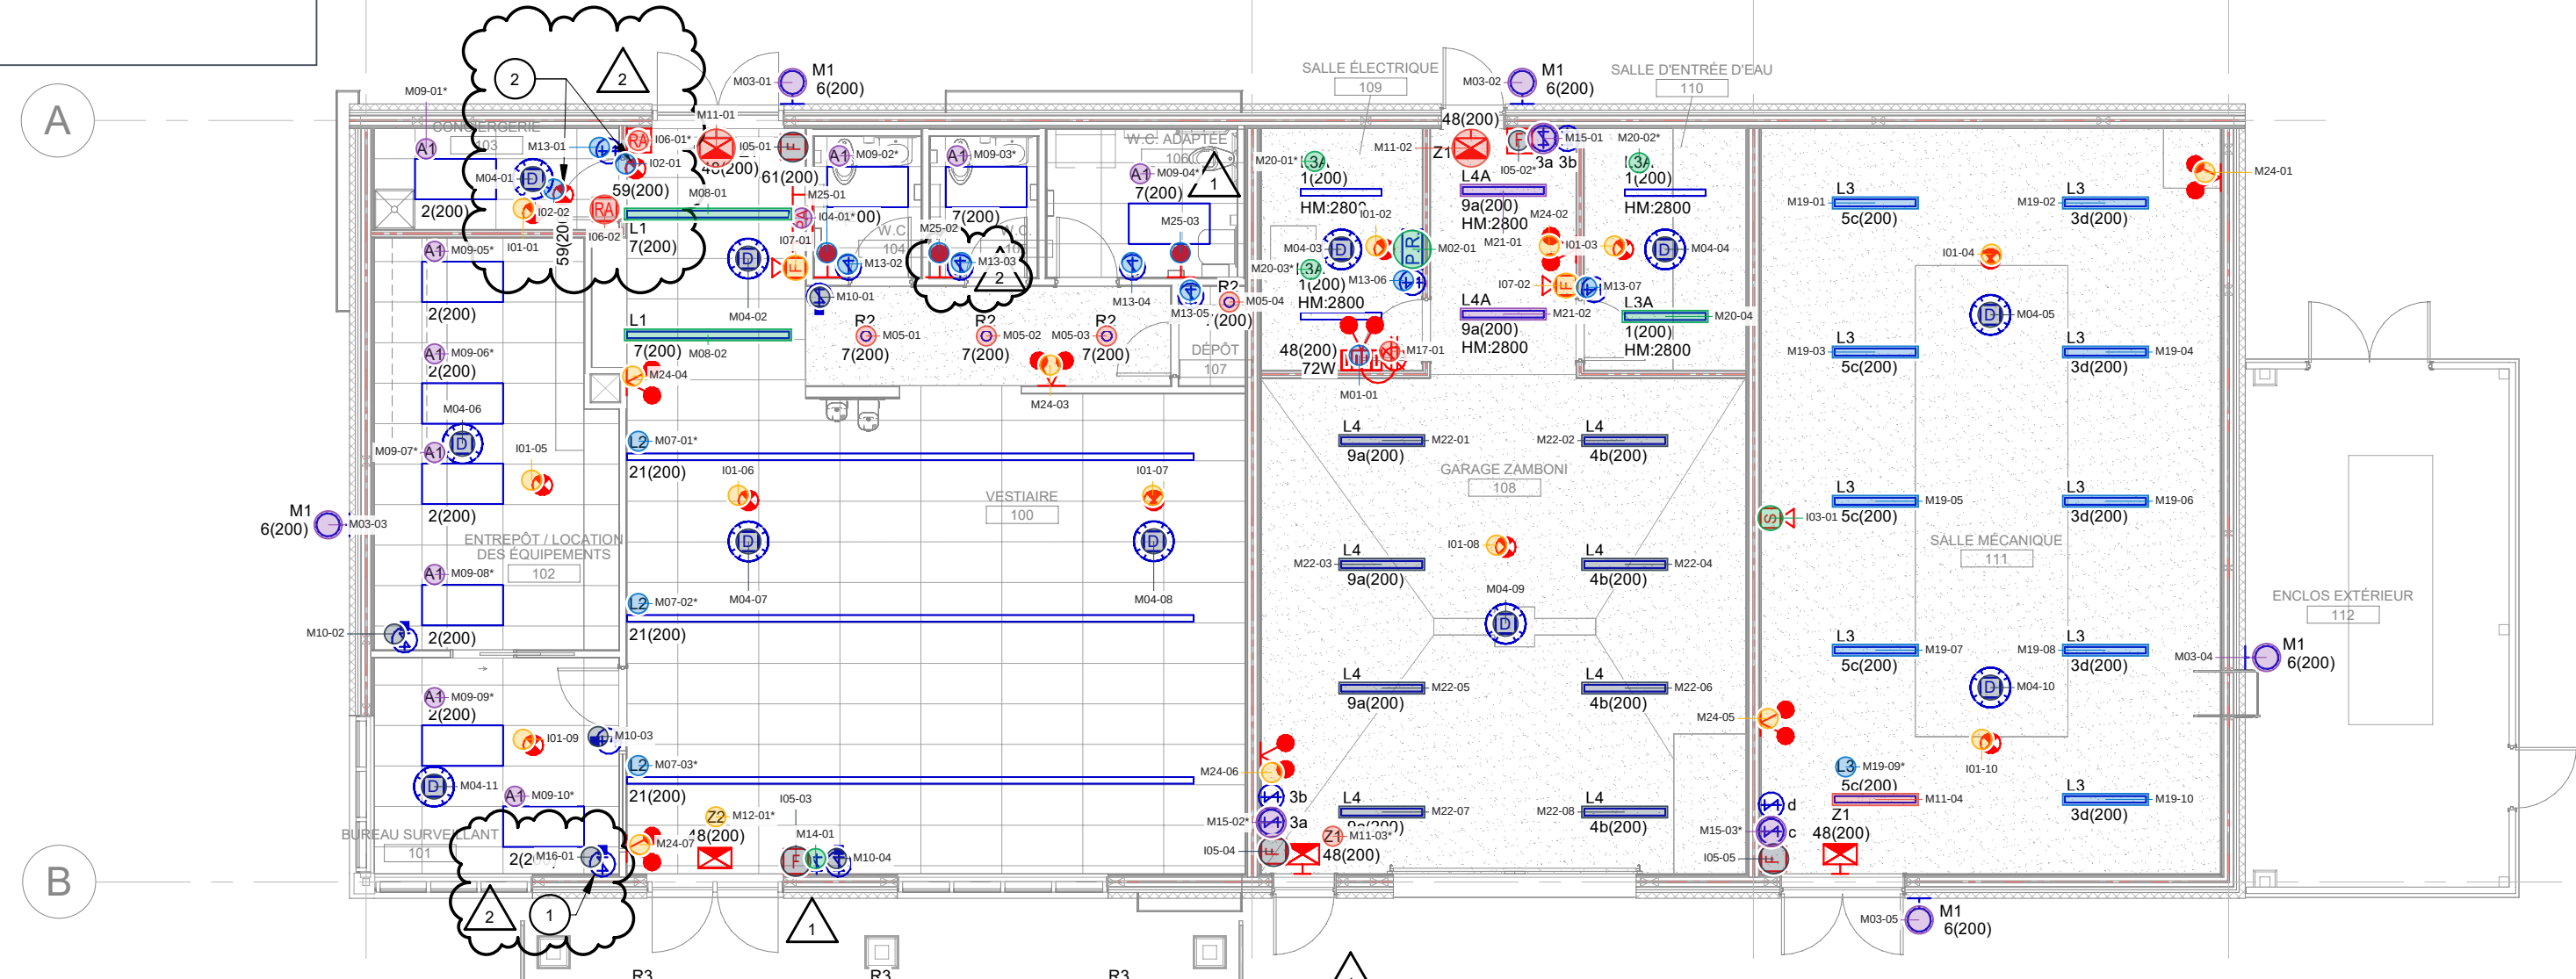
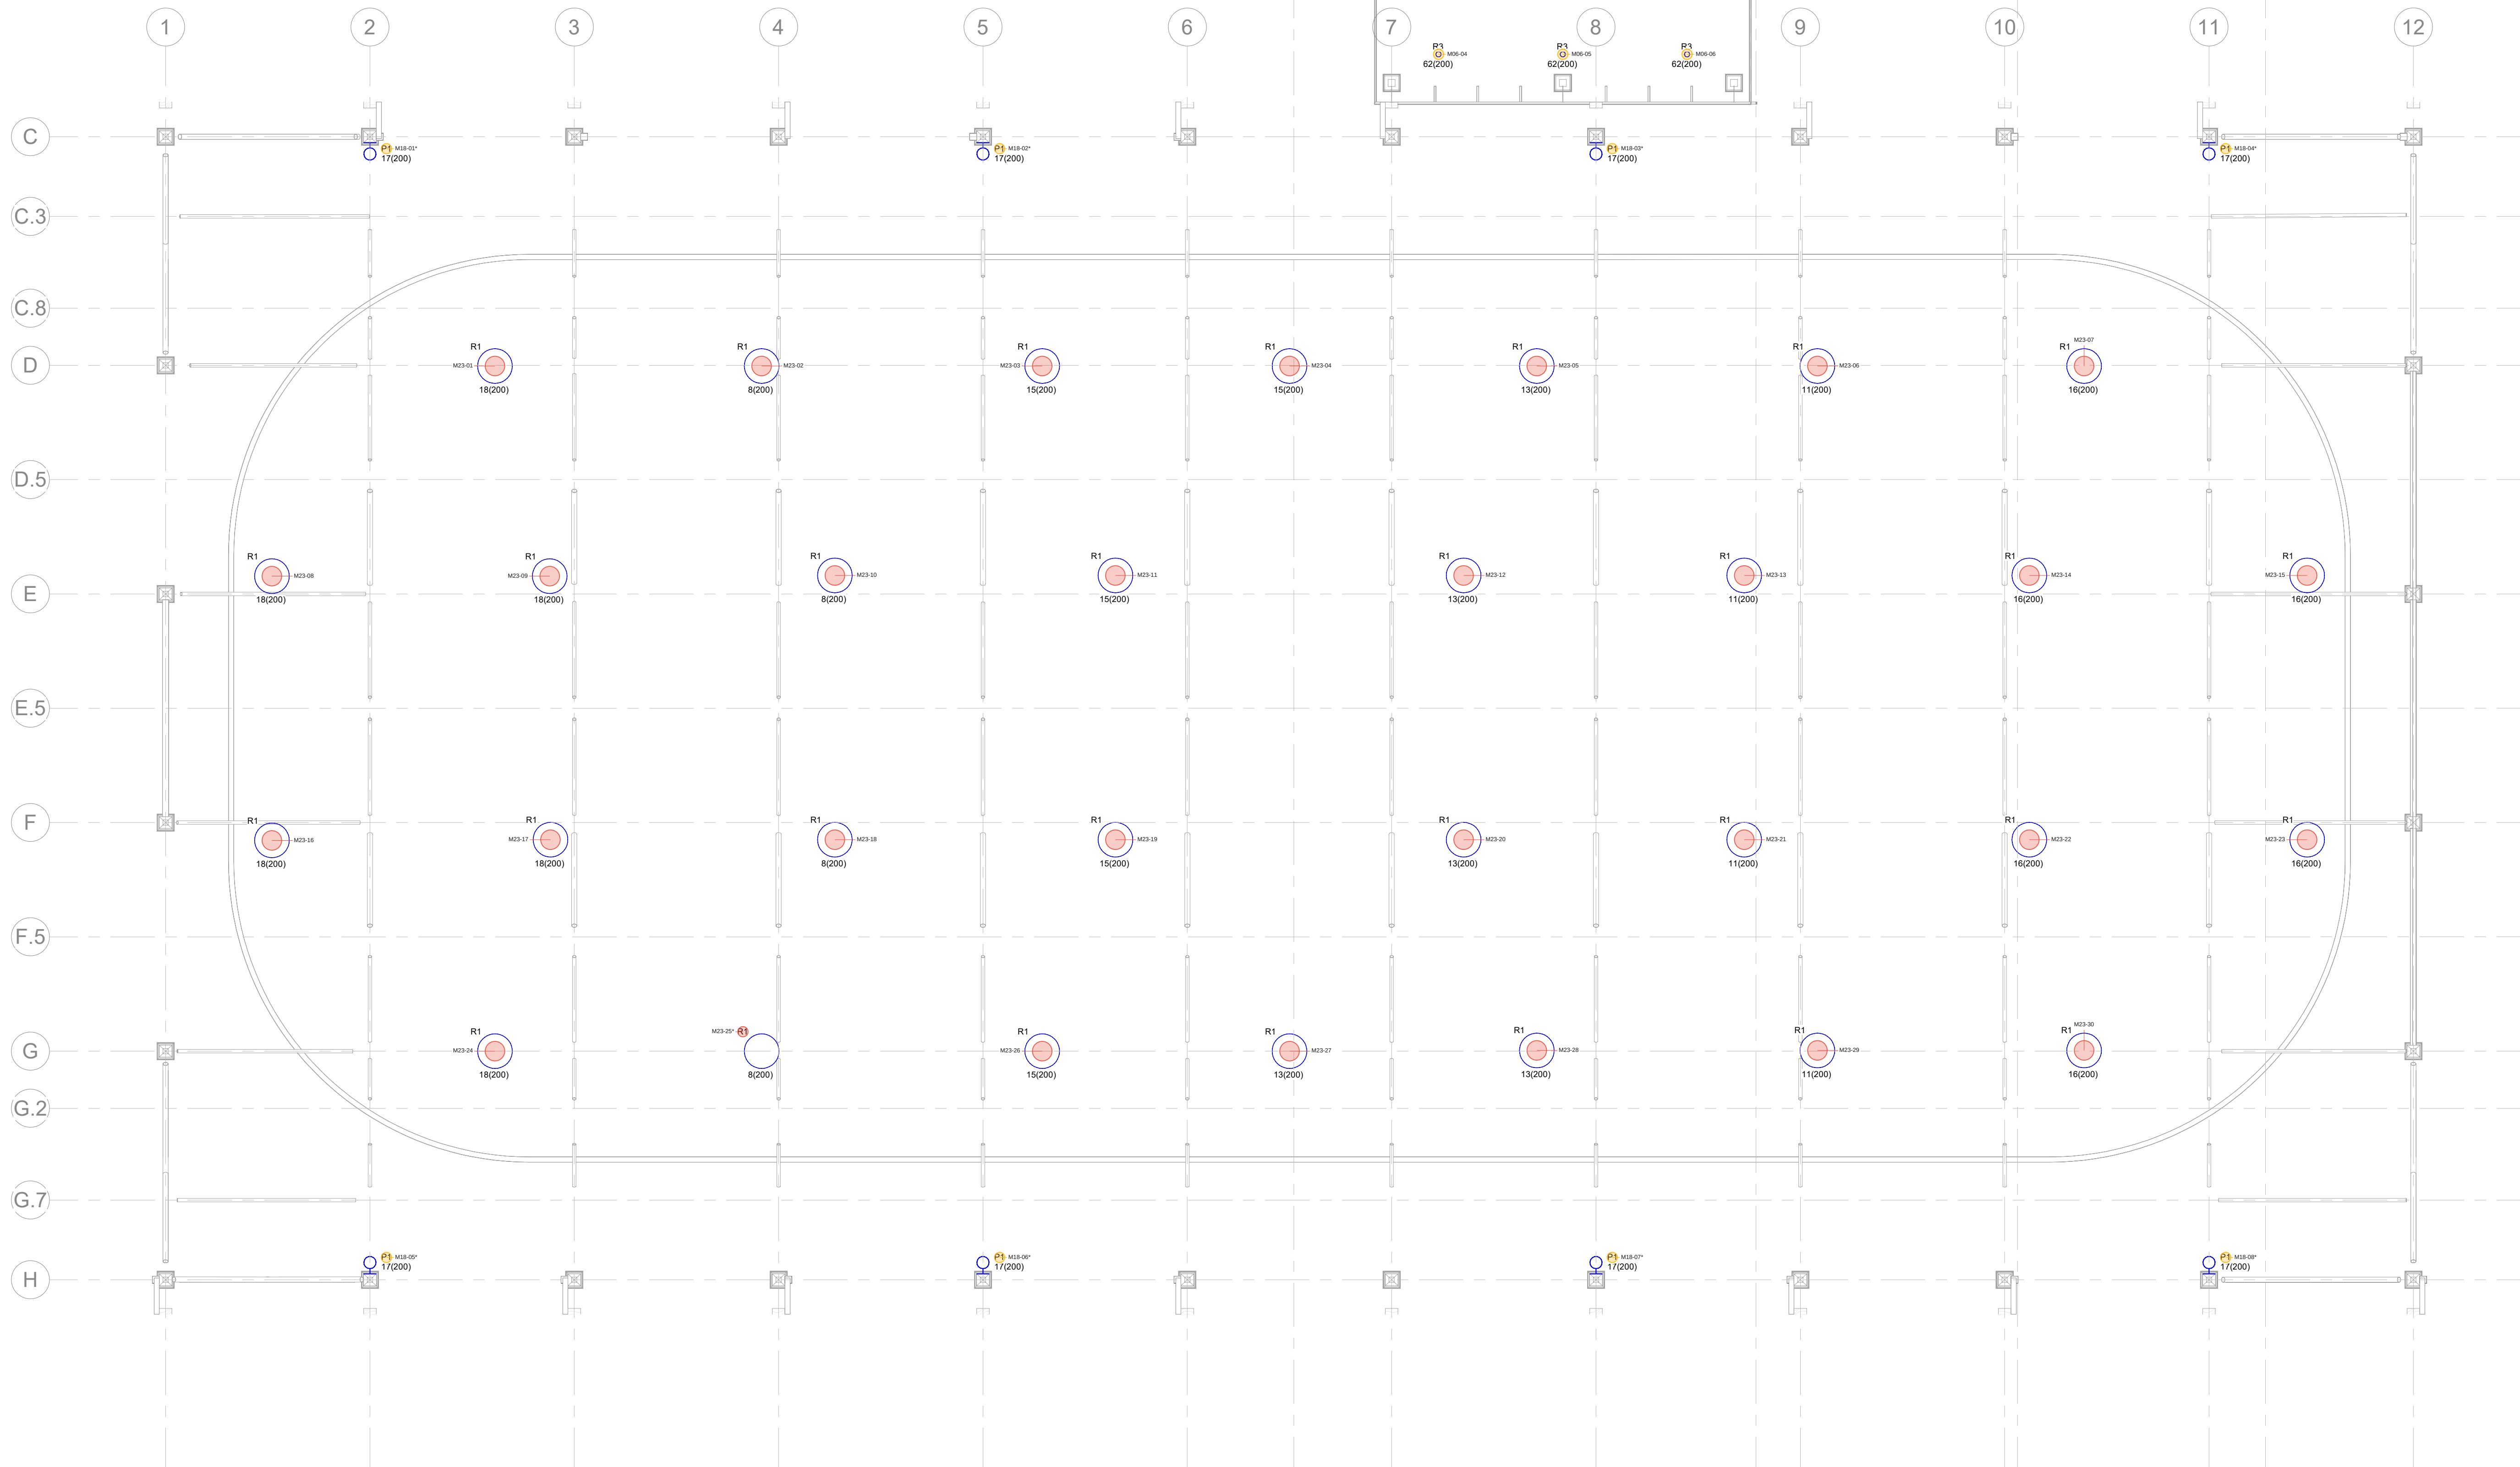
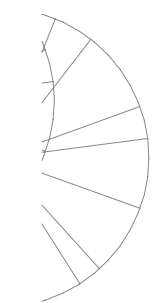
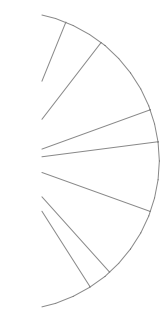
RELEVÉ E201 - MATÉRIEL 180 appareils / 32 borniers / RES 160

RES : réserve stock, modèle, position, joint ou incorporation, * = identification à valider

Câblages activables, modèles, prescriptions et réserves complètes page 9

I01	DETECTEUR DE FUMÉE	10 / R10	M05	ENCASTRE COOPER LCR4-08-RD-RP5-6300 11 VA	4 / R4	M16	PANNEAU DE CONTRÔLE D'ÉCLAIRAGE DES APPARELS TYPE P1 (NOTE SPÉCIFIQUE 1 E-201)	1 / R1
I02	DETECTEUR DE FUMÉE INSTALLÉ DANS UN CONDUIT POUR VOILETS COUPE-FEU	2 / R2	M06	ENCASTRE COOPER LCR6SRDPSE040-18W-300K 18 VA (MARQUÉE)	6 / R6	M17	PRISE DOUBLE 15A HAUTEUR SPÉCIALE	1 / R1
I03	KLAXON ET LAMPE STROBOSCOPIQUE AU MUR	1 / R1	M07	ENCASTRE DEL AXIS 88RLED-500-RD-35-FL-28 30W VA	3 / R3	M18	PROJECTEUR RGBW 55L OLMP-UNV-RGBW-BK-90 SUR COLONNE 85 VA (DMO)	8 / R8
I04	PANNEAU D'ALARME INCENDIE (CEDEULE RC-PSND-200 CCT E)	1 / R1	M08	ENCASTRE DEL AXIS 88RLED-500-RD-35-FL-8 78 VA	2 / R2	M19	SURFACE COOPER 48XK-41SL-LW-UNV-L840-CD-26 VA	10 / R10
I05	POSTE MANUEL D'ALARME INCENDIE	5 / R5	M09	ENCASTRE DEL COOPER 34CZSD33-UNV-LW-3500K 24 VA 120 V	10 / R10	M20	SURFACE COOPER 48XK-41SL-LW-UNV-L840-CD-26 VA (PM 2800)	4 / R4
I06	RELAIS ADRESSABLE D'ALARME INCENDIE	2 / R2	M10	GRADATEUR BASSE TENSION (POSTE WAVELINK WST-C-30)	4 / R4	M21	SURFACE COOPER 4V73-LO5-6-G-UNV-L840-CD3-U-V73-SS-VBK 51 VA	2 / R2
I07	SIGNALISATION SONORE TYPE KLAXON (P AVEC TRIANGLE)	2 / R2	M11	INDICATEUR D'ÉTAT AU MUR, TYPE Z1 ABSENT DU TABLEAU DES LUMINAIRES	4 / R4	M22	SURFACE COOPER 4V73-LO5-6-G-UNV-L840-CD3-U 51 VA	8 / R8
M01	ACCUMULATEUR D'ÉCLAIRAGE DE SECOURS AVEC TÊTE DOUBLE TYPE AUX (72 W)	1 / R1	M12	INDICATEUR D'ÉTAT AU PLAFOND, TYPE Z2 ABSENT DU TABLEAU DES LUMINAIRES	1 / R1	M23	SUSPENSU COOPER LH852-2436-MV-L8C-U 133 VA (PATINOIRE)	30 / R30
M02	ARMURE DE RELAIS BASSE TENSION	1 / R1	M13	INTERRUPTEUR BASSE TENSION (POSTE WAVELINK WST)	7 / R7	M24	TÊTE DOUBLE TYPE A AU MUR ALIMENTÉE PAR ACCUMULATEUR	7 / R7
M03	AU MUR COOPER GWC-SASA-E30-U-T4W 34 VA	5 / R5	M14	INTERRUPTEUR UNIPOLAIRE 120 V	1 / R1	M25	TÊTE SIMPLE TYPE A AU MUR ALIMENTÉE PAR ACCUMULATEUR	3 / R3
M04	DETECTEUR DE PRÉSENCE 300 (WAVELINK OSC-C-P00)	11 / R11	M15	PAIRE D'INTERRUPTEURS BT 3A/38 OU C0-1 UN POSTE WAVELINK WST-C-3 (UNE MARQUE PAR PAIRE)	3 / R3			

Quartier source et réseau, voir bardeau détaillé.

**NOTE(S) SPÉCIFIQUE(S)**

- PANNEAU DE CONTRÔLE D'ÉCLAIRAGE DES APPARELS DE TYPE P1.
- DETECTEURS DE FUMÉE POUR UNE INSTALLATION DANS UN CONDUIT POUR LES VOILETS COUPE-FEU/COUPE-FUMÉE.

LEGENDE DES COULEURS

LES PLANS DU PROJET DOIVENT ÊTRE CONSULTÉS EN COULEUR AUX FINS DE COMPRÉHENSION.

■ NIVEAU NORMAL

■ SÉCURITÉ DES PERSONNES

■ ALARME INCENDIE

■ EXISTANT

Client:

VILLE DE SALABERRY-DE-VALLEYFIELD
61, RUE SAINTÉ-CECILE, SALABERRY-DE-VALLEYFIELD (QUÉBEC), J6T 1L8CONSTRUCTION D'INFRASTRUCTURES
SPORTIVES AU PARC LIONEL-GROUX

118, RUE MATHIAS, SALABERRY-DE-VALLEYFIELD (QUÉBEC), J6T 3J6

CHALET, PATINOIRE ET STATIONNEMENT

POUR ADDENDA ELE-002

Architectes:

BBC
architectes
1535, chemin Sainte-Foy, suite 120
Québec (Québec) G1S 2P1
418 684-5185
architectes@bbcarchitectes.ca

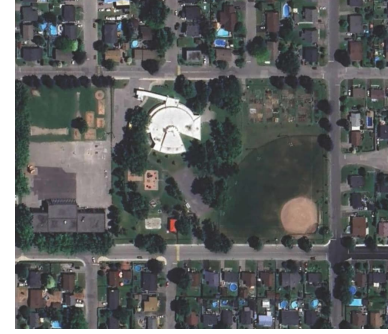
Ingénieurs mécanique / électricité:




Ingénieurs structure:

1105, BOULEVARD LEBLANC
QUÉBEC (QUÉBEC) CANADA G2H 4B6
TEL : 418 683-0441 / 1-877-418-6831 / WWW.WSP.COM

Plan clé:



Scellé:

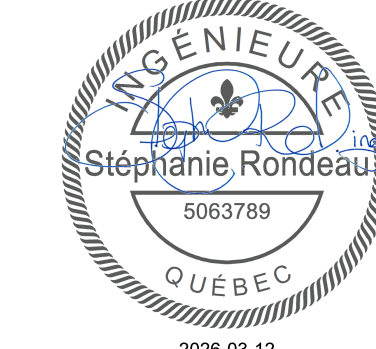

No.	Revisions	Date
1	POUR ADDENDA ELE-001	2026-03-02
2	POUR ADDENDA ELE-002	2026-03-12
0	POUR SOUMISSIONS	2026-02-06

CES DOCUMENTS NE DOIVENT PAS
ÊTRE UTILISÉS À DES FINS DE
CONSTRUCTION.**ÉLECTRICITÉ**

Titre: Échelle: 1 : 100

**ÉLECTRICITÉ
ÉCLAIRAGE ET ALARME
INCENDIE
NIVEAU 1**Conçu par: D. DUSSAULT
Dessiné par: M. GUAY
Vérifié par: D. DUSSAULT
Dossier BPA: 25-13561
Dossier BBC: 25-1811

Page

E-201

DE

11