



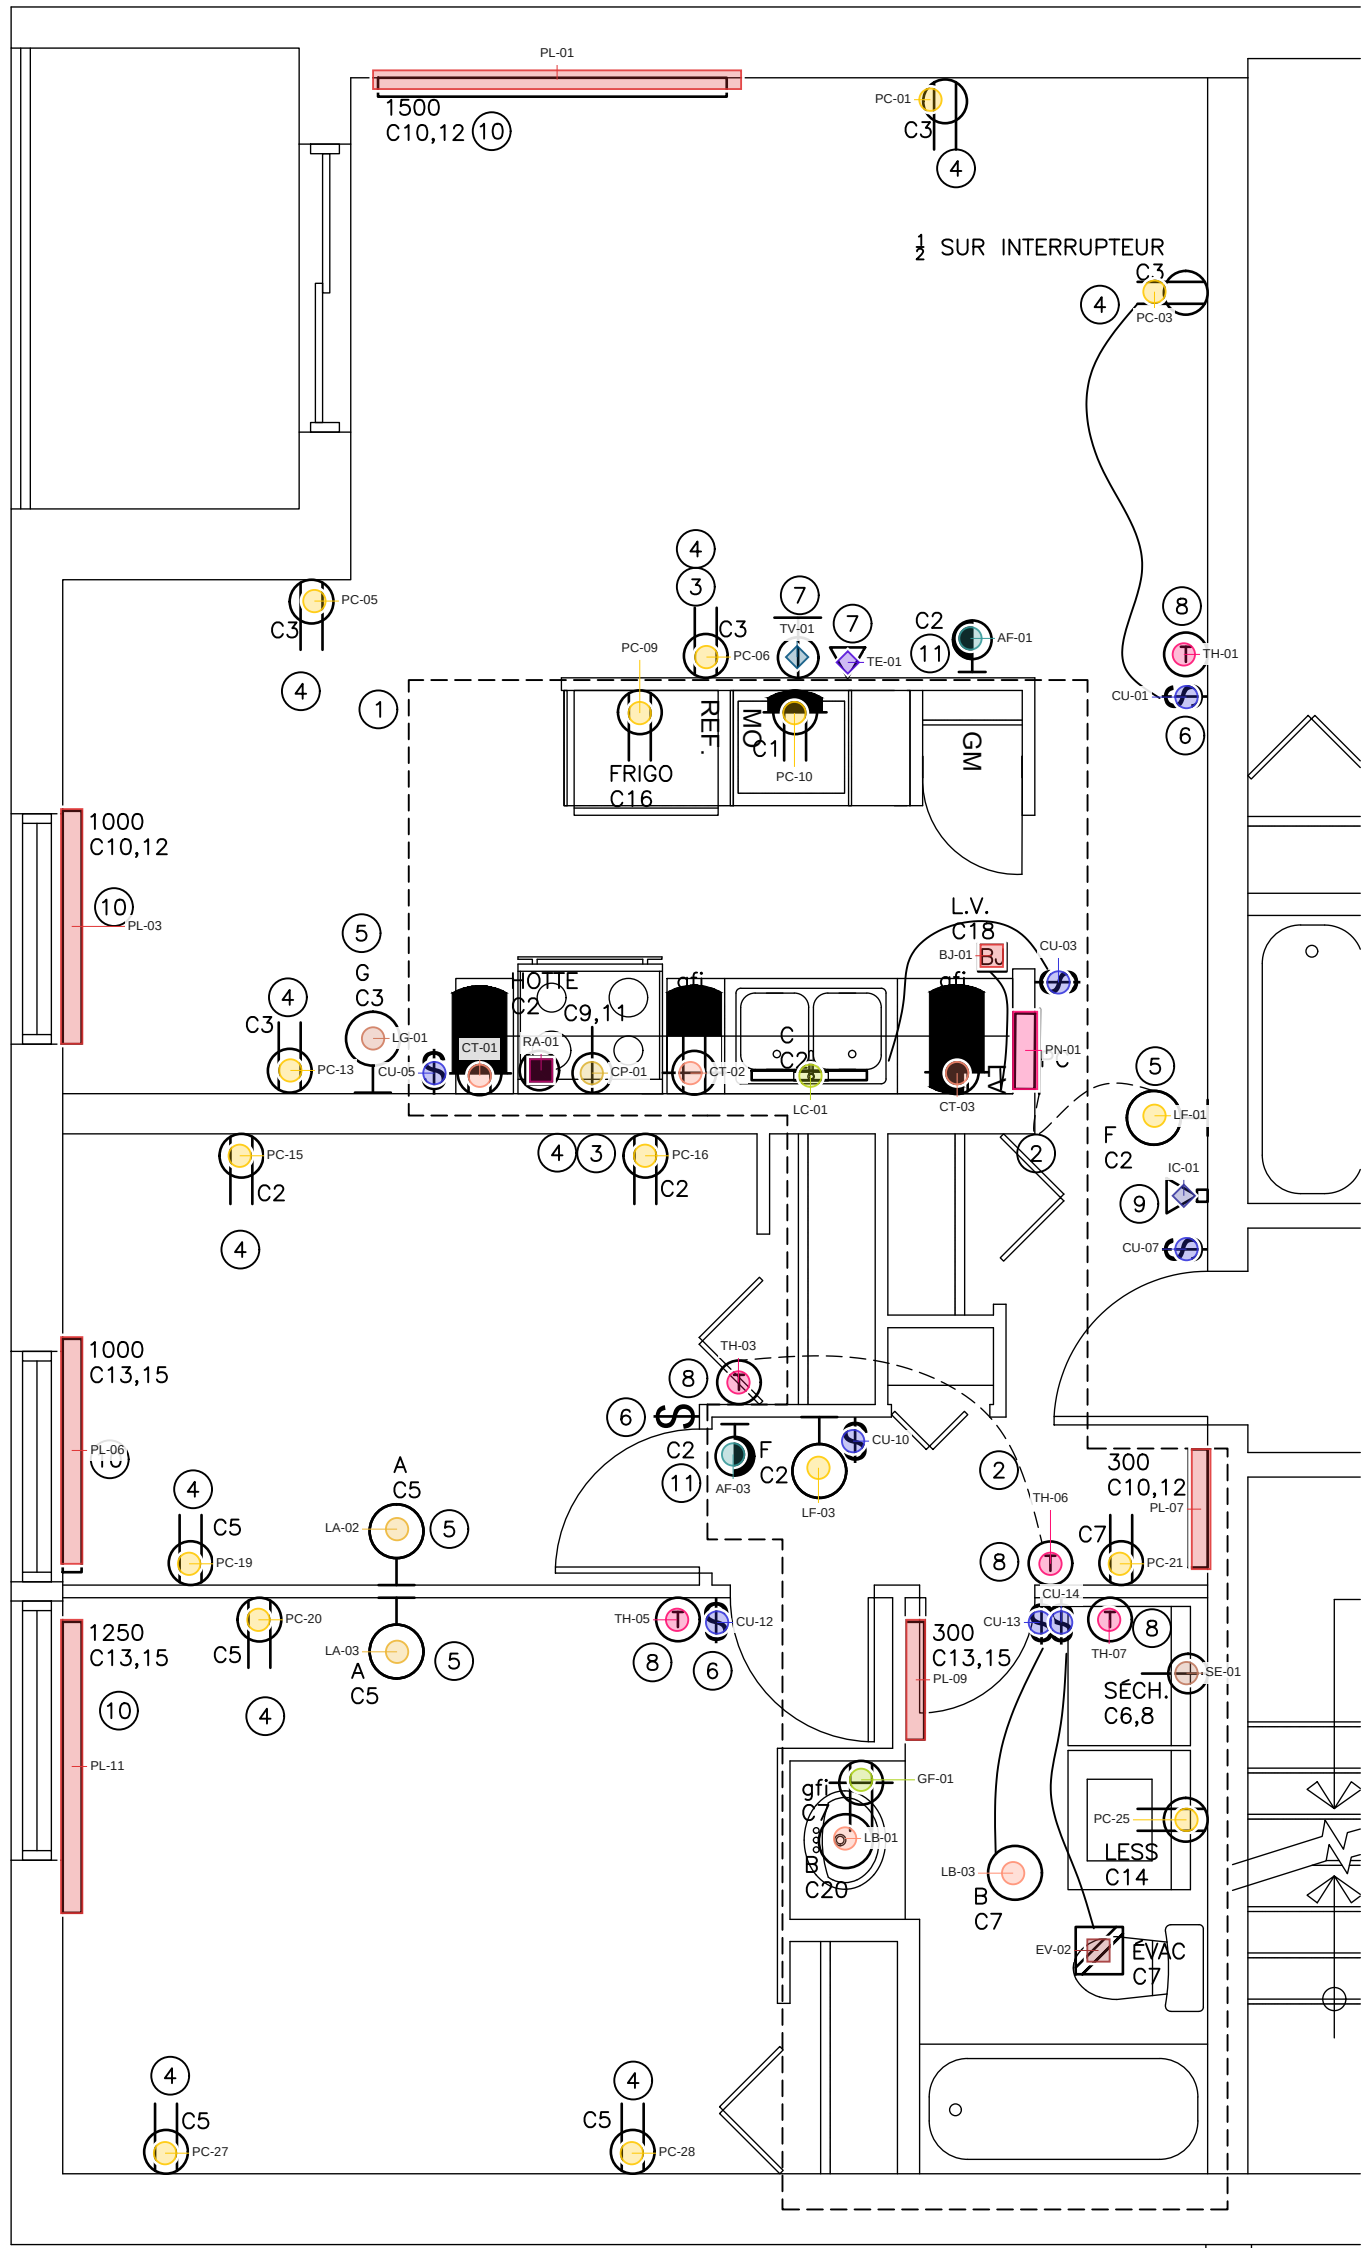

LOGEMENT TYPE C (RDC ET 2E ÉTAGE)

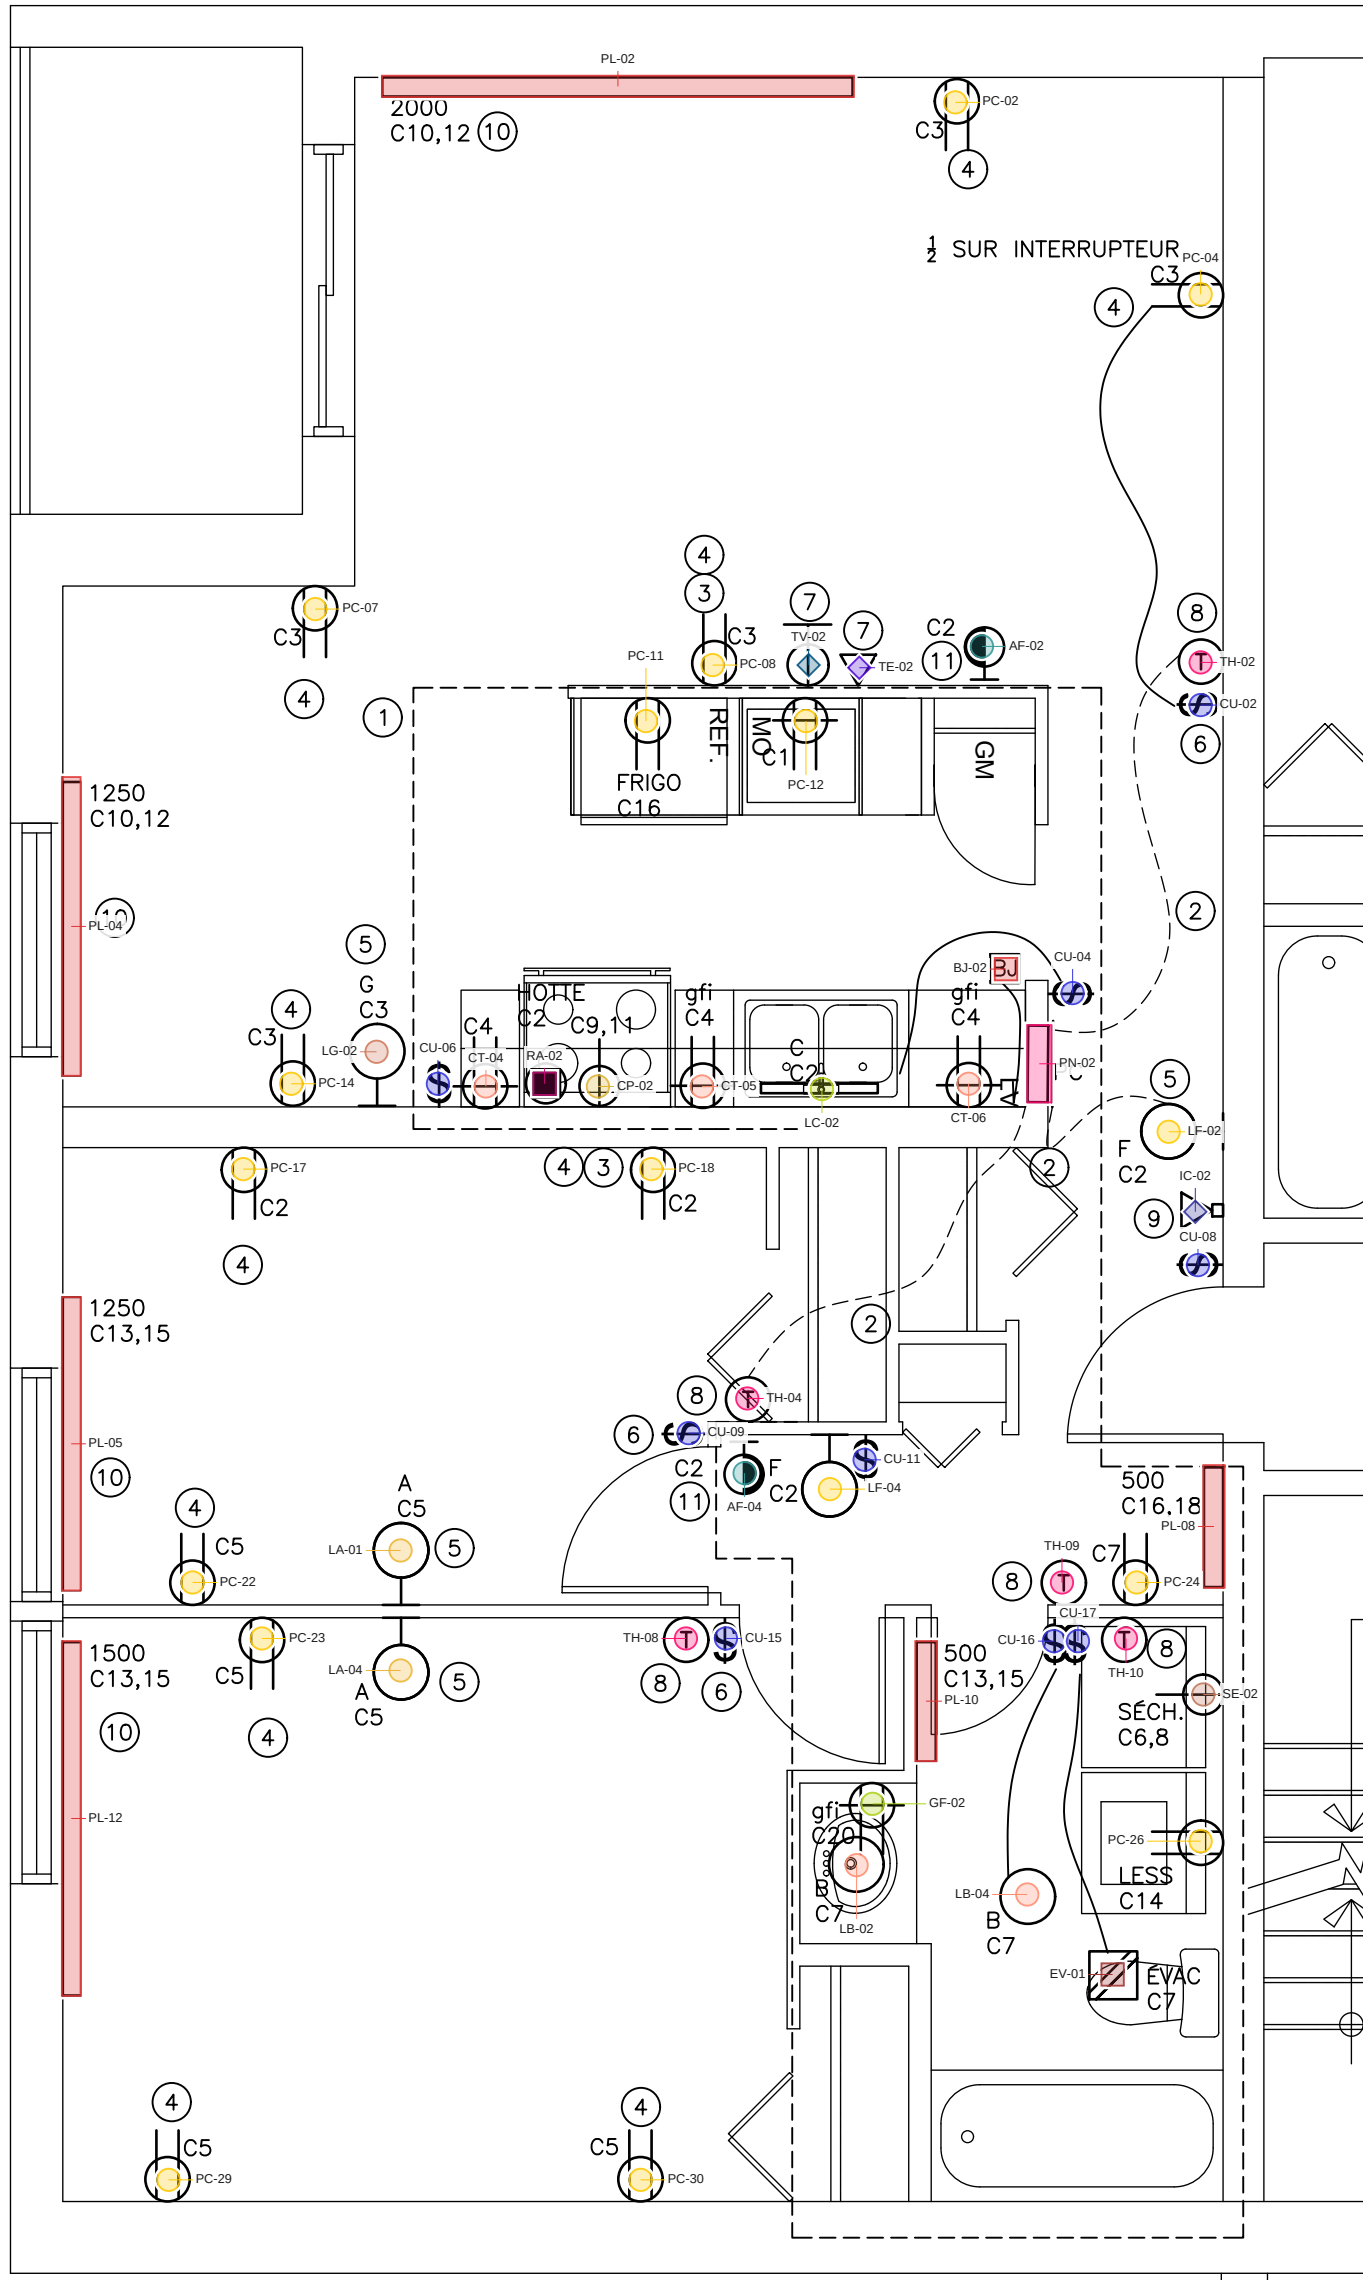

LOGEMENT TYPE F (3E ÉTAGE)

PORTÉE DES TRAVAUX – 145 ST-GEORGES

- LES TRAVAUX ÉLECTRIQUES COMPRENNENT ENTRE AUTRES, MAIS SANS S'Y LIMITER :
- LE REMPLACEMENT DE TOUS LES COMPOSANTS ET ÉQUIPEMENTS DE LA DISTRIBUTION PRINCIPALE (INCLUANT LES MÂTS DE LIVRAISON) TELS QU'INDIQUÉS SUR LES UNIFILAIRES.
 - LES MESURES DE MAINTIEN DE SERVICES ÉLECTRIQUE DURANT LES TRAVAUX REMPLACEMENT DE LA DISTRIBUTION PRINCIPALE, TEL QU'INDIQUÉ SUR L'UNIFILAIRE ET DÉCRITS AU DEVIS.
 - LE REMPLACEMENT DE TOUS LES PANNEAUX DE DISTRIBUTION DES LOGEMENTS.
 - LE REMPLACEMENT DES PANNEAUX DE DISTRIBUTION DE SERVICE.
 - LE REMPLACEMENT DE TOUS LES APPAREILS DE CHAUFFAGE, INCLUANT LES THERMOSTATS DE PIÈCE AFFÉRENTS, DE TOUS LES LOGEMENTS, DES CORRIDORS DES ESCALIERS, DES DÉPÔTS ET DES ESPACES COMMUNS.
 - LE REMPLACEMENT DE TOUTES LES PRISES DE SERVICE INDICUÉES : NEMA 5-15P, NEMA 5-20P, NEMA 14-30P (SÈCHEUSE) ET NEMA 14-50P (CUISINIÈRE).
 - LE REMPLACEMENT DE TOUS LES INTERRUPTEURS DE COURANT POUR LE CONTRÔLE D'ÉCLAIRAGE TELS D'INDIQUÉS.
 - POUR CHAQUE LOGEMENT, LA FOURNITURE ET L'INSTALLATION D'UNE NOUVELLE PRISE DE SERVICE DÉDIÉE POUR UNE UNITÉ DE CLIMATISATION DE FENÊTRE À CONFIRMER?
 - LE REMPLACEMENT DE LA DISTRIBUTION ÉLECTRIQUE AU NIVEAU DE LA CUISINE ET DE LA SALLE DE BAIN DE CHAQUE DES LOGEMENTS, VOIR LIMITES DES TRAVAUX SUR LES VUES DES LOGEMENTS TYPES.
 - LE REMPLACEMENT DE TOUTES LES PRISES DE SERVICE EXTÉRIEURES INDICUÉES ET ATTACHÉES AU BÂTIMENT.

NOTES GÉNÉRALES

- LA POSITION DES SERVICES EXISTANTS SUR LES PLANS EST APPROXIMATIVE ET DOIT ÊTRE VÉRIFIÉE ET CONFIRMÉE SUR LE SITE.
- LA POSITION DES NOUVEAUX SERVICES INDICUÉE SUR LES PLANS EST APPROXIMATIVE ET DOIT ÊTRE CONFIRMÉE AVEC LES PLANS D'AMÉNAGEMENT EN ARCHITECTURE.
- ASSURER LA CONTINUITÉ DES ALIMENTATIONS ÉLECTRIQUES DES SERVICES NON TOUCHÉS PAR LES TRAVAUX DE REMPLACEMENT DE CIRCUITS DANS LES LOGEMENTS. À CET EFFET, PRÉVOIR, POUR FIN DE SOUMISSION, ET CE, POUR CHAQUE LOGEMENT, DEUX CONTINUITÉS DE SERVICE INCLUANT UNE LONGUEUR TOTALE DE CÂBLES DE 10 MÈTRES (30 PIEDS) ET DEUX BOÎTIERS ÉLECTRIQUES MURAUX ENCASTRÉS (2X4) AVEC COUVERCLE AVEUGLE.
- LA TOTALITÉ DES CIRCUITS D'ALIMENTATION EXISTANTS À CONSERVER SONT FAITS AVEC DU CÂBLE AVEC CONDUCTEUR D'ALUMINIUM. PRÉVOIR DES DISPOSITIFS (PRISE DE SERVICE, INTERRUPTEUR, ETC.) ET DES MÉTHODES DE RACCORDEMENT ET D'INSTALLATION, APPROPRIÉES ET COMPATIBLES AVEC DES CONDUCTEURS D'ALUMINIUM.
- L'ENTREPRENEUR EST RESPONSABLE DE NE PAS CASSER LES EXTRÉMITÉS DES CONDUCTEURS D'ALUMINIUM EXISTANT. L'ENTREPRENEUR SERA TENU DE REMPLACER, À SES FRAIS (INCLUANT LES TRAVAUX GÉNÉRAUX) TOUS LES CÂBLES AVEC CONDUCTEURS D'ALUMINIUM RENDUS TROP COURTS PAR SA MANIPULATION.
- LA POSITION DES SERVICES EST DONNÉE À TITRE INDICATIF SEULEMENT. LA POSITION EXACTE DE CES SERVICES DOIT ÊTRE DÉTERMINÉE SUR LE CHANTIER.
- L'IDENTIFICATION DES CIRCUITS D'ALIMENTATION EST DONNÉE À TITRE INDICATIF SEULEMENT. ELLE DOIT ÊTRE VÉRIFIÉE ET VALIDÉE AU CHANTIER.
- L'ENTREPRENEUR DOIT RESPECTER L'IDENTIFICATION ET LA POSITION DES CIRCUITS D'ALIMENTATION INDICUÉ SUR CE PLAN, LORS DES BRANCHEMENTS DE CIRCUITS DANS LES NOUVEAUX PANNEAUX DE DISTRIBUTION.

NOTES EN PLAN

- PRÉVOIR LE REMPLACEMENT DES CÂBLES D'ALIMENTATION, DES BOÎTIERS ET SERVICES (APPAREILS D'ÉCLAIRAGE, INTERRUPTEUR, PRISE DE SERVICE, PLINTE DE CHAUFFAGE) POUR TOUS LES SERVICES INDICUÉS À L'INTÉRIEUR DE CETTE LIMITE.
- CÂBLE D'ALIMENTATION EXISTANT À CONSERVER ET À REALIMENTER À PARTIR DU NOUVEAU CÂBLE D'ALIMENTATION DANS LE NOUVEAU SERVICE INDICUÉ.
- PRÉVOIR REMPLACER LE CÂBLE D'ALIMENTATION POUR CES SERVICES EXISTANTS.
- PRISE DE SERVICE EXISTANTE À REMPLACER.
- APPAREILS D'ÉCLAIRAGE EXISTANT À REMPLACER.
- INTERRUPTEUR EXISTANT À REMPLACER.
- PLAQUE DE SERVICE EXISTANTE À REMPLACER (TÉLÉPHONIE OU CABLE DISTRIBUTION).
- THERMOSTAT DE PIÈCE ÉLECTRONIQUE EXISTANT À CONSERVER.
- INTERCOM (CONTRÔLE DE PORTE) EXISTANT À CONSERVER.
- PLINTE DE CHAUFFAGE ÉLECTRIQUE EXISTANTE À REMPLACER.
- NOUVEL AVERTISSEUR D'INCENDIE AUTONOME (VOIR DÉTECTION ET SIGNALISATION INCENDIE).

PERCEMENT DE DALLE STRUCTURALE

JUSTIFICATION : LES DALLES DE PLAFOND ET PLANCHER SONT DES DALLES DE CIMENT VIDÉES AVEC DES CÂBLES EN PRÉ-TENSION. IL EST PRIMORDIAL DE NE PAS TOUCHER LES CÂBLES EN PRÉ-TENSION LORS DES PERCEMENTS. CELI N'EST PAS APPLICABLE À LA DALLE SUR SOL AU SOUS-SOL.

APPLICATION : POUR TOUS LES PERCEMENTS ET ANCRAGES DEVANT ÊTRE EFFECTUÉS DANS UNE DALLE STRUCTURALE DE PLANCHER ET/OU PLAFOND, EXCLUANT LA DALLE SUR SOL.

PROCÉDURE : PRÉVOIR UN "SCAN" LOCAL DE LA DALLE VISÉE PAR LES TRAVAUX. IDENTIFIER À L'AIDE D'UN MARQUEUR LA POSITION DES CÂBLES EN PRÉ-TENSION ET DES SECTIONS VIDÉES DE DALLE. EFFECTUER TOUT PERCEMENT À UNE DISTANCE MINIMUM DE 50MM DE TOUS CÂBLES EN PRÉ-TENSION.

RELEVÉ E05 - MATÉRIEL

115 repères / 21 familles / calques activables

0 non identifiés - 0 identifications à revalider (*)

RES 115 : modes non précises / portes à confirmer - voir bordereau page 2

AF	AVERTISSEUR DE FUMÉE MURAL 120V	4 / R4
BJ	BOÎTE DE JONCTION POUR LAVE-VAISSELLE	2 / R2
CP	PRISE DE COURANT POUR CUISINIÈRE	2 / R2
CT	PRISE DE COURANT AU DESSUS D'UN COMPTOIR	6 / R6
CU	COMMUTATEUR UNIPOLAIRE	17 / R17
EV	EVACUATEUR DE TOILETTE	2 / R2
GF	PRISE DE COURANT AVEC DISJONCTEUR DIFFÉRENTIEL DE FUITE À LA TERRE	2 / R2
IC	INTERCOM (CONTRÔLE DE PORTE) EXISTANT - MODÈLE NON INDICUÉ	2 / R2
LA	LUMINAIRE TYPE A	4 / R4
LB	LUMINAIRE TYPE B	4 / R4
LC	LUMINAIRE TYPE C	2 / R2
LF	LUMINAIRE TYPE F	4 / R4
LG	LUMINAIRE TYPE G	2 / R2
PC	PRISE DE COURANT DOUBLE	30 / R30
PL	PLINTE DE CHAUFFAGE	12 / R12
PN	PANNEAU DE LOGEMENT	2 / R2
RA	RACCORD DIRECT HOTTE	2 / R2
SE	PRISE DE COURANT SÈCHEUSE	2 / R2
TE	SORTIE TÉLÉPHONIQUE	2 / R2
TH	THERMOSTAT EXISTANT - MODÈLE NON INDICUÉ	10 / R10
TV	SORTIE POUR CABLE-DISTRIBUTION (TV)	2 / R2

RES = réserve source, modèle, position ou porte; * = identification à revalider.
Quantités = repères de cette feuille; les renvois ne s'additionnent pas.
Modèles, prescriptions et sources : bordereau page 2.

NE PAS UTILISER
POUR CONSTRUCTION

CONSULTANT:



SCEAU:

CLIENT:

**OFFICE D'HABITATIONS
HAUT RICHELIEU
145, RUE LATOUR, BUREAU 100
ST-JEAN-SUR-RICHELIEU, QC**

ÉMISSION

No.	DATE	PAR	DESCRIPTION
3	2026-08-31	AR	POUR APPEL D'OFFRES

RÉVISION

No.	DATE	PAR	DESCRIPTION
△	2026-06-16	AR	COMPLÉT
△			
△			
△			

PROJET:

**RÉFECTION DES CUISINES ET
SALLES DE BAIN ET
ET DIVERS TRAVAUX**

DESSIN:

**LOT A - 145 SAINT-GEORGES
LOGEMENTS TYPES, 3 DE 3
SERVICES ET ÉCLAIRAGE
ÉLECTRICITÉ**

No. DOSSIER CLIENT:

HR26-14

DESSINATEUR:

AR

ÉCHELLE:

1:40

No. DOSSIER ARI:

OMR2402RCB

FEUILLE:

E05

CONCEPTEUR:

AR

DATE:

24-03-15

FICHER:

ME.dwg

RÉVISION

C